עבור אישור מתקן לאשפה

22

ב21 - 1160

עיריית תל-אביב-יפו מינהל ההנדסה
תכנית מאושרת
לסידורי אצירה ופינוי אשפה
12-02-2002
אישור מס׳ ...
הערות ...
אדר׳ פינחסוב יוסף, מהנדס רישוי
חתימה ...

הוראות ביצוע בהתאם לקובץ
התחנויות-פרק 12 "אצירת אשפה"
לפני איכלוס המבנה
לתאם סופית עם
אגף התברואה
את המתקנים לאצירת אשפה

עיריית תל-אביב מינהל הנדסה
נתקבל
04-04-2002
תיק

עיריית תל - אביב - יפו

מינהל ההנדסה, אגף רישוי ופיקוח על הבנייה
שדרות בן-גוריון 68 תל-אביב 64514 (פקס 5231340) טלפון 5217120, 5217045

לכבוד ☒ הוועדה המקומית לתכנון ולבנייה
☐ רשות הרישוי המקומית

חוק התכנון והבנייה, התשכ"ה-1965
תקנות התכנון והבנייה (בקשה להיתר תנאיו ואגרות) התש"ל-1970

בקשה להיתר בנייה או לשימוש במקרקעין - בניין חדש

יש להקפיד למלא את כל הפרטים בטופס הבקשה ולצרף מסמכים כמפורט ברשימת התיוג המצורפת.

על פי טופס 1 תקנה 2(א)

מס׳ תיק הבניין	מס׳ בקשה קודמת להיתר בנייה	מס׳ הבקשה למידע	מתאריך
4047-27	–	מ/210238	22-02-2001

א. פרטי הנכס והמבקשים

הכתובת	רחוב	מס׳ בית	גוש	חלקה	תת חלקה	מגרש	הוראות התכניות החלות על המקום
	תשבי	27	6135	110 (חלק)			ת/N2215,2215,ג

פרטים אישיים	שם משפחה / שם פרטי	מס׳ זהות/חברה או מס׳ רישום תאגיד	רחוב ומספר בית / ישוב ומיקוד	מספר טלפון / מספר פקס
מבקש 1	גורדון ג׳ונתהן	309898773	רח׳ התשבי 27 תל - אביב	053-247447
מבקש 2				
מבקש 3				
בעל הזכות בנכס	סושניק גוליין	מס׳ דרכוני 101982845	בוסטון ארה״ב	
החוכר				
עורך הבקשה הראשי	אורנת זוהר	13041496	בית צורי 12 ת״א 69122	03-5618868 03-5615675
מתכנן שלד הבניין	סגל מיכאל	6903184	רח׳ נתן ילין-מור 6 תל - אביב	03-5627020 03-5617999

ב. מהות הבקשה לבנייה חדשה

☒ הריסת מבנה קיים הכולל 1 קומות מגורים/ ___
☒ הקמת מבנה חדש הכולל:
☐ מרתף/ים ☐ קומה מפולשת ☐ קומה מסחרית ל ___
☒ 3 קומות מגורים ובהן 1 יחידות דיור ~~משרדים~~
☐ המרתף/ים כולל/ים: ☐ מקלט ☐ מחסן ☐ חדרי עזר ___
☐ קומת הקרקע כוללת: ☐ אולם כניסה ☐ חדר גז
☐ חדר אשפה ☐ ___ חניות ☐ מסעדה
☒ 1 חדרי שירותים ☐ ___
☐ על הגג: ☐ חדרי יציאה ☐ חדרי מכונות ☒ קולטי שמש
☐ חדר מדרגות כללי ☐ פרגולה ☐ ___
☐ בחצר: ☐ ___ מקומות חנייה ☒ גינה
☒ שטחים מרוצפים ☐ פרגולה
☐ בגבולות המגרש גדר בגובה 1.80 מטר
פירוט נוסף ___

ג. מפרט - תיאור הבקשה

תיאור הקיים על המגרש (פרט מספר מבנים, גובהם, מקומם וכד׳): בית בן קומה 1 המיועד להריסה

שימוש עיקרי: ☒ מגורים ☐ משרדים ☐ מסחר ☐ מלונאות ☐ בידור ☐ נופש וספורט ☐ תעשייה ☐ בניין ציבורי ☐ מלאכה ☐ חקלאי ☐ שימוש אחר, פרט:

סוג העבודה או השימושים המוצעים: ☒ הריסה ☒ בניין חדש

הגורם שמתבצעת בעבורו הבנייה: ☐ משרד ממשלתי ☐ רשות מקומית ☐ מוסד ציבורי ☒ גורם פרטי ☐ בנה ביתך ☐ אחר:

שטחים: שטח הבנייה הכולל המבוקש 117.39 מ״ר
שטח המגרש/החלקה 112 לפי טאבו, 76 לפי מודד מ״ר; אחוזי הבנייה 154.5%

ד. חומרי הבניה

סוג הבנייה: ☒ רגילה ☐ בית מוכן ☐ מתועשת ☐ אחר
קירות חיצוניים: ☐ בטון מזוין ☒ בלוקים ☐ אבן טבעית ☐ לבנים שרופות ☐ אחר
חומרי גימור: ☐ אבן מלאכותית ☐ אבן טבעית ☒ טיח ☒ זכוכית ☐ אחר מתכת
תקרות: ☒ בטון מזוין ☐ עץ ☐ אחר
גג: ☒ בטון מזוין ☐ רעפים ☐ אסבסט ☐ פח ☐ אחר
גדרות: ☒ אבן טבעית ☐ אבן מלאכותית ☐ בטון ☐ בלוקים ☒ ברזל ☐ עץ ☐ רשת ☐ אחר
קיימות ___ מ״א מוצעות 7.60 מ״א סה״כ 7.60 מ״א

מקרא חומרים (צבעים): ■ בטון או בטון מזוין; ■ בלוקים או לבנים מבטון; ☐ סיליקט או לבנים אדומות; ☐ אבן; ☐ עץ; ☐ איטום; ☐ זכוכית; ☐ הריסה; ☐ אחר

ו. קווי בנייה

הכיוון		מוצע	מותר	הסטייה במטר	הסטייה ב-%
לרחוב (שם)	התשבי	0	0	0	0
לצד	צפון	0	0	0	0
לצד	דרום	0	0	0	0
לאחור	מזרח	3	3	0	0

ז. מספר יחידות דיור

אם השימוש המבוקש הוא מגורים – רשום להלן:
מספר הדירות המבוקשות: 1 (מעל ל - 120 מ״ר / מתחת ל - 120 מ״ר)
מספר הדירות המותרות: 1

ח. השטחים המבוקשים לבנייה (על-פי תכני ת הבנייה) והמותרים לבנייה (על-פי "אסמכתא": חוק, תקנות, תכנית) בכל מפלס בנפרד ולפי שימוש

הקומה/המפלס	(א) מגורים מ״ר מבוקש	מגורים מ״ר מותר	סך כל שטחי הבנייה העיקריים מ״ר	% משטח המגרש	סך כל השטחים המותרים	ממ״ד	מתקנים חדרים ומערכות מכניות	החסנה	חניה	מבואות וחדרי מדרגות	קומת עמודים מפולשת	מעברים לכלל הציבור	בליטות	אחר	בנייה קיימת	(ב) סך כל שטחי השרות מ״ר	% משטח המגרש	סך כל השטחים המותרים	(ג) סך כל שטחי הבניין מ״ר	% משטח המגרש	סך כל השטחים המותרים	משטחים לא מקורים
קרקע	44.45		44.45	58.5%		7.5	0	0	0	0	0	0	0	0	0	7.5	9.9%	7.5	51.95	68.4%		0.00
קומה א׳	39.04		39.04	51.4%															39.04	51.4%		11.57
קומה ב׳	26.40		26.40	34.7%															26.40	34.7%		2.40
סה״כ מעל הקרקע	109.89	112.10	109.89	144.6%	112.10	7.5										7.5	9.9%	7.5	117.39	154.5%	119.6	13.97
סה״כ מתחת לקרקע	0		0	0																		
סה״כ	109.89	112.10	109.89	144.6%	112.10	7.5										7.5	9.9%	7.5	117.39	154.5%	119.6	13.97

ת. פרטי הבנייה – לשימוש הלשכה המרכזית לסטטיסטיקה

היעוד	פירוט היעוד	השטח על פי ההיתר	מספר חדרים	מספר דירות	מספר מגורים
למגורים	דירת מגורים	109.89	4	1	1
להארחה					
לעסקים ולמשרדים					
לבנייני ציבור					
לתעשייה ולמלאכה					
למשק חקלאי					
למקלט או למרתף					
למבני עזר					
סך כל שטח הבנייה		109.89	סה״כ	1	1

ט. הבקשה מוגשת לאישור

☒ הוועדה המקומית
הבקשה כוללת בקשה להקלה – כלהלן:

פירוט הבקשה להקלה	נימוקי הבקשה להקלה
1.	
2.	
3.	

☐ רשות הרישוי המקומית
☐ רשות הרישוי המקומית באמצעות מורשה להיתר

י. הצהרת עורך הבקשה הראשי

אני מצהיר על נכונות הפרטים בסעיפים א עד ט.
תאריך 20-05-2001 שם אורנת זוהר חתימה ___

יא. חתימות נוספות

המבקש: תאריך 5-06-2001 שם גורדון ג׳ונתהן חתימה X
בעל הזכות בנכס/בעל הנכס/החוכר: תאריך 5-06-2001 שם סושניק גוליין חתימה ___
תאריך ___ שם ___ חתימה ___
מתכנן שלד הבניין: תאריך 5-06-2001 שם סגל מיכאל חתימה ___

הערות: תאריך ___ שם ___ חתימה ___

הנדון בדוח / הנדון בתביעה; מס׳ הדוח/התביעה; תאריך הדוח/התביעה; ☐ הוכן דוח לתביעה משפטית ☐ הוגשה תביעה משפטית ☐ הוגשה תביעה חוזרת; התוכנית תואמת את המצב בשטח ☐ כן ☐ לא; לשימוש המשרד – הערות הפיקוח

מספר היתר הבנייה; תאריך היתר הבנייה; תאריך התחלת הבנייה; תאריך גמר הבנייה; מספר הקומות כולל קומת עמודים מפולשת

יב. מינויים מטעם מבקש ההיתר

נוספת אדם אחד ליותר מתפקיד אחד, ימולא פרטיו ליד כל אחד מהתפקידים שהוא ממלא על פי הוראות כל דין.

מינוי עורך הבקשה הראשי: ☐ אני ממנה בזה את אורנת זוהר בעל/ת מס׳ זהות 13041496 הרשום בסעיף א להיות עורך הבקשה הראשי להיתר, ולייצגני לפני מוסדות התכנון והרשויות המוסמכות בכל הנוגע לטיפול בבקשה להיתר ולקבלתו, לרבות התיקונים ככל שידרשו הרשויות המוסמכות.

מינוי עורכי בקשה לפי תחומים: ☐ אני ממנה בזה את הרשומים להלן להיות עורכי הבקשה להיתר בתחום הפעולה הרשום ליד שמו, ולייצגני לפני מוסדות התכנון והרשויות המוסמכות בכל הנוגע לטיפול בבקשה להיתר ולקבלתו לרבות התיקונים ככל שידרשו הרשויות המוסמכות.

	שם משפחה ושם פרטי	תחום פעולה	המען	מספר טלפון	מספר פקס
1.	מרקוביץ׳ מרינלה	מתכנן האינסטלציה הסניטרית	רח׳ גוטך 15, ת.ד. 7497 קרית מטלון פתח - תקווה 49160	03-9234941/2	03-9234945
2.	פינטר יוסי	מתכנן חשמל	רח׳ סירקין 15 א גבעתיים	03-6701652	03-6739688
3.					

מינוי מתכנן שלד הבניין: ☐ אני ממנה בזה את סגל מיכאל בעל/ת מס׳ זהות 6903184 הרשום בסעיף א להיות אחראי לתכנון שלד הבניין שבעבורו מבוקש ההיתר, להגיש לוועדה המקומית לרשות הרישוי המקומית את החישובים לגבי הבניין שבעבורו מבוקש היתר ולפקח פיקוח עליון על הקמת השלד.

מינוי הקבלן האחראי לבנייה: ☐ אני ממנה בזה את ___ בעל/ת מס׳ זהות ___ ובעל תעודת רישום בפנקס הקבלנים מספר ___ במדור ___ ובעל רישיון לביצוע עבודה בתוקף עד ___ לבצע את העבודה הנדונה בהיתר כמחייב לפי כל דין.
☒ אני מצהיר, כי פרט מסרתי את ביצוע העבודה הנדונה בהיתר לידי קבלן, ומתחייב למסור אותה לידי קבלן רשום בפנקס הקבלנים, כמחייב על פי כל דין, ולהודיע על כך לרשות הרישוי המקומית פרט התחלת ביצוע העבודות, ותחימתו של הקבלן תצורף להודעה המפרטת את פרטי רישומו של הקבלן.

מינוי האחראי לביצוע שלד הבניין: ☐ אני ממנה בזה את ___ בעל/ת מס׳ זהות ___ כתובת ___ טלפון ___ פקס ___ הרשום לעיל להיות אחראי לביצוע שלד הבניין.
☒ אני מצהיר, כי פרט מינוי אחראי/ת לביצוע עבודות הבנייה בתחומים האלה: כל התחומים ומתחייב לעשות זאת כמפורט בתקנות, ולהודיע על כך לרשות הרישוי המקומית פרט התחלת ביצוע העבודה.

מינוי אחראים לביקורת: ☐ אני ממנה בזה את הרשומים להלן להיות אחראים לביקורת על ביצוע עבודות בתחום הפעולה כרשום ליד שמם.

שם משפחה ושם פרטי	תחום פעולה	המען	מספר טלפון	מספר פקס
	אחראי ראשי			

☒ אני מצהיר כי פרט מינוי אחראי/ם לביקורת על ביצוע עבודות הבנייה את כולם או את קצתם בתחומים האלה: כל התחומים ומתחייב לעשות זאת כמפורט בתקנות, ולהודיע על כך לרשות הרישוי המקומית פרט התחלת ביצוע העבודה.

חתימת המבקש על המינויים X ___

יג. הצהרות

הצהרת עורכי הבקשה כולל הצהרת עורך הבקשה על לחץ המים: אנו החתומים מטה מצהירים בזה:
1) כל אחד מאתנו מאשר שהאמור בנוגע לרשימה שבסעיף יב לעיל הוא נכון.
2) כל אחד מאתנו מסכים לקבל עליו את התפקיד המיועד לו בסעיף יב לעיל.
3) אנו מצהירים, כל אחד בנוגע לתחום פעולתו, שיש לנו כישורים מקצועיים לערוך בקשה זו וכי בדקנו את המסמכים הנוגעים לבקשה, לרבות כל תכנית הנוגעת לבקשה, וידוע לנו כי אם הצהרה זו אינה נכונה, הרי היא תיחשב מסירת ידיעה שהיא כוזבת או מטעה בפרט חשוב, כמשמעותה בסעיף 214 לחוק, וצפויים לנו העונשים הקבועים לפי כל דין.
☒ אני אורנת זוהר (עורך בקשה ראשי) אחראי/ת לכך שהבקשה, ובכלל זה נספחיה, נערכה לפי מיטב הידיעה המקצועית ובהתאם לכל חיקוק החל על הבניין או העבודה המוצעת, שכל הנתונים שנמסרו על ידי בבקשה זו נכונים ושהתכנון המוצע תואם את כל התכניות, פרט לסטיות שפורטו לעיל.
☒ אני עורך הבקשה מתכנן האינסטלציה הסניטרית, מצהיר בזאת ואחראי לכך שתכניות הבקשה בכל הנוגע לסידורים הסניטריים נערכו כדין וכי קויימו בהן הוראות החוק וההוראות למתקני תברואה התש"ל 1970 (הל"ת) לענין זה, לרבות בדיקת לחץ המים הקיים בבנין ותיכנון בהתאם.

	תאריך	שם משפחה ושם פרטי	מספר רישיון	חתימה
עורך בקשה ראשי	2-06-2001	אורנת זוהר	23050	
עורך בקשה 1 מתכ׳ האינס׳ הסניט׳		מרקוביץ׳ מרינלה	10230	
עורך בקשה 2		סגל מיכאל	09036	
עורך בקשה 3		פינטר יוסי	47064	

הצהרת מתכנן שלד הבניין: אני החתום מטה (שם משפחה ושם פרטי) סגל מיכאל מס׳ זהות 6903184 מהנדס רשוי מס׳ 09036 /הנדסאי בעל רישיון מס׳ ___ (ל"מבנה פשוט") מצהיר בזאת כדלקמן:
1) אני מסכים להיות מתכנן שלד הבניין הנדון בבקשה ולפקח פיקוח עליון על הקמת השלד.
2) אני מתחייב להגיש לפני מתן ההיתר, נושא הבקשה את החישובים הסטטיים בדבר הבנייה בעבודות ההיתר.
3) ידוע לי, שאם אחרי הגשת הנתונים הסטטיים יתגלה צורך בשינוי מהותי בהם, אני מתחייב להגיש חישובים סטטיים מתוקנים מיד עם גילוי הצורך בכך.
4) אני מצהיר, כי יש לי כישורים מקצועיים לערוך בקשה זו וכי בדקתי את כל המסמכים הנוגעים לבקשה, לרבות כל תכנית הנוגעת לבקשה, וידוע לי כי אם הצהרה זו אינה נכונה, הרי היא תיחשב מסירת ידיעה שהיא כוזבת או מטעה בפרט חשוב, כמשמעותה בסעיף 214 לחוק, וצפויים לי העונשים הקבועים לפי כל דין.
5) ידוע לי כי עלי לשמור את תכניות הקונסטרוקציה לתקופה של לא פחות מ-10 שנים לאחר גמר הבנייה.
תאריך 30-05-2001 חתימה ___

הצהרת האחראי לביצוע שלד הבניין (כאשר מונה): אני החתום מטה (שם משפחה ושם פרטי) ___ מס׳ זהות ___ מהנדס רשוי מס׳ ___/הנדסאי בעל רישיון מס׳ ___ (ל"מבנה פשוט") מצהיר בזאת כדלקמן:
1) אני מסכים להיות האחראי לביצוע שלד הבניין.
2) אני מצהיר, כי יש לי כישורים מקצועיים להיות אחראי לביצוע שלד הבניין, ואני מתחייב לדאוג לביצוע שלד הבניין על פי תוכניות והוראות של מתכנן השלד כפי שיינתנו בכתב וכן למלא את תפקידי על פי שנקבע בכל חיקוק הנוגע להן.
תאריך ___ חתימה ___

הצהרת אחראים לביקורת (כאשר מונו): אנו החתומים מטה מצהירים בזה:
1) כל אחד מאיתנו מאשר שהאמור בנוגע לו ברשימה שבסעיף יב לעיל הוא נכון.
2) כל אחד מאיתנו מסכים לקבל עליו את התפקיד המיועד לו בסעיף יב.
3) אנו מצהירים כל אחד בנוגע לתחום פעולתו, שיש לנו כישורים מקצועיים לערוך את הביקורת כהלכה ולדווח על תוצאותיה לרשות הרישוי המקומית, כמתחייב על פי כל דין.
אני ___ (עורך הביקורת הראשי) אחראי/ת לכך שהביקורת תיערך על פי מיטב הידיעה המקצועית, ושכל הדיווחים לרשות הרישוי המקומית ייערכו על פי כל דין.

תאריך	שם משפחה ושם פרטי	מספר רישיון	חתימה

תל-אביב-יפו מפה טופוגרפית

מס׳ סדורי 2073 / 2000
ק.מ. 1 : 250

שכונת התקווה
גוש : 6135
חלקה 110 (חלק)
רח׳ תשבי 27

הוכן עבור: סושניק גוליין
מהות הבקשה: התר בניה

שטח לפי נסח טאבו: 112 מ״ר
שטח מדוד: 76 מ״ר

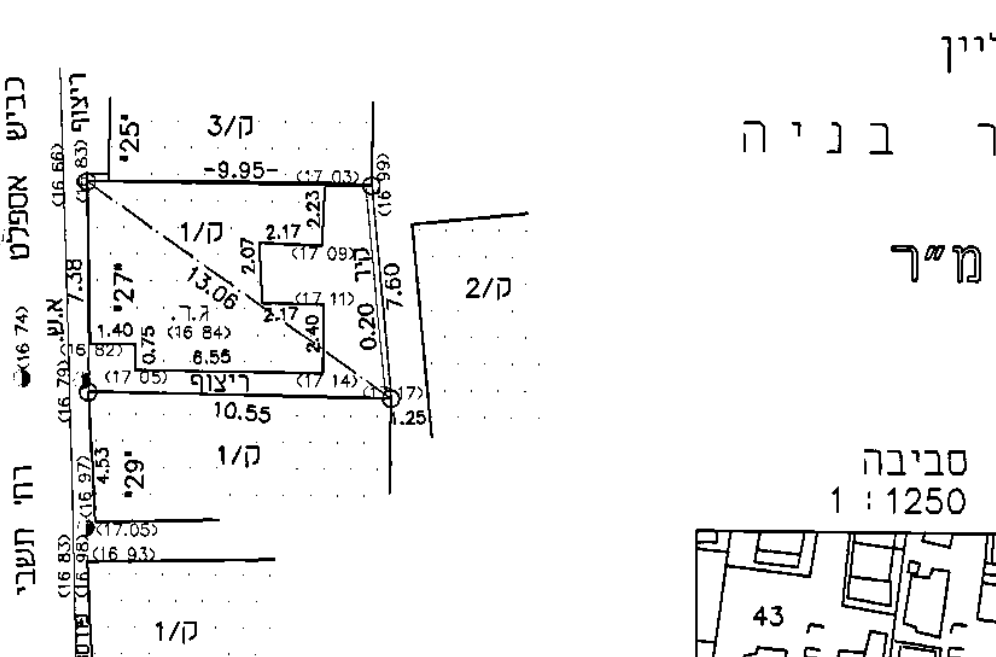

תרשים סביבה
קנה מדה 1 : 1250

43
רחוב
4046
4047
4048
4049
27
דרך לוד "3843"
גוש 6136

לא לצרכי רישום

הנני מצהיר בזה שהמפה נעשתה לפי חוק התכנון והבניה, התקנות וההנחיות של עיריית תל אביב יפו

תל - אביב 8.11.2000 מודד מוסמך
ראובן לאופר - מודד מוסמך מס׳ רשיון 574
משרד טכני למדידות
משרד: רח׳ חרכבת 20 תל - אביב טל׳: 03 - 5608221
מען: רח׳ בורלא 32 תל - אביב טל׳: 03 - 6993398

הערות:
1. הגבהים מבוססים על נ.ק. 187 של רשת האיזון העירונית שגובהה 17.549 מ׳.
2. הגבהים נרשמו בסוגריים.
3. ייתכנו שינויים בשטחים ובמידות בעת עריכת תכניות לצרכי רישום והסדר הקרקע אצל רשם המקרקעין.

מפת איתור העבודה (תרשים מגרש)

תל-אביב-יפו מפה טופוגרפית

מס׳ סדורי 2073 / 2000
ק.מ. 1 : 250

שכונת התקווה
גוש : 6135
חלקה 110 (חלק)
רח׳ תשבי 27

הוכן עבור: סושניק גוליין
מהות הבקשה: התר בניה

שטח לפי נסח טאבו: 112 מ״ר
שטח מדוד: 76 מ״ר

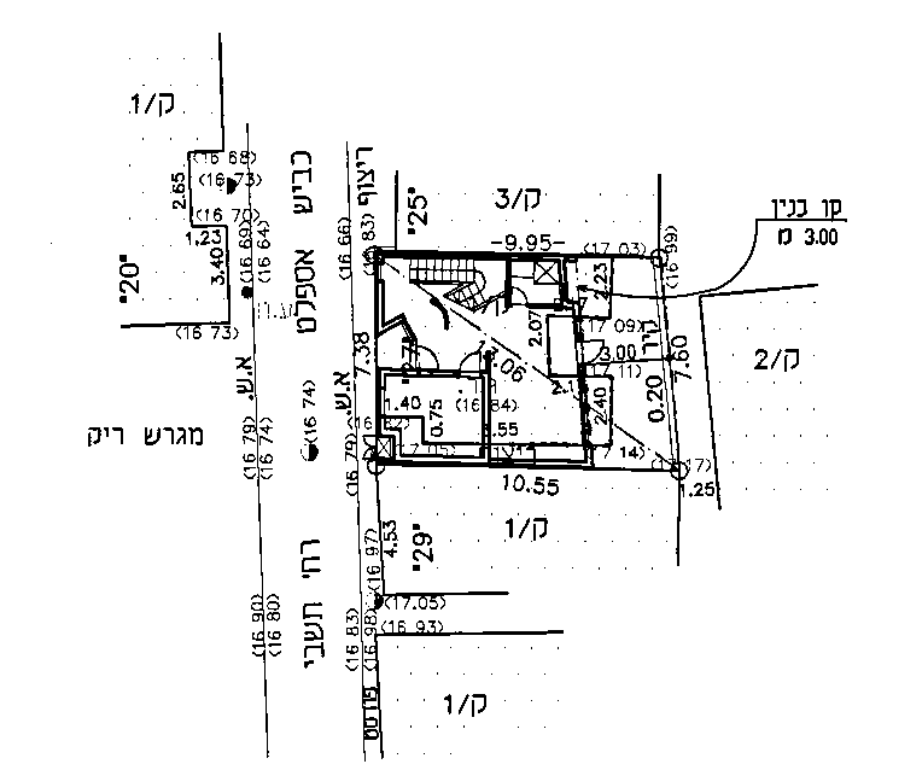

תרשים סביבה
קנה מדה 1 : 1250

43
4046
4047
4048
דרך לוד "3843"
גוש 6136

לא לצרכי רישום

הנני מצהיר בזה שהמפה נעשתה לפי חוק התכנון והבניה, התקנות וההנחיות של עיריית תל אביב יפו

תל - אביב 8.11.2000 מודד מוסמך
ראובן לאופר - מודד מוסמך מס׳ רשיון 574
משרד טכני למדידות
משרד: רח׳ חרכבת 20 תל - אביב טל׳: 03 - 5608221
מען: רח׳ בורלא 32 תל - אביב טל׳: 03 - 6993398

הערות:
1. הגבהים מבוססים על נ.ק. 187 של רשת האיזון העירונית שגובהה 17.549 מ׳.
2. הגבהים נרשמו בסוגריים.
3. ייתכנו שינויים בשטחים ובמידות בעת עריכת תכניות לצרכי רישום והסדר הקרקע אצל רשם המקרקעין.

תכנית העמדה

תשריט סכימטי של שטחי הבניה

ק.מ. 1:100

חישוב שטח קומת קרקע

1. חישוב שטח מסגרת
7.38 × 7.54 =55.65

2. הורדות
① (7.38 × 0.60) : 2 = 2.21
② 1.78 × 0.40 = 0.71
③ (1.12×1.94):2 - (0.60×1.04):2 = 0.78
סה״כ 3.70 מ״ר

3. חישוב שטח שירות 7.5 מ״ר
סה״כ שטח שירות : 7.5 מ״ר

4. חישוב שטח עיקרי - קומת קרקע
55.65 - 3.70 - 7.5 = 44.45 מ״ר

חישוב שטח קומה א׳

1. חישוב שטח מסגרת
7.38 × 7.54 =55.65

2. הורדות
① (7.38 × 0.60) : 2 = 2.21
④ (5.61×3.18) : 2 = 8.92
⑤ 1.15 × 3.60 = 4.14
⑥ (2.24×0.60):2×2 = 1.34
סה״כ 16.61 מ״ר

4. חישוב שטח עיקרי - קומה א׳
55.65 - 16.61 = 39.04 מ״ר

חישוב שטח קומה ב׳

1. חישוב שטח מסגרת
7.38 × 7.54 =55.65

2. הורדות
① (7.38 × 0.60) : 2 = 2.21
④ (5.61×3.18):2 = 8.92
⑤ 1.15 × 3.60 = 4.14
⑦ (0.60×0.35):2 = 0.10
⑧ (1.30×0.70):2 = 0.45
⑨ (3.00×1.30):2 = 1.95
⑩ 3.44 × 1.81 = 6.22
⑪ (1.77×2.93):2 = 2.59
⑫ 0.39 × 2.27 = 0.89
⑬ (1.42 × 2.45):2 = 1.74
⑭ (0.39 × 0.18):2 = 0.04
סה״כ 29.25 מ״ר

4. חישוב שטח עיקרי - קומה ב׳
55.65 - 29.25 = 26.40 מ״ר

סה״כ שטח עיקרי

44.45 + 39.04 + 26.40 = 109.89

סה״כ שטח (עיקרי+שרות)

109.89 + 7.5 = 117.39

שטחים לא מקוריים קומת א׳ :
④+⑤-②-③ = 8.92+4.14-0.71-0.78 = 11.57

שטחים לא מקוריים קומת ב׳ :
⑦+⑧+⑨ = 0.10+0.45+1.95 = 2.40

סה״כ שטחים לא מקוריים (מרפסות) :
= 13.97

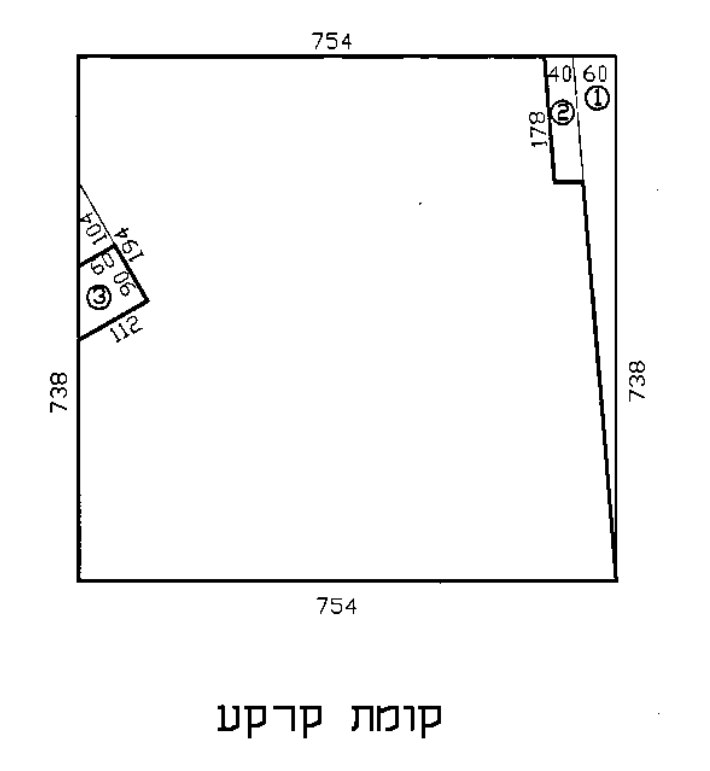

קומת קרקע

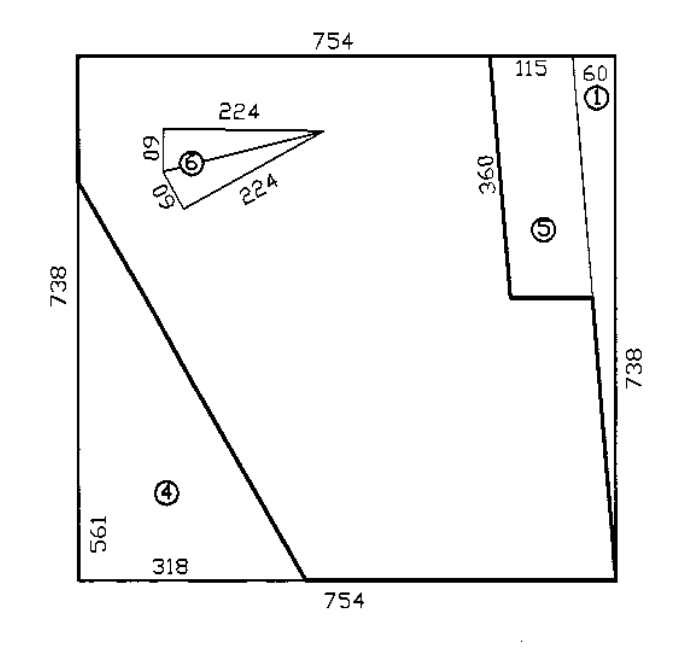

קומת א׳

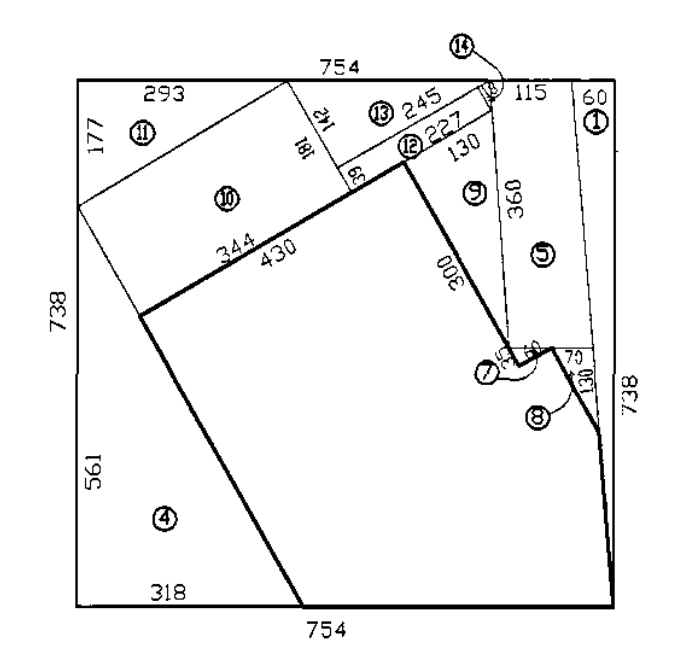

קומת ב׳

חישוב תכסית:

סה״כ שטח קומת קרקע:
55.65 - 3.70 = 51.95 מ״ר

סה״כ שטח מגרש: 76 מ״ר

תכסית: 51.95 : 76 = 0.68 %

חישוב זכוית בניה

לפי ת.ב.ע. מס׳ 2215

שטח המגרש לפי נסח טאבו :	112 מ״ר
שטח המגרש לפי מדידה עלידי מודד מוסמך:	76 מ״ר
% הבניה המותרים לפי ת.ב.ע.:	140.0 %
תוספת % בניה עבור הריסת בית קיים :	7.5 %
שטח שרות עבור בנית ממ״ד :	7.5 מ״ר

חישוב סה״כ שטח בניה מותר :

76.0 × 1.4 = 106.4 מ״ר
76.0 × 0.075 = 5.7 מ״ר

סה״כ שטח עיקרי מותר : 112.1 מ״ר
(ממ״ד) 7.5 מ״ר = 7.5 מ״ר

סה״כ זכויות בניה מותרים :
(עיקרי + שירות) 119.6 מ״ר

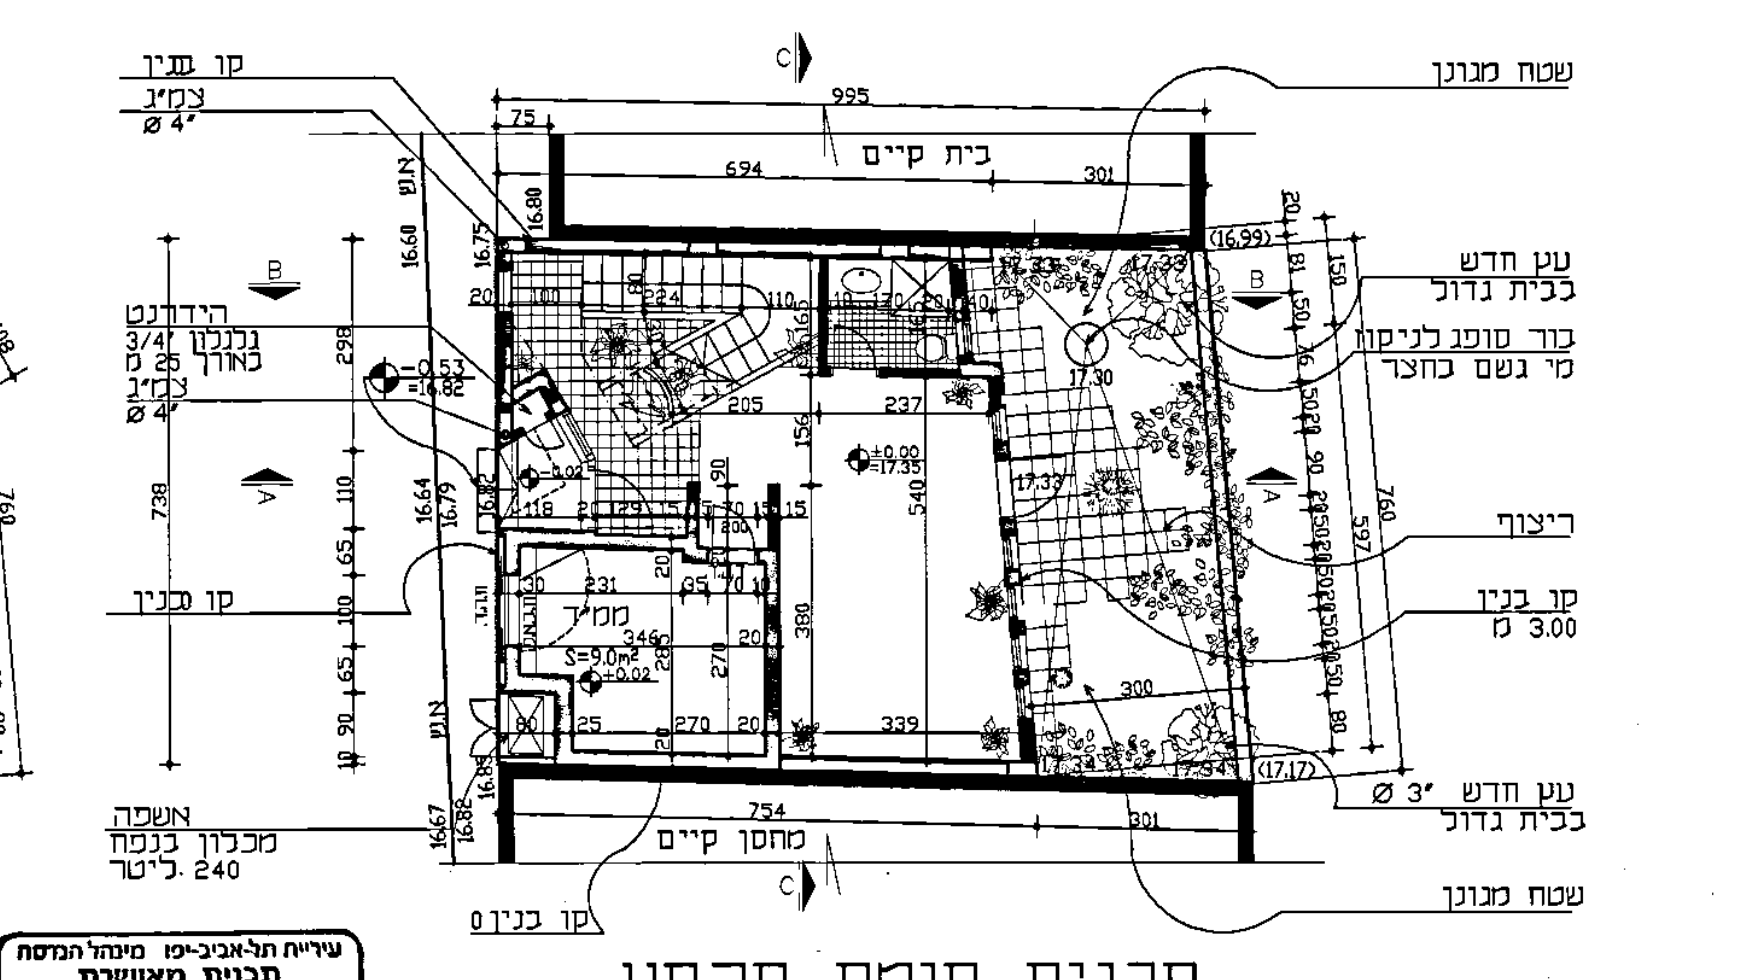

תכנית קומת קרקע
ותכנית פיתוח שטח
מפלס ±0.00

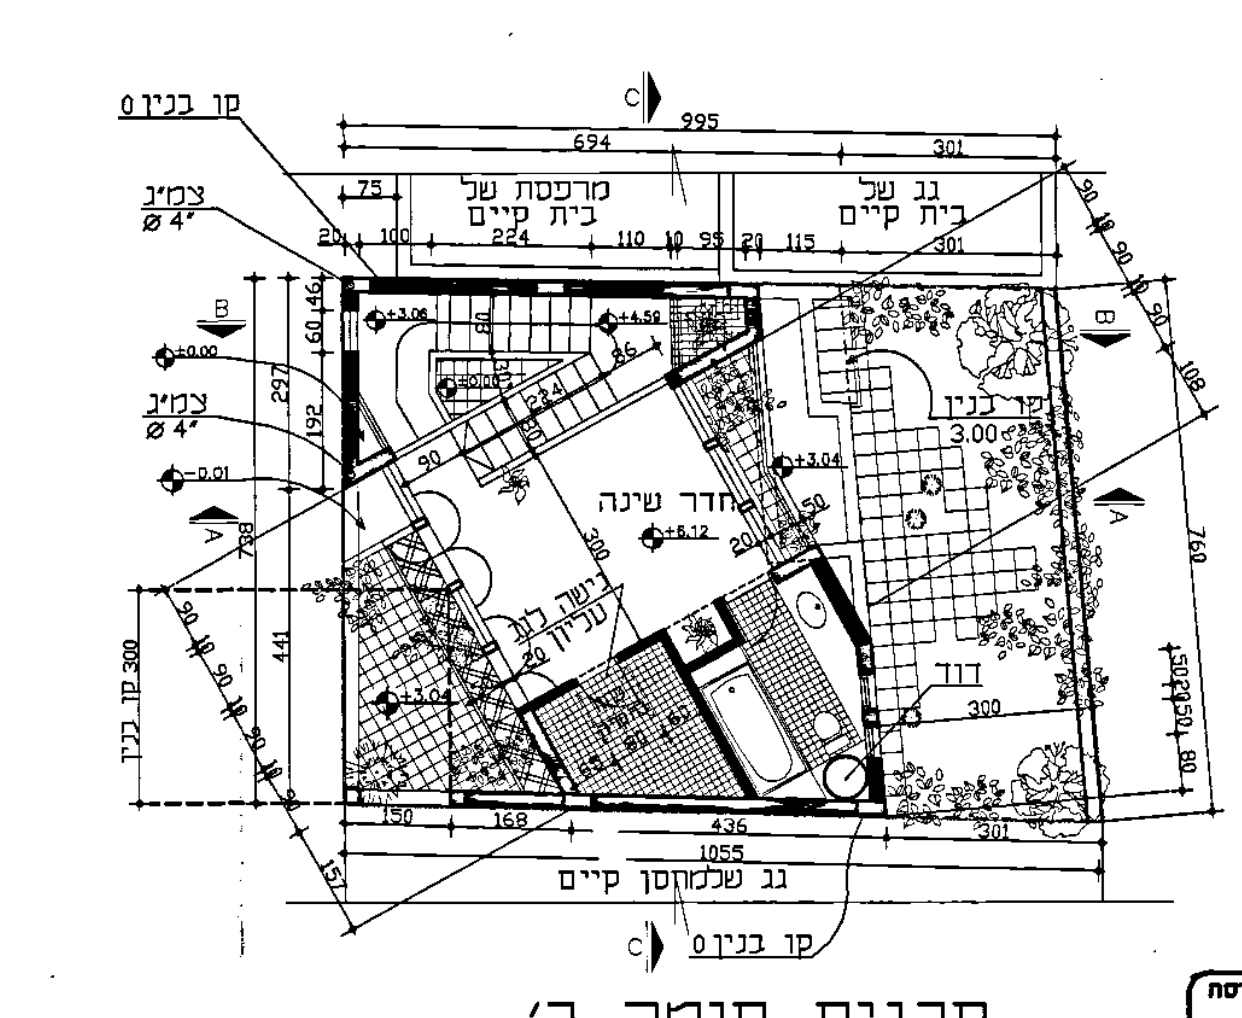

תכנית קומה ב׳
+6.12 מפלס

עיריית תל-אביב-יפו מינהל ההנדסה
תכנית מאושרת
לסידורי אצירה ופינוי אשפה
12-02-2002
הוראות ביצוע בהתאם לקובץ
התחנויות-פרק 12 "אצירת אשפה"
לפני איכלוס המבנה
לתאם סופית עם אגף התברואה
את המתקנים לאצירת אשפה

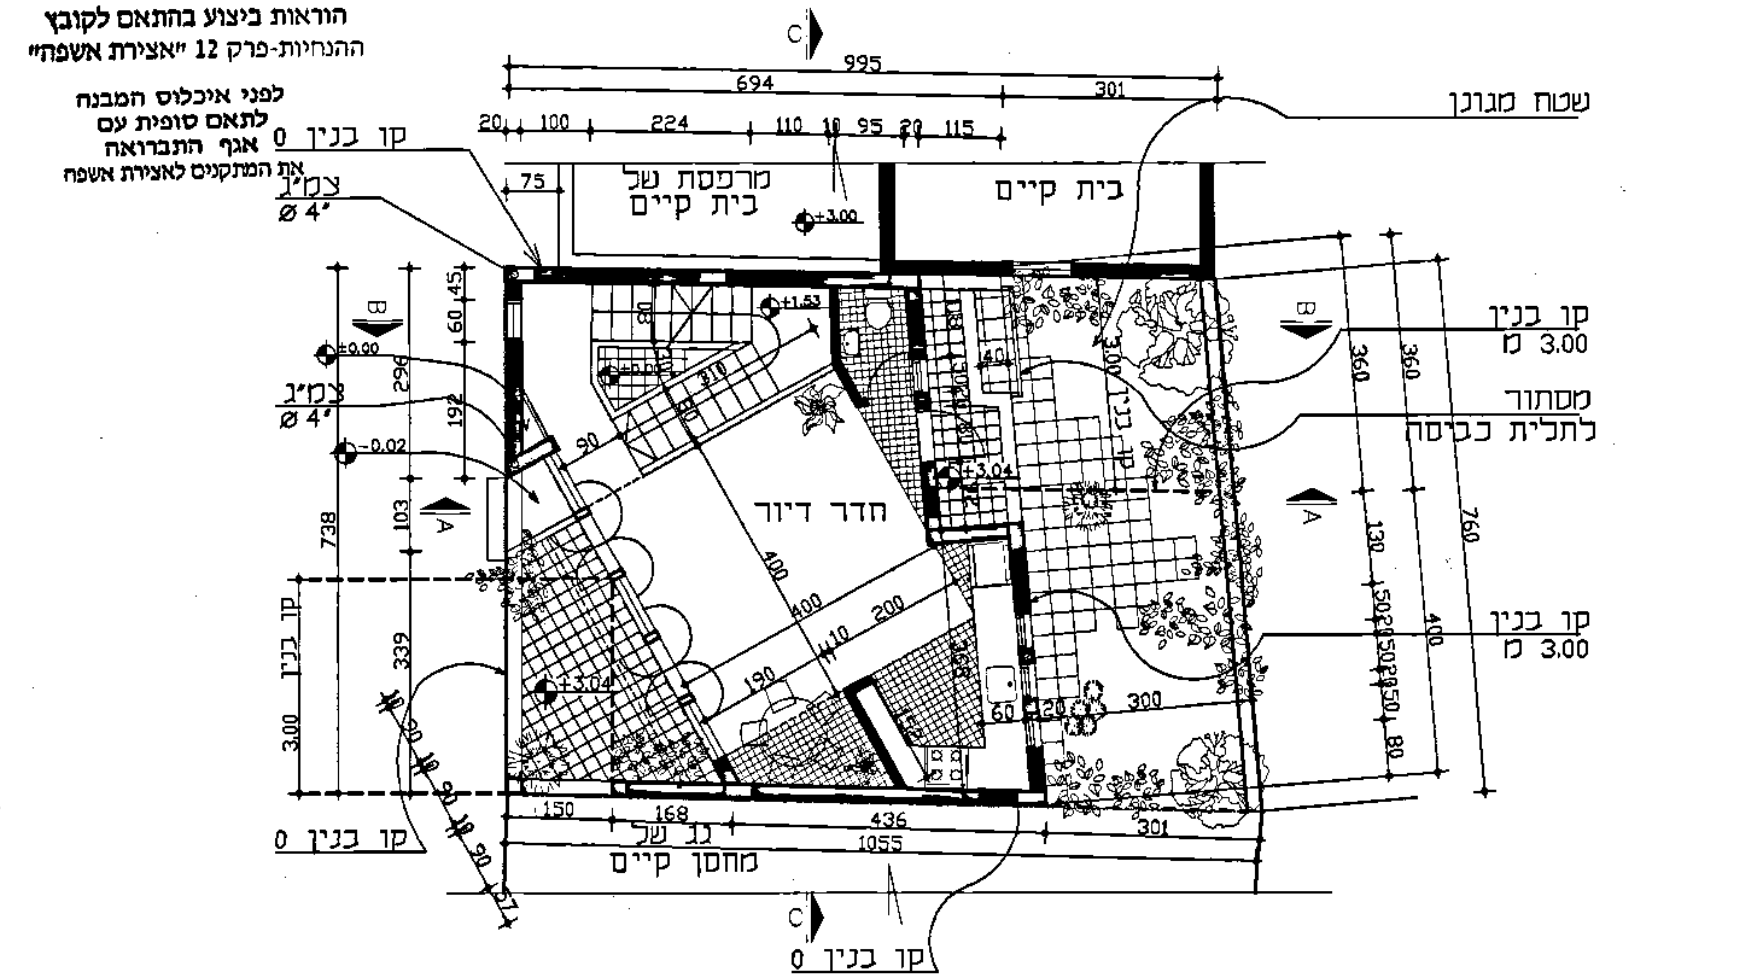

תכנית קומה א׳
+3.06 מפלס

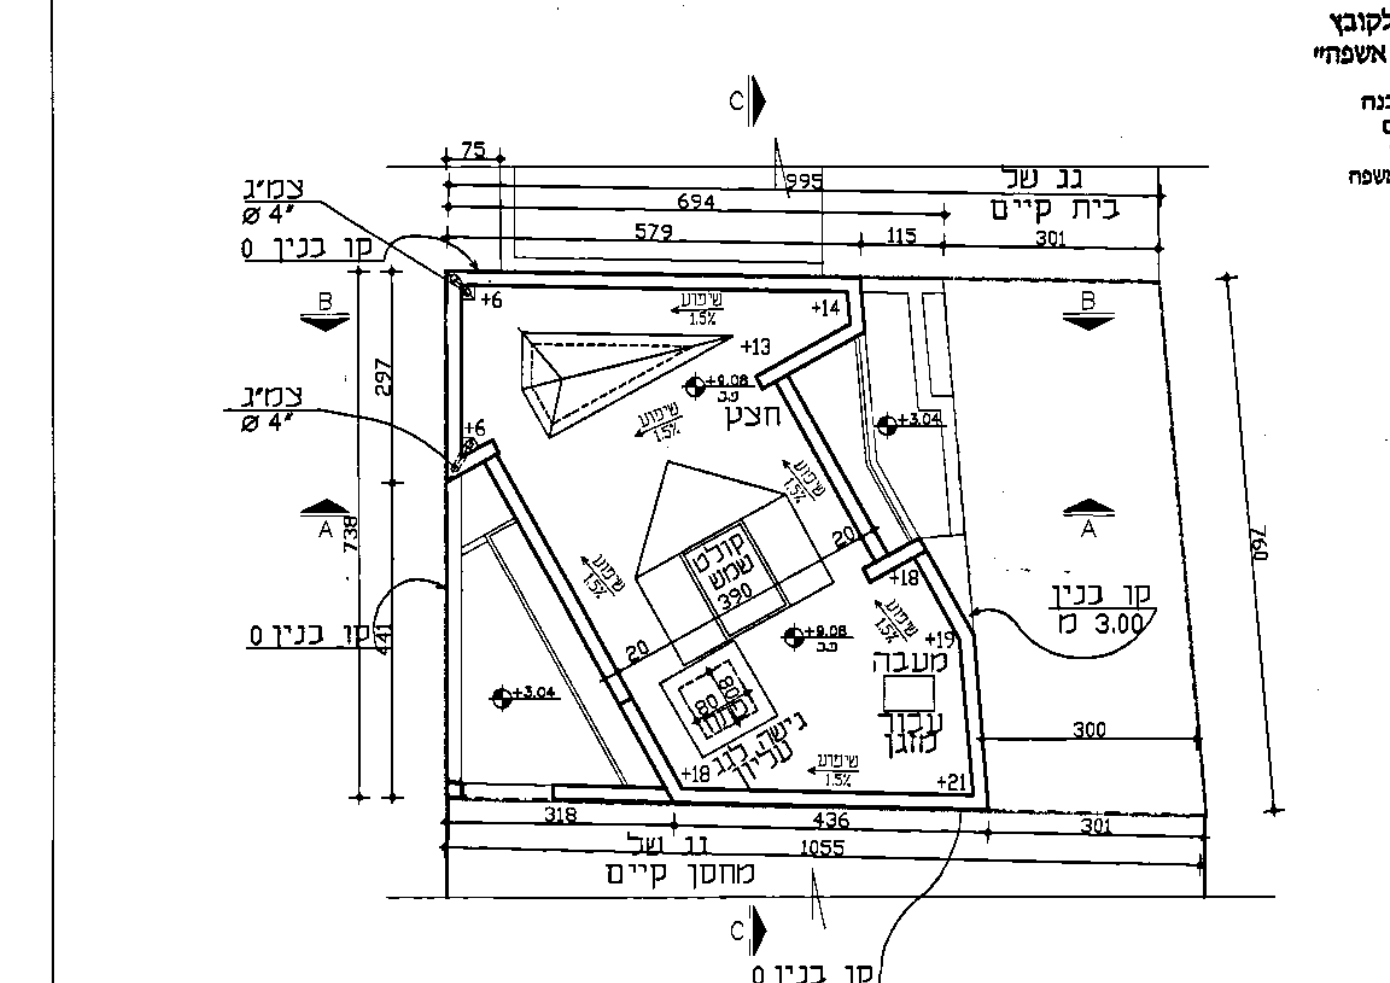

תכנית גג

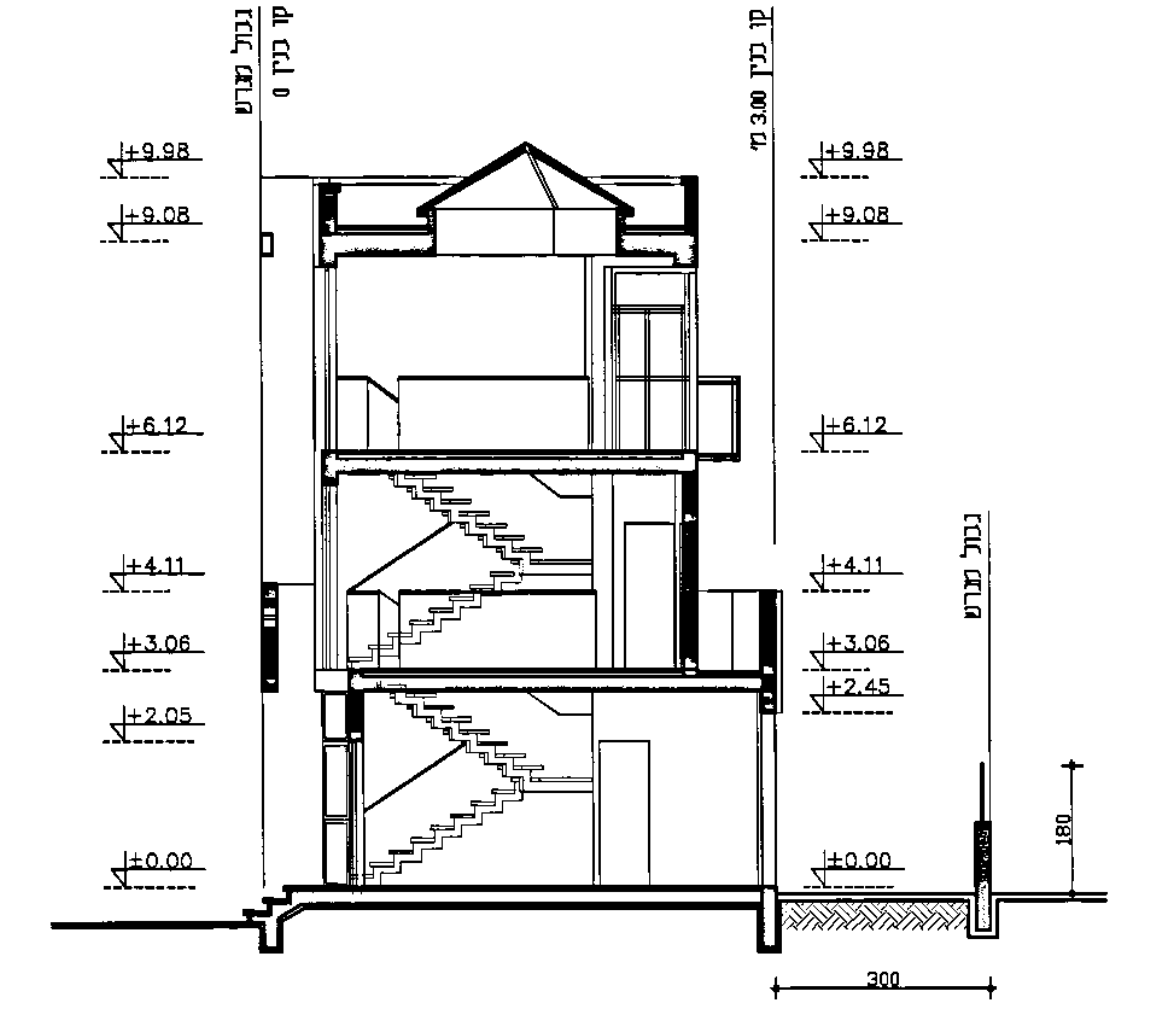

חתך A-A

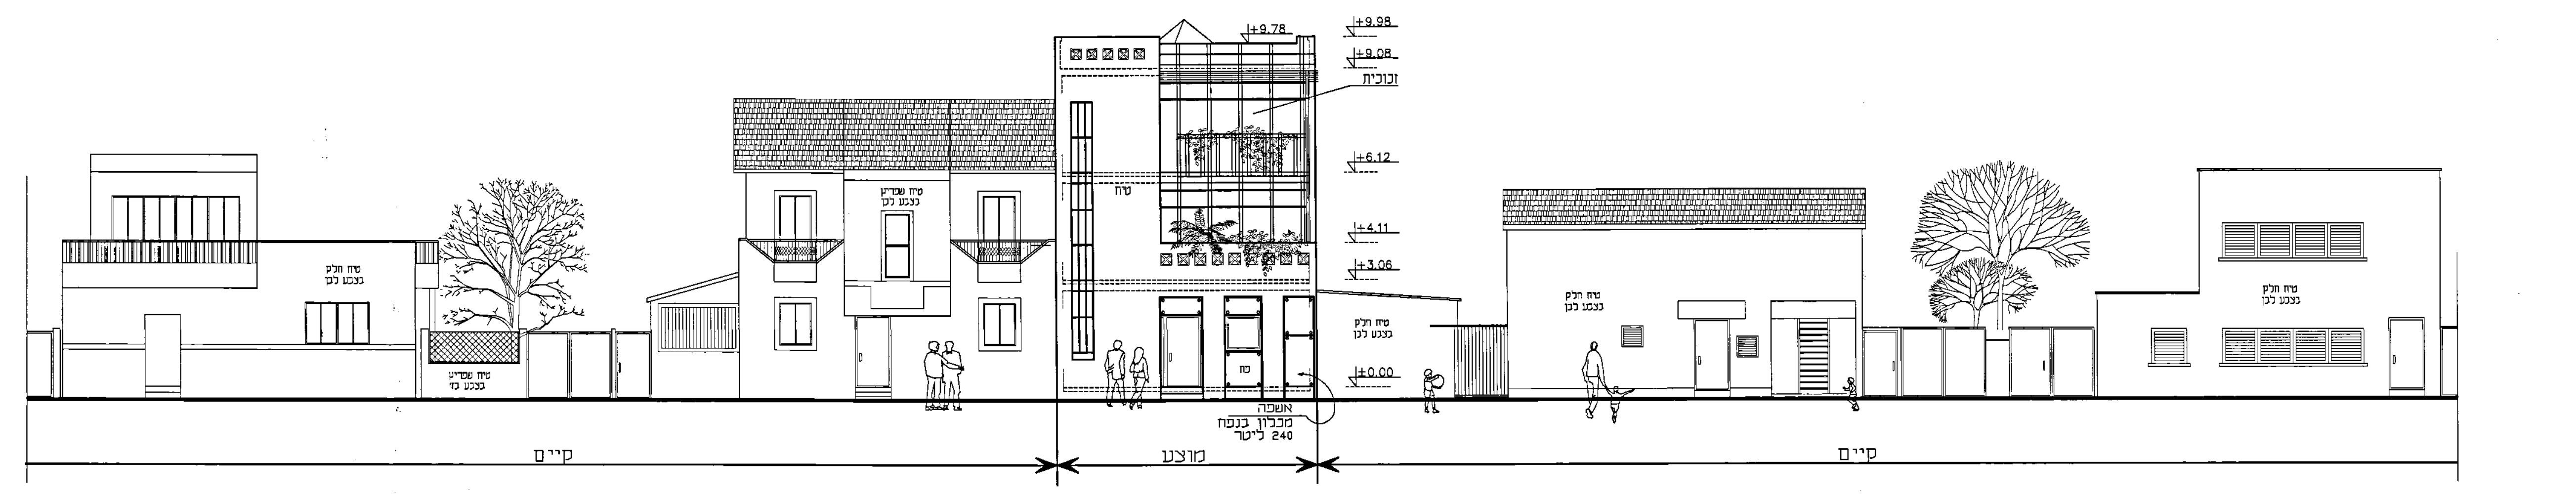

חזית מערבית

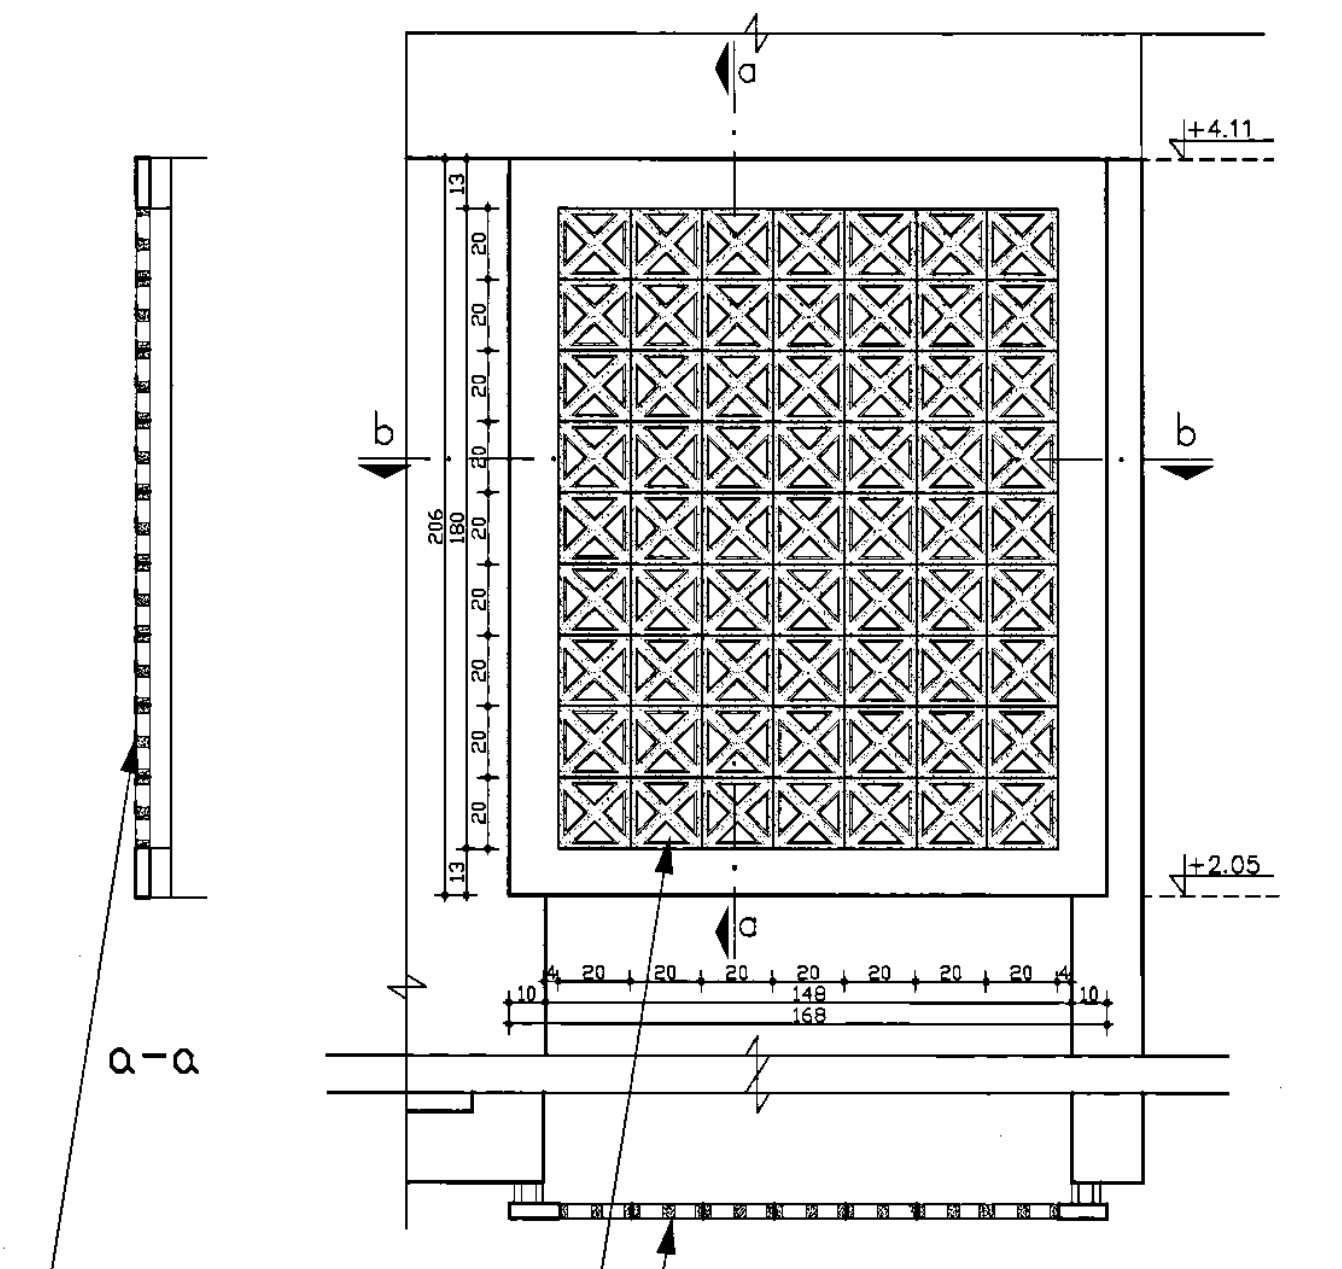

מסתור כביסה
ק.מ. 1:20

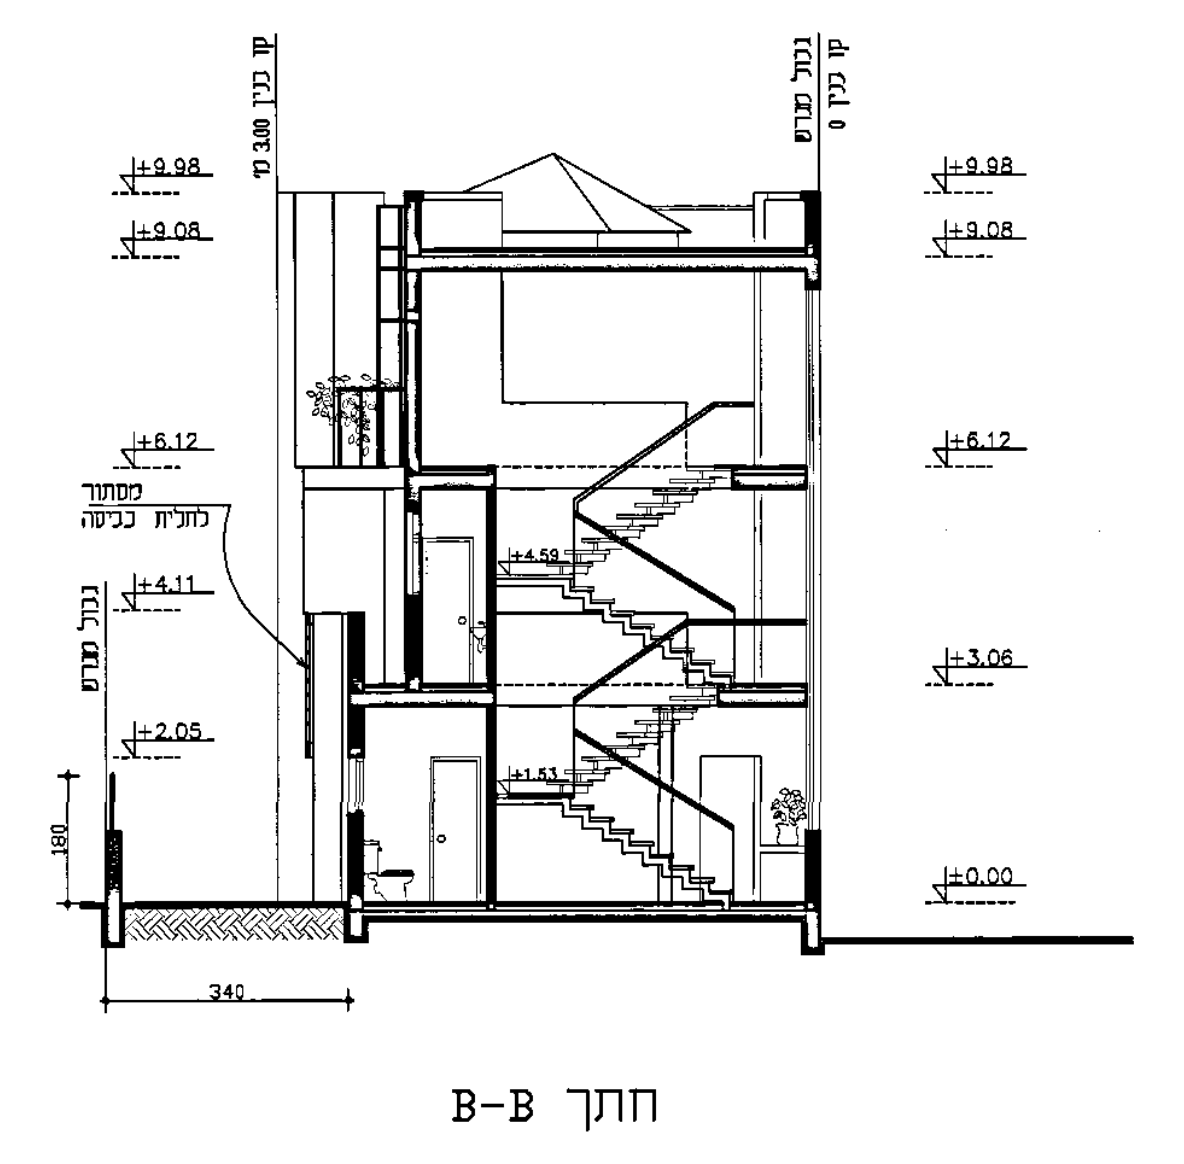

חתך B-B

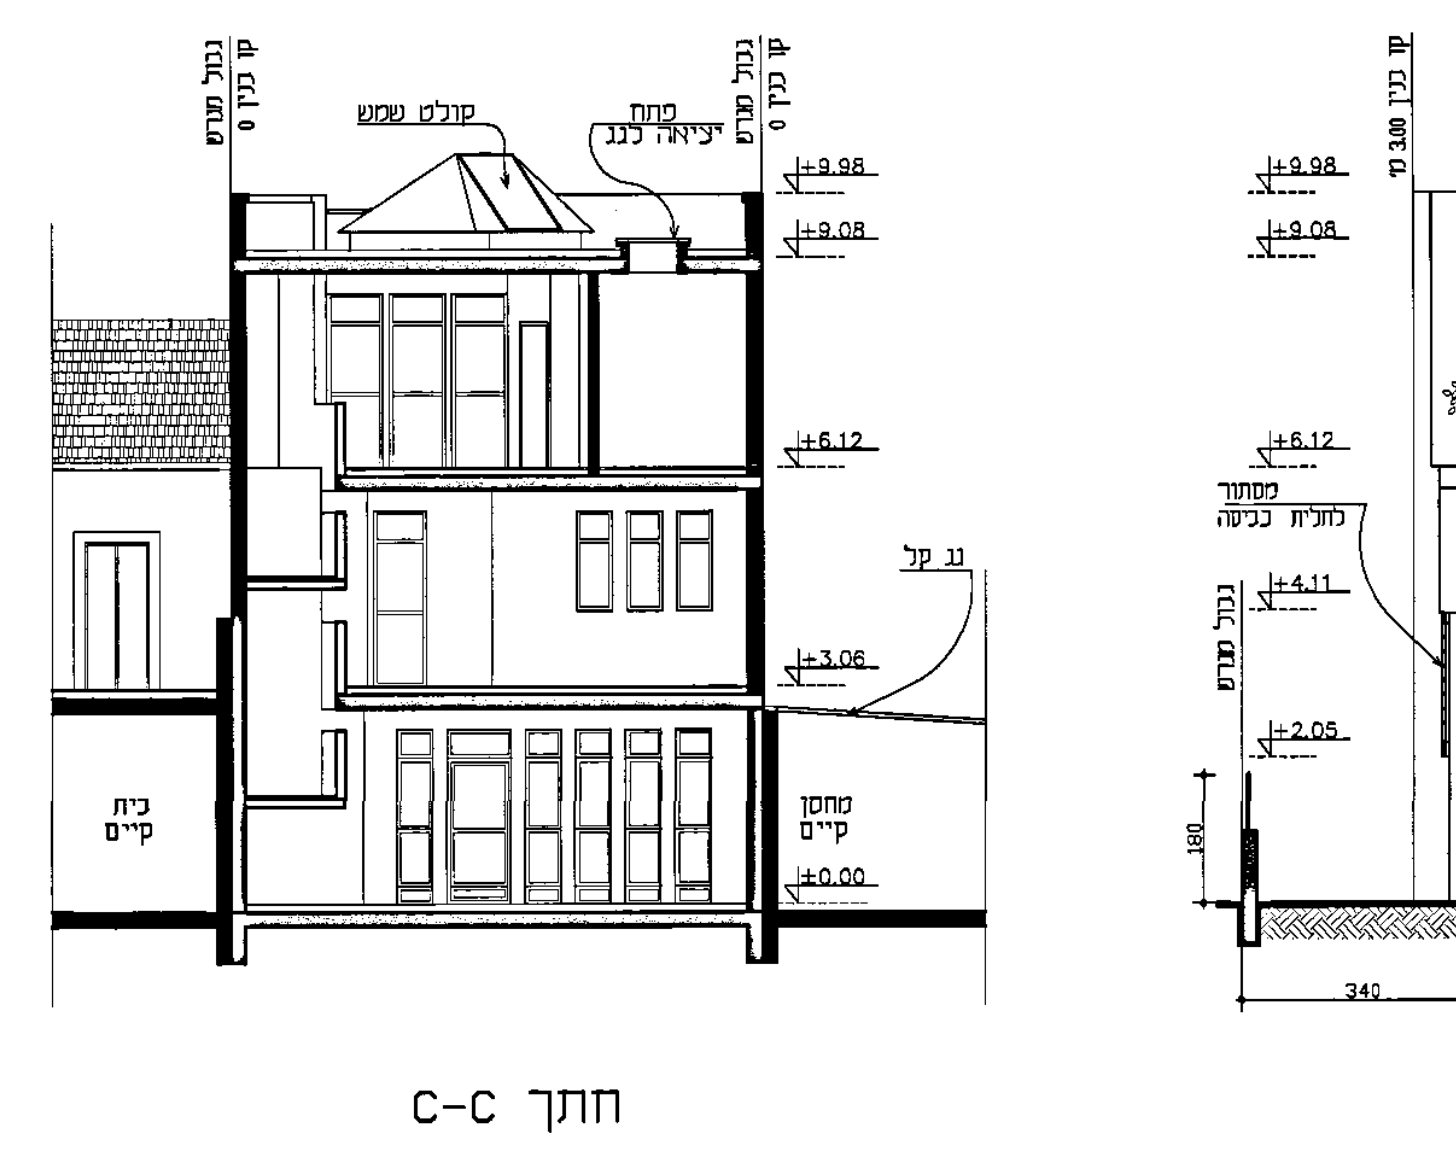

חתך C-C

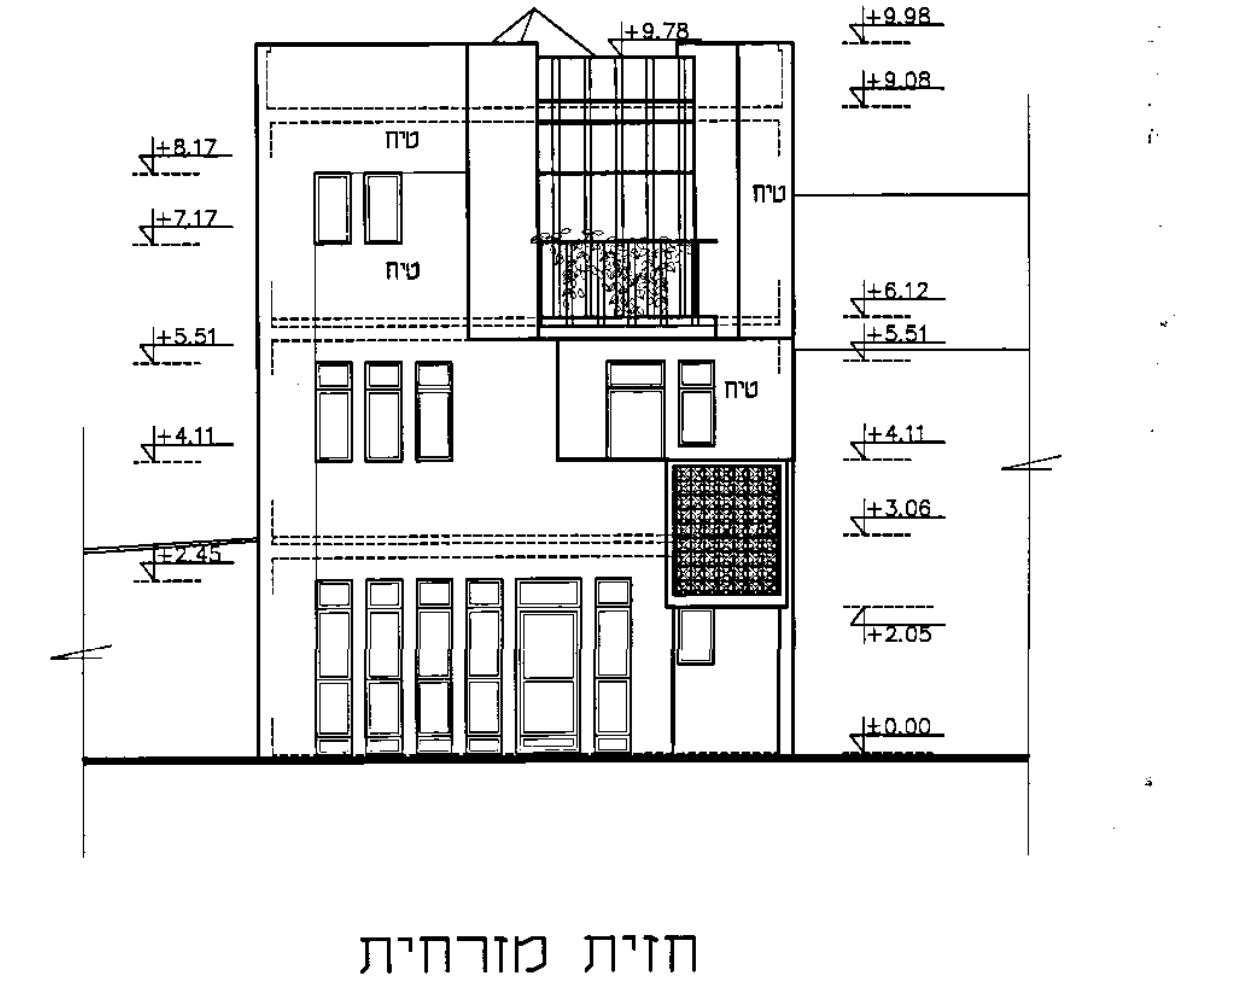

חזית מזרחית

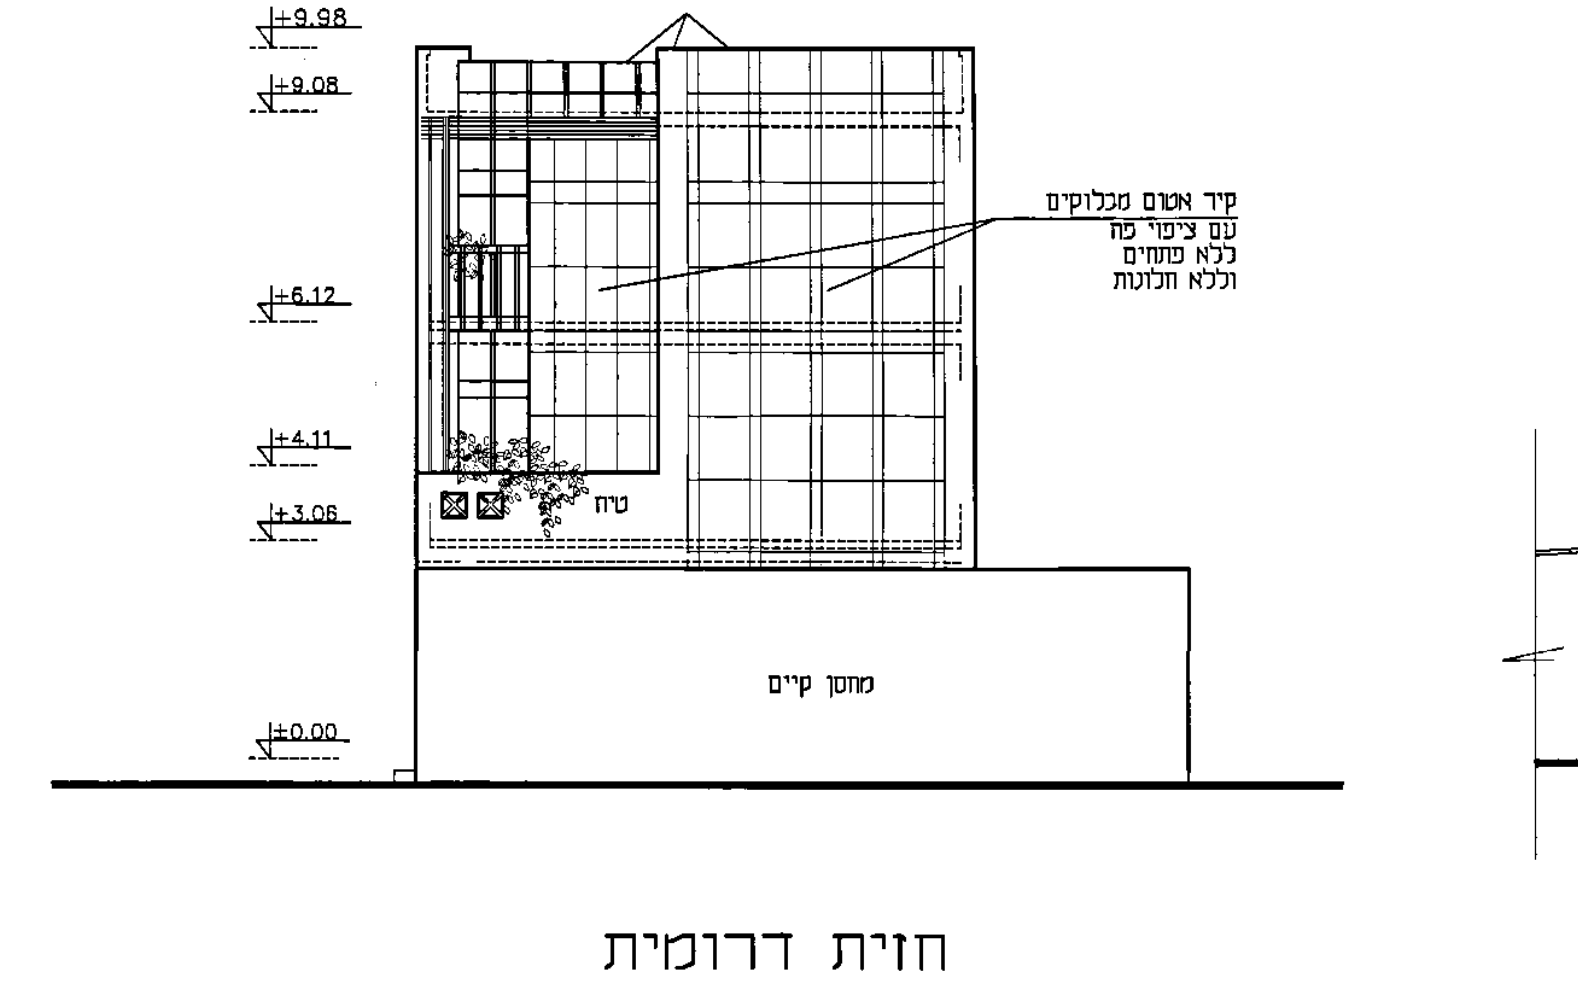

חזית דרומית

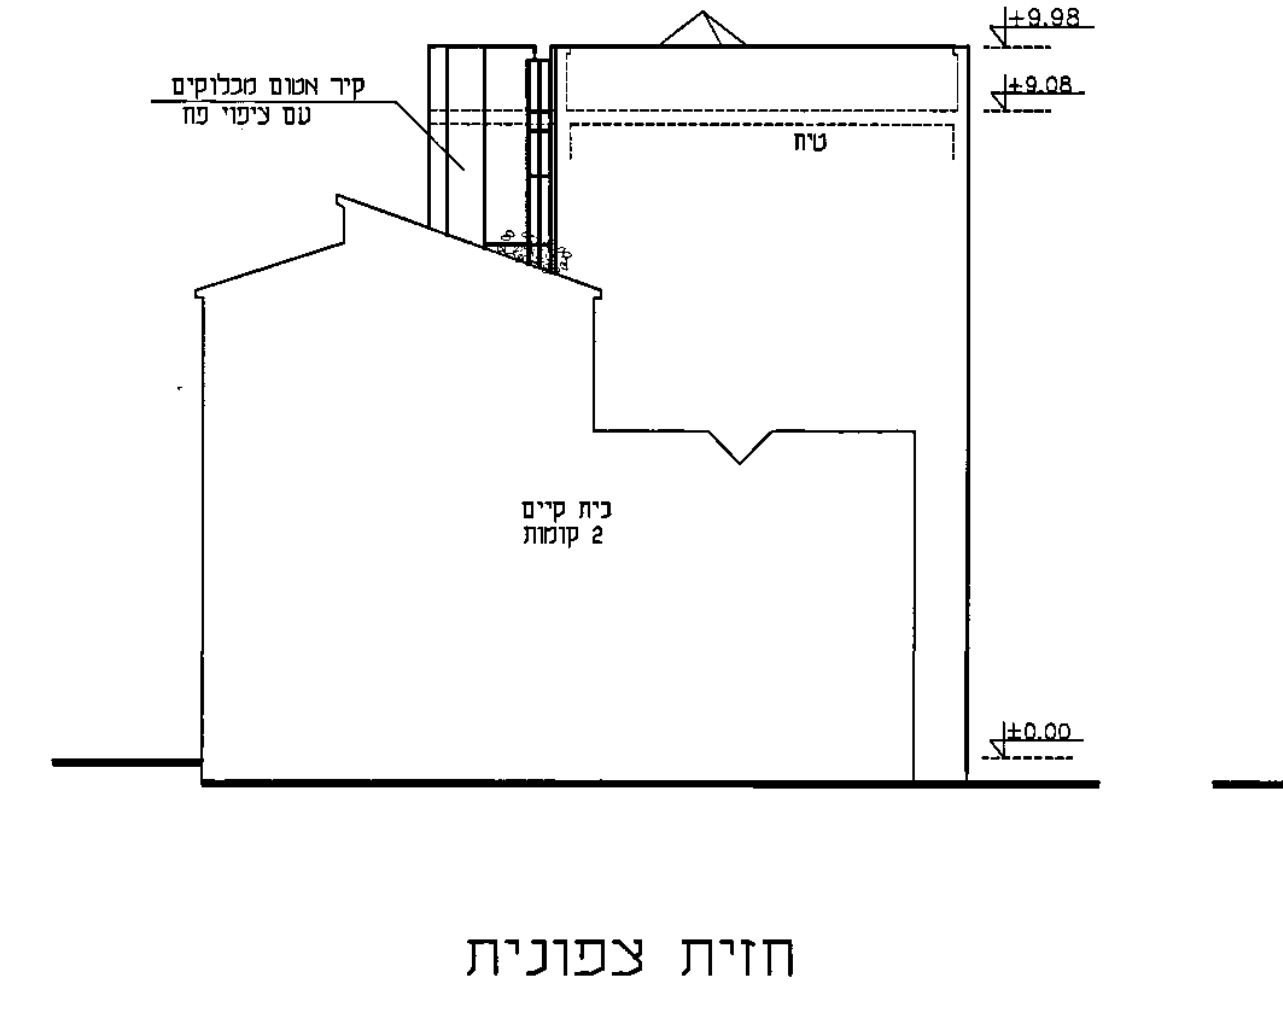

חזית צפונית

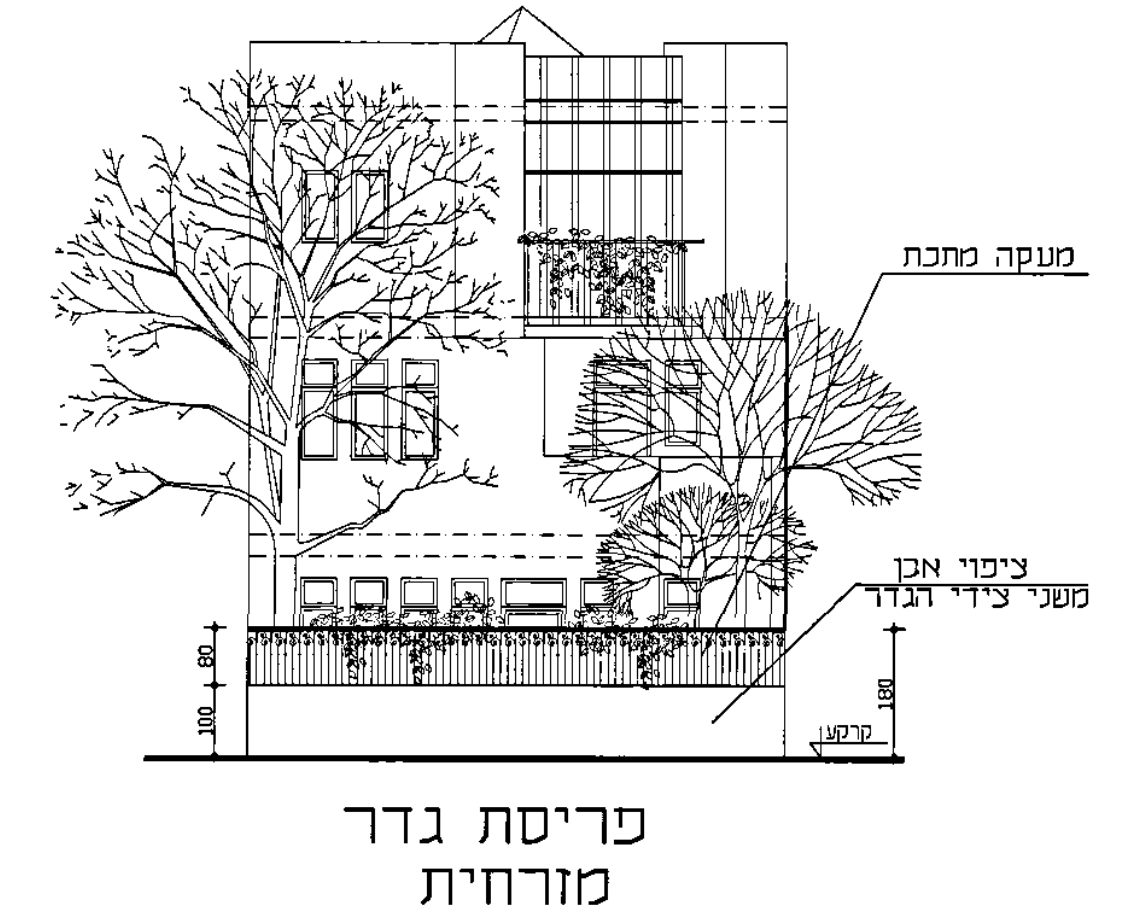

פריסת גדר
מזרחית
ק.מ. 1:100