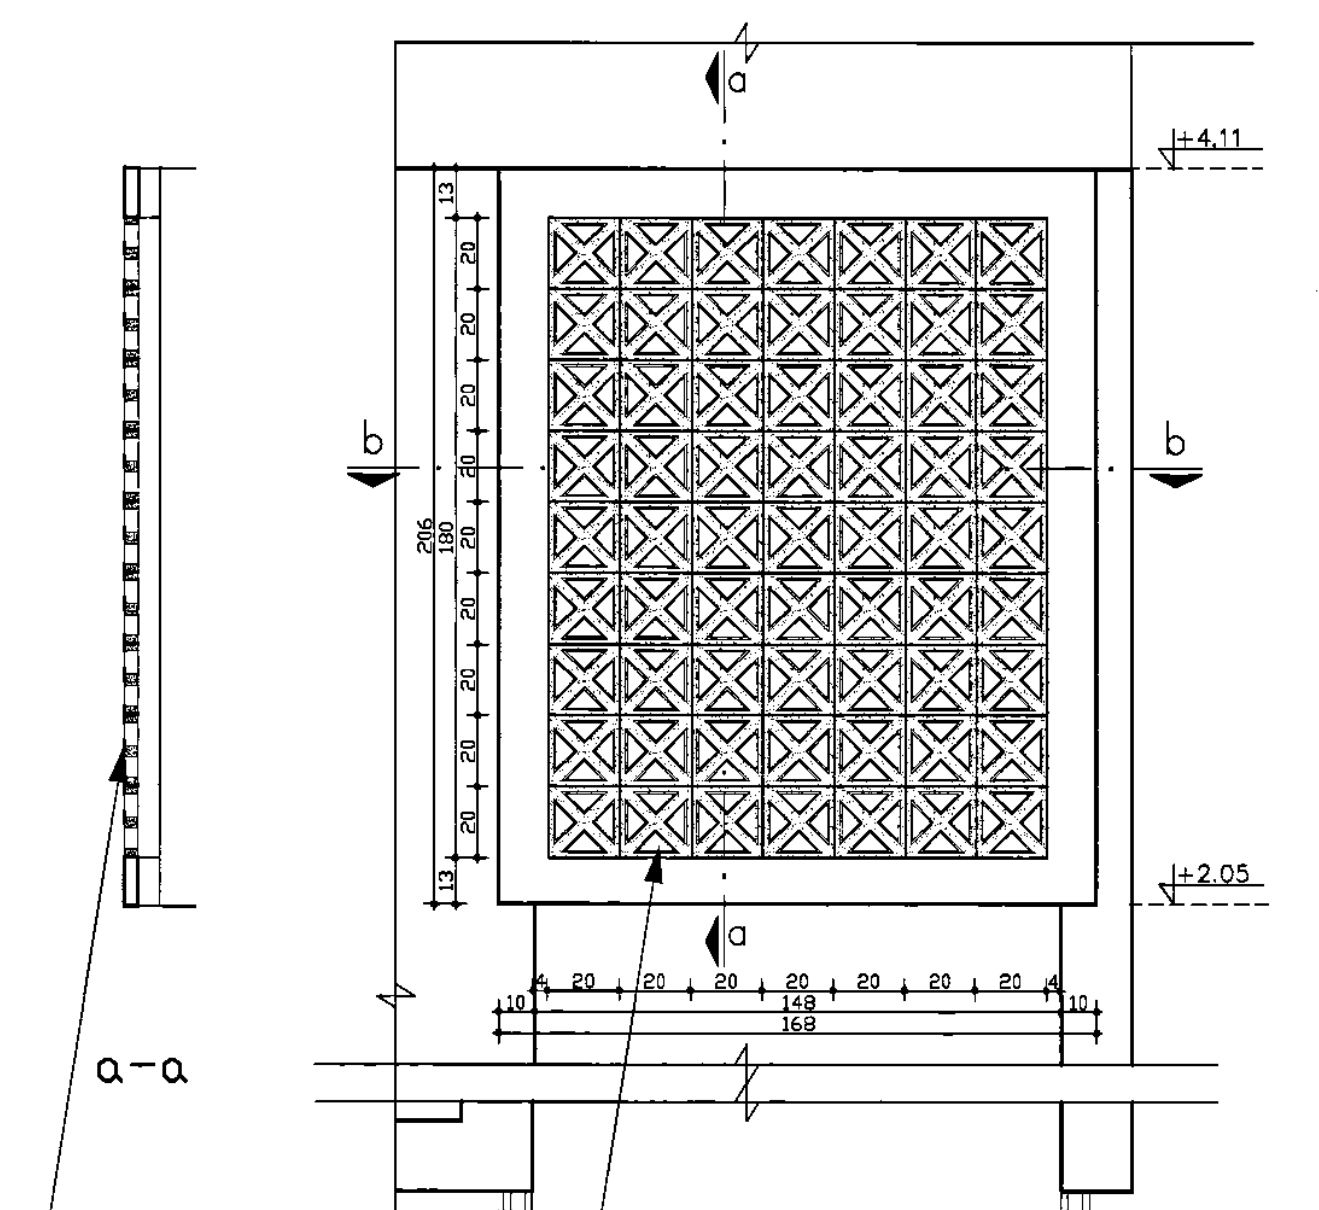
a-a
b-b
+4.11
+2.05
20x20 GRC מסתורי כביסה
של אקרשטיין או גל תעשיות או ש"ע

מסתור כביסה
ק.מ. 1:20

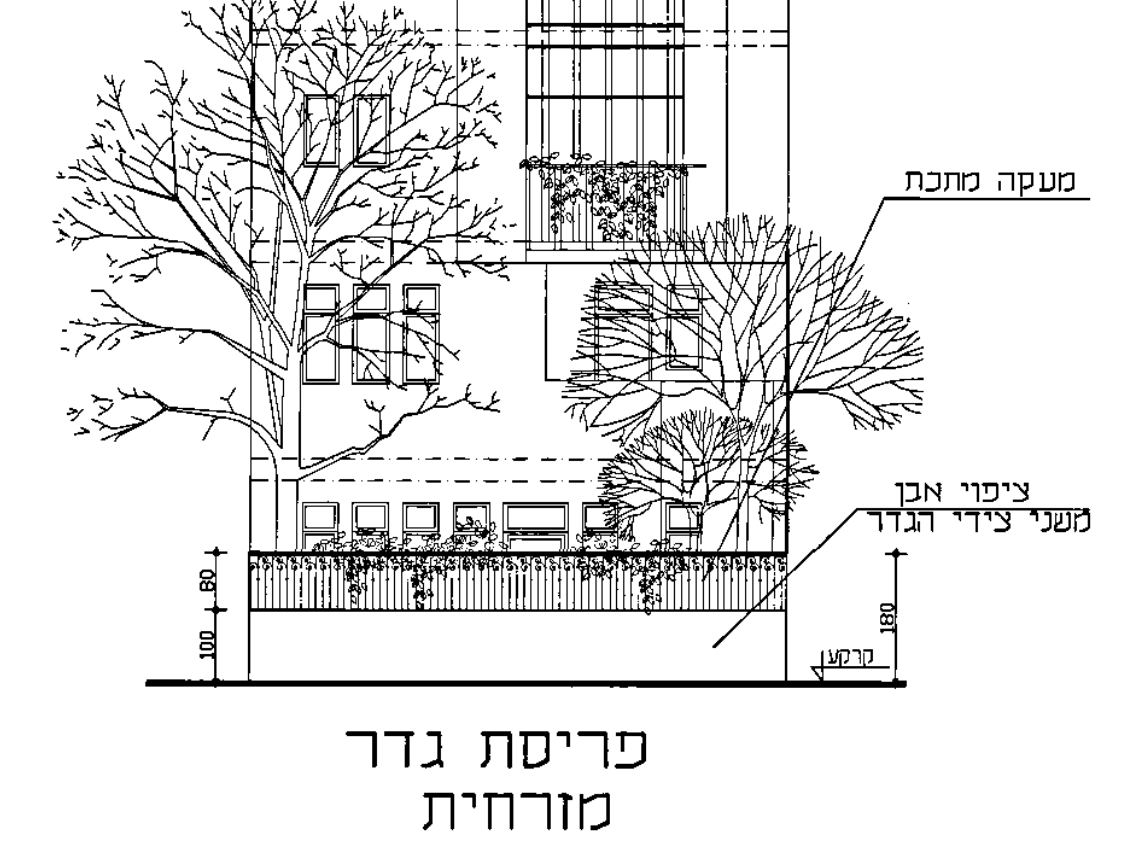
מעקה מתכת
ציפוי אבן
משני צידי הגדר

פריסת גדר
מזרחית
ק.מ. 1:100

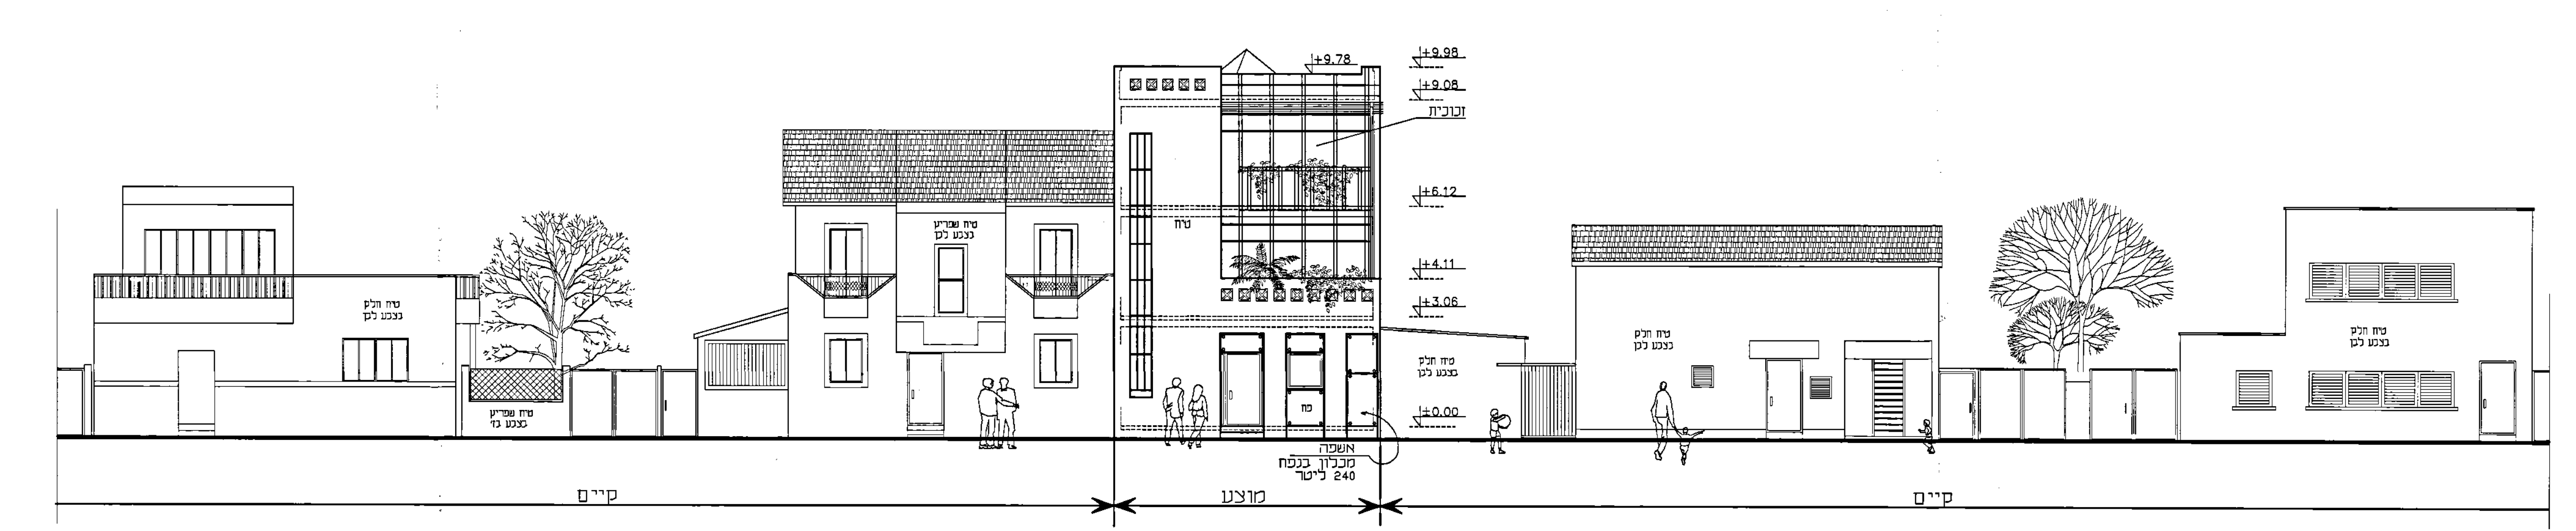
+9.98
+9.78
+9.08
זכוכית
+6.12
+4.11
+3.06
+0.00
טיח
טיח ופרייד
טיח חלק בגוון לבן
משפרה
מכבנה בנפח
240 ליטר
קיים
מוצע
קיים

חזית מערבית

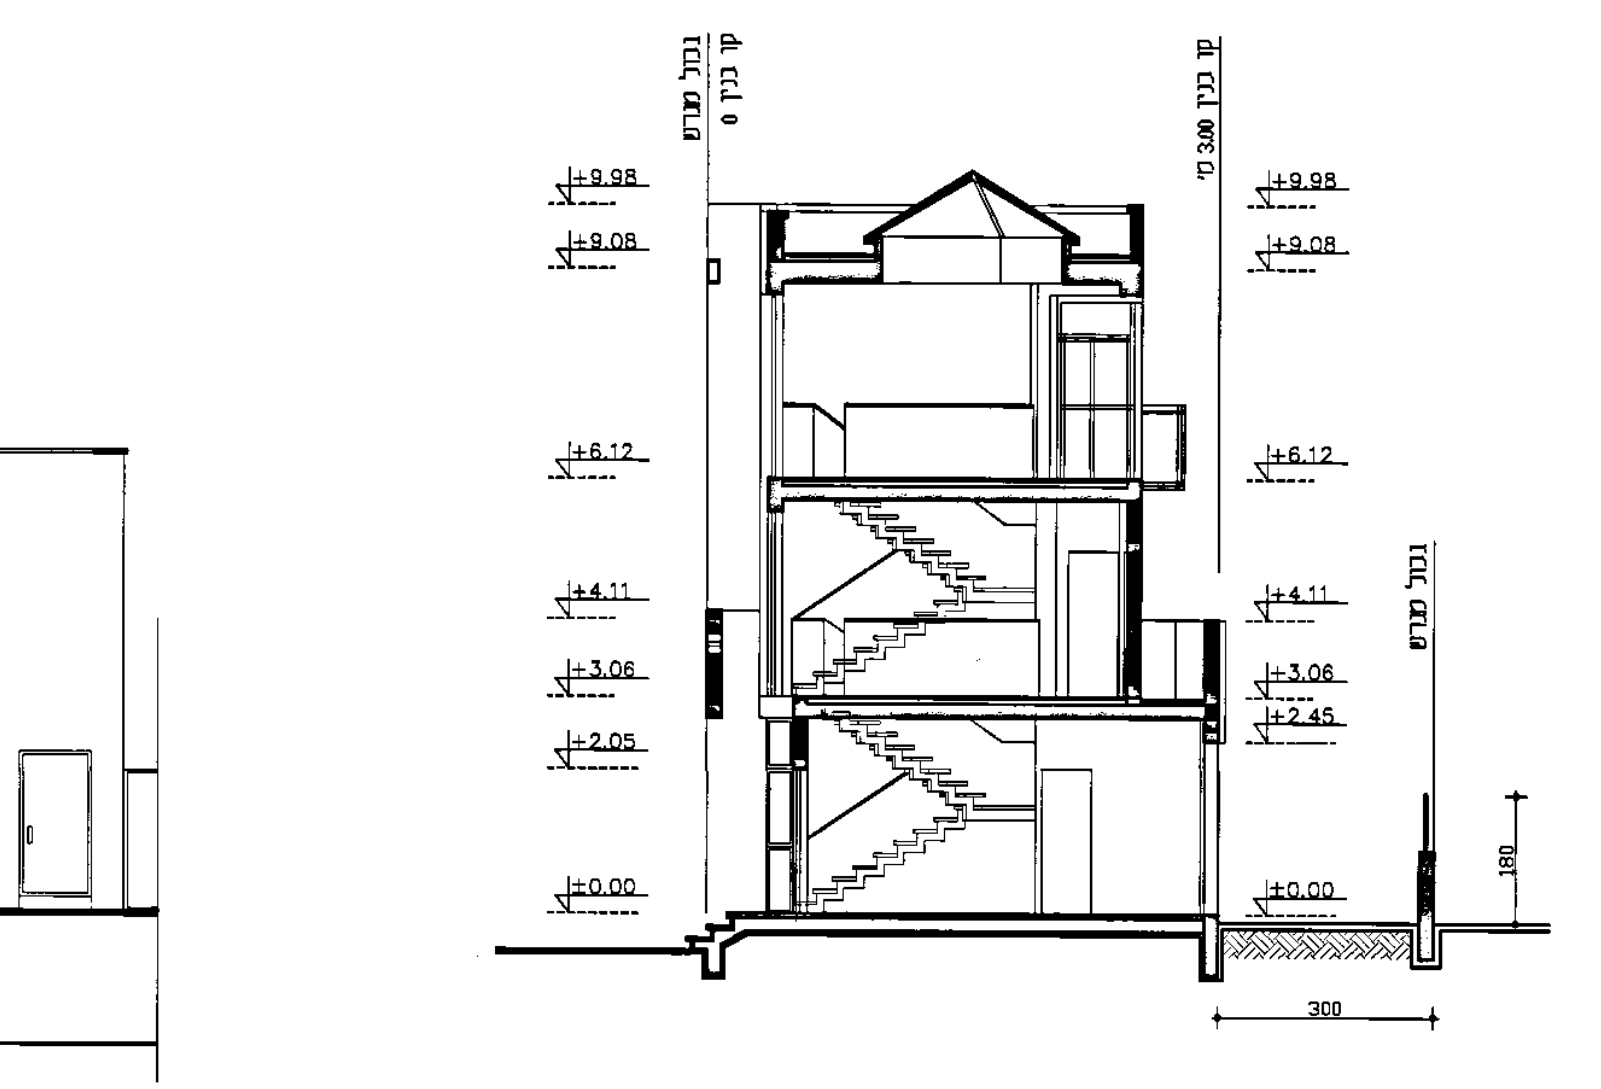
קו בנין 0
קו בנין 3.00
+9.98
+9.08
+6.12
+4.11
+3.06
+2.45
+2.05
+0.00
גבול מגרש
300

חתך A-A

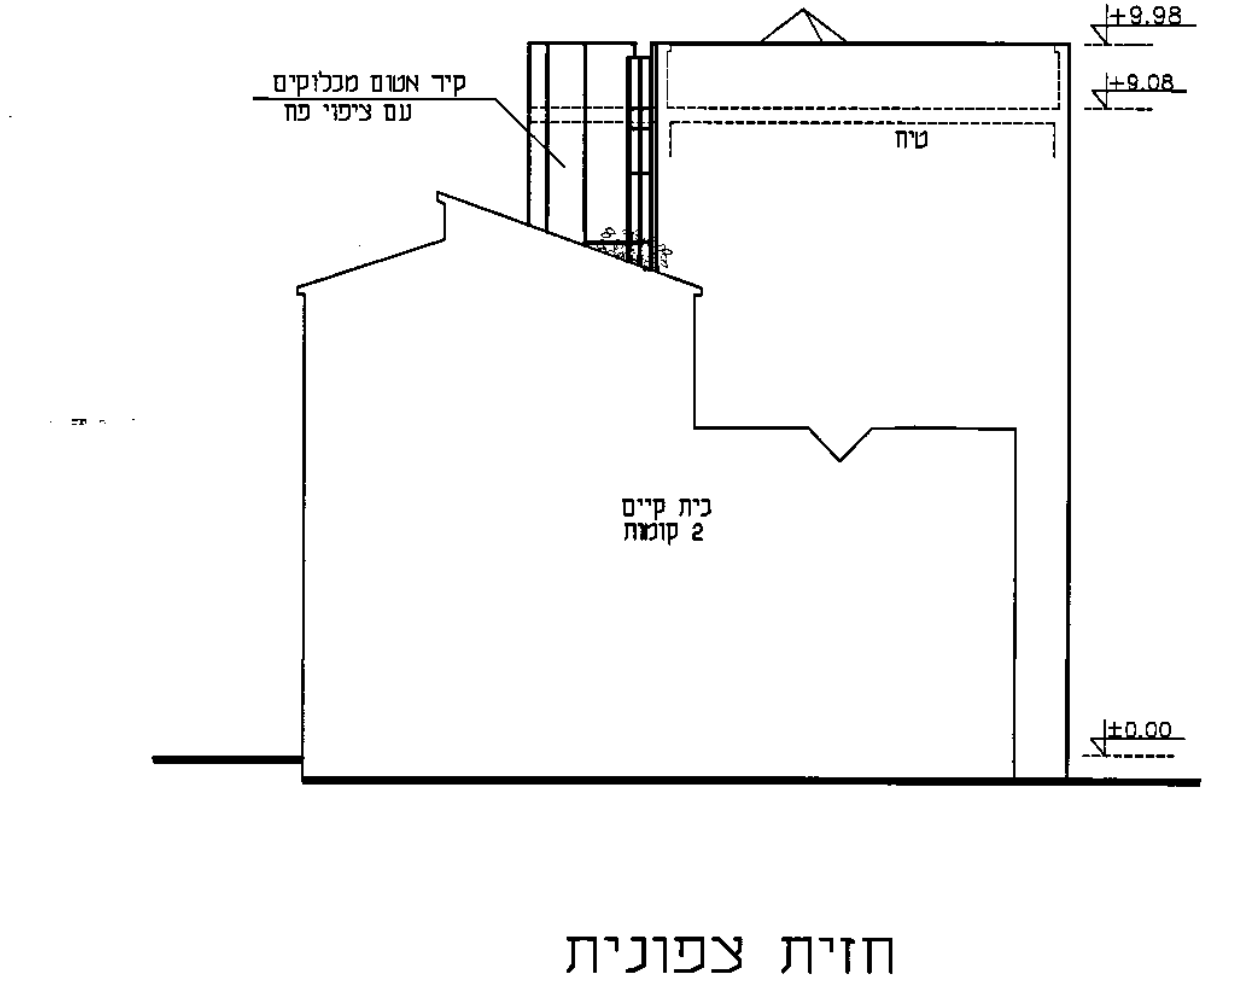
קיר אטום מגלופים
עם ציפוי פח
טיח
בית קיים
2 קומות
+9.98
+9.08
+0.00

חזית צפונית

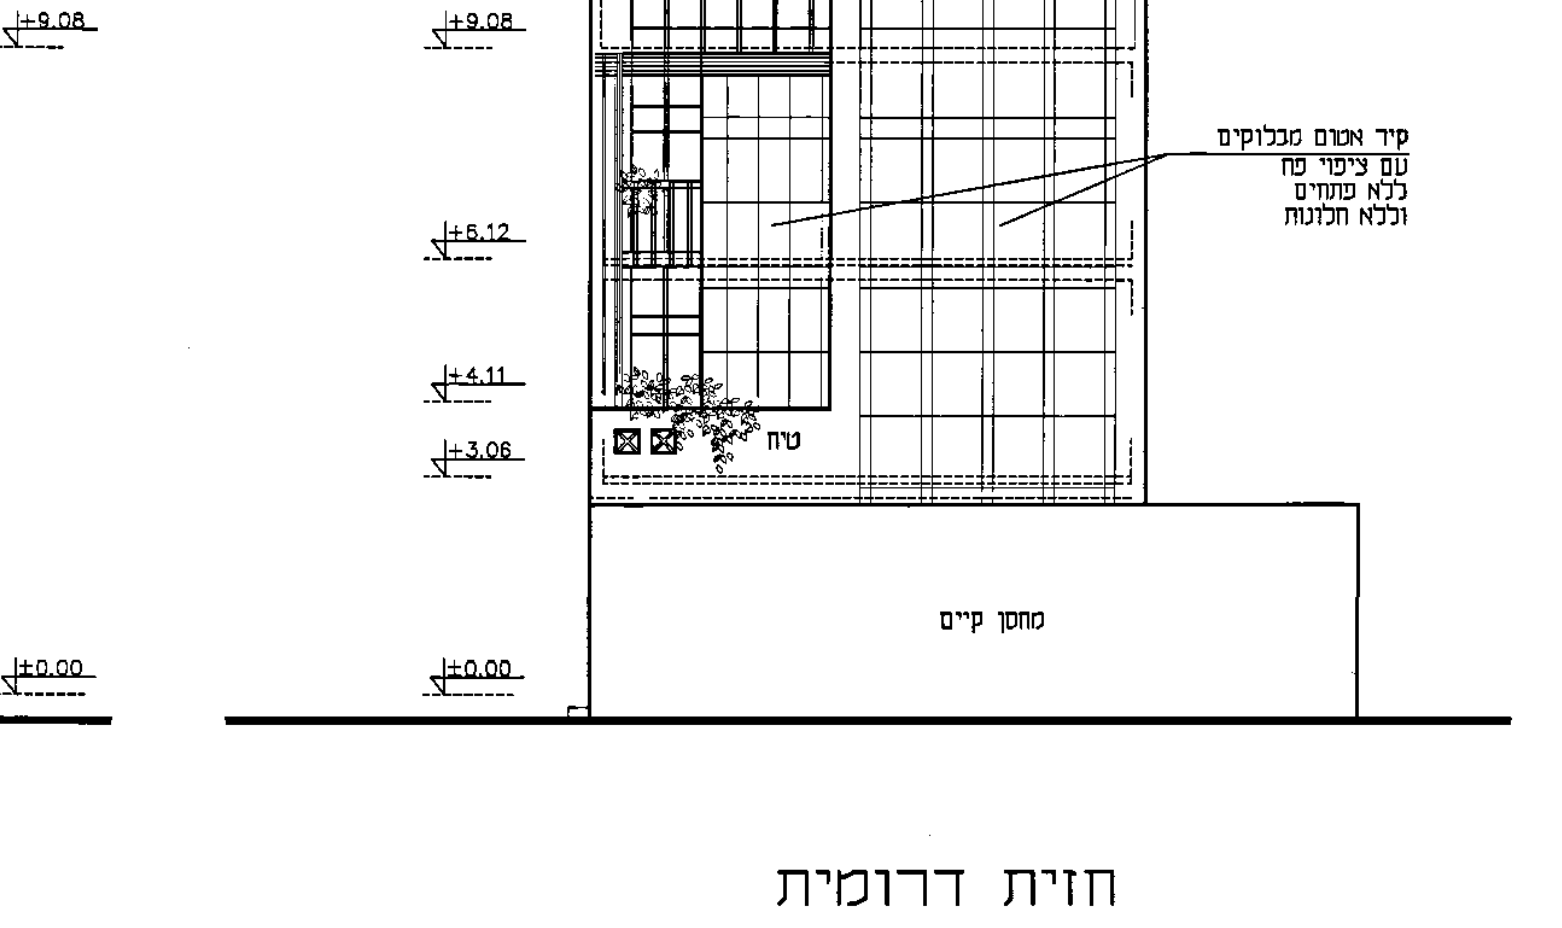
קיר אטום מגלופים
עם ציפוי פח
ללא פתחים
וללא הבלטות
טיח
מחסן קיים
+9.98
+9.08
+6.12
+4.11
+3.06
+0.00

חזית דרומית

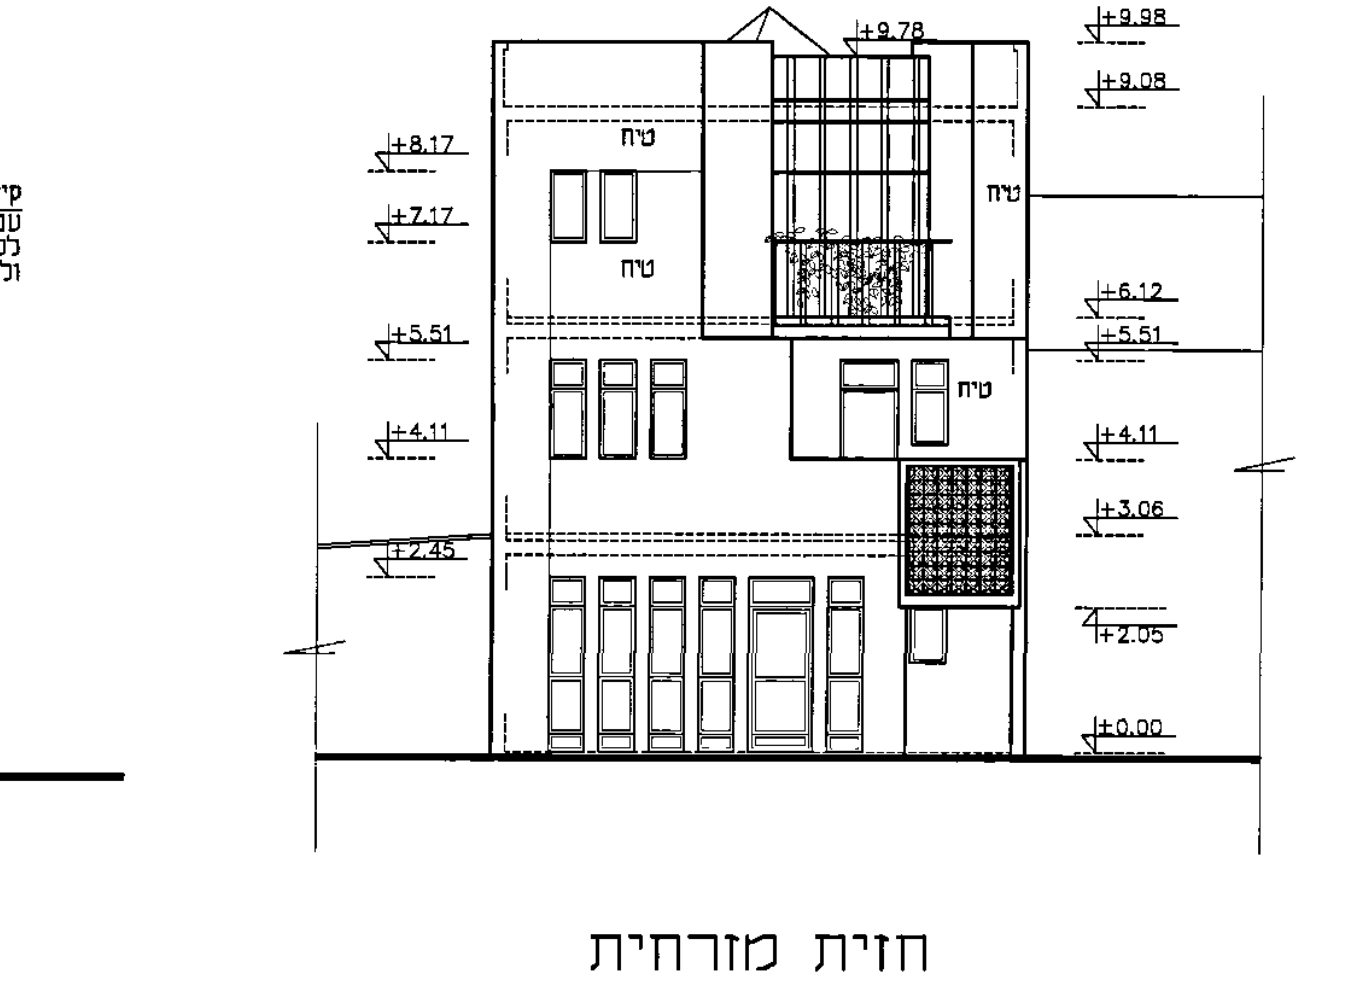
+9.98
+9.78
+9.08
+8.17
+7.17
+6.12
+5.51
+4.11
+3.06
+2.45
+2.05
+0.00
טיח

חזית מזרחית

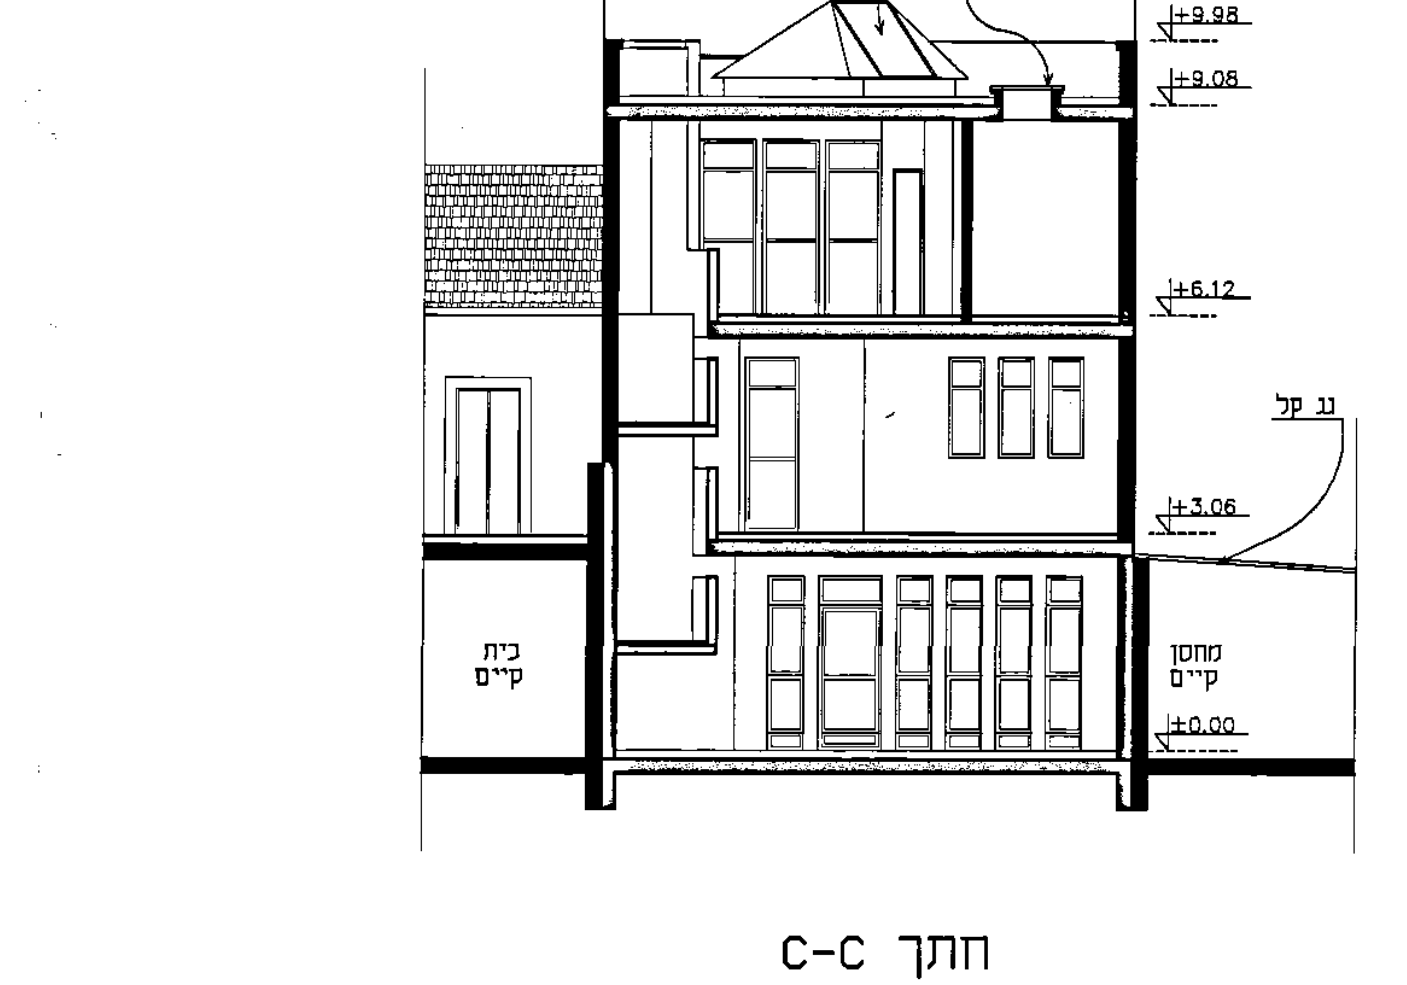
קו בנין
גבול מגרש
קולט שמש
מחזה
ציגואה לגג
+9.98
+9.08
+6.12
+3.06
+0.00
גג קל
מחסן קיים
בית קיים

חתך C-C

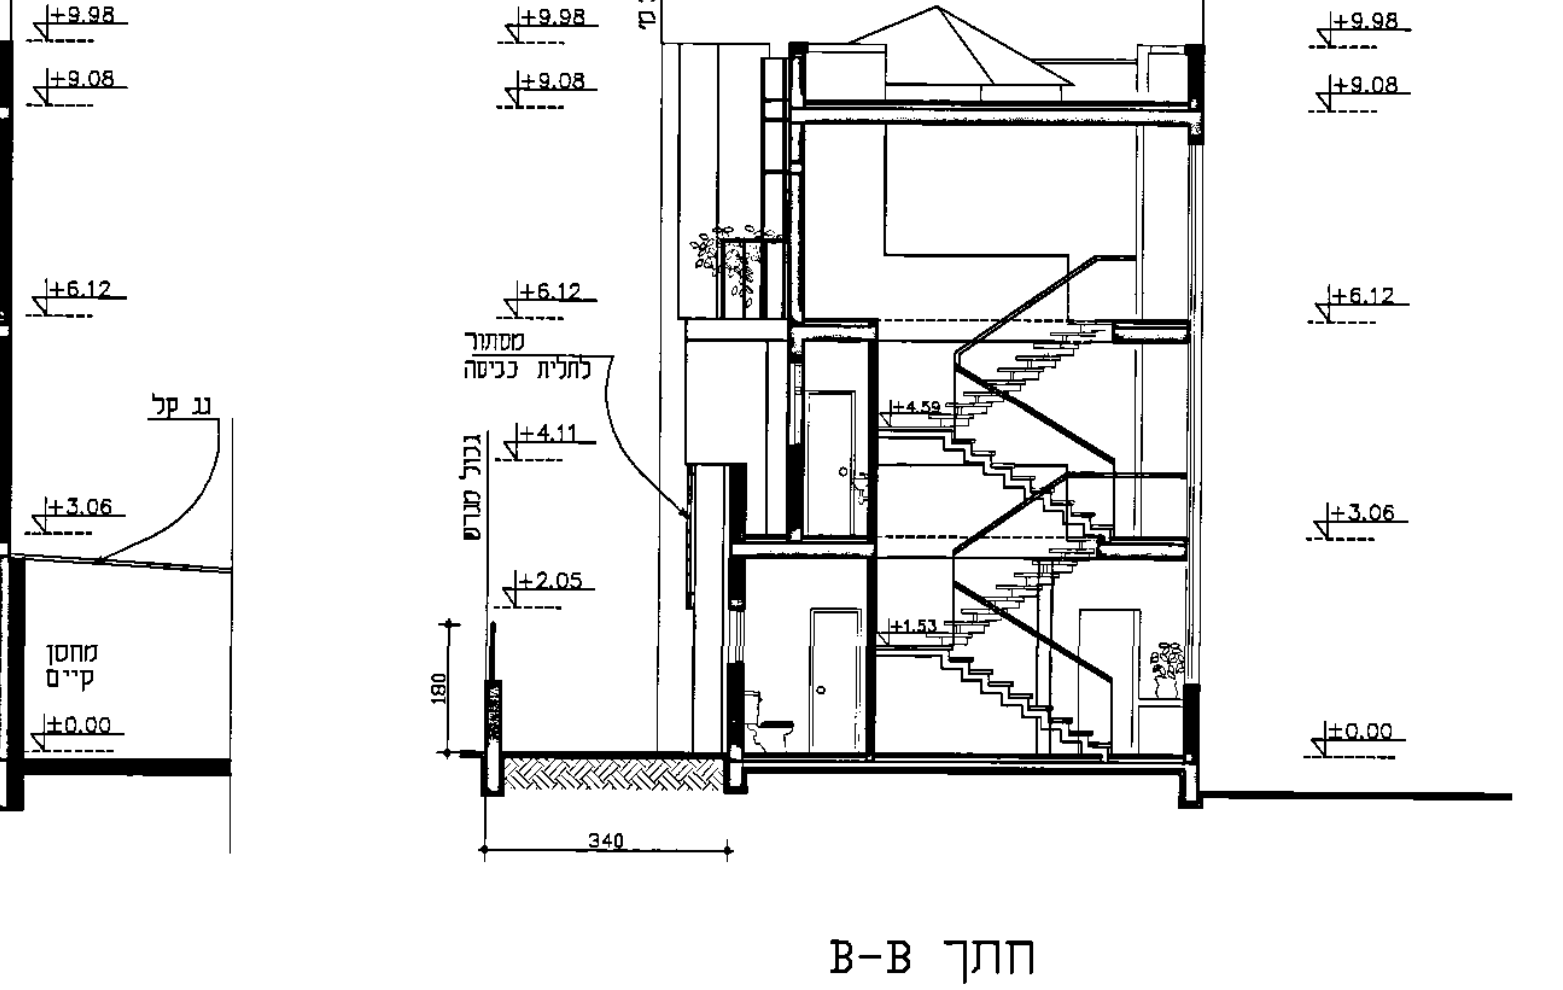
קו בנין 3.00 מ'
גבול מגרש
+9.98
+9.08
+6.12
+4.11
+3.06
+2.05
+0.00
מסתור
לתלית כביסה
240

חתך B-B

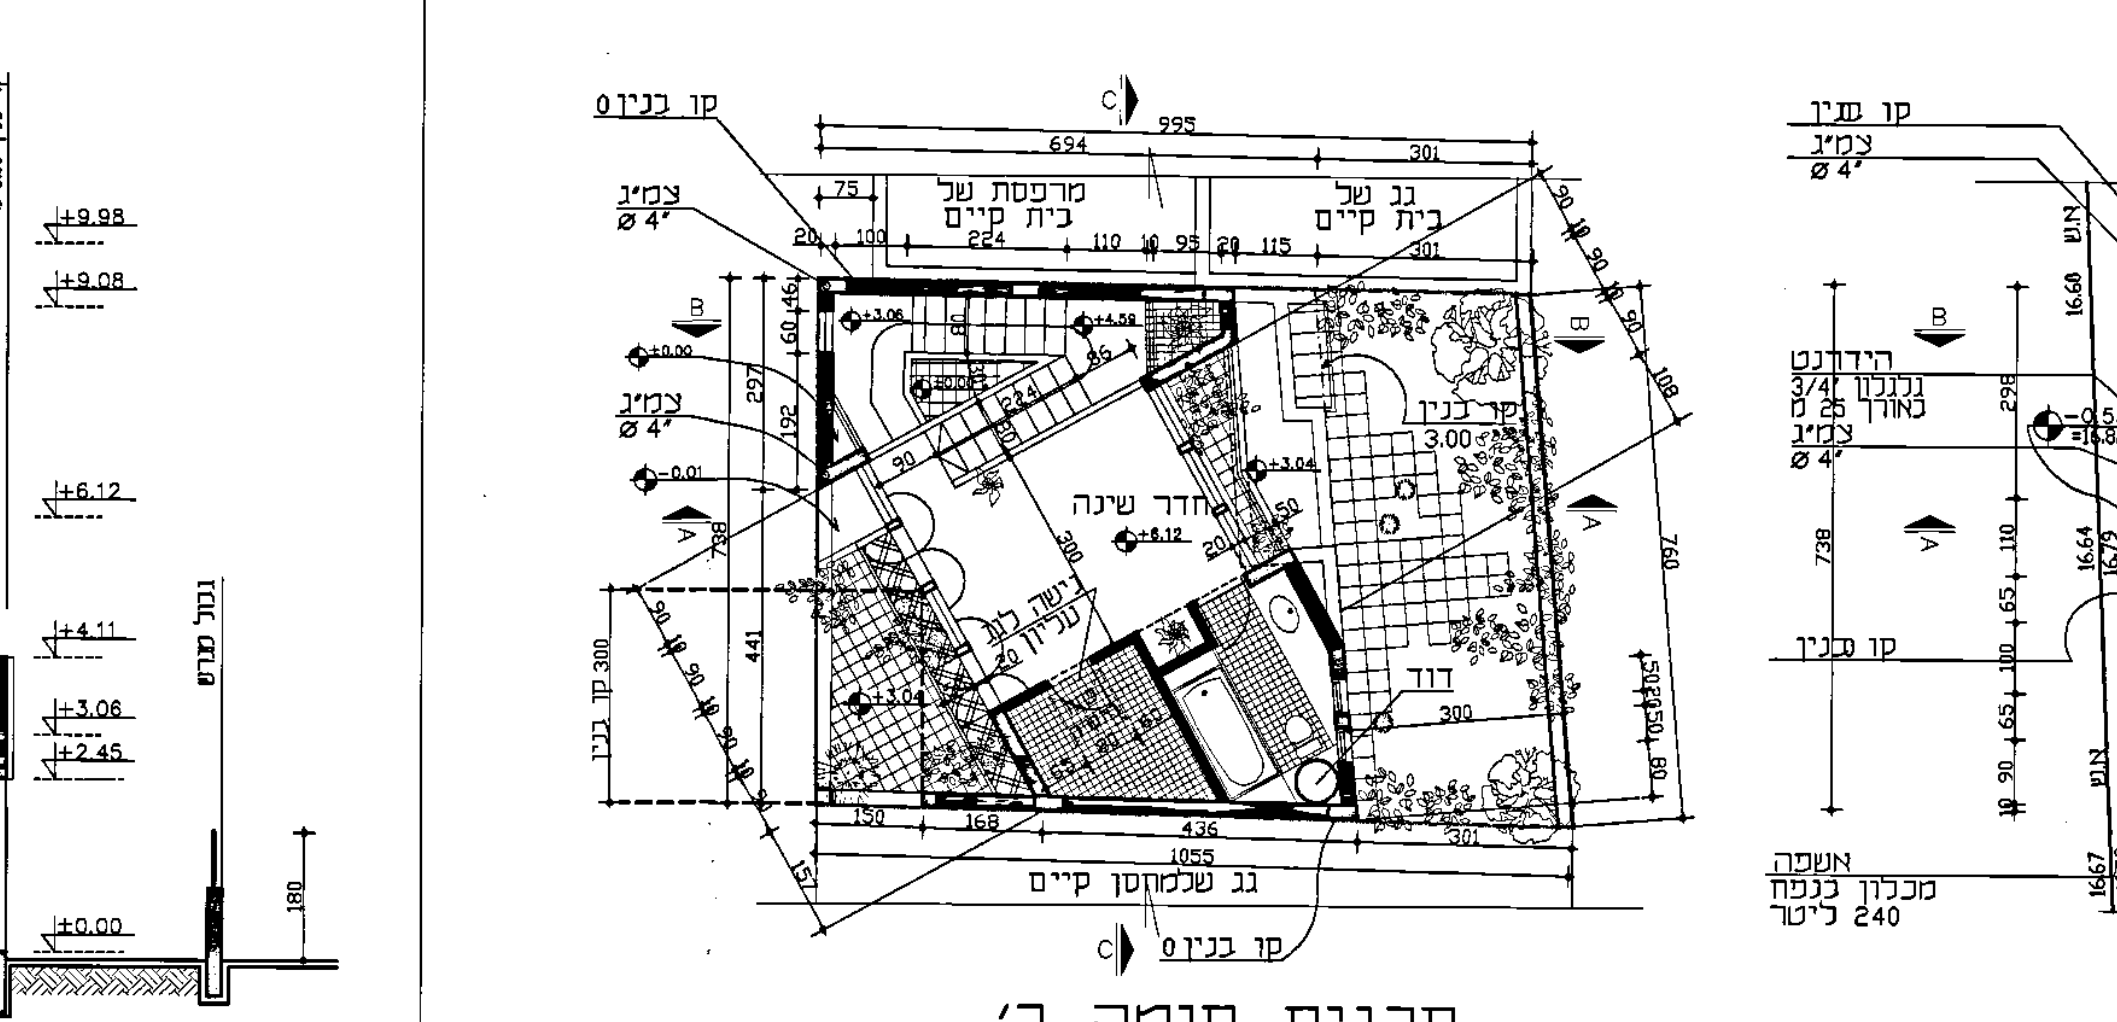
קו בנין 0
צמיג ø4"
בית קיים
מרפסת של בית קיים
גג של בית קיים
חדר שינה
דוד
מחסן קיים
גג שלמטון קיים
קו בנין 3.00
995
654
579
1055
426
236

תכנית קומה ב'
+6.12 מפלס

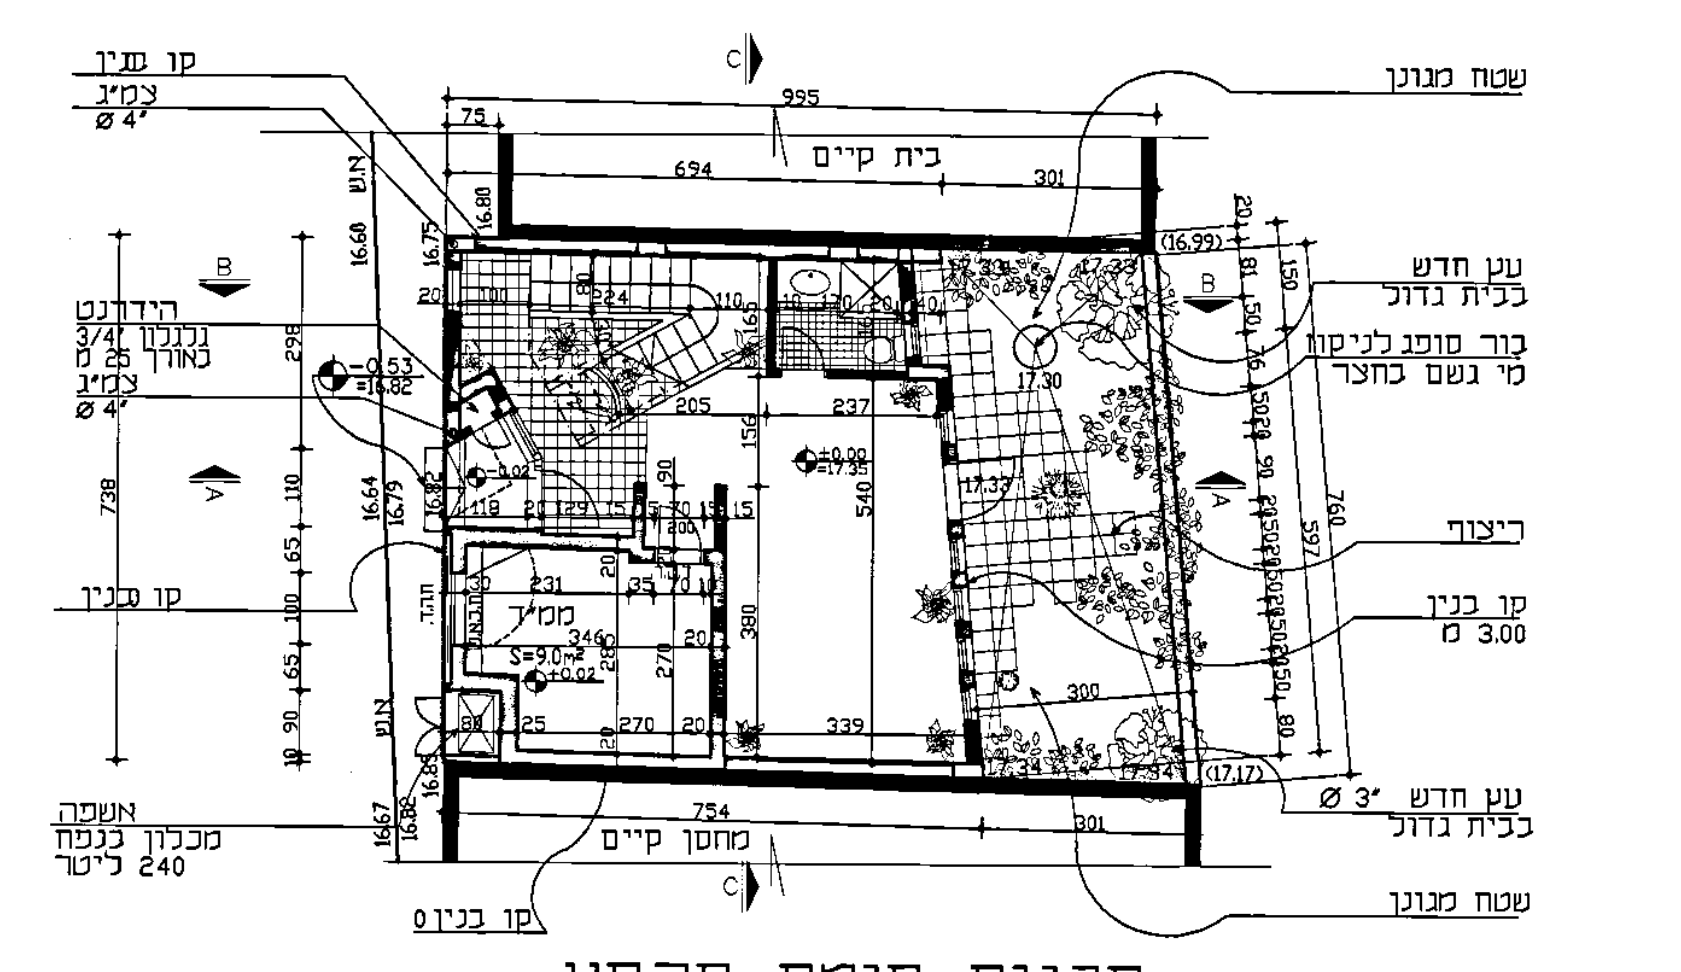
קו מגן
צמיג ø4"
בית קיים
שטח מגונן
עץ חדש
בבית גדול
בור סופג לניקוז
מי גשם בחצר
ריצוף
קו בנין 3.00
עץ חדש ø 3"
בבית גדול
אשפה
מכבנה בנפח
240 ליטר
מחסן קיים
995
694
754

תכנית קומת קרקע
ותכנית פיתוח שטח
מפלס ±0.00

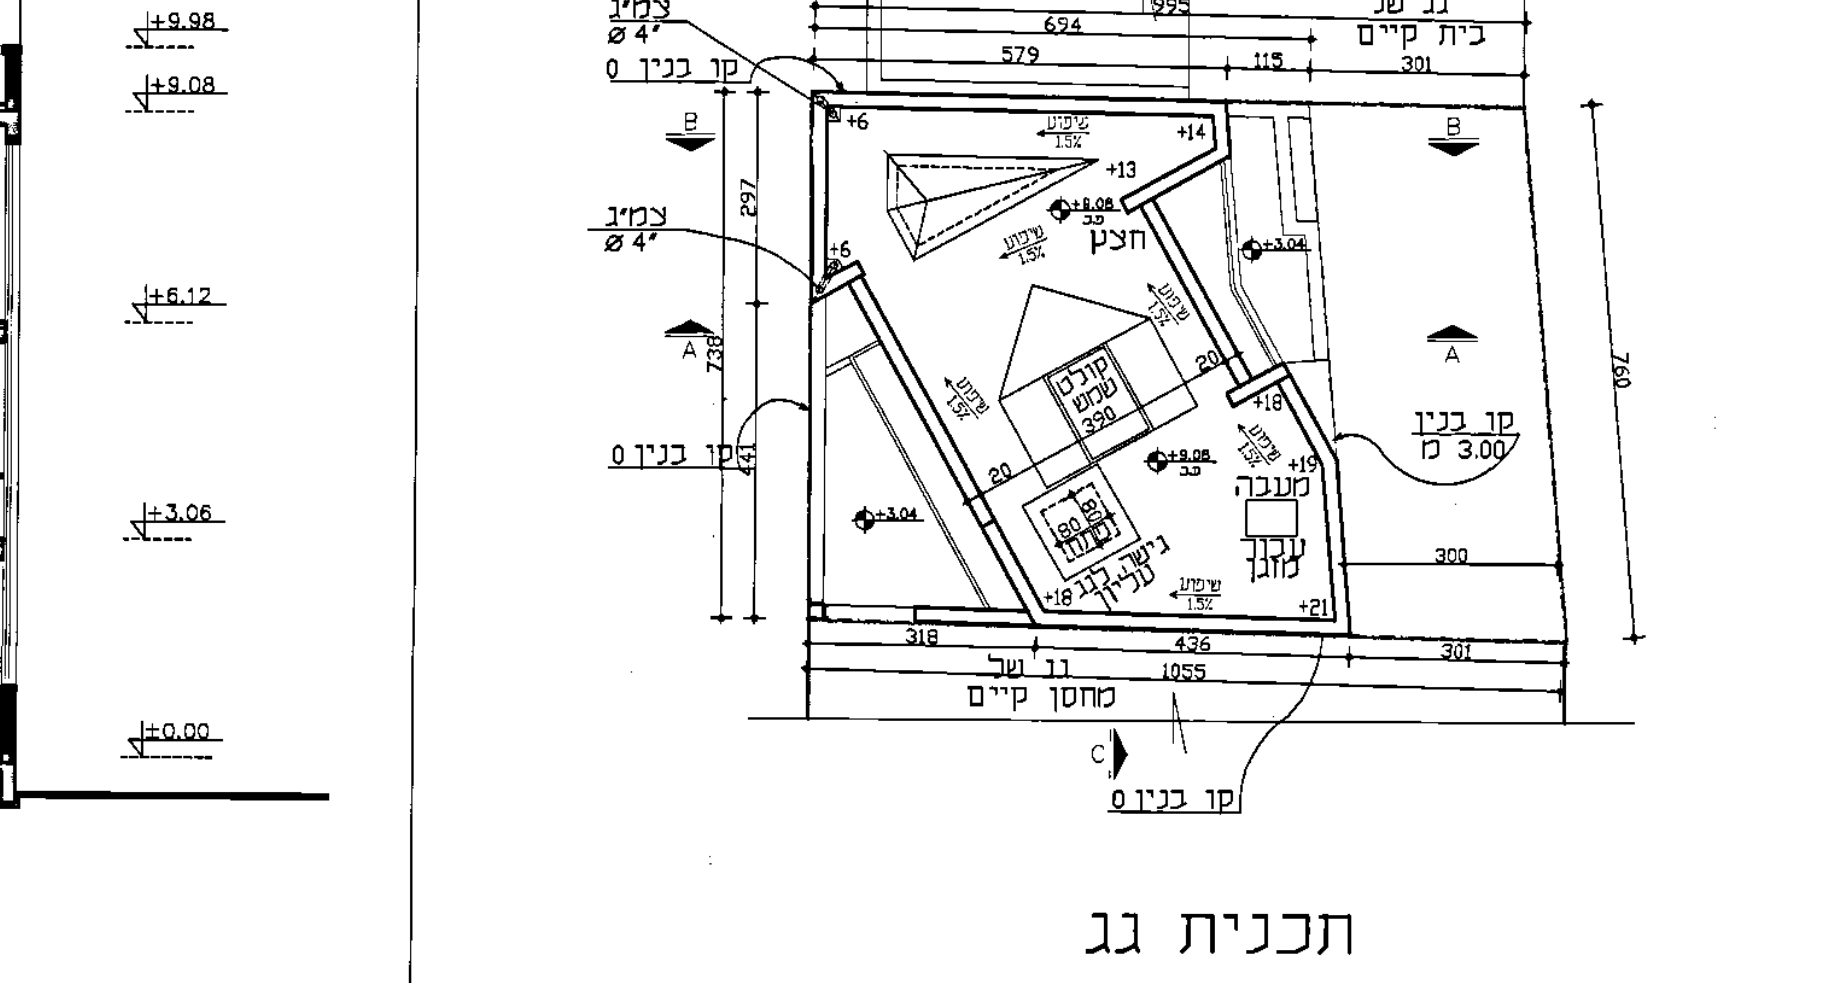
קו בנין 0
צמיג ø4"
גג של בית קיים
קו בנין 3.00
מחסן קיים
995
654
579
1055

תכנית גג

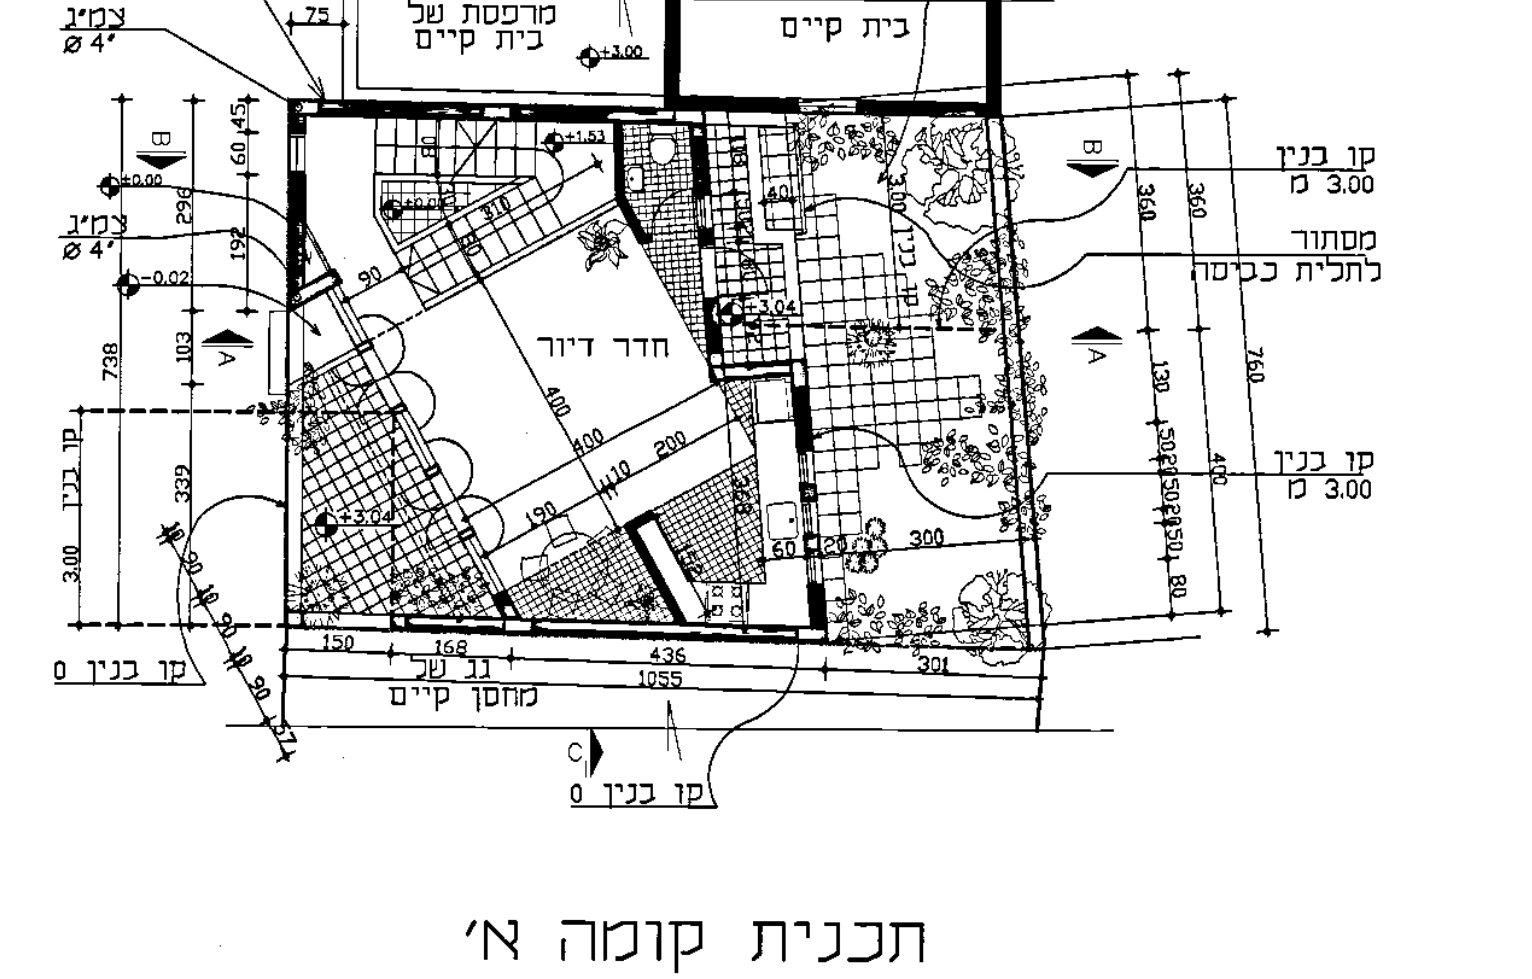
שטח מגונן
צמיג ø4"
מרפסת של בית קיים
בית קיים
חדר דיור
קו בנין 3.00
מסתור
לתלית כביסה
מחסן קיים
קו בנין 0
995
694
1055

תכנית קומה א'
+3.06 מפלס

חישוב תכסית:

סה"כ שטח קומת קרקע:
55.65 - 3.70 = מ"ר 51.95

סה"כ שטח מגרש: מ"ר 76

תכסית: 51.95 : 76 = 0.68 %

חישוב זכויות בניה

לפי ת.ב.ע. מס' 2215

שטח המגרש לפי נסח טאבו :	112 מ"ר
שטח המגרש לפי מדידה עלידי מודד מוסמך:	76 מ"ר
% הבניה המותרים לפי ת.ב.ע.:	140.0 %
תוספת % בניה עבור הריסת בית קיים :	7.5 %
שטח שרות עבור בנית ממ"ד :	7.5 מ"ר

חישוב סה"כ שטח בניה מותר :

76.0 x 1.4 =	106.4 מ"ר
76.0 x 0.075 =	5.7 מ"ר
סה"כ שטח עיקרי מותר :	112.1 מ"ר
(ממ"ד) 7.5 מ"ר =	7.5 מ"ר
סה"כ זכויות בניה מותרים : (עיקרי + שירות)	119.6 מ"ר

תשריט סכימטי של שטחי הבניה
ק.מ. 1:100

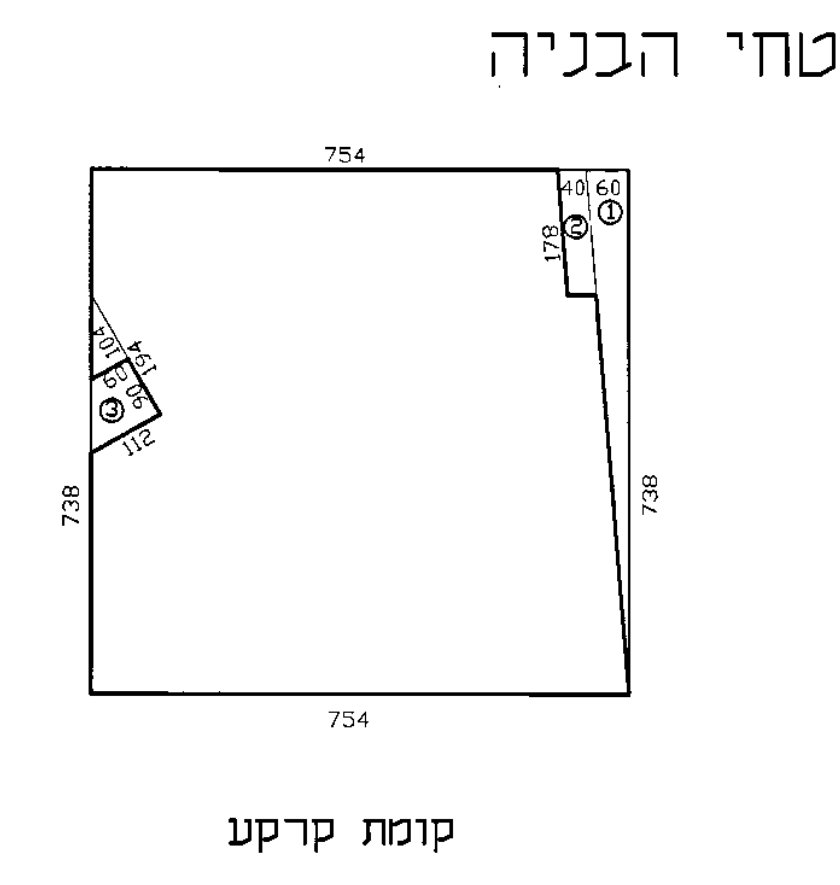
754
738
40
60
178
104
194
60
90
112
①
②
③

קומת קרקע

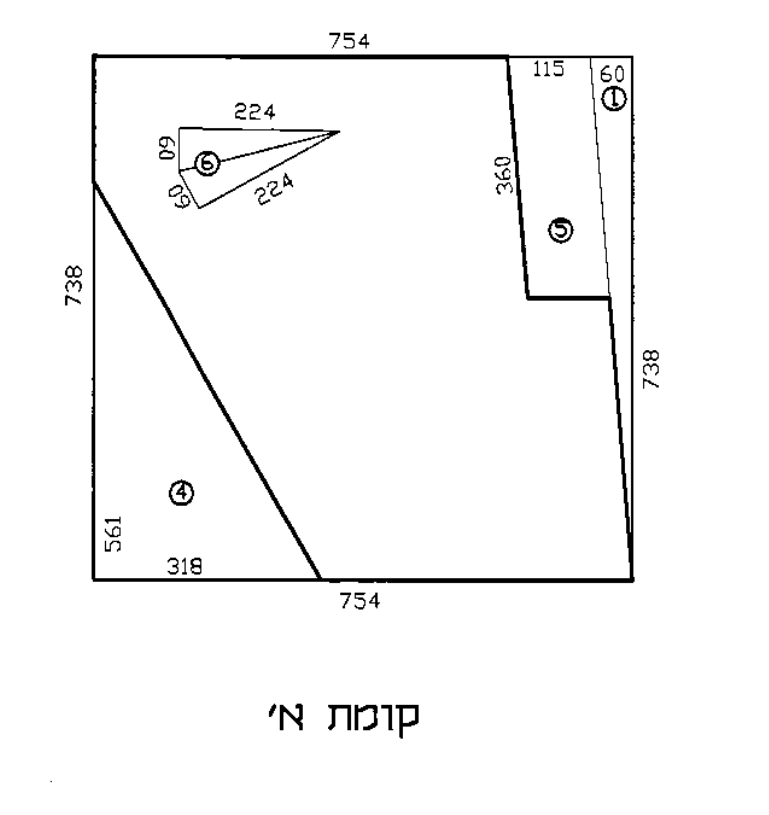
754
738
115
60
360
224
60
561
318
①
④
⑤
⑥

קומת א'

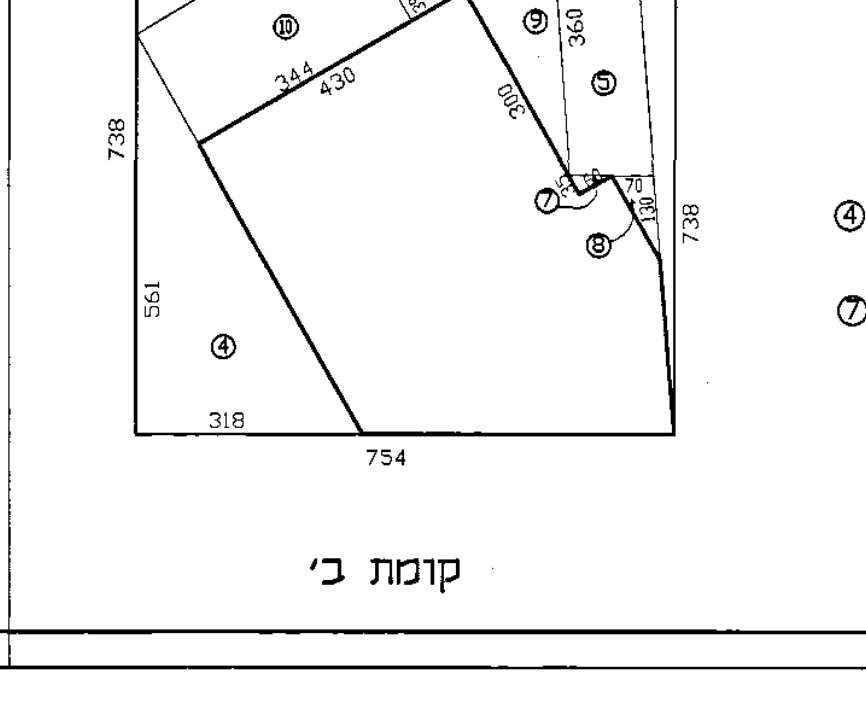
754
738
293
177
142
181
245
227
130
115
60
360
344
430
300
70
130
561
318
①
④
⑤
⑦
⑧
⑨
⑩
⑪
⑫
⑬
⑭

קומת ב'

חישוב שטח קומת קרקע

1. חישוב שטח מסגרת
7.38 x 7.54 =55.65
2. הורדות
① (7.38 x 0.60) : 2 = 2.21
② 1.78 x 0.40 = 0.71
③ (1.12x1.94):2 - (0.60x1.04):2 = 0.78
סה"כ 3.70 מ"ר
3. חישוב שטח שירות 7.5 מ"ר
סה"כ שטח שירות : 7.5 מ"ר
4. חישוב שטח עיקרי - קומת קרקע
55.65 - 3.70 - 7.5 = 44.45 מ"ר

חישוב שטח קומה א'

1. חישוב שטח מסגרת
7.38 x 7.54 =55.65
2. הורדות
① (7.38 x 0.60) : 2 = 2.21
④ (5.61x3.18) : 2 = 8.92
⑤ 1.15 x 3.60 = 4.14
⑥ (2.24x0.60):2x2 = 1.34
סה"כ 16.61 מ"ר
4. חישוב שטח עיקרי - קומה א'
55.65 - 16.61 = 39.04 מ"ר

חישוב שטח קומה ב'

1. חישוב שטח מסגרת
7.38 x 7.54 =55.65
2. הורדות
① (7.38 x 0.60) : 2 = 2.21
④ (5.61x3.18):2 = 8.92
⑤ 1.15 x 3.60 = 4.14
⑦ (0.60x0.35):2 = 0.10
⑧ (1.30x0.70):2 = 0.45
⑨ (3.00x1.30):2 = 1.95
⑩ 3.44 x 1.81 = 6.22
⑪ (1.77x2.93):2 = 2.59
⑫ 0.39 x 2.27 = 0.89
⑬ (1.42 x 2.45):2 = 1.74
⑭ (0.39 x 0.18):2 = 0.04
סה"כ 29.25 מ"ר
4. חישוב שטח עיקרי - קומה ב'
55.65 - 29.25 = 26.40 מ"ר

סה"כ שטח עיקרי
44.45 + 39.04 + 26.40 = 109.89

סה"כ שטח (עיקרי+שרות)
109.89 + 7.5 = 117.39

שטחים לא מקוריים קומת א' :
④+⑤-②-③ = 8.92+4.14-0.71-0.78 = 11.57

שטחים לא מקוריים קומת ב' :
⑦+⑧+⑨ = 0.10+0.45+1.95 = 2.40

סה"כ שטחים לא מקוריים (מרפסות) :
= 13.97

תל-אביב-יפו מפה טופוגרפית
מס' סדורי 2073 / 2000
ק.מ. 1 : 250

שכונת התקוה
גוש : 6135
חלקה 110 (חלק)
רח' תשבי 27

הוכן עבור: סושניק גוליין
מהות הבקשה: התר בניה

שטח לפי נסח טאבו: 112 מ"ר
שטח מדוד: 76 מ"ר

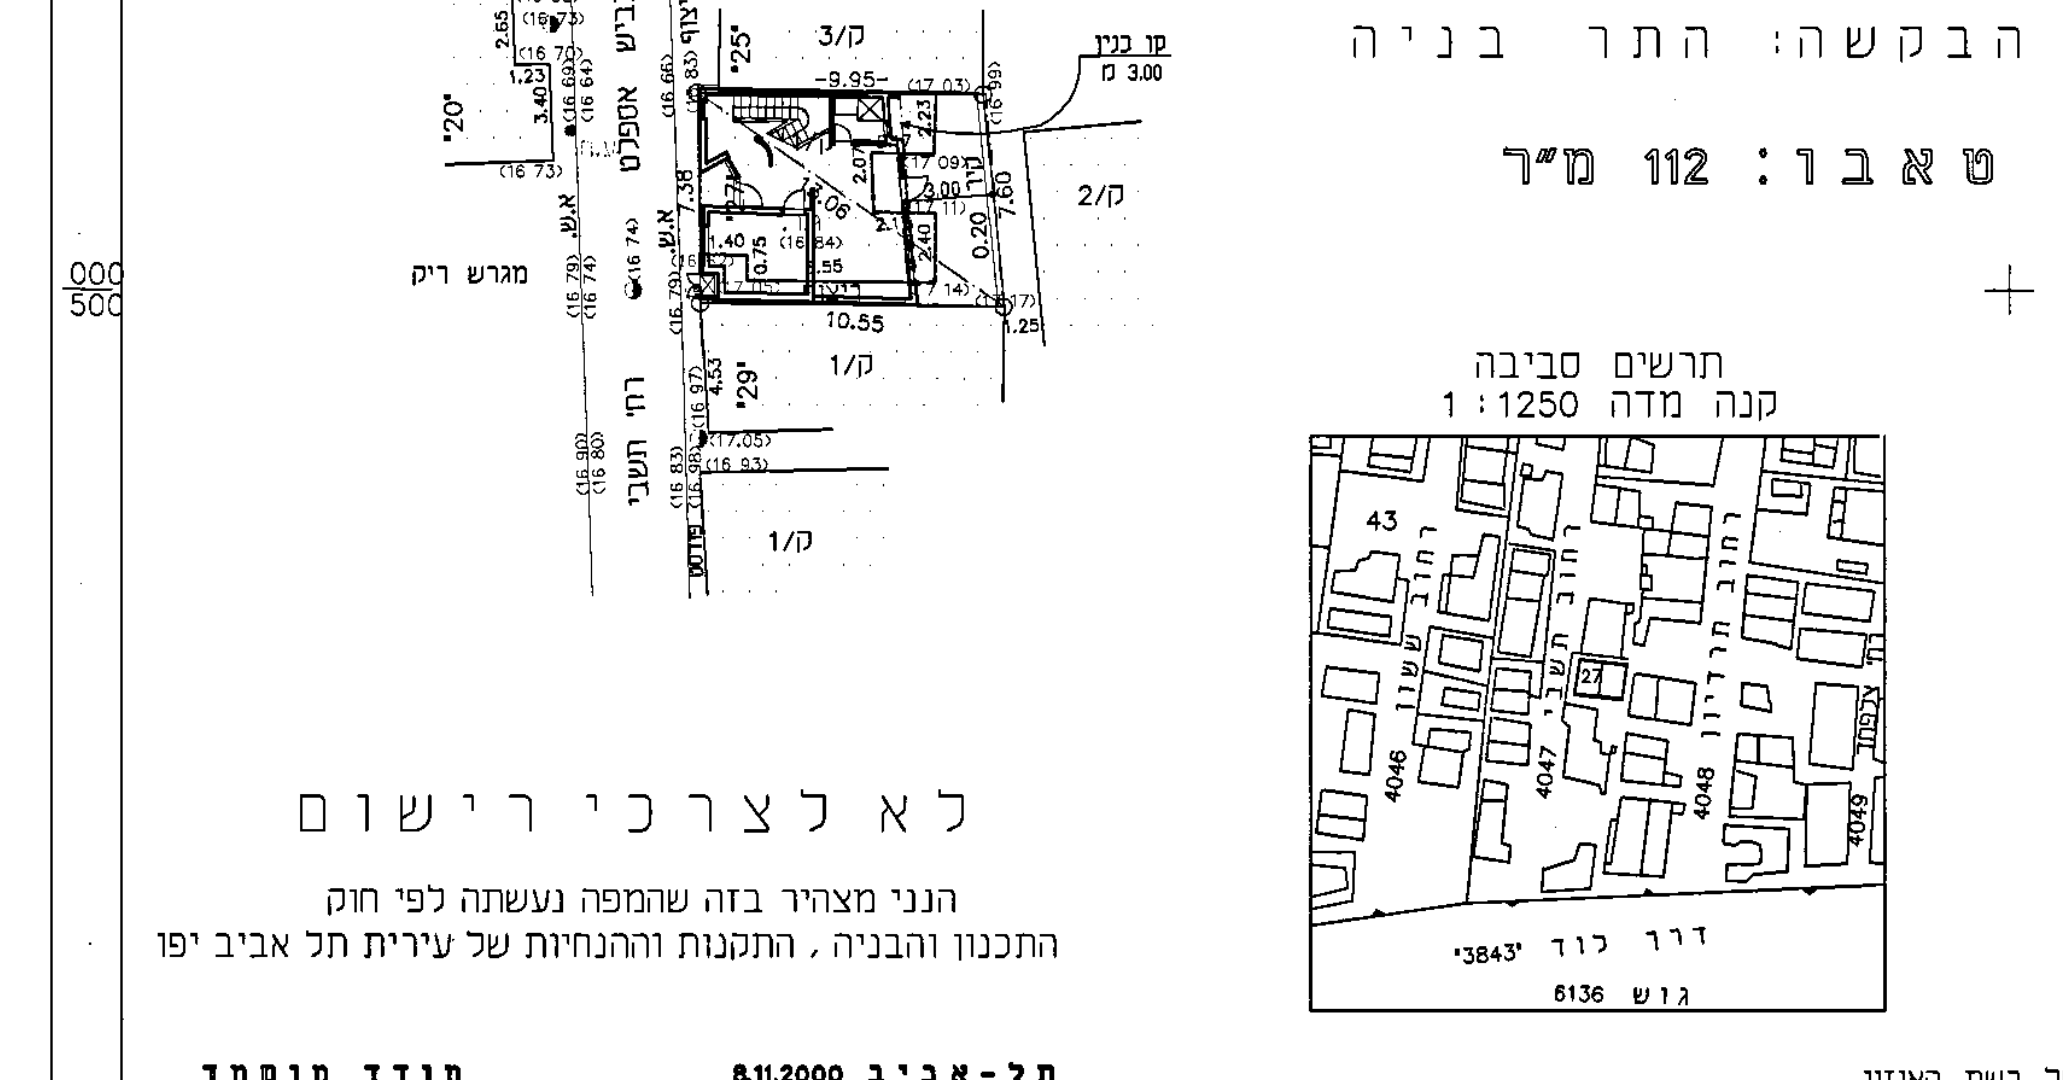
ק/1
ק/3
ק/2
רח' רבדי אספלט
מגרש ריק
רח' תשבי
ריצוף
גדר
-9.95-
10.55
6.55
13.06
7.38
7.60
"20
"25
"27
"29
ג.ר.
תרשים סביבה
קנה מדה 1:1250
43
27
4046
4047
4048
4049
דרך לוד
"3843"
גוש 6136

לא לצרכי רישום

הנני מצהיר בזה שהמפה נעשתה לפי חוק
התכנון והבניה, התקנות וההנחיות של עירית תל אביב יפו

תל-אביב 8.11.2000 מודד מוסמך
ראובן לאופר - מודד מוסמך מס' רשיון 574
משרד טכני למדידות
משרד : רח' הרכבת 20 תל - אביב טל': 5608221 - 03
מען : רח' בורלא 32 תל - אביב טל': 6993398 - 03

הערות:
1. הגבהים מבוססים על נ.ק. 187 של רשת האיזון העירונית שגובהה 17.549 מ.'
2. הגבהים נרשמו בסוגריים.
3. ייתכנו שינויים בשטחים ובמידות בעת עריכת תכניות לצרכי רישום והסדר הקרקע אצל רשם המקרקעין.

תכנית העמדה

תל-אביב-יפו מפה טופוגרפית
מס' סדורי 2073 / 2000
ק.מ. 1 : 250

שכונת התקוה
גוש : 6135
חלקה 110 (חלק)
רח' תשבי 27

הוכן עבור: סושניק גוליין
מהות הבקשה: התר בניה

שטח לפי נסח טאבו: 112 מ"ר
שטח מדוד: 76 מ"ר

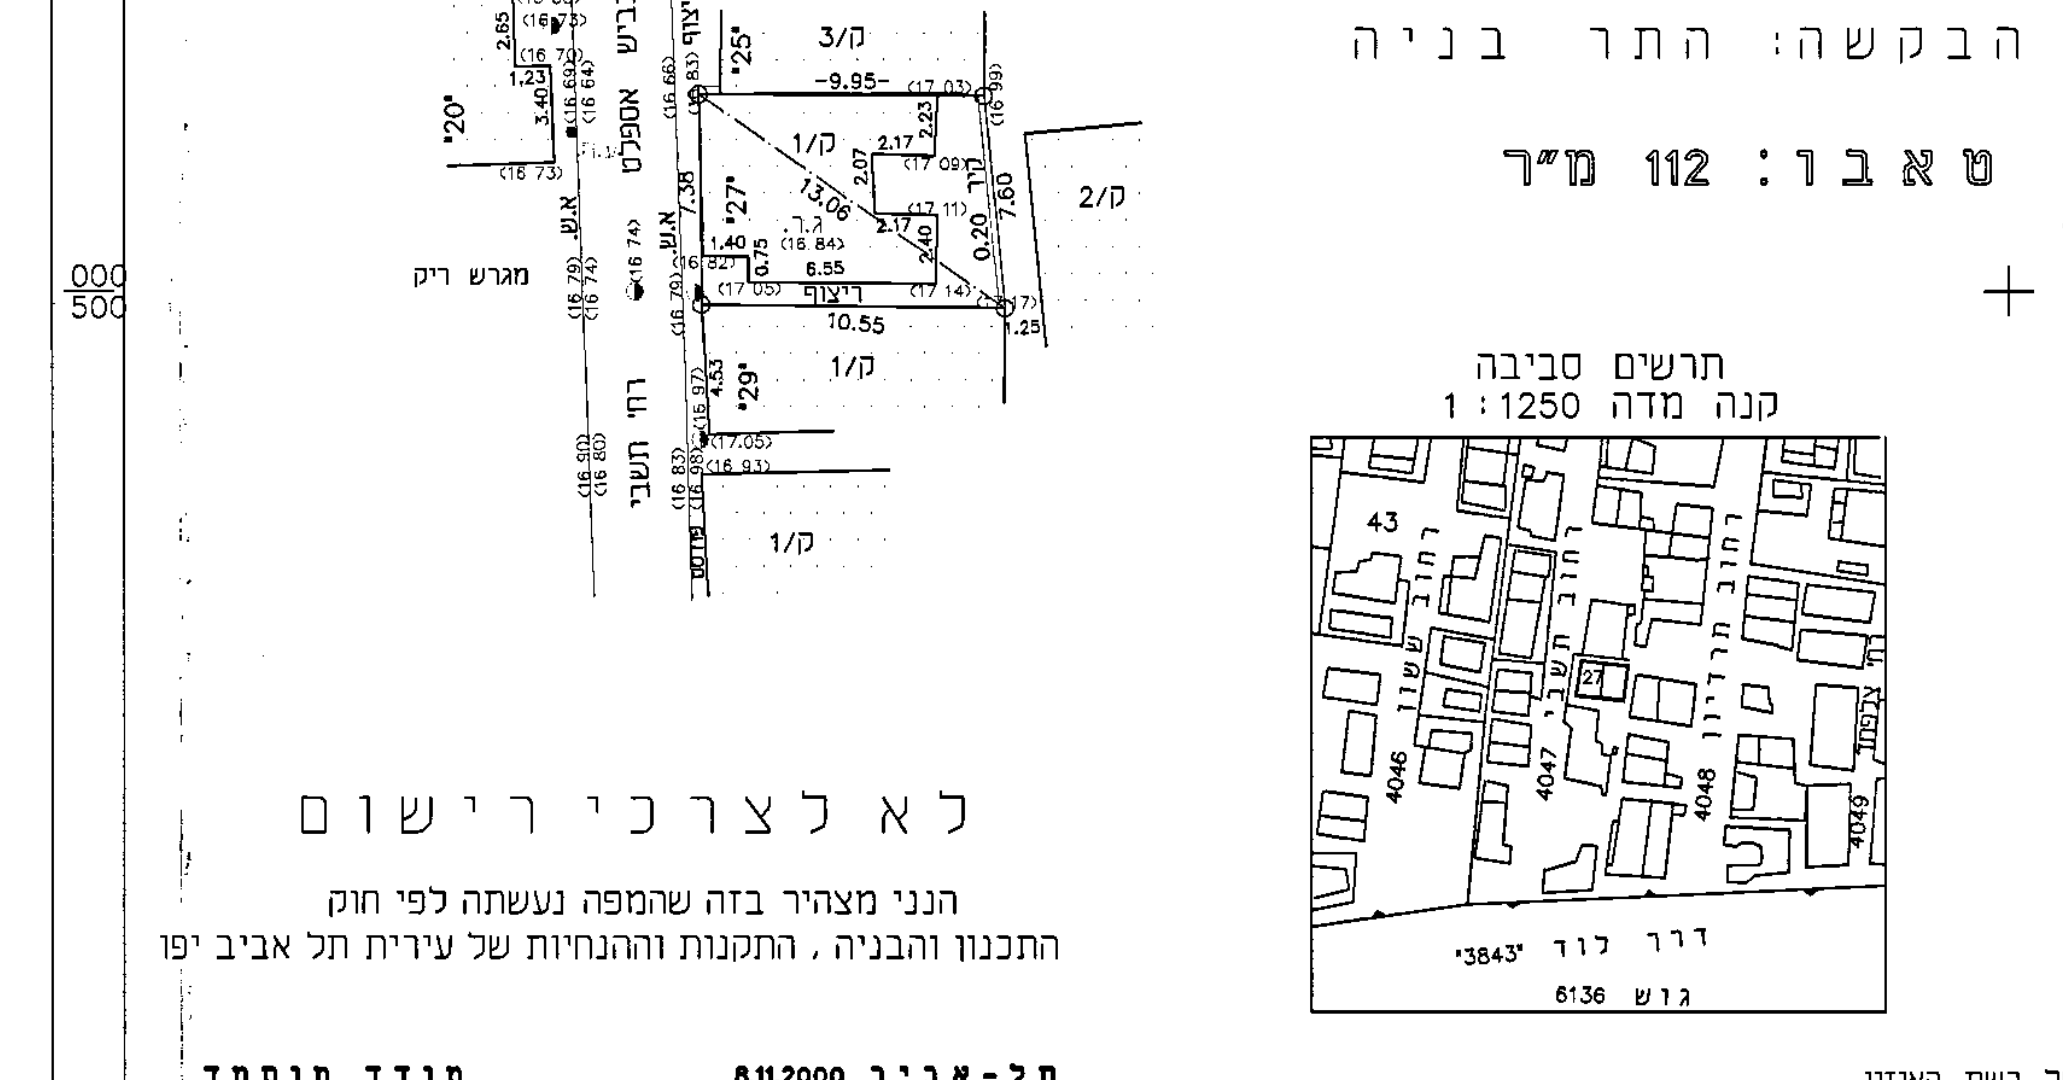
ק/1
ק/3
ק/2
רח' רבדי אספלט
מגרש ריק
רח' תשבי
ריצוף
גדר
-9.95-
10.55
6.55
13.06
7.38
7.60
תרשים סביבה
קנה מדה 1:1250
43
27
4046
4047
4048
4049
דרך לוד
"3843"
גוש 6136

לא לצרכי רישום

הנני מצהיר בזה שהמפה נעשתה לפי חוק
התכנון והבניה, התקנות וההנחיות של עירית תל אביב יפו

תל-אביב 8.11.2000 מודד מוסמך
ראובן לאופר - מודד מוסמך מס' רשיון 574
משרד טכני למדידות
משרד : רח' הרכבת 20 תל - אביב טל': 5608221 - 03
מען : רח' בורלא 32 תל - אביב טל': 6993398 - 03

הערות:
1. הגבהים מבוססים על נ.ק. 187 של רשת האיזון העירונית שגובהה 17.549 מ.'
2. הגבהים נרשמו בסוגריים.
3. ייתכנו שינויים בשטחים ובמידות בעת עריכת תכניות לצרכי רישום והסדר הקרקע אצל רשם המקרקעין.

מפת איתור העבודה (תרשים מגרש)

מנהל מחלקה [illegible] עבור אישור איכות הסביבה

22

עיריית תל - אביב - יפו
מינהל ההנדסה, אגף רישוי ופיקוח על הבניה
שדרות בן-גוריון 68 תל-אביב 64514 (פקס 5231340) טלפון 5217120, 5217045

הנדסה - התקבל 04-04-2002
במחלקה לרישוי הבניה
☒ הועדה המקומית לתכנון ולבניה
☐ רשות הרישוי המקומית

חוק התכנון והבניה, התשכ"ה-1965
תקנות התכנון והבניה (בקשה להיתר תנאיו ואגרות) התש"ל-1970

על פי טופס 1 תקנה 2(א)

בקשה להיתר בניה או לשימוש במקרקעין - בניין חדש

יש להקפיד למלא את כל הפרטים בטופס הבקשה ולצרף מסמכים כנדרש ברשימת התיוג המצורפת.

מס' תיק הבניין	מס' בקשה קודמת להיתר בניה	מס' הבקשה למידע	תאריך
4047-27	—	מ/210238	22-02-2001

א. פרטי הבקשה

הכתובת	רחוב	מס' בית	גוש	חלקה	תת חלקה	מגרש	הוראות התכניות החלות על המקום
	תשבי	27	6135	110 (חלק)			2215,2215,א,N

פרטים אישיים	שם משפחה	שם פרטי	מס' זהות/חברה	רחוב ומספר בית / ישוב ומיקוד	מספר טלפון
מבקש 1	גורדון	ג'ינתהן	309898773	רח' התשבי 27 / תל - אביב	053-247447
מבקש 2					
מבקש 3					
בעל הזכות בנכס	סושניק	גוליין	מס' דרכוני: 101982845	בוסטון / ארה"ב	
החוכר					
עורך הבקשה הראשי	אורנת	זוהר	13041496	בית צורי 12 / ת"א 69122	03-5618868 03-5615675
מתכנן שלד הבניין	סגל	מיכאל	6903184	רח' נתן יליו-מור 6 / תל - אביב	03-5627020 03-5617999

ב. מהות הבקשה לבניה חדשה

☒ הריסת מבנה קיים הכולל 1 קומות מגורים/
☒ הקמת מבנה חדש הכולל:
☐ מרתף/ים ☐ קומה מפולשת ☐ קומה מסחרית ל
☒ 3 קומות מגורים ובהן 1 יחידות דיור
☐ המרתף/ים כולל/ים:
☐ מקלט ☐ מחסן ☐ חדרי עזר ☐
☐ קומת הקרקע כוללת: ☐ אולם כניסה ☐ חדר גז
☐ חדר אשפה ☐ חניות ☐ מסעדה
☒ 1 חדרי שירותים
☒ על הגג: ☐ חדרי יציאה ☐ חדרי מכונות ☒ קולטי שמש
☐ חדר מדרגות כללי ☐ פרגולה
☐ בחצר: ☐ מקומות חניה ☒ גינה
☒ שטחים מרוצפים ☐ פרגולה
☐ בגבולות המגרש גדר בגובה 1.80 מטר
פירוט נוסף:

ג. מפרט - תיאור הבקשה

תיאור הקיים על המגרש: בית בן קומה 1 המיועד להריסה

שימוש עיקרי: ☒ מגורים ☐ תעשיה ☐ משרדים ☐ בניין ציבורי ☐ מסחר ☐ מלאכה ☐ מלונאות ☐ חקלאי ☐ בידור ☐ שימוש אחר, פרט: ☐ מעון וסעודה

סוג העבודה או השימושים המוצעים: ☒ הריסה ☒ בניין חדש

הגורם המתבצעת העבודה בבניין: ☐ משרד ממשלתי ☐ בנה ביתך ☐ רשות מקומית ☐ אחר: ☐ מוסד ציבורי ☒ גורם פרטי

שטחים: שטח הבנייה הכולל המבוקש 117.39 מ"ר; שטח המגרש/ החלקה 112 לפי טאבו, 76 לפי מודד; אחוזי הבניה 154.5%

ד. חומרי הבניה

סוג הבנייה: ☒ רגילה ☐ בית מוכן ☐ טרומית
קירות חיצוניים: ☐ בטון מזוין ☒ בלוקים ☐ אבן מבנית ☐ לבנים שרופות ☐ אחר
חומרי גימור: ☒ אבן מלאכותית ☒ זכוכית ☐ אבן מבנית ☒ טיח — מתכת
תקרות: ☒ בטון מזוין ☐ עץ ☐ אחר
גג: ☒ בטון מזוין ☐ אסבסט ☐ רעפים ☐ פח ☐ אחר
גדרות: ☒ אבן מבנית ☐ בלוקים ☐ רשת ☐ אבן מלאכותית ☒ ברזל ☐ עץ ☐ בטון ☐ אחר
קיימות 7.60 מ"א, מוצעות 7.60 מ"א, סה"כ 7.60 מ"א

ה. קווי בנייה

הכיוון	מוצע	מותר	הסטיה במטר	ב-%
לרחוב (גבול) התשבי	0	0	0	0
לצד ~~לרחוב (גבול)~~ צפון	0	0	0	0
לצד דרום	0	0	0	0
לאחור מזרח	3	3	0	0

ו. השטחים המבוקשים לבנייה

	מגורים מ"ר (שטח עיקרי)	% משטח המגרש	סה"כ שטחי השירות מ"ר	% משטח המגרש	סה"כ שטחי הבניין מ"ר	% משטח המגרש	שטחים לא מקוריים
קרקע	44.45	58.5%	7.5	9.9%	51.95	68.4%	0.00
קומה א'	39.04	51.4%			39.04	51.4%	11.57
קומה ב'	26.40	34.7%			26.40	34.7%	2.40
סה"כ מעל הקרקע	109.89	144.6%	7.5	9.9%	117.39	154.5%	13.97
סה"כ מתחת לקרקע	0	0					
סה"כ	109.89	144.6%	7.5	9.9%	117.39	154.5%	13.97

סה"כ שטחים מותרים: 112.10 מ"ר עיקרי, 119.6 סה"כ.

COLD

ז. מספר יחידות דיור

מספר הדירות המבוקשות: 1 (מעל ל- 120 מ"ר)
מספר הדירות המותרות: 1

ח. פרטי הבנייה - לשימוש הבקשה המרכזית לסטטיסטיקה

השימוש	מספר בניינים	מספר קומות	מספר דירות	שטח הבנייה מ"ר
דירת מגורים	1	1	4	109.89
סך כל שטח הבנייה	1	1		109.89

ט. הבקשה מוגשת לאישור

☒ הועדה המקומית

י. הצהרת עורך הבקשה הראשי

אורנת זוהר, תאריך 20-05-2001

יא. חתימות נוספות

	שם	תאריך
המבקש	גורדון ג'ינתהן	5-06-2001
בעל הזכות בנכס	סושניק גוליין	5-06-2001
מתכנן שלד הבניין	סגל מיכאל	5-06-2001

יב. שינויים מטעם מבקש ההיתר

אני ממנה בזה את אורנת זוהר בעל/ת מס' זהות 13041496 הרשום בסעיף א' להיות עורך הבקשה הראשי להיתר.

שם משפחה ושם פרטי	תחום פעולה	המען	מספר טלפון	מספר פקס
1. מרקוביץ' מרינלה	מתכנן האינסטלציה הסניטרית	רח' גונן 5 ת.ד. 7497 קרית מטלון פתח - תקוה 49160	03-9234941/2	03-9234945
2. פיונטר יוסי	מתכנן חשמל	רח' סירקין 15 א גבעתיים	03-6701652	03-6739688

אני ממנה בזה את סגל מיכאל בעל/ת מס' זהות 6903184 הרשום בסעיף א' להיות אחראי לתכנון שלד הבניין.

☒ אני מצהיר, כי פרט מינויו אחראי/ם לביצוע עבודות הבנייה בתחומים האלה : כל התחומים

תחום פעולה
אחראי ראשי

☒ אני מצהיר כי פרט מינויי אחראי/ם לביקורת על ביצוע עבודות הבנייה בתחומים האלה : כל התחומים

חתימת המבקש פל המינויים X

יג. הצהרות

שם משפחה ושם פרטי	מספר רישיון	התאריך
אורנת זוהר	23050	2-06-2001
מרקוביץ' מרינלה	10230	
סגל מיכאל	09036	
פיונטר יוסי	47064	

סגל מיכאל, מס' זהות 6903184, מהנדס בעל רישיון מס' 09036, תאריך 30-05-2001

[illegible] שינוקו [illegible]
[illegible] מטעם על הבניה [illegible]
[illegible] [illegible] [illegible]
כי הועדה [illegible]

נחמה עמירב
אחראית תכנון סביבתי
הרשות לאיכות הסביבה
13.2.02