22 בן11160

עיריית תל-אביב-יפו
מינהל ההנדסה
נתקבל
01-08-2001
במחלקת בקרה ותיעוד

עיריית תל-אביב-יפו
מינהל ההנדסה, אגף רישוי ופיקוח על הבנייה

לכבוד
☒ הוועדה המקומית לתכנון ולבנייה
☐ רשות הרישוי המקומית

חוק התכנון והבנייה, התשכ"ה-1965
תקנות התכנון והבנייה (בקשה להיתר תנאיו ואגרות) התש"ל-1970

בקשה להיתר בנייה או לשימוש במקרקעין - בניין חדש

מס' תיק הבניין	מס' בקשה קודמת להיתר בנייה	מס' הבקשה למידע	תאריך
4047-27	-	מ/210238	22-02-2001

א. פרטי הנכס והמבקשים

	רחוב	מס' בית	גוש	חלקה	
הכתובת	התשבי	27	6135	110 (חלק)	

הוראות התכנית החלות על המקום: U,IN2215,2215

	שם משפחה / שם פרטי	מס' זהות	רחוב ומספר בית / ישוב	מספר טלפון / פקס
מבקש 1	גורדון ג'ונתהן	309898773	רח' התשבי 27 תל - אביב	053-247447
בעל הזכות בנכס	סושניק גוליין	מס' דרכון: 101982845	בוסטון ארה"ב	
עורך הבקשה הראשי	אורדנת זוהר	13041496	בית צורי 12 ת"א 69122	03-5618868 03-5615675
מתכנן שלד הבניין	סגל מיכאל	6903184	רח' נתן ילין-מור 6 תל - אביב	03-5627020 03-5617999

ב. מהות הבקשה לבנייה חדשה
- ☒ הריסת מבנה קיים הכולל 1 קומות מגורים
- ☒ הקמת מבנה חדש הכולל:
- ☒ 3 קומות מגורים ובהן 1 יחידות דיור
- ☒ חדרי שירותים 1
- ☒ גינה
- ☒ שטחים מרוצפים
- ☐ גבולות המגרש גדר בגובה 1.80 מטר

ג. מפרט - תיאור הבקשה
תיאור הקיים על המגרש: בית בן קומה 1 המיועד להריסה
שימוש עיקרי: ☒ מגורים
סוג העבודה: ☒ הריסה ☒ בניין חדש

שטח הבנייה הכולל המבוקש	117.39 מ"ר
שטח המגרש / החלקה	112 לפי טאבו 76 לפי מודד מ"ר
אחוזי הבנייה	154.5 %

ד. חומרי הבנייה
- גמר: ☒ טיח; ☒ זכוכית; מתכת
- קירות: 7.60 מ"א

ה. השטחים המבוקשים לבנייה

הקומה/המפלס	מבוקש (מ"ר)	% משטח המגרש	שטחי שירות מ"ר	%	סה"כ
קרקע	44.45	58.5%	7.5	9.9%	51.95 (68.4%)
קומה א'	39.04	51.4%			39.04 (51.4%)
קומה ב'	26.40	34.7%			26.40 (34.7%)
סה"כ מעל הקרקע	109.89	144.6%	7.5	9.9%	117.39 (154.5%)
סה"כ	109.89	144.6%	7.5	9.9%	117.39 (154.5%)

שטחים לא מקוריים: 0.00; 11.57; 2.40; סה"כ 13.97; 119.6

ו. קווי בניין

הכיוון	מוצע	מותר	הסטייה
לרחוב (שם) התשבי	0	0	0
צד צפון	0	0	0
צד דרום	0	0	0
לאחור מזרח	3	3	0

ז. מספר יחידות דיור
מספר הדירות המבוקשות: 1
מספר הדירות המותרות: 1

ח. פרטי הבנייה - לשימוש הלשכה המרכזית לסטטיסטיקה
למגורים: דירת מגורים — 1 — 1 — 4 — 109.89
סה"כ שטחי הבנייה: 1 — 1 — 109.89

ט. הבקשה מוגשת לאישור: ☒ הוועדה המקומית

י. הצהרת עורך הבקשה הראשי
אדר' אורדנת זוהר — 20-05-2001
אורדנת זוהר, אדריכלית ומעצבת פנים, רח' בית צורי 12 ת"א 69122

יא. חתימות נוספות

	שם	תאריך
המבקש	גורדון ג'ונתהן	5-06-2001
בעל הזכות בנכס	סושניק גוליין	5-06-2001
מתכנן שלד הבניין	סגל מיכאל	5-06-2001

יב. מינויים מטעם מבקש ההיתר
אני ממנה בזה את אורדנת זוהר בעל/ת מס' זהות 13041496
אני ממנה בזה את סגל מיכאל בעל/ת מס' זהות 6903184
מהנדס רשוי מס' 09036

שם משפחה ושם פרטי	תאריך
אורדנת זוהר	2-06-2001
מרקוביץ' מרינלה	2-06-2001
סגל מיכאל	2-06-2001
פיינר יוסי	2-06-2001

אינג' מיכאל סגל, מהנדס בניין, ת"א רח' נתן ילין מור 6, טל. 5627020

תל-אביב-יפו מפה טופוגרפית

מס' סדורי 2073 / 2000
ק.מ. 1 : 250
שכונת התקוה
גוש : 6135
חלקה 110 (חלק)
רח' תשבי 27

הוכן עבור: סושניק גוליין
מהות הבקשה: התר בניה
שטח לפי נסח טאבו: 112 מ"ר
שטח מדוד: 76 מ"ר

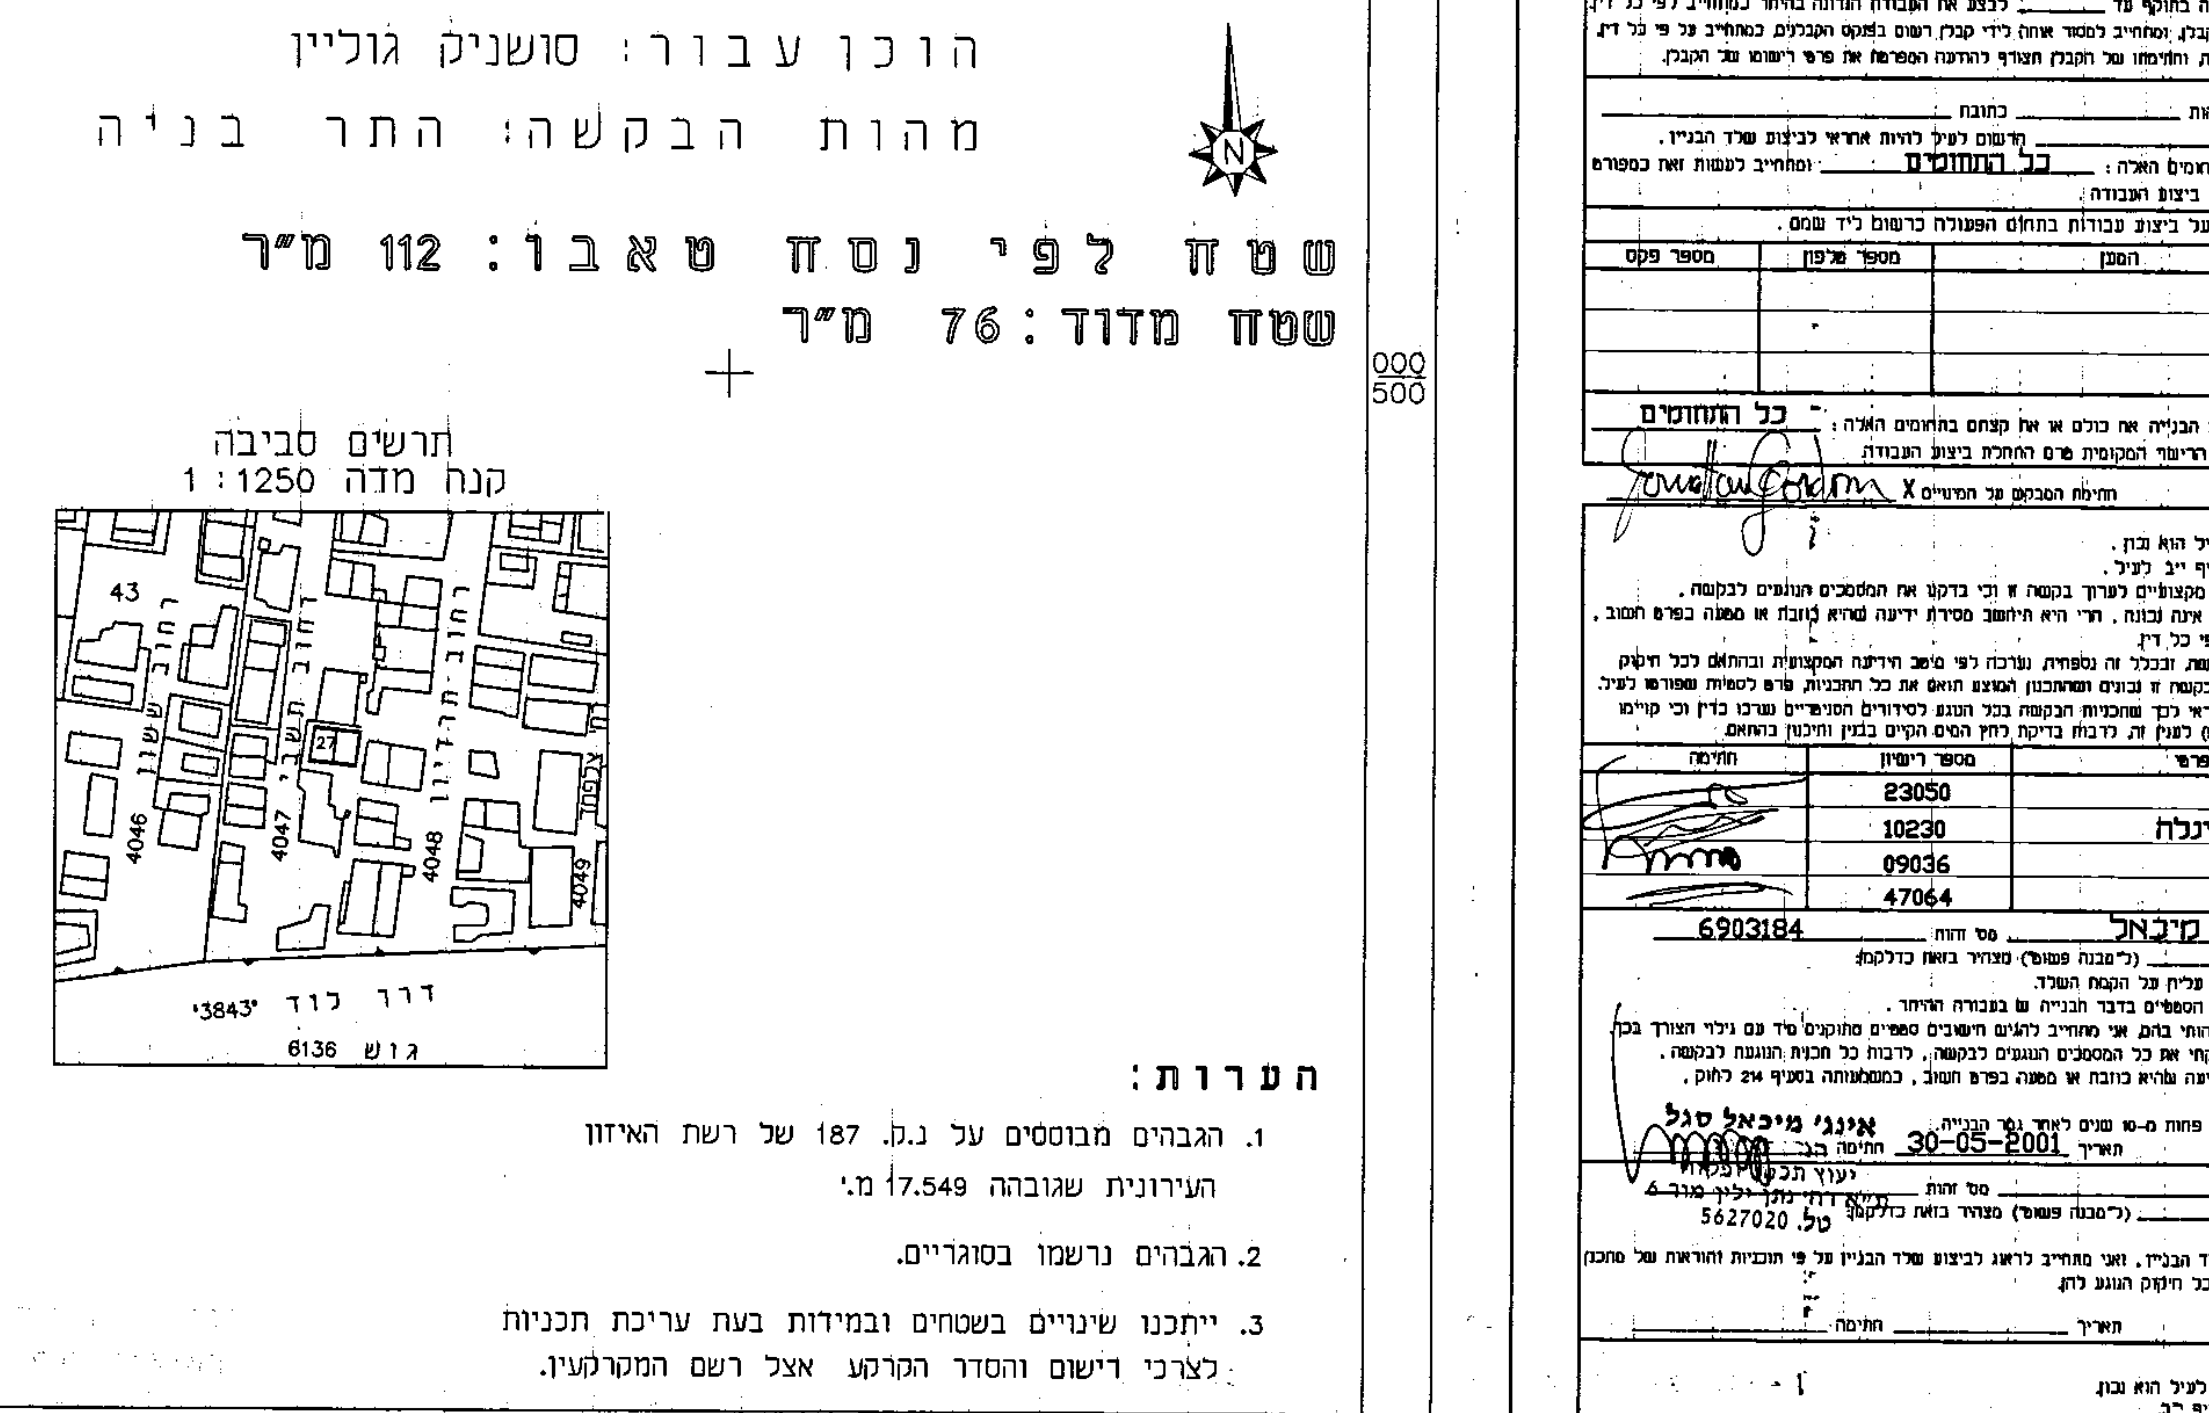

ק/1
3/ק
2/ק
מגרש ריק
רח' תשבי
10.55
"20"
N
תרשים סביבה
קנה מדה 1:1250
רח' לוד
גוש 6136

לא לצרכי רישום
הנני מצהיר בזה שהמפה נעשתה לפי חוק התכנון והבניה, התקנות וההנחיות של עיריית תל אביב יפו

תל-אביב 8.11.2000 מודד מוסמך
ראובן לאופר - מודד מוסמך מס' רשיון 574
משרד מכני למדידות
משרד: רח' הרכבת 20 תל - אביב טל': 03-5608221
מען: רח' בורלא 32 תל - אביב טל': 03-6993398

הערות:
1. הגבהים מבוססים על נ.ג. 187 של רשת האיזון העירונית שגובהה 17.549 מ'.
2. הגבהים נרשמו בסוגריים.
3. ייתכנו שינויים בשטחים ובמידות בעת עריכת תכניות לצרכי רישום והסדר הקרקע אצל רשם המקרקעין.

מפת איתור העבודה (תרשים מגרש)

תל-אביב-יפו מפה טופוגרפית

מס' סדורי 2073 / 2000
ק.מ. 1 : 250
שכונת התקוה
גוש : 6135
חלקה 110 (חלק)
רח' תשבי 27

הוכן עבור: סושניק גוליין
מהות הבקשה: התר בניה
שטח לפי נסח טאבו: 112 מ"ר
שטח מדוד: 76 מ"ר

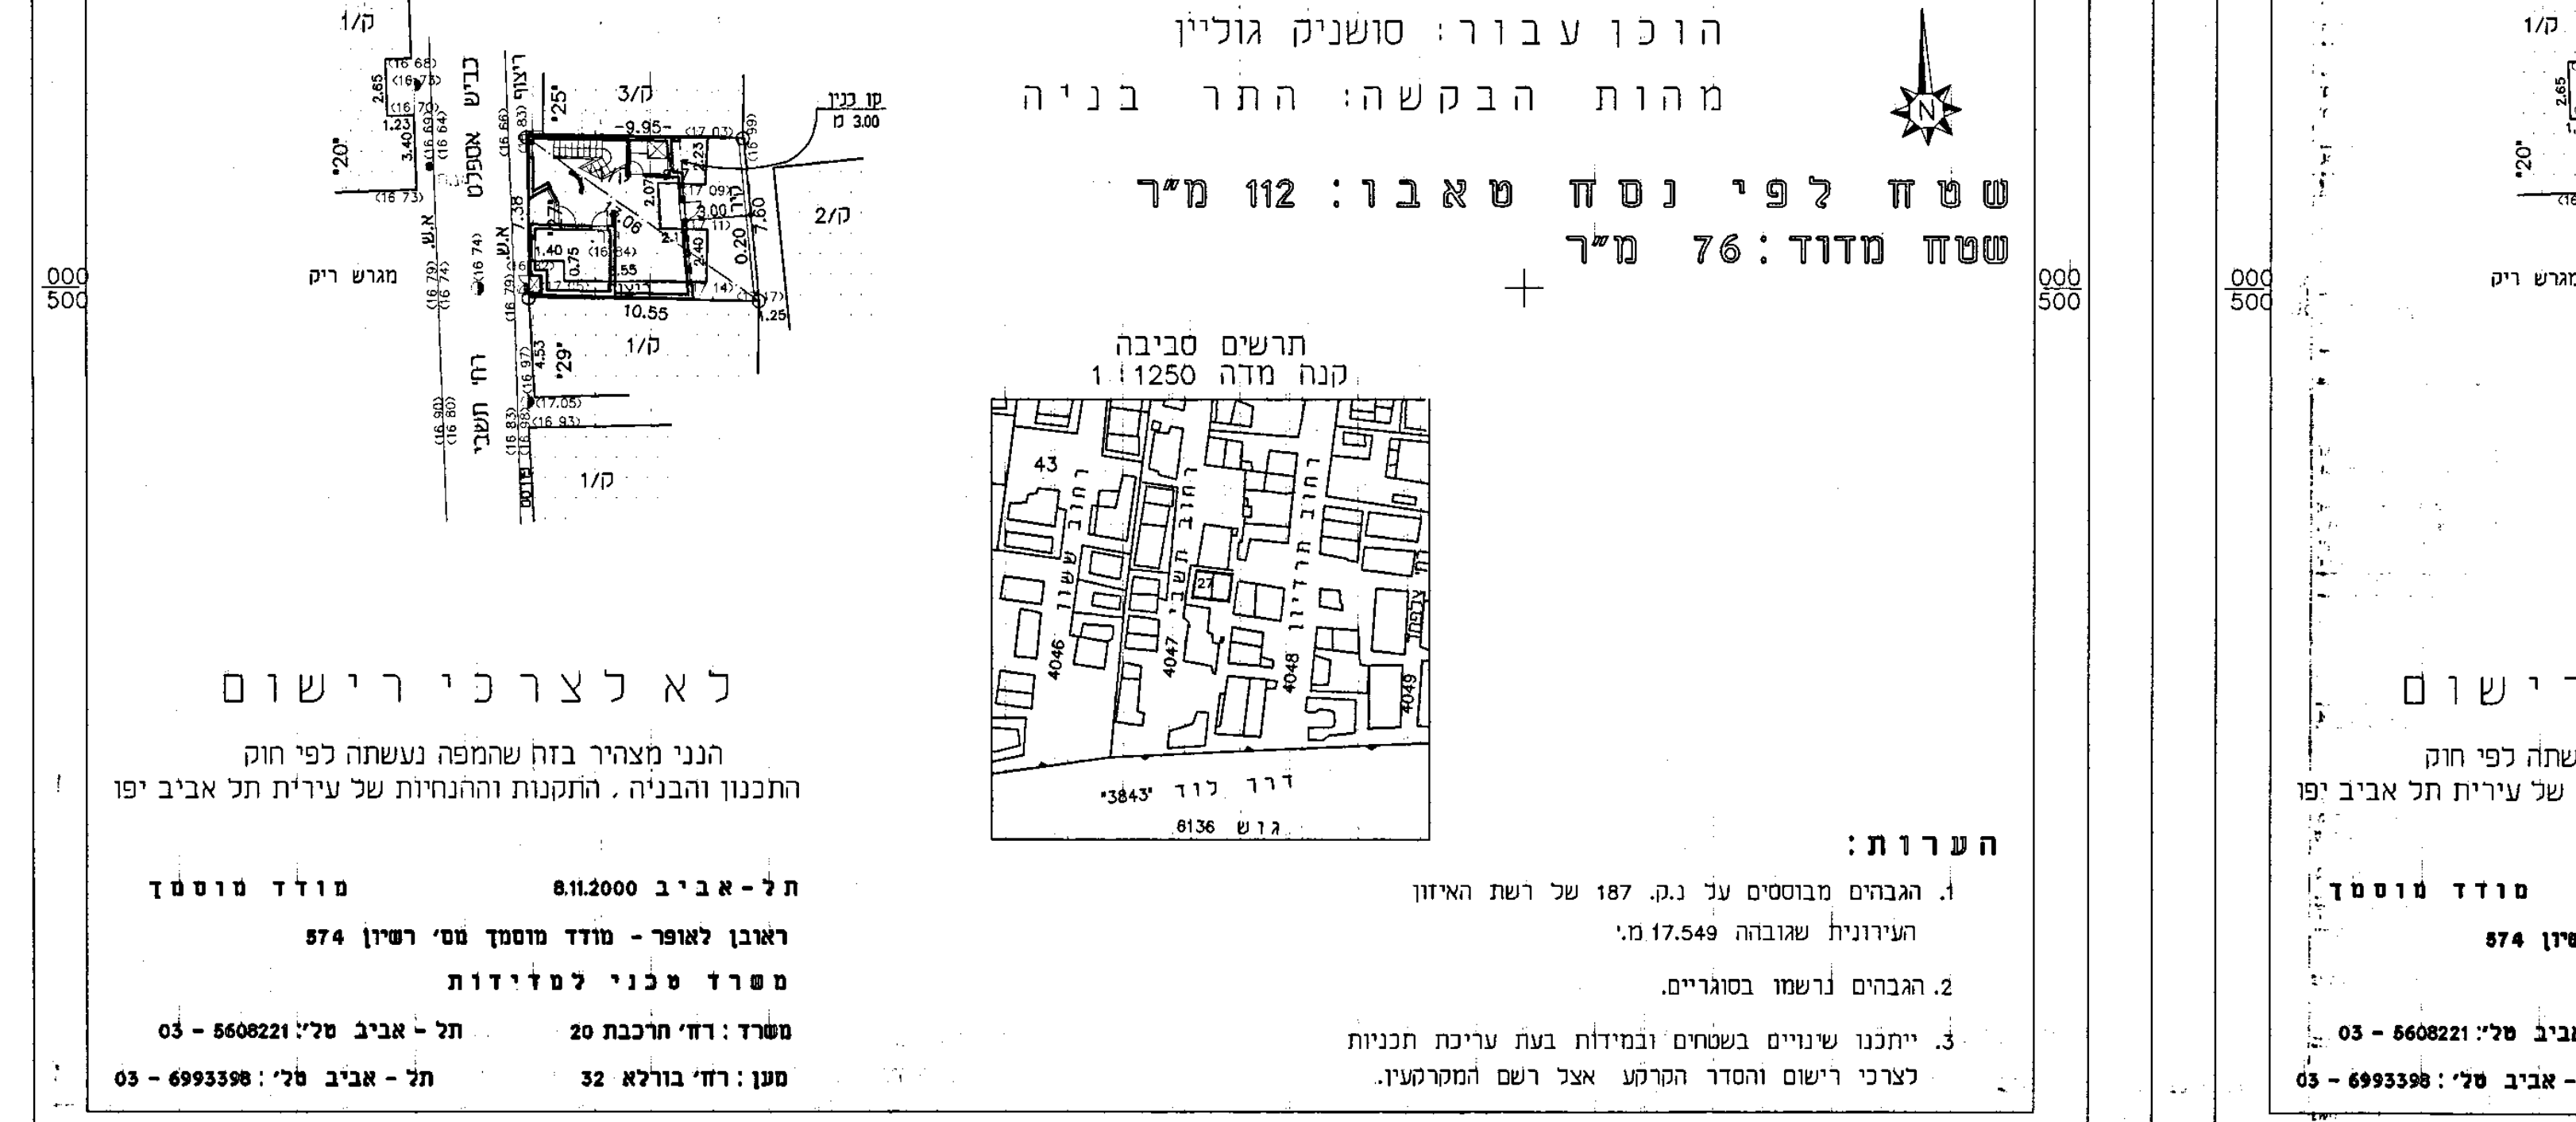

ק/1
3/ק
2/ק
מגרש ריק
רח' תשבי
N
תרשים סביבה
קנה מדה 1:1250
רח' לוד
גוש 6136

לא לצרכי רישום
הנני מצהיר בזה שהמפה נעשתה לפי חוק התכנון והבניה, התקנות וההנחיות של עיריית תל אביב יפו

תל-אביב 8.11.2000 מודד מוסמך
ראובן לאופר - מודד מוסמך מס' רשיון 574
משרד מכני למדידות
משרד: רח' הרכבת 20 תל - אביב טל': 03-5608221
מען: רח' בורלא 32 תל - אביב טל': 03-6993398

הערות:
1. הגבהים מבוססים על נ.ג. 187 של רשת האיזון העירונית שגובהה 17.549 מ'.
2. הגבהים נרשמו בסוגריים.
3. ייתכנו שינויים בשטחים ובמידות בעת עריכת תכניות לצרכי רישום והסדר הקרקע אצל רשם המקרקעין.

תכנית העמדה

תשריט סכימטי של שטחי הבניה
ק.מ. 1:100

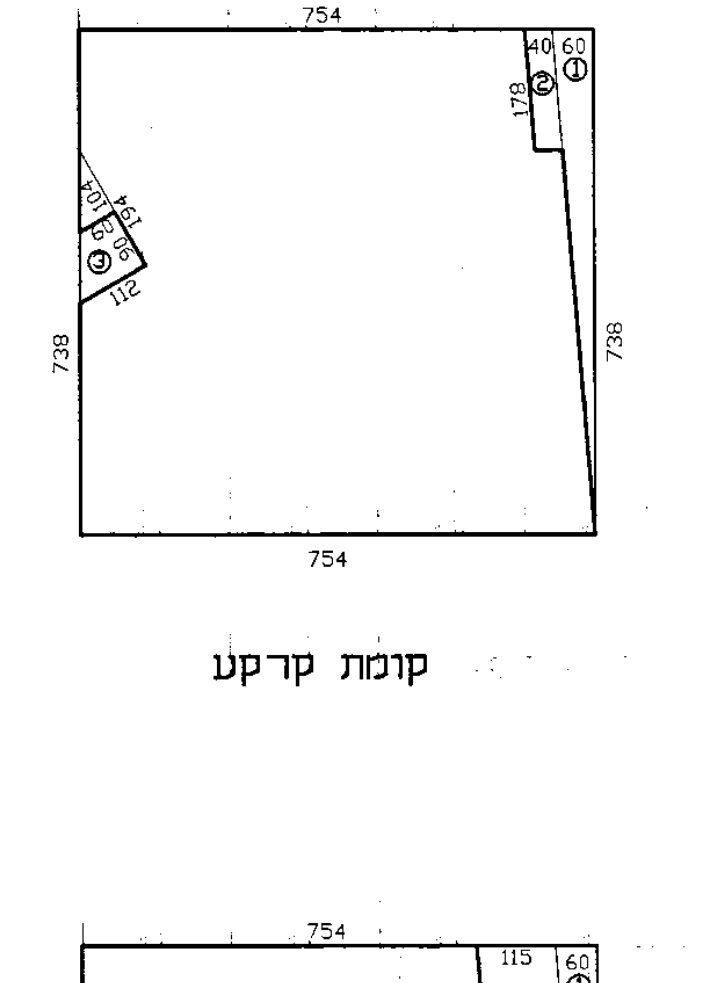
קומת קרקע

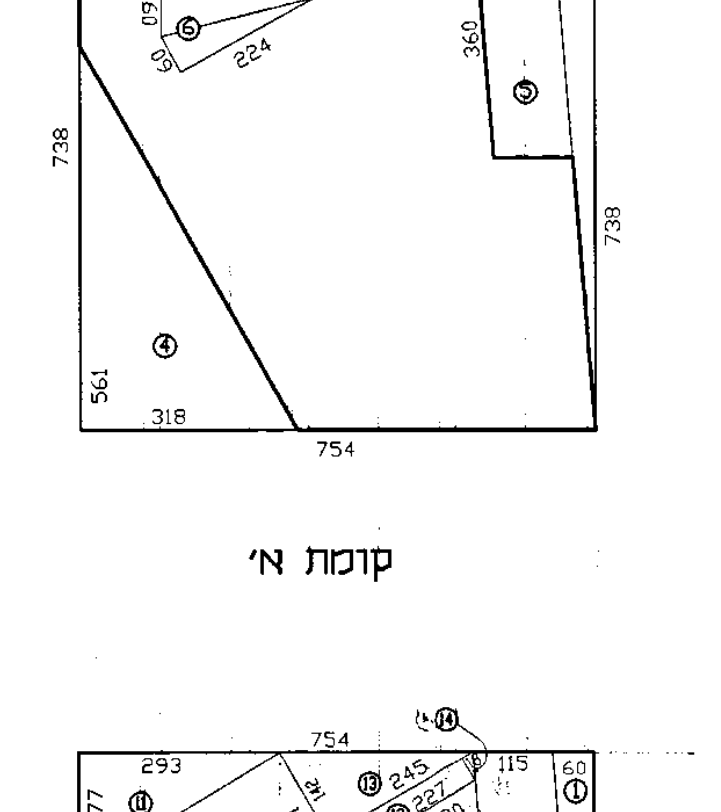
קומת א'

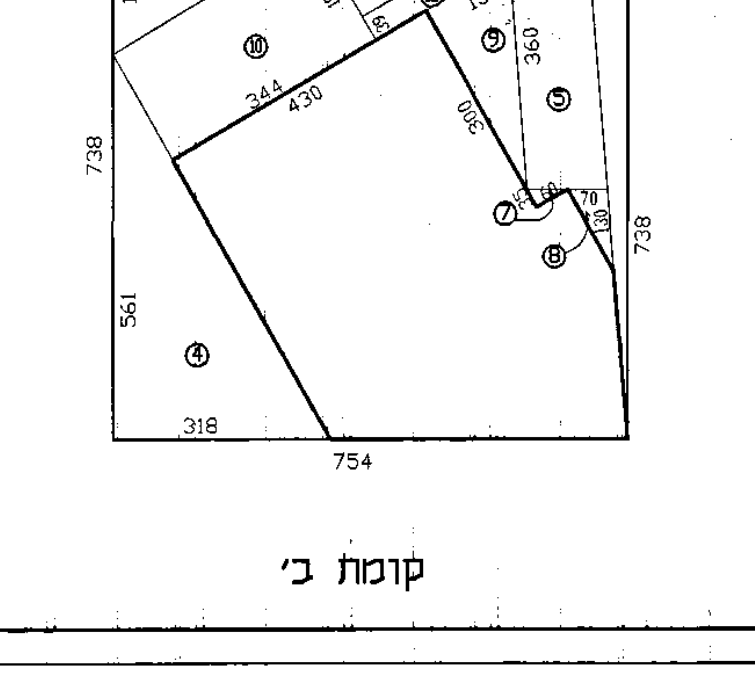
קומת ב'

חישוב שטח קומת קרקע
1. חישוב שטח מסגרת
7.38 × 7.54 = 55.65
2. הורדות
① (7.38 × 0.60) : 2 = 2.21
② 1.78 × 0.40 = 0.71
③ (1.12×1.94):2 - (0.60×1.04):2 = 0.78
סה"כ 3.70 מ"ר
3. חישוב שטח שירות 7.5 מ"ר
סה"כ שטח שירות: 7.5 מ"ר
4. חישוב שטח עיקרי - קומת קרקע
55.65 - 3.70 - 7.5 = 44.45 מ"ר

חישוב שטח קומה א'
1. חישוב שטח מסגרת
7.38 × 7.54 = 55.65
2. הורדות
① (7.38 × 0.60) : 2 = 2.21
④ (5.61×3.18) : 2 = 8.92
⑤ 1.15 × 3.60 = 4.14
⑥ (2.24×0.60):2×2 = 1.34
סה"כ 16.61 מ"ר
4. חישוב שטח עיקרי - קומה א'
55.65 - 16.61 = 39.04 מ"ר

חישוב שטח קומה ב'
1. חישוב שטח מסגרת
7.38 × 7.54 = 55.65
2. הורדות
① (7.38 × 0.60) : 2 = 2.21
④ (5.61×3.18):2 = 8.92
⑤ 1.15 × 3.60 = 4.14
⑦ (0.60×0.35):2 = 0.10
⑧ (1.30×0.70):2 = 0.45
⑨ (3.00×1.30):2 = 1.95
⑩ 3.44 × 1.81 = 6.22
⑪ (1.77×2.93):2 = 2.59
⑫ 0.39 × 2.27 = 0.89
⑬ (1.42 × 2.45):2 = 1.74
⑭ (0.39 × 0.18):2 = 0.04
סה"כ 29.25 מ"ר
4. חישוב שטח עיקרי - קומה ב'
55.65 - 29.25 = 26.40 מ"ר

סה"כ שטח עיקרי
44.45 + 39.04 + 26.40 = 109.89

סה"כ שטח (עיקרי+שרות)
109.89 + 7.5 = 117.39

שטחים לא מקוריים קומה א':
④+⑤-②-③ = 8.92+4.14-0.71-0.78 = 11.57
שטחים לא מקוריים קומה ב':
⑦+⑧+⑨ = 0.10+0.45+1.95 = 2.40
סה"כ שטחים לא מקוריים (מרפסות):
= 13.97

חישוב תכסית:

סה"כ שטח קומת קרקע: 55.65 - 3.70 = 51.95 מ"ר
סה"כ שטח מגרש: 76 מ"ר
תכסית: 51.95 : 76 = 0.68 %

חישוב זכוית בניה
לפי ת.ב.ע. מס' 2215

שטח המגרש לפי נסח טאבו:	112 מ"ר
שטח המגרש לפי מדידה על-ידי מודד מוסמך:	76 מ"ר
% הבניה המותרים לפי ת.ב.ע.:	140.0 %
תוספת % בניה עבור הריסת בית קיים:	7.5 %
שטח שרות עבור בנית ממ"ד:	7.5 מ"ר

חישוב סה"כ שטח בניה מותר:

76.0 × 1.4 =	106.4 מ"ר
76.0 × 0.075 =	5.7 מ"ר
סה"כ שטח עיקרי מותר:	112.1 מ"ר
(ממ"ד) 7.5 מ"ר =	7.5 מ"ר
סה"כ זכויות בניה מותרים: (עיקרי + שירות)	119.6 מ"ר

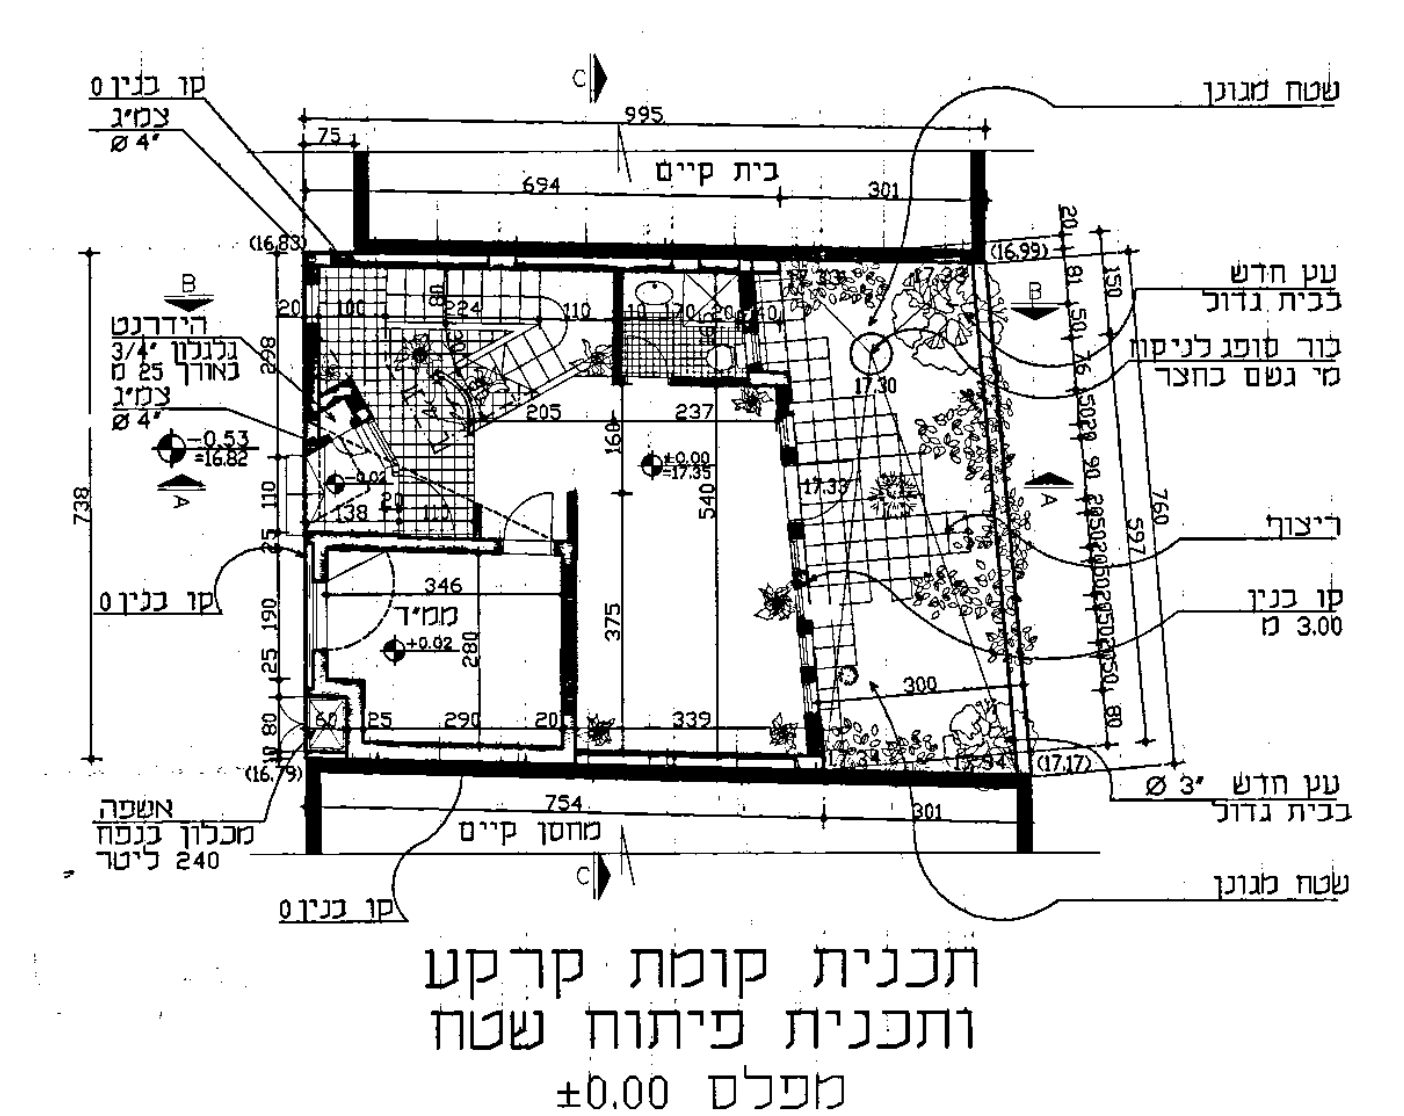

קו בניין
קו בניין 3.00 מ
שטח מגונן
עץ חדש בבית גדול
בור סופג לניקוז מי גשם בחצר
ריצוף
עץ חדש Ø 3" בבית גדול
ארונות
הידרנט
עציץ Ø 4"
מחסן קיים
אשפה
מכבון בנפח 240 ליטר
בית קיים

תכנית קומת קרקע ותכנית פיתוח שטח
מפלס ±0.00

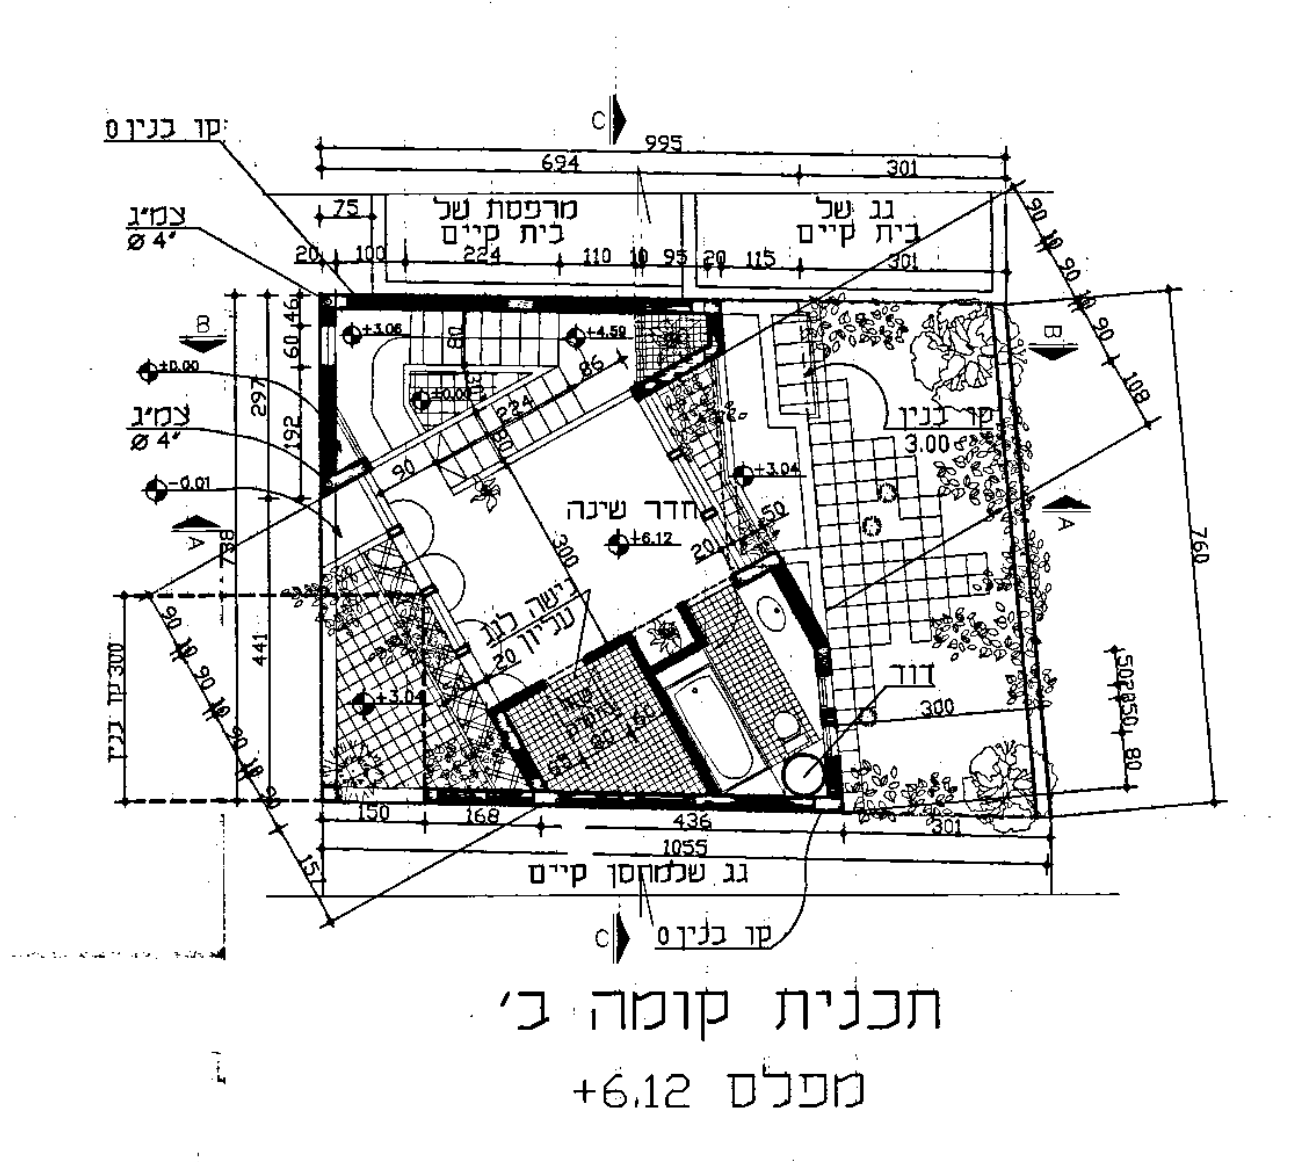

קו בניין
עציץ Ø 4"
מרפסת של בית קיים
גג גג בית קיים
חדר שינה
גג שלטונות
ממ"ד

תכנית קומה ב'
מפלס +6.12

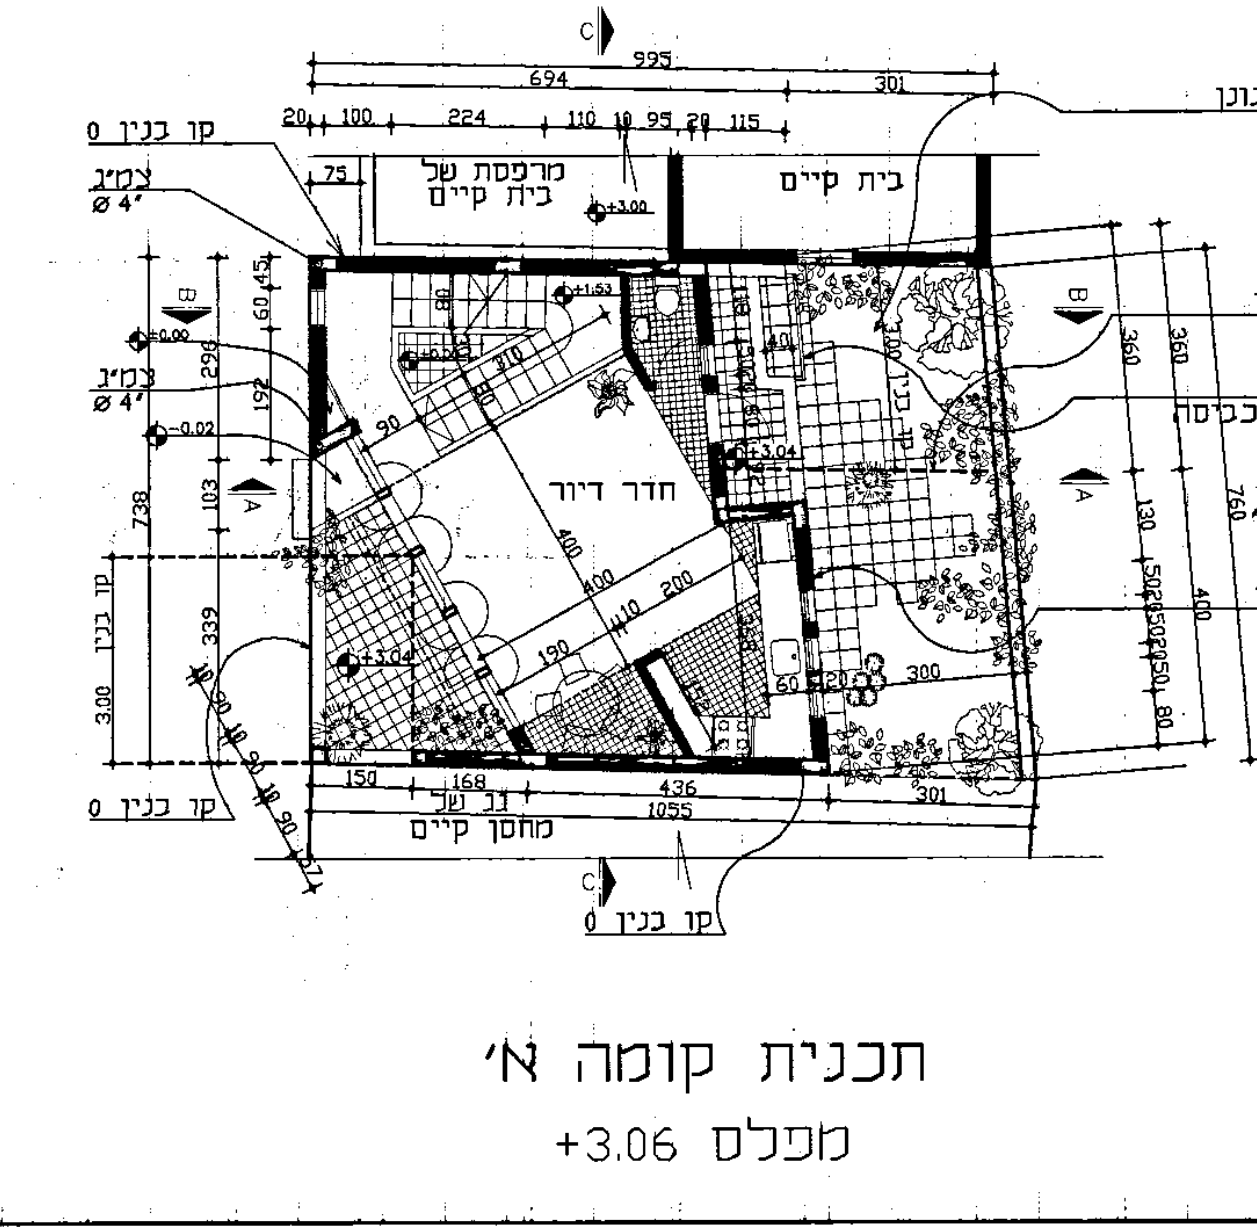

קו בניין
קו בניין 3.00 מ
מסתור לתלית כביסה
עציץ
חדר דיור
מחסן קיים
בית קיים

תכנית קומה א'
מפלס +3.06

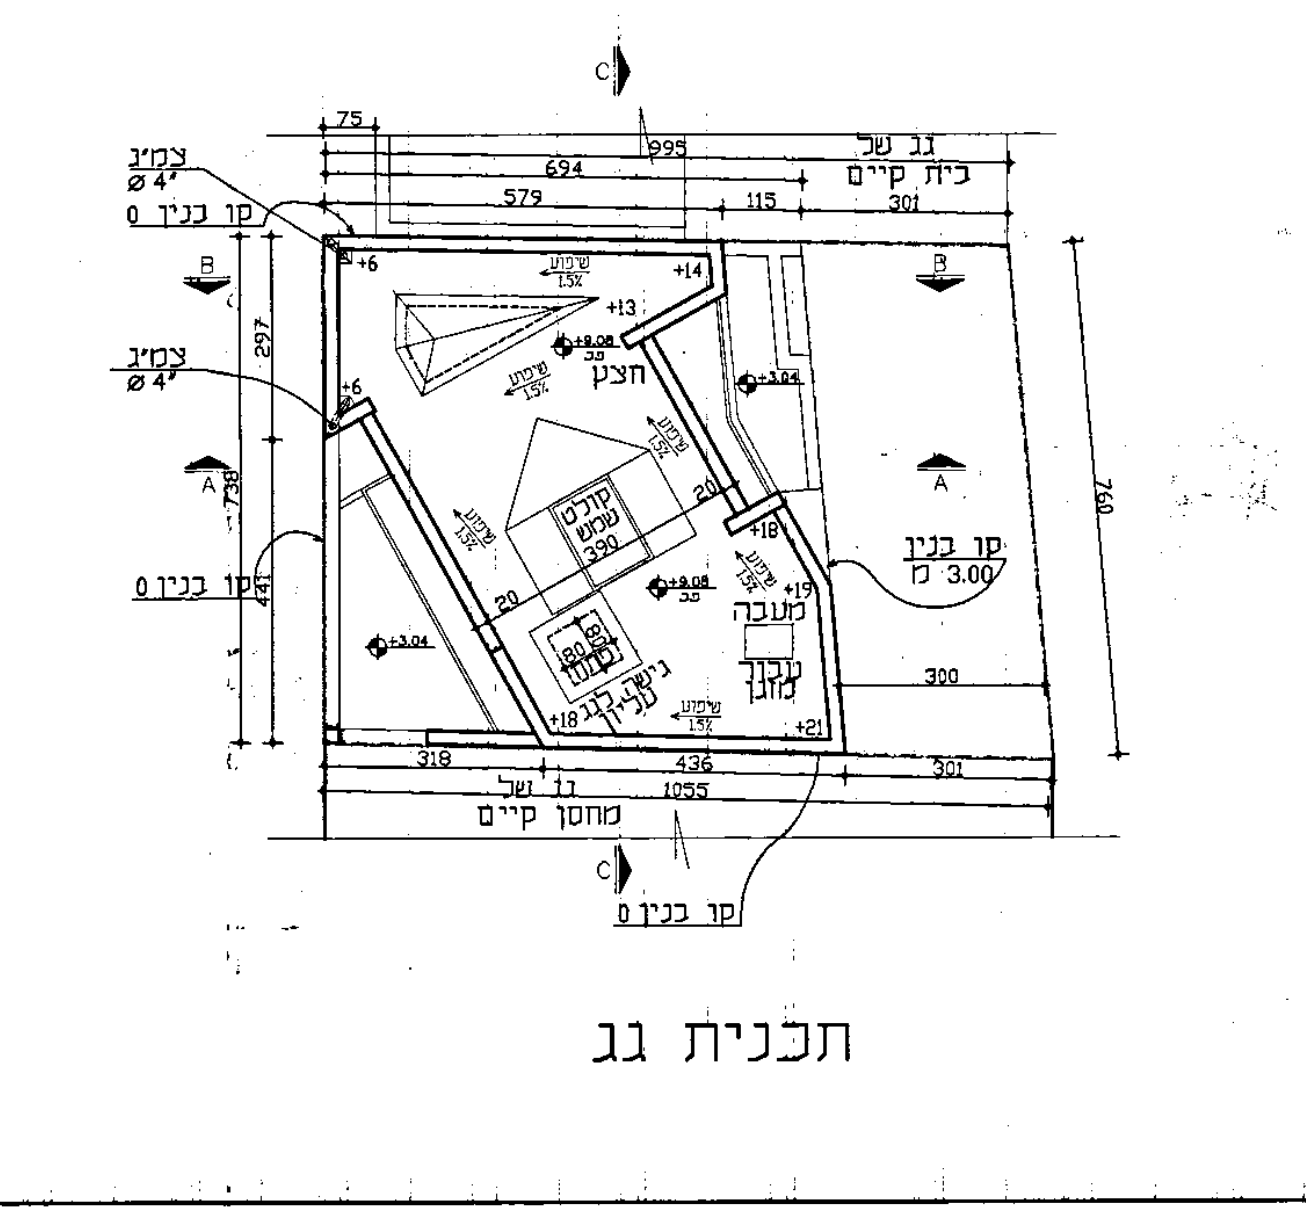

קו בניין
קו בניין 3.00 מ
גג
חובב
מחסן קיים

תכנית גג

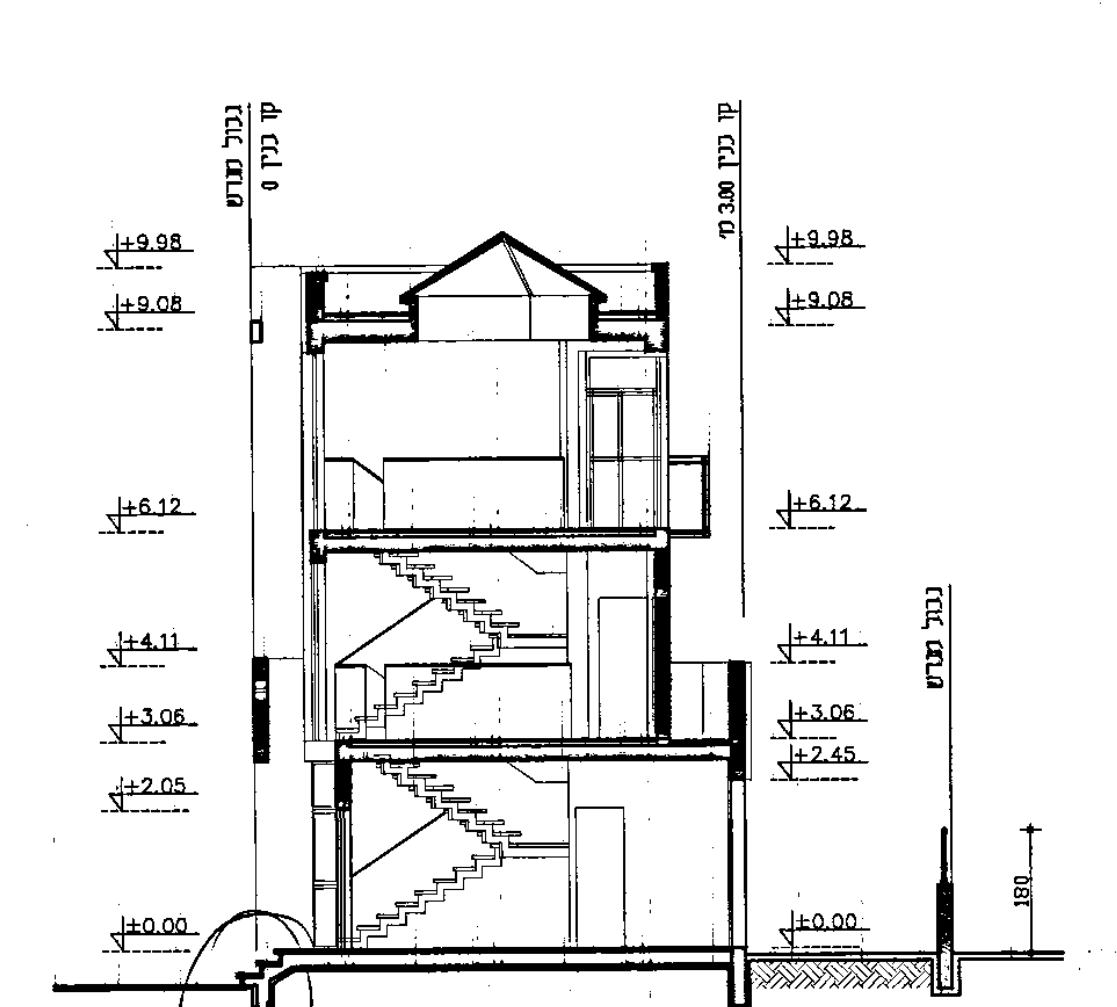

+9.98
+9.08
+6.12
+4.11
+3.06
+2.05
±0.00
קו בניין
גבול מגרש
303

חתך A-A

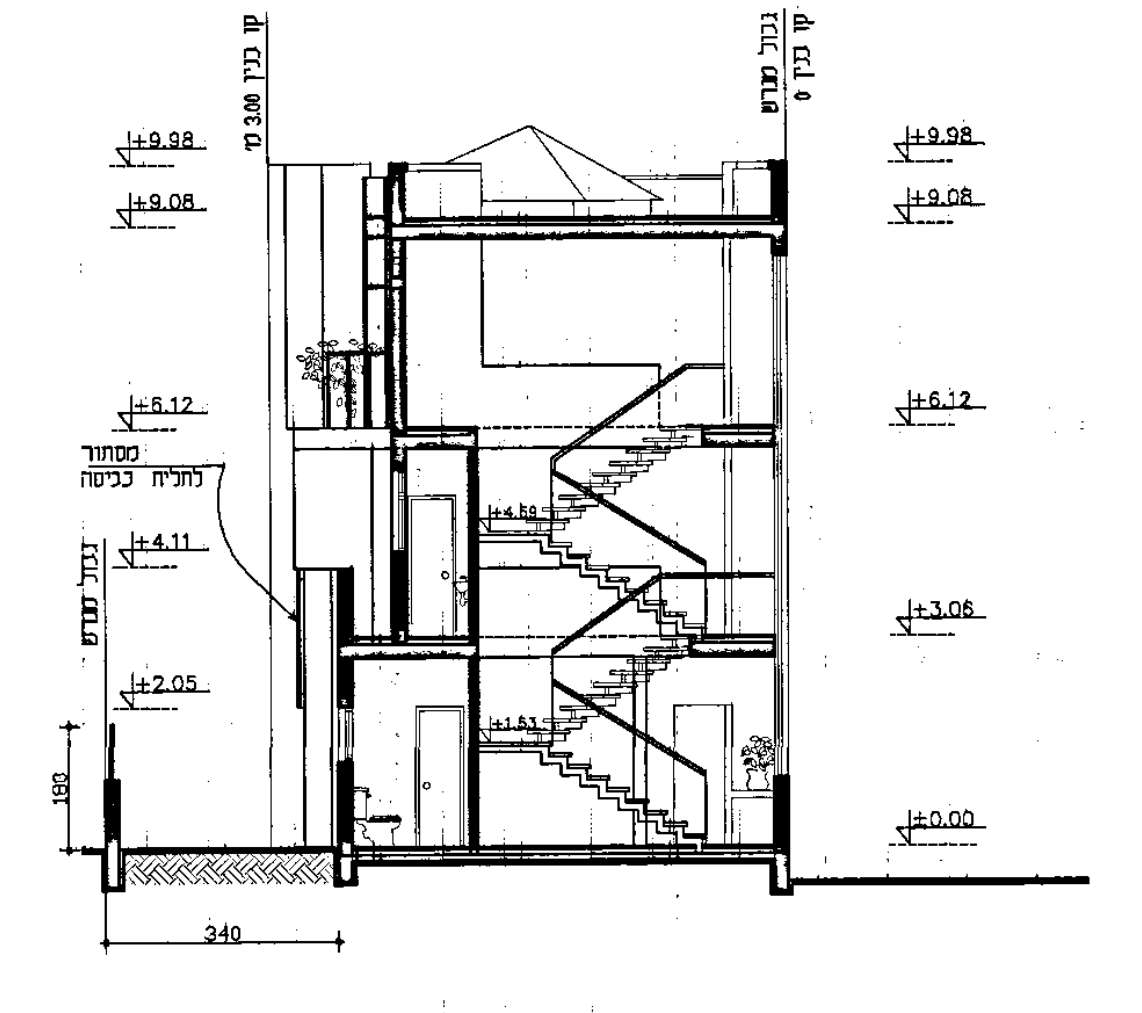

+9.98
+9.08
+6.12
+4.11
+2.05
±0.00
מחסן קיים
240

חתך B-B

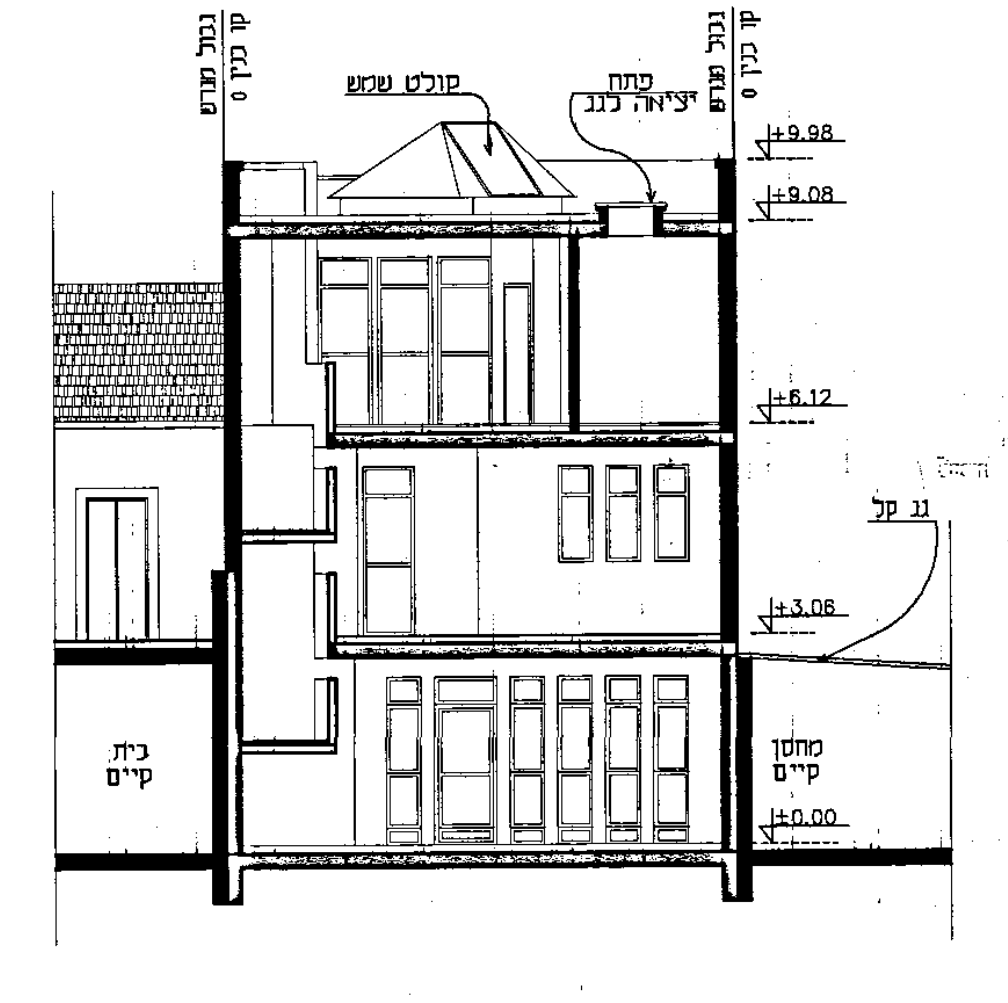

+9.98
+9.08
+6.12
+4.11
+3.06
±0.00
בית קיים
מחסן קיים

חתך C-C

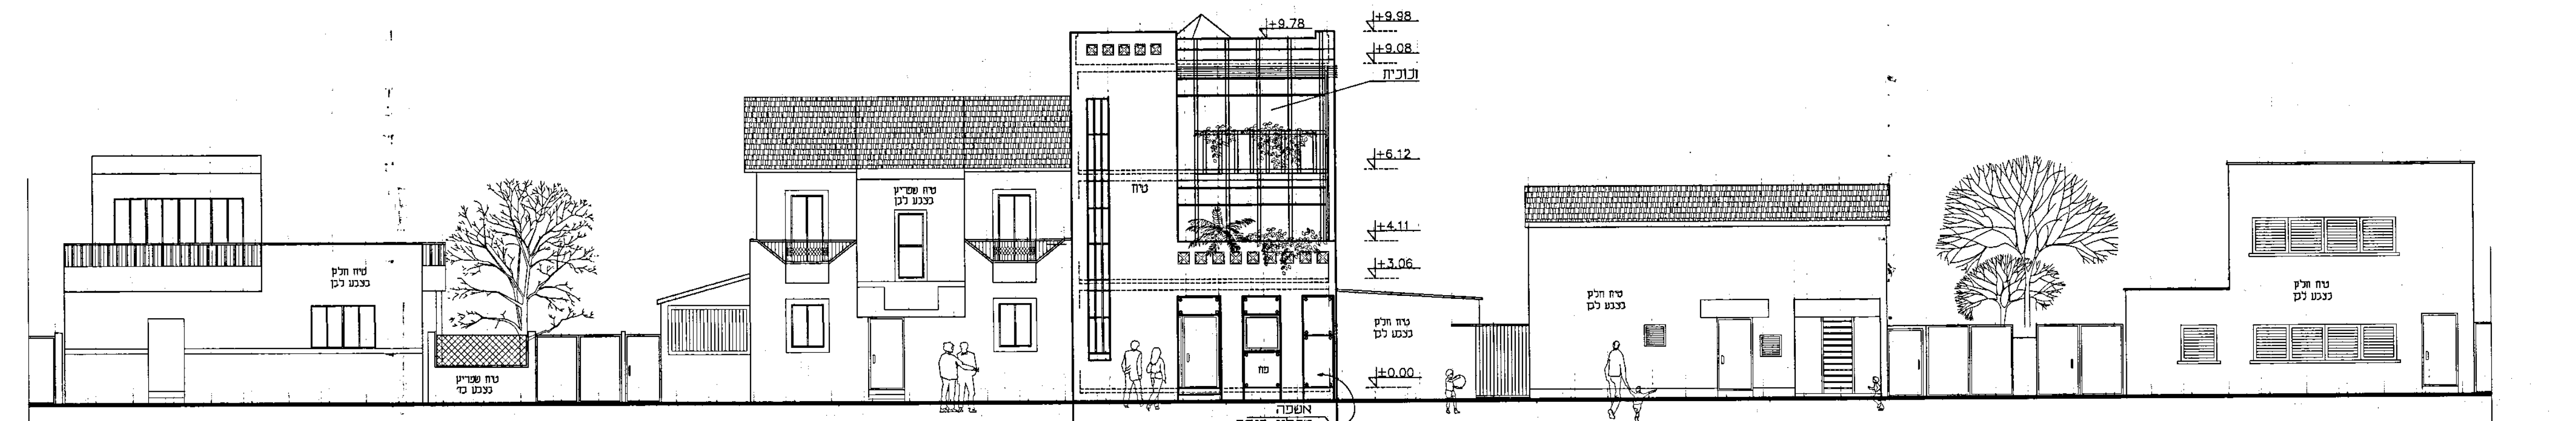

+9.98
+9.08
+6.12
+4.11
+3.06
+2.05
±0.00
טיח חלק בגוון לבן
אשפה
מכבון בנפח 240 ליטר
קיים
מוצע
קיים

חזית מערבית

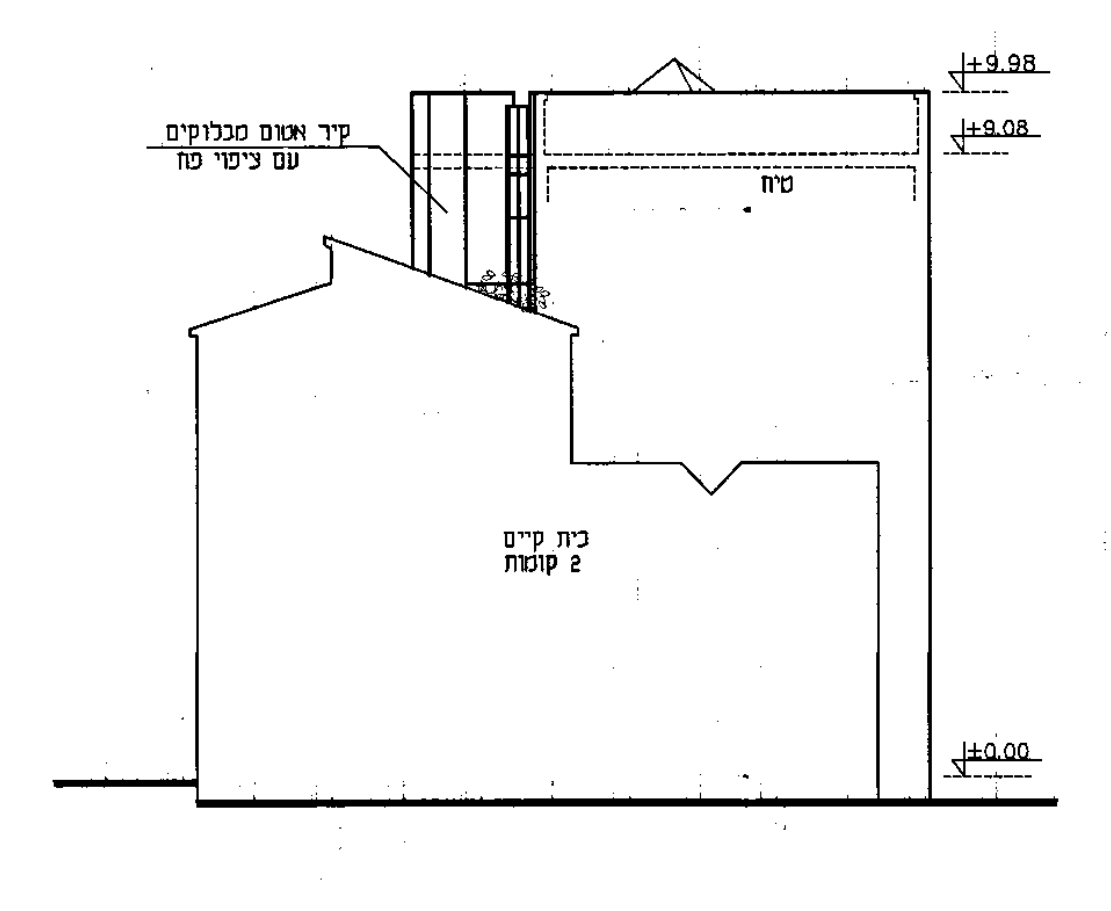

קיר אטום מבלוקים עם ציפוי טיח
בית קיים 2 קומות
±0.00
+9.98
+9.08

חזית צפונית

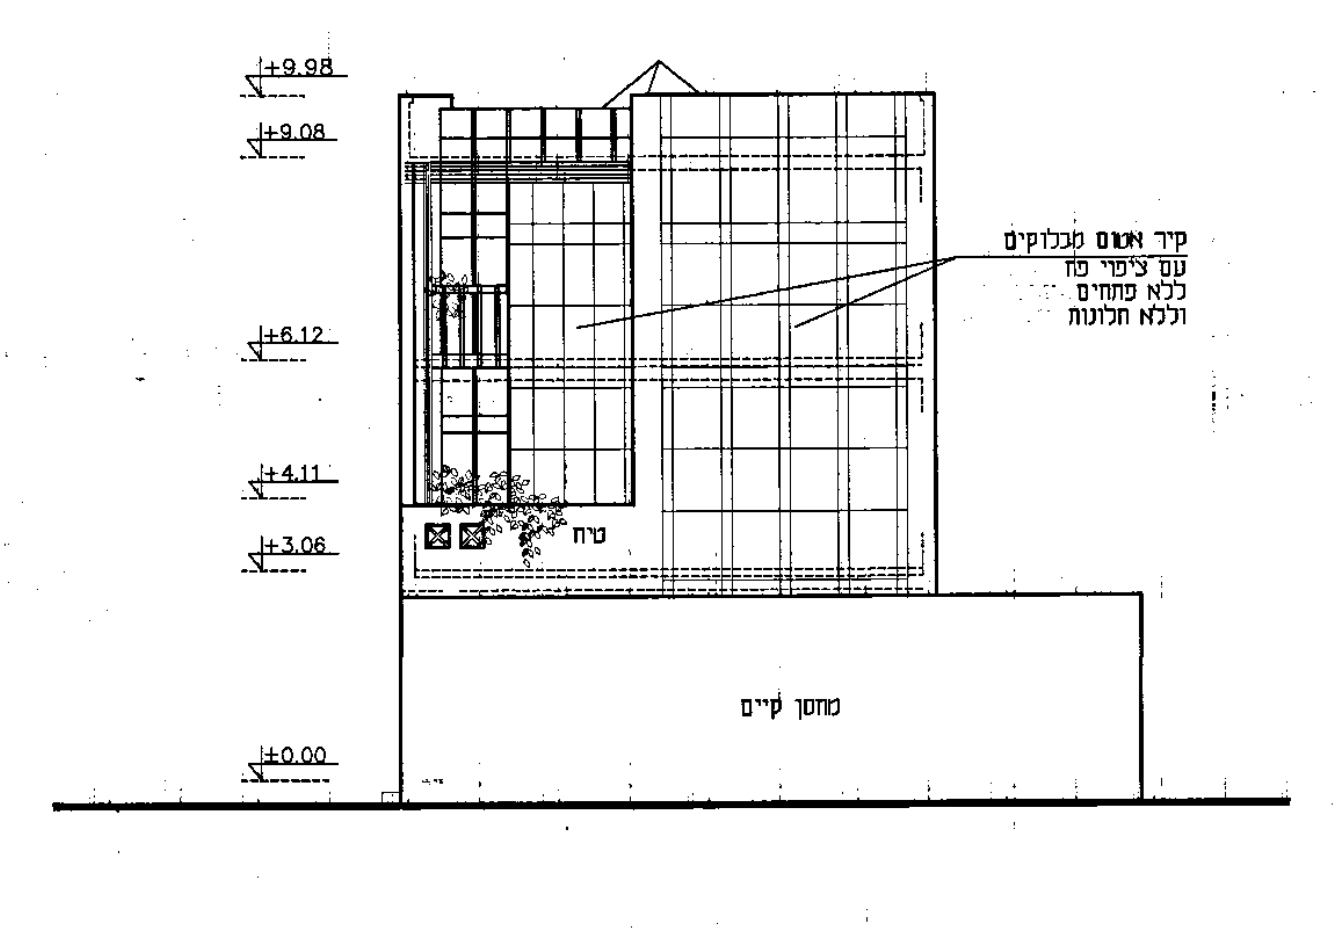

+9.98
+9.08
+6.12
+4.11
+3.06
±0.00
קיר אטום מבלוקים עם ציפוי טיח
מחסן קיים

חזית דרומית

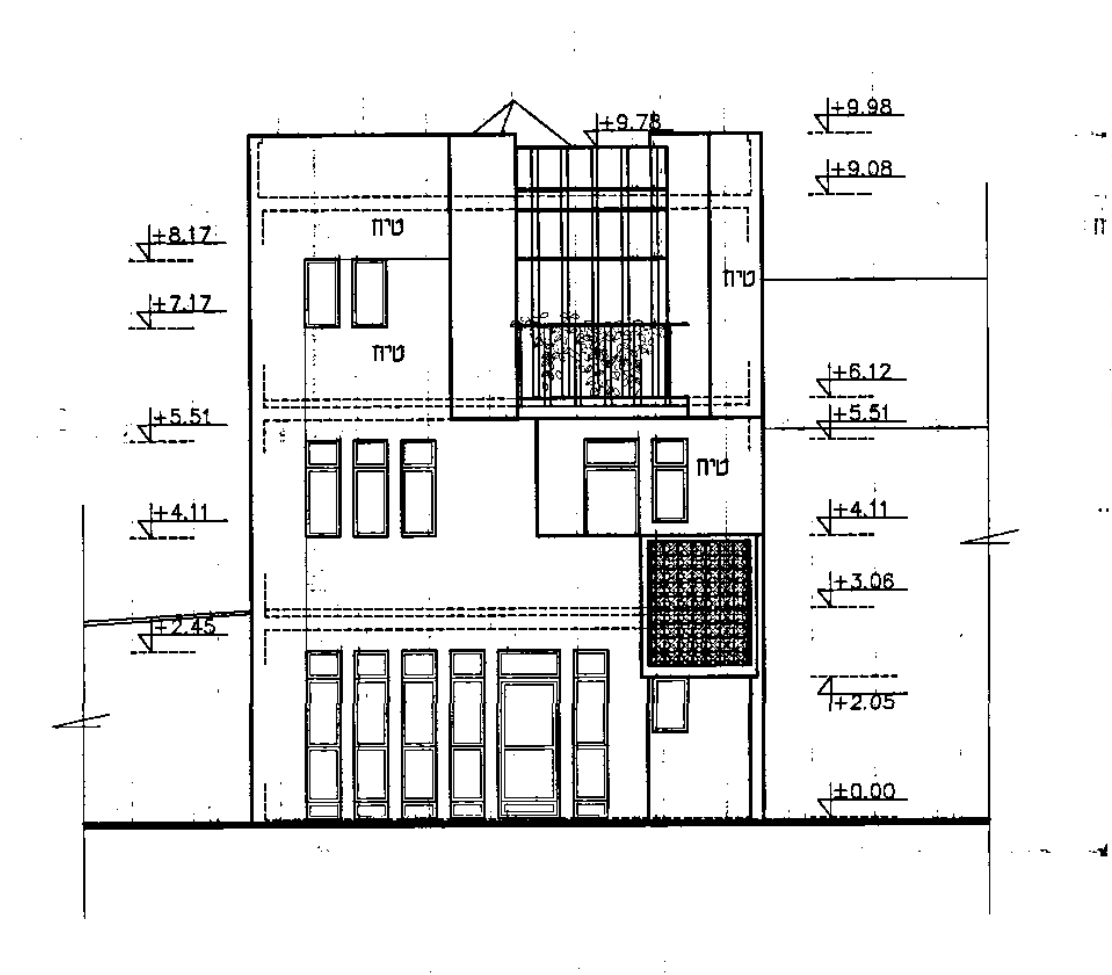

+9.98
+9.08
+8.17
+7.17
+6.12
+5.51
+4.11
+3.06
+2.05
±0.00
טיח

חזית מזרחית

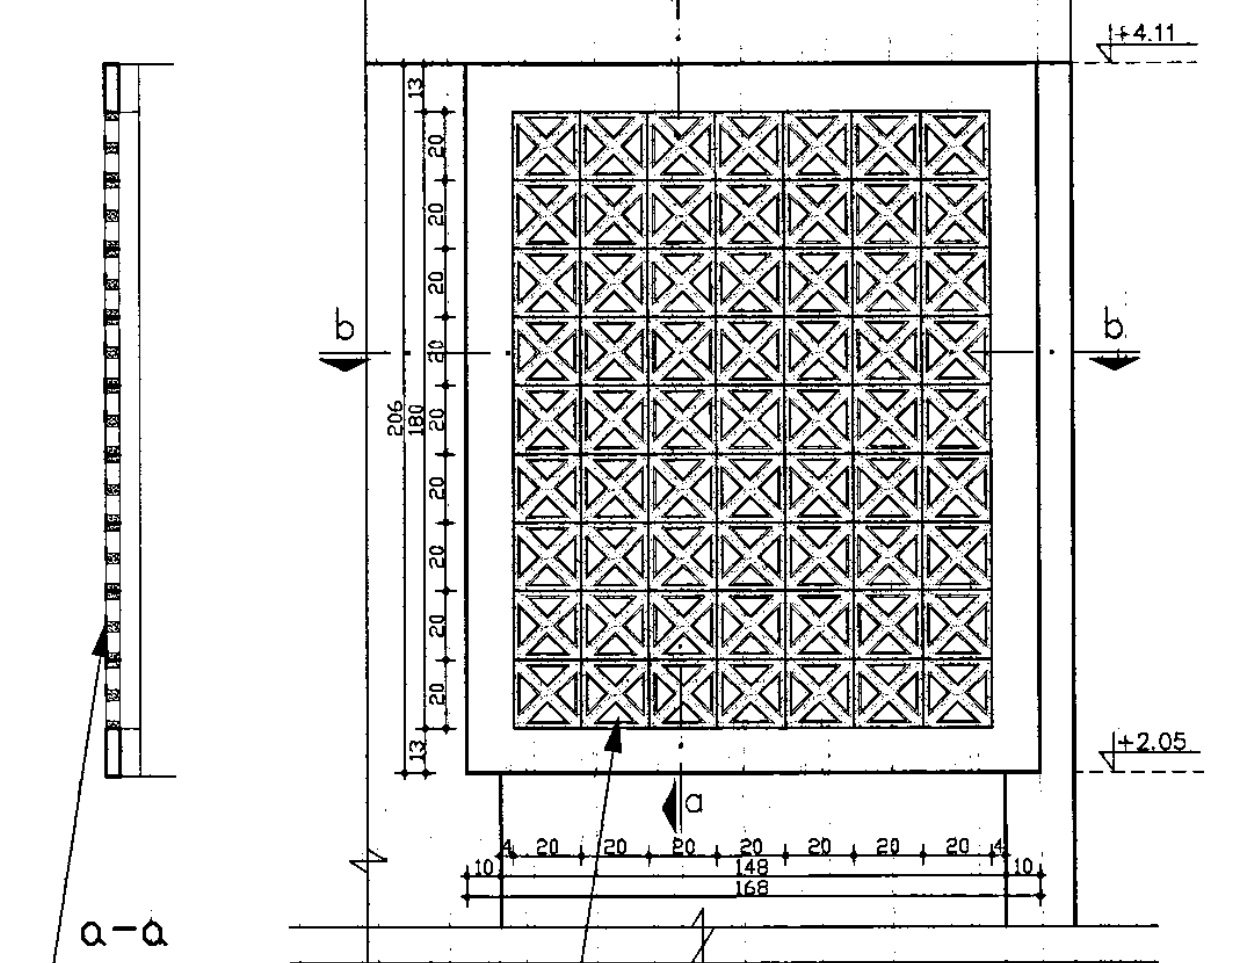

a-a
b-b
20×20 GRC
מסתור כביסה של אקורשטיין או גל תעשיות או שיש
+4.11
+2.05

מסתור כביסה
ק.מ. 1:20

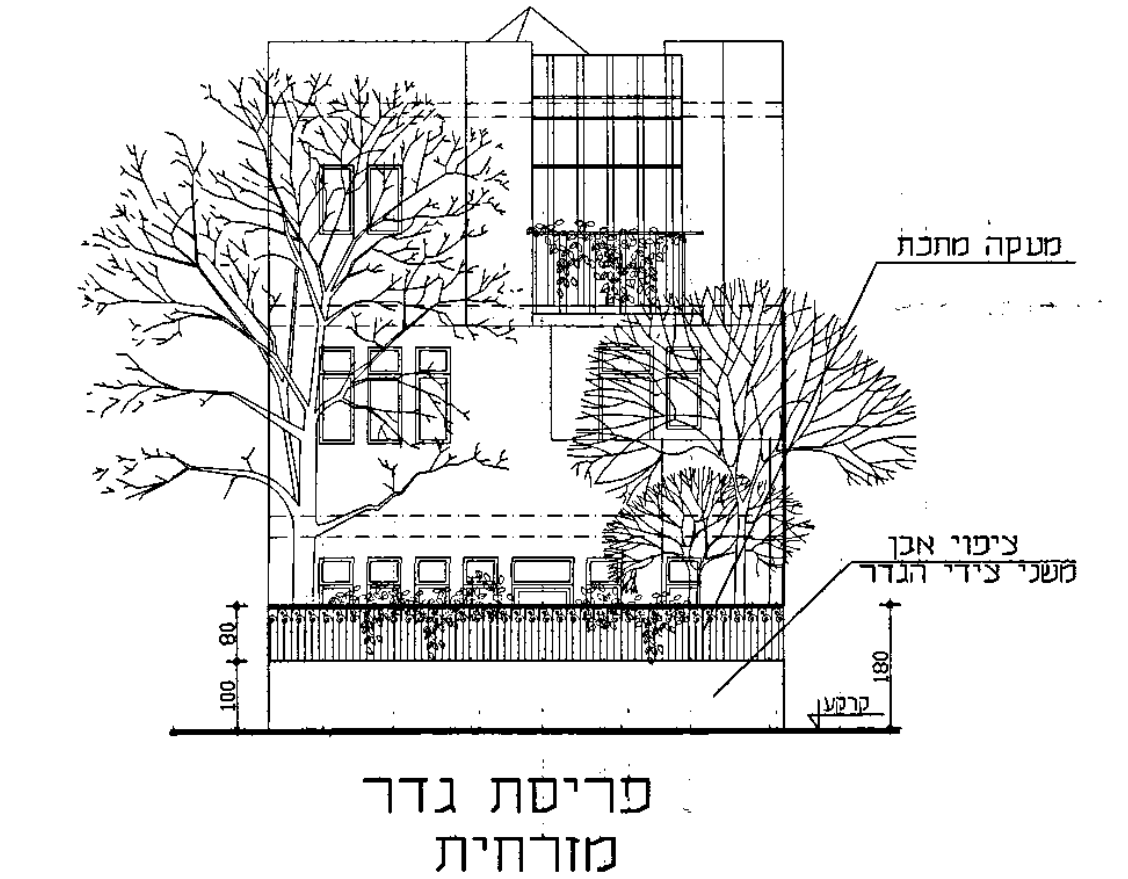

מעקה מתכת
ציפוי אבן
משני צידי הגדר

פריסת גדר מזרחית
ק.מ. 1:100

חישוב שטח ממ"ד
ק.מ. 1:50

1. חישוב שטח מסגרת
3.96 × 3.25 = 12.9
2. הורדות
⑥ 0.60 × 0.60 = 0.5
סה"כ הורדות 0.50 מ"ר
סה"כ שטח ממ"ד 12.40 מ"ר

מקרא:

ꟷ	בית תקע חשמל
⊚	טלפון
T.V.	בית תקע לאנטנה רדיו וטלביזיה
	מפסק
	גוף תאורה פלואורסצנטי 2 נורות 36 וואט בכתח 230 וולט
ח.כ.א.פ.	חלון בטחון אטום פנימי
ה.ה.ד.	חלון הדף דרתי
ד.ה.ד.	דלת הדף דרתי

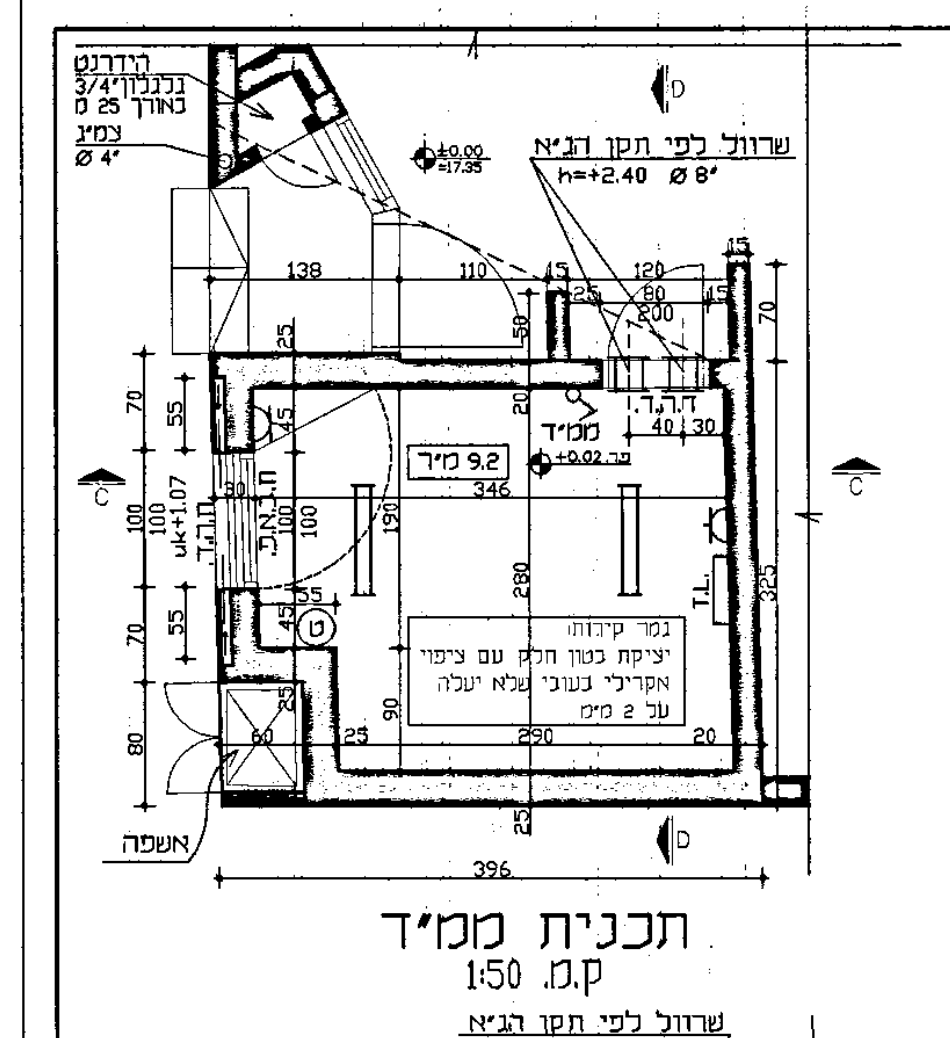

שרוול לפי תקן הג"א
h=+2.40 Ø 8"
ממ"ד 9.2 מ"ר
אשפה
296

תכנית ממ"ד
ק.מ. 1:50

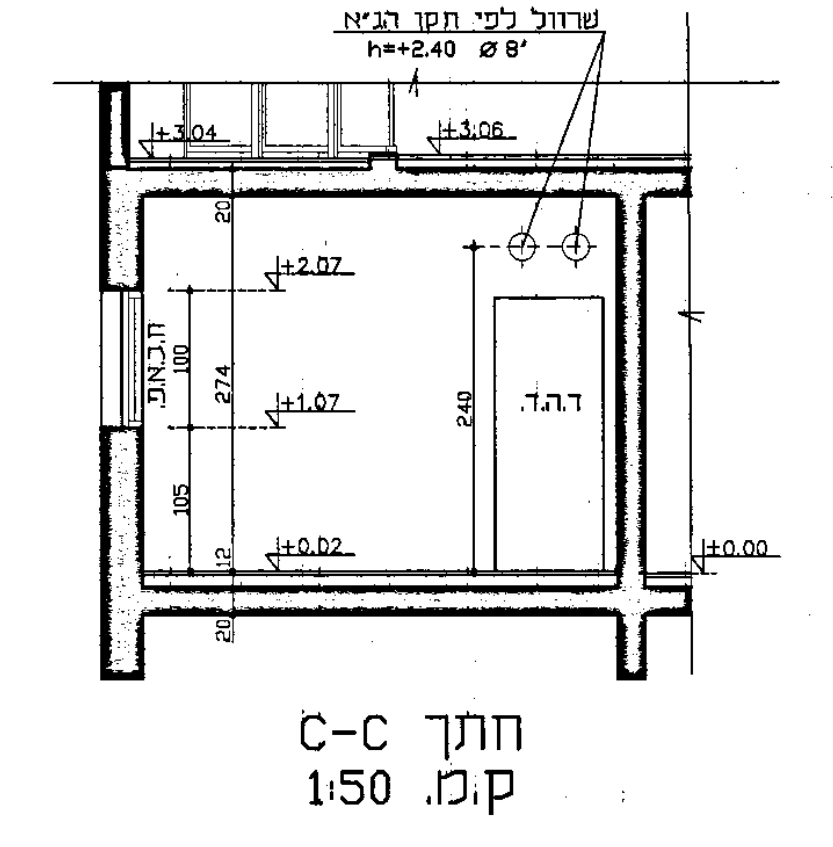

+3.04
+3.06
+2.07
+1.07
+0.02
±0.00
ד.ה.ד.

חתך C-C
ק.מ. 1:50

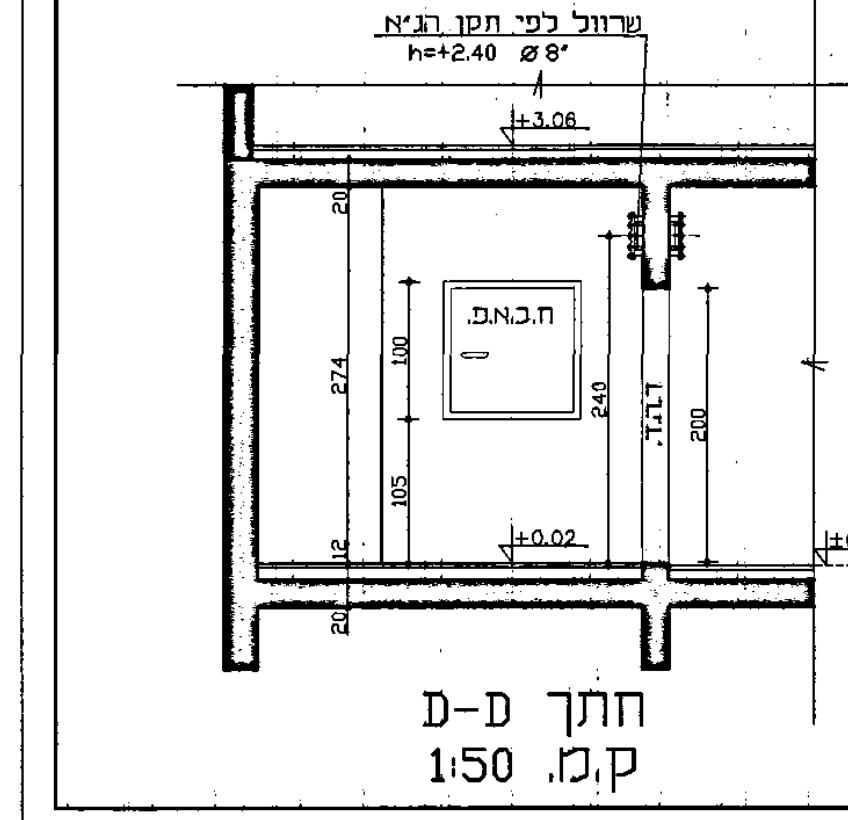

שרוול לפי תקן הג"א
h=+2.40 Ø 8"
ח.כ.א.פ.
+3.06
+0.02
±0.00

חתך D-D
ק.מ. 1:50

סוף המסמך