סוף המסמך

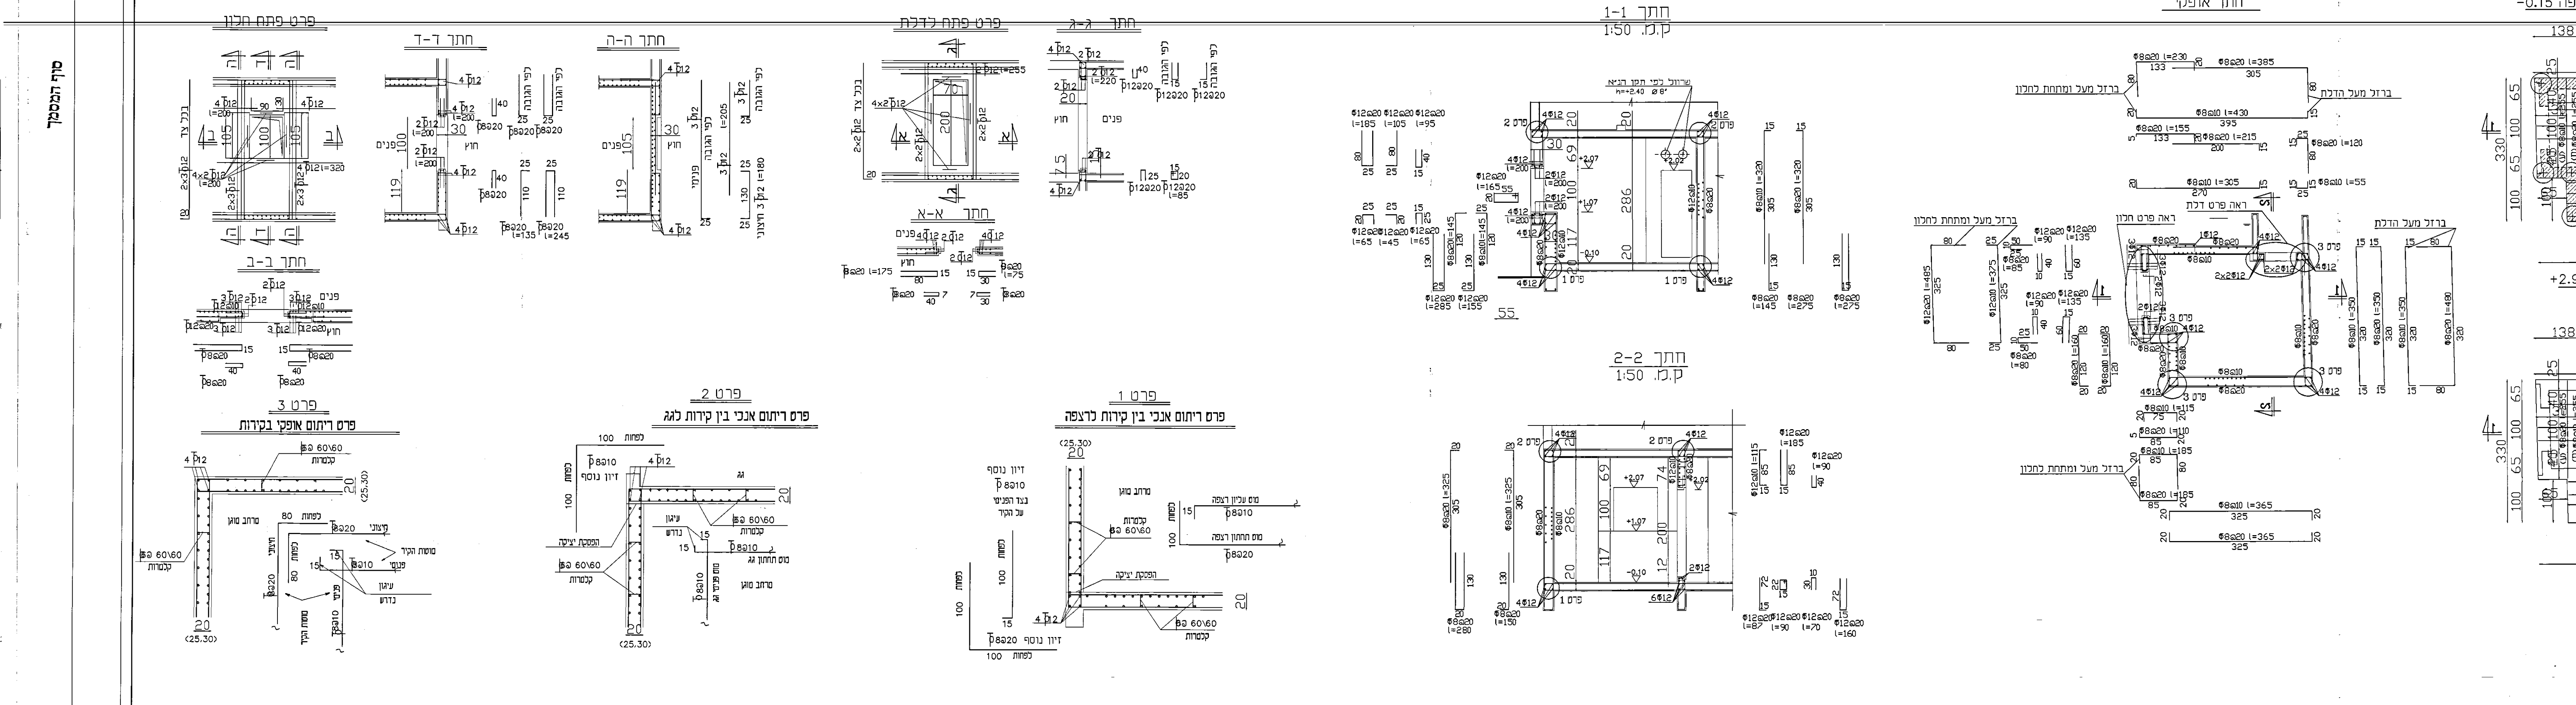

פרט פתח הגג
חתך ד-ד
חתך ה-ה
חתך ב-ב
פרט 3
פרט ריתום אפקי בקירות
פרט 2
פרט ריתום אנכי בין קירות לגג
חתך 1-1
ק.מ. 1:50
חתך 2-2
ק.מ. 1:50
פרט 1
פרט ריתום אנכי בין קירות לרצפה
פרט פתח לדלת
חתך ג-ג
חתך א-א
חתך אופקי
ברזל מעל ומתחת לחלון
ברזל מעל הדלת
תכנית רצפה -0.15
תכנית תקרה +2.96

רח' התשבי 27	
ת"א	
ממ"ד 1	
1715mmd	
1:25 1:50 קנים	

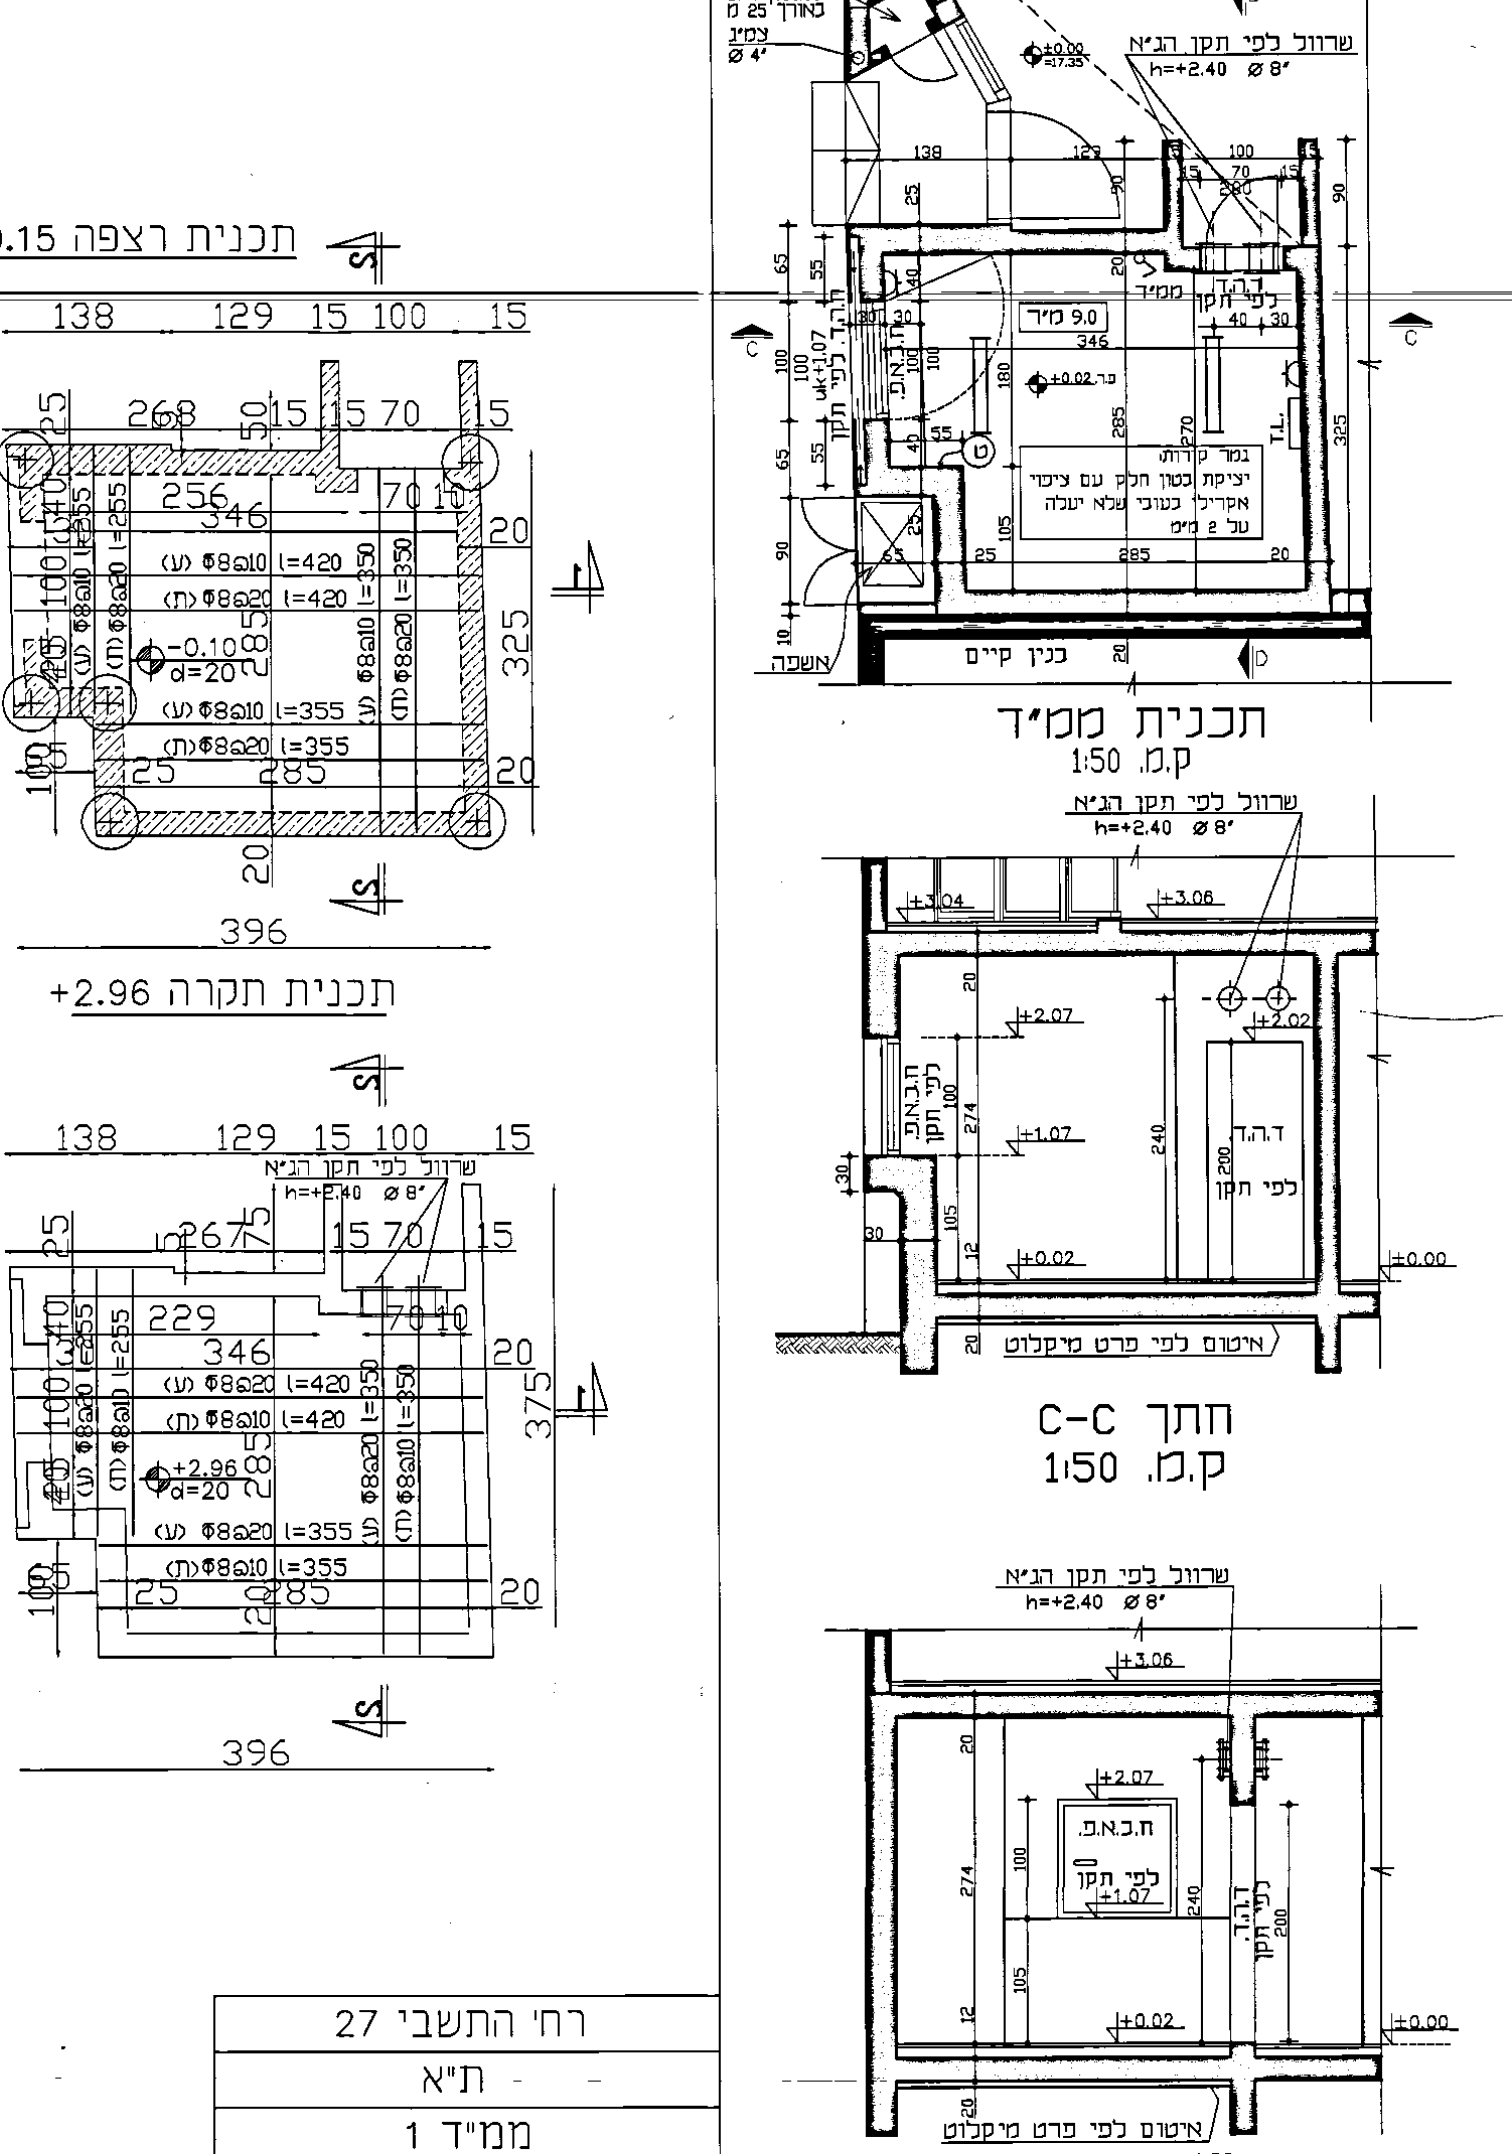

שרוול לפי תקן הג"א
h=+2.40 Ø 8"
9.0 מ"ר
ממ"ד
ד.ה.ד. לפי תקן
בנין קיים
גמר קירות: יציקת בטון חלק עם ציפוי אקרילי בעובי שלא יעלה על 2 מ"מ
תכנית ממ"ד
ק.מ. 1:50
חתך C-C
ק.מ. 1:50
חתך D-D
ק.מ. 1:50

מקרא :

בית תקע חשמל	
טלפון	Ⓣ
בית תקע לאנטנה רדיו וטלביזיה	T.L.
מפסק	
גוף תאורה פלואורסצנטי 2 נורות 36 ווט במתח 230 וולט	
חלון בטחון אטום פנימי	ח.ב.א.פ.
חלון הדף דרתי	ח.ה.ד.
דלת הדף דרתי	ד.ה.ד.

חישוב שטח ממ"ד

ק.מ. 1:50

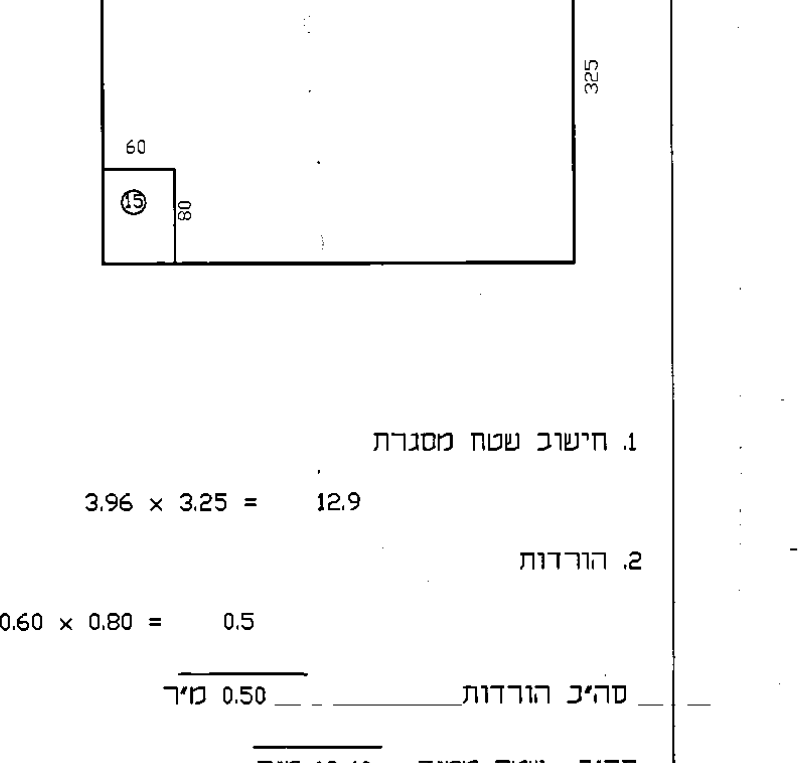

396
325
60
80

1. חישוב שטח מסגרת
3.96 × 3.25 = 12.9

2. הורדות
① 0.60 × 0.80 = 0.5

סה"כ הורדות 0.50 מ"ר

סה"כ שטח ממ"ד 12.40 מ"ר

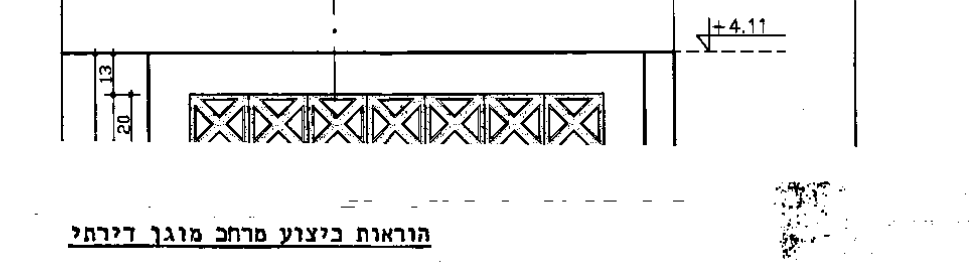

הוראות ביצוע מרחב מוגן דירתי

המרחב המוגן הדירתי יבנה בהתאם לתקנות התגוננות האזרחית (מפרטים לבניה מקלטים). (תיקון) תשנ"א 1991 שפורסם מס' 5425 מיום 3.3.1992 .

עקרונות התכנון

בתכנון המרחב המוגן הדירתי יתקיימו עקרונות יסוד אלה:

המרחב המוגן הדירתי ייבנה בטון במבנה דמוי תיבה, עשוי מקשה אחת ורתום בכל חלקיו, ללא קורות ועמודים.

רצפת המרחב המוגן הדירתי, קירותיו ותקרתו יהיו משוריים (יצוקים בדיקטים בלבד).

קירות המרחבים המוגנים הדירתיים יהיו רציפים לכל גובה הבניין, ליצירת מגדל מוגן. יציבות המגדל המוגן של המרחבים המוגנים הדירתיים תובטח מפני כוחות אופקיים.

העובי המזערי של חלקי המרחב המוגן הדירתי יהיה כאמור בתקניה 208.

תכנון שלד המרחב המוגן הדירתי ייעשה בהתאם לת"י 466.

מידות מזעריות של פתח אור - דלת כניסה - 60/200 ס"מ או 70/200 .

סוג דלת הכניסה - דלת הדף דירתית כמפורט בתקנה 202.

הגנה על דלת כניסה - כמפורט בתקנות (ע"י מחיצות ומרחקים מקווי בניין).

חלון - בשטח מירבי 1.21 מ"ר, גובה מפלס אדן לא יפחת מ-1.05 מ' .
חלון ההדף הדירתי יכלול שני חלקים עיקריים:
א. חלון בטחוני פנימי אטום מפני גזים
ב. אלמנט מגן חיצוני להדף-תקן לפי תקנה 205 .

בטון

הבטון בכל חלקי המרחב המוגן הדירתי יהיה מסוג ב-300 לפי דרישות ת"י 118.
החוזק האופייני וחוזקי תוכן של הבטון השונות ייקבע לפי ת"י 466.

הכנת המרחב המוגן הדירתי לקשר, טלפון, טלויזיה וחשמל

באחד מקירות המרחב המוגן יותקן מוביל לצורך הכנת כבל טלפון, תיבת הסתעפות לטלפון ונקודת טלפון יותקנו בהתאם לדרישות חברת בזק.

במרחב מוגן יותקנו שני בתי-תקע, אחד לאנטנת טלויזיה ואחד לאנטנת רדיו.
בבית התקע יותקן צינור שקוטרו לא יפחת מ-16 מ"מ, אשר יוביל אל מחוץ למרחב.

א. לצורך תאורה רגילה יותקנו לפחות שני גופי תאורה פלורסנטיים, כל אחד שתי מנורות של 36 ווט.
ב. לצורך תאורת חרום, תותקן מנורת חירום אחת לפחות של 36 ווט לפעולה של 4 שעות.
ג. יותקנו שני שקעי חשמל 220 וולט.
ד. יותקן שקע אחד לטלפון חוץ.
ה. תותקן נקודת טלויזיה אחת.

עבודות גימור

פני הדופן הפנימי של הקירות והתקרה של המרחב המוגן הדירתי יהיו חלקים עם גמר יציקת בטון ואין לטייח אותם.
הקירות והתקרה של המרחב המוגן יהיו בגימור צבע או ציפוי אקרילי בעובי שלא יעלה על 2 מ"מ.
קירות המרחב המוגן לא יצופו בצדם הפנימי באריחי חרסינה, באריחים מסוג אחר או בטיח.

את רצפת המרחב המוגן יש לרצף באריחי ריצוף מותר להשתמש בכל חומר ציפוי. שיפולים (פנלים) מותר שיהיו מחומר כגון: פי.וי.סי. אולם אין להשתמש בחומרים כגון אריחי ריצוף, חרסינה, טיח וכיוצא באלה.

פריסת גדר מזרחית
ק.מ. 1:100

642835 ·מ.ר.ב 6426354 ·ס.ע
69122 ת"א 12 בית צורי 12
23050 ·מ.ר. רשיון
אדר' אורנת זוהר

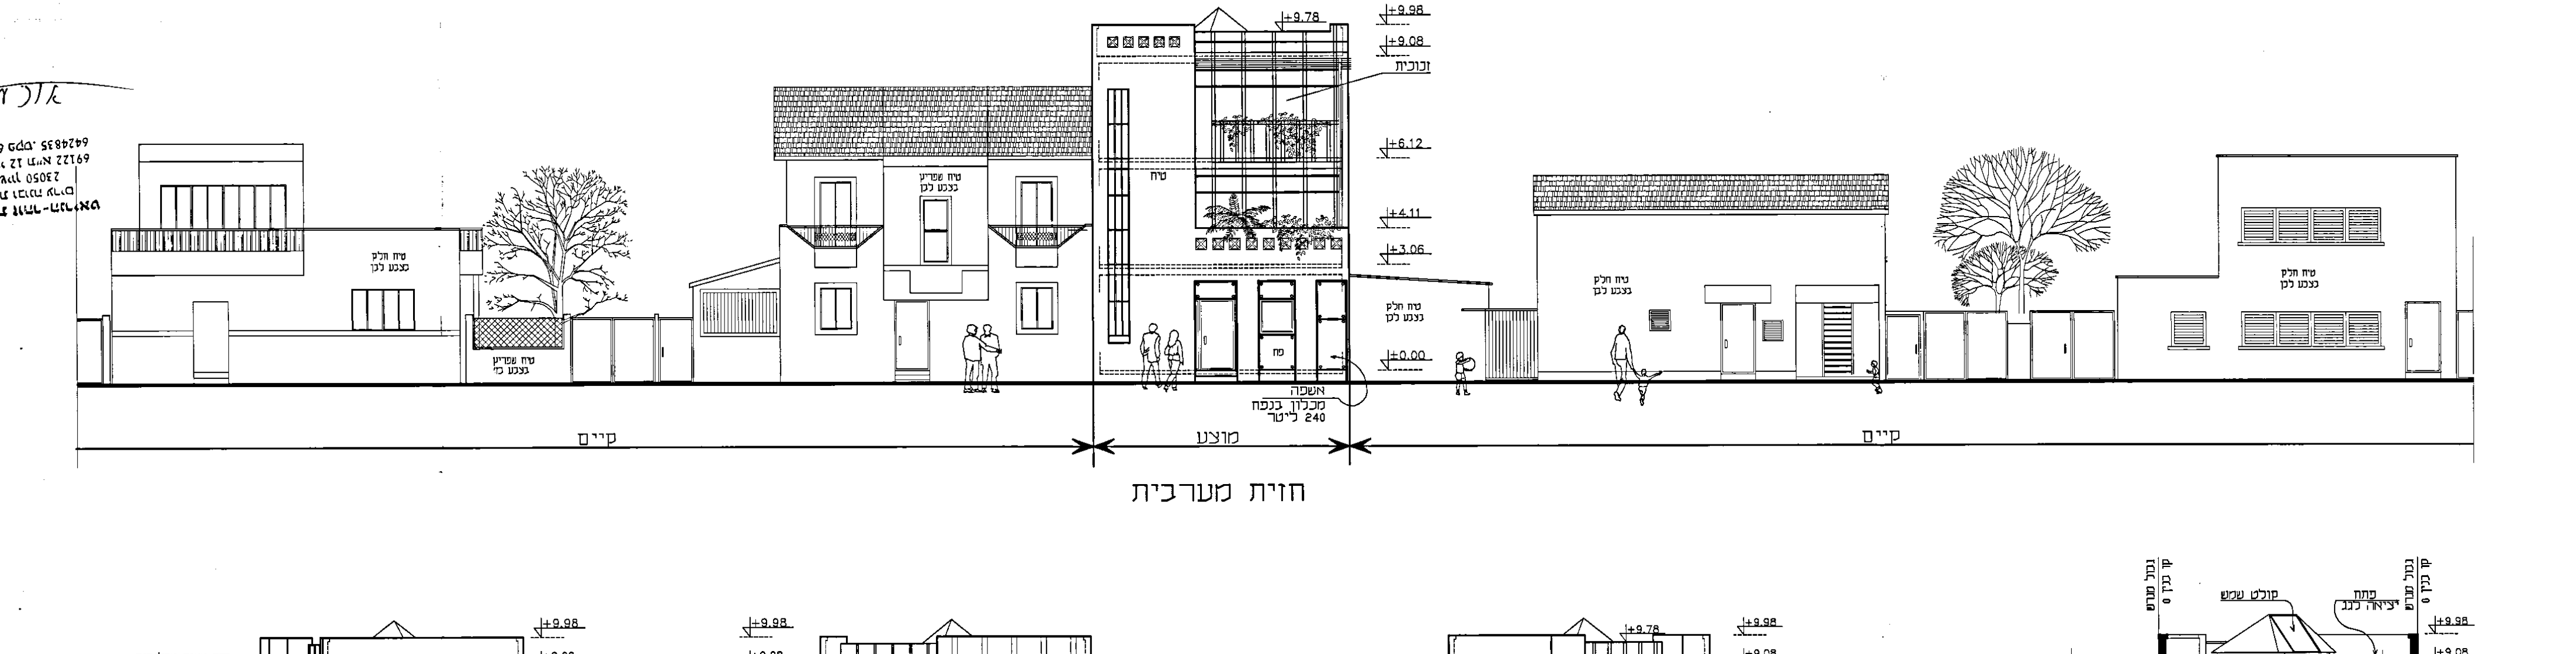

+9.98
+9.08
+6.12
+4.11
+3.06
+0.00
קיים
מוצע
קיים

חזית מערבית

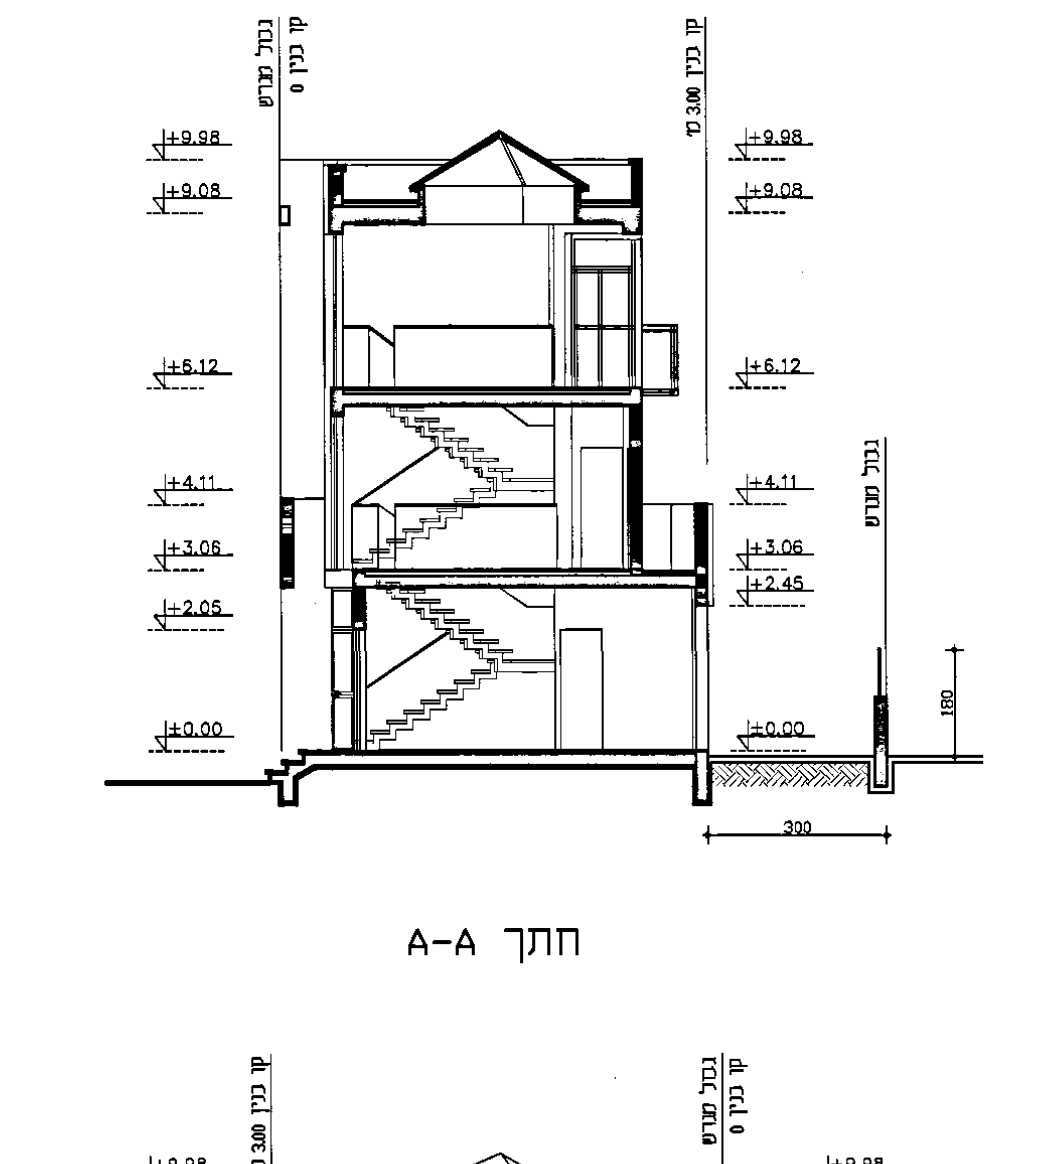

חתך A-A

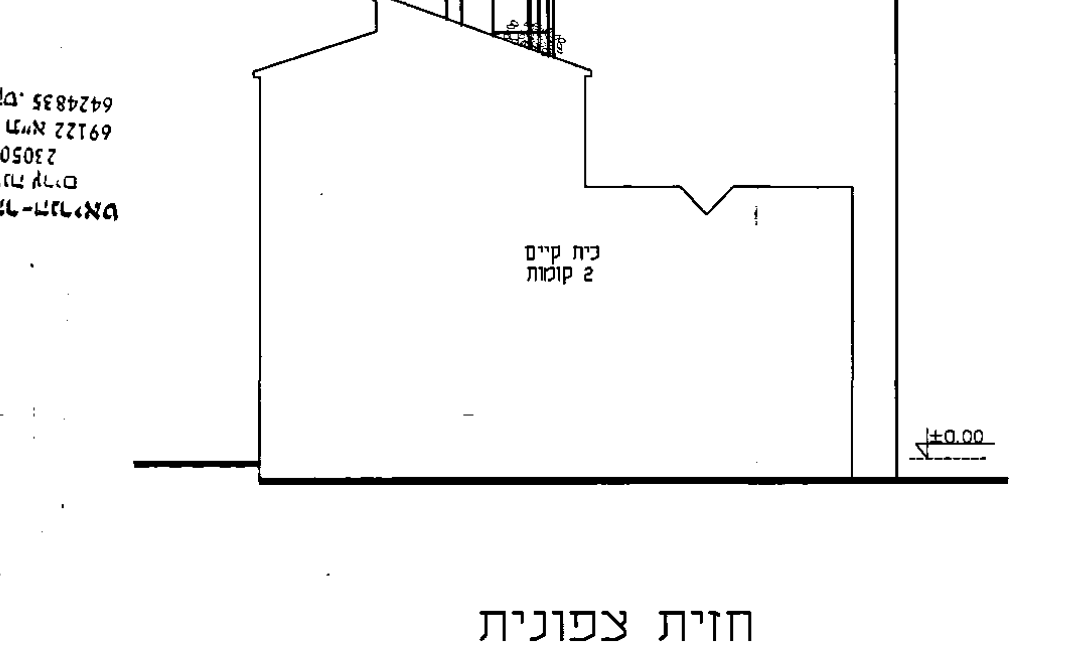

קיר אטום מבלוקים עם ציפוי פח
בית קיים 2 קומות

חזית צפונית

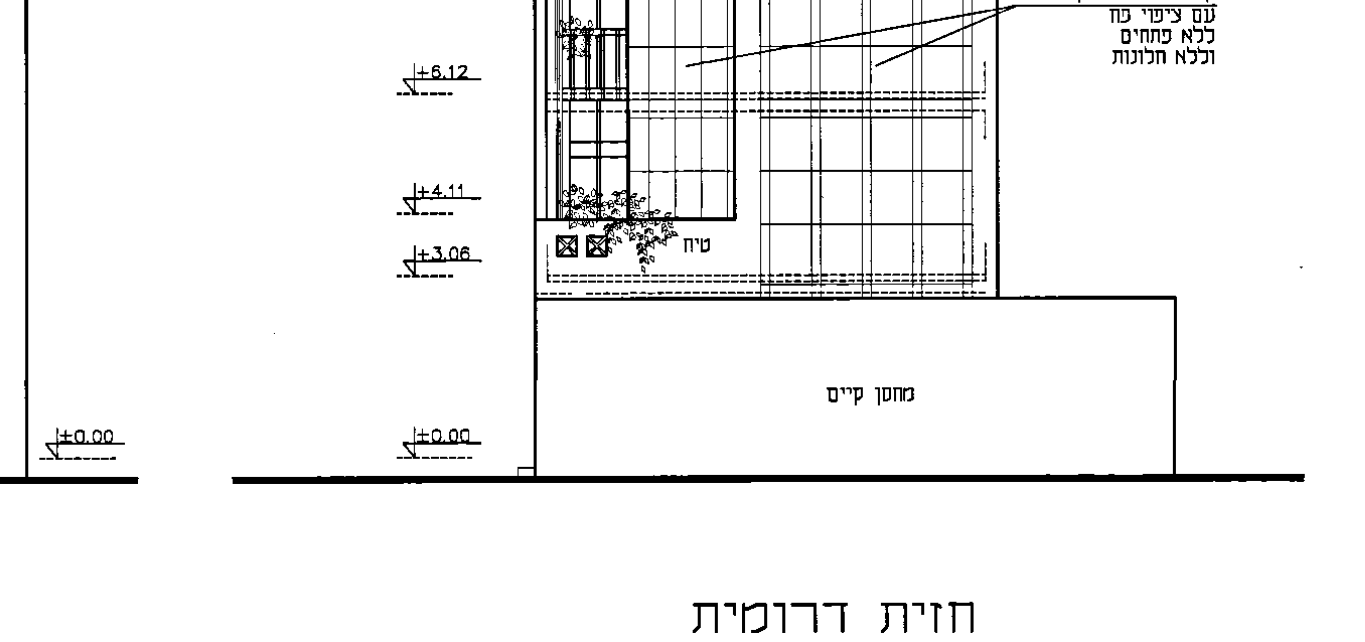

חזית דרומית

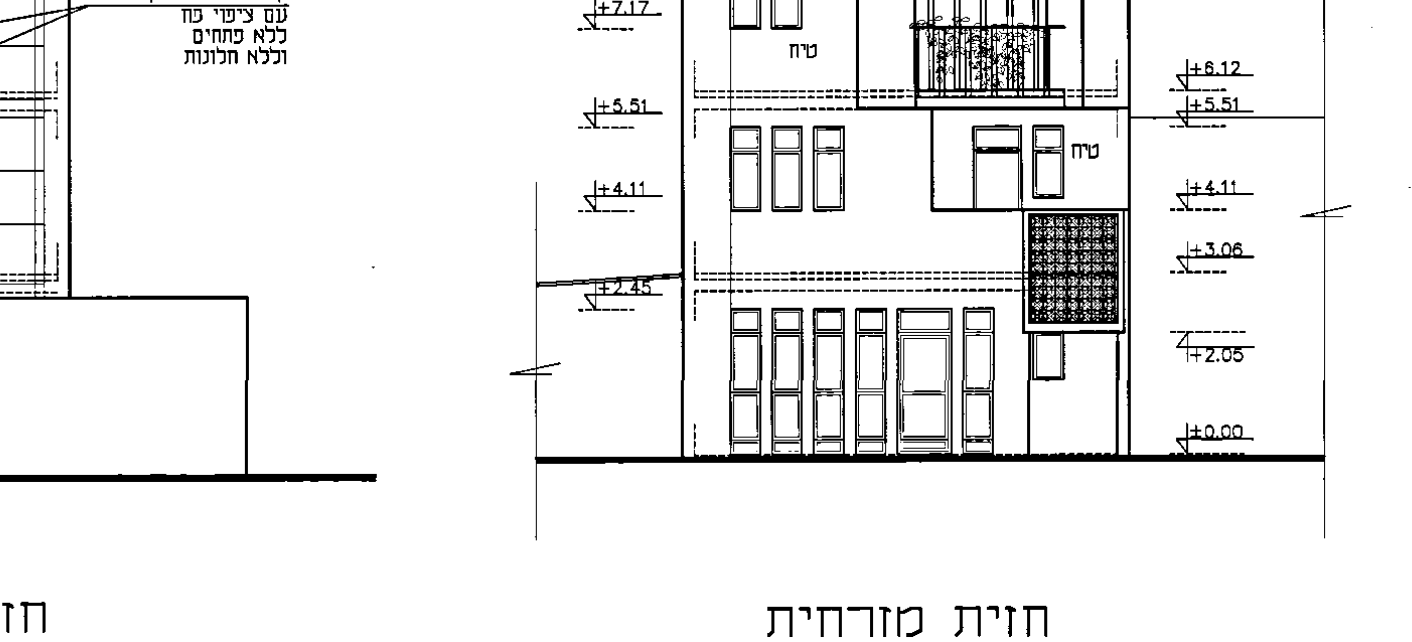

חזית מזרחית

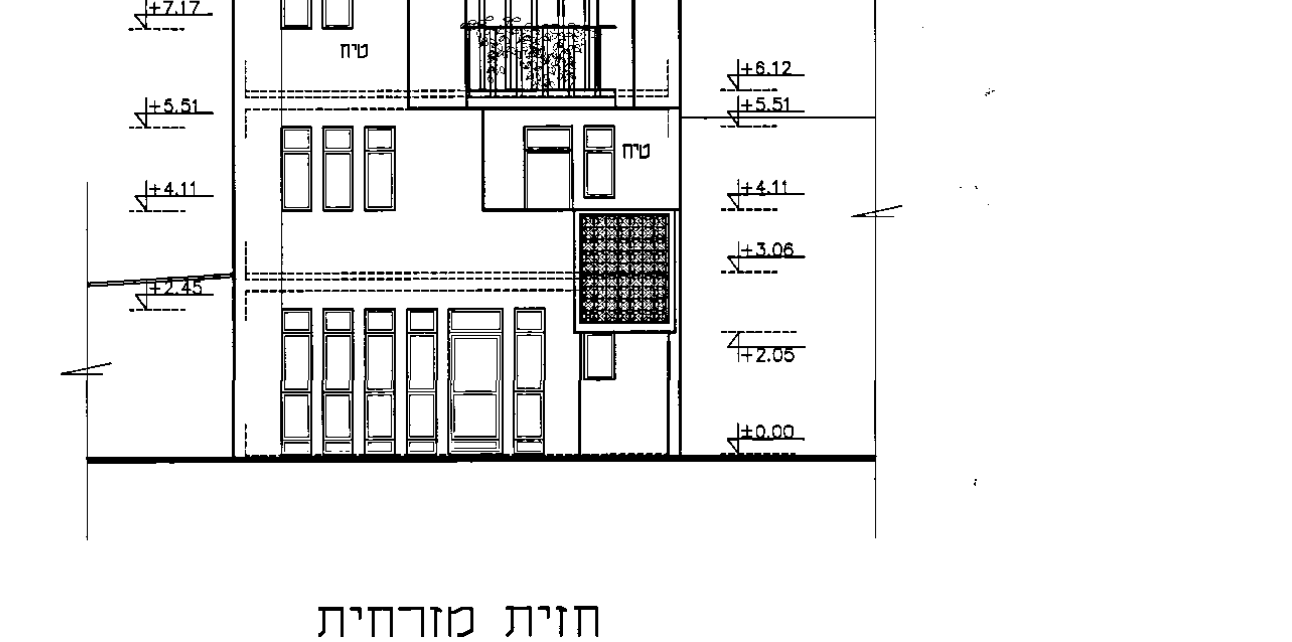

חתך C-C

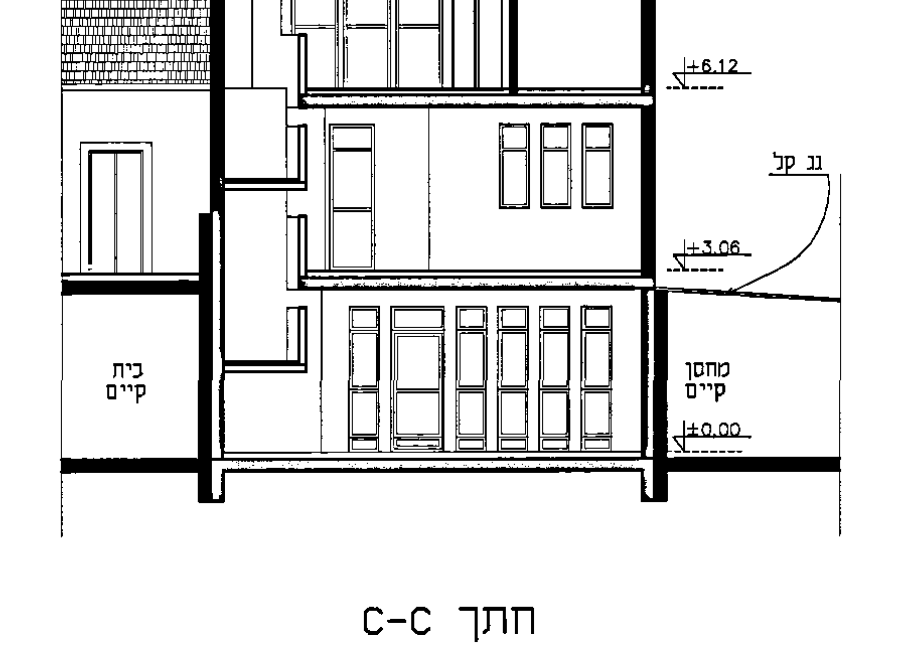

חתך B-B

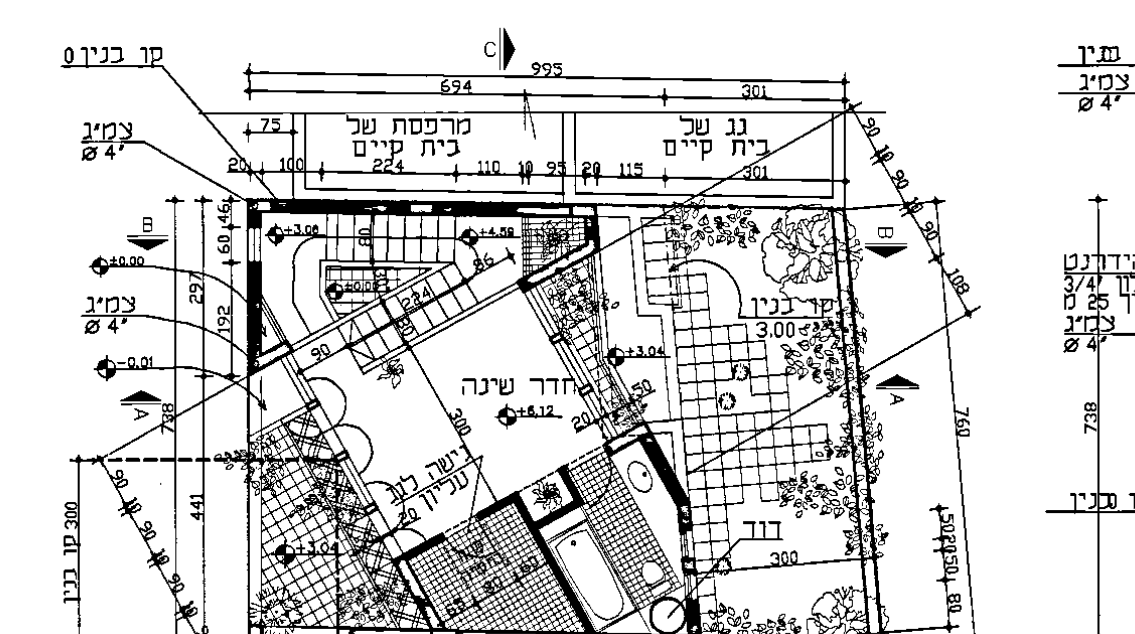

תכנית קומה ב'
+6.12 מפלס

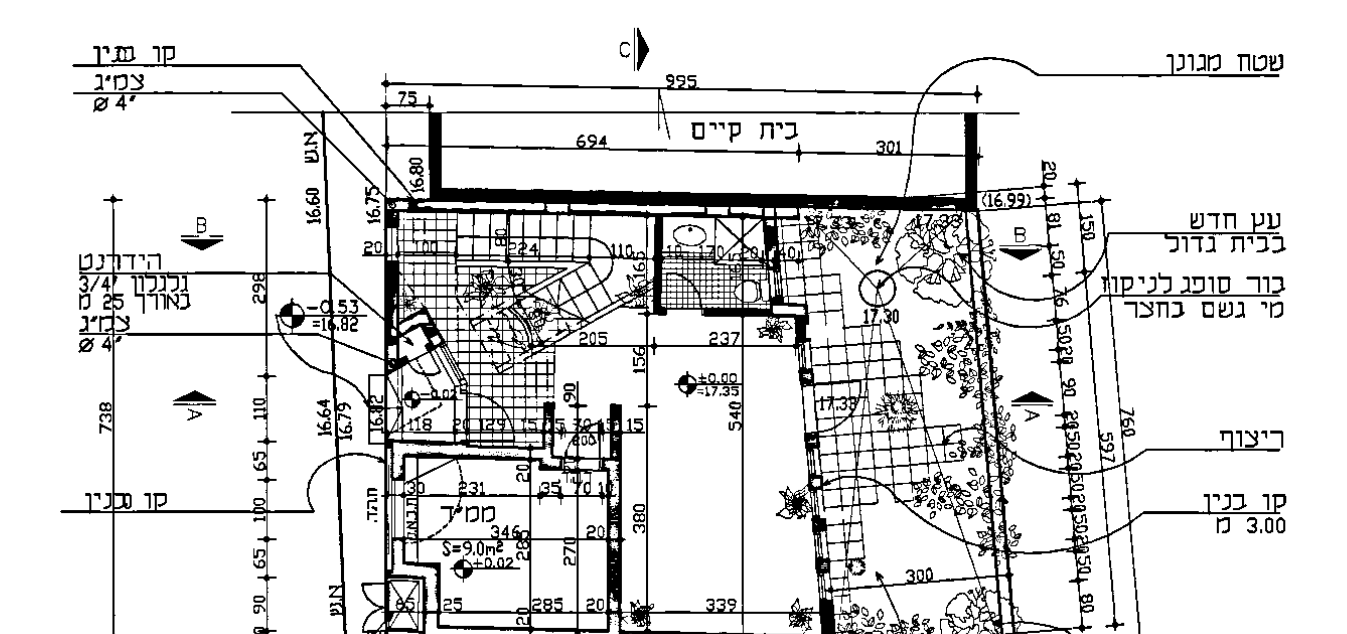

שטח מגונן
עץ חדש בבית גדול
בור סופג לניקוז מי גשם בחצר
ריצוף
קו בנין 3.00 מ
עץ חדש Ø 3" בבית גדול
שטח מגונן

תכנית קומת קרקע
ותכנית פיתוח שטח
מפלס ±0.00

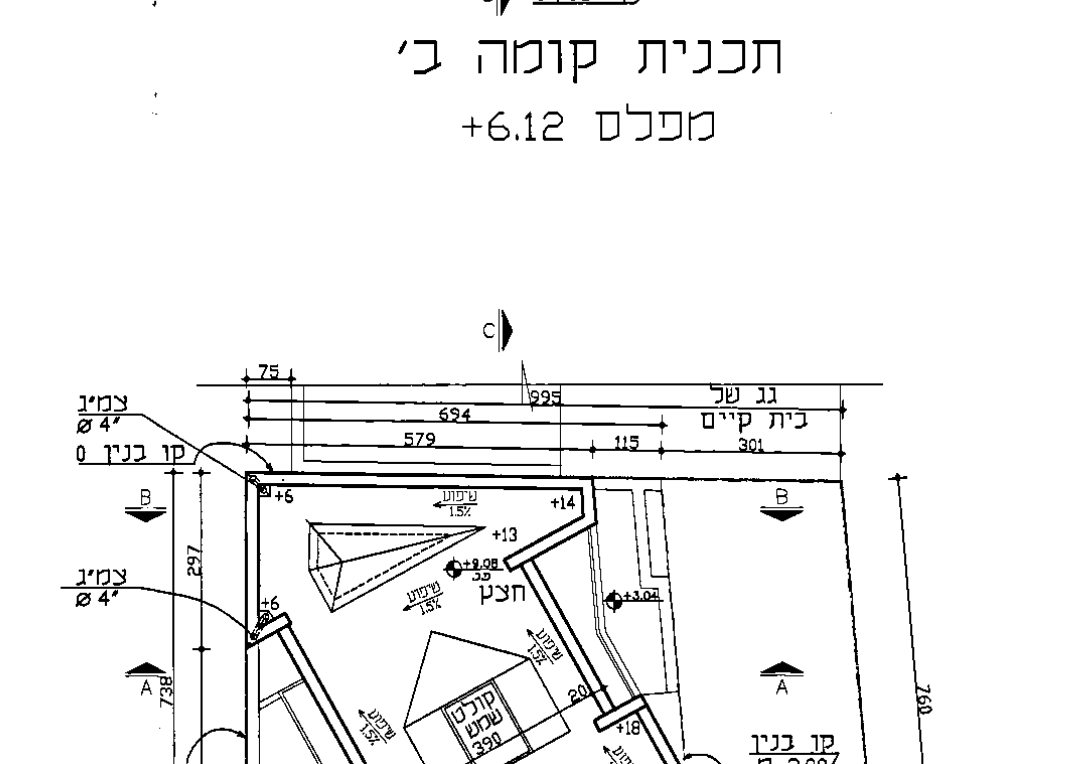

תכנית גג

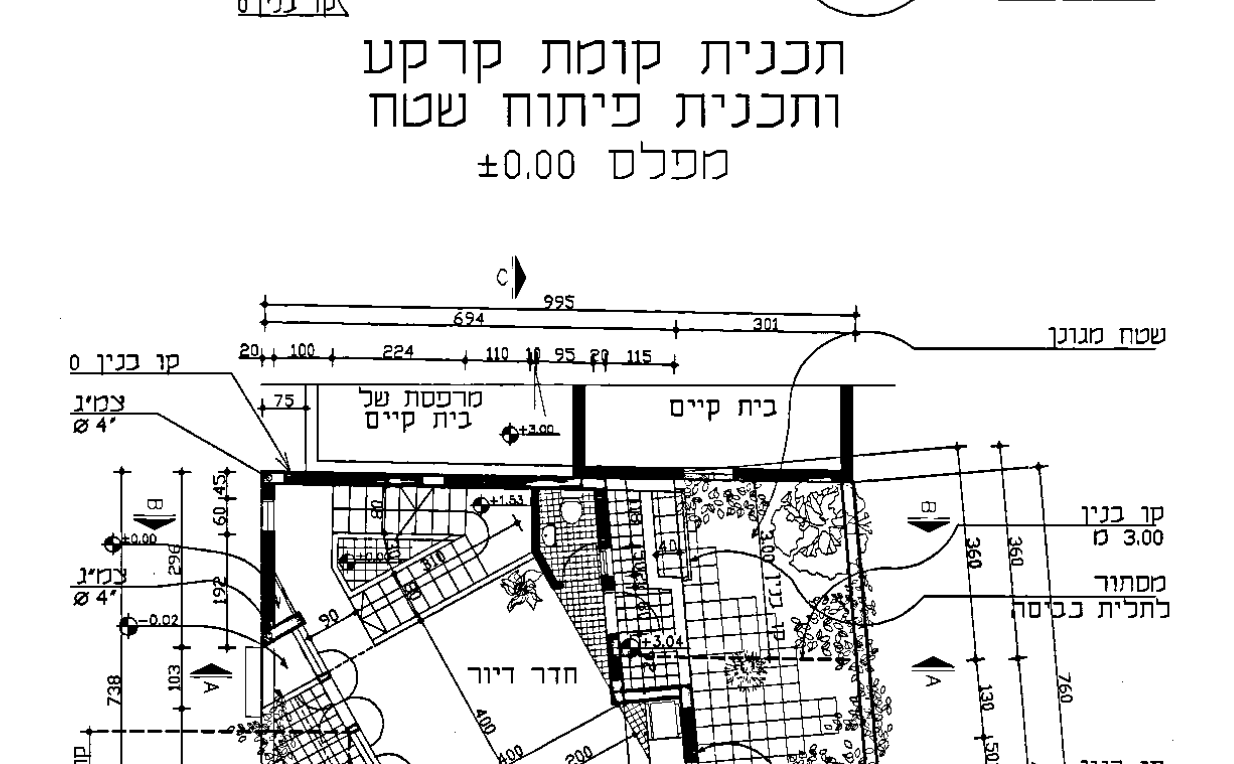

שטח מגונן
בית קיים
קו בניין 3.00 מ
מסתור לתלית כביסה
קו בניין 3.00 מ

תכנית קומה א'
+3.06 מפלס

חישוב תכסית:

סה"כ שטח קומת קרקע:
55.65 - 3.70 = 51.95 מ"ר

סה"כ שטח מגרש: 76 מ"ר

תכסית: 51.95 : 76 = 0.68 %

חישוב זכות בניה

לפי ת.ב.ע. מס' 2215

שטח המגרש לפי נסח טאבו :	112 מ"ר
שטח המגרש לפי מדידה עלידי מודד מוסמך:	76 מ"ר
% הבניה המותרים לפי ת.ב.ע.:	140.0 %
תוספת % בניה עבור הריסת בית קיים :	7.5 %
שטח שרות עבור בנית ממ"ד :	7.5 מ"ר
חישוב סה"כ שטח בניה מותר :	
76.0 × 1.4 =	106.4 מ"ר
76.0 × 0.075 =	5.7 מ"ר
סה"כ שטח עיקרי מותר :	112.1 מ"ר
(ממ"ד) 7.5 מ"ר =	7.5 מ"ר
סה"כ זכויות בניה מותרים : (עיקרי + שירות)	119.6 מ"ר

תשריט סכימטי של שטחי הבניה

ק.מ. 1:100

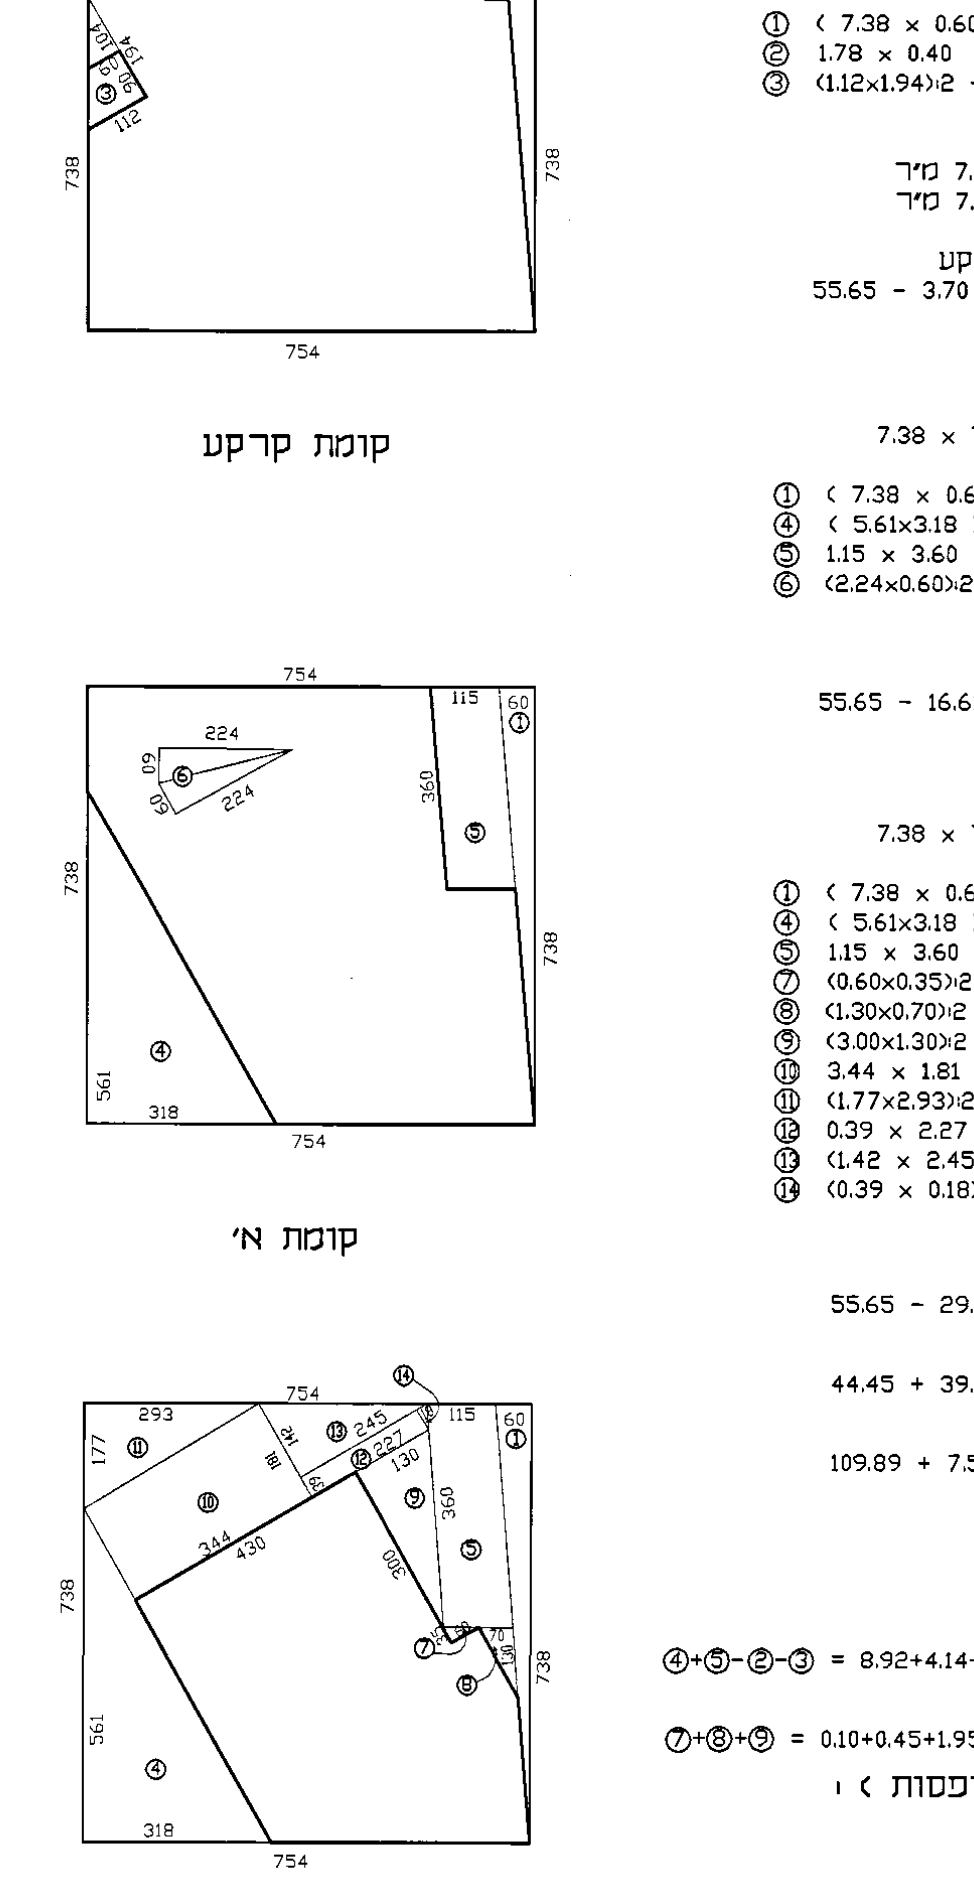

754
738
קומת קרקע
קומת א'
קומת ב'

חישוב שטח קומת קרקע

1. חישוב שטח מסגרת
7.38 × 7.54 =55.65

2. הורדות
① (7.38 × 0.60) : 2 = 2.21
② 1.78 × 0.40 = 0.71
③ (1.12×1.94):2 - (0.60×1.04):2 = 0.78
סה"כ 3.70 מ"ר

3. חישוב שטח שירות 7.5 מ"ר
סה"כ שטח שירות : 7.5 מ"ר

4. חישוב שטח עיקרי - קומת קרקע
55.65 - 3.70 - 7.5 = 44.45 מ"ר

חישוב שטח קומה א'

1. חישוב שטח מסגרת
7.38 × 7.54 =55.65

2. הורדות
① (7.38 × 0.60) : 2 = 2.21
④ (5.61×3.18) : 2 = 8.92
⑤ 1.15 × 3.60 = 4.14
⑥ (2.24×0.60):2×2 = 1.34
סה"כ 16.61 מ"ר

4. חישוב שטח עיקרי - קומה א'
55.65 - 16.61 = 39.04 מ"ר

חישוב שטח קומה ב'

1. חישוב שטח מסגרת
7.38 × 7.54 =55.65

2. הורדות
① (7.38 × 0.60) : 2 = 2.21
④ (5.61×3.18):2 = 8.92
⑤ 1.15 × 3.60 = 4.14
⑦ (0.60×0.35):2 = 0.10
⑧ (1.30×0.70):2 = 0.45
⑨ (3.00×1.30):2 = 1.95
⑩ 3.44 × 1.81 = 6.22
⑪ (1.77×2.93):2 = 2.59
⑫ 0.39 × 2.27 = 0.89
⑬ (1.42 × 2.45):2 = 1.74
⑭ (0.39 × 0.18):2 = 0.04
סה"כ 29.25 מ"ר

4. חישוב שטח עיקרי - קומה ב'
55.65 - 29.25 = 26.40 מ"ר

סה"כ שטח עיקרי

44.45 + 39.04 + 26.40 = 109.89

סה"כ שטח (עיקרי+שרות)

109.89 + 7.5 = 117.39

שטחים לא מקוריים קומת א' :

④+⑤-②-③ = 8.92+4.14-0.71-0.78 = 11.57

שטחים לא מקוריים קומת ב' :

⑦+⑧+⑨ = 0.10+0.45+1.95 = 2.40

סה"כ שטחים לא מקוריים (מרפסות) :

= 13.97

תל-אביב-יפו מפה טופוגרפית

מס' סדורי 2073 / 2000

ק.מ. 1 : 250

שכונת התקוה
גוש : 6135
חלקה 110 (חלק)
רח' תשבי 27

הוכן עבור: סושניק גוליין
מהות הבקשה: התר בניה

שטח לפי נסח טאבו: 112 מ"ר
שטח מדוד: 76 מ"ר

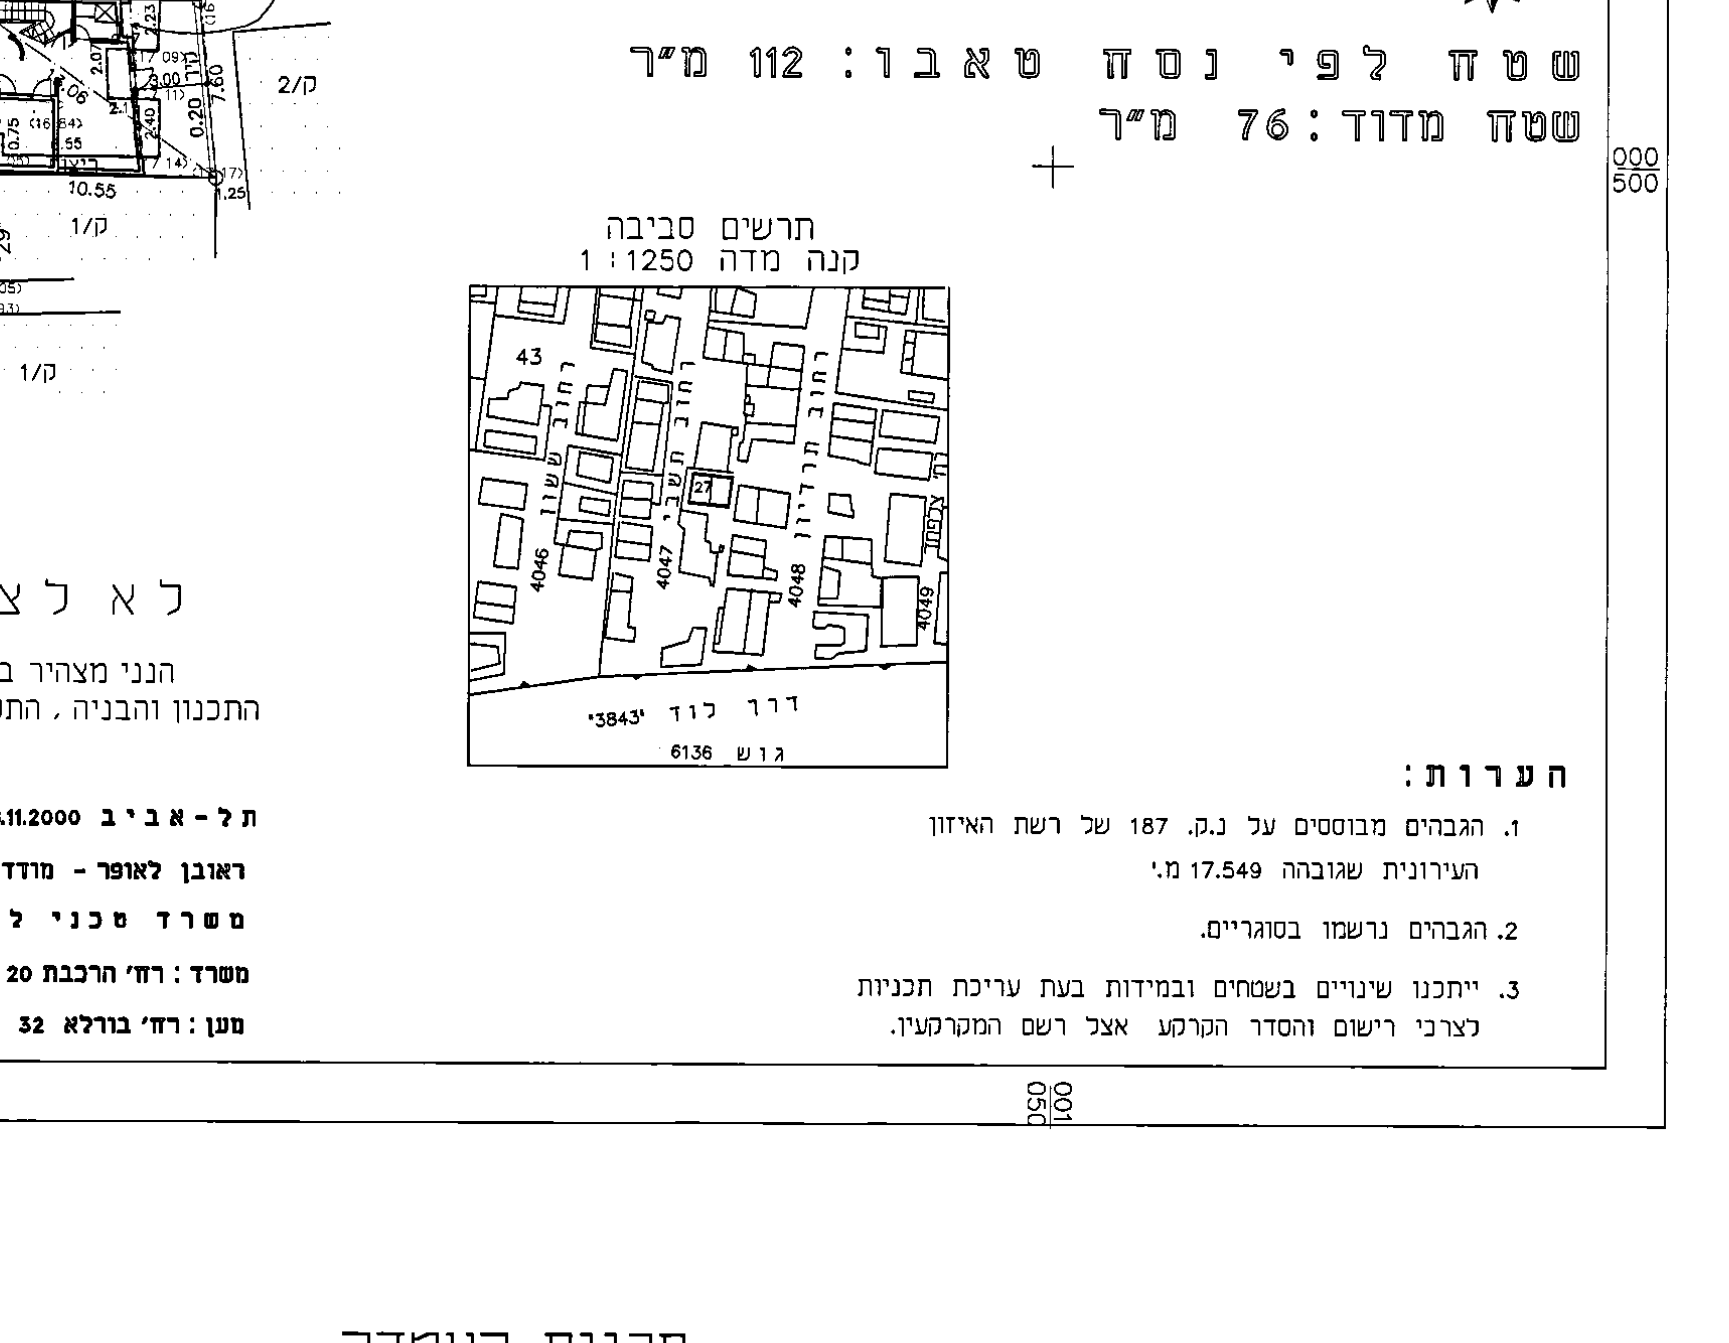

ק/1
ק/3
קו בנין 3.00 מ
מגרש ריק
רח' תשבי
ריצוף
כביש אספלט
ק/2
תרשים סביבה
קנה מדה 1 : 1250
דרך לוד
גוש 6136

לא לצרכי רישום

הנני מצהיר בזה שהמפה נעשתה לפי חוק התכנון והבניה , התקנות וההנחיות של עירית תל אביב יפו

תל-אביב 8.11.2000 מודד מוסמך
ראובן לאופר - מודד מוסמך מס' רשיון 874
משרד טכני למדידות
משרד : רח' הרכבת 20 תל - אביב טל': 5608221 - 03
מען : רח' בורלא 32 תל - אביב טל' : 6993398 - 03

הערות:

1. הגבהים מבוססים על נ.ק. 187 של רשת האיזון העירונית שגובהה 17.549 מ'.
2. הגבהים נרשמו בסוגריים.
3. ייתכנו שינויים בשטחים ובמידות בעת עריכת תכניות לצרכי רישום והסדר הקרקע אצל רשם המקרקעין.

תכנית העמדה

תל-אביב-יפו מפה טופוגרפית

מס' סדורי 2073 / 2000

ק.מ. 1 : 250

שכונת התקוה
גוש : 6135
חלקה 110 (חלק)
רח' תשבי 27

הוכן עבור: סושניק גוליין
מהות הבקשה: התר בניה

שטח לפי נסח טאבו: 112 מ"ר
שטח מדוד: 76 מ"ר

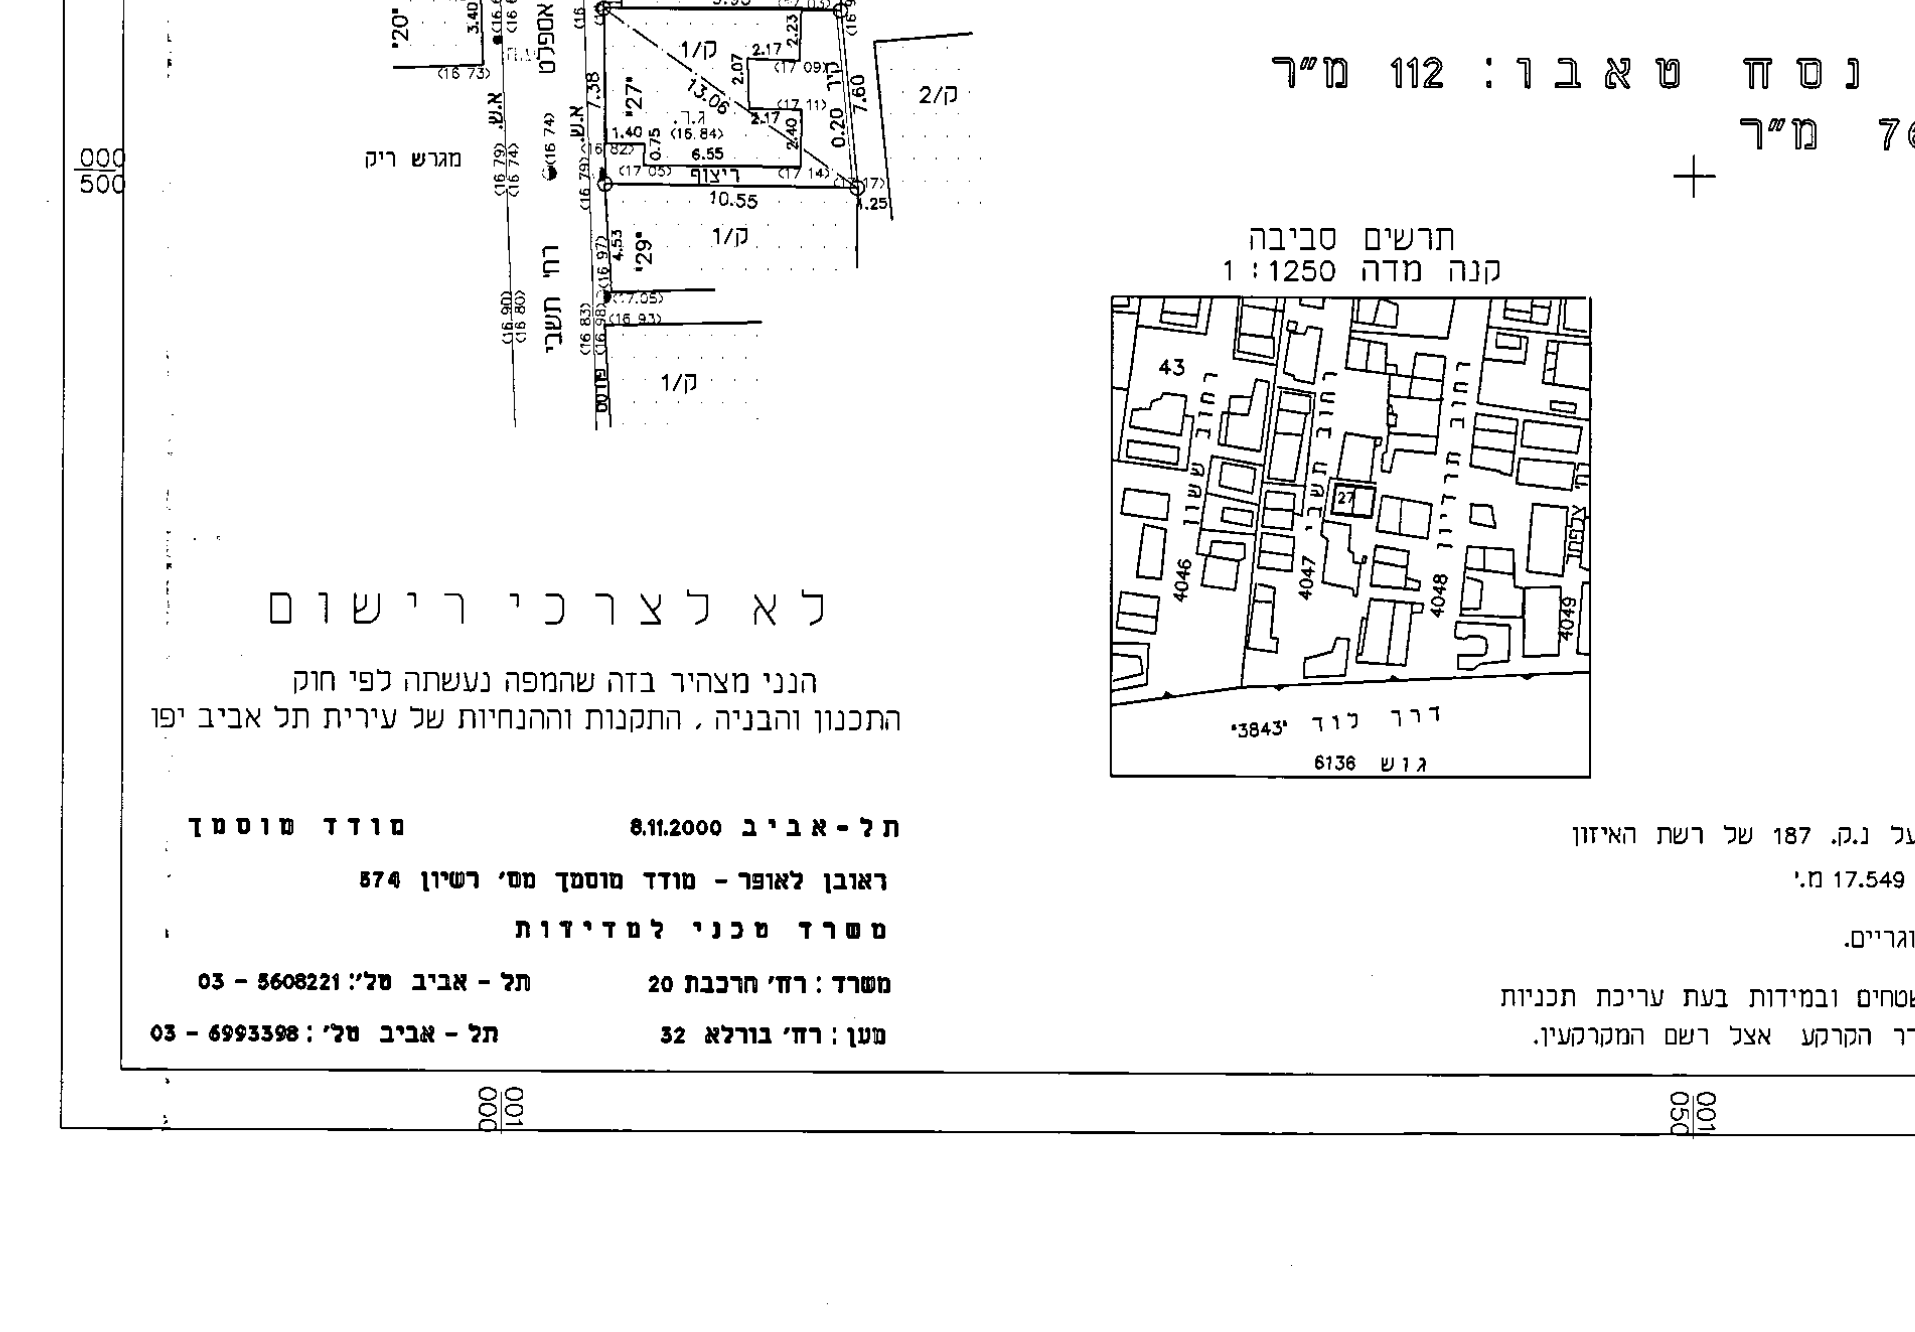

לא לצרכי רישום

הנני מצהיר בזה שהמפה נעשתה לפי חוק התכנון והבניה , התקנות וההנחיות של עירית תל אביב יפו

תל-אביב 8.11.2000 מודד מוסמך
ראובן לאופר - מודד מוסמך מס' רשיון 874
משרד טכני למדידות
משרד : רח' הרכבת 20 תל - אביב טל': 5608221 - 03
מען : רח' בורלא 32 תל - אביב טל' : 6993398 - 03

הערות:

1. הגבהים מבוססים על נ.ק. 187 של רשת האיזון העירונית שגובהה 17.549 מ'.
2. הגבהים נרשמו בסוגריים.
3. ייתכנו שינויים בשטחים ובמידות בעת עריכת תכניות לצרכי רישום והסדר הקרקע אצל רשם המקרקעין.

מפת איתור העבודה (תרשים מגרש)

עיריית תל-אביב-יפו
מינהל ההנדסה
נתקבל
05-02-2002
במחלקת בקרה ותיעוד

22

21-1160

5-2613
04.02.02

עיריית תל - אביב - יפו
מינהל ההנדסה, אגף רישוי ופיקוח על הבנייה

חוק התכנון והבניה, התשכ"ה-1965

בקשה להיתר בנייה או לשימוש במקרקעין - בניין חדש

לכבוד
☒ הועדה המקומית לתכנון ולבנייה
☐ רשות הרישוי המקומית

מס' תיק הבניין	מס' בקשה להיתר בנייה	מס' בקשה במידע	תאריך
4047-27	—	מ/210238	22-02-2001

א. פרטי הנכס והמבקשים

רחוב	מס' בית	גוש	חלקה	מגרש
תשבי	27	6135	110 (חלק)	

	שם משפחה ושם פרטי	מס' זהות/חברה	רחוב ומספר בית, ישוב ומיקוד	מספר טלפון
מבקש 1	גורדון גיונתן	309898773	רח' התשבי 27, תל - אביב	053-247447
בעל זכות בנכס	סושניק גוליין	מס' דרכון: 101982845	בוסטון, ארה"ב	
עורך הבקשה הראשי	אורנת זוהר	13041496	בית צורי 12, ת"א 69122	03-5618868 03-5615675
מתכנן שלד הבניין	סגל מיכאל	6903184	רח' נתן ילין-מור 6, תל - אביב	03-5627020 03-5617999

ב. מהות הבקשה לבניה חדשה
☒ הריסת מבנה קיים או חלקו
☒ הקמת מבנה חדש
קומות מגורים/ים 3 קומות מגורים ובהן 1 יחידות דיור
חדרי שירותים 1
גובה גדר 1.80
☒ שטחים מרוצפים

בית בן קומה 1 המיועד להריסה

שטח המגרש: 112 לפי טאבו, 76 לפי מודד
154.5% אחוזי הבנייה
117.39 מ"ר סה"כ שטח הבנייה המבוקש

ח. השטחים המבוקשים לבניה

תכלית	מבוקש מ"ר	%	מותר	מ"ר שירות	שטחים לא מקוריים
קרקע	44.45	58.5%		7.5	0.00
קומה א'	39.04	51.4%			11.57
קומה ב'	26.40	34.7%			2.40
סה"כ	109.89	144.6%	112.10	7.5	13.97

סה"כ שטח הבנייה 117.39, 154.5%; מותר 119.6

ד. קווי בניה

כיוון	מוצע	מותר	הבסיס
התשבי	0	0	0 0
צפון	0	0	0 0
דרום	0	0	0 0
מזרח	3	3	0 0

דירת מגורים 1 1 4 109.89

שם	תאריך	מס' רשיון
אורנת זוהר	2-06-2001	23050
מרקוביץ' מריגלה		10230
סגל מיכאל		09036
פינטר יוסי		47064

סגל מיכאל 6903184 09036

30-05-2001

אורנת זוהר 20-05-2001

גורדון גיונתן	5-06-2001
סושניק גוליין	5-06-2001
סגל מיכאל	5-06-2001

אדר' אורנת זוהר
בית צורי 12 ת"א 69122
642835 ·מ.ר.ב 6426354

מפקדת ראש הג"א - ענף הנדסה ומיגון

אישור תוכנית מוקטנת משעם ראש הג"א
התכנית נבדקה ונמצאה בהתאמה לדרישות תקנות ההתגוננות האזרחית (מפרטים לבנית מקלטים)
5-2613
04.02.02

אישורנו הותנה בתנאים כדלקמן:

1. ביצוע מרחב מוגן במפורט בתכנית המאושרת (חסי... באחריות המבקש, עורך הבקשה והמהנדס אחראי על ביצוע השלד.
2. אישור על חיבור חשמל ינתן ע"י המהנדס המקסים בעירייה, אחו קבלת הצהיר המהנדס אחראי על ביצוע השלד בנ ורשט.
3. בדיקת מרחב מוגן תעשה בשני שלבים: בתהליך הבניה, ובגמר הבניה.