22

עיריית תל-אביב-יפו
מינהל ההנדסה
בתקשה
13-05-2001

תיק: 4047-0674

עיריית תל-אביב-יפו
מינהל ההנדסה, אגף רישוי ופיקוח על הבנייה
שדרות בן-גוריון 68 תל-אביב 64514 (פקס 5231340) טלפון 5217120, 5217045
לכבוד הוועדה המקומית לתכנון ולבנייה
ת"א - רשות הרישוי המקומית

חוק התכנון והבנייה, התשכ"ה-1965
תקנות התכנון והבנייה (בקשה להיתר תנאיו ואגרות), התש"ל-1970

על פי טופס 1 תקנה 2(א)

בקשה להיתר בנייה או לשימוש במקרקעין

יש להקפיד למלא את כל הפרטים בטופס הבקשה ולצרף מסמכים כמפורט ברשימת התיוג המצורפת.

מס' תיק הבניין	מס' בקשה קודמת להיתר בנייה	מס' הבקשה למידע / מתאריך
4047-029		מי 20992 / 17.5.2000

א. פרטי הנכס והמבקשים

הכתובת: רחוב תשבי; מס' בית 31; גוש 6135; חלקה 110; תת חלקה; מגרש; הוראות התכניות החלות על המקום 2215

פרטים אישיים	שם משפחה / שם פרטי, שם חברה או תאגיד	מס' זהות/חברה או מס' רישום תאגיד	רחוב ומספר בית, יישוב ומיקוד	מספר טלפון, מספר פקס
מבקש 1	לוי שלמה	0551849	תשבי 31	5372048
מבקש 2				
מבקש 3				
בעל הזכות בנכס	לוי שלמה	0551849	תשבי 31	5372048
החוכר				
עורך הבקשה הראשי	ז'יבגורסקי מלכס	1468785-9	רח' [illegible] 12 בת-ים	052-544459
מתכנן שלד הבניין	ז'יבגורסקי מלכס	1468785-9	רח' [illegible] 12 בת-ים	5071765

אם המבקש חברה או תאגיד, יש לרשום את שם המנהל כחותם.

ב. מהות הבקשה

☒ בקשה לתוספת בנייה ☐ בקשה להרחבת דיור (במסגרת הרחבת דיור שכונתית)

☐ תוספת ____ קומות לבניין

☐ הכוללות: ____ יחידות דיור

☐ ____

☐ תוספת בנייה בקומה ____ ☐ לחזית ☐ לאחור ☐ לצד

בשטח של ____ מ"ר.

שטח הדירה/המשרד לאחר התוספות יהיה ____ מ"ר.

☐ שינויים פנימיים הכוללים:

☒ אישור מצב קיים

☐ הבקשה לא

המקום משמש כיום ל- מגורים

☐ בהיתר ☐ בלי היתר

ג. מפרט - תיאור הבקשה

תיאור הקיים על המגרש (פרט מספר מבנים, גובהם, מקומם, ייעודם וכד'): בניה קיימת בן 2 קומות

שימוש עיקרי: ☒ מגורים ☐ מלונאות ☐ תעשייה ☐ חקלאי ☐ משרדים ☐ בידור ☐ בניין ציבורי ☐ מלאכה ☐ מסחר ☐ נופש וספורט ☐ שימוש אחר, פרט: ____

סוג העבודה או השימושים המוצעים: ☐ תוספת לבניין ☐ תיקונים ☐ שינוי בשימוש ממטרה ____ למטרה ____ ☒ שינוי לבניין ☐ הריסה

הגורם שמבוצעת בעבורו הבנייה: ☐ משרד ממשלתי ☐ מוסד ציבורי ☐ בנה ביתך ☐ רשות מקומית ☒ גורם פרטי ☐ אחר ____

שטחים: שטח המגרש/החלקה 112 מ"ר; שטח הבנייה הכולל המבוקש 186,84 מ"ר; אחוזי הבנייה ____ %

אם במסגרת הרחבת דיור שכונתית: מספר יחידות דיור מורחבות ____; מספר תכנית ההרחבה 2215

ד. חומרי הבנייה

סוג הבנייה: ☒ רגילה ☐ בית מוכן ☐ מתועשת ☐ אחר ____

קירות חיצוניים: ☐ בטון מזוין ☒ בלוקים ☐ אבן טבעית ☐ לבנים שרופות ☐ אחר ____

חומרי גימור: ☐ אבן מלאכותית ☐ אבן טבעית ☒ טיח ☐ זכוכית ☐ אחר ____

תקרות: ☒ בטון מזוין ☐ עץ ☐ אחר ____

גג: ☐ בטון מזוין ☒ רעפים ☐ אסבסט ☐ טיח ☐ אחר ____

גדרות: ☐ אבן טבעית ☐ אבן מלאכותית ☐ בטון ☐ בלוקים ☐ ברזל ☐ עץ ☐ רשת ☐ אחר ____

קיימות ____ מ"א מוצעות ____ מ"א סה"כ ____ מ"א

מקרא חומרים (צבעים): בטון או בטון מזוין; בלוקים או לבנים מבטון; סיליקט או לבנים אדומות; אבן; עץ; איטונג; זכוכית; הריסה; אחר

ה. השטחים המבוקשים לבנייה (על פי תכנית הבנייה) והמותרים לבנייה (על פי "אסמכתא": חוק, תקנות, תכנית) בכל מפלס בנפרד ולפי שימוש

(א) שטחי השימוש העיקריים

הקומה/המפלס בבניין	קיים בהיתר	קיים ללא היתר ומבוקש לאישור בדיעבד	בנייה חדשה מוצעת	מותר	מ"ר	% משטח המגרש	סך כל השטחים המותרים	ה"אסמכתא" לשטחים המותרים
1) מגורים ±0.00 ק.ק	93.42	93,42			93.42	83,41	2215	2215
+3.00	93.42	93,42			93.42	83,41	2215	2215
ס"ה מעל הקרקע	186,84	166,82			186.84	166,82		
ס"ה מתחת לקרקע								
סה"כ								

(ב) שטחי השירות: מקלט; מתקנים חדרים ומערכות טכניות; החסנה; חניה; מבואות וחדרי מדרגות; קומת עמודים מפולשת; מעברים לכלל הציבור; בליטות; אחר; בנייה קיימת; סך כל שטחי השירות (קיים, מוצע, % משטח המגרש, סך כל השטחים המותרים)

(ג) סך כל שטחי הבניין

מ"ר	% משטח המגרש	סך כל השטחים המותרים	משטחים לא מקורים
93,42	83,41		
93.42	83,41		
186,84	166,82		

ו. פרטי הבנייה - לשימוש הלשכה המרכזית לסטטיסטיקה

הייעוד	פירוט הייעוד (כגון דירות למגורים, בית מלון וכו')	השטח על פי ההיתר	מספר חדרים	מספר דירות	מספר מגורים
למגורים			1		
להארחה			2		
לעסקים ולמשרדים			3		
לבנייני ציבור			4		
לתעשייה ולמלאכה			5		
למשק חקלאי			6		
למקלט או למרתף					
למבני עזר					
סך כל שטח הבנייה			סה"כ		

נבדק

מספר היתר הבנייה; תאריך היתר הבנייה שנה חודש; תאריך התחלת הבנייה שנה חודש; תאריך גמר הבנייה שנה חודש; מספר הקומות כולל קומת עמודים מפולשת

ז. קווי בנייה

הכיוון	מוצע	מותר	הסטייה במטר	הסטייה ב-%
לרחוב (שם) ____				
לרחוב (שם) ____				
לצד				
לאחור				

ח. מספר יחידות דיור

☐ אם השימוש המבוקש הוא מגורים - רשום להלן:

מספר דירות קיימות (מעל ל-120 מ"ר / מתחת ל-120 מ"ר) ____ מספר הדירות המבוקשות ____ מספר הדירות המותרות ____

ט. הבקשה מוגשת לאישור

☐ הוועדה המקומית

הבקשה כוללת בקשה להקלה - כלהלן:

	פירוט הבקשה להקלה	נימוקי הבקשה להקלה
1.		
2.		
3.		

☐ רשות הרישוי המקומית

☐ רשות הרישוי המקומית באמצעות מורשה להיתר

י. הצהרת עורך הבקשה הראשי

☐ אני מצהיר על נכונות הפרטים בסעיפים א עד ט.

שם ז'יבגורסקי מלכס חתימה; תאריך

ז'יבגורסקי אלכס
מהנדס בנין
רשיון מס' 15320

יא. חתימות נוספות

	תאריך	שם	חתימה
המבקש			X
בעל הזכות בנכס / בעל הנכס / החוכר			
מתכנן שלד הבניין		ז'יבגורסקי	

ז'יבגורסקי אלכס
מהנדס בנין
רשיון מס' 15320

לשימוש המשרד / הערות הפיקוח

התכנית תואמת את המצב בשטח: ☒ כן ☐ לא

☐ הוכן דוח לתביעה משפטית ☒ הוגשה תביעה משפטית ☐ הוגשה תביעה חוזרת

מס' הדוח/התביעה: 15101225; תאריך הדוח/התביעה

הנדון בדיון/הנדרי בתביעה: אין קומה שניה

הערות: מאושר כולל כל קיר בליטה (הגבהה)

תאריך 16.05.2001; שם; חתימה

אינג' אמיל פרידמן
מהנדס איזורי
מח' פיקוח על הבניה
עיריית תל-אביב-יפו

96

אינג' אמיל פרידמן
מהנדס איזורי
מח' פיקוח על הבניה
עיריית תל-אביב-יפו

מקומי: לא

נבדק מטעם הוועדה/רשות הרישוי: תאריך; שם; חתימה

5131B 11/95

יב. מינויים מטעם מבקש ההיתר - נתמנה אדם אחד ליותר מתפקיד אחד, ימולאו פרטיו ליד כל אחד מהתפקידים שהוא ממלא על פי הוראות כל דין.

מינוי עורך הבקשה הראשי: אני ממנה בזה את ז'יבגורסקי מלכס בעל/ת מספר זהות 1468785-9 הרשום בסעיף א להיות עורך הבקשה הראשי להיתר, ולייצגני לפני מוסדות התכנון והרשויות המוסמכות בכל הנוגע לטיפול בבקשה להיתר ולקבלתו, לרבות התיקונים ככל שידרשו הרשויות המוסמכות.

מינוי עורכי בקשה לפי תחומים: אני ממנה בזה את הרשומים להלן להיות עורכי הבקשה להיתר בתחום הפעולה כרשום ליד שמם, ולייצגני בתחום פעולתם לפני מוסדות התכנון והרשויות המוסמכות בכל הנוגע לטיפול בבקשה להיתר ולקבלתו, לרבות התיקונים ככל שידרשו הרשויות המוסמכות.

	שם משפחה ושם פרטי	תחום פעולה	המען	מספר טלפון	מספר פקס
1	ז'יבגורסקי	מתכנן האינסטלציה הסניטרית	[illegible]		
2					

מינוי מתכנן שלד הבניין: אני ממנה בזה את ז'יבגורסקי מלכס בעל/ת מס' זהות 1468785-9 הרשום בסעיף א להיות אחראי לתכנון שלד הבניין שבעבורו מבוקש ההיתר, להגיש לוועדה המקומית לרשות הרישוי המקומית את החישובים לגבי הבנייה שבעבורה מבוקש היתר, ולפקח פיקוח עליון על הקמת השלד.

מינוי הקבלן האחראי לבנייה: ☐ אני ממנה בזה את ____ בעל/ת מספר זהות ____ ובעל תעודת רישום בפנקס הקבלנים מספר ____ במדור ____ ובעל רישיון לביצוע עבודה בתוקף עד ____ לבצע את העבודה הנדונה בהיתר כמתחייב לפי כל דין.

☐ אני מצהיר, כי טרם מסרתי את ביצוע העבודה הנדונה בהיתר לידי קבלן, ומתחייב כי אמסור אותה לידי קבלן רשום בפנקס הקבלנים, כמתחייב על פי כל דין, ולהודיע על כך לרשות הרישוי המקומית טרם התחלת ביצוע העבודה. וחתימתו של הקבלן תצורף להודעה המפרטת את פרטי רישומו של הקבלן.

מינוי האחראי לביצוע שלד הבניין: ☐ אני ממנה בזה את ____ בעל/ת מס' זהות ____ כתובת ____ טלפון ____ פקס ____ הרשום לעיל להיות אחראי לביצוע שלד הבניין.

☐ אני מצהיר, כי טרם מיניתי אחראי/ת לביצוע עבודות הבנייה בתחומים האלה: ____ ומתחייב לעשות זאת כמפורט בתקנות, ולהודיע על כך לרשות הרישוי המקומית טרם התחלת ביצוע העבודה.

מינוי אחראים לביקורת: ☐ אני ממנה בזה את הרשומים להלן להיות אחראים לביקורת על ביצוע עבודות בתחום הפעולה כרשום ליד שמם.

	שם משפחה ושם פרטי	תחום פעולה	המען	מספר טלפון	מספר פקס
1.		אחראי ראשי			
2.					
3.					

☐ אני מצהיר, כי טרם מיניתי אחראי/ם לביקורת על ביצוע עבודות הבנייה את כולם או את קצתם בתחומים האלה: ____ ומתחייב לעשות זאת כמפורט בתקנות, ולהודיע על כך לרשות הרישוי המקומית טרם התחלת ביצוע העבודה.

חתימת המבקש על המינויים X

יג. הצהרות

הצהרת עורכי הבקשה: אנו החתומים מטה מצהירים בזה:
1) כל אחד מאתנו מאשר שהאמור לגביו ברשימה שבסעיף י"ב לעיל הוא נכון.
2) כל אחד מאתנו מסכים לקבל עליו את התפקיד המיועד לו בסעיף י"ב לעיל.
3) אנו מצהירים, כל אחד בנוגע לתחום פעולתו, שיש לנו כישורים מקצועיים לערוך בקשה זו וכי בדקנו את המסמכים הנוגעים לבקשה, לרבות כל תכנית הנוגעת לבקשה, וידוע לנו, כי אם הצהרה זו אינה נכונה, הרי היא תיחשב מסירת ידיעה שהיא כוזבת או מטעה בפרט חשוב, כמשמעותה בסעיף 214 לחוק, וצפויים לנו העונשים הקבועים לפי כל דין.

כולל הצהרת עורך הבקשה: אני ז'יבגורסקי מלכס (עורך בקשה ראשי) אחראי/ת לכך שהבקשה, ובכלל זה נספחיה, נערכה לפי מיטב הידיעה המקצועית ובהתאם לכל חיקוק החל על הבניין או העבודה המוצעת, שכל הנתונים שנמסרו על ידי בבקשה זו נכונים ושהתכנון המוצע תואם את כל התכניות, פרט לסטיות שפורטו לעיל.

☐ אני עורך הבקשה מתכנן האינסטלציה הסניטרית מצהיר בזאת ואחראי לכך שתכניות הבקשה בכל הנוגע לסידורים הסניטריים נערכו כדין לפי קיומו בהן הוראות החוק וההוראות למתקני תברואה התש"ל 1970 (הל"ת) לעניין זה, לרבות בדיקת לחץ המים הקיים בבניין ותכנון בהתאם.

	תאריך	שם משפחה ושם פרטי	מספר רישיון	חתימה
עורך בקשה ראשי	4.02.98	ז'יבגורסקי מלכס	15320	ז'יבגורסקי אלכס מהנדס בנין
עורך בקשה 1 מתכ' האינס' הסניט'				
עורך בקשה 2				

הצהרת מתכנן שלד הבניין: אני החתום מטה (שם משפחה ושם פרטי) ז'יבגורסקי מלכס מספר זהות 1468785-9 מהנדס רשוי מס' 15320 /הנדסאי בעל רישיון מס' 15320 (ל"מבנה פשוט") מצהיר בזאת כדלקמן:
1) אני מסכים להיות מתכנן שלד הבניין הנדון בבקשה, ולפקח פיקוח עליון על הקמת השלד.
2) אני מתחייב להגיש לפני מתן ההיתר, נושא הבקשה, את החישובים הסטטיים בדבר הבנייה שבעבורה ההיתר.
3) ידוע לי, שאם אחרי הגשת הנתונים הסטטיים יתגלה צורך בשינוי מהותי בהם, אני מתחייב להגיש חישובים סטטיים מתוקנים מיד עם גילוי הצורך בכך.
4) אני מצהיר, כי יש לי כישורים מקצועיים לערוך בקשה זו וכי בדקתי את כל המסמכים הנוגעים לבקשה, לרבות כל תכנית הנוגעת לבקשה, וכי אם הצהרה זו אינה נכונה, הרי היא תיחשב מסירת ידיעה שהיא כוזבת או מטעה בפרט חשוב, כמשמעותה בסעיף 214 לחוק, וצפויים לי העונשים הקבועים לפי כל דין.
5) ידוע לי, כי עלי לשמור את תכניות הקונסטרוקציה לתקופה של לא פחות מ-10 שנים לאחר גמר הבנייה.

ז'יבגורסקי אלכס
מהנדס בנין
רשיון מס' 15320
חתימה ____ תאריך ____

הצהרת האחראי לביצוע שלד הבניין (כאשר מונה): אני החתום מטה (שם משפחה ושם פרטי) ____ מספר זהות ____ מהנדס רשוי מס' ____ /הנדסאי בעל רישיון מס' ____ (ל"מבנה פשוט") מצהיר בזאת כדלקמן:
1) אני מסכים להיות האחראי לביצוע שלד הבניין.
2) אני מצהיר, כי יש לי כישורים מקצועיים להיות אחראי לביצוע שלד הבניין ואני מתחייב לדאוג לביצוע שלד הבניין, על פי תכניות והוראות של מתכנן השלד כפי שייתנו בכתב וכן לבצע תפקידי על פי שנקבע בכל חיקוק הנוגע להן.
חתימה ____ תאריך ____

הצהרת אחראים לביקורת (כאשר מונו): אנו החתומים מטה מצהירים בזה:
1) כל אחד מאתנו מאשר שהאמור בנוגע לו ברשימה שבסעיף י"ב לעיל הוא נכון.
2) כל אחד מאתנו מסכים לקבל עליו את התפקיד המיועד לו בסעיף י"ב.
3) אנו מצהירים, כל אחד בנוגע לתחום פעולתו, שיש לנו כישורים מקצועיים לערוך את הביקורת כהלכה ולדווח על תוצאותיה לרשות הרישוי המקומית, כמתחייב על פי כל דין.
אני ____ (עורך הביקורת ראשי) אחראי/ת לכך שהביקורת תיערך על פי מיטב הידיעה המקצועית, ושכל הדיווחים לרשות הרישוי המקומית ייערכו על פי כל דין.

תאריך	שם משפחה ושם פרטי	מספר רישיון	חתימה

תל-אביב

גוש: 6135
חלקה: 110 (מקורית) - חלק -

מהות הבקשה: תוספת בניה
החודרת הבנין לקדמותו - כגונית טיל

הוכן עבור: מר לוי שלמה

השטח לפי מדידה = 178 מ"ר
" נסח = 308 מ"ר

מפה טופוגרפית

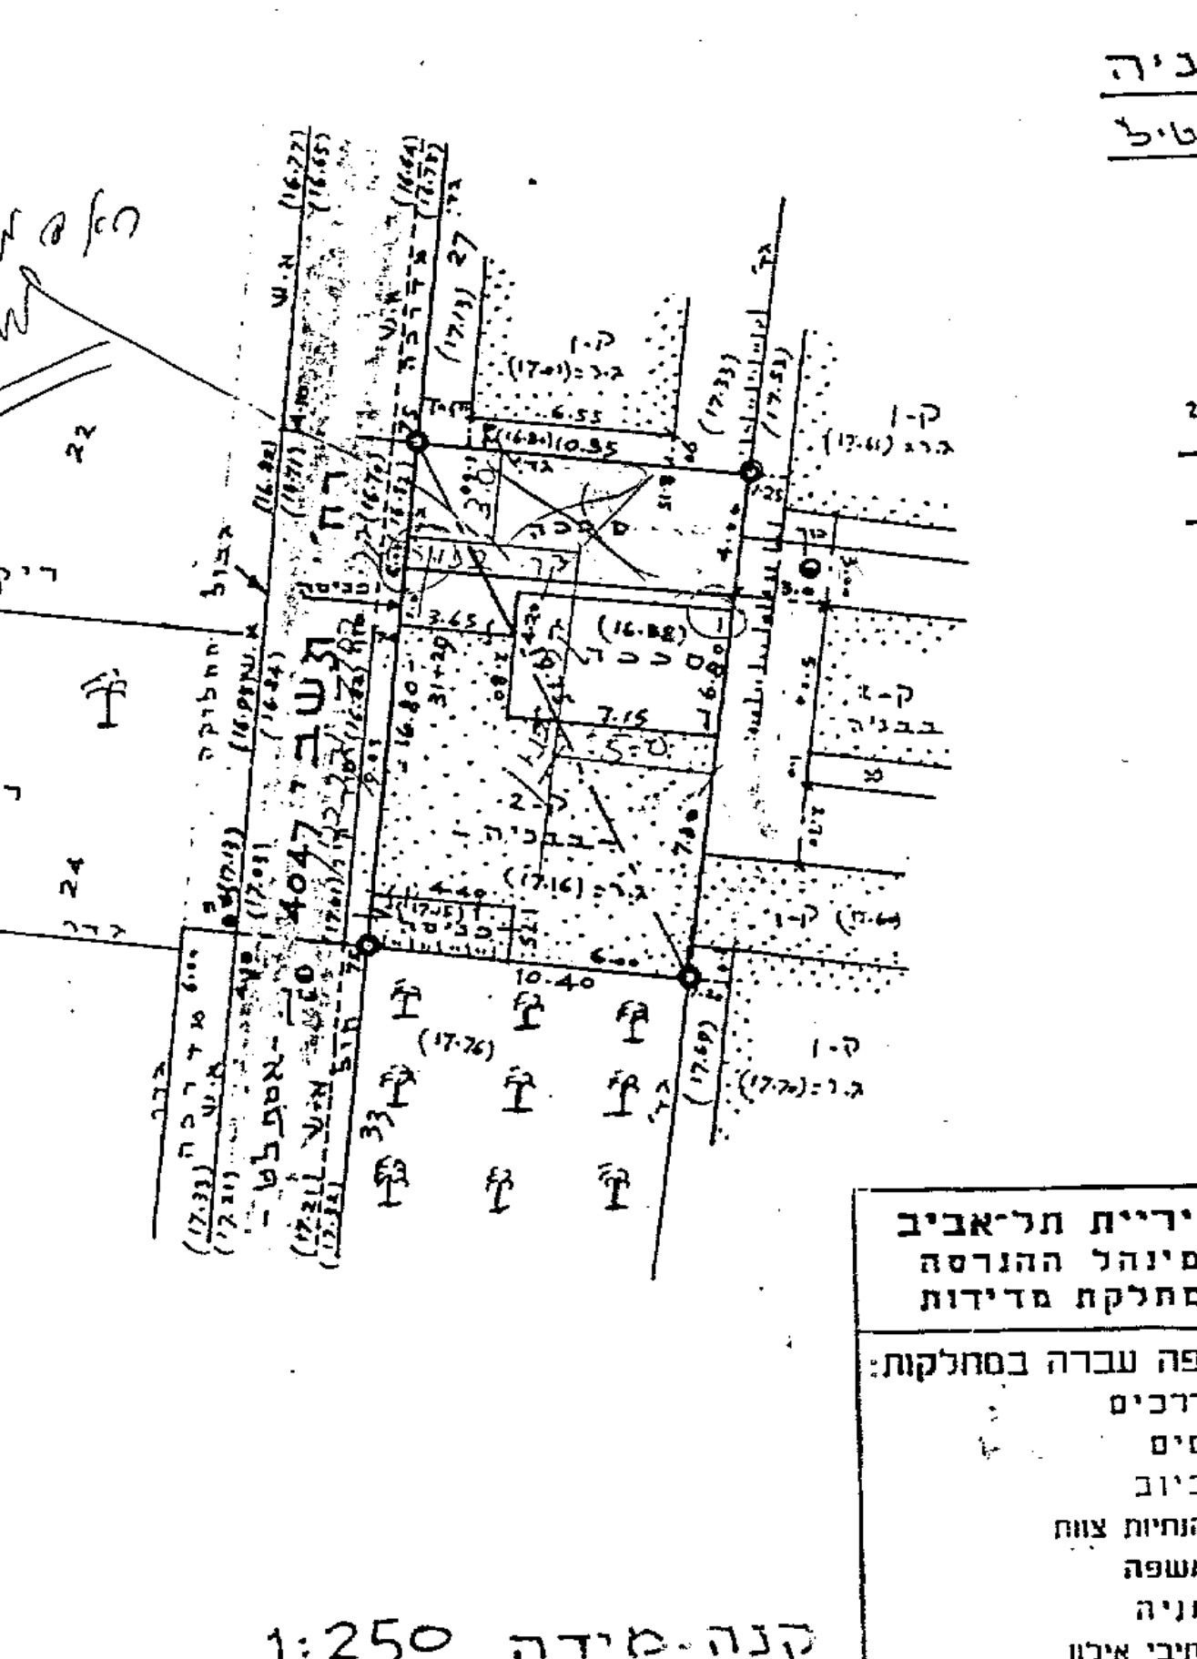

קנה-מידה 1:250

עיריית תל-אביב
מינהל ההנדסה
מחלקת מדידות
הספה עברה במחלקות:
☐ דרכים
☐ מים
☐ ביוב
☑ הנחיות צוות
☐ אשפה
☐ חניה
☐ וחיבי אילון
☐
עדינת כהן

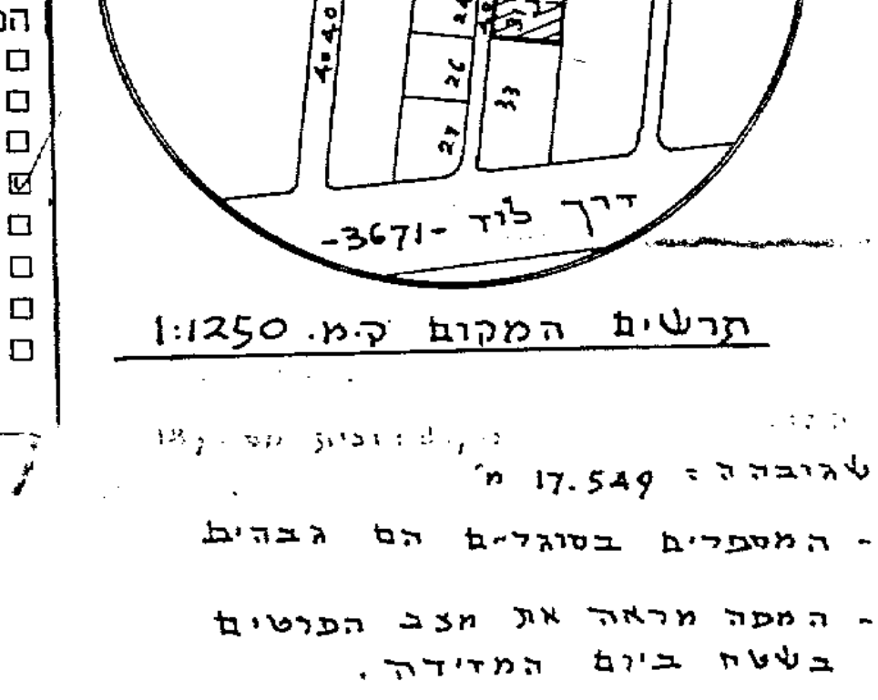

תרשים המקום ק.מ. 1:1250

הערות:
1- הגובה = 17.549 מ'
2- המספרים בסוגריים הם גבהים
3- המפה מראה את מצב הפרטים בשטח ביום המדידה.

חישוב שטחים

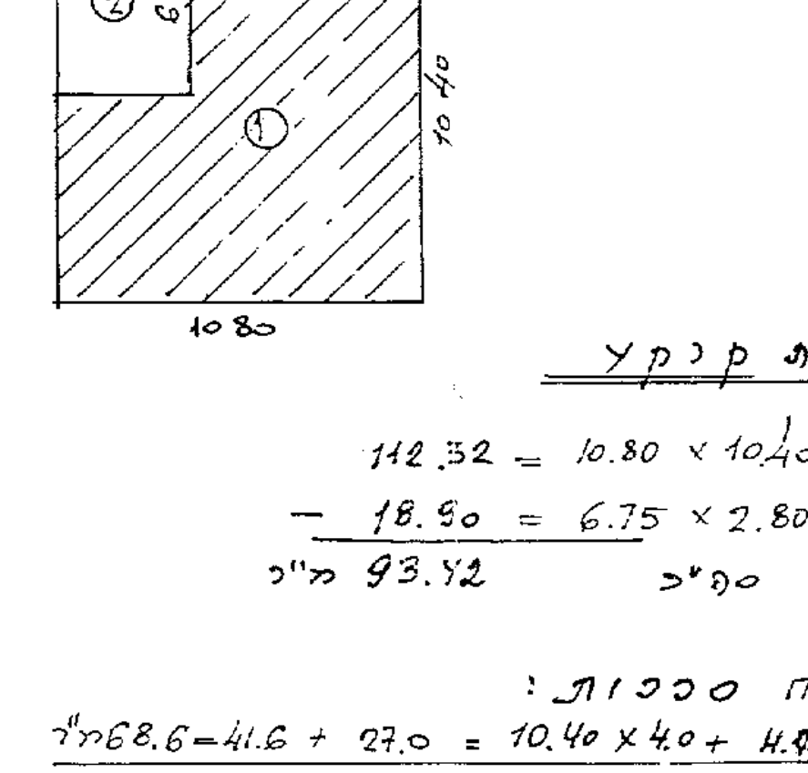

קומת קרקע

112.32 = 10.80 × 10.40 ①
− 18.90 = 6.75 × 2.80 ②
93.42 מ"ר סה"כ

שטח סככות:
68.6−41.6 + 27.0 = 10.40 × 4.0 + 4.0 × 6.75 מ"ר

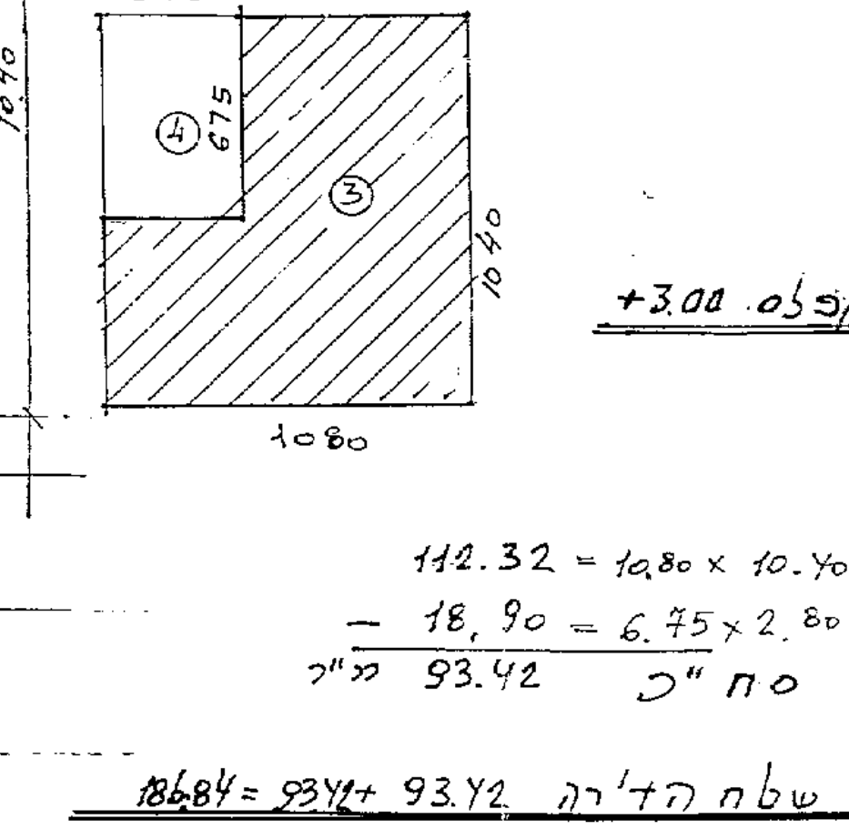

שטח במפלס +3.00

112.32 = 10.80 × 10.40 ①
− 18.90 = 6.75 × 2.80 ②
93.42 מ"ר סה"כ

שטח הדירה 93.42 + 93.42 = 186.84

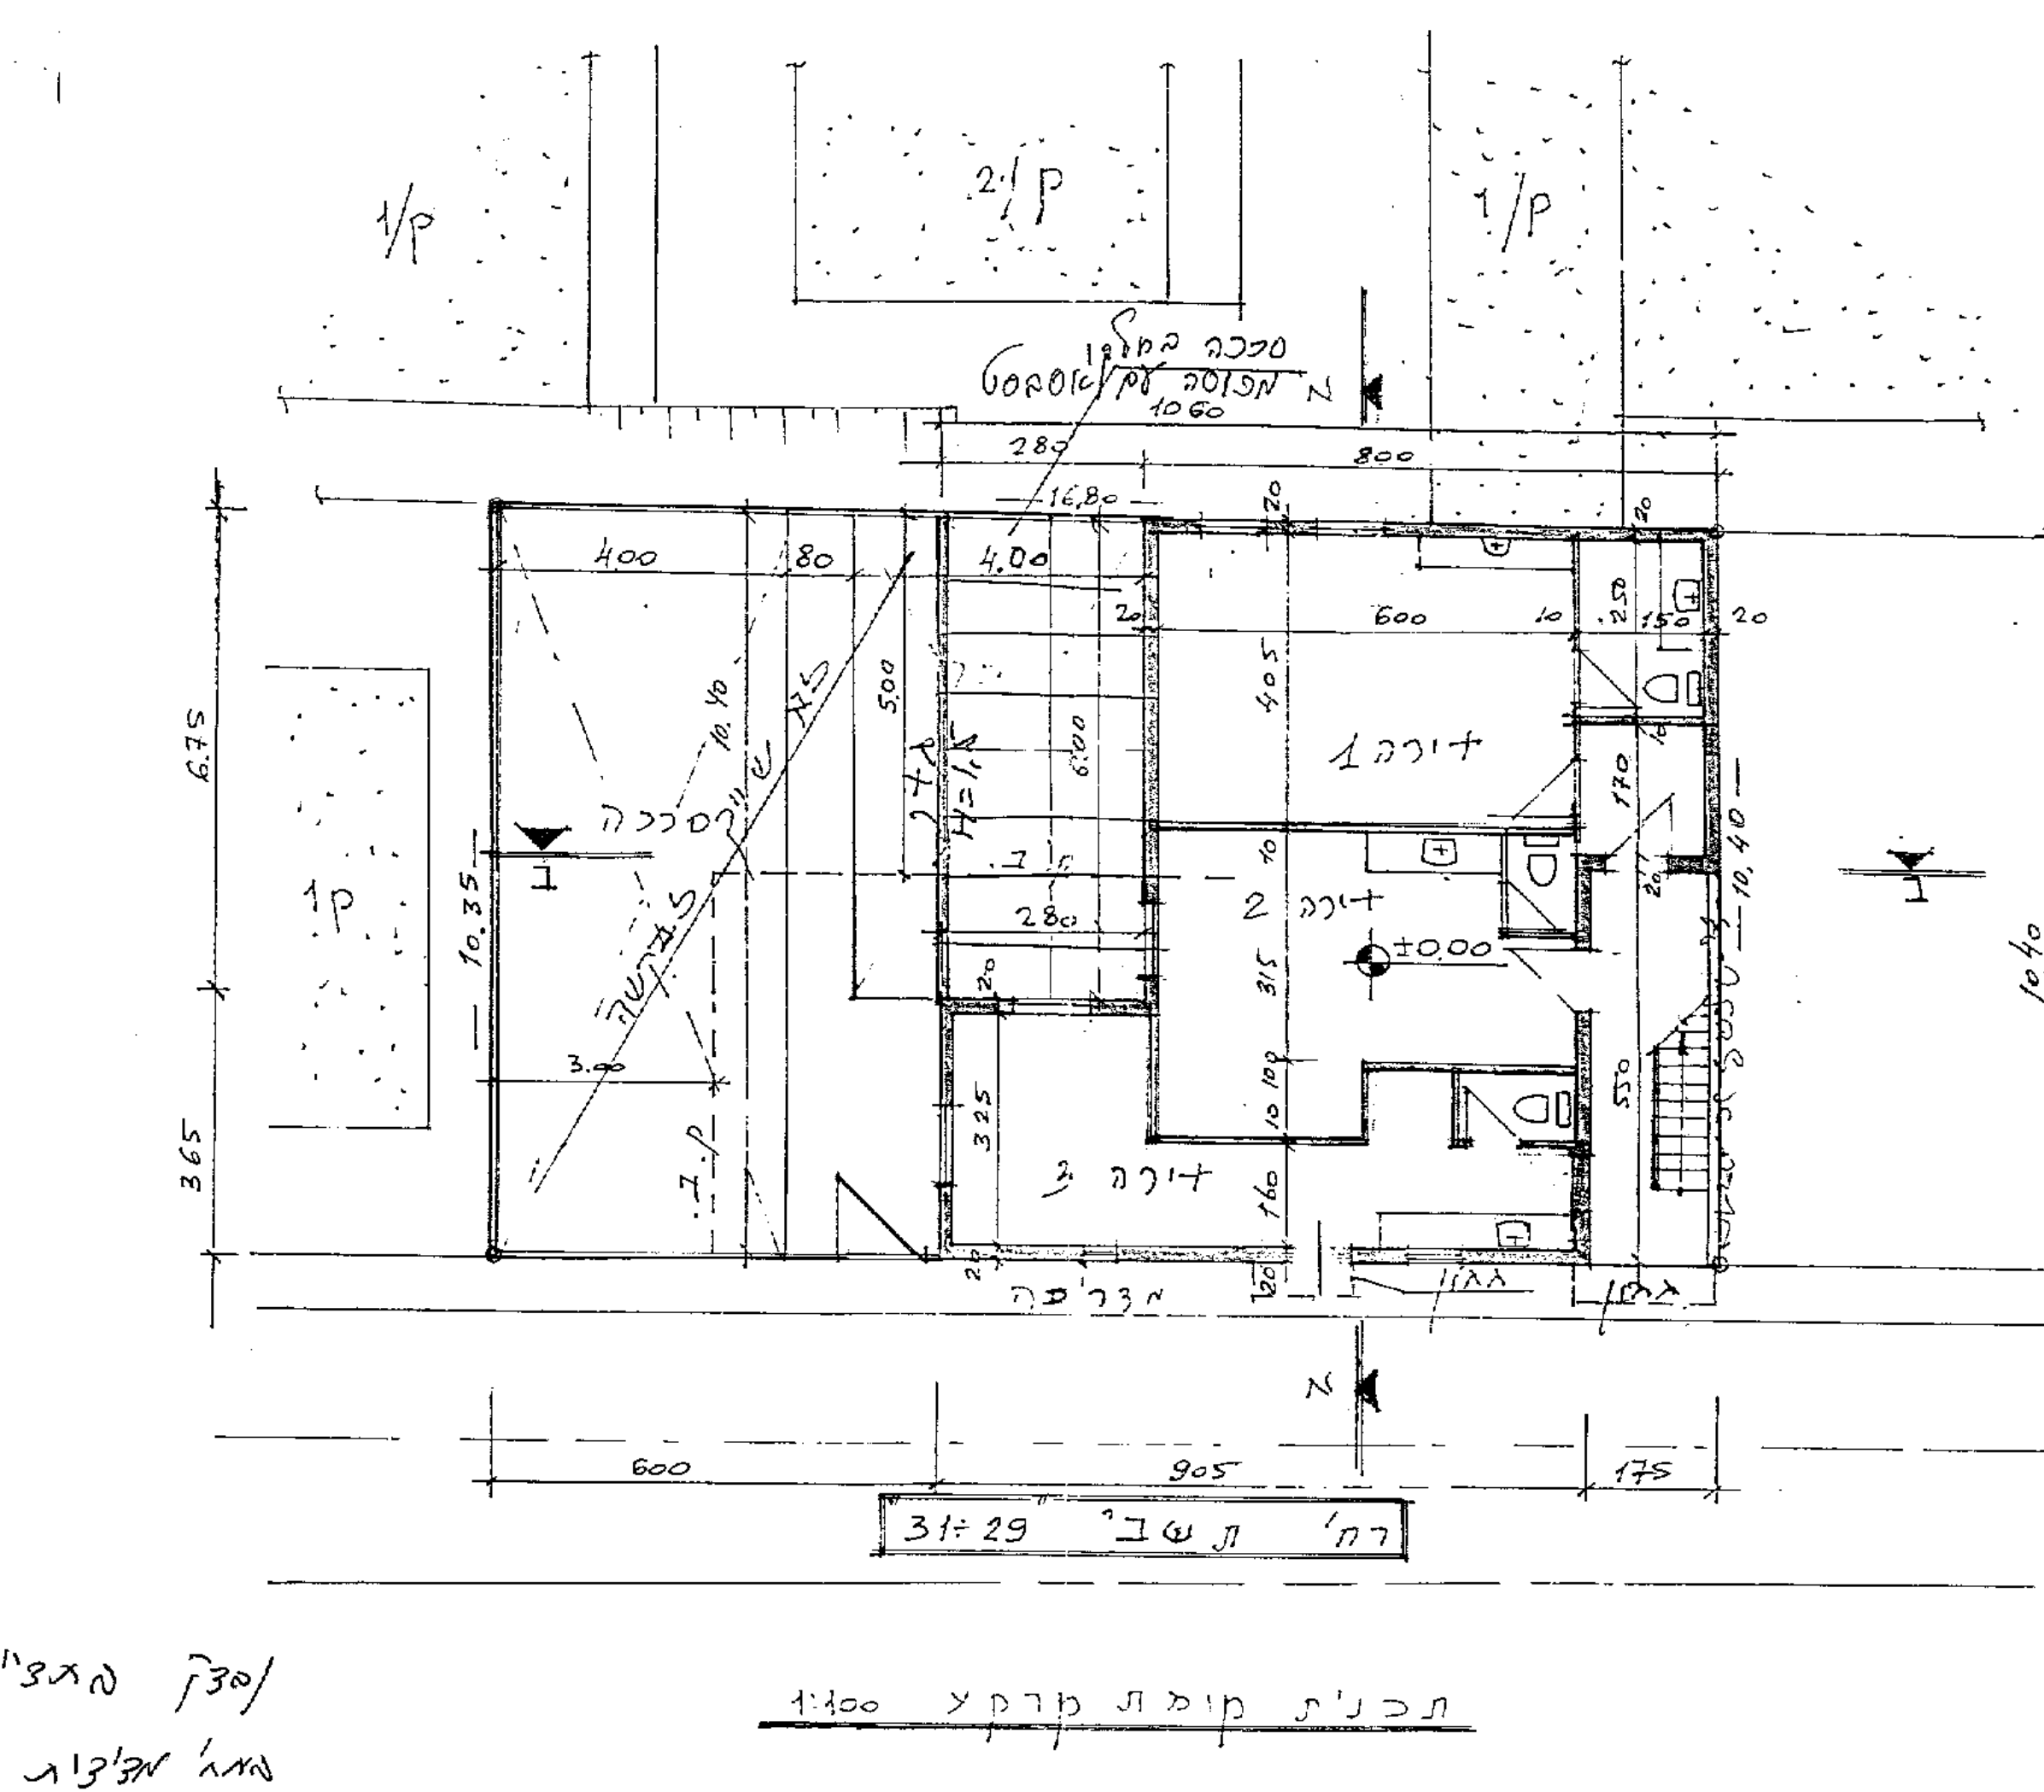

רח' תשבי 31÷29

תכנית קומת קרקע 1:100

נבדק בתצ"א ביום 24.8.01
מאז' מבנית ונמצא שיש [illegible]
בתצלום האוויר 1981.
24/8/01

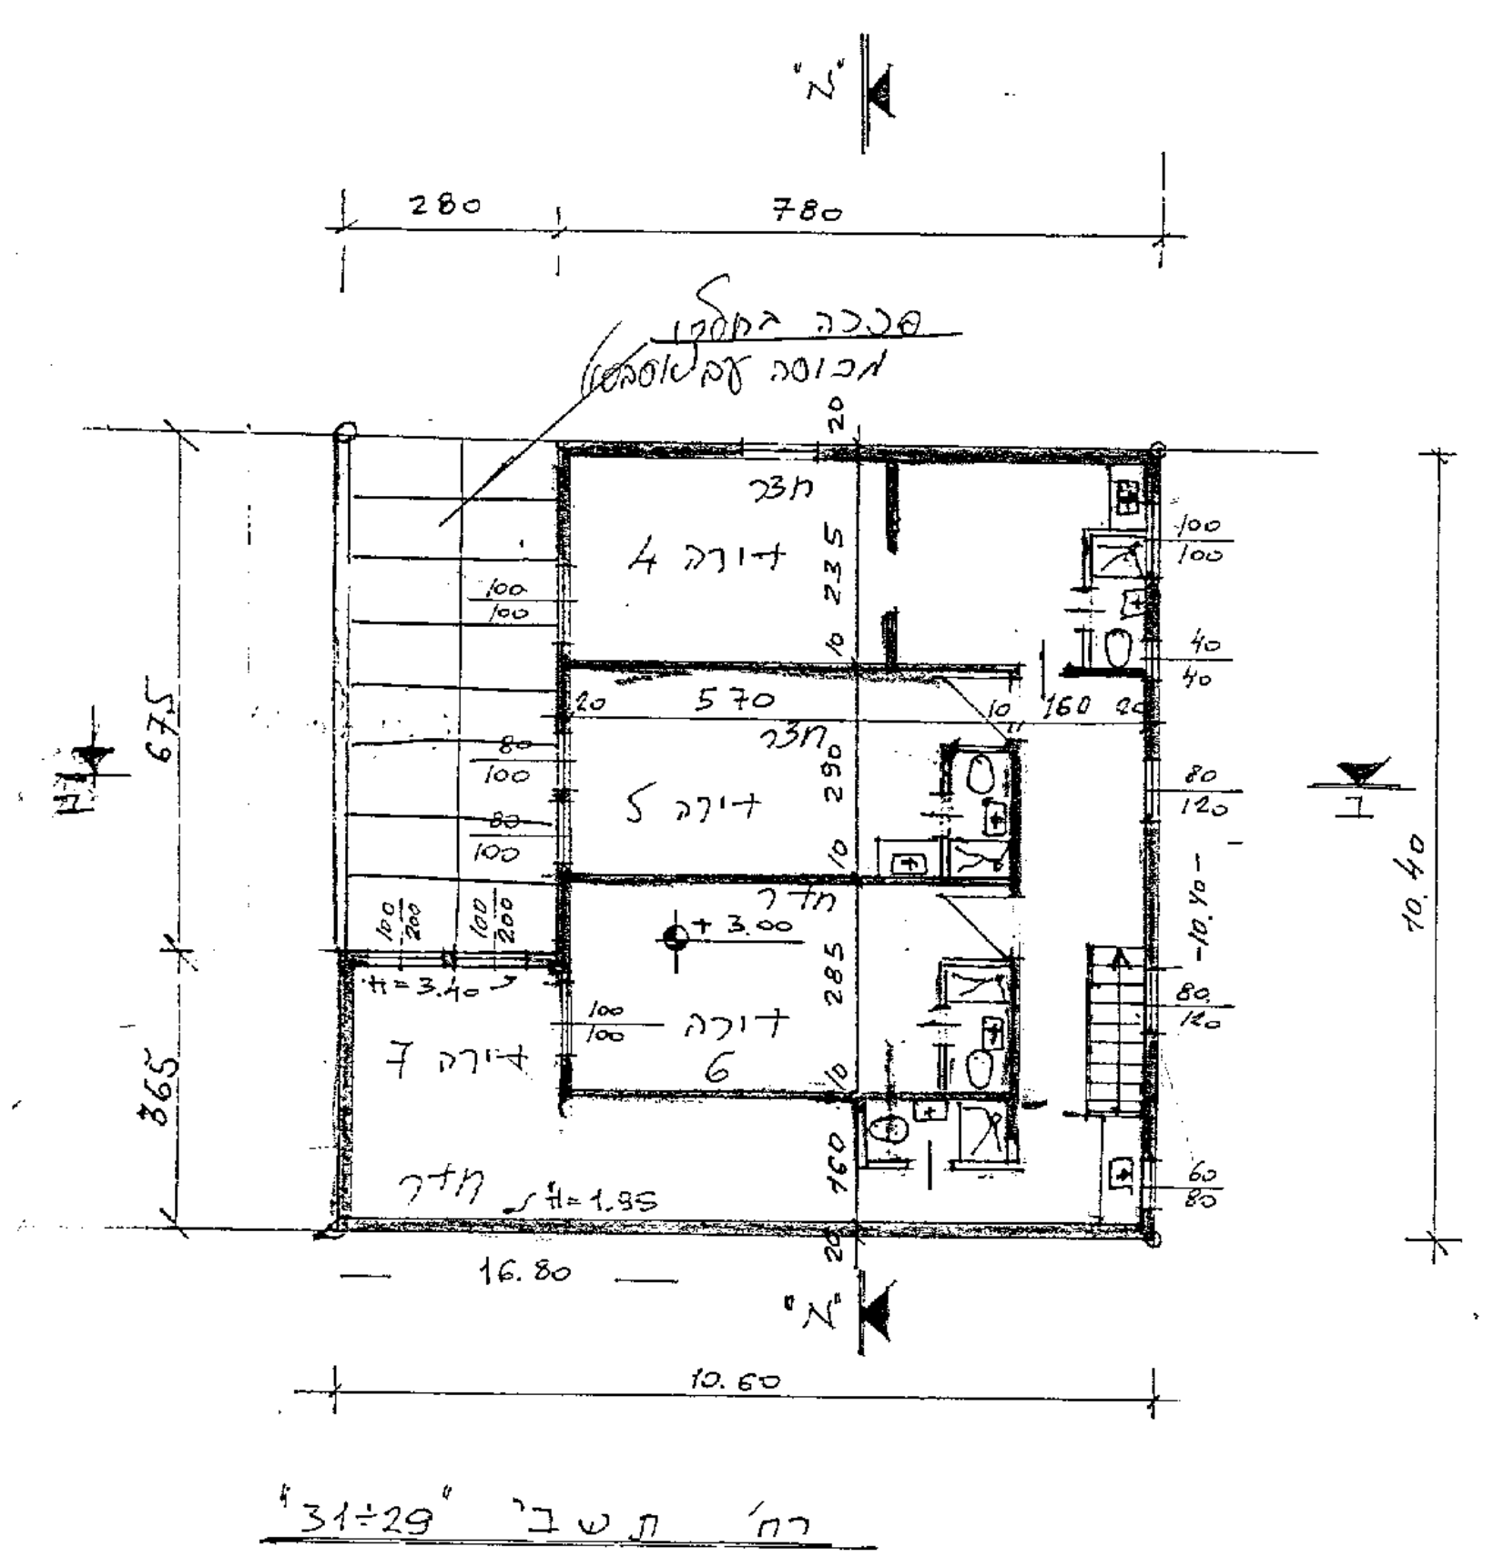

רח' תשבי 31÷29

תכנית קומה "א" 1:100

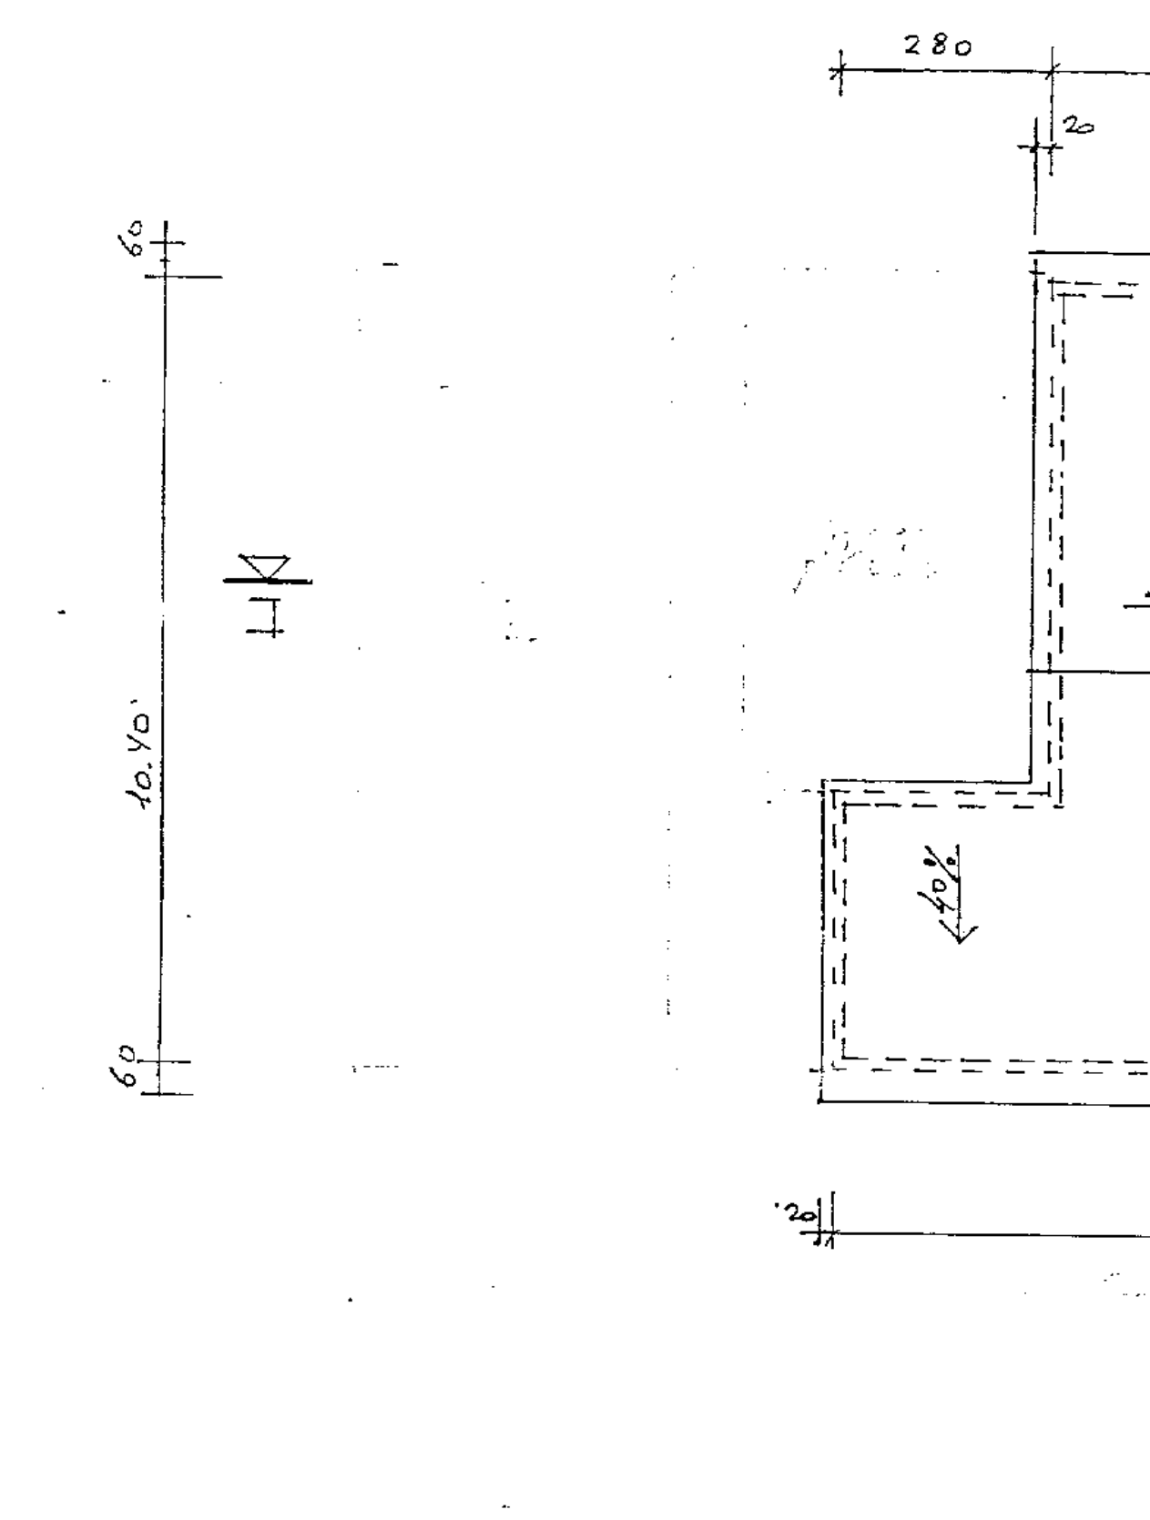

תכנית גג 1:100

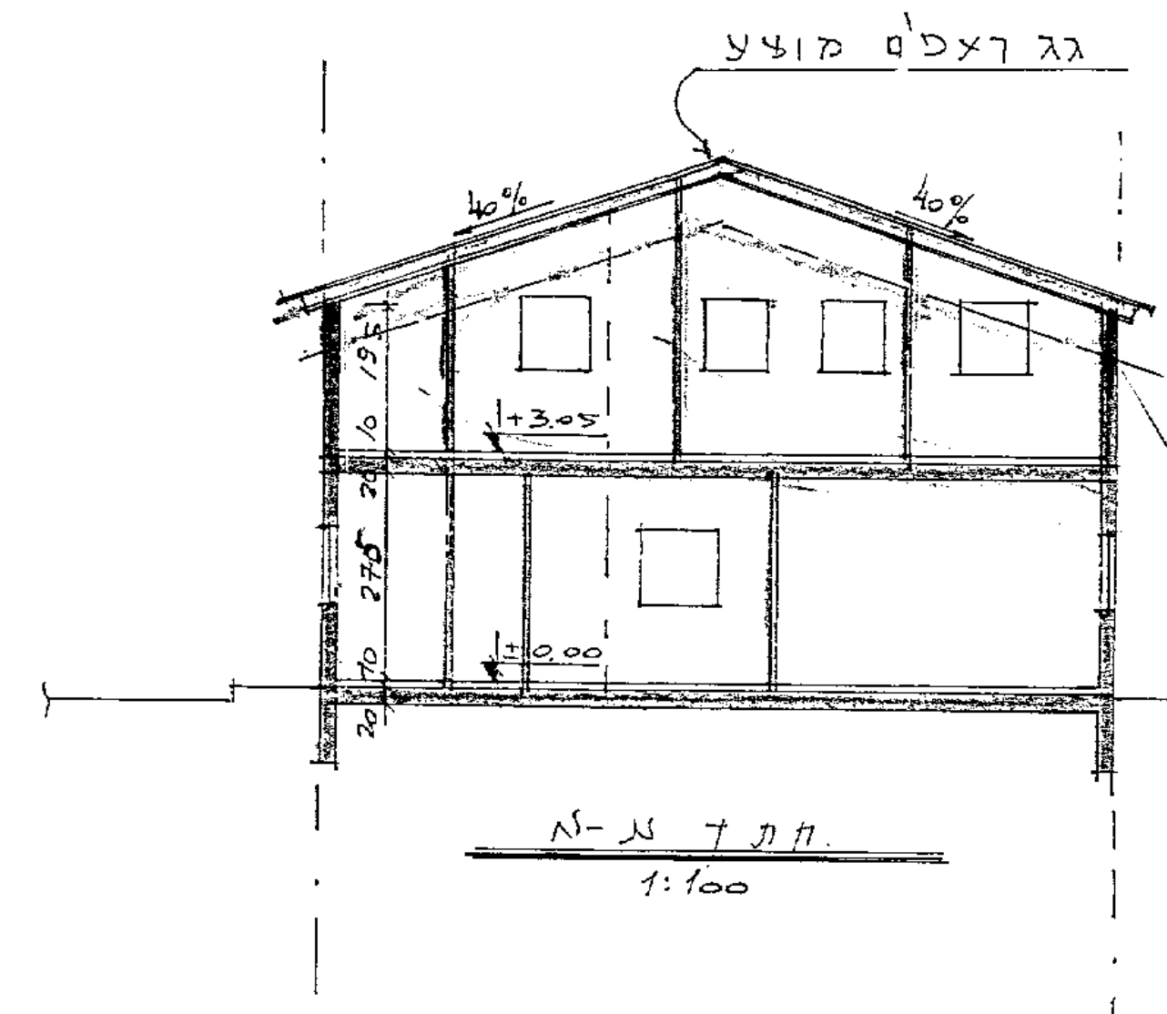

חתך א-א 1:100

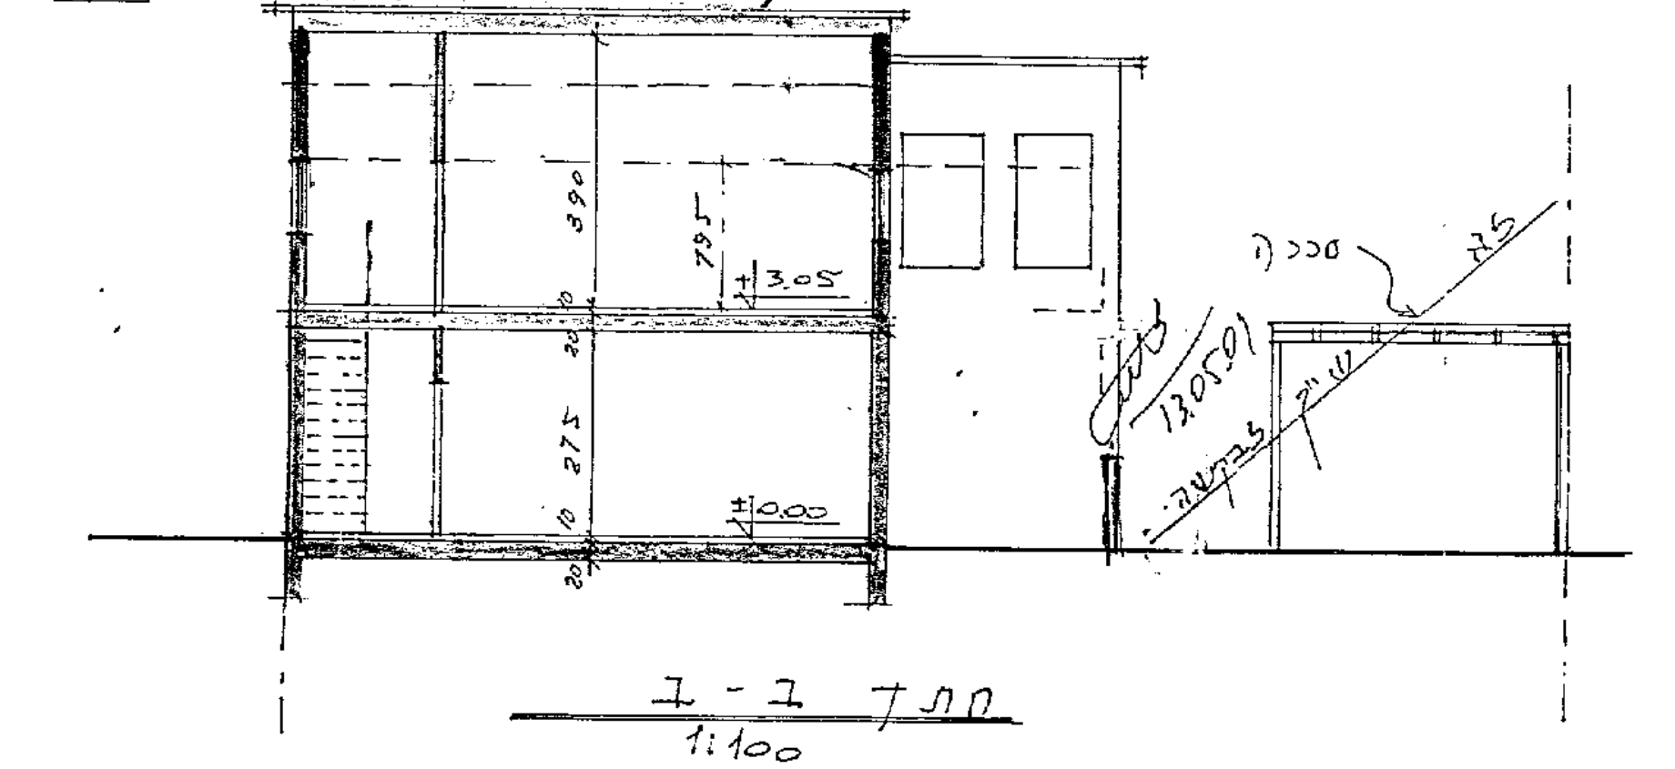

חתך ב-ב 1:100

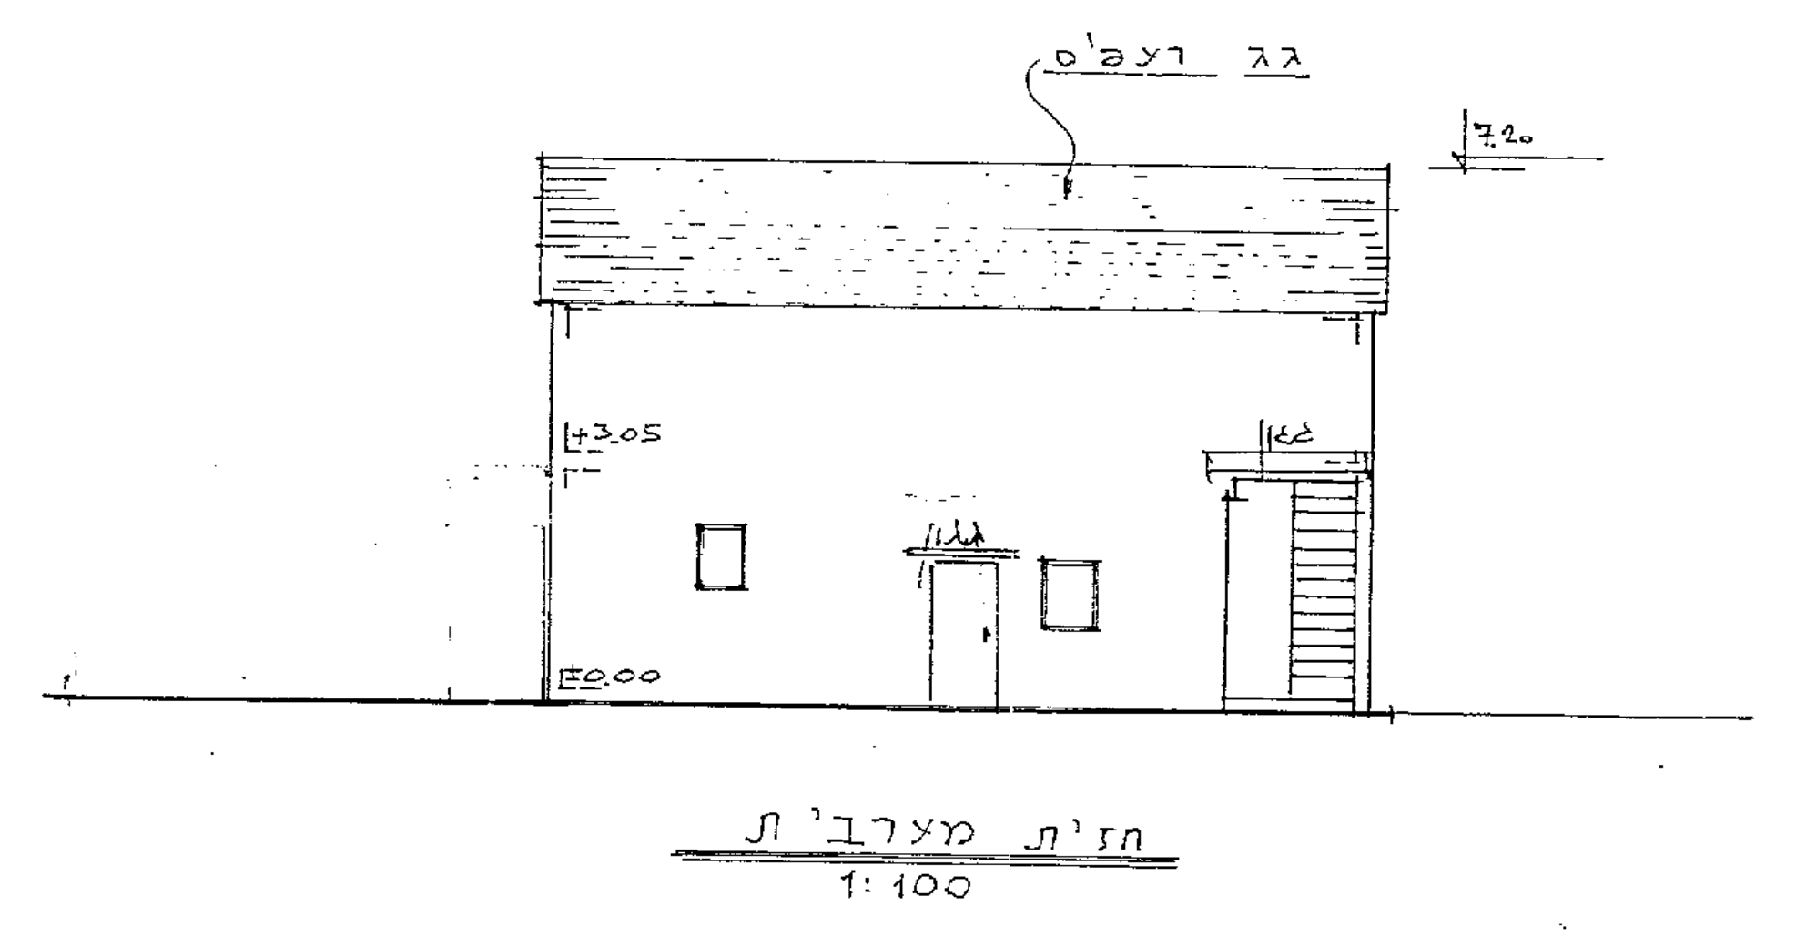

חזית מערבית 1:100

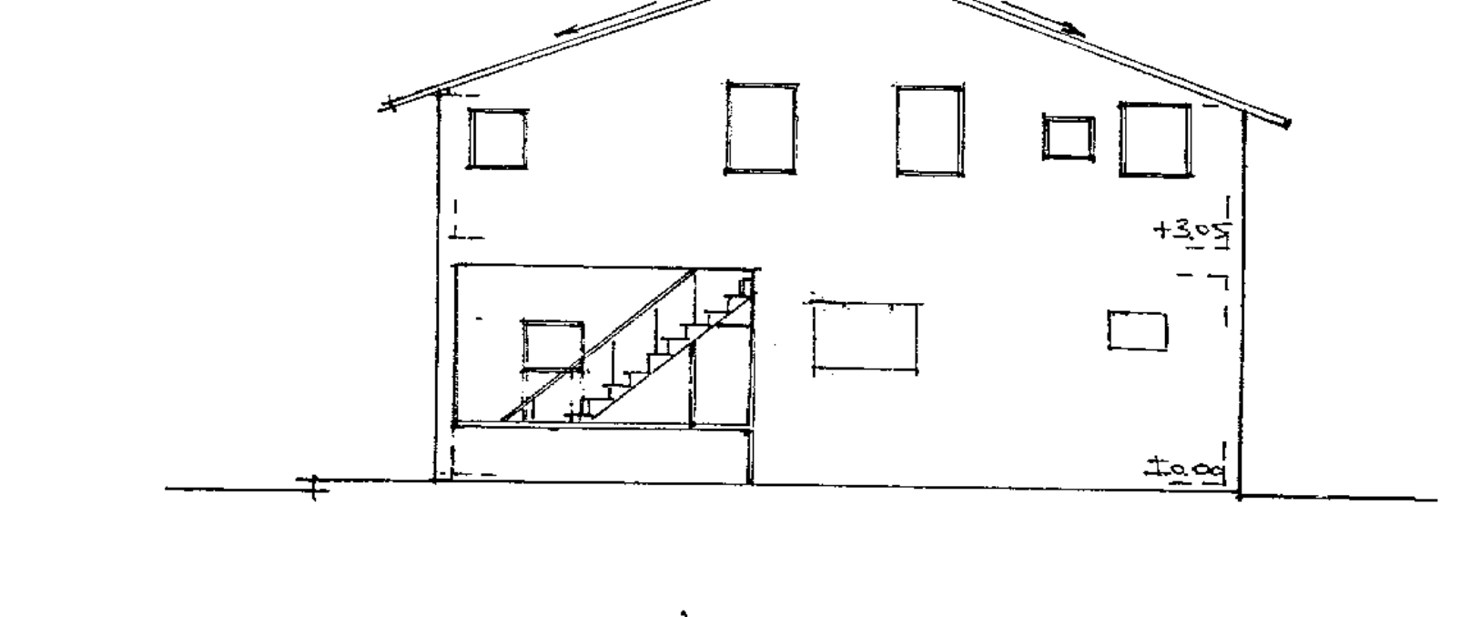

חזית דרומית 1:100

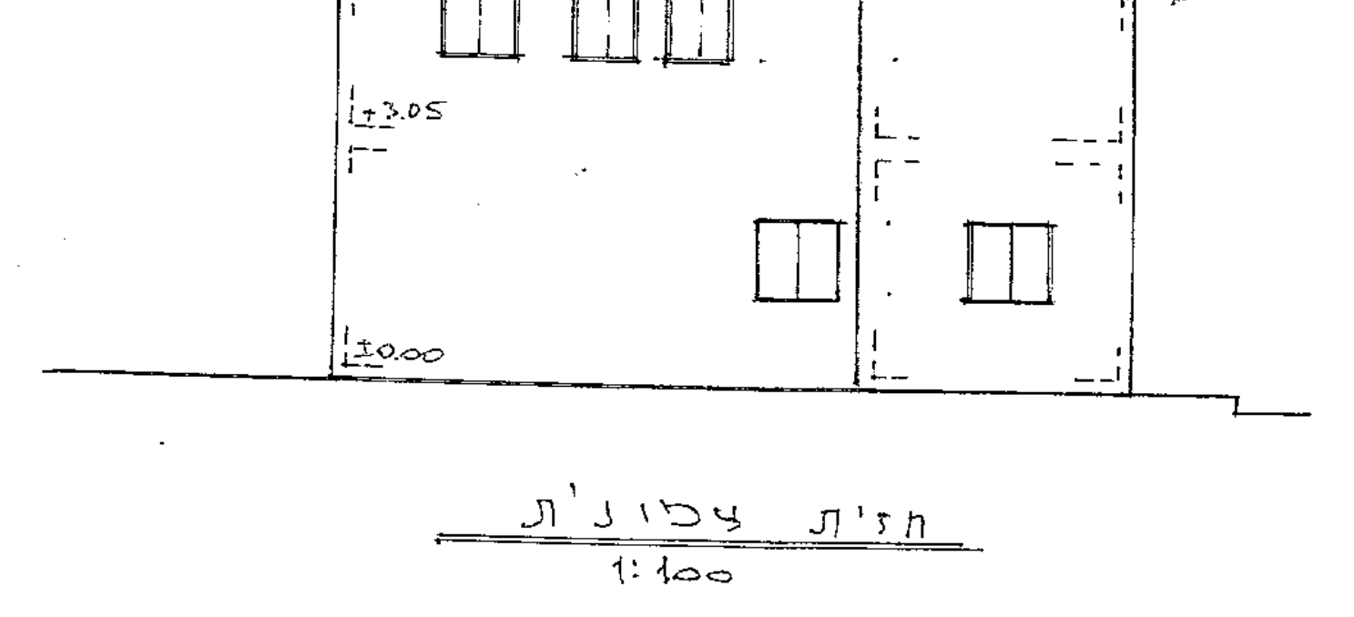

חזית צפונית 1:100

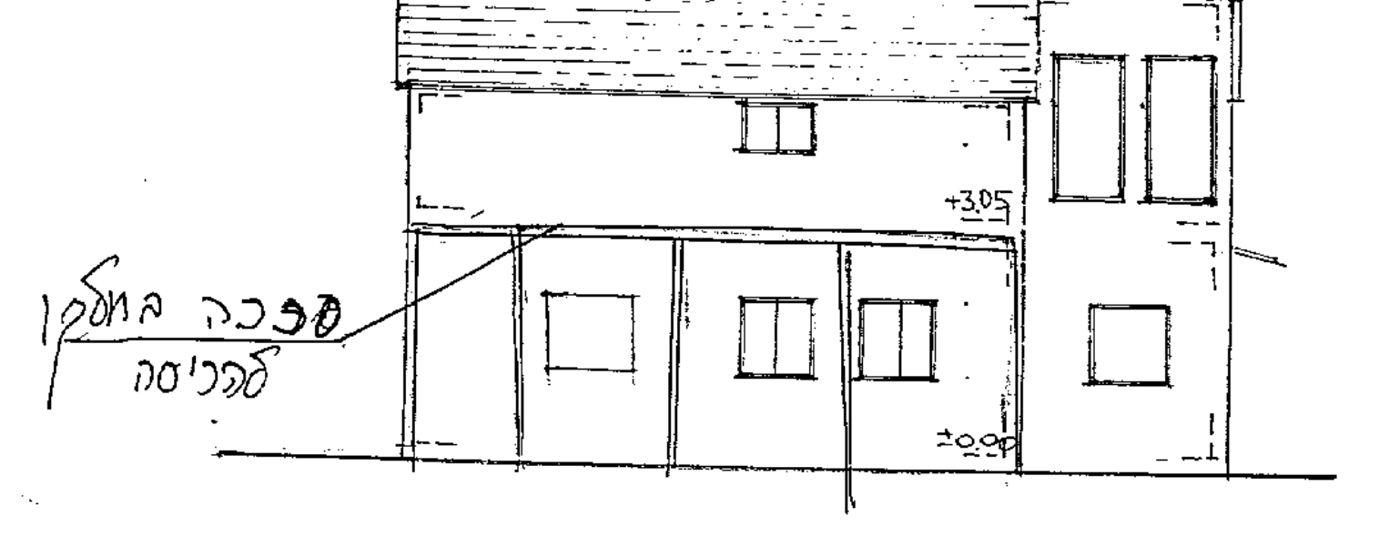

חזית מזרחית 1:100

סוף מסמך