



מנהל ההנדסה / אגף תכנון ובנין ערים
מח' שירותי בנין ערים - מדור המידע

הערות למפה טופ' / מצבית


גוש - 6135 חלקה - 110
מס' תיק מידע 238-21
רח' 4047-תשבי 27 רוחב דרך-8.0
קווי בנין: צד 1 - 3.00 צד 2 - 3.00 אחר - 5.00
יעוד בתוקף - מגורים ב שיקום
תכניות בתוקף - ג, ע, 2215, 1א2215, 2215
תכניות בתכנון - ח
הפקעה
הערות - רחוב 4047-תשבי ברוחב של 8-4 מ', קו בנין 0 מ'.

עיריית תל-אביב
מנהל ההנדסה
מחלקת מדידות

המפה עברה במחלקות:
☒ דרכים
☒ מים
☒ ביוג
☒ הנחיות צוות
☒ אשפה
☒ חניה
☒ נחילי אינן
☒ עדינה כח
חלוקת מדידות
מנהל ההנדסה

קוי הבניה לצדדים 3 מ' ואו 0 מ'.
שיעור הבניה המירבי 140% משטח המגרש, ותכנית
הקרקע לא תעלה על 60% נובה הבנין 3 קומות.
צפיפות הדיוור לפי תכנית 1א2215 לפיה נקבע
כי שטח יחיד לא יקטן מ-90 מ"ר כולל ממ"ד
למעט מקרים בהם הועדה המקומית תהיה רשאית
לאשר עד שתי יחיד לא פחות מ-70 מ"ר כ"א.
עפ"י תכנית "ג" ניתן לבנות עליית גג בחלל
גג הרעפים בבית צמוד קרקע וחדר יציאה לגג
בשטח 23 מ"ר ופרנולה בבנין דירות בתנאים.
לפי תכנית "ע" ניתן לבנות מרתף בחיקף הבנין
לשימוש דיירי הבנין.
אין היטל השבחה כל עוד השכונה מוכרזת לשיקום.
תיאום הבניה עם צוות תכנון מזרח.

הסדר המגרש והקרקע חסר כולל לכל הגוש.
סוכן (שלוש)
ממונה על פיקוח ומקרקעין
אגף מבנה ובנין ערים
חתימה
15-02-2001
14.2.2001

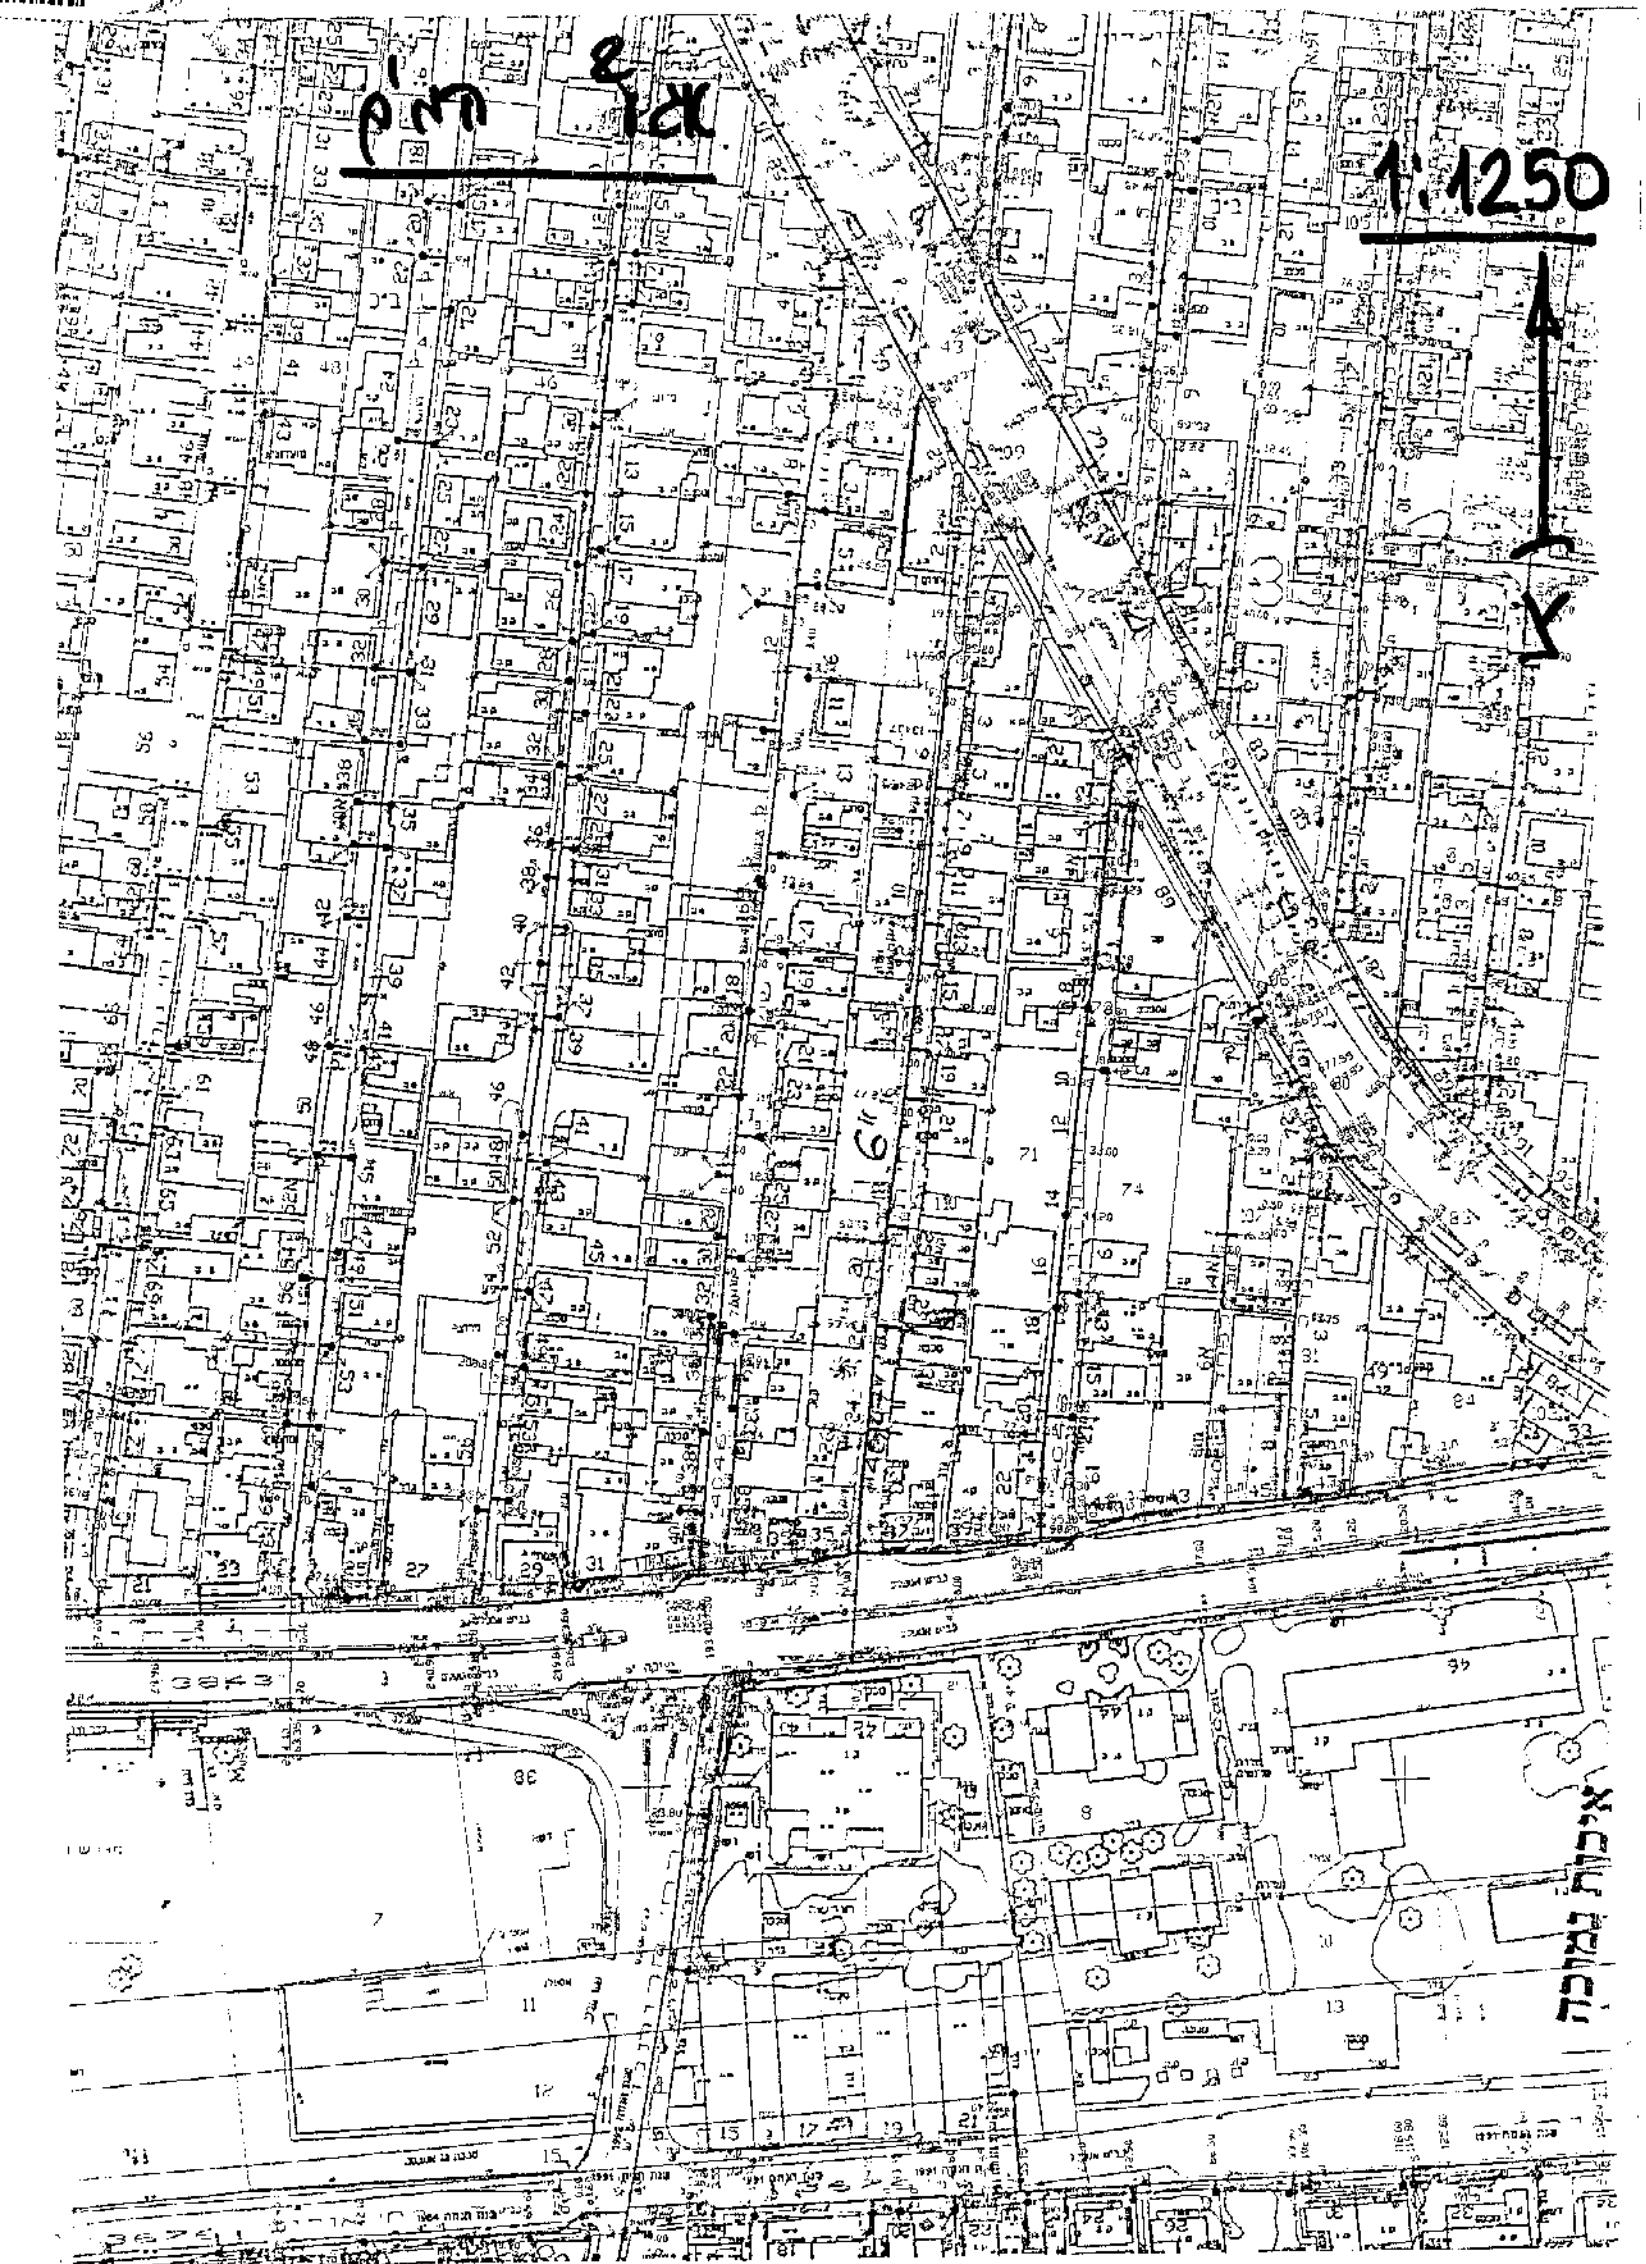

תל-אביב-יפו מפה טופוגרפית

שכונת התקווה

גוש : 6135

חלקה 110 (חלק)

רח' תשבי 27

הוכן עבור: סושניק גולין


מהות הבקשה: התר בניה

שטח לפי נסח טאבו : 112 מ"ר

שטח מדוד : 76 מ"ר



תושים סביבה
קנה מדה 1:1250

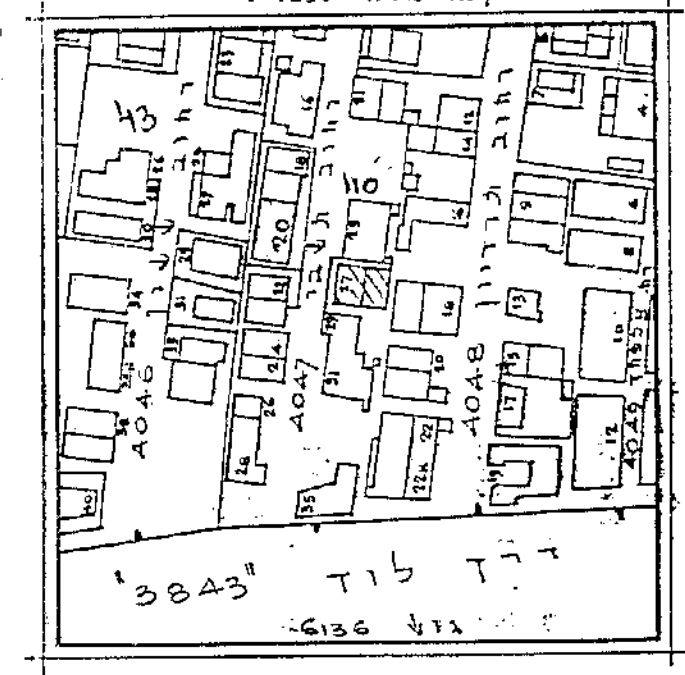

עיריית תל-אביב-יפו
מנהל ההנדסה
מחלקת מדידות


עיריית תל-אביב-יפו / מנהל ההנדסה
מחלקת המדידות

אישור כתובת
רחוב תשבי מס' 27
רחוב מס' 27
רחוב מס' 27
תאריך 15.11.00

הערות:

- הגבהים מבוססים על נק. של רשת האיזון העירונית שאובה 17.549 מ'.
- הגבהים נרשמו בסוגריים.
- ייתכנו שינויים בשטחים ובמידות בעת עריכת תכניות לצרכי רישום והסדר הקרקע אצל רשם המקרקעין.

מס' סדורי 2000 \ 2073

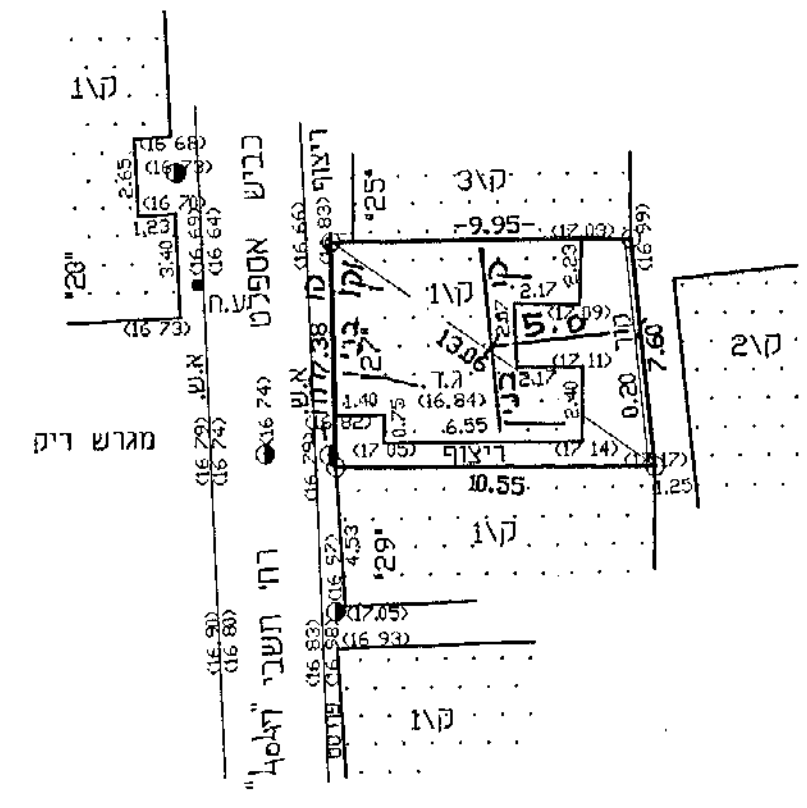

לא לצרכי רישום

הנני מצהיר בזה שהמפה נעשתה לפי חוק התכנון והבניה, התקנות וההנחיות של עיריית תל אביב יפו

תל-אביב 8.11.2000 מודד מוסמך
ראובן לאופר - מודד מוסמך מס' רשיון 574
משרד סכני למדידות
משרד: רח' הרבנות 20 תל - אביב טל': 5608221 - 03
מען: רח' בורלא 32 תל - אביב טל': 6993398 - 03

(52) 171787 'חזק' 171788

① כ"ס / תכנ"ל / מחלקת המחקר / 4048 - מסמך 2810

② מח' חשב' 4047 העלמי' תכנן / מפורט - לא עפלות ע'אח' אכס' ושקיה ע
פ'ר'ר' פ'ר'ר' (521-72-34, 521-72-72)

עו"ת: חל-אביב י"ט
 שם: ד"ר ח' ש"ח - א"ר עובד
 חלק: חדרים
 נא להכין נתיב בקר רחוק
 מס': 1047
 לני חבה בבית קים 1/2 טונה
 אקט טונה על 15 ס"מ + טמט 2
 לחורב הסדוקה.
 חת: פה
 תאריך:

③

עיריית תל-אביב-יפו
מח' דרכים
יג' שטלה שוורץ

מחלקת הדרכים - מדור המדרכות
מחובו של המבצע להודיע לעדור המדרכות
על המועד למילוי הדר כדי להימנעם. לעדור
היקות, כדי למנוע כתנאי המעורבות העירוניים
לא וניתן תעודת נמר
ללא אישור המפקח על בד

⑥

עיריית תל-אביב-יפו
מנהל בנין ומשתת - אגף עבודות ציבוריות
מהלקת דרכים
מ"ב
שישה הורשים לפני בצוע עבודות ציבוריות
המדרגה על הקבלן להגיע בקשה
לתאום הורסי במהלקת תאום הורסי
חדר וועד רחוב פילון 5, תל-אביב
החיסה
תאריך

ס' דרכים - מדור מדרכות
הוא למתן אישור לביצוע היתר התחייבות
של מבקש הרישוי לעשיית המדרכה כולה
יש לבצע את עשיית המדרכה בהתאם
להתחייבות ואישור מדור מדרכות של
ס' דרכים לפי חכמת פתח סאשרת.

תכנית פתוחה ושטח יש להגיש.
לאישור מח' דרכים לאחד אישור
של אגף התנועה

מחלקת הדרכים - מדור המדרכות
 תנאי למתן היתר הינה התחייטת כתובה של
 מבקש ההיתר לתחזק את המדרכה שבחזית
 אתר העבודה בצורה שתבטיח רלויה בטוחה
 בכל תקופת העבודות, עד לסלילת המדרכה
 המתוכננת והמאוסרת.
 העבודה תתואם עם מדור המדרכות -
 כדי לעמוד במפרטים של עירונית תיא.

5

הואם התעורר כמי שהתבצע בתוך הסיוע ייעוץ: ~~לא לפני הגשת הבקשה לחוקה~~

(4)

~~28.02.2001~~