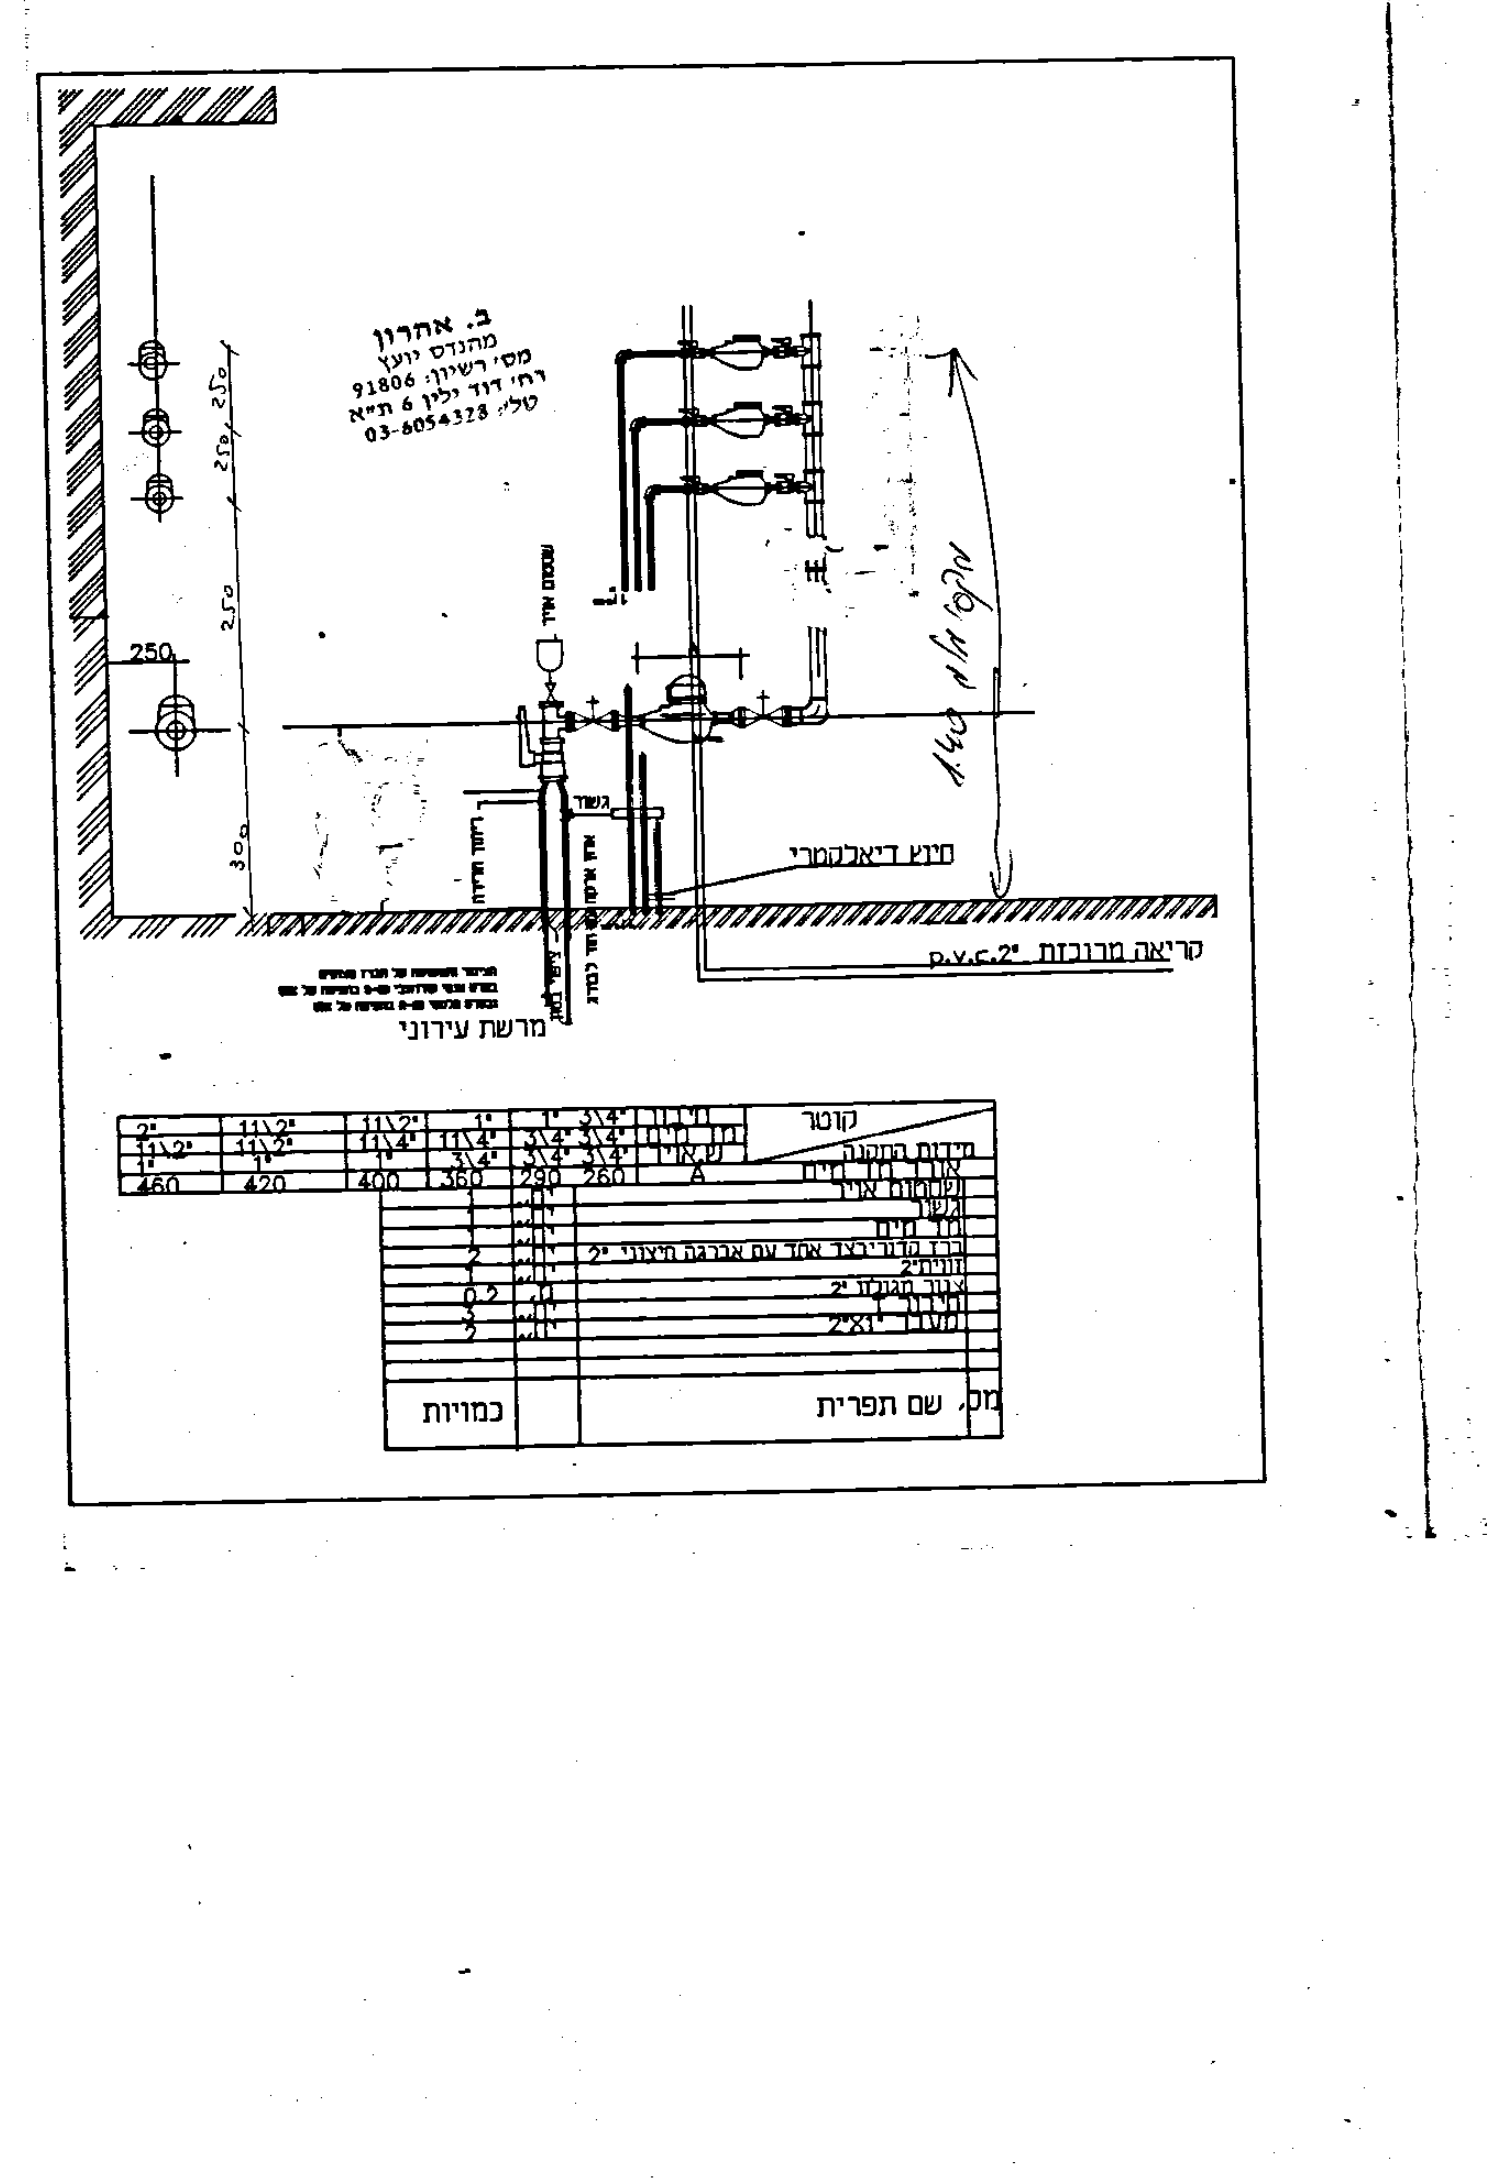

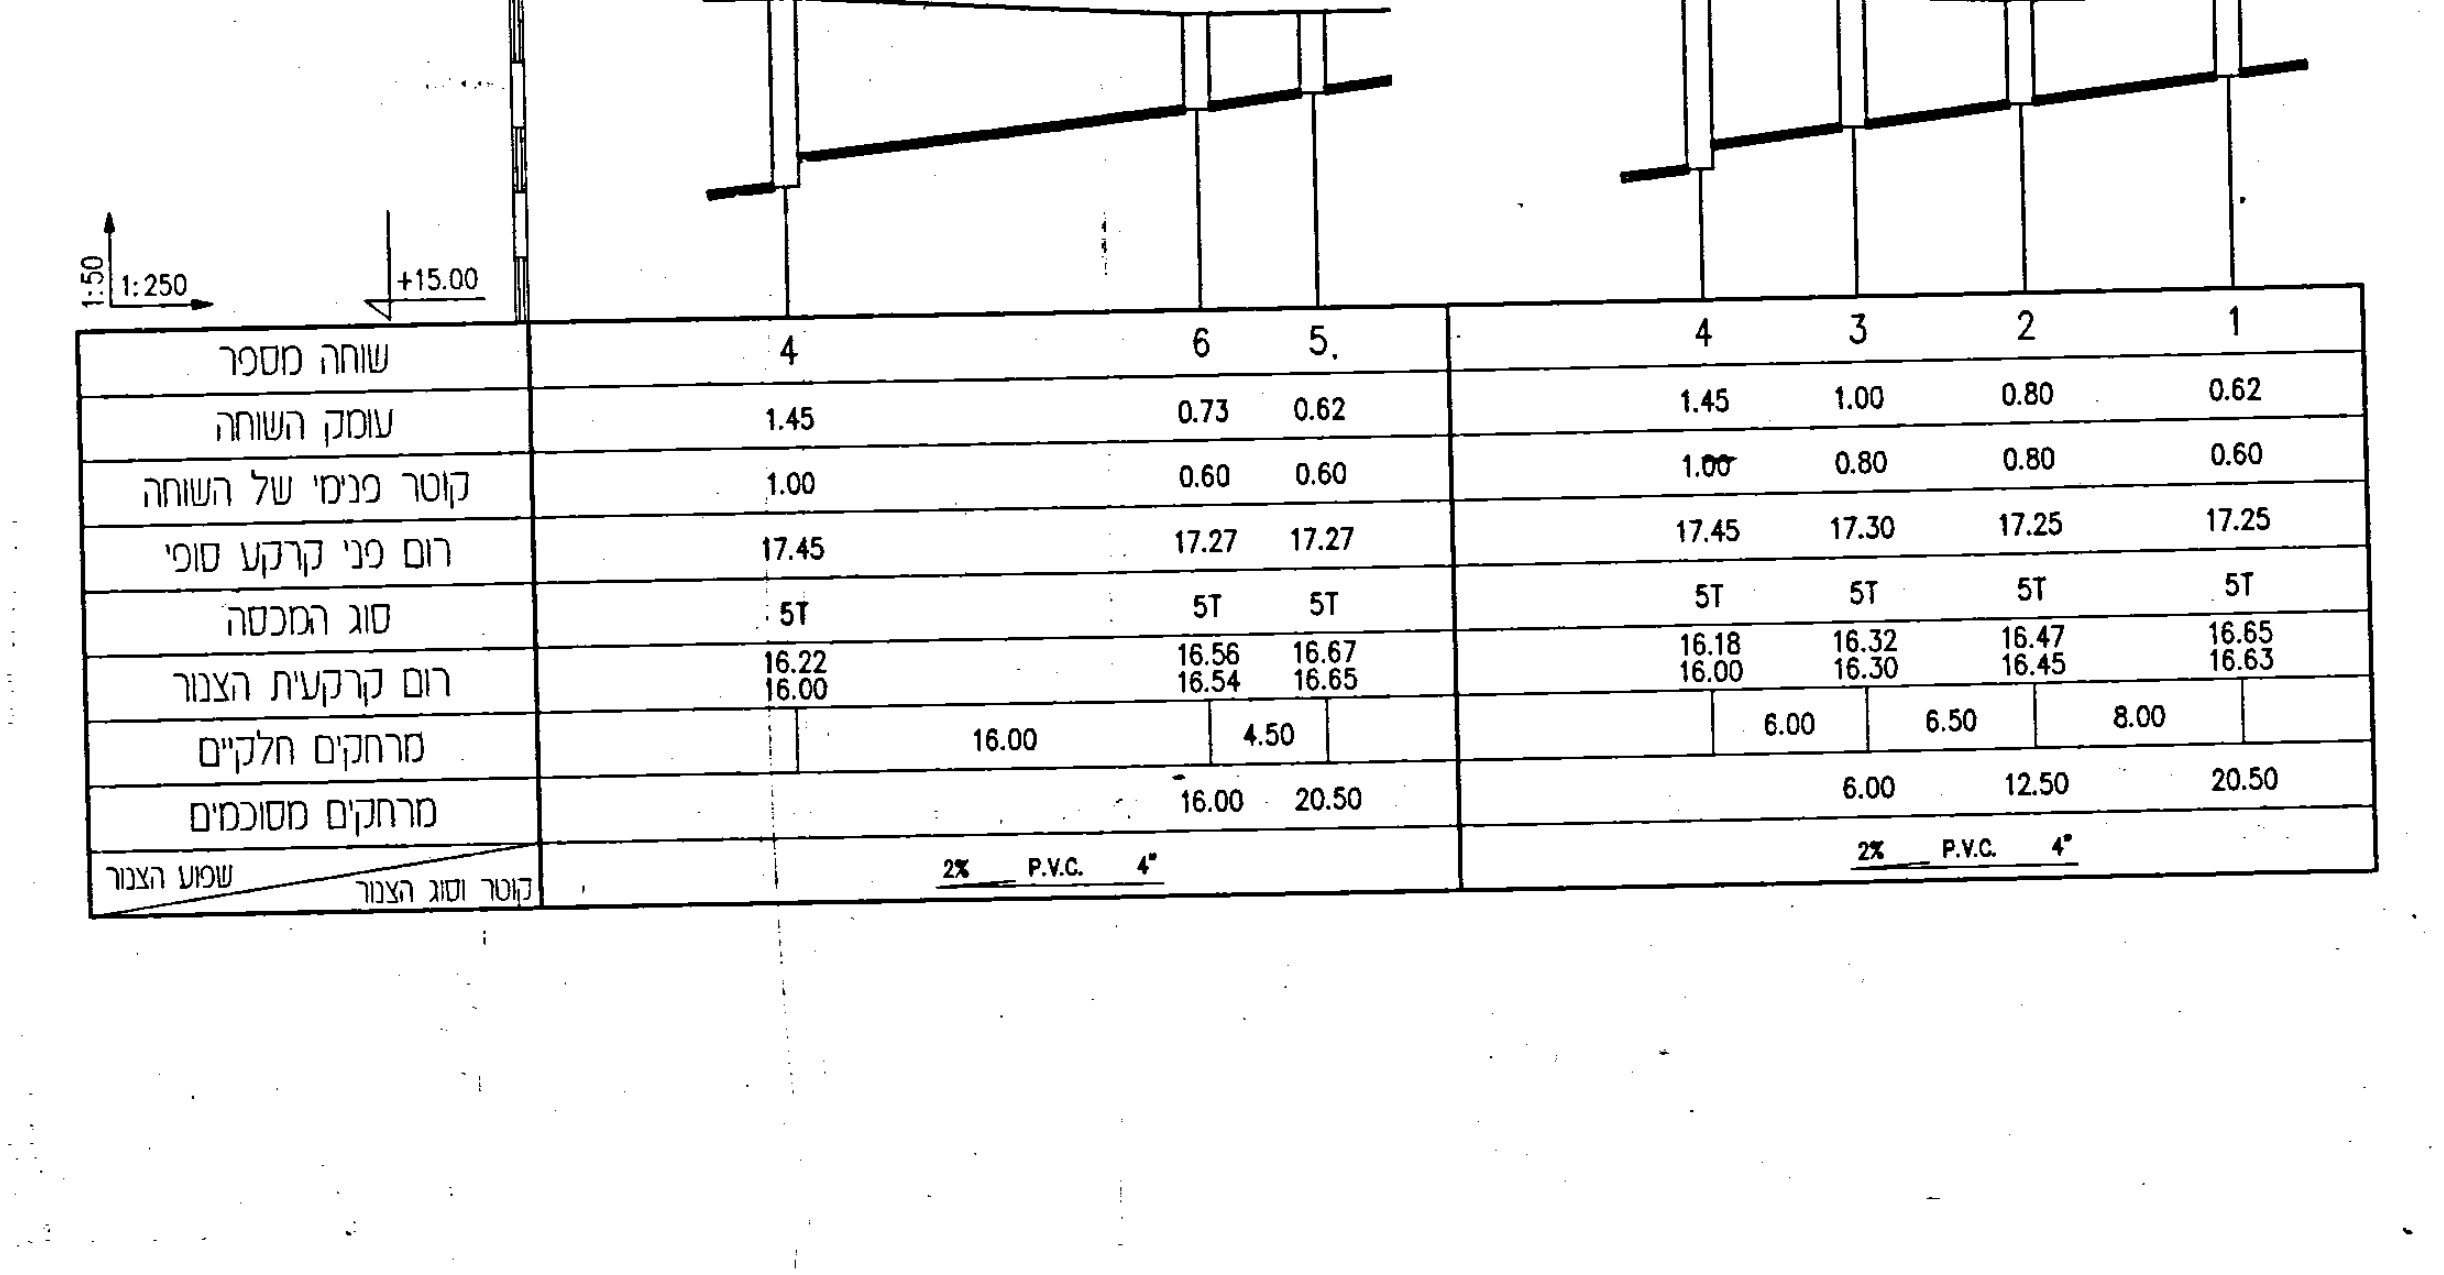

	4	6	5	4	3	2	1
שוחה מספר	4	6	5	4	3	2	1
עומק השוחה	1.45	0.73	0.62	1.45	1.00	0.80	0.62
קוטר פנימי של השוחה	1.00	0.60	0.60	1.00	0.80	0.80	0.60
רום פני קרקע סופי	17.45	17.27	17.27	17.45	17.30	17.25	17.25
סוג המכסה	5T	5T	5T	5T	5T	5T	5T
רום קרקעית הצנור	16.22 16.00	16.56 16.54	16.67 16.65	16.18 16.00	16.32 16.30	16.47 16.45	16.65 16.63
מרחקים חלקים	16.00	4.50		6.00	6.50	8.00	
מרחקים מסוכמים		16.00	20.50		6.00	12.50	20.50
קוטר וסוג הצנור שיפוע הצנור	2% P.V.C. 4"			2% P.V.C. 4"			

סכמת ביוב ומים

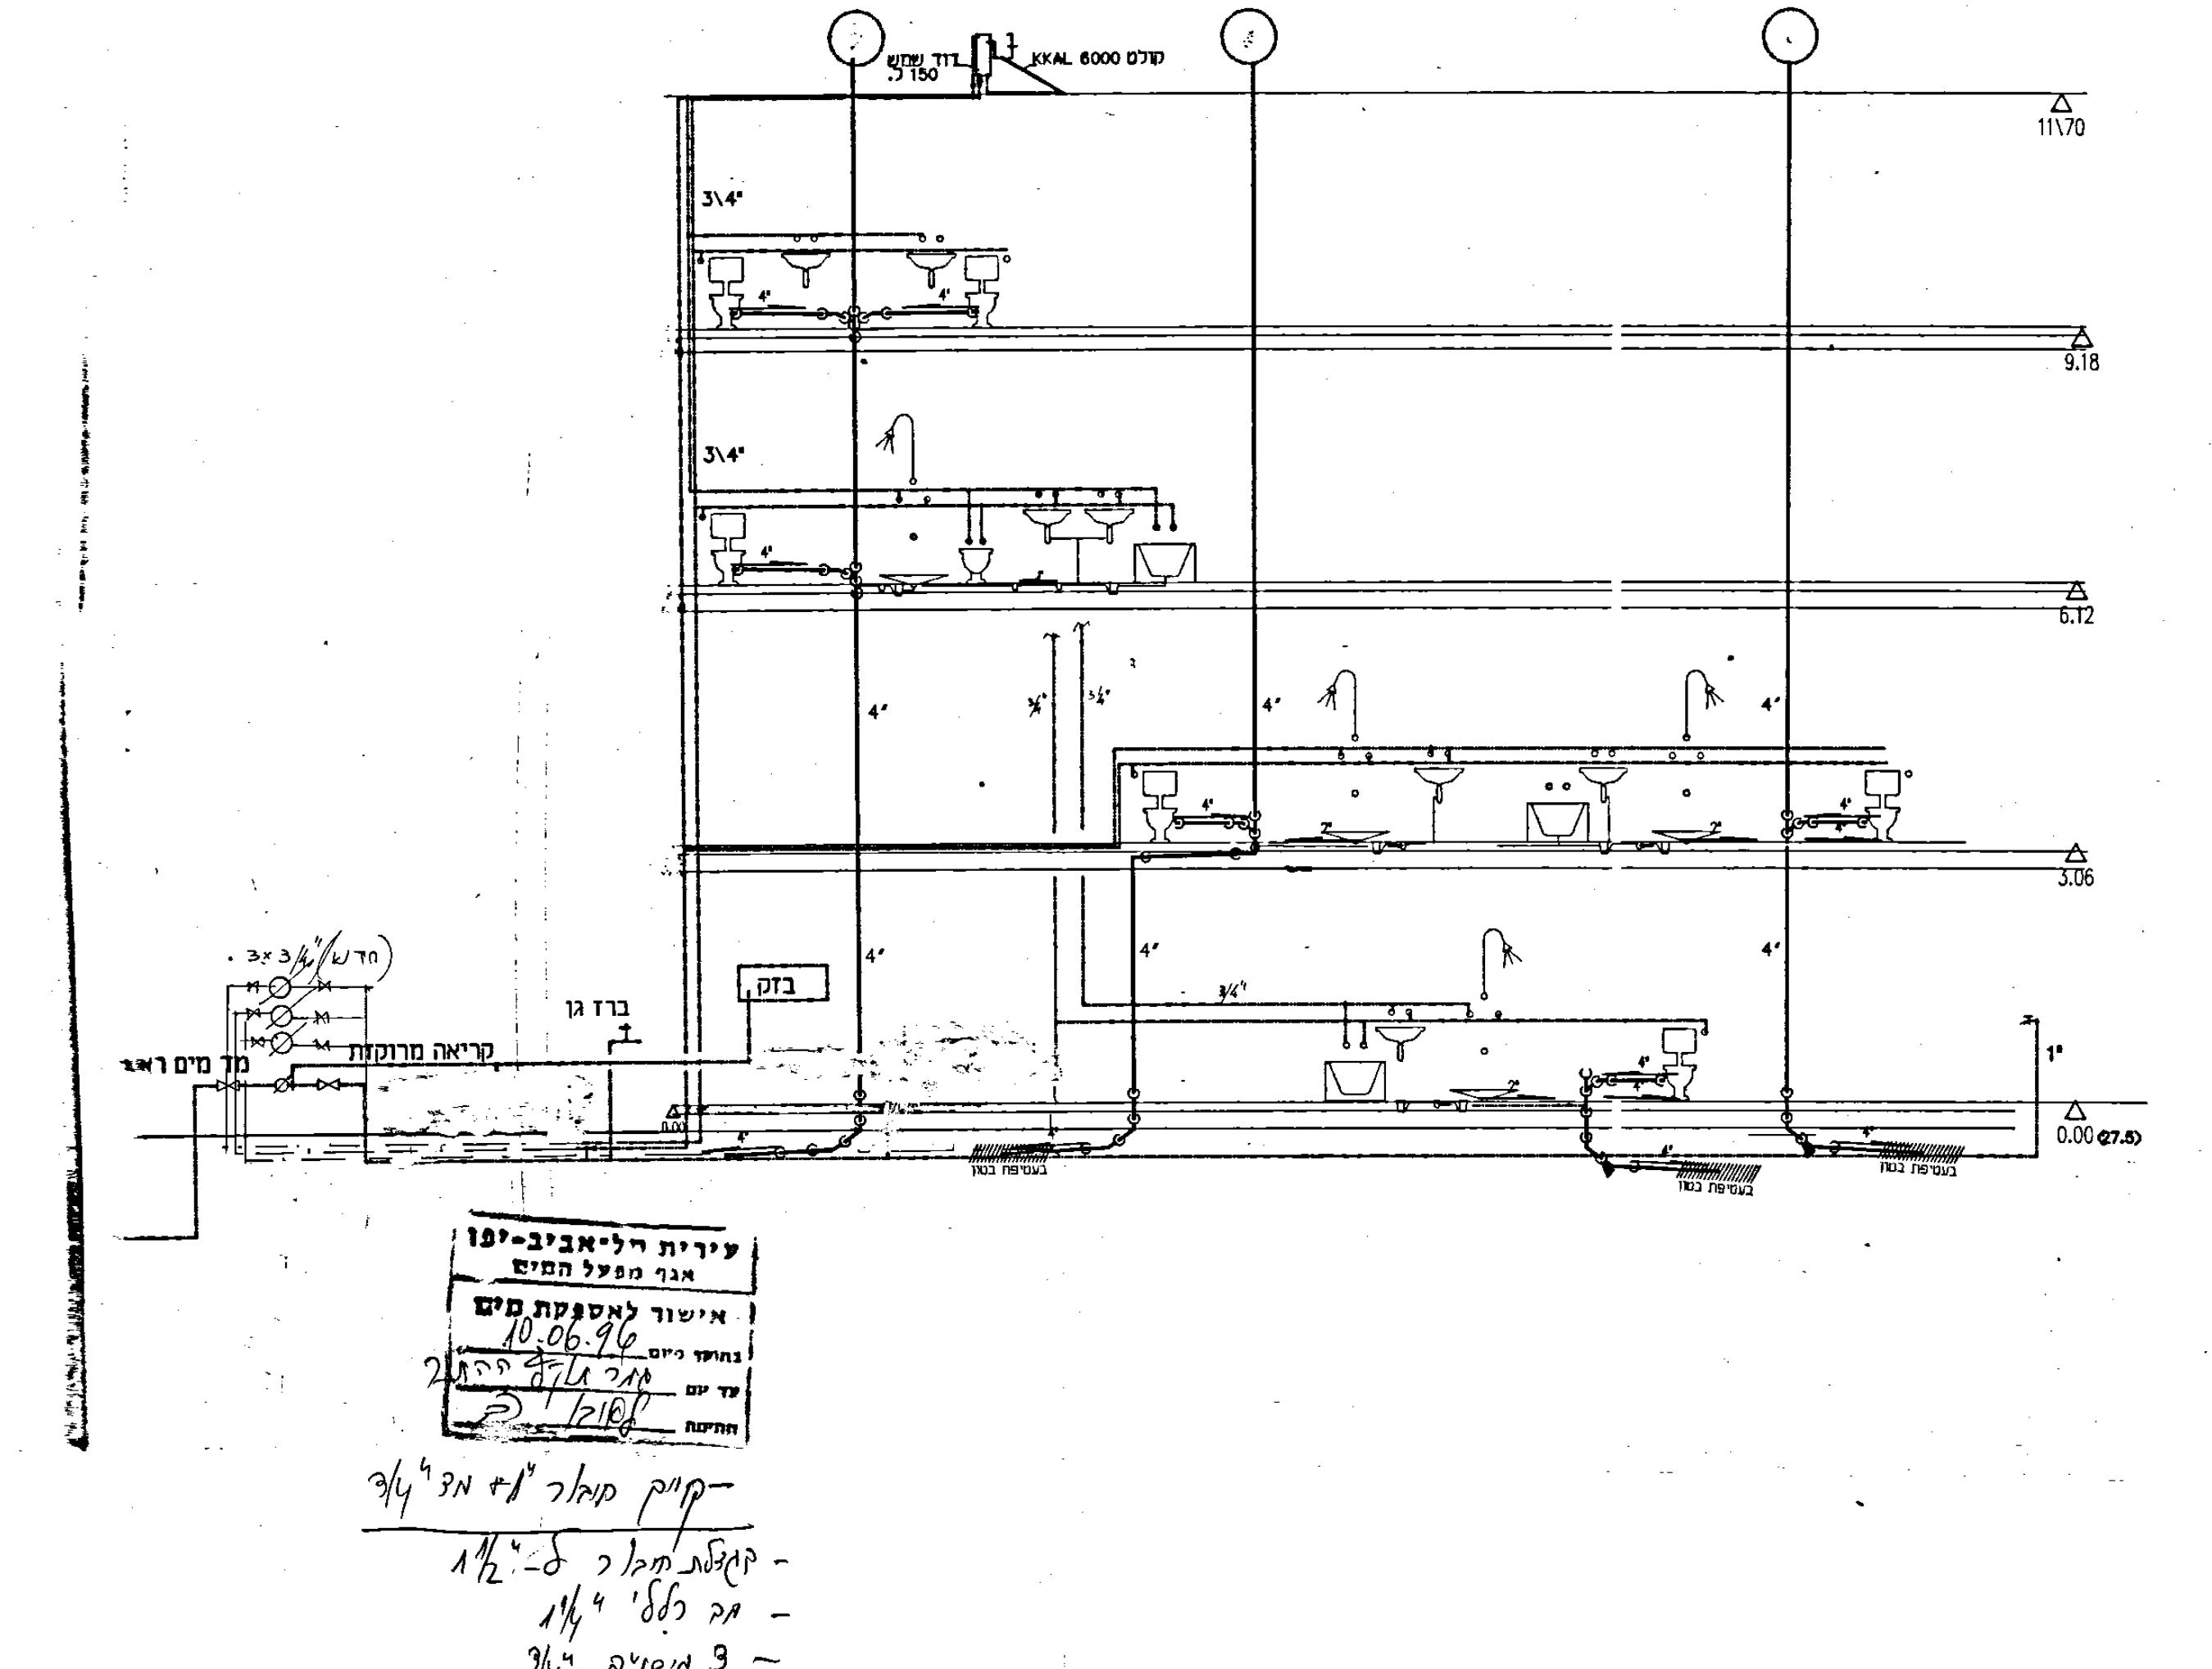

עירית תל-אביב-יפו
אגף מפעל המים
אישור לאספקת מים
10.06.96

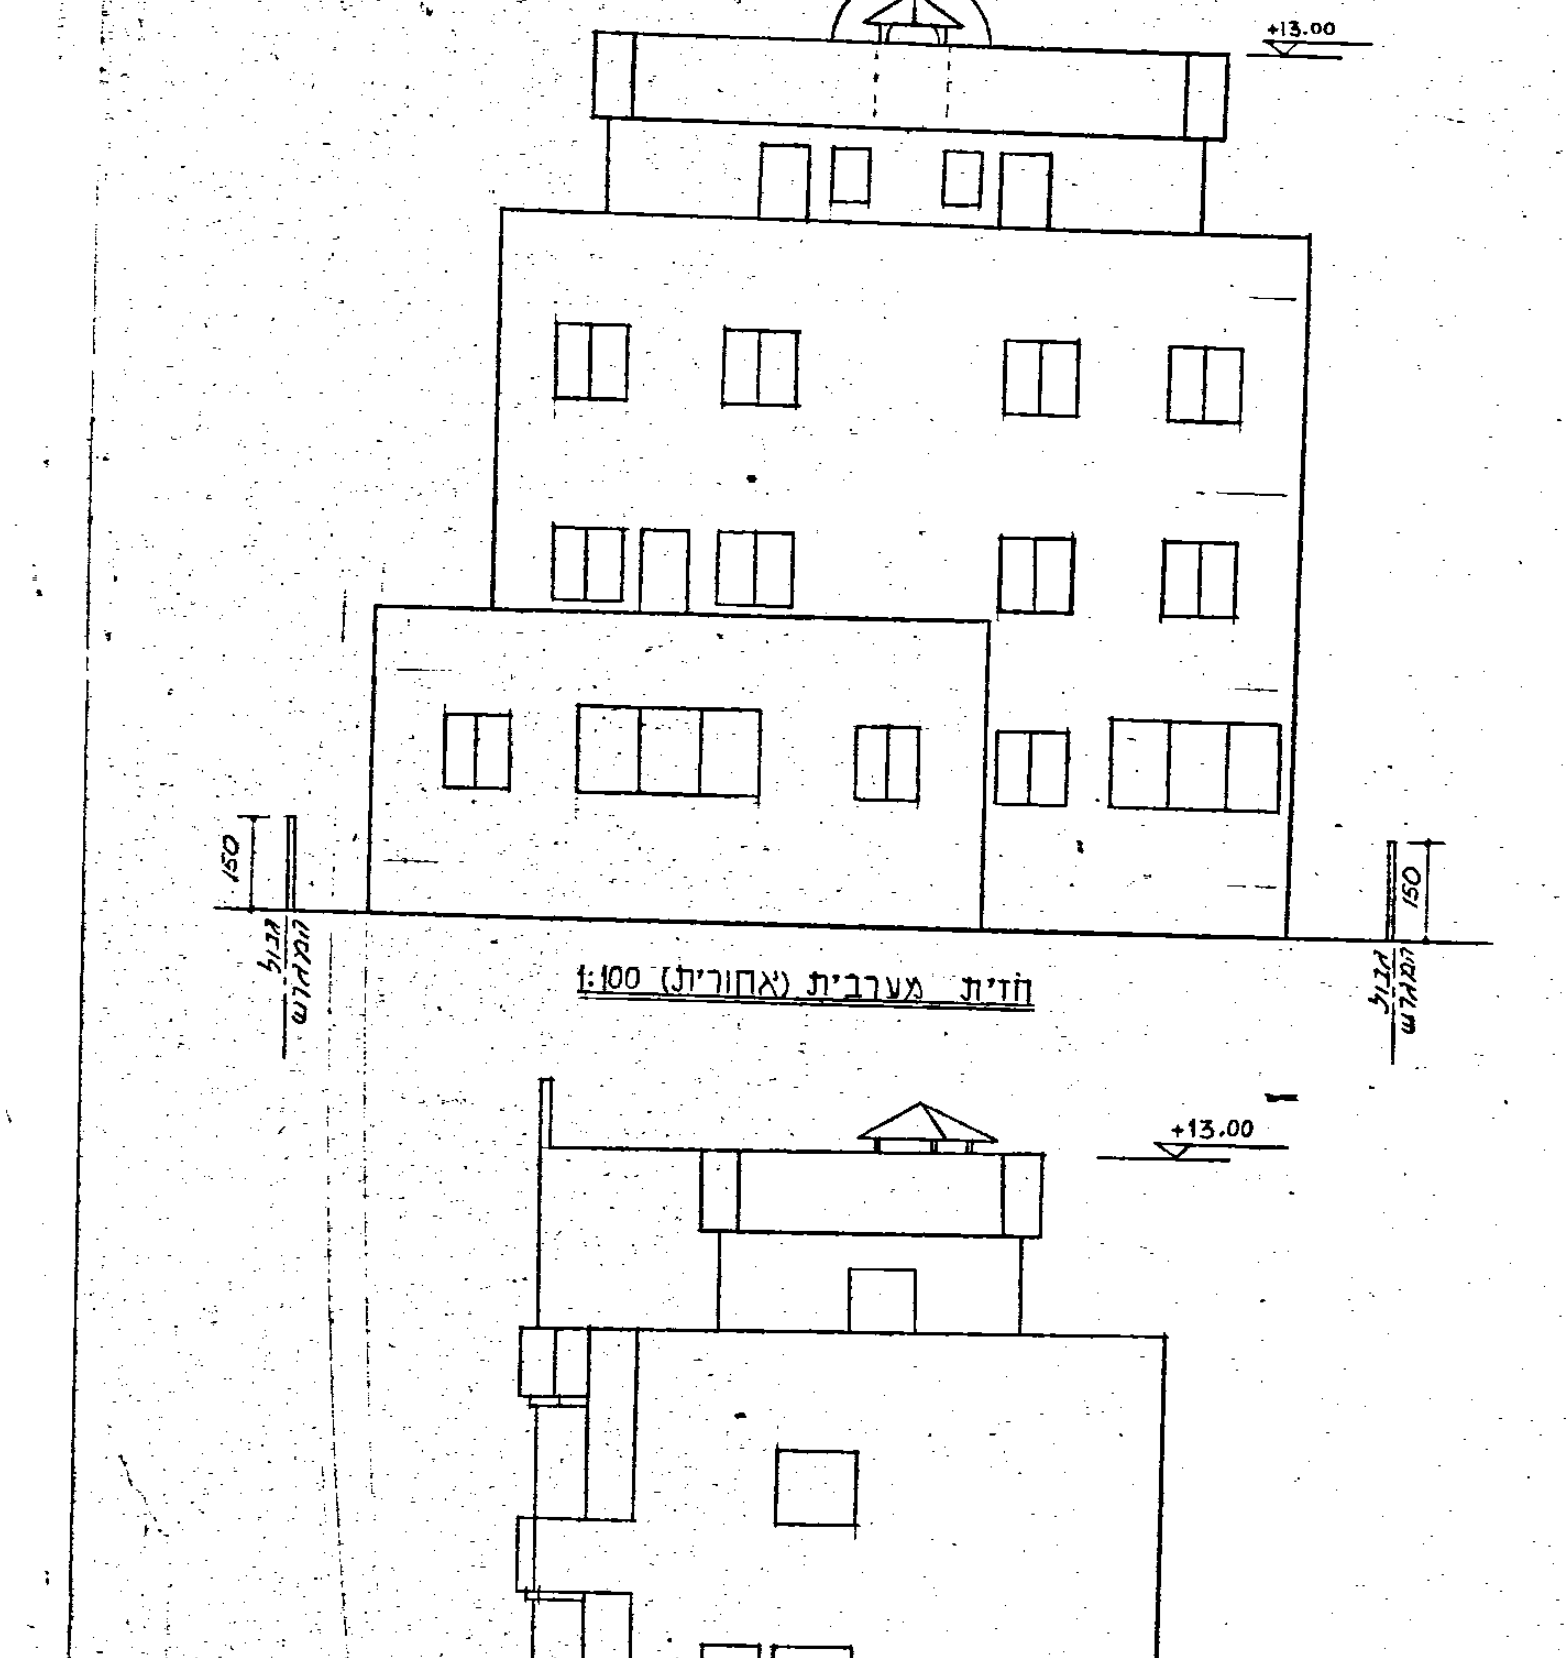
חזית מערבית (אחורית) 1:100

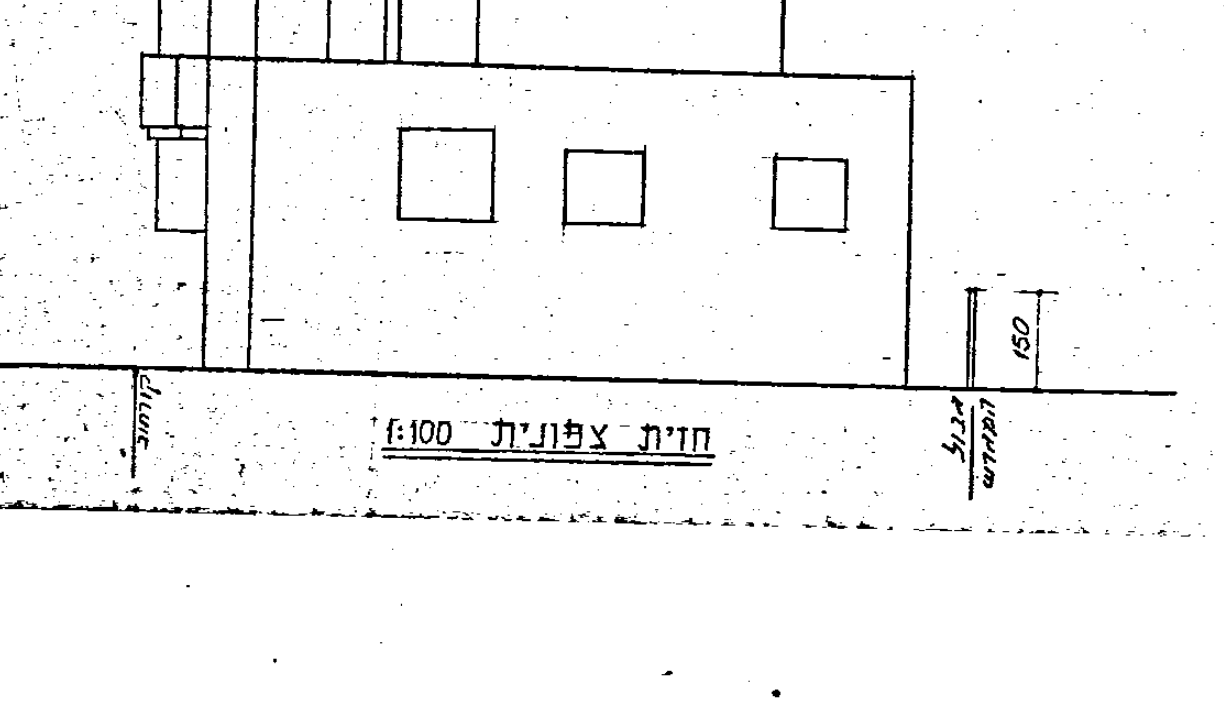
חזית צפונית 1:100

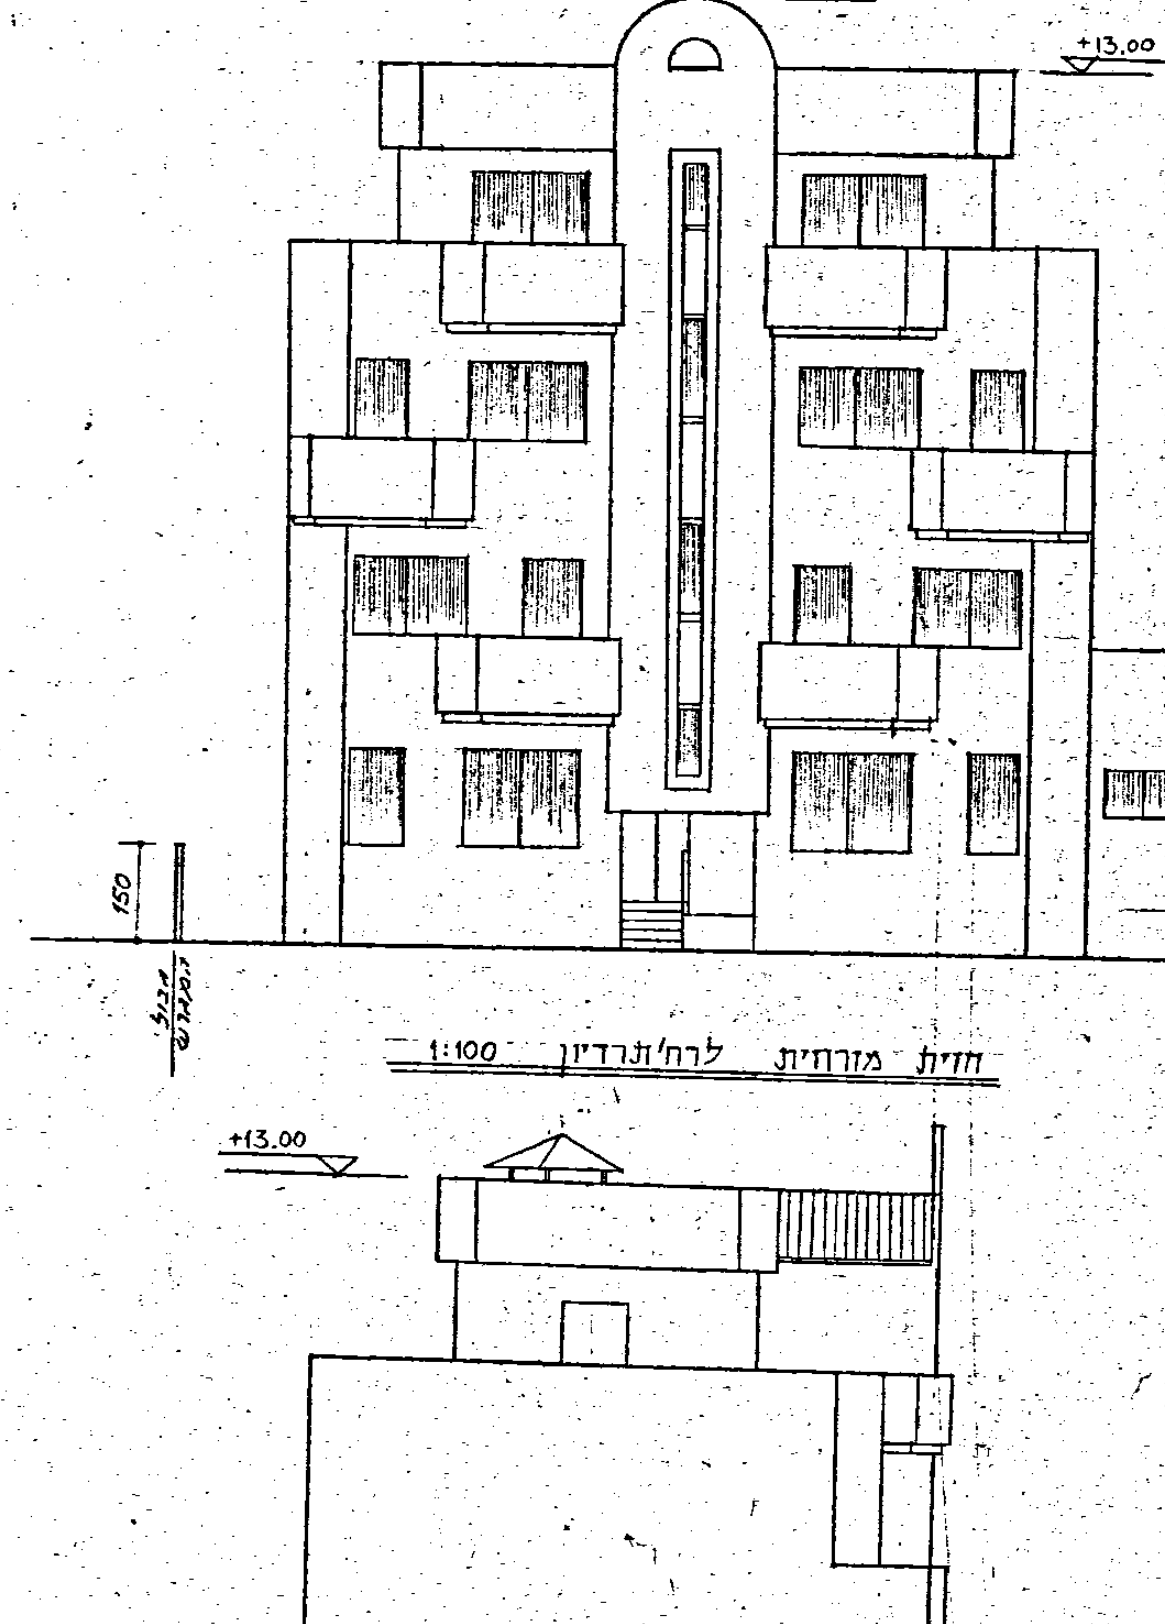
חזית מזרחית לרח' תרדיון 1:100

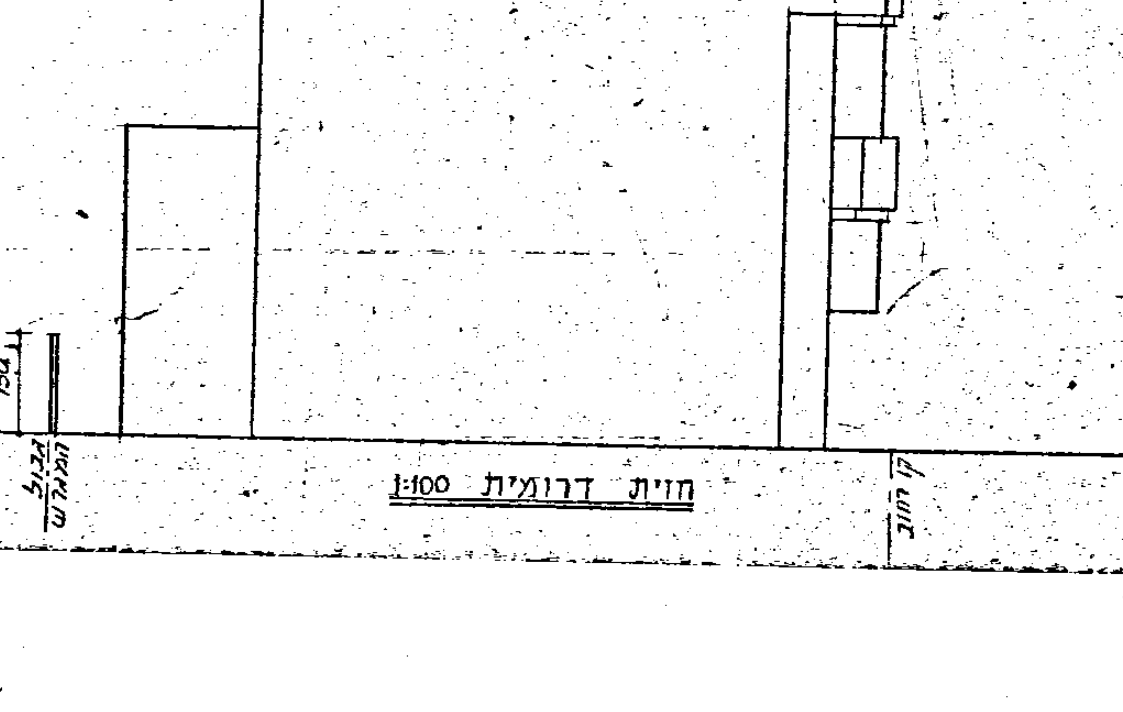
חזית דרומית 1:100

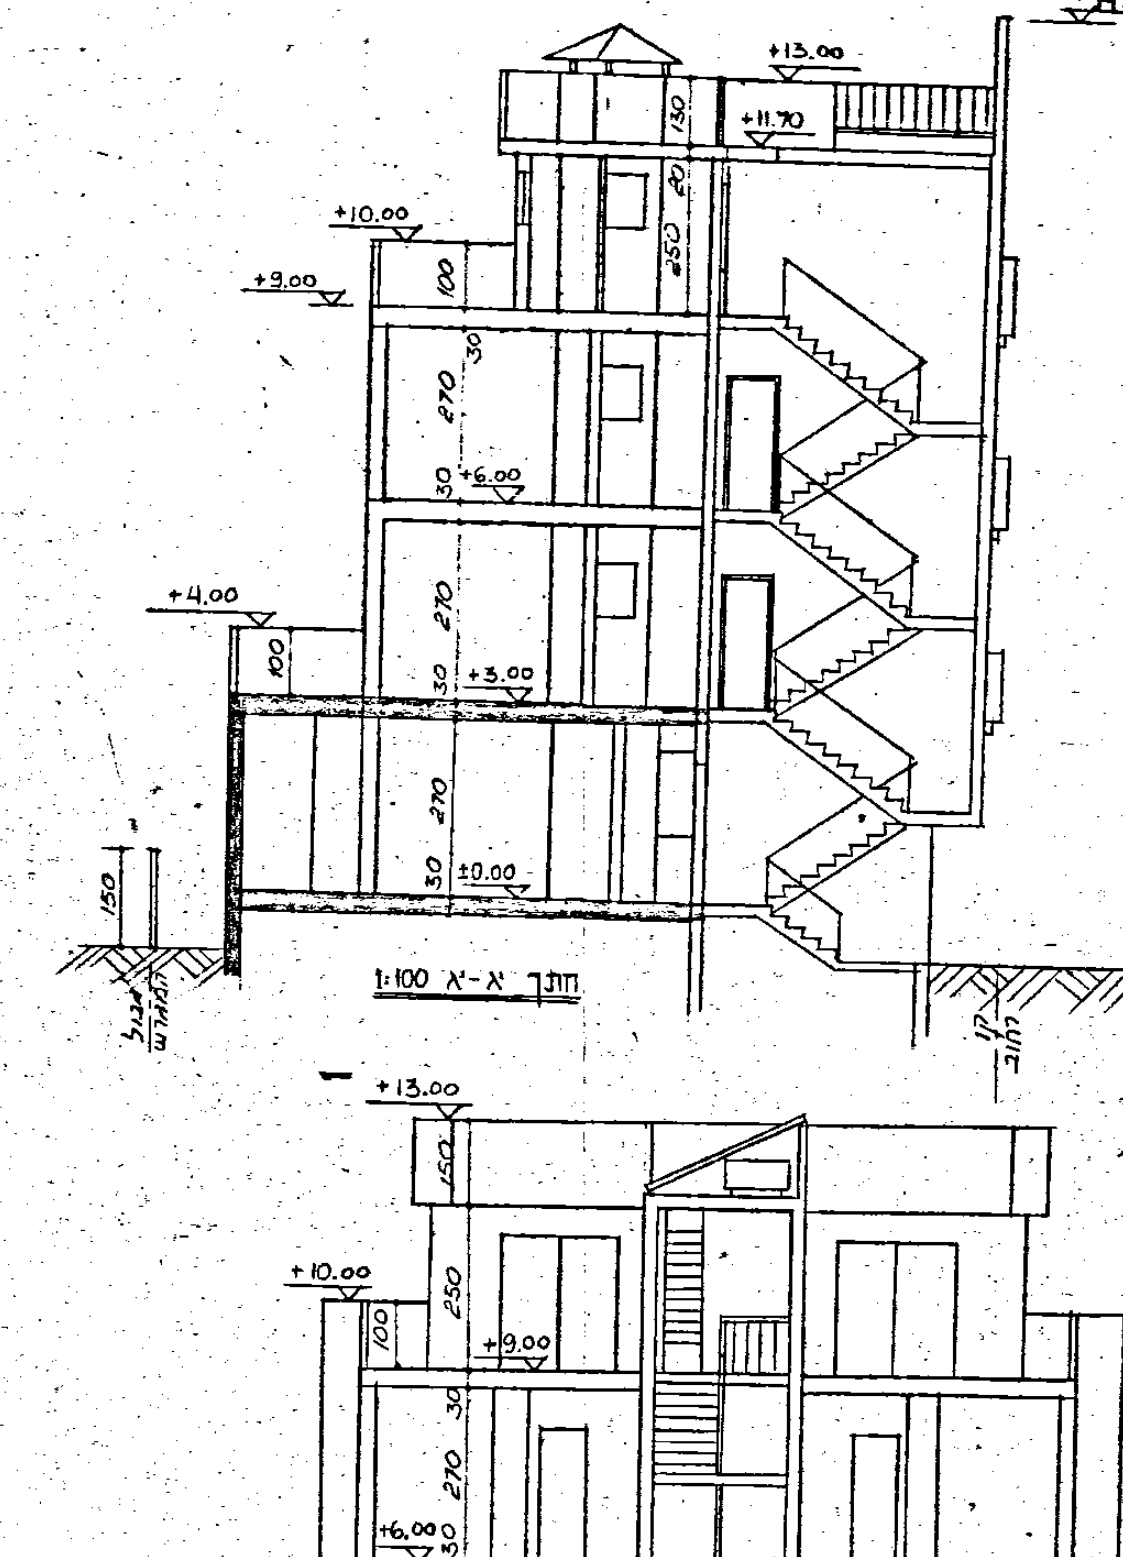
חתך א-א 1:100

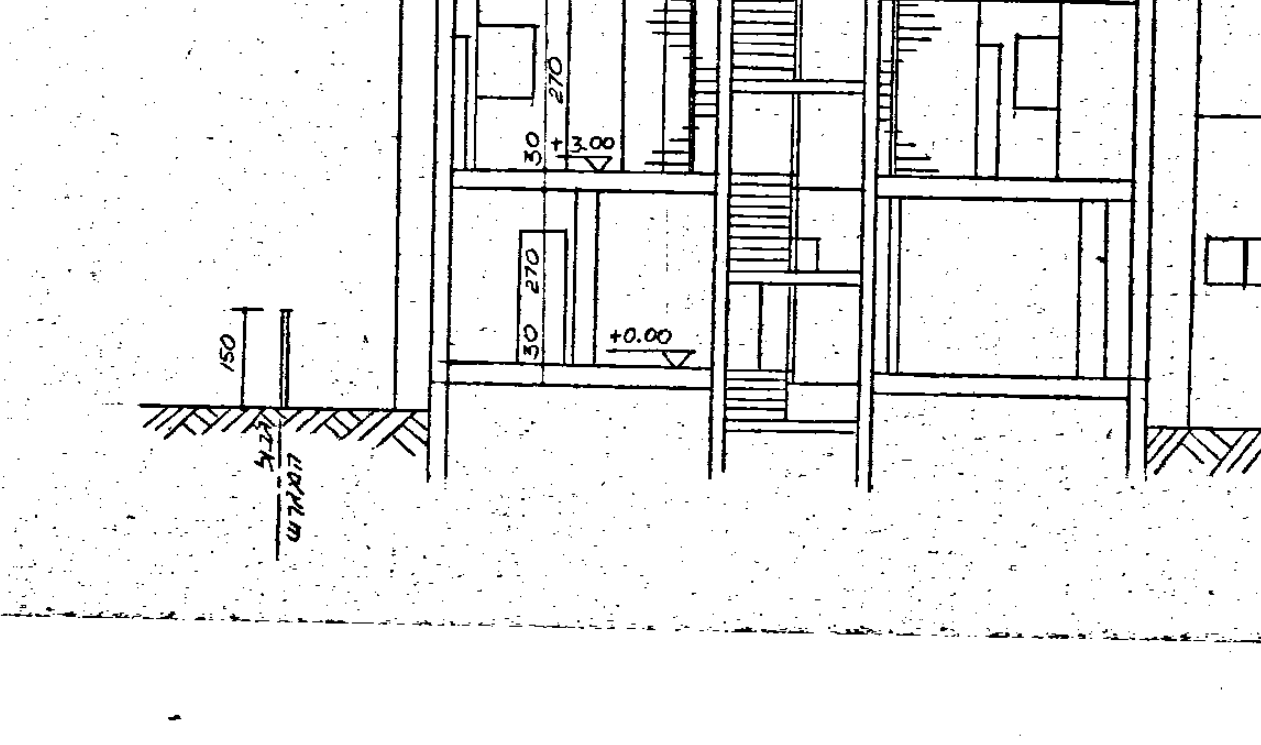

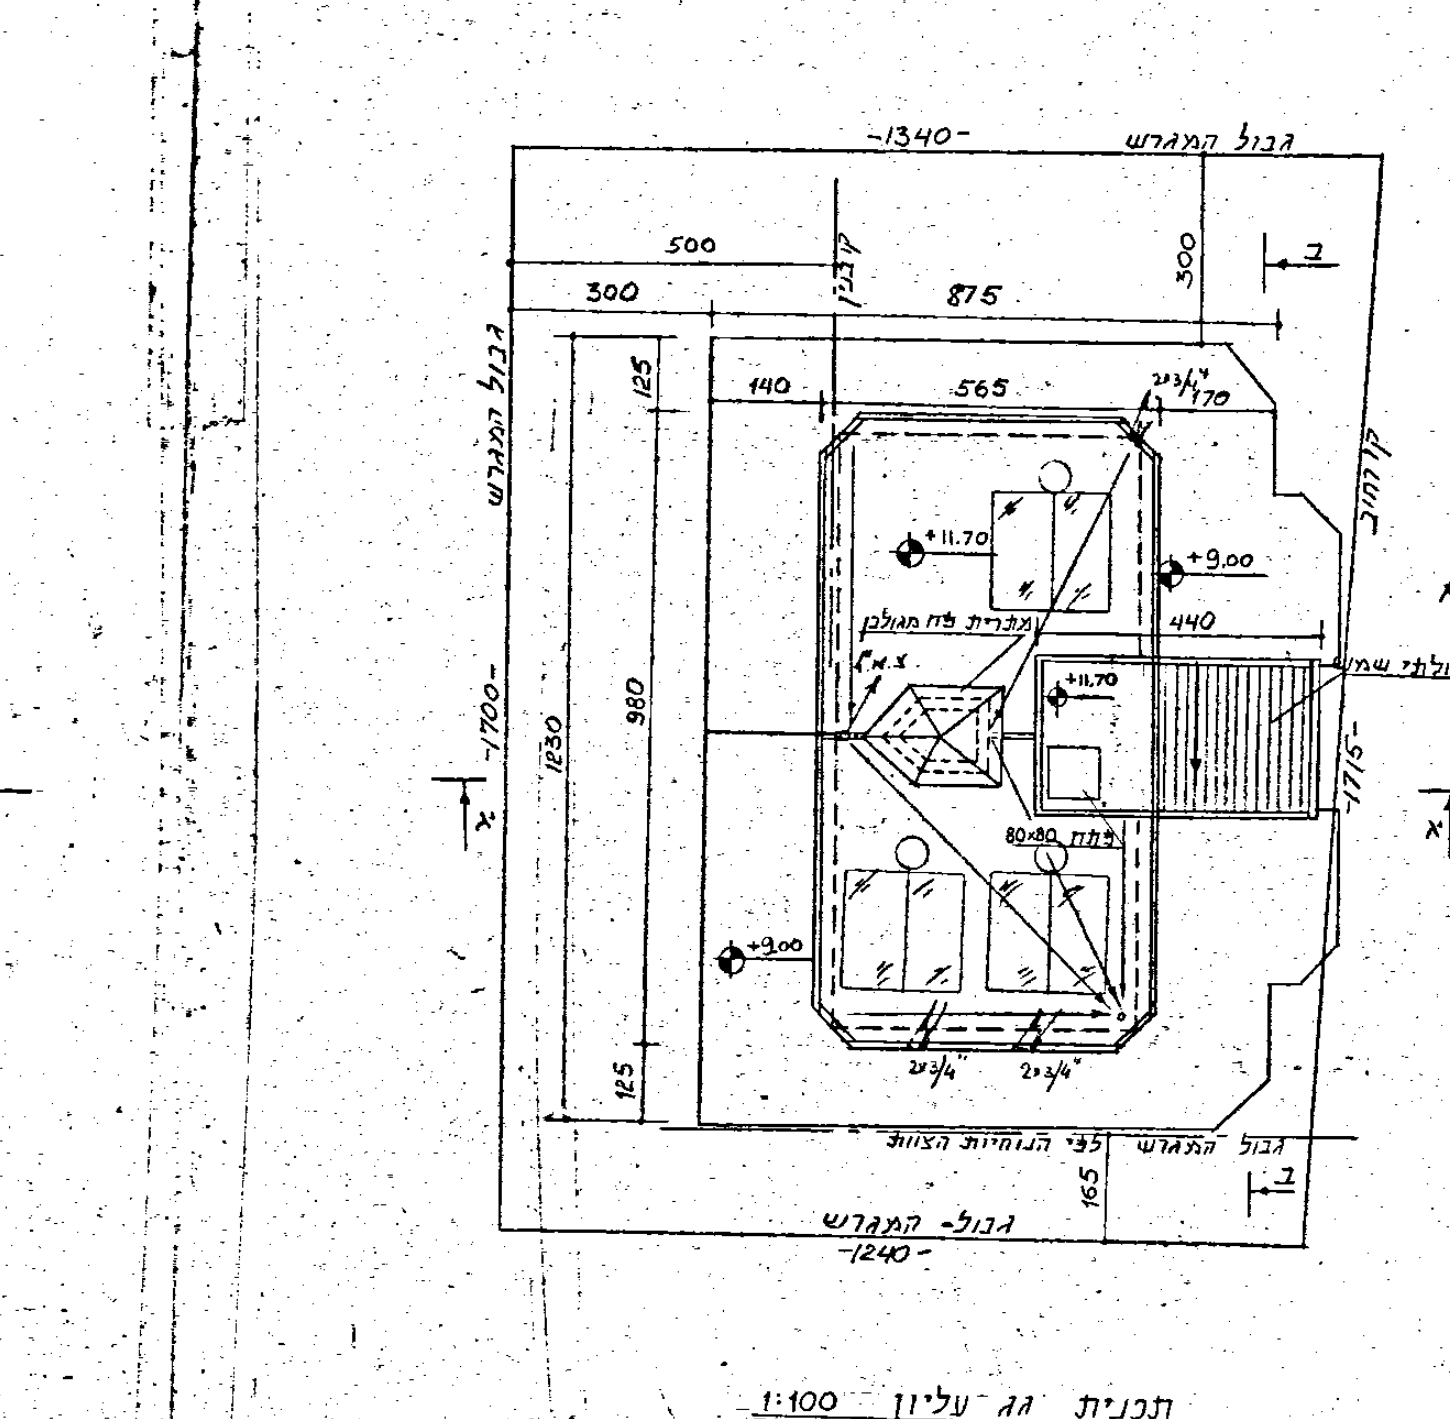
תכנית גג עליון 1:100

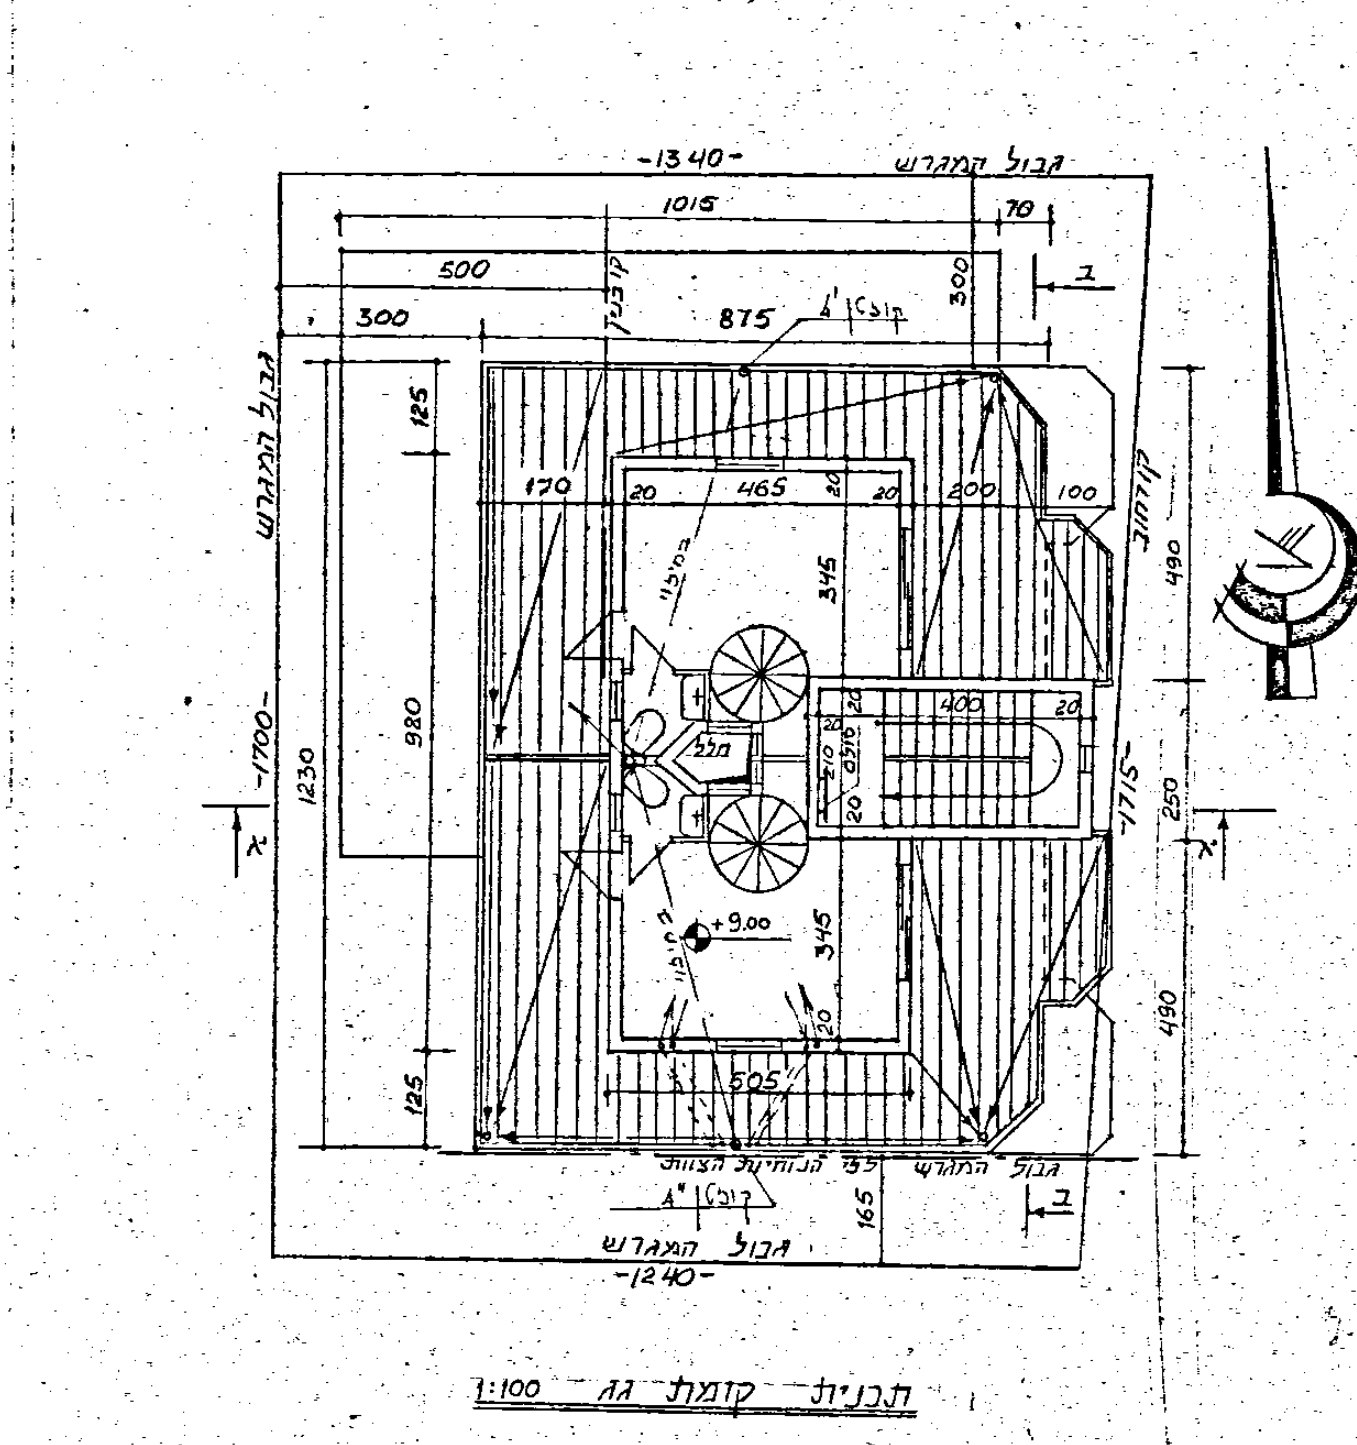
תכנית קומת גג 1:100

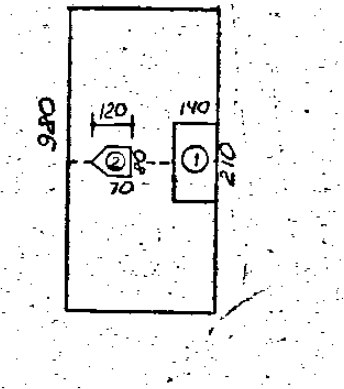
9.8×5.05=49.49

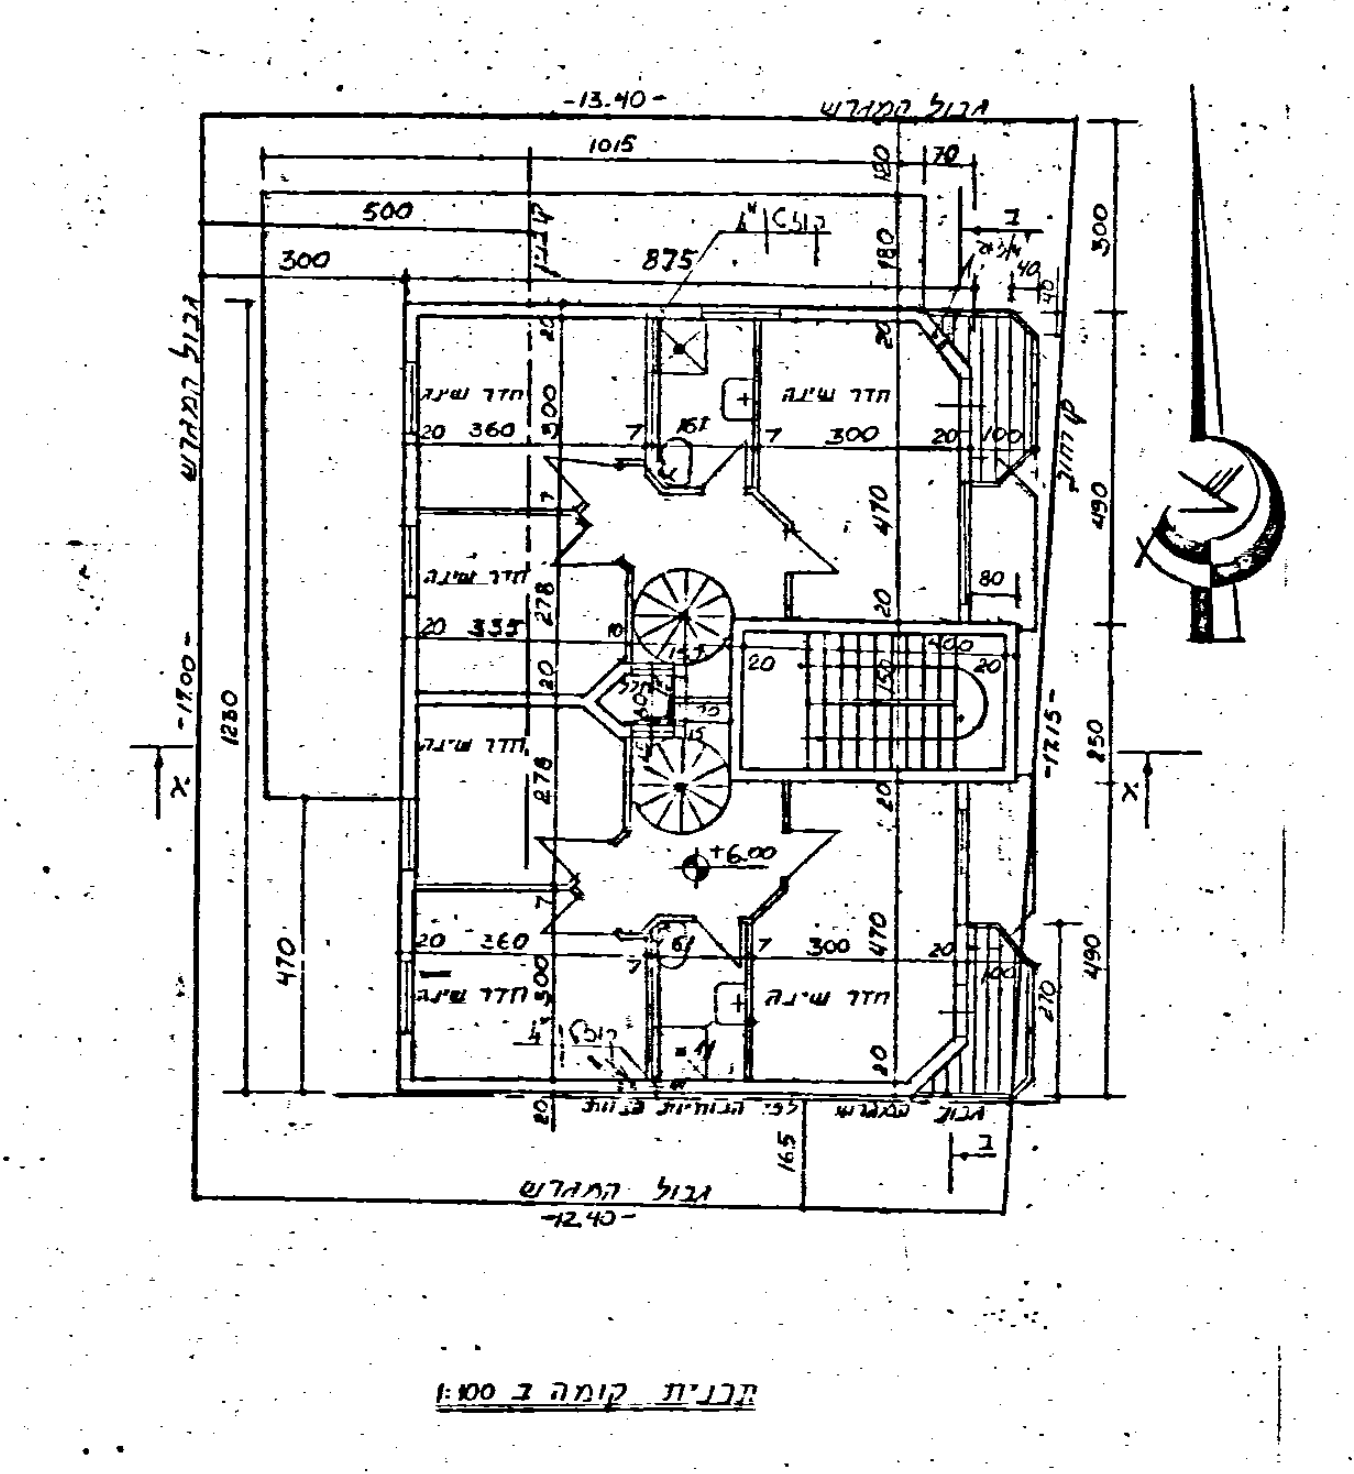
תכנית קומה ב 1:100

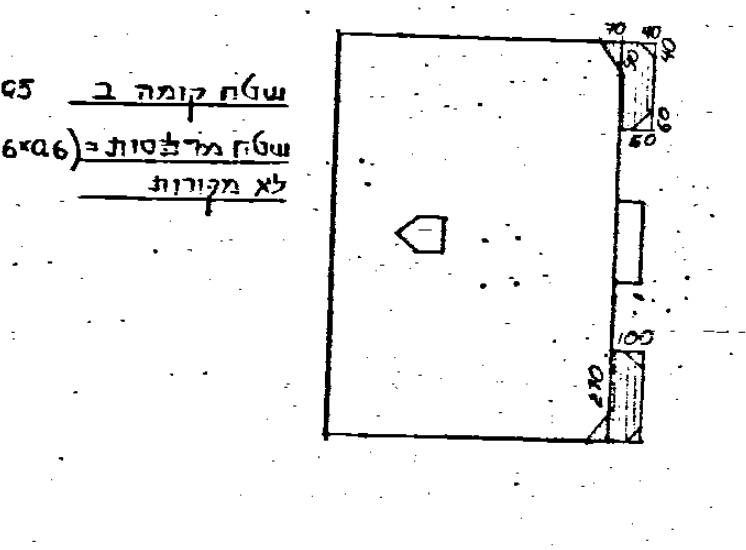

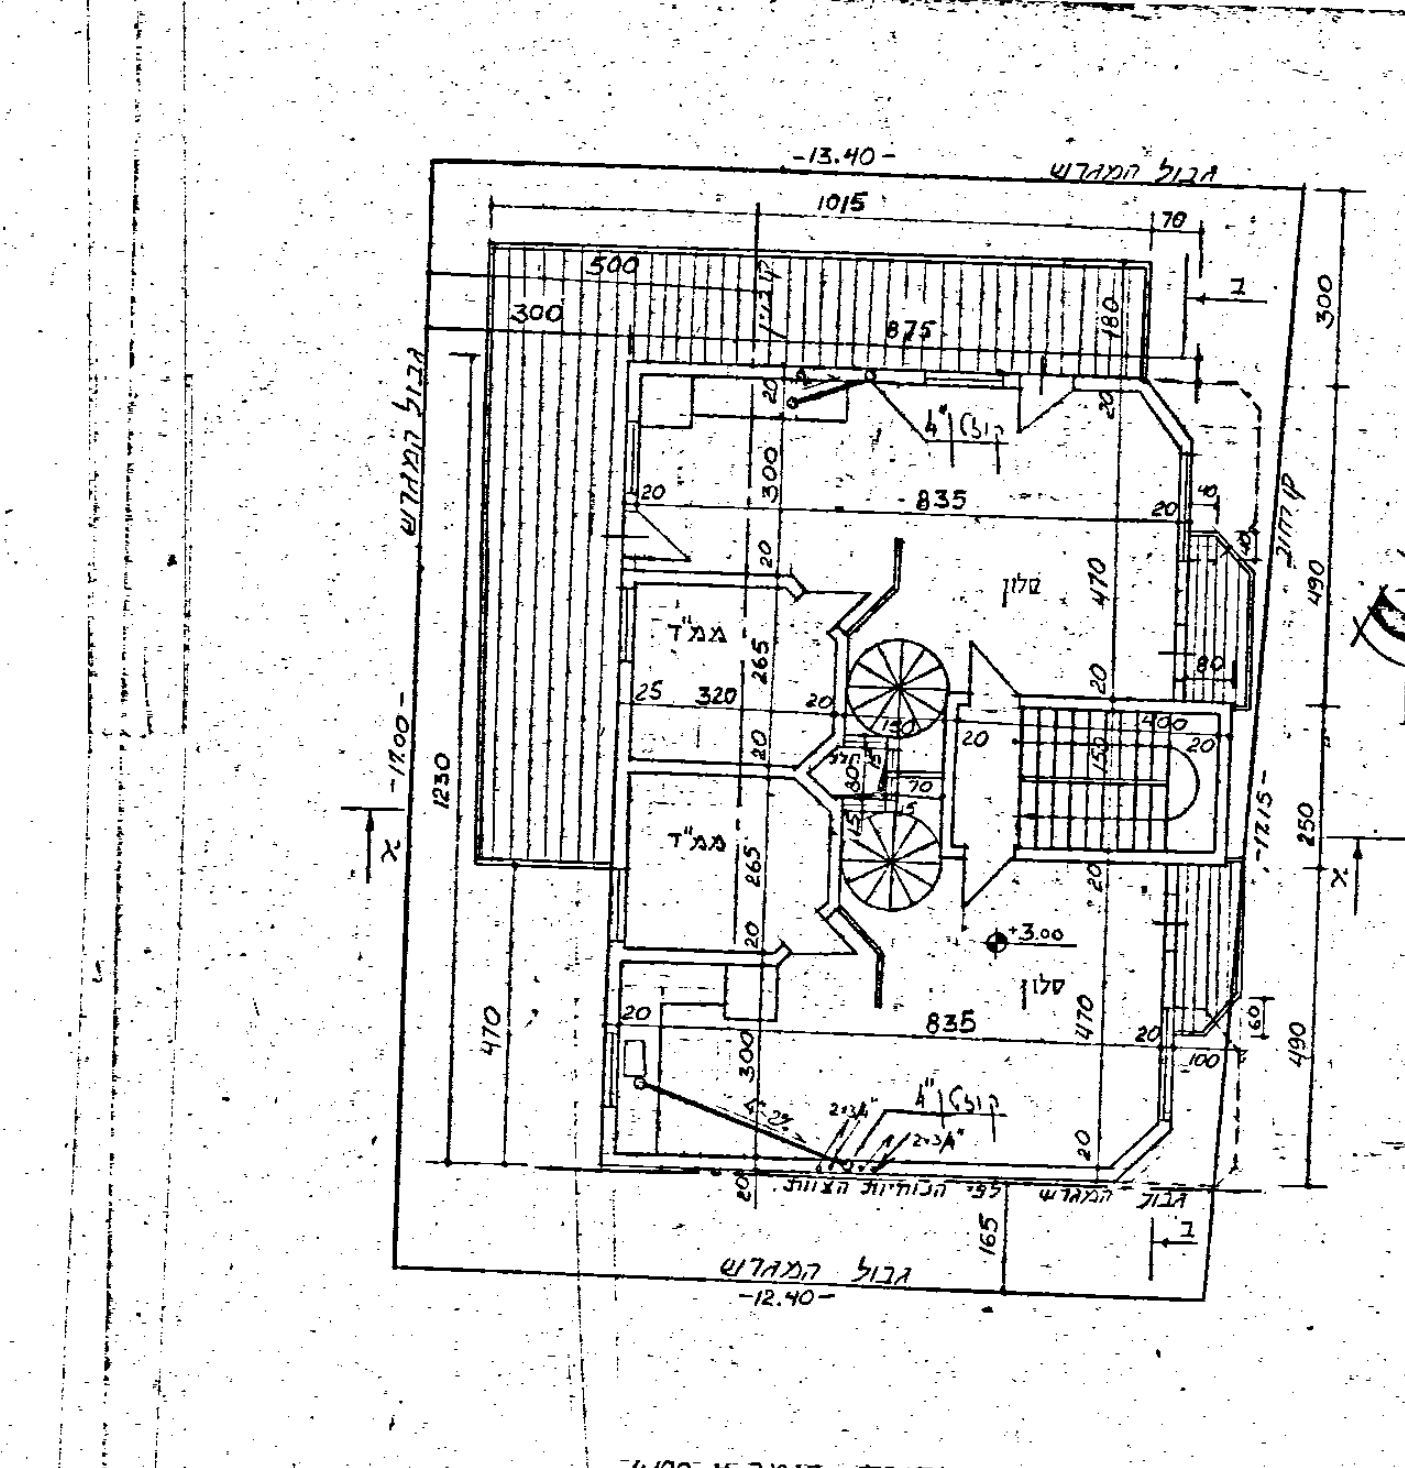
תכנית קומה א 1:100

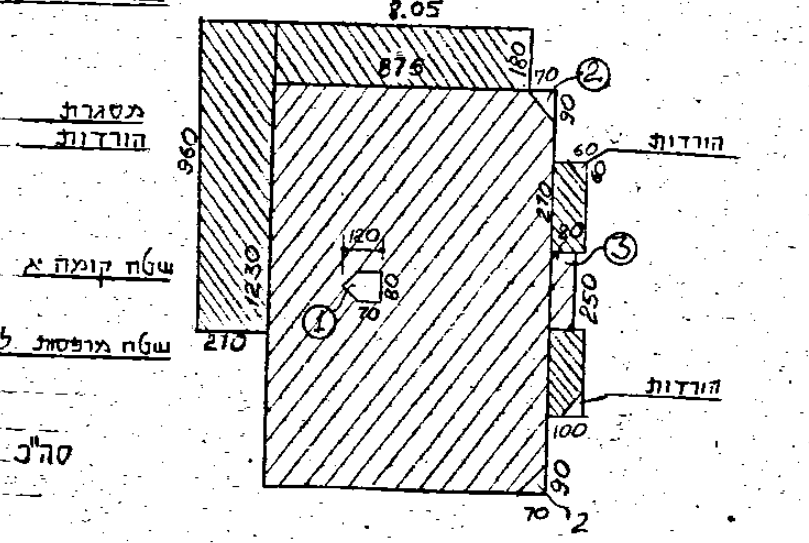

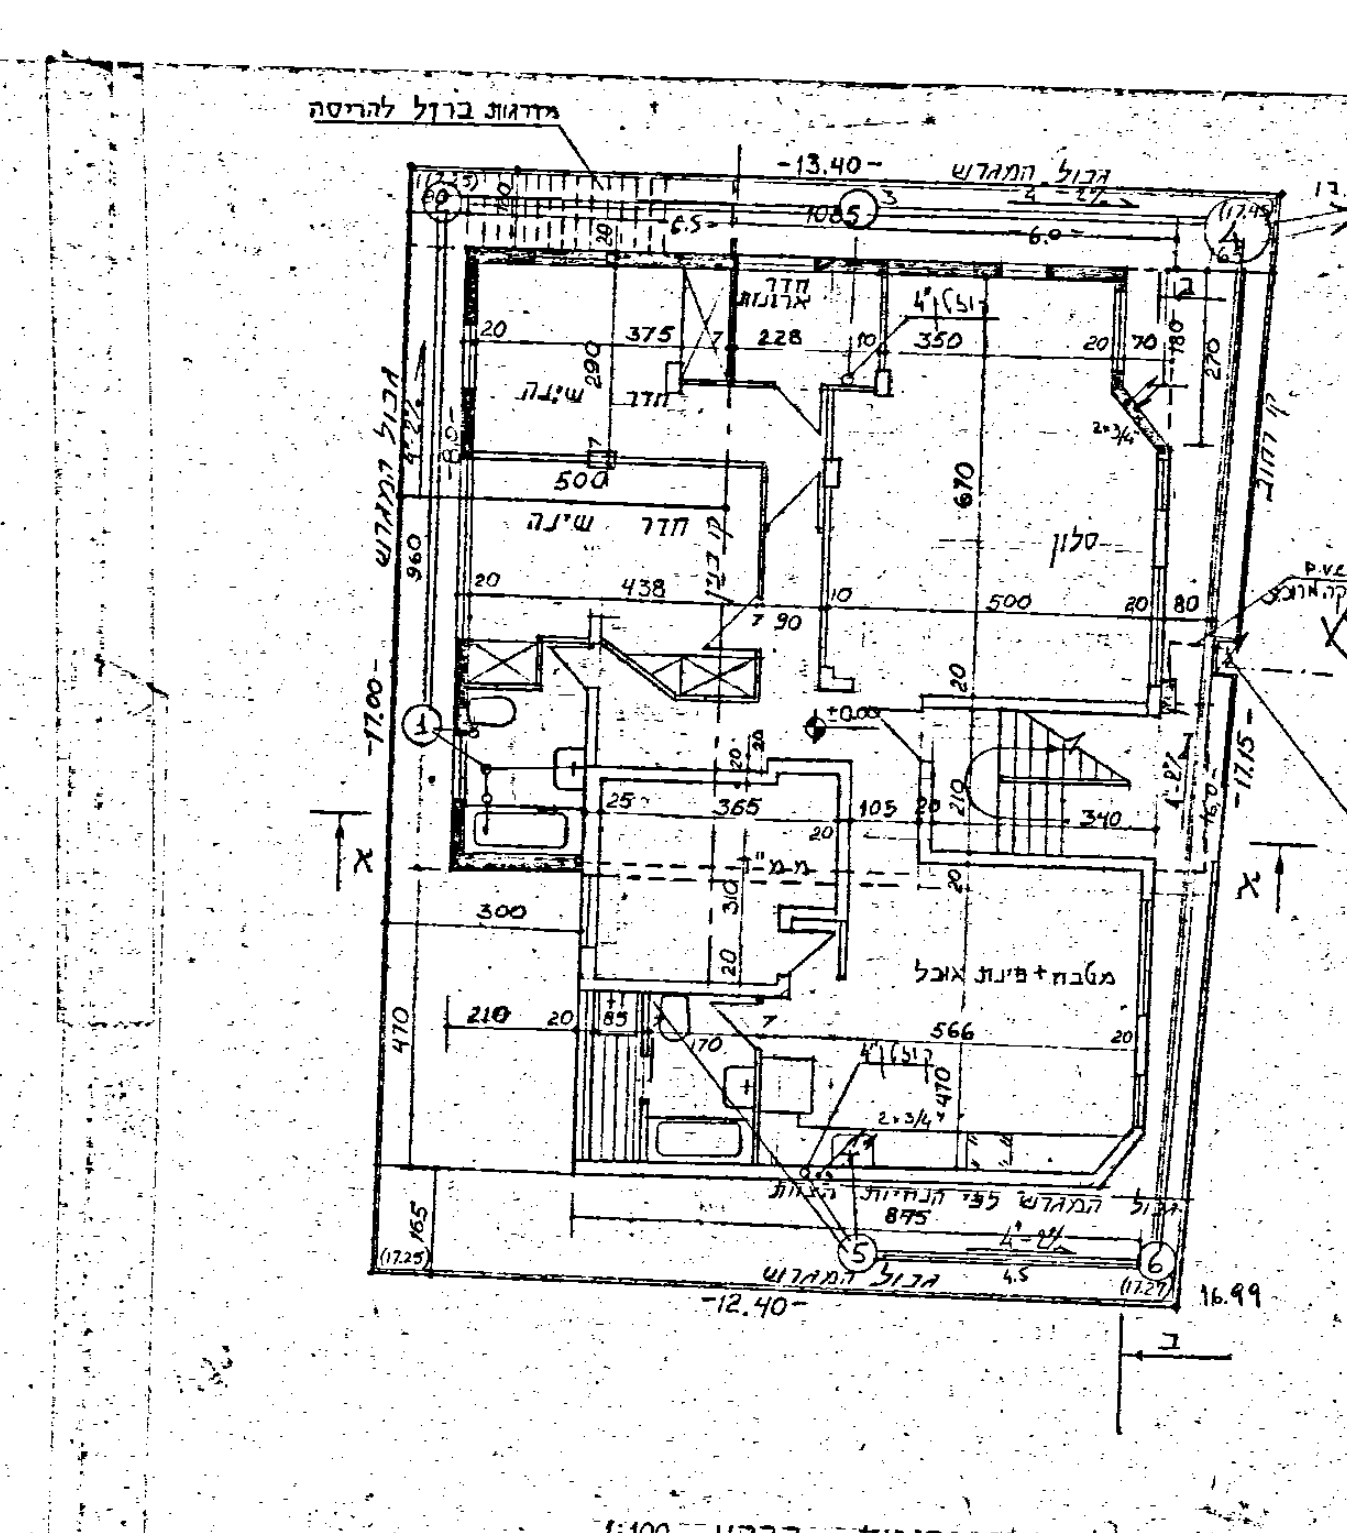
תכנית קומת קרקע 1:100

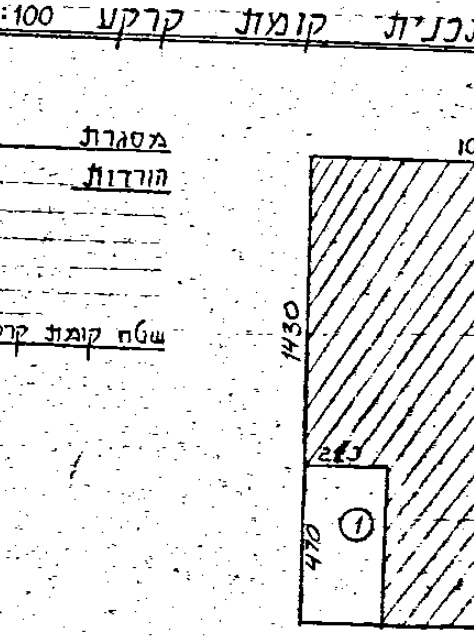
14.5×10.85=155.155

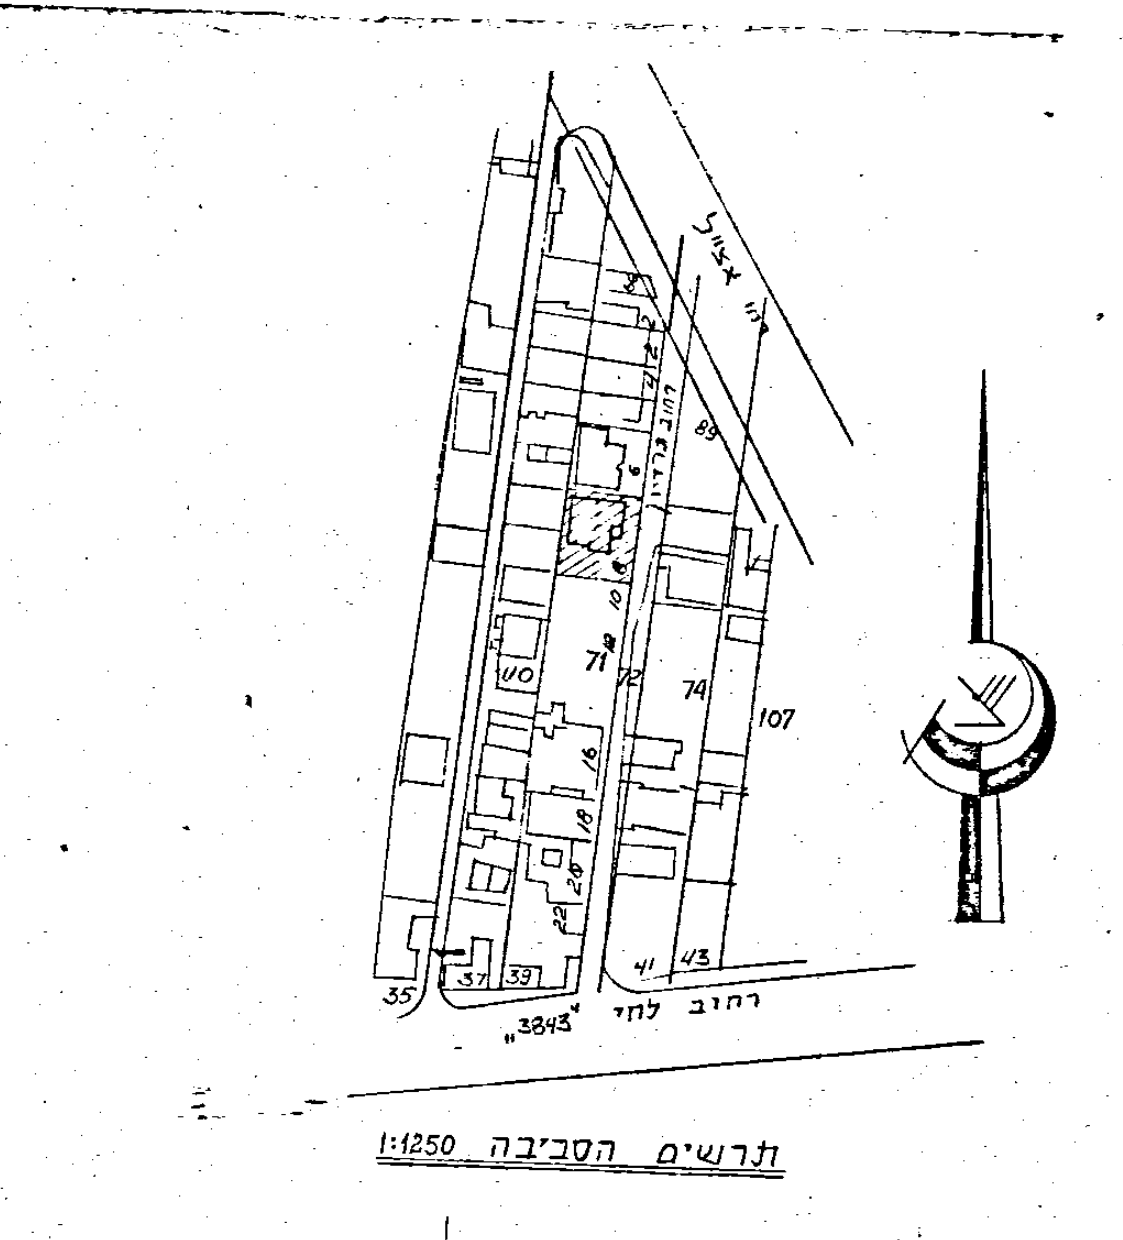

תרשים הסביבה 1:250

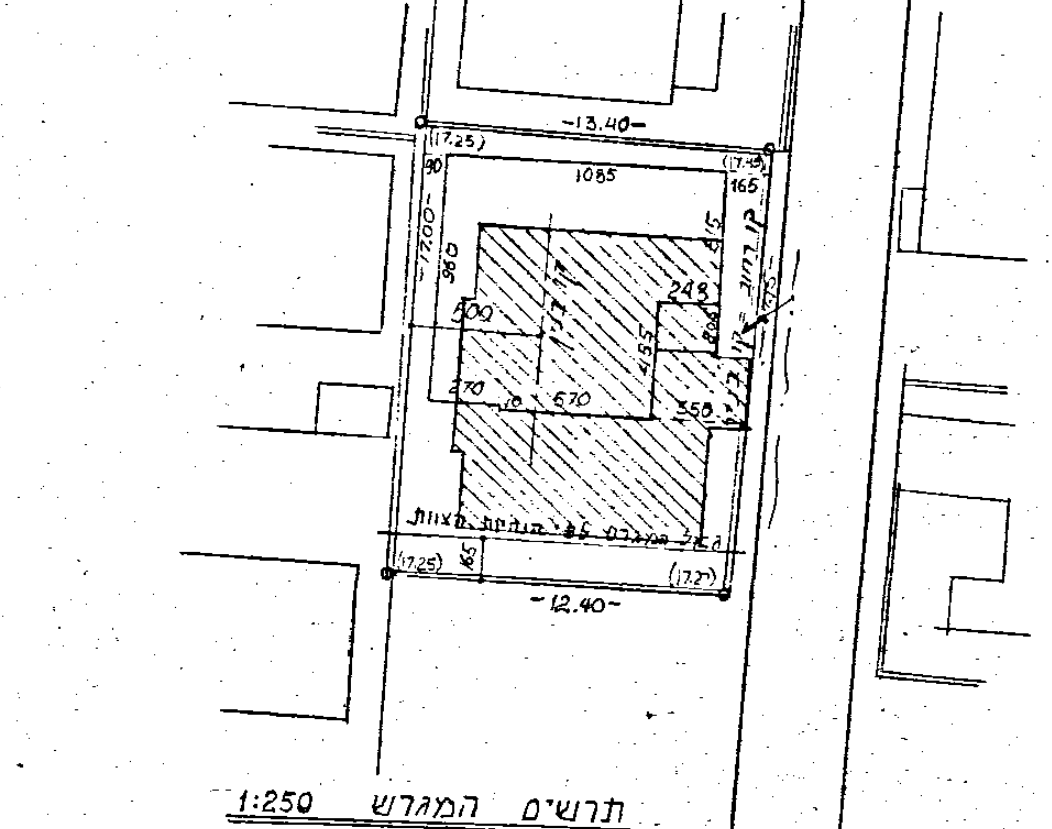
תרשים המגרש 1:250

עיריית תל-אביב-יפו

מופס המבקש פרטים

השטחים המבוקשים לבניה בכל מפלס בנפרד (עפ"י תכנית הבניה)

השטחים המותרים לבניה בכל המפלסים יחד (עפ"י אספקלרית חוק, תקנות, תכנית)

פרטי הבניין - לשימוש הלשכה המרכזית לסטטיסטיקה

איכות נמוכה

196-0116

חוק התכנון והבניה, התשכ"ה-1965

בקשה להיתר בניה או לשימוש במקרקעין

תאור הנכס

4048-008

2215

71

6135

חומרי הבניה