הועדה המקומית לתכנון ולבניה
למרחב תכנון תל-אביב - יפו
בהתאם לסעיף 145/ב לחוק התכנון והבניה נבקשה להיתר.
בניה/שימוש מס׳ 6980394
מהנדס העיר
1.1.09.1997

מינהל ההנדסה
אגף הרישוי
העתק מאושר

297-0991

ביטול היתר

הוראות לביצוע מרחב מוגן דירתי

המרחב המוגן הדירתי יבנה בהתאם לתקנות התגוננות האזרחית (מפרטים לבניה מקלטים) (תיקון) התשנ״א 1991 שפורסם מס׳ 5425 מיום 3.3.1992.

עקרונות התכנון

בתכנון המרחב המוגן הדירתי יתקיימו עקרונות יסוד אלה:

המרחב המוגן הדירתי ייבנה בטון במבנה דמוי תיבה, עשוי מקשה אחת והדום בכל חלקיו, ללא קורות ועמודים.

רצפת המרחב המוגן הדירתי, קירותיו ותקרתו יהיו [illegible] (יצוקים בדיקטים בלבד).

קירות המרחבים המוגנים הדירתיים יהיו רציפים לכל גובה הבניין, לצירת מגדל מוגן.

יציבות המגדל המוגן של המרחבים המוגנים הדירתיים הובטח מפני כוחות אופקיים.

העובי המזערי של חלקי המרחב המוגן הדירתי יהיה באמור בתקניה 208.

תכנון שלד המרחב המוגן הדירתי ייעשה בהתאם לת״י 466.

מידות מזעריות של פתח אור - דלת כניסה - 60/200 ס״מ או 70/200.

סוג דלת הכניסה - דלת הדף דירתית במפורט בתקנה 202.

הגנה על דלת כניסה - במפורט בתקנות (ע״י מחיצות ומרחקים מקווי בניין).

חלון - בשטח מירבי של 1.22 מ״ר, גובה מפלס אדן לא יפחת מ-1.05 מ׳.

חלון ההדף הדירתי יכלול שני חלקים עיקריים:

א. חלון בהתוגל בגימא אטום מפני גזים

ב. אלמנט מגן חיצוני להדף-התקן לפי תקנה 202

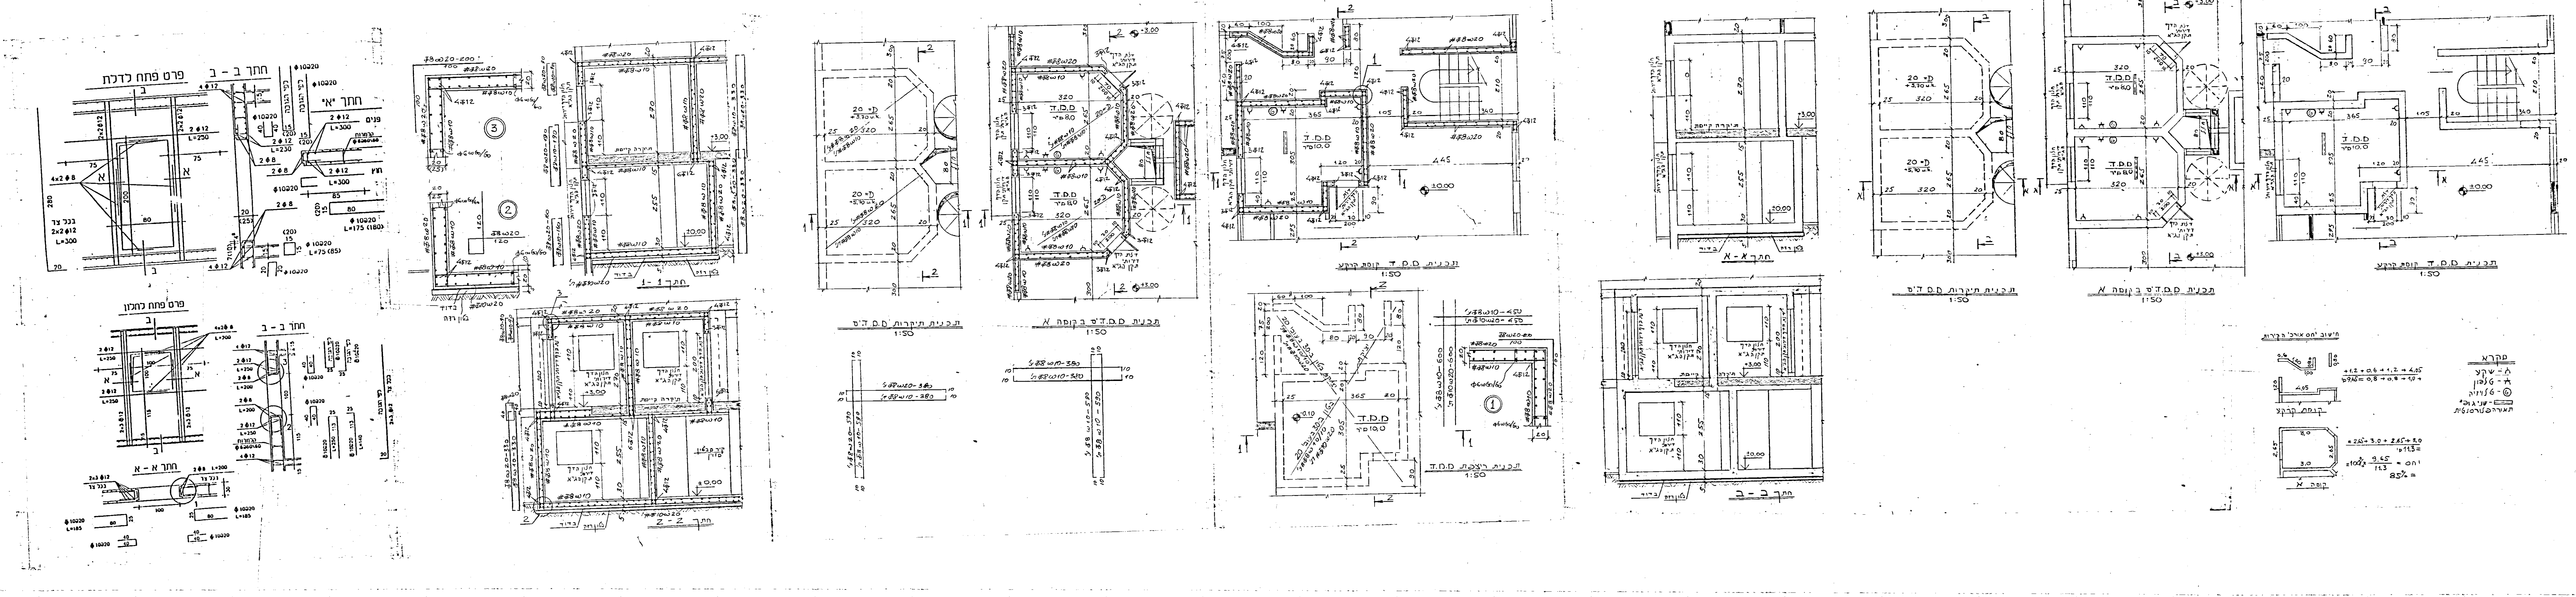

פרט פתח לדלת
חתך ב - ב
חתך א׳
פרט פתח חלון
חתך א - א
חתך ב - ב
חתך 1 - 1
חתך 2 - 2
תכנית ממ״ד קומת קרקע 1:50
תכנית תקרות ממ״ד 1:50
תכנית ממ״ד בקומה א 1:50
תכנית רצפת ממ״ד 1:50
חתך א - א
חתך ב - ב

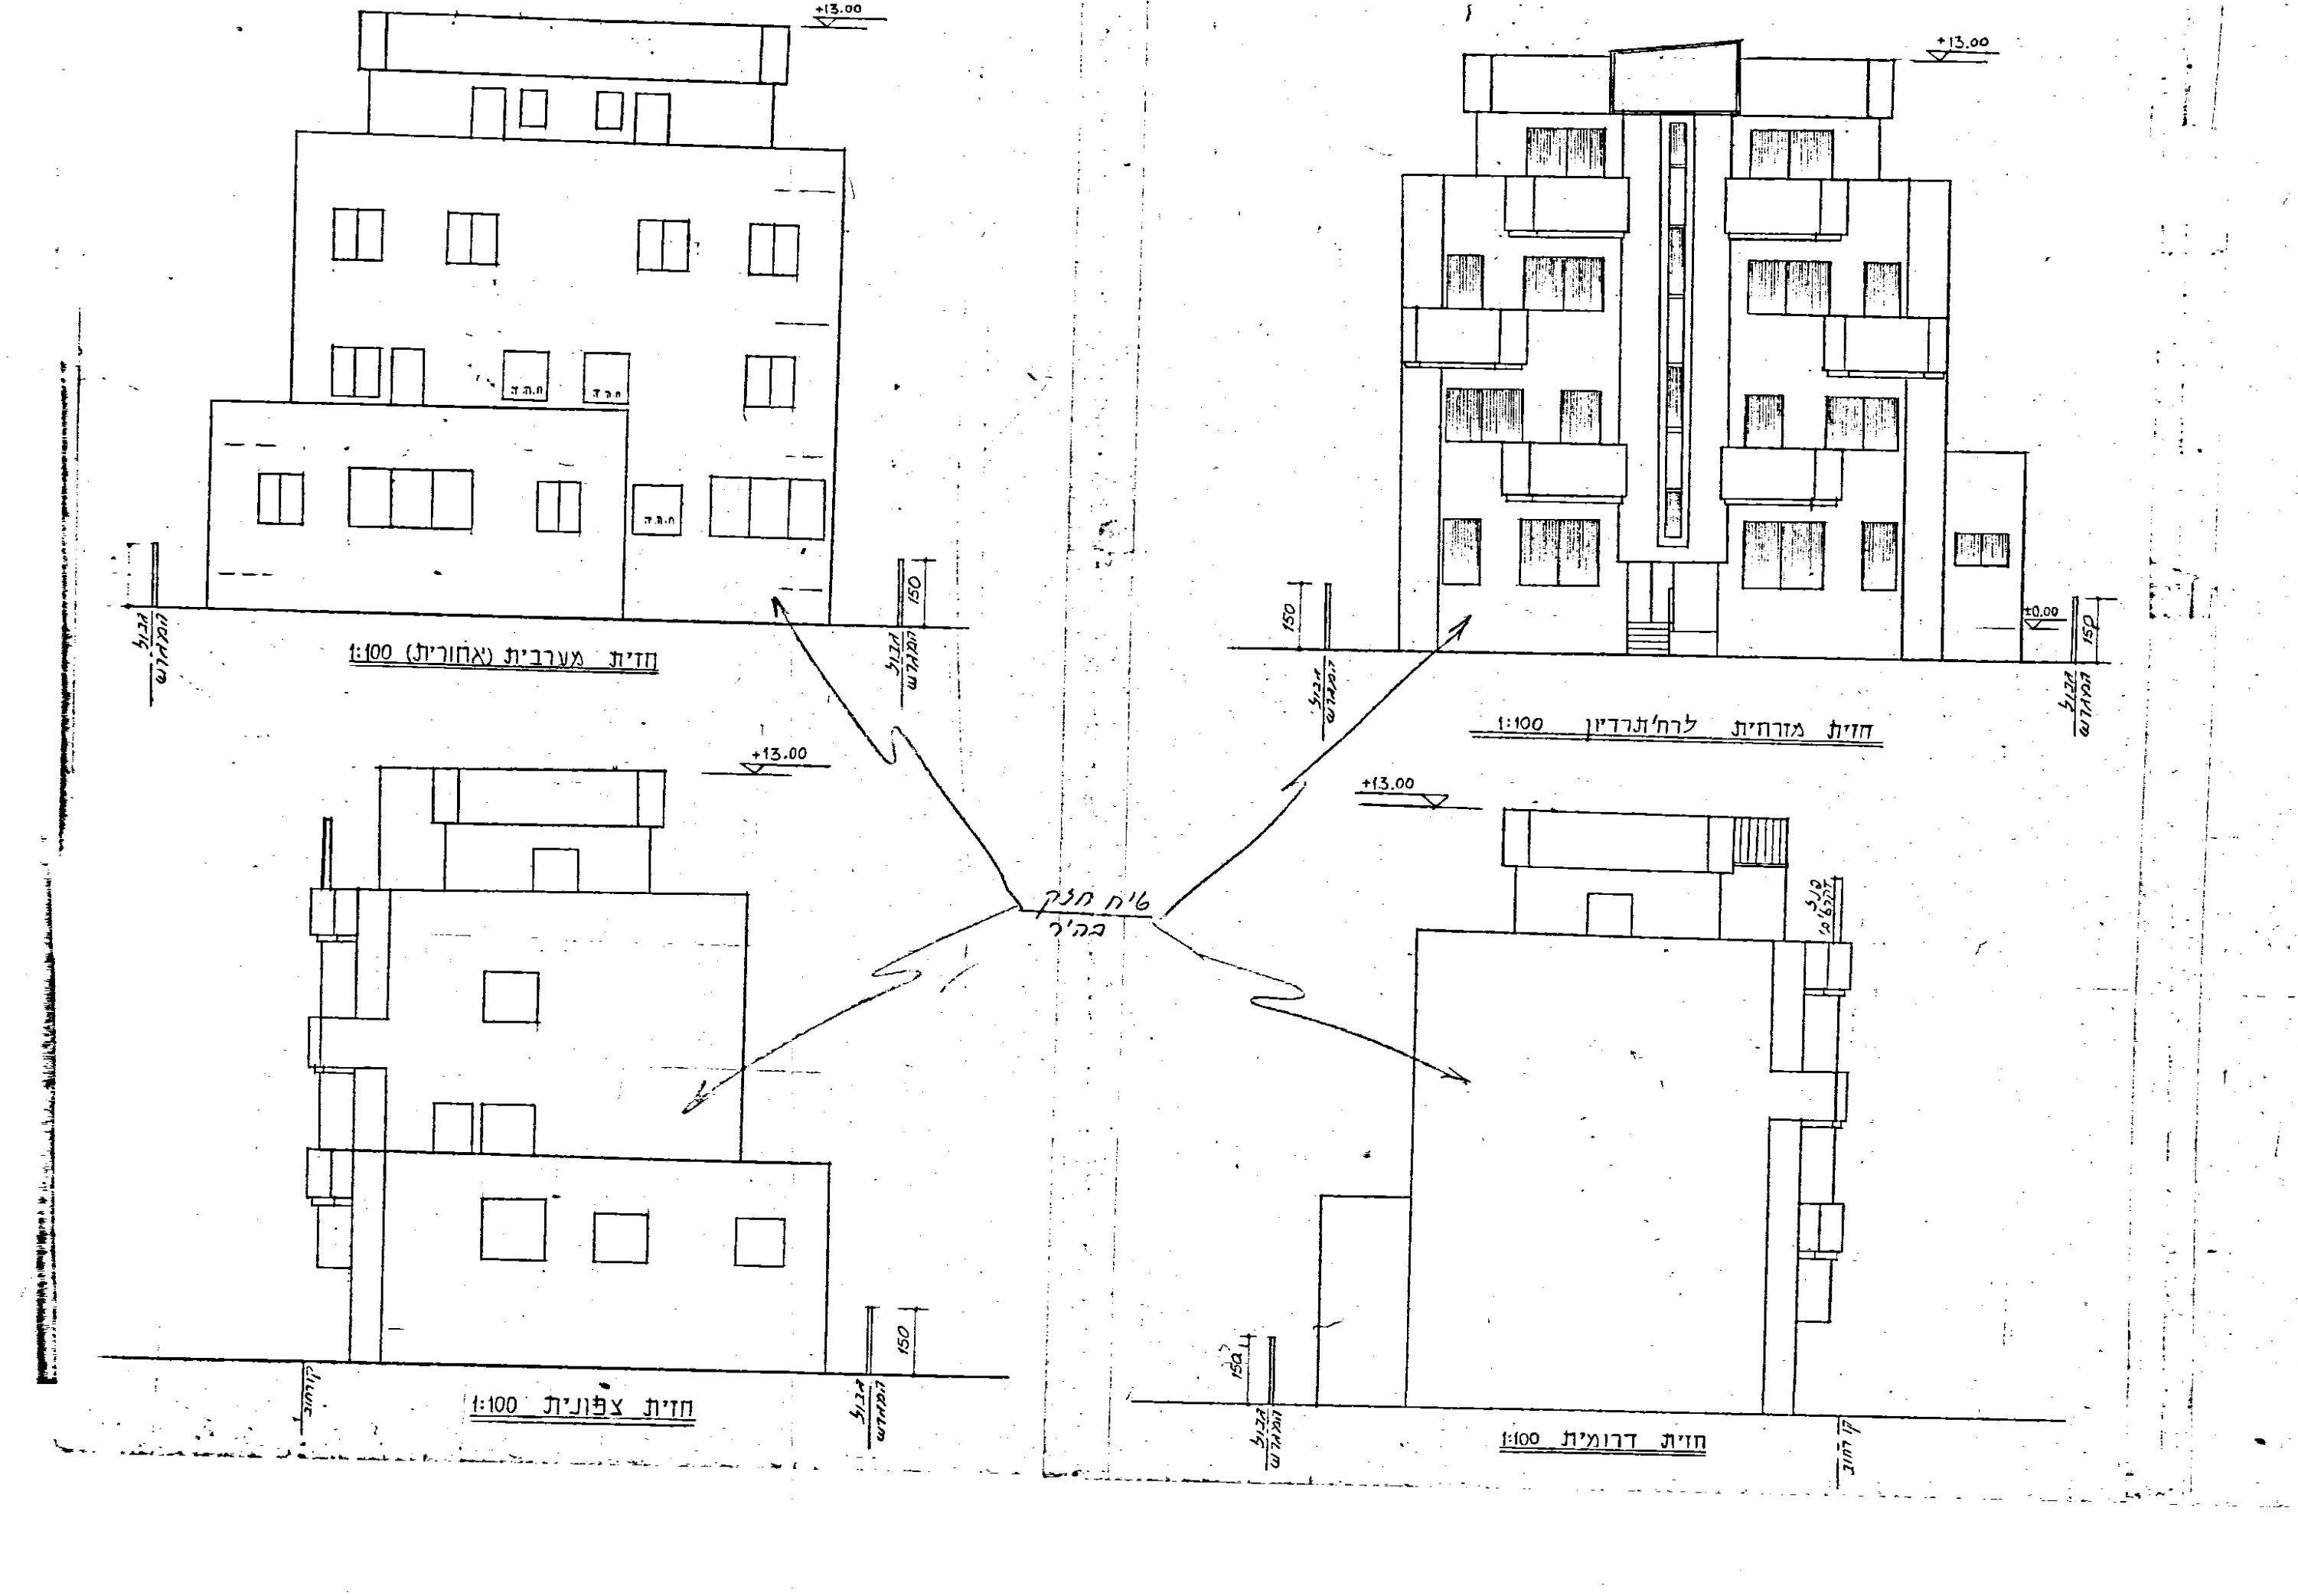

+13.00
חזית מערבית (אחורית) 1:100
חזית מזרחית לרחוב 1:100
חזית צפונית 1:100
חזית דרומית 1:100
+15.00

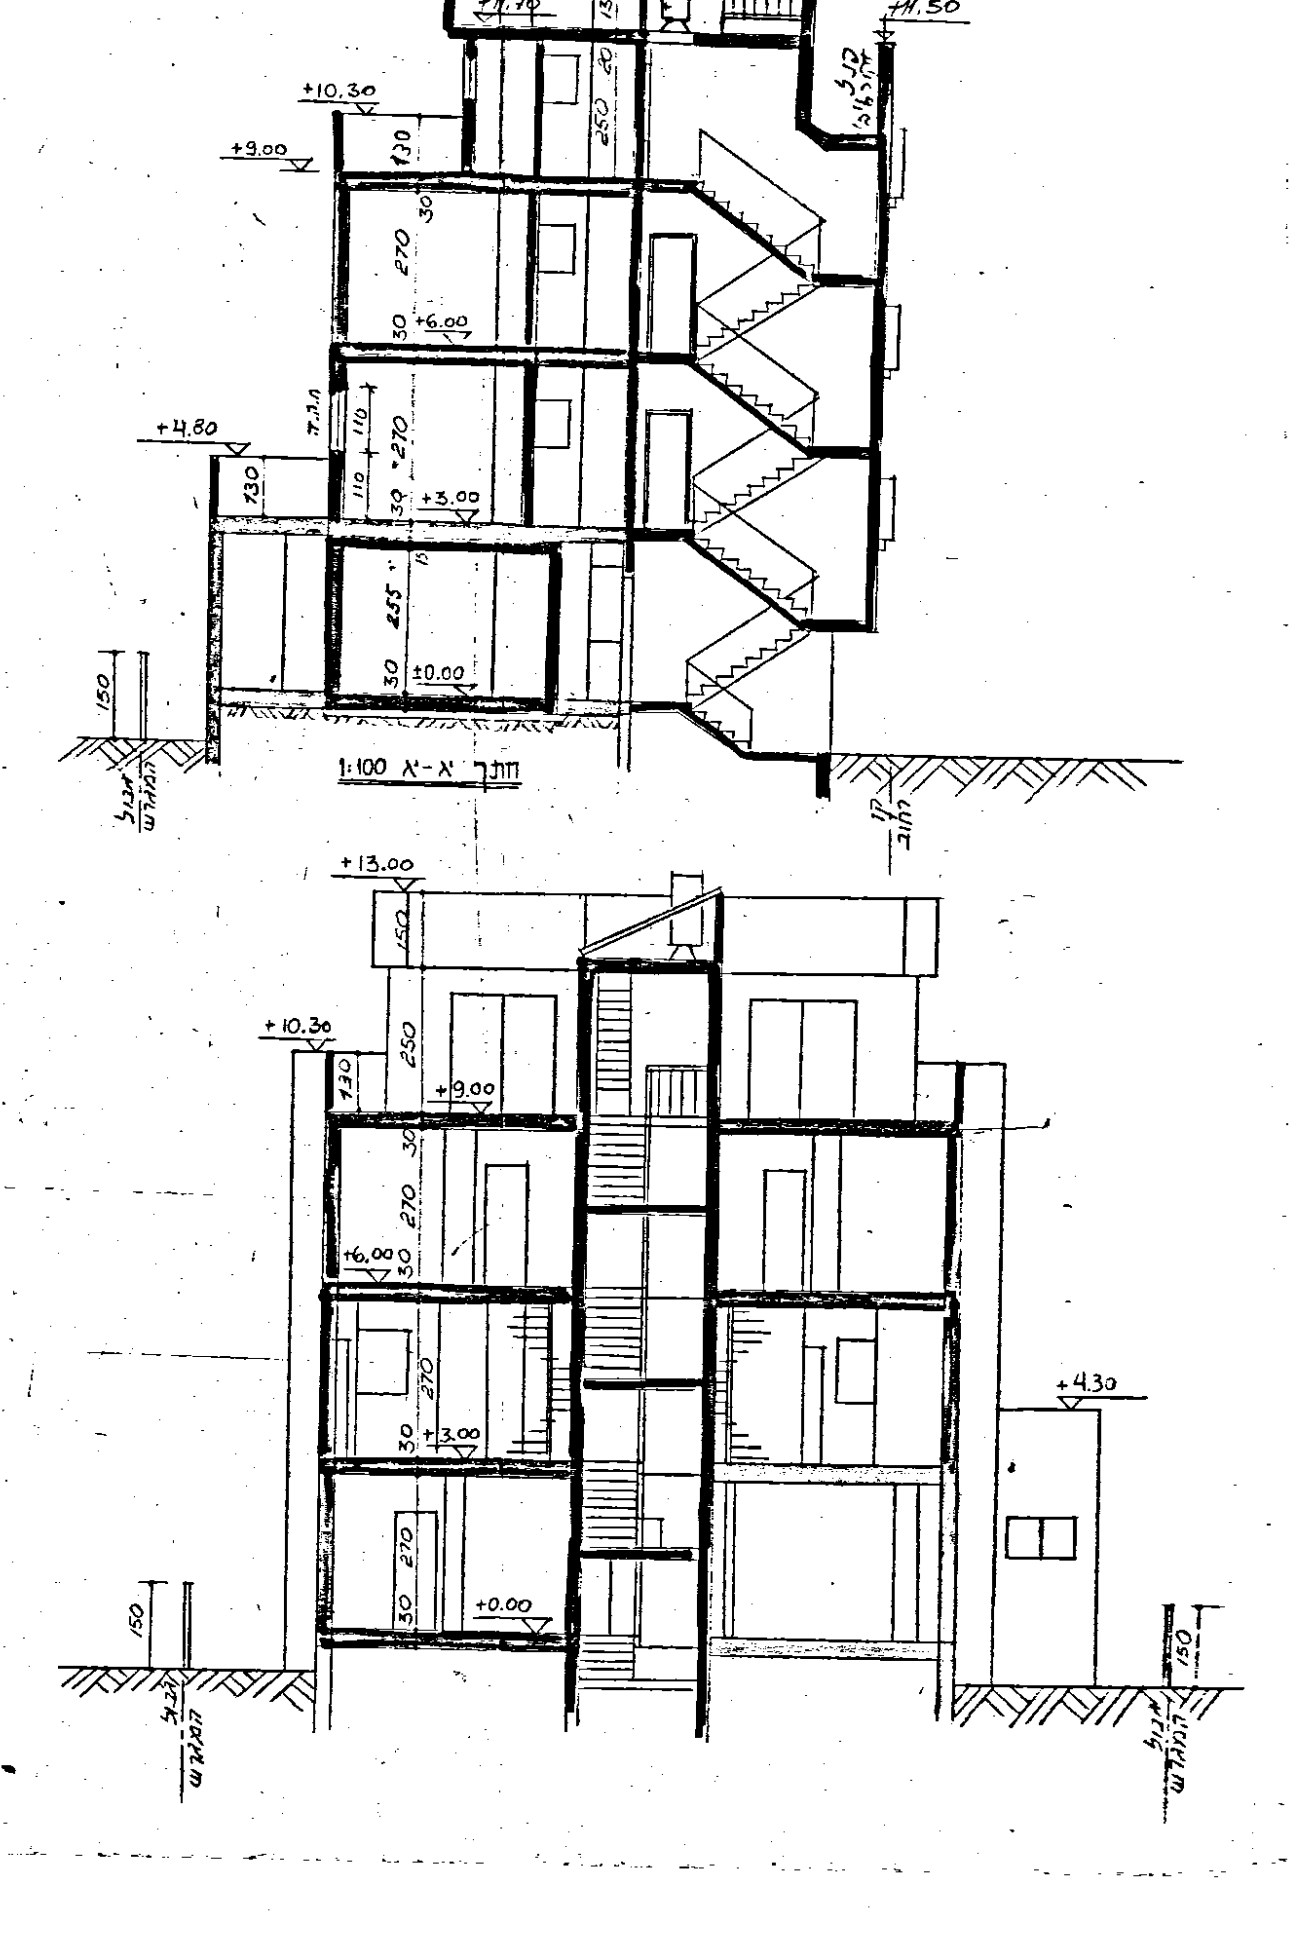

חתך א - א 1:100
+13.00
+10.36
+3.00
+0.00

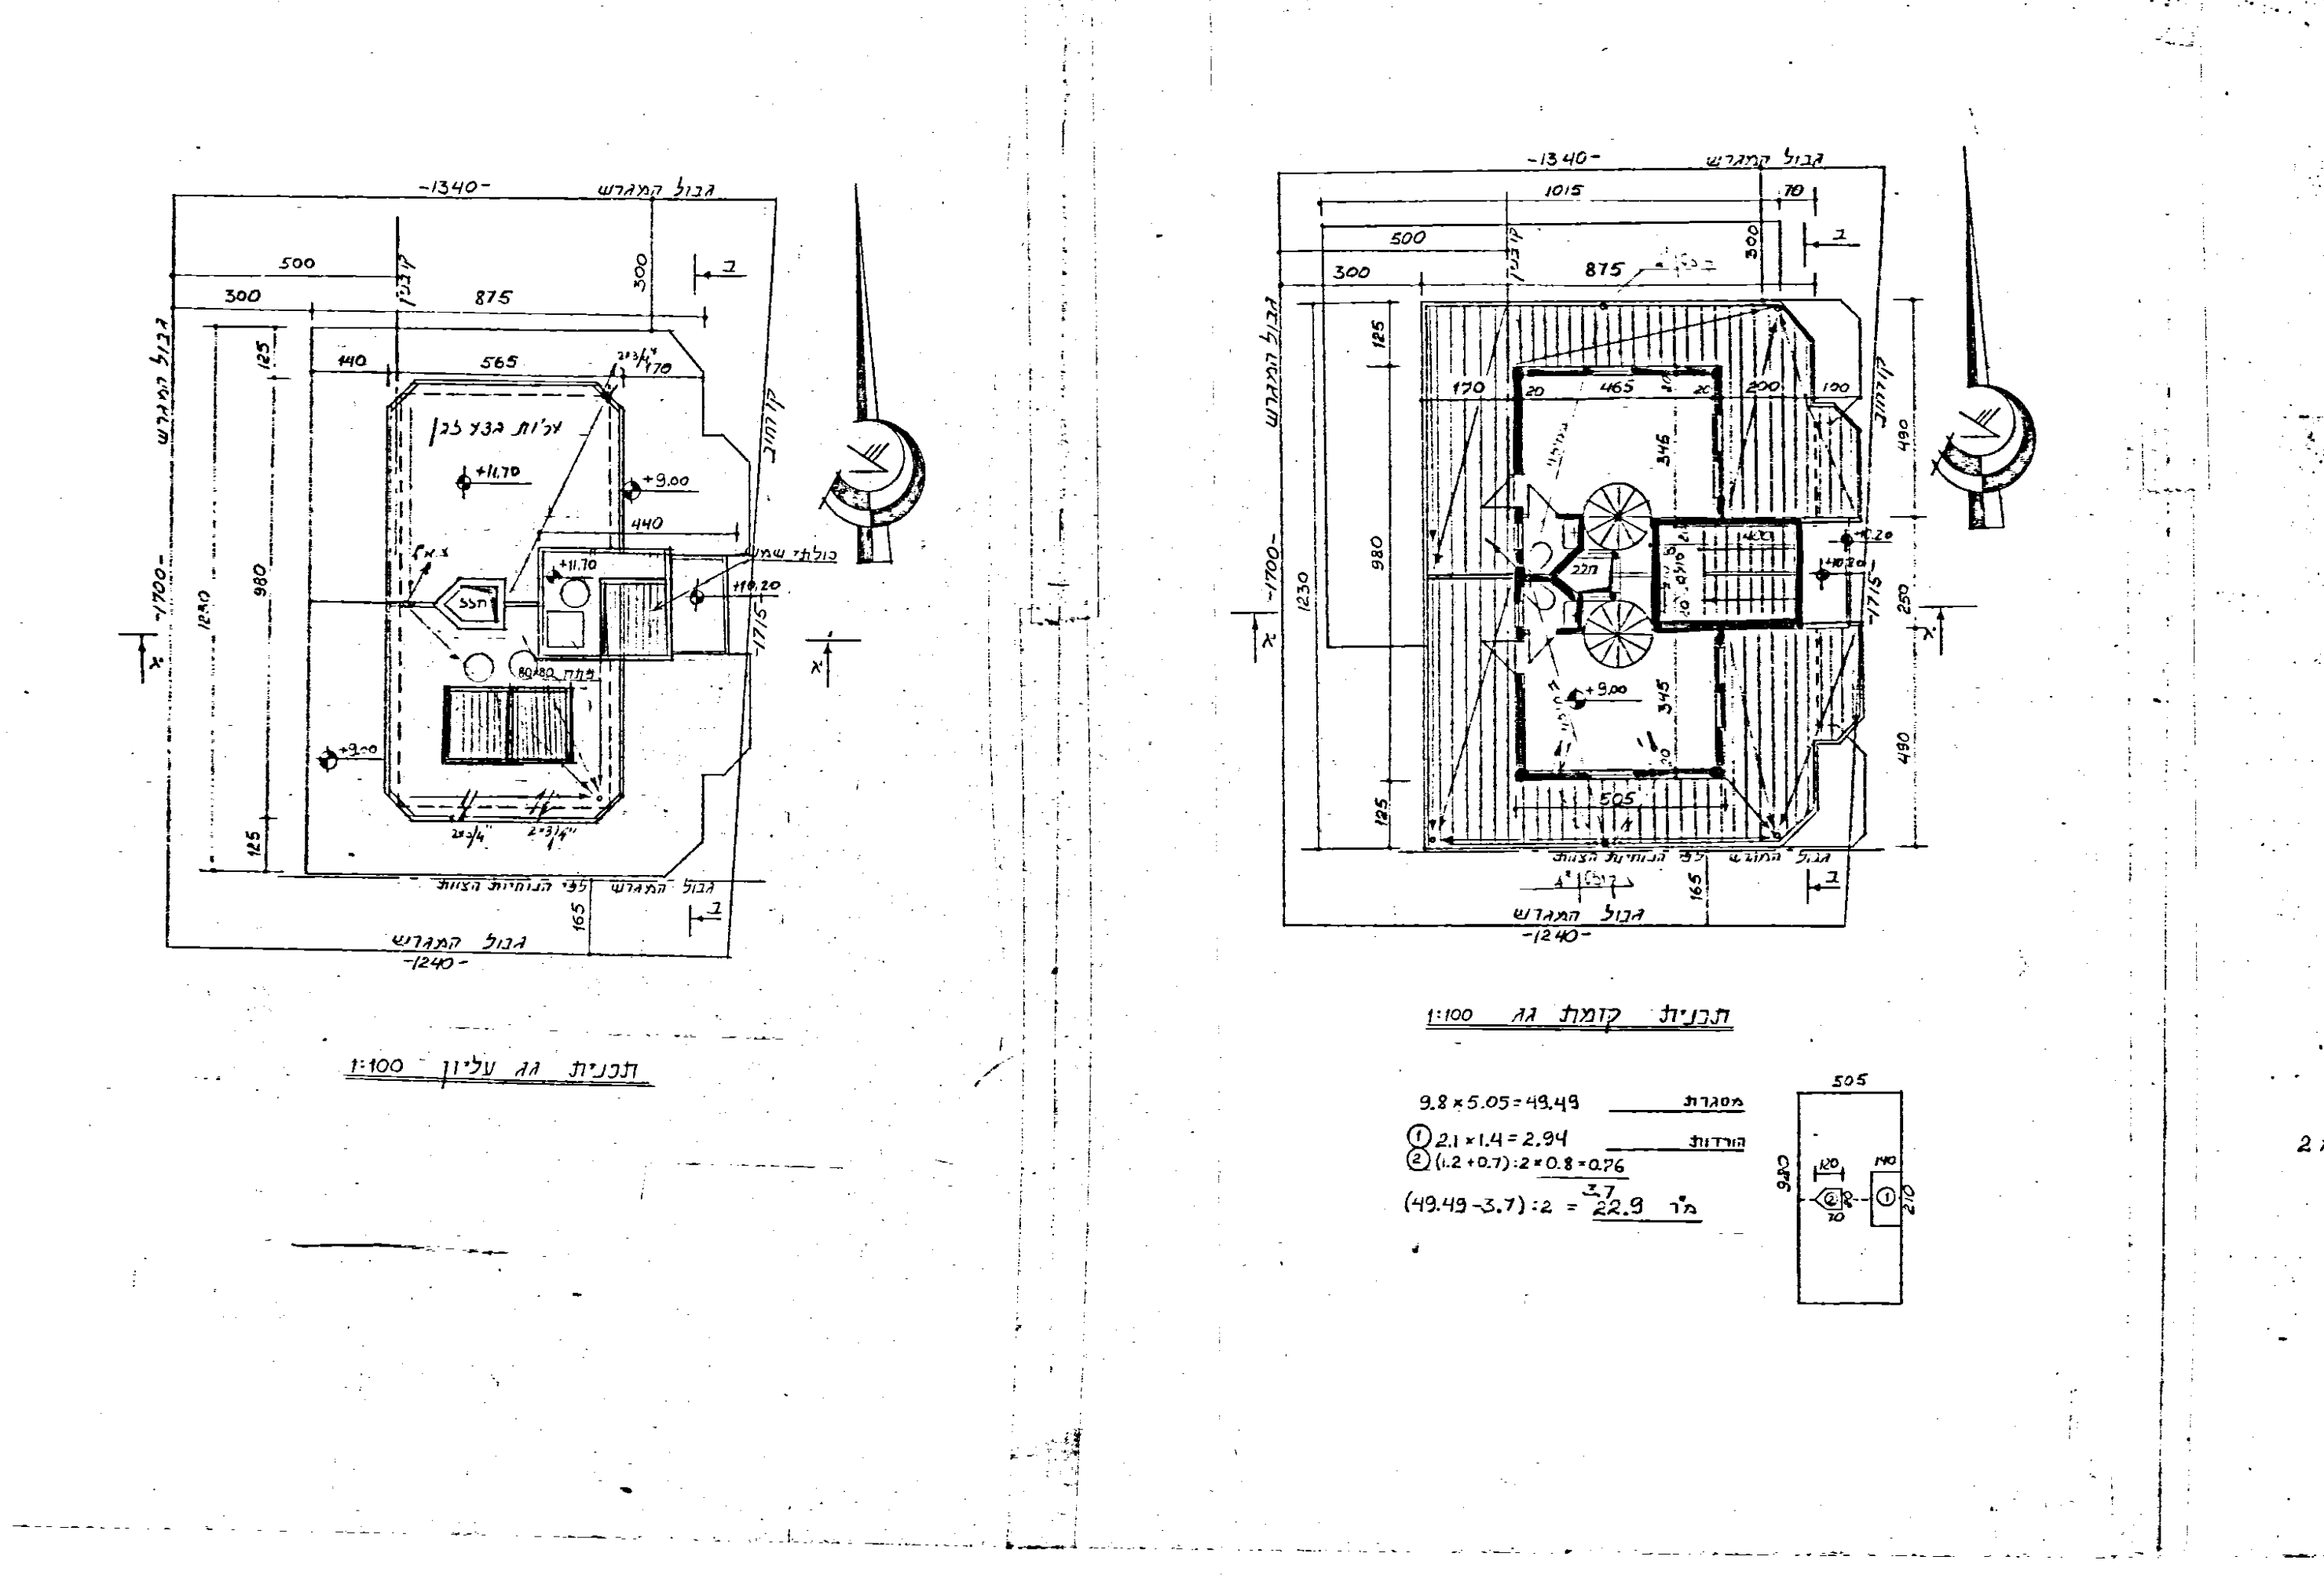

תכנית גג עליון 1:100
תכנית קומת גג 1:100
13.40
875

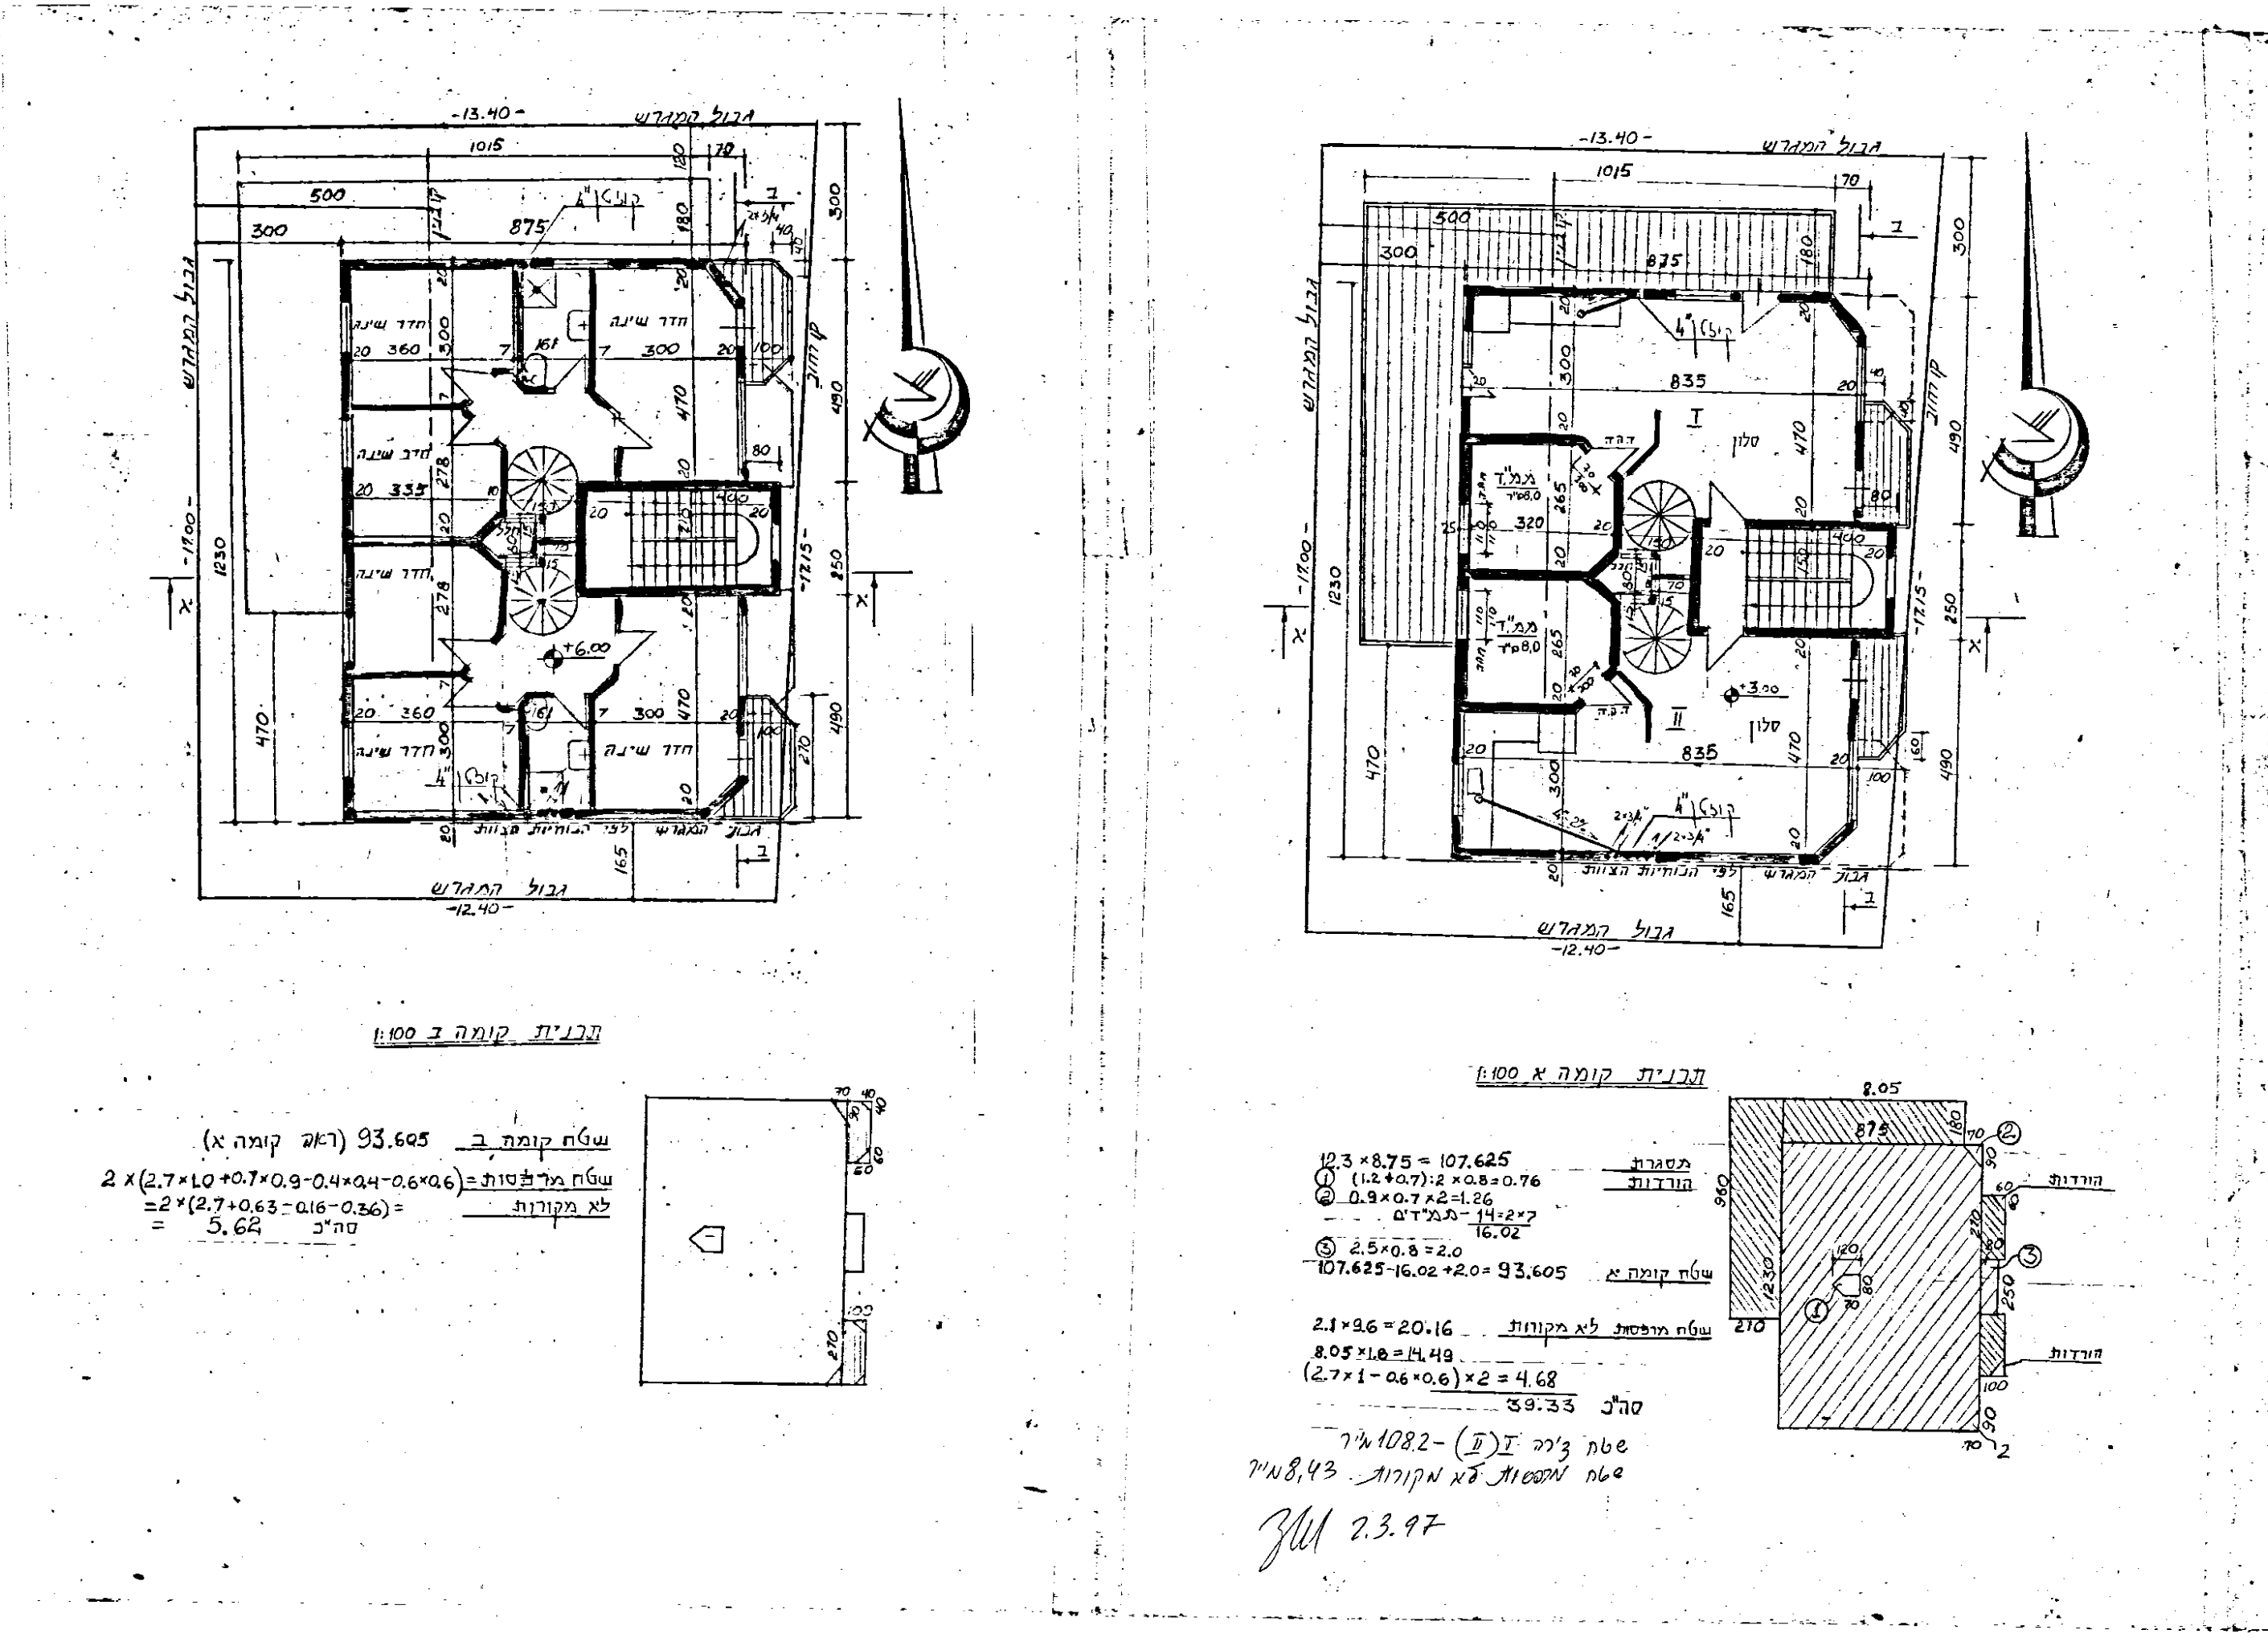

תכנית קומה ב 1:100
תכנית קומה א 1:100
13.40

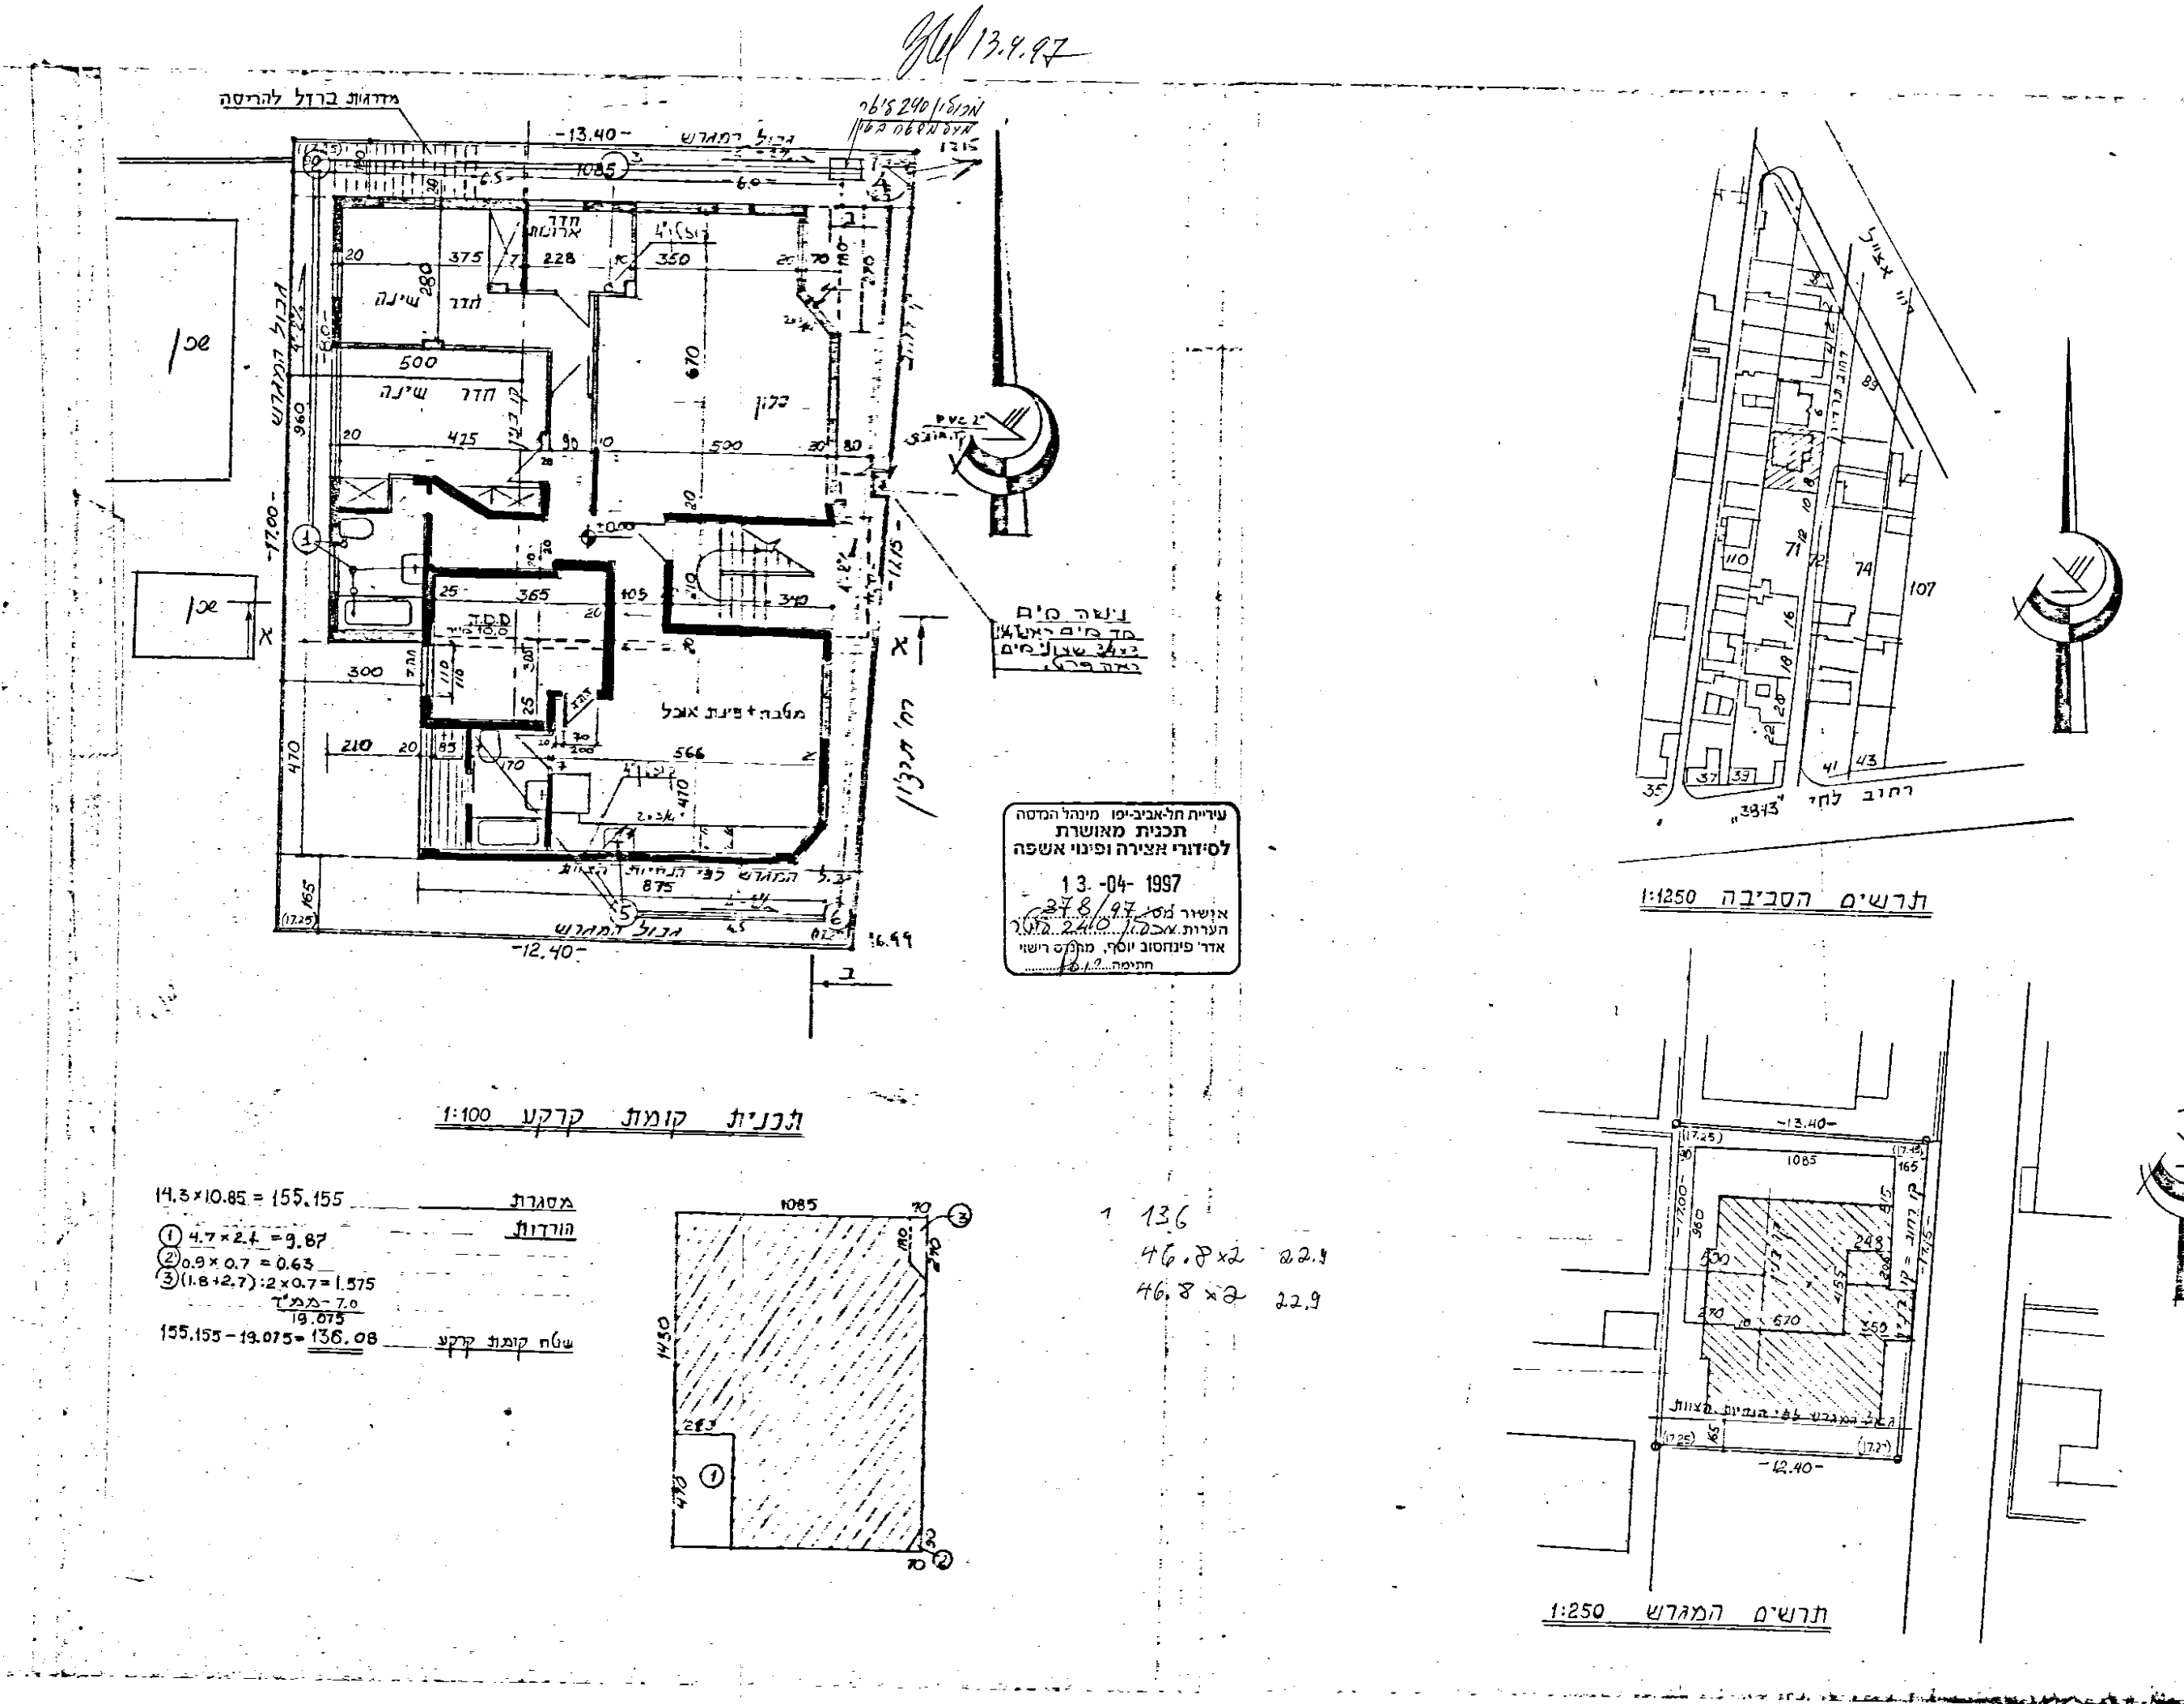

תכנית קומת קרקע 1:100

13.4.97

עיריית תל-אביב-יפו
הועדה המקומית
13-04-1997

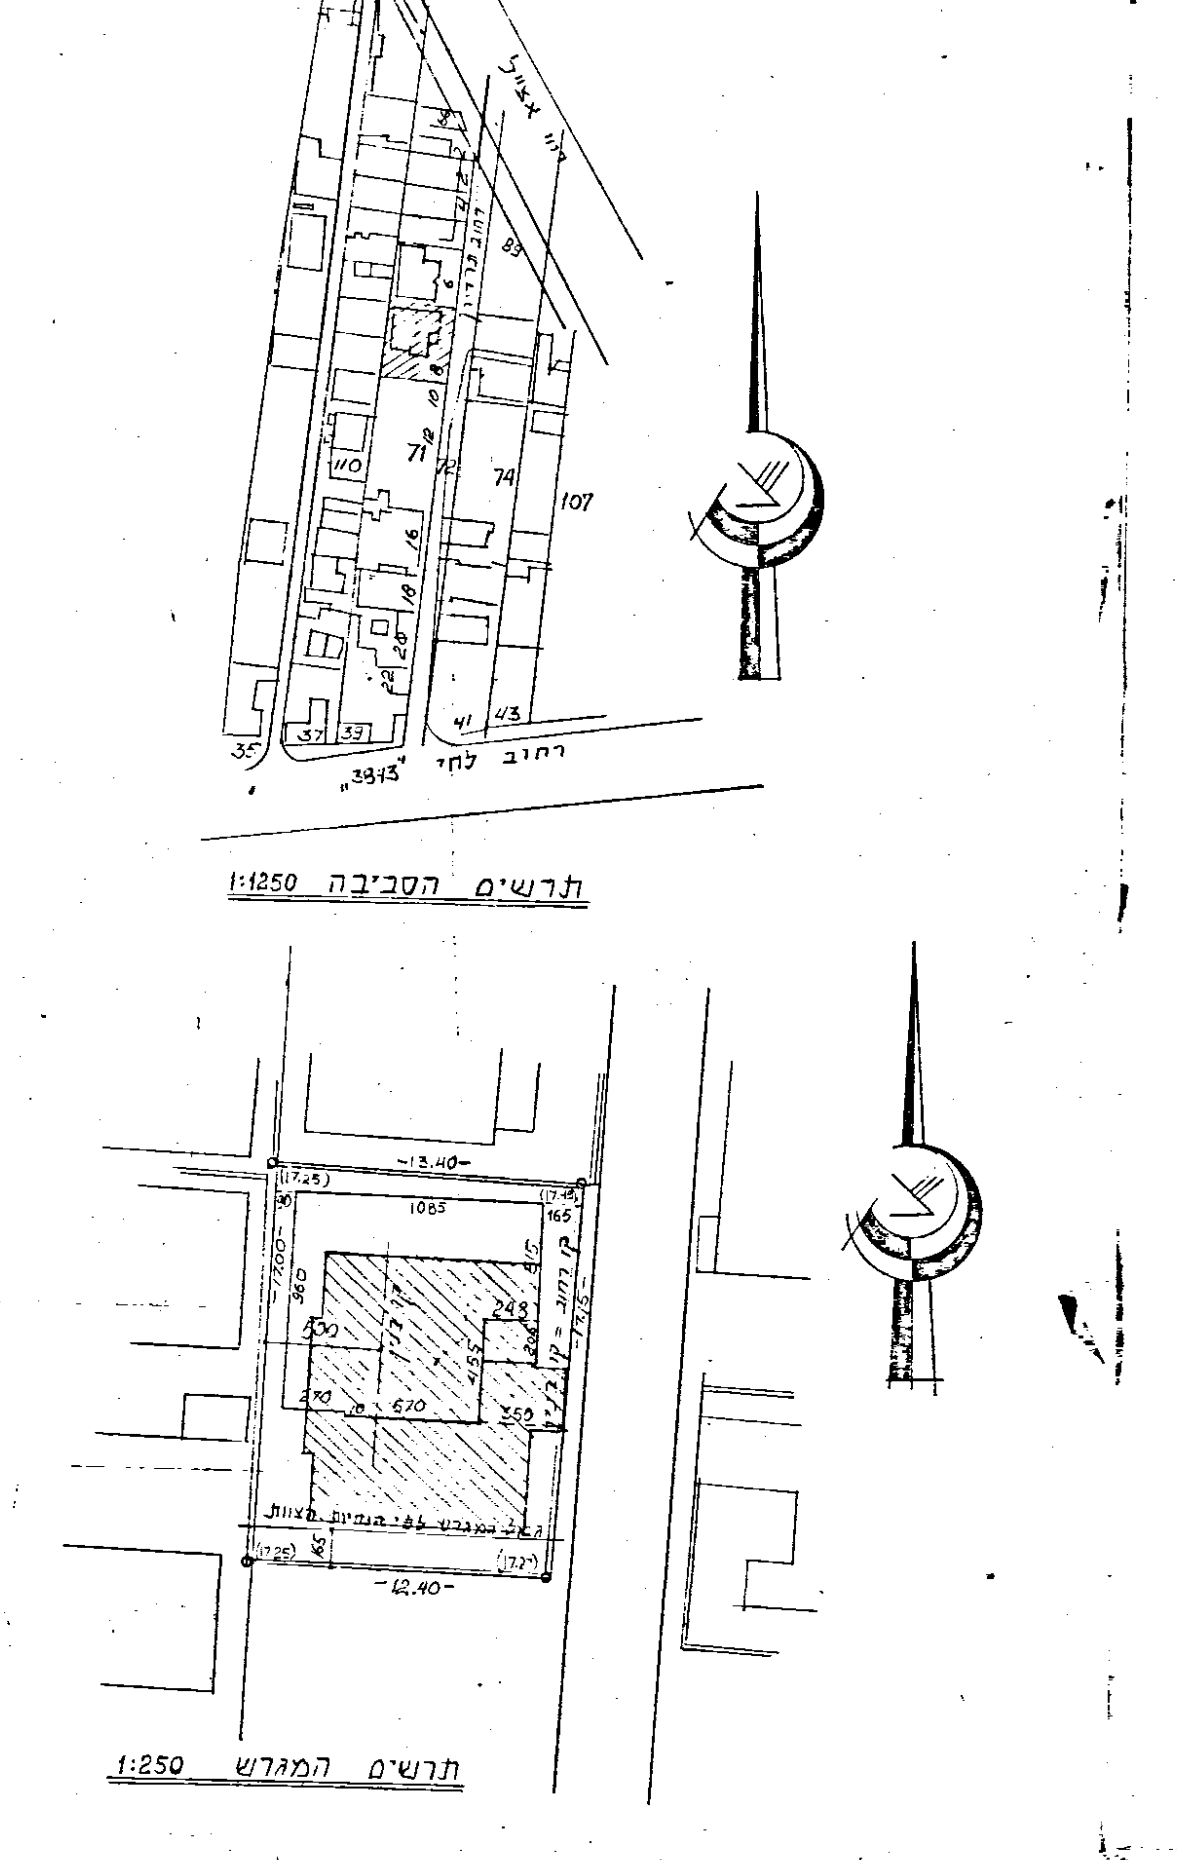

תרשים הסביבה 1:1250
תרשים המגרש 1:250

טופס 1
תקנה 2(א)

חוק התכנון והבניה, התשכ״ה-1965
בקשה להיתר בניה או לשימוש במקרקעין

4048-008

ביטול היתר

איכות נמוכה

נתקבל 25-07-1997

378
13.04.97

השטחים המבוקשים לבניה בכל מפלס בנפרד (עפ״י תכנית הבניה)

השטחים המותרים לבניה בכל המפלסים יחד (עפ״י אסמכתא: חוק, תקנות, תכנית)

2215	71	6135	8	4048

גרניט 8

הוספת קומה ד׳ ו-2 חדרי על גג

30394840
גרינשטיין
שמאי רמלק 60
5240857