הוראה ביצוע מרחב מוגן דירתי

המרחב המוגן הדירתי יבנה בהתאם לתקנות ההתגוננות האזרחית (מפרטים לבניה מקלטים), (תיקון) תשנ"א 1991 שפורסם בס' 5425 מיום 3.3.1992.

עקרונות התכנון

בתכנון המרחב המוגן הדירתי יתקיימו עקרונות יסוד אלה:

המרחב המוגן הדירתי ייבנה בטון במבנה "קופסה", עשוי יציקה אחת והדוק בכל חלקיו, ללא קורות ועמודים.

רצפת המרחב המוגן הדירתי, קירותיו ותקרתו יהיו [illegible] (יצוקים בדיקטים בלבד).

קירות המרחבים המוגנים הדירתיים יהיו רציפים לכל גובה הבניין, ליצירת מגדל מוגן. יציבות המגדל המוגן של המרחבים המוגנים הדירתיים תובטח מפני בוהות אופקיים.

העובי המזערי של חלקי המרחב המוגן הדירתי יהיה כאמור בתקנה 208.

התכנון שלד המרחב המוגן הדירתי ייעשה בהתאם לת"י 466.

מידות מזעריות של פתח אור - דלת כניסה - 60/200 ס"מ או 70/200.

סוג דלת הכניסה - דלת הדף הידראית במפורט בתקנה 202.

הגנה על דלת כניסה - במפורט בתקנות (ע"י מחיצות ומרחקים מקווי בניין).

חלון - בשטח מירבי 1.21 מ"ר, גובה מפלס אדן לא יפחת מ-1.05 מ'.
חלון ההדף הדירתי יכלול שני חלקים עיקריים:
א. חלון בהתוגי פגיע/ אטום מפני גזים
ב. אלמנט מגן חיצוני להדף-הקן לפי תקנה 205.

בטון

הבטון בכל חלקי המרחב המוגן הדירתי יהיה מסוג ב-300 לפי דרישות ת"י 118. ההוזק האופייני והורקי הוכן של הבטון השובנות ייקבע לפי ת"י 466.

הכנת המרחב המוגן הדירתי לחשמל, טלפון, טלויזיה וחשמל

באחד מקירות המרחב המוגן יותקן מוביל לצורך הכנה כבל טלפון, תיבת הסתעפות לטלפון ונקודת טלפון יותקנו בהתאם לדרישות חברת בזק.

במרחב מוגן יותקנו שני בתי-תקע, אחד לאנטנת טלויזיה ואחד לאנטנת רדיו. בבית התקע יותקן צינור שקוטרו לא יפחת מ-16 מ"מ, אשר יוצ"א אל מחוץ למרחב.

א. לצורך תאורה רגילה יותקנו לפחות שני גופי תאורה פלורסנטיים, כל אחד שתי מנורות של 36 ווט.
ב. לצורך תאורת חרום, תותקן מנורת חירום אחת לפחות של 36 ווט לפעולה של 4 שעות.
ג. יותקנו שני שקעי חשמל 220 וולט.
ד. יותקן שקע אחד לטלפון חוץ.
ה. תותקן נקודת טלויזיה אחת.

עבודות גימור

פני הדופן הפנימי של הקירות והתקרה של המרחב המוגן הדירתי יהיו חלקים עם גמר יציקת בטון ואין לטייח אותם.
הקירות והתקרה של המרחב המוגן יהיו בגימור צבע או ציפוי אקרילי בעובי שלא יעלה על 2 מ"מ.
קירות המרחב המוגן לא יצופו בצידם הפנימי באריחי חרסינה, באריחים מסוג אחר או בטיח.

את ריצפת המרחב המוגן יש לרצף באריחי ריצוף, מותר להשתמש בכל חומר ציפוי, שיפולים (פנלים) מותר שיהיו מחומר כגון: פי.וי.סי., אולם אין להשתמש בחומרים כגון אריחי ריצוף, חרסינה, טיח וכיוצא באלה.

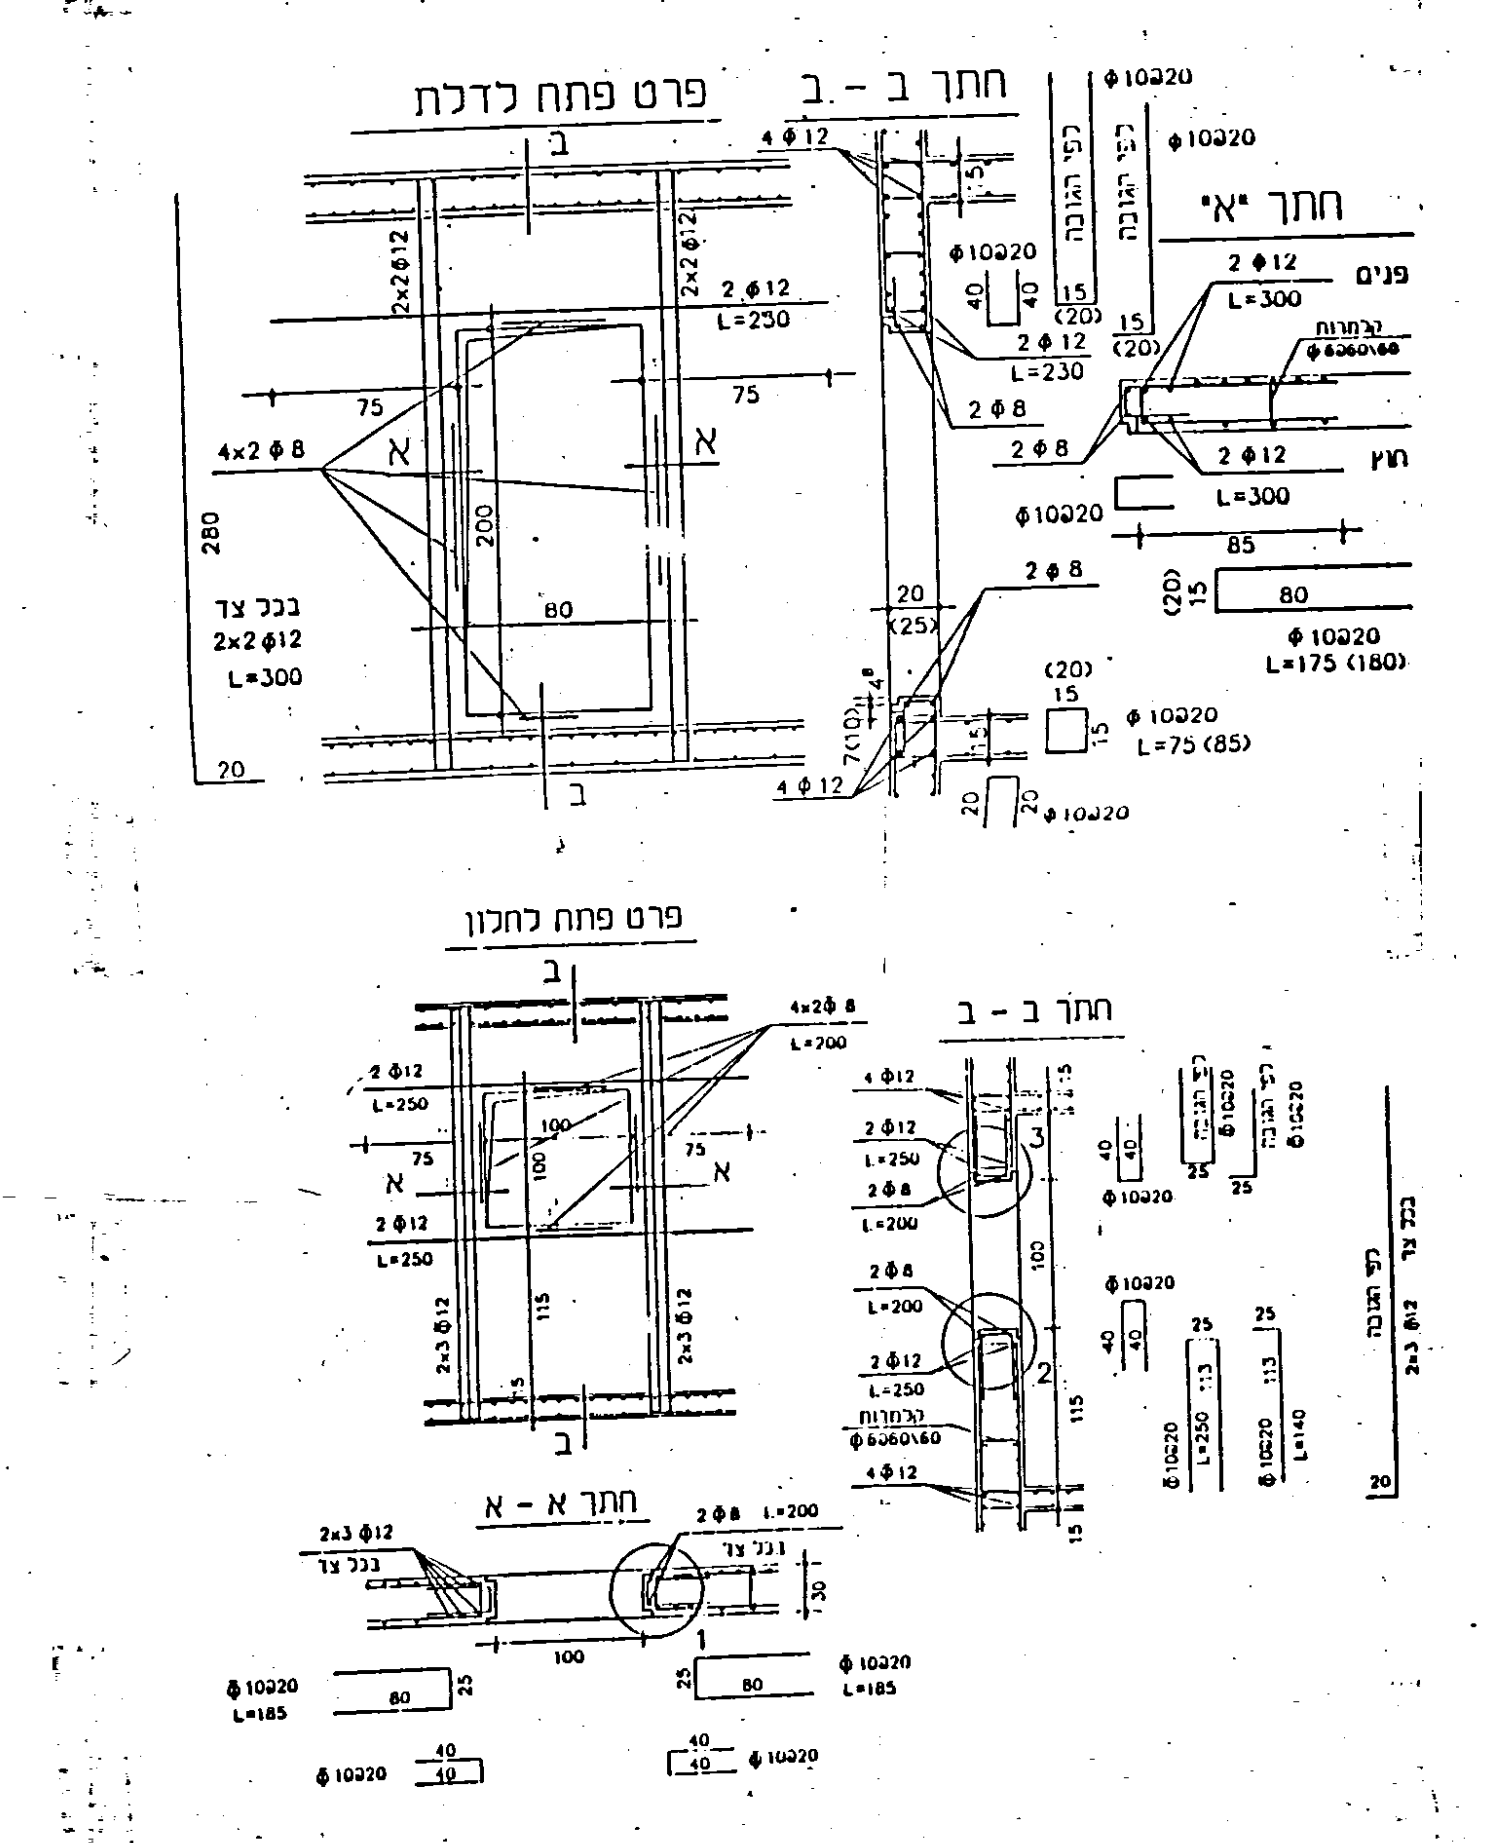

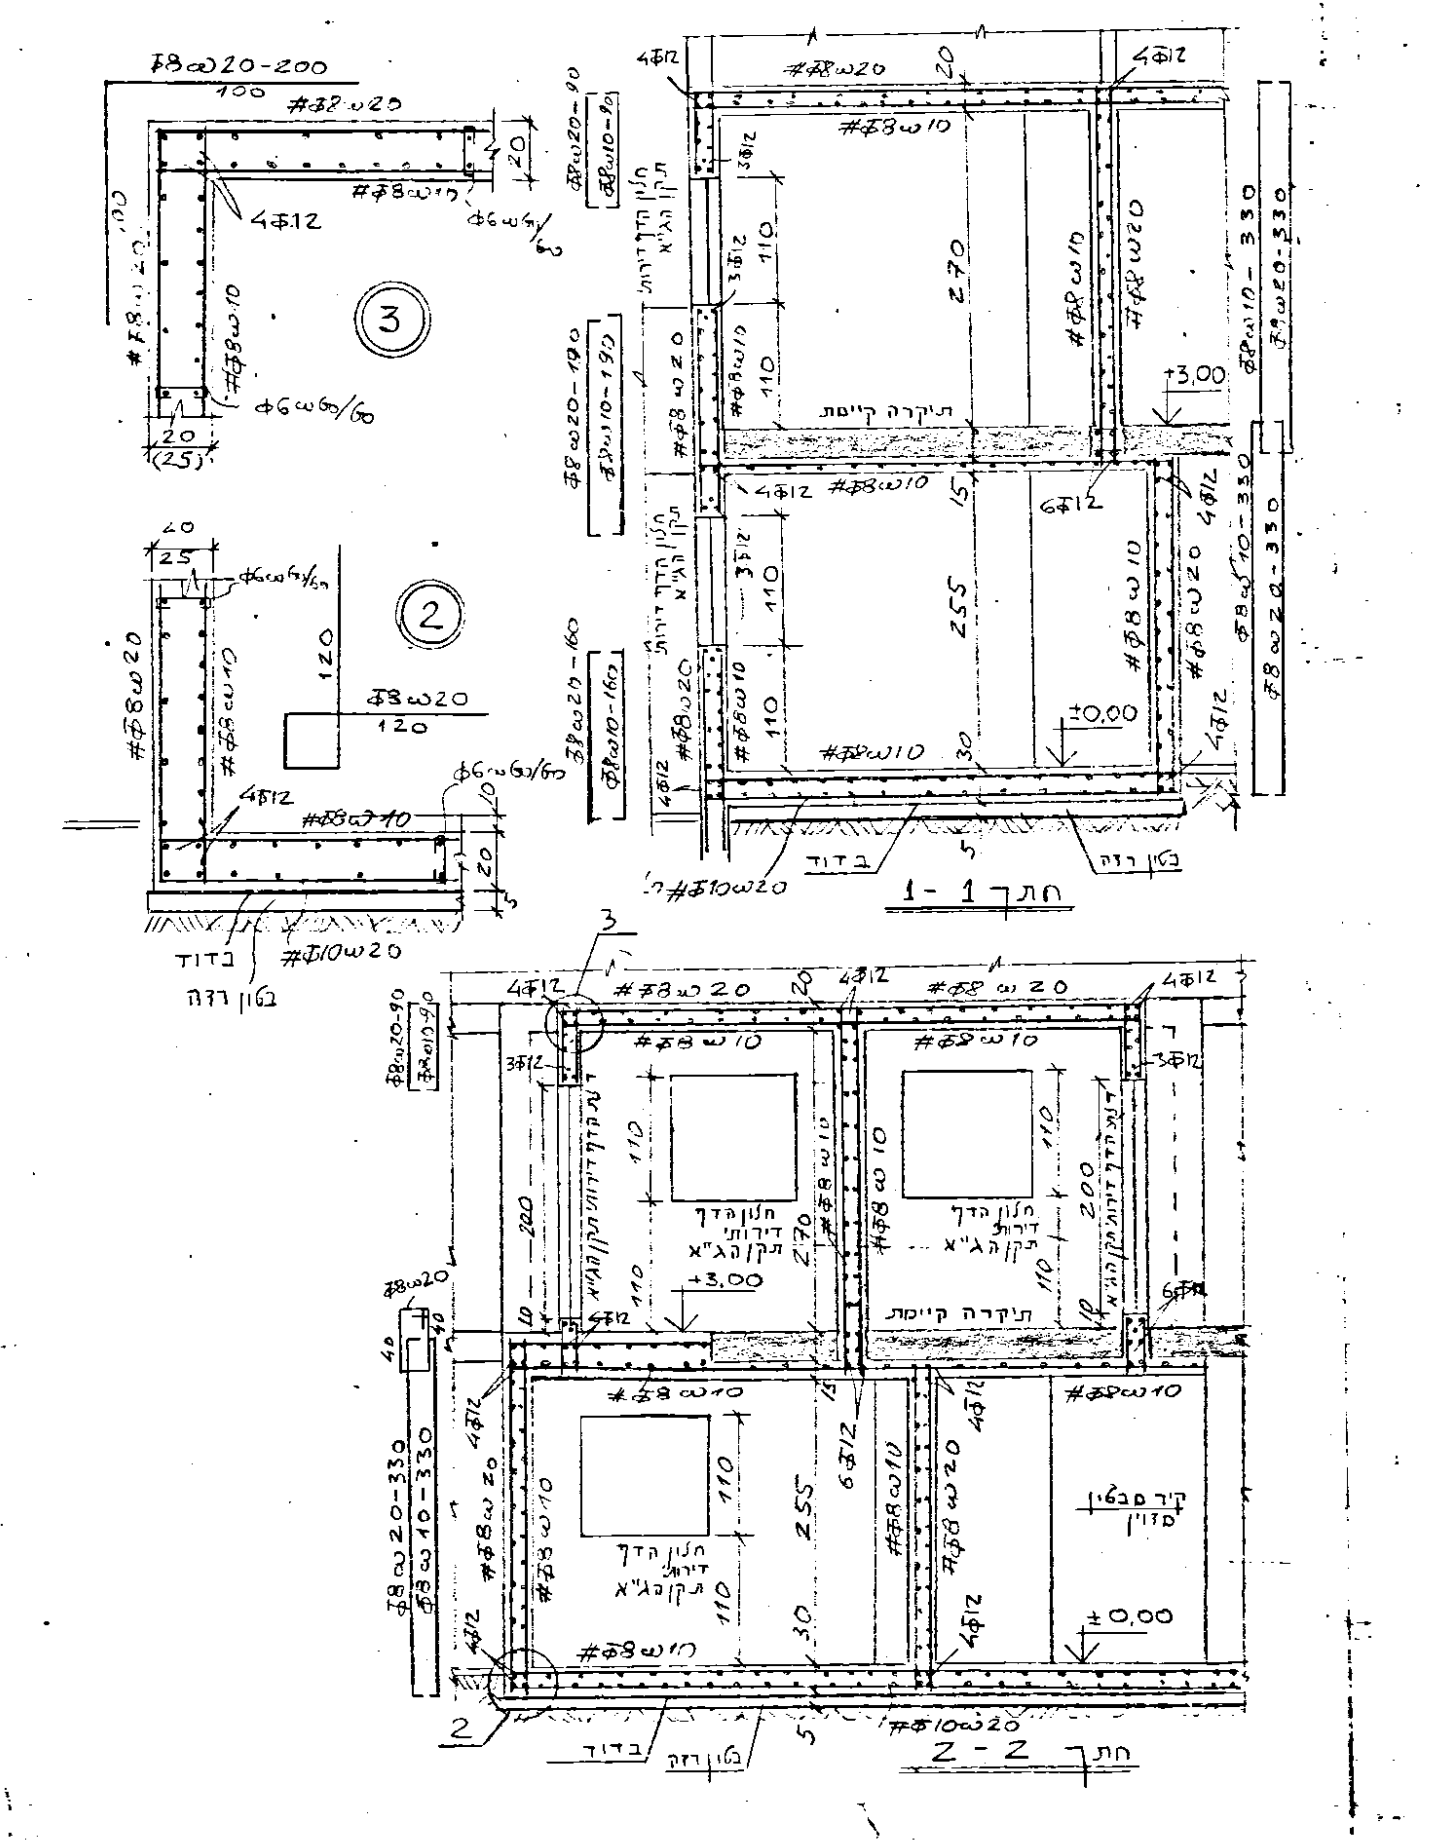

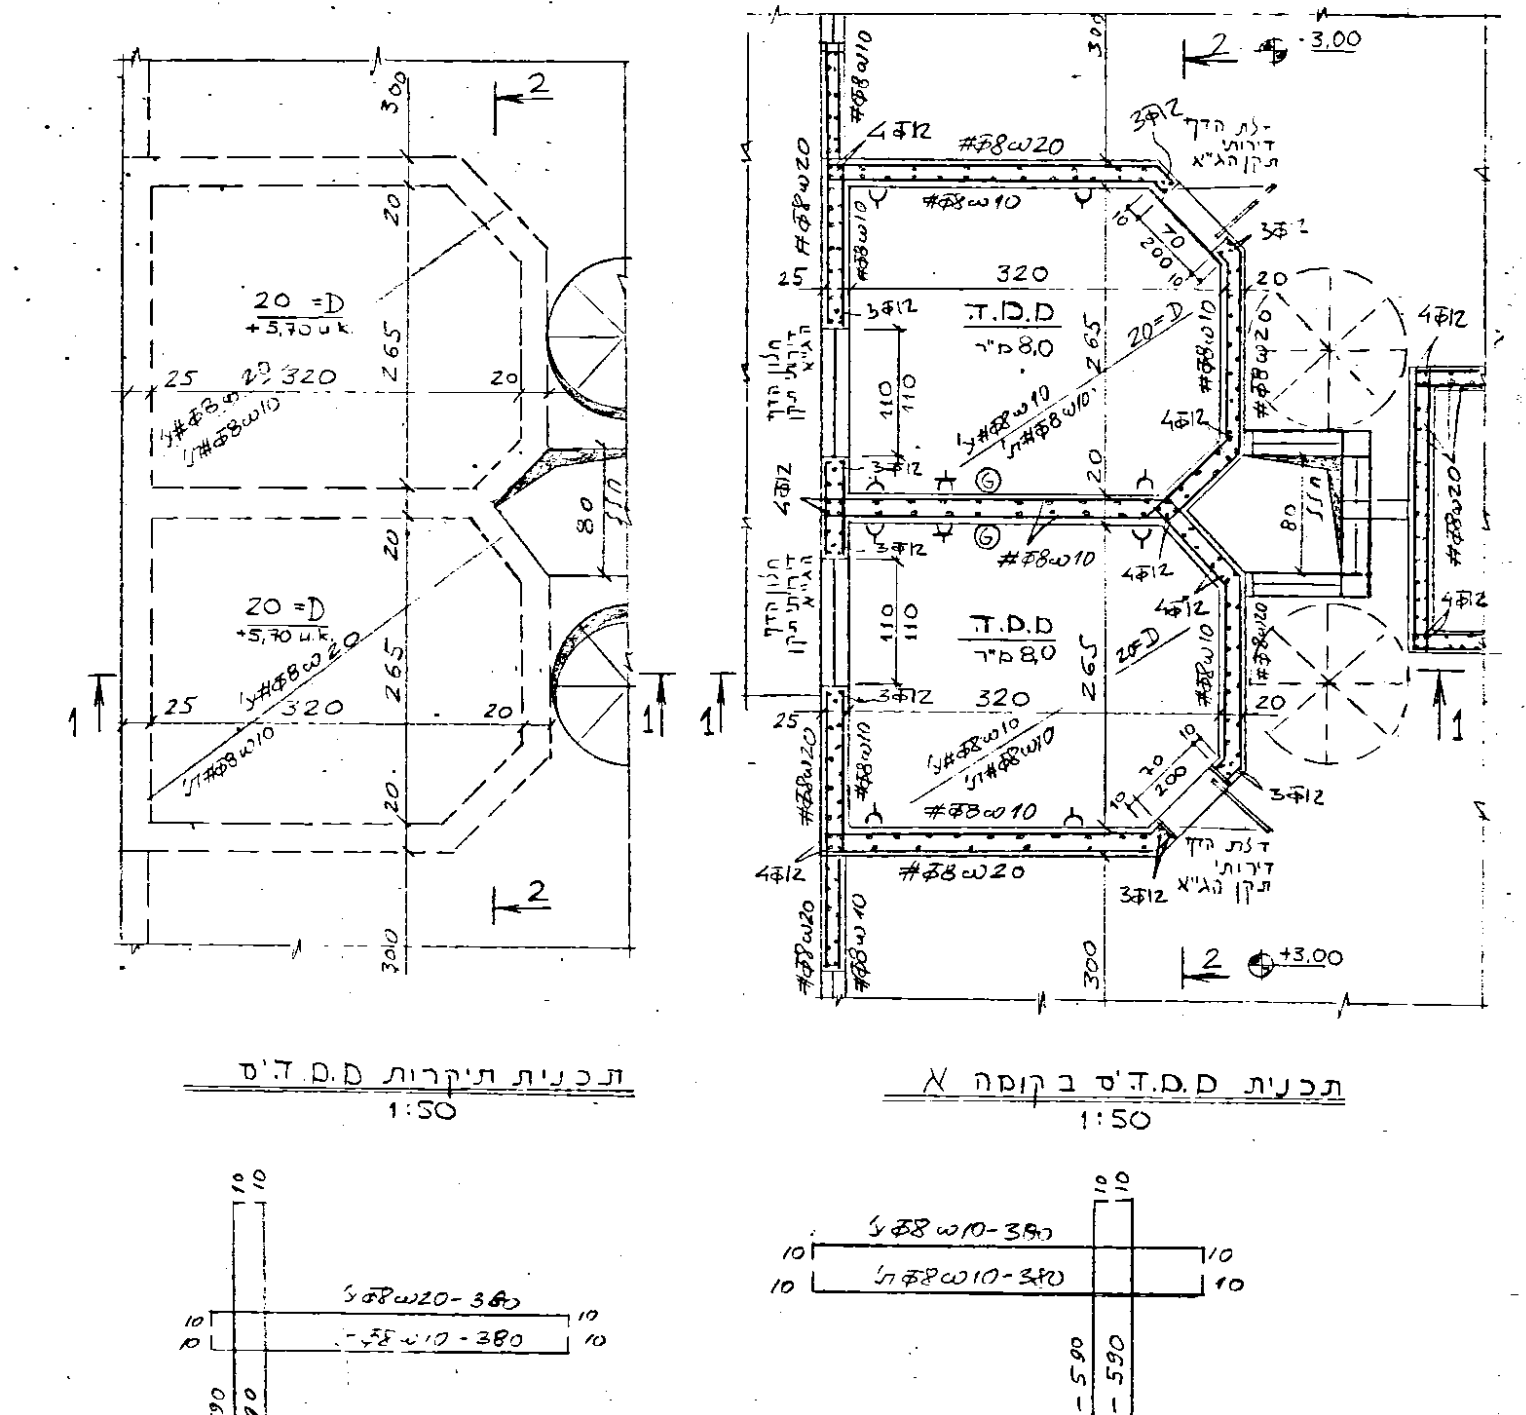
תכנית תקרות ממ"ד 1:50

תכנית ממ"ד בקומה א 1:50

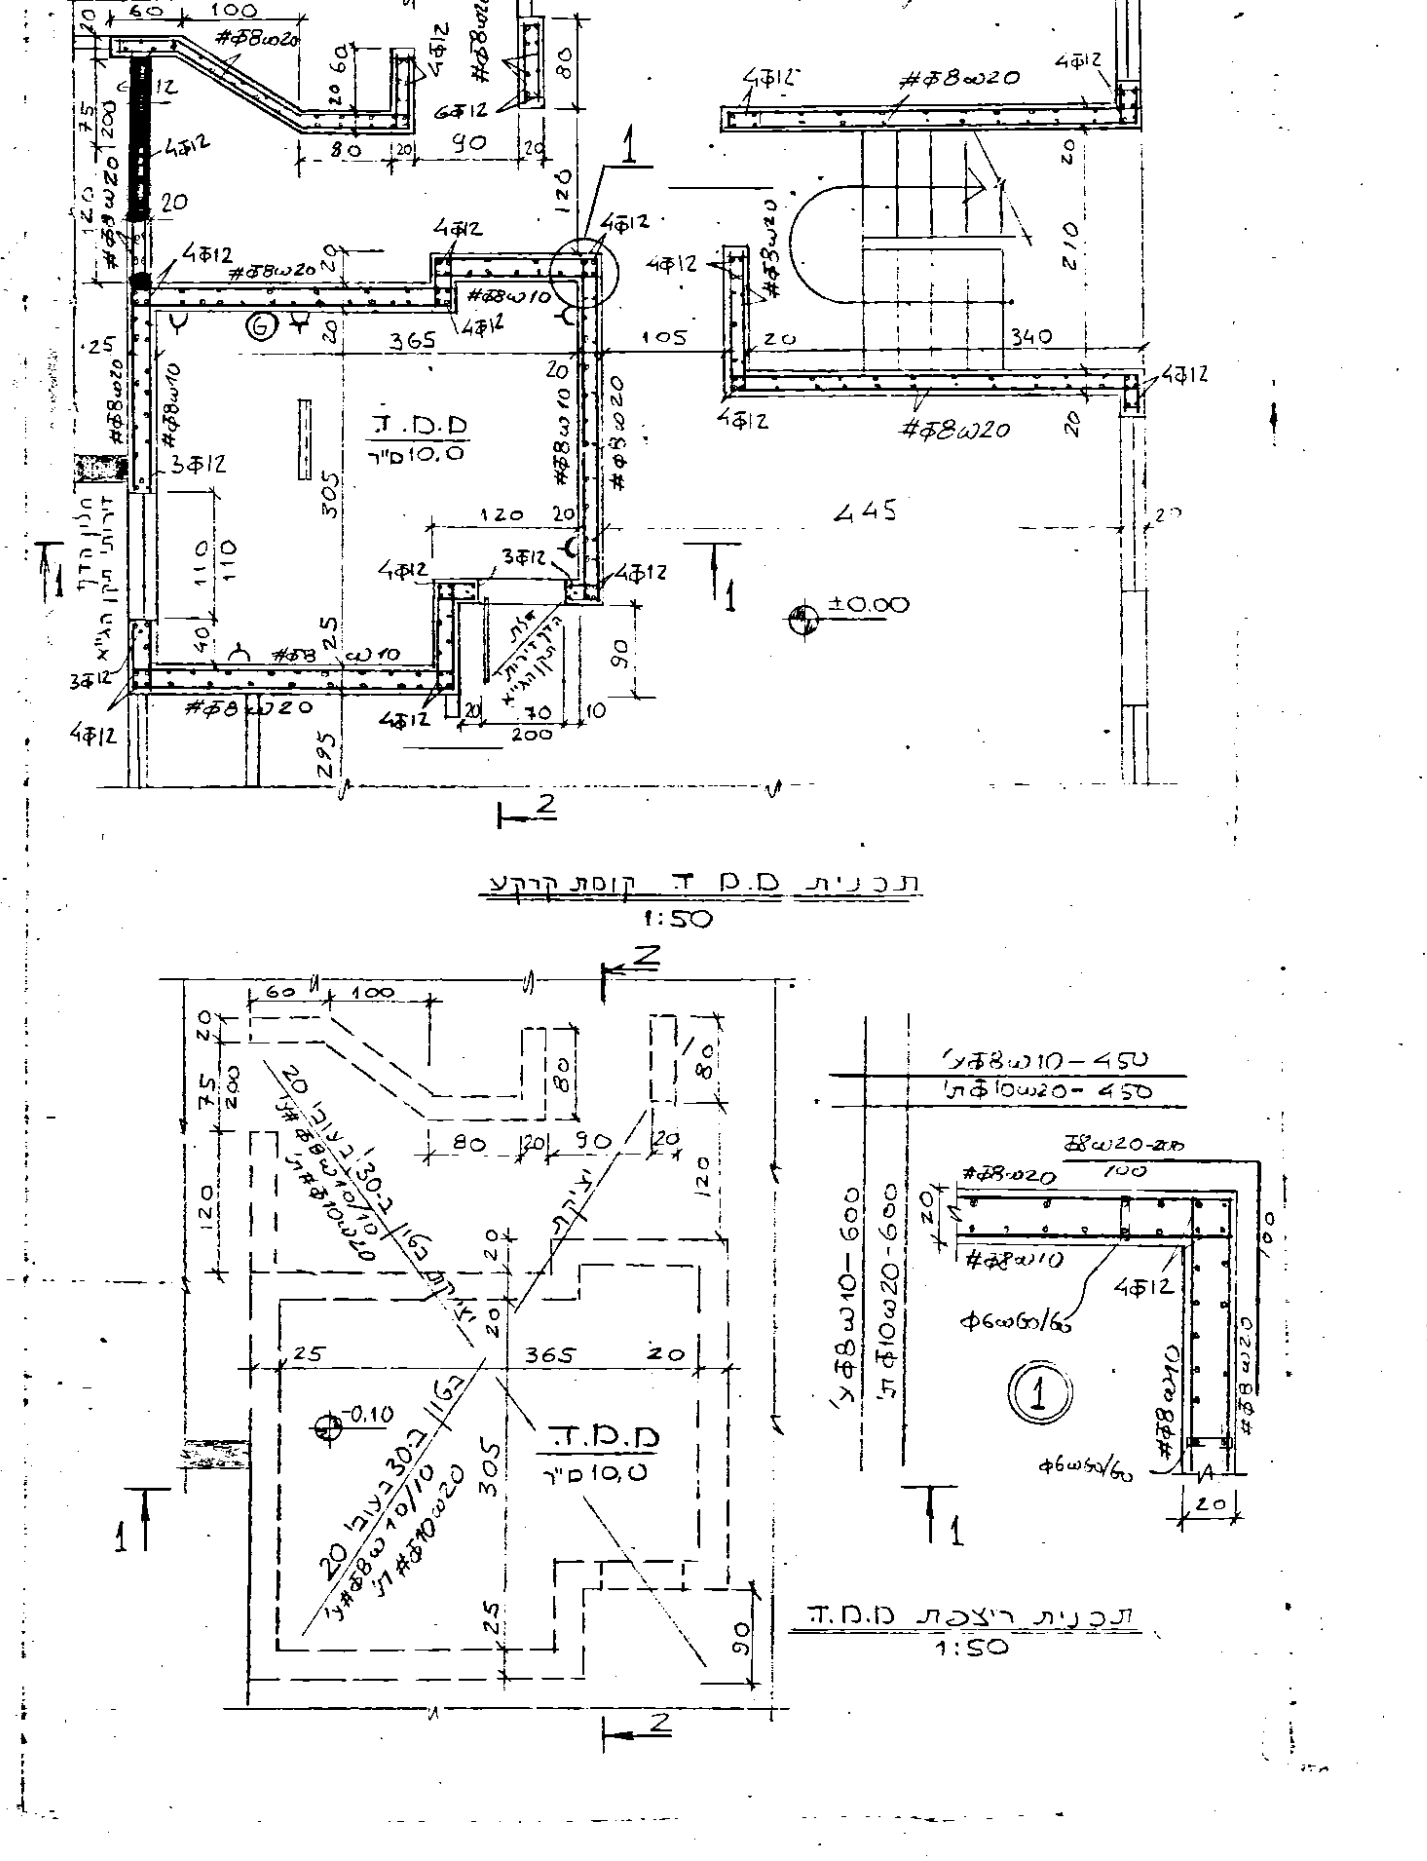
תכנית ממ"ד קומת קרקע

תכנית רצפת ממ"ד 1:50

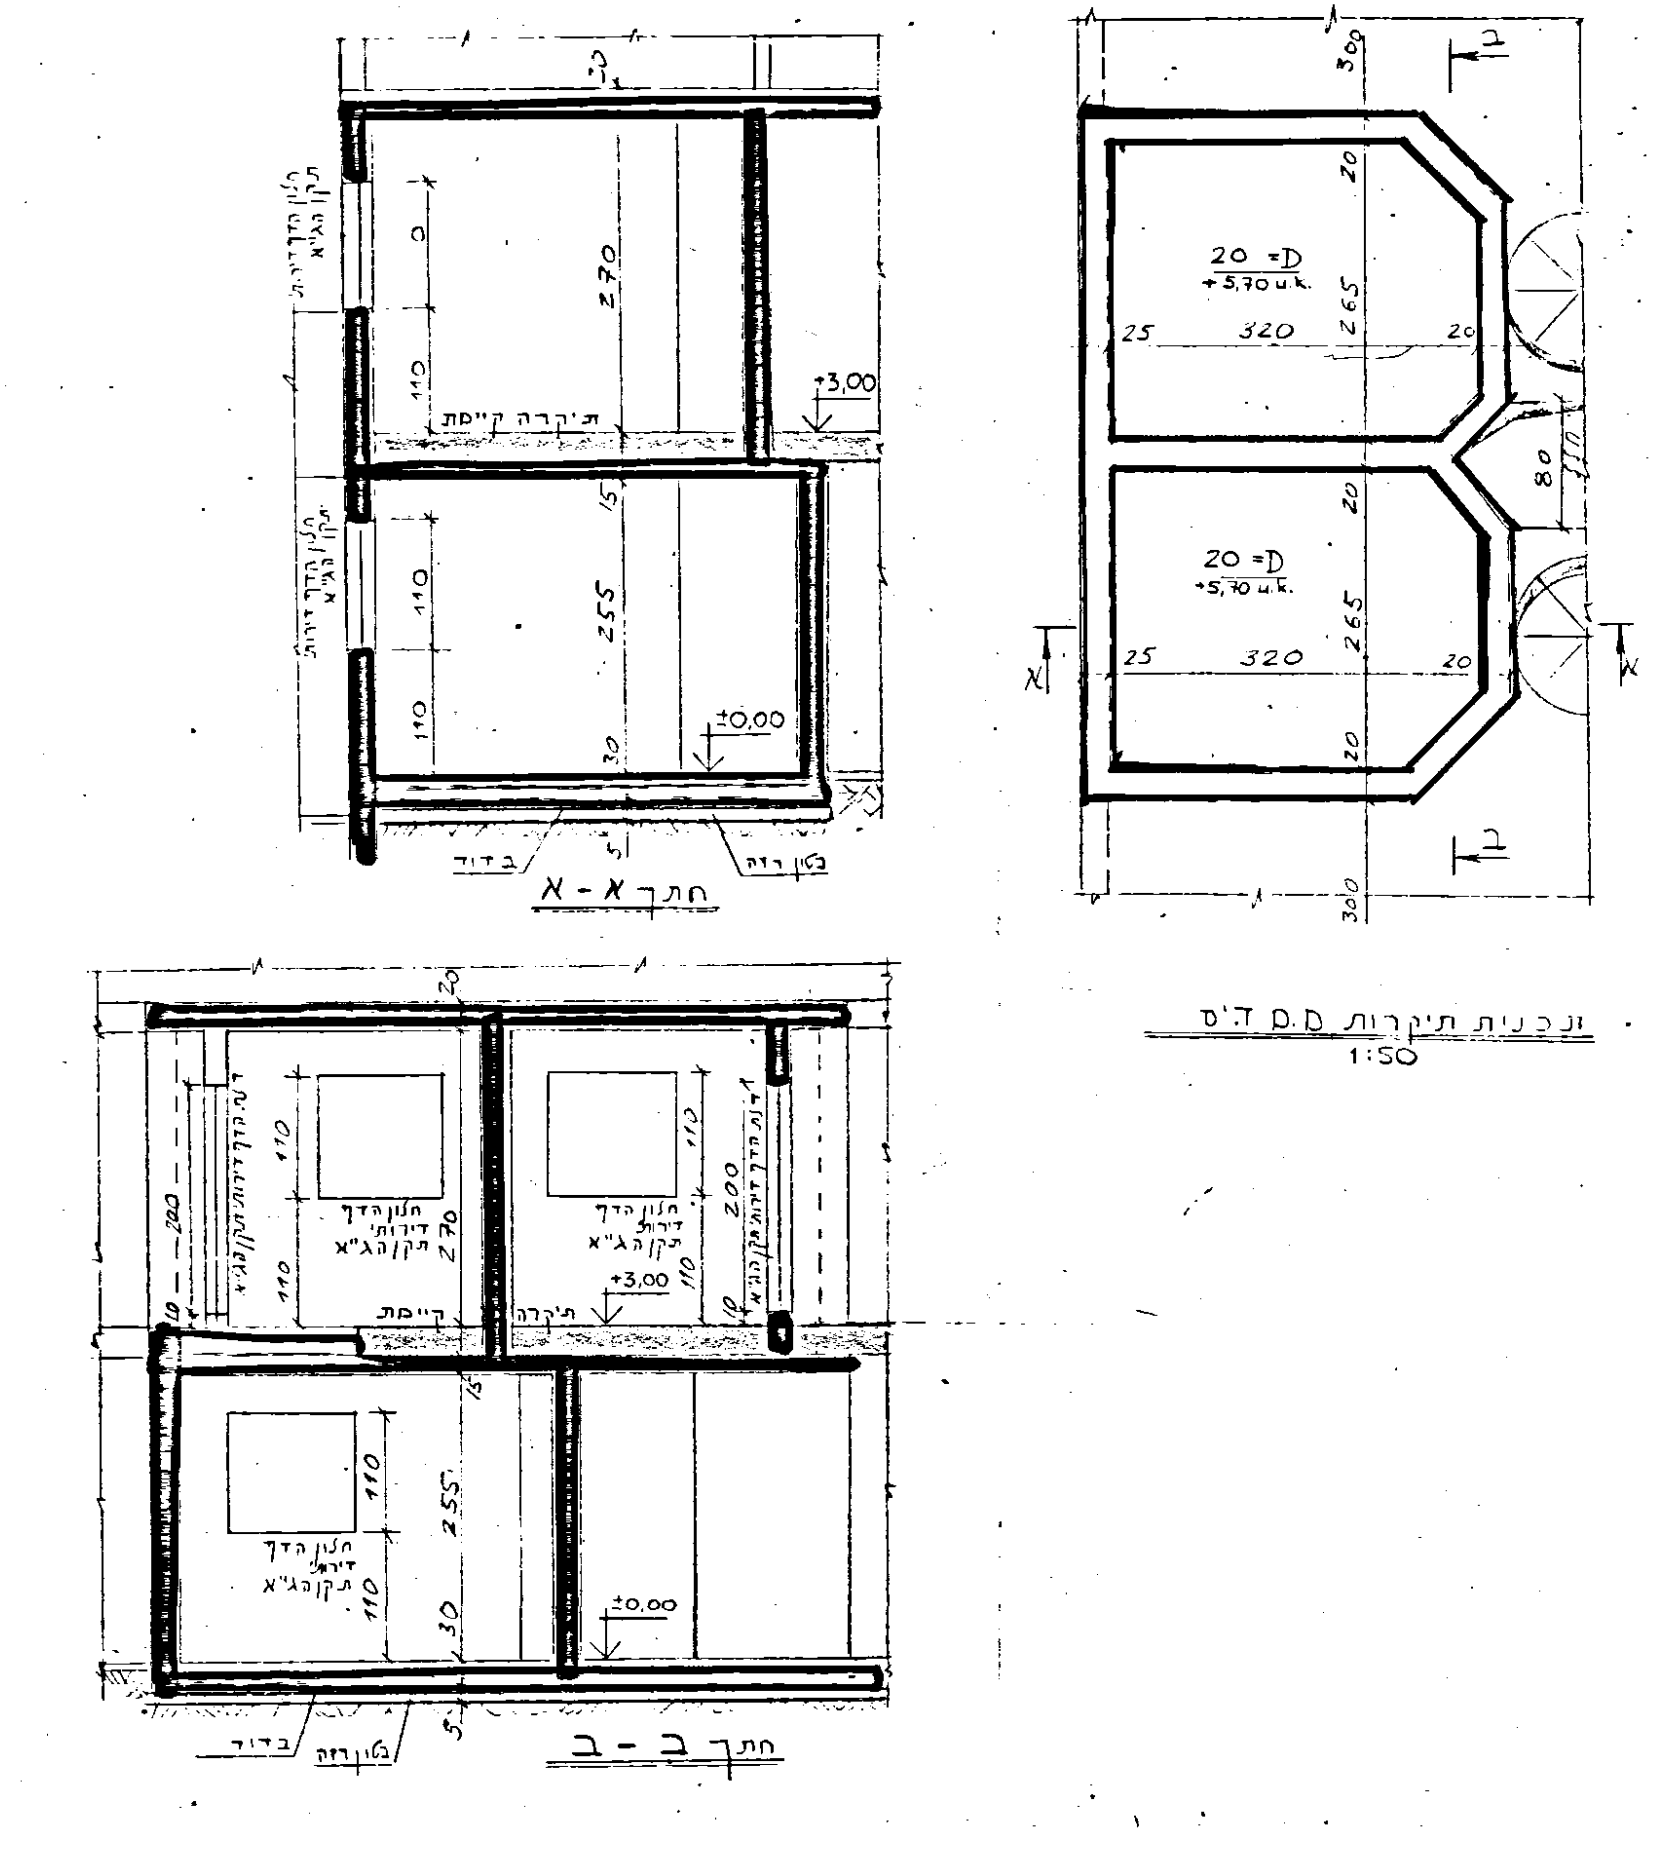

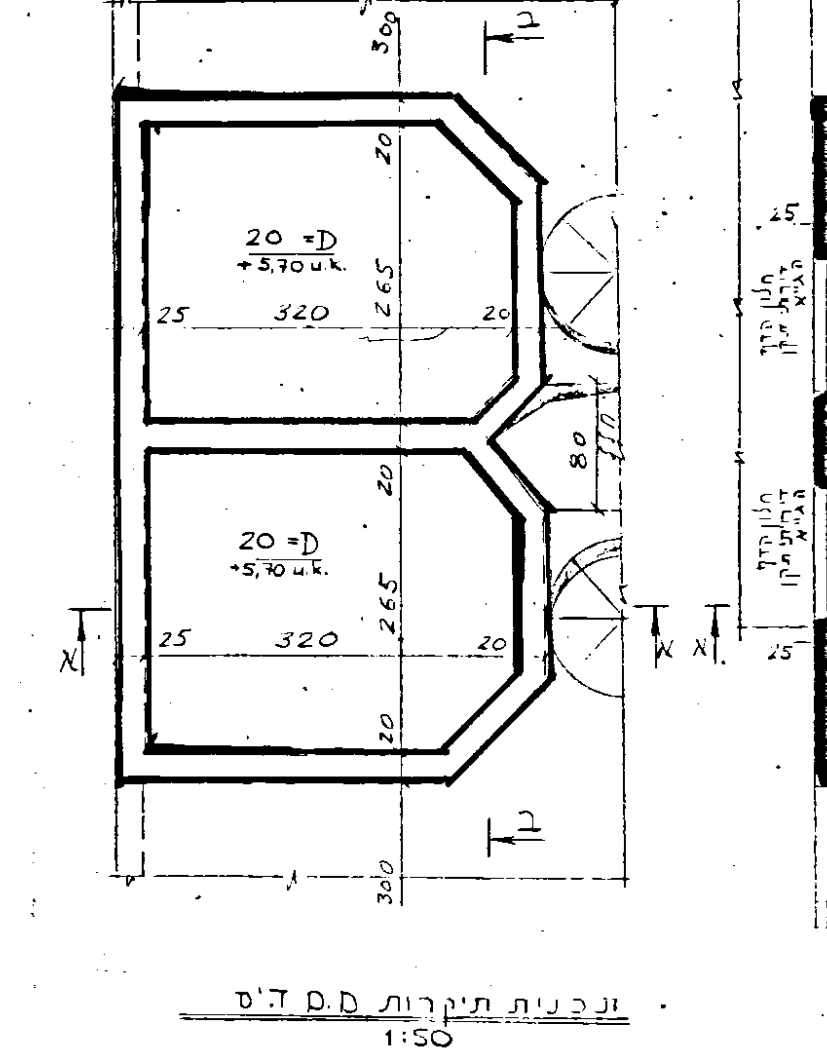
תכנית תקרות ממ"ד 1:50

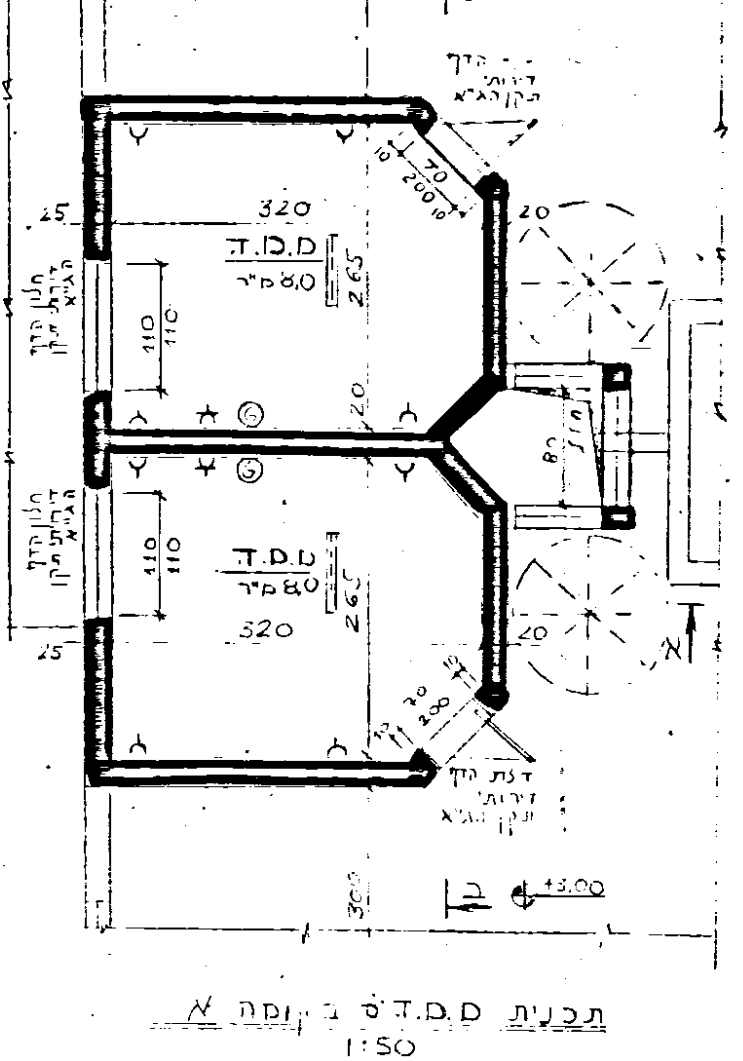
תכנית ממ"ד בקומה א 1:50

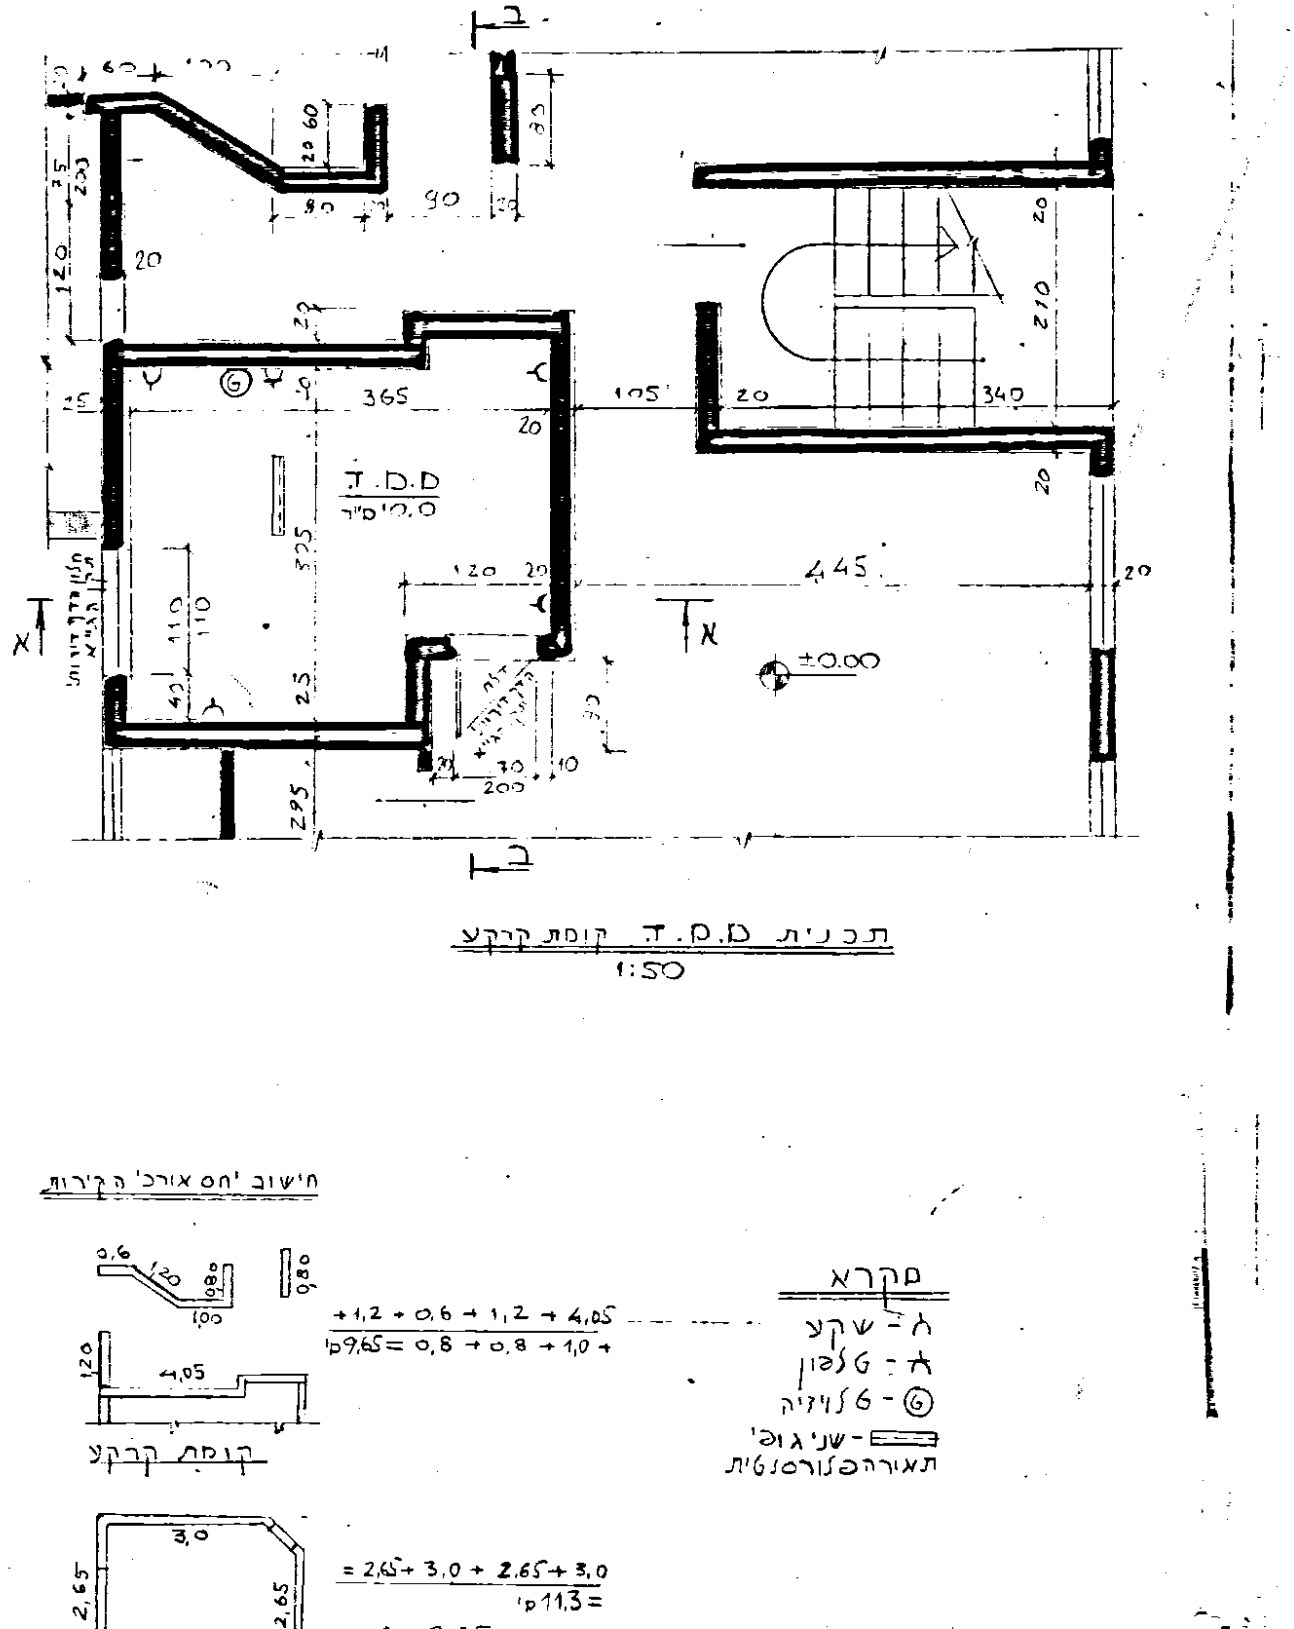
תכנית ממ"ד קומת קרקע 1:50

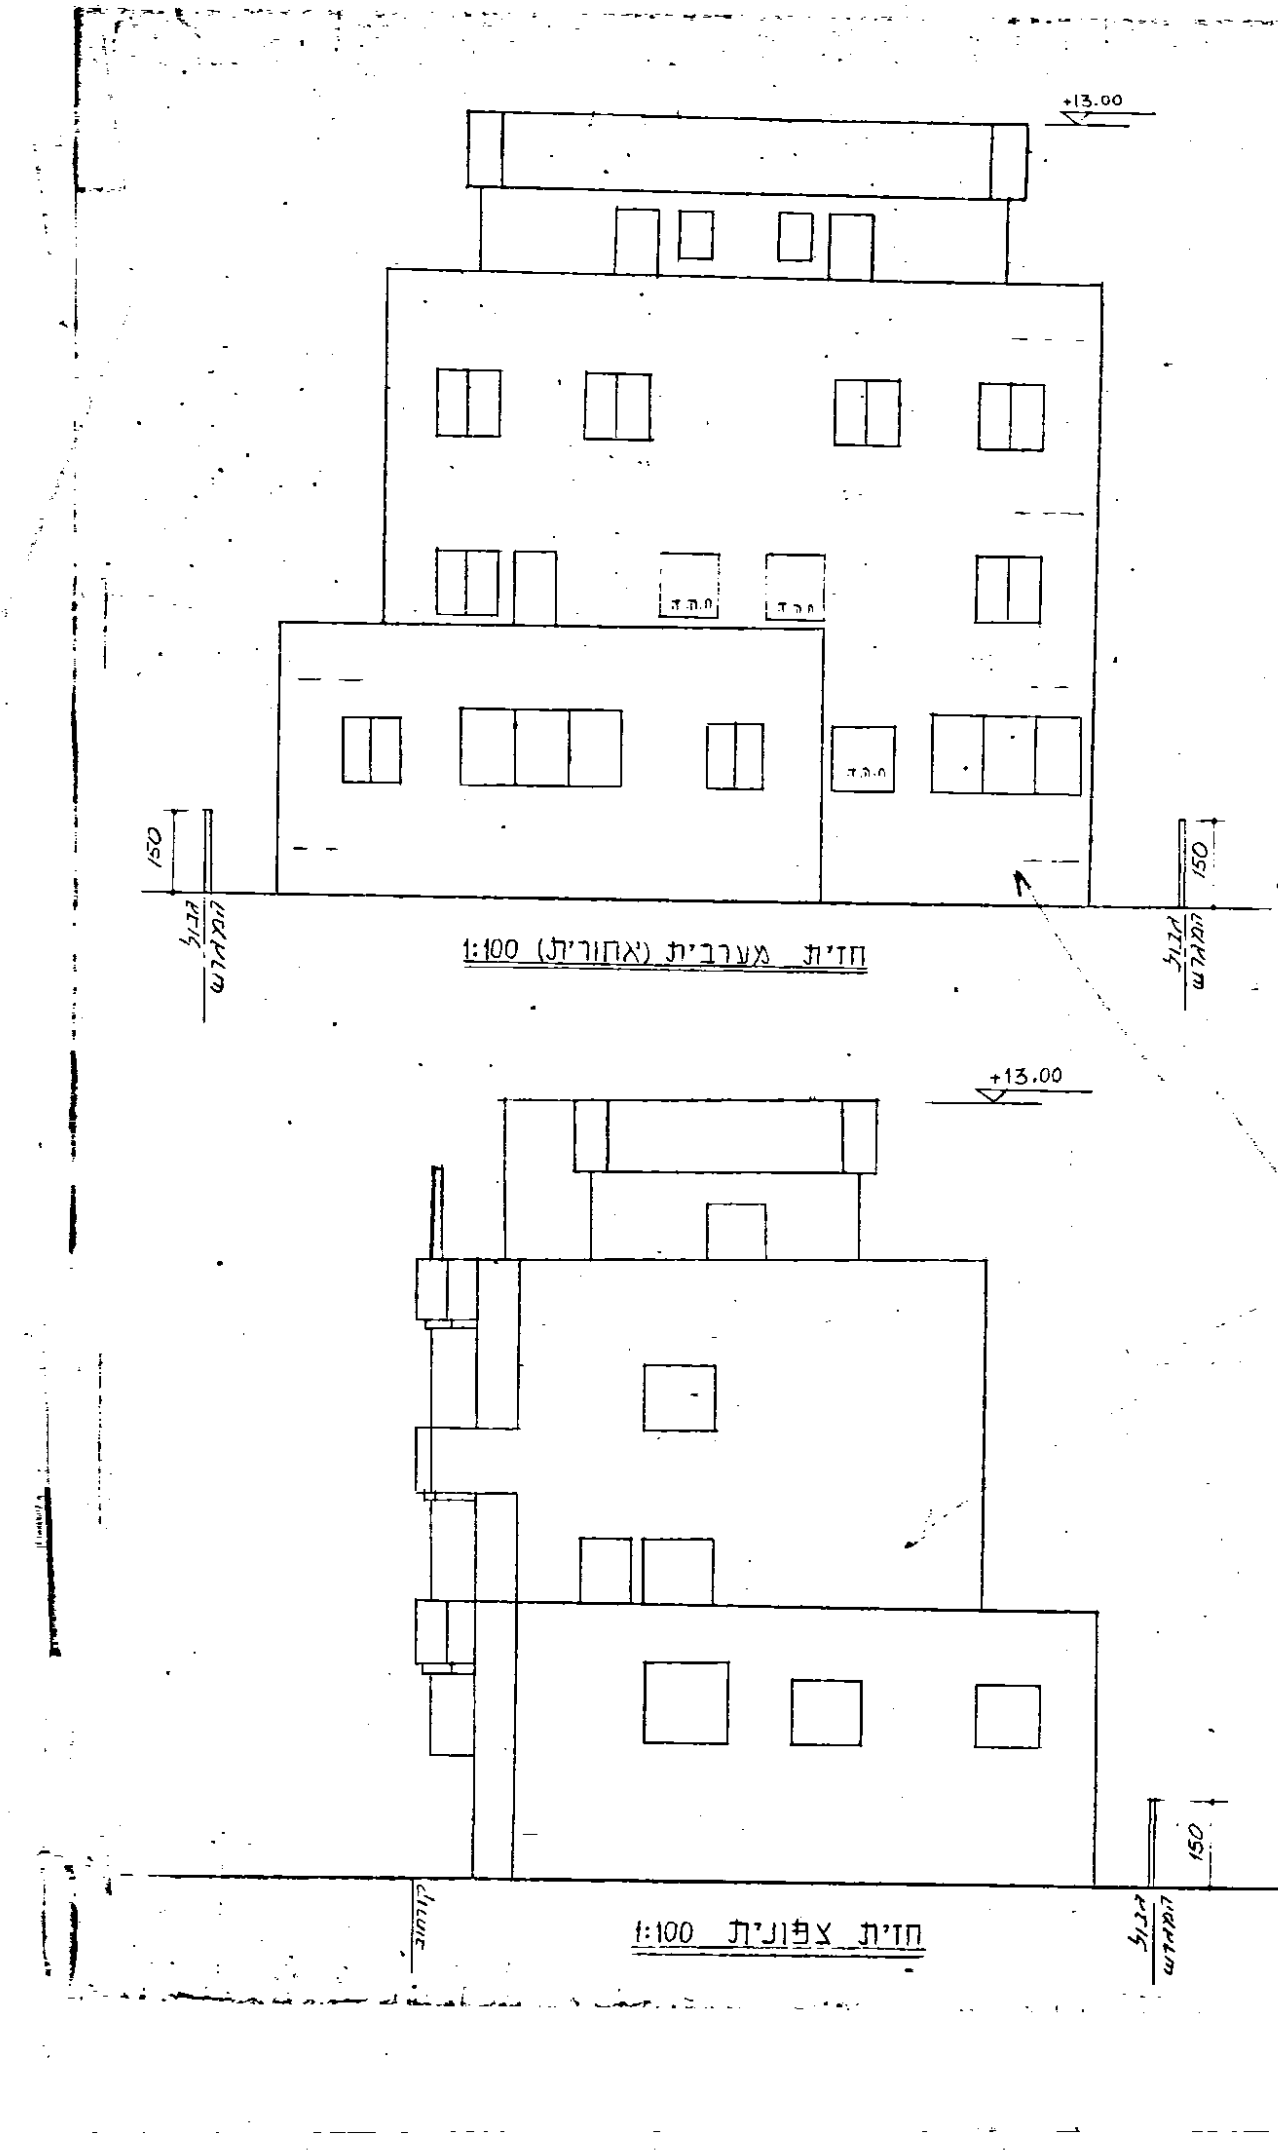
חזית מערבית (אחורית) 1:100

חזית צפונית 1:100

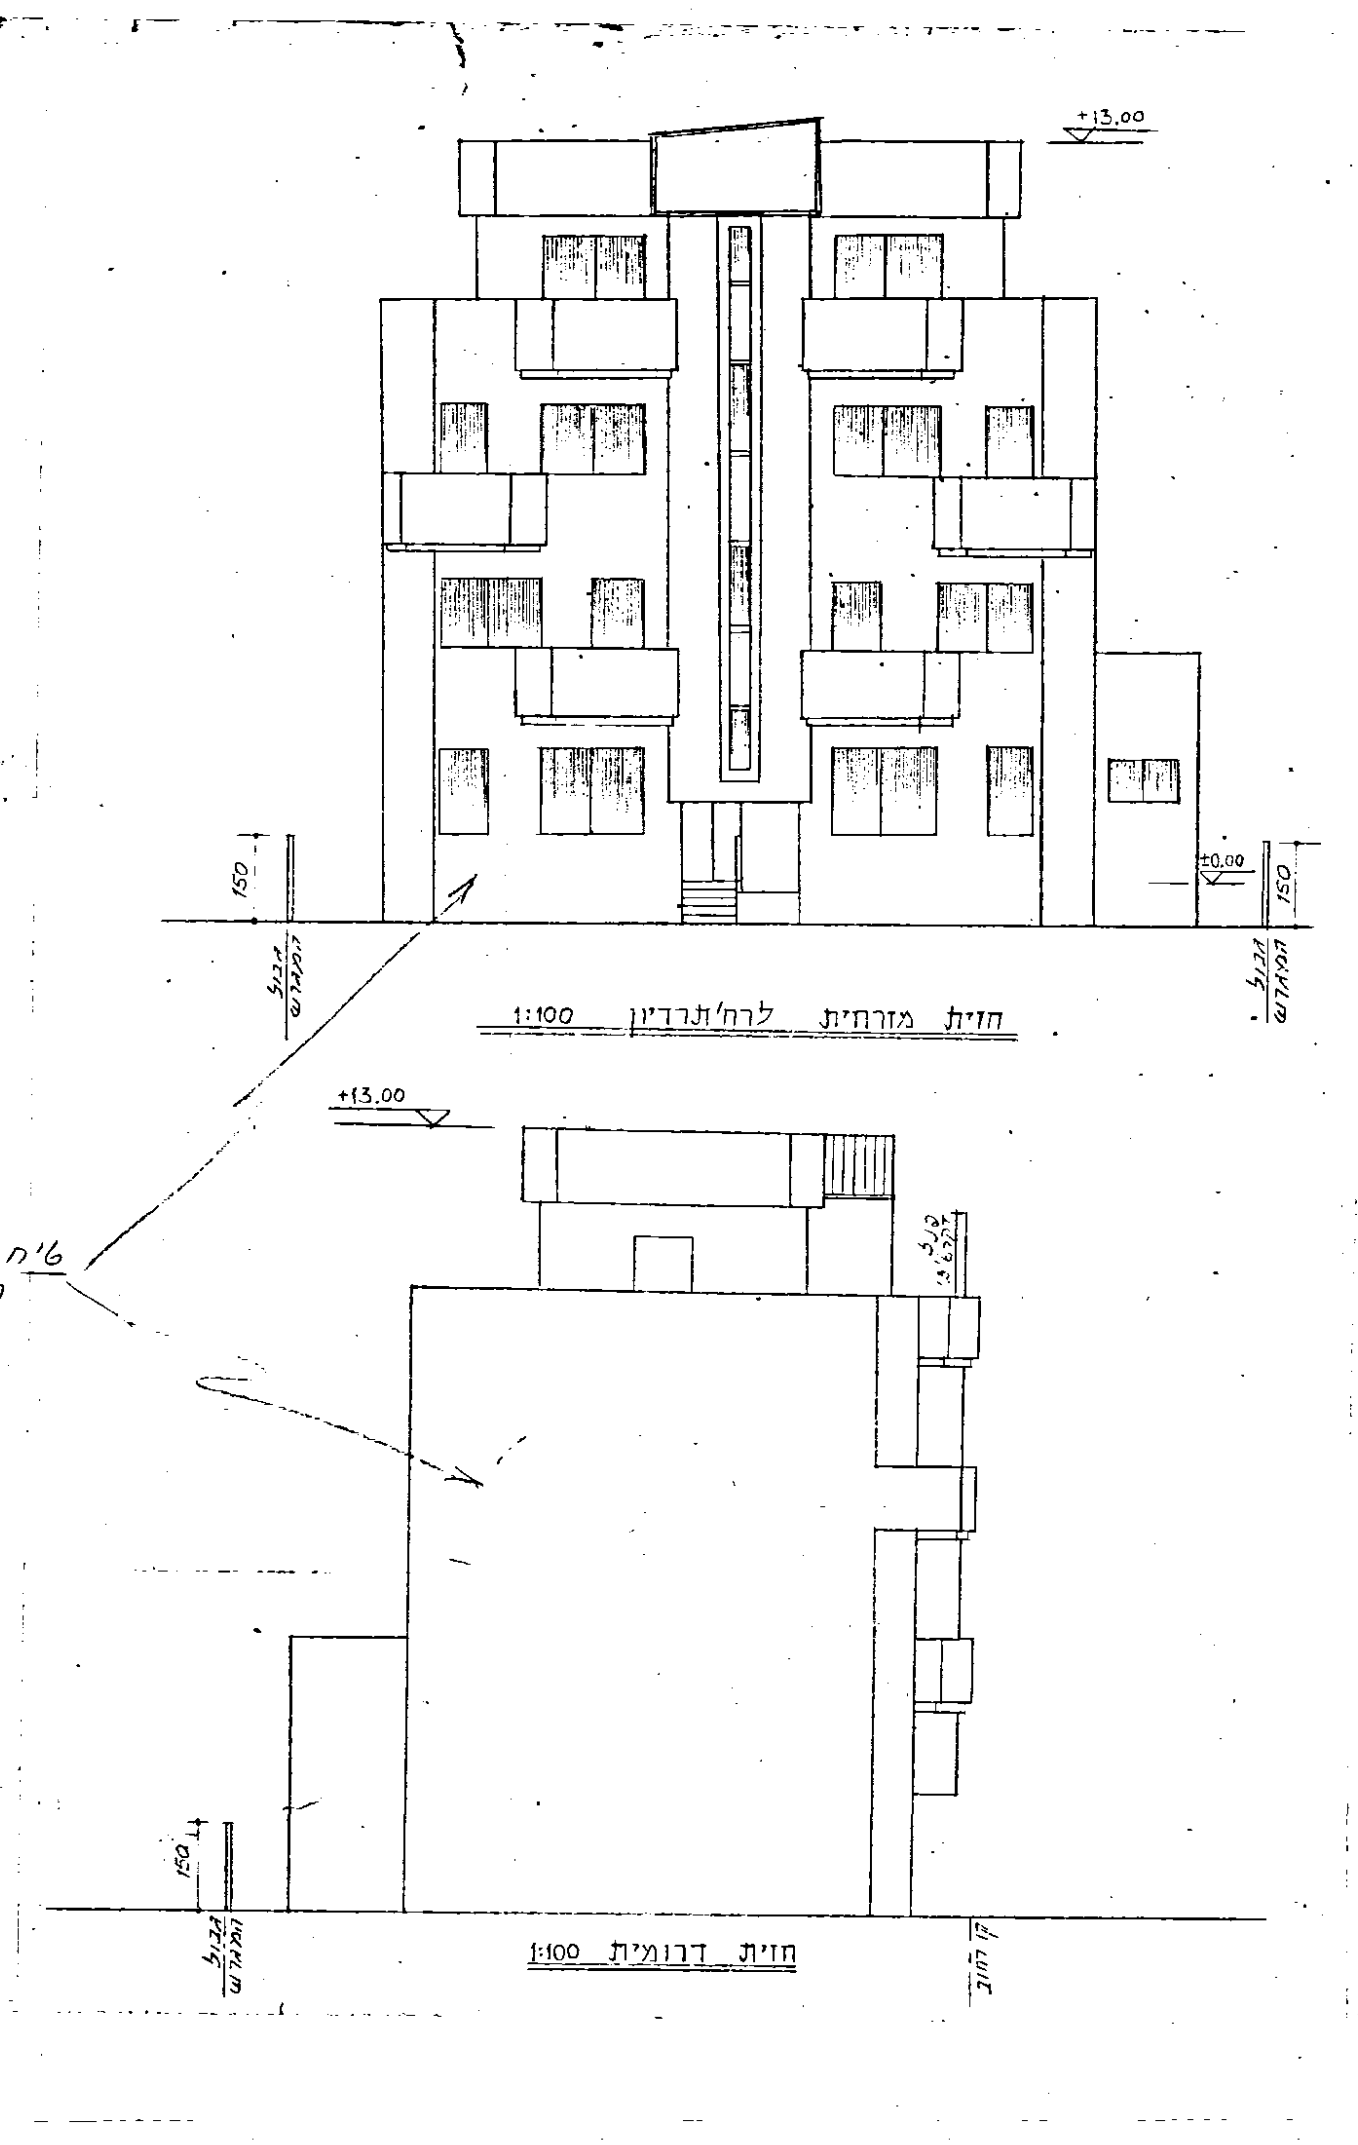
חזית מזרחית 1:100

חזית דרומית 1:100

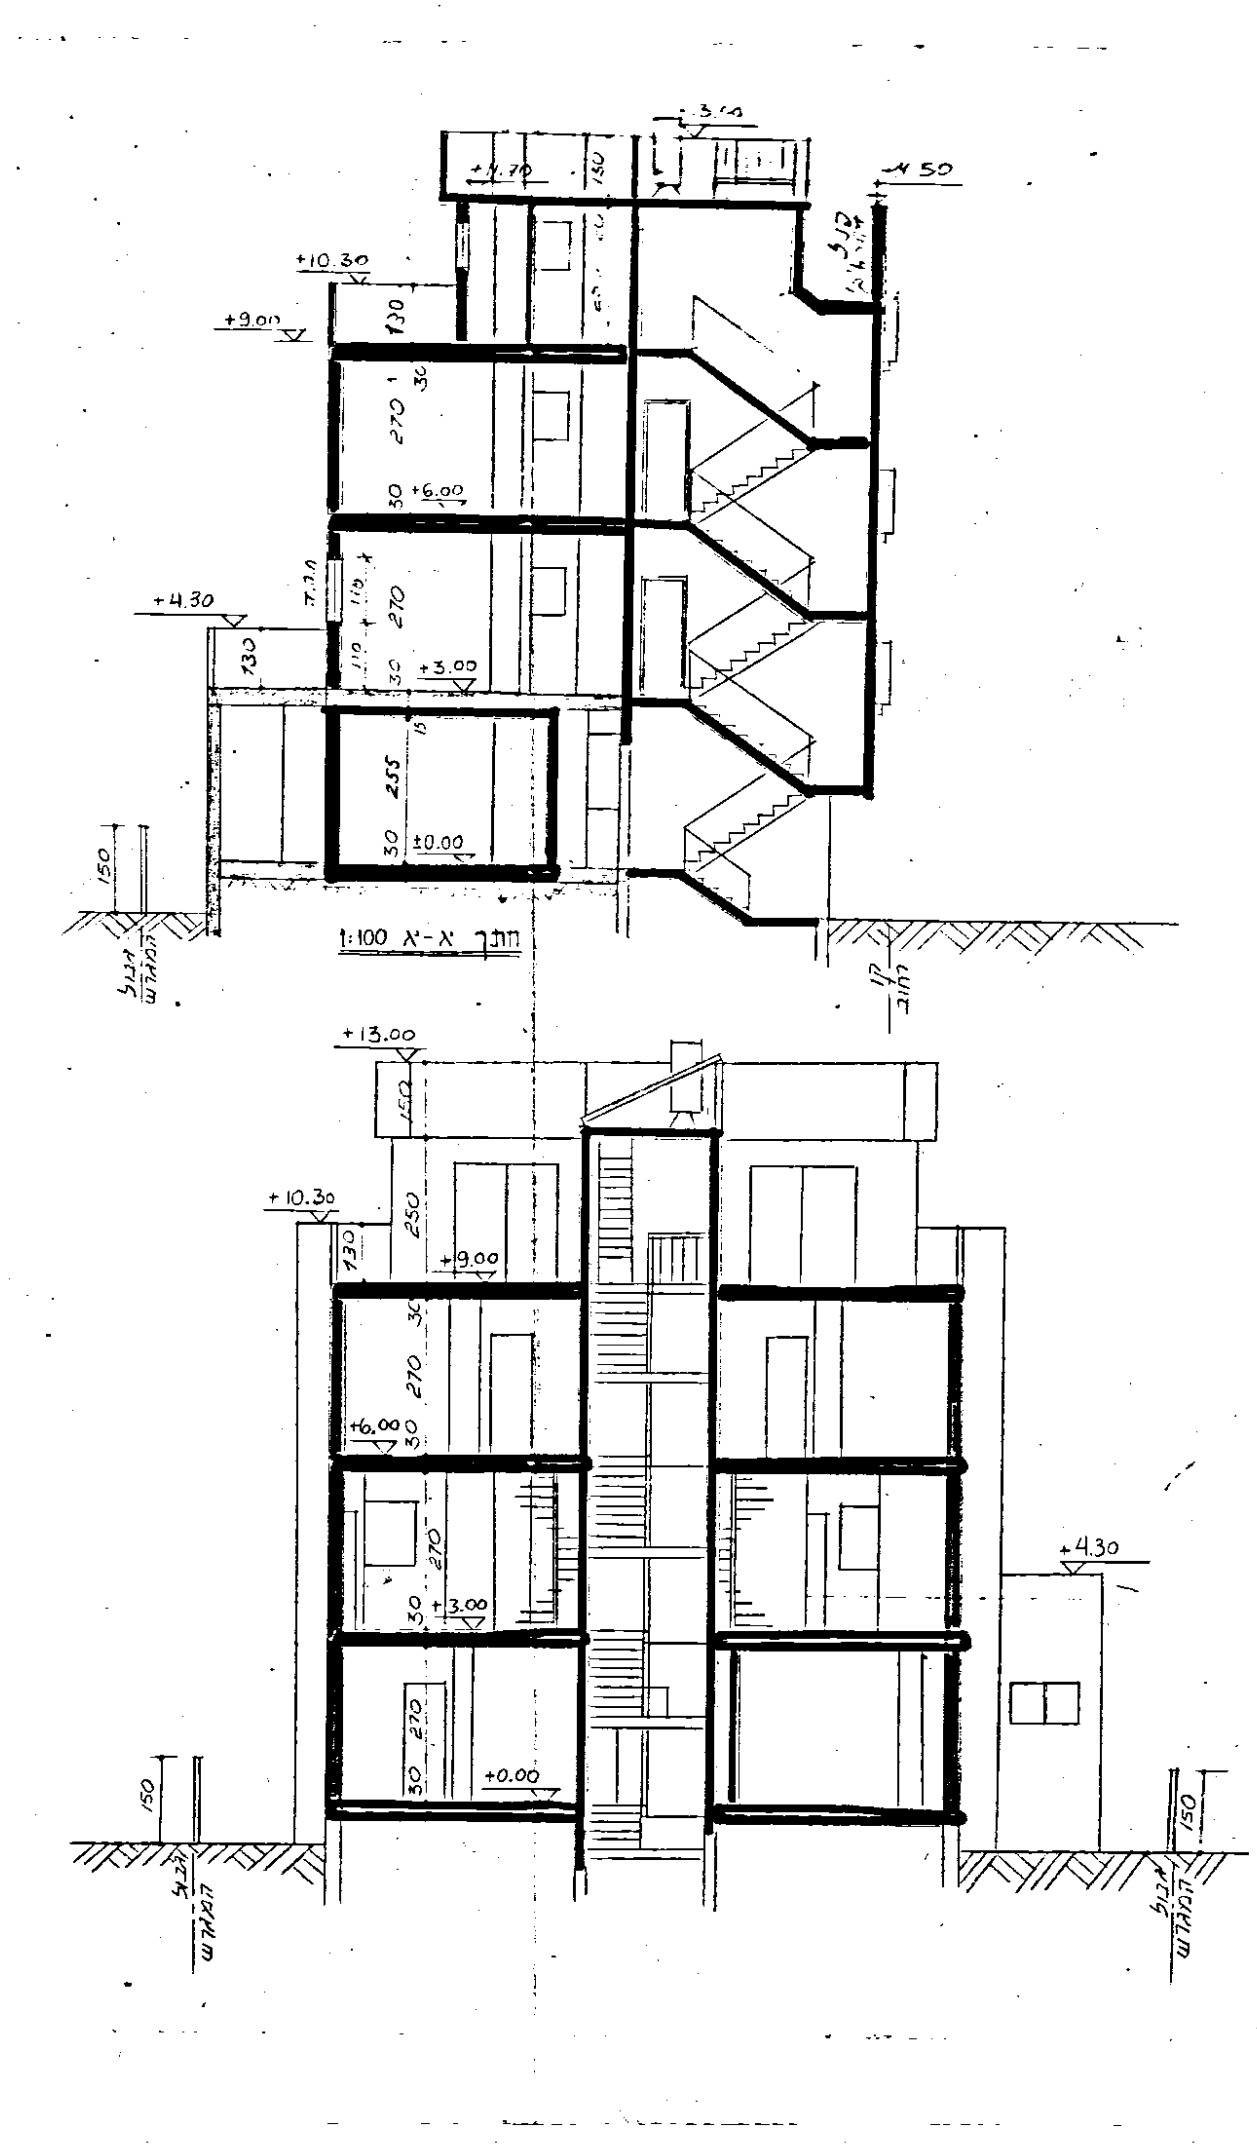
חתך א-א 1:100

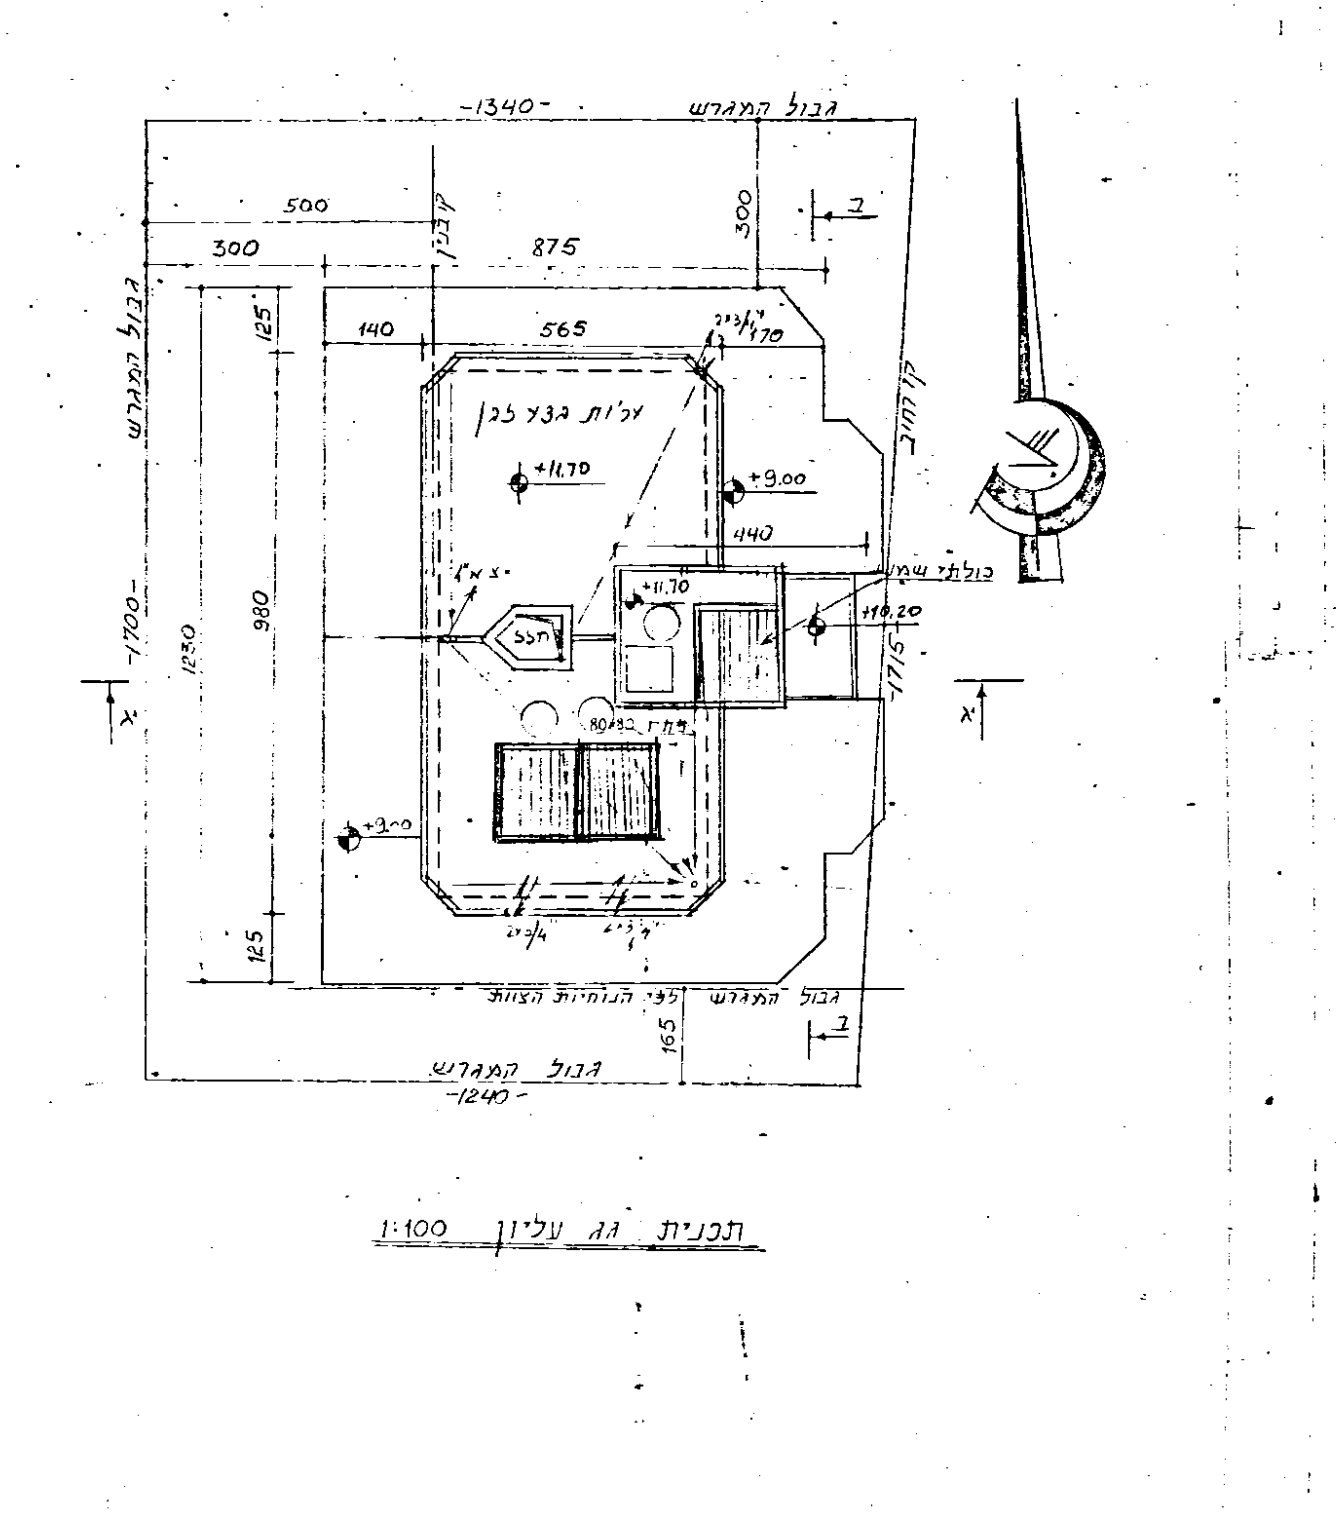
תכנית גג עליון 1:100

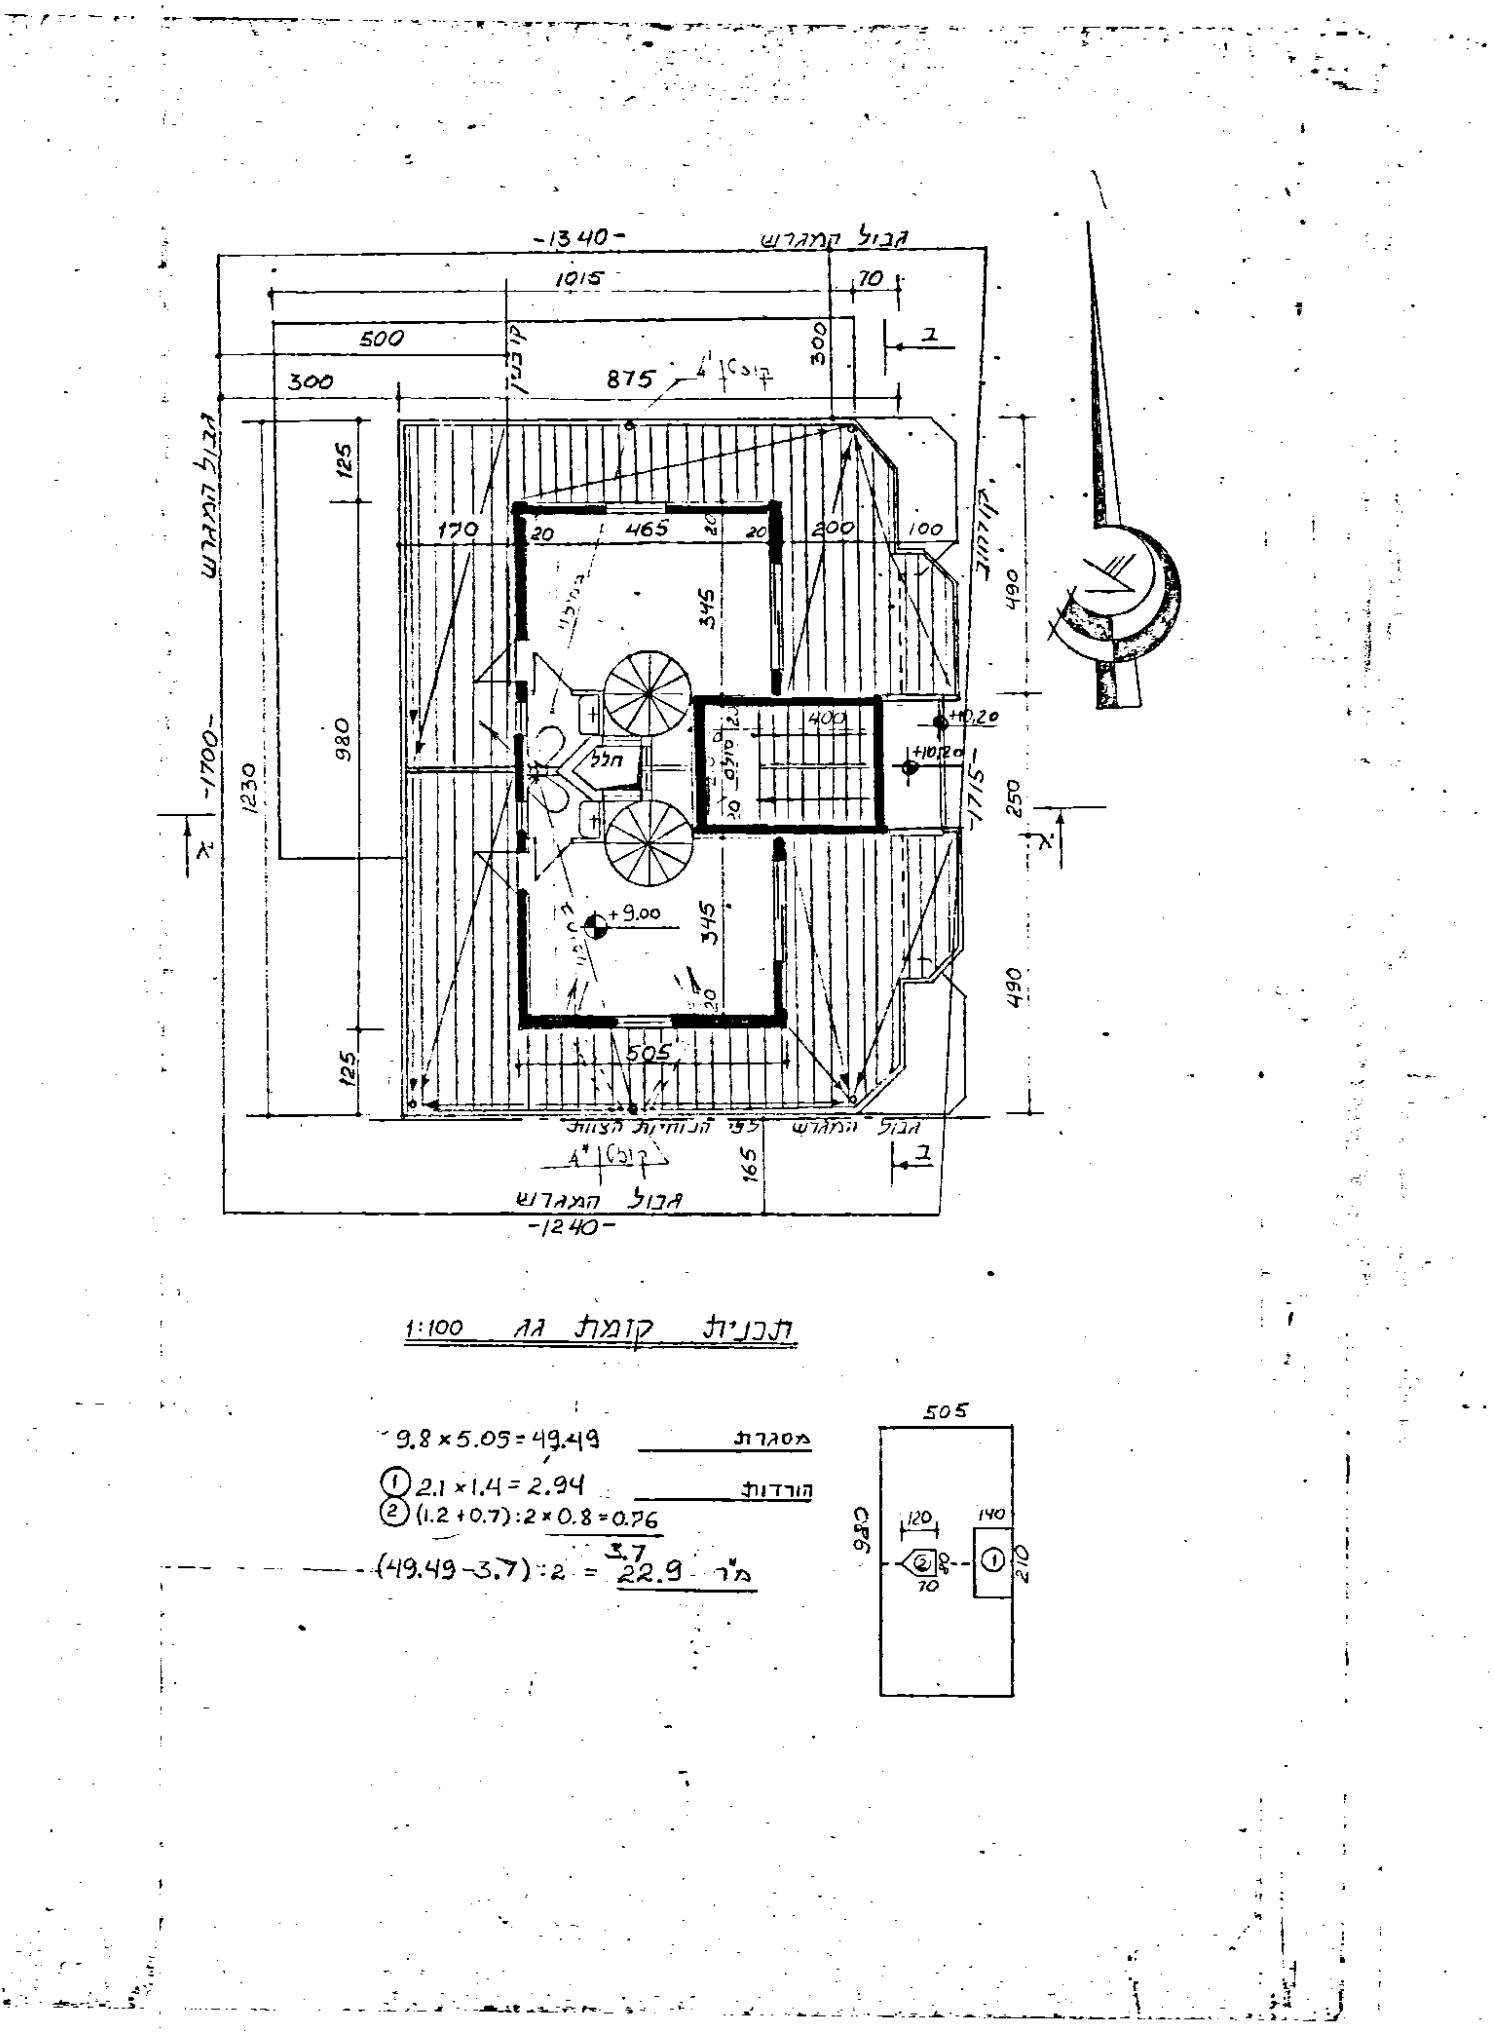
תכנית קומת גג 1:100

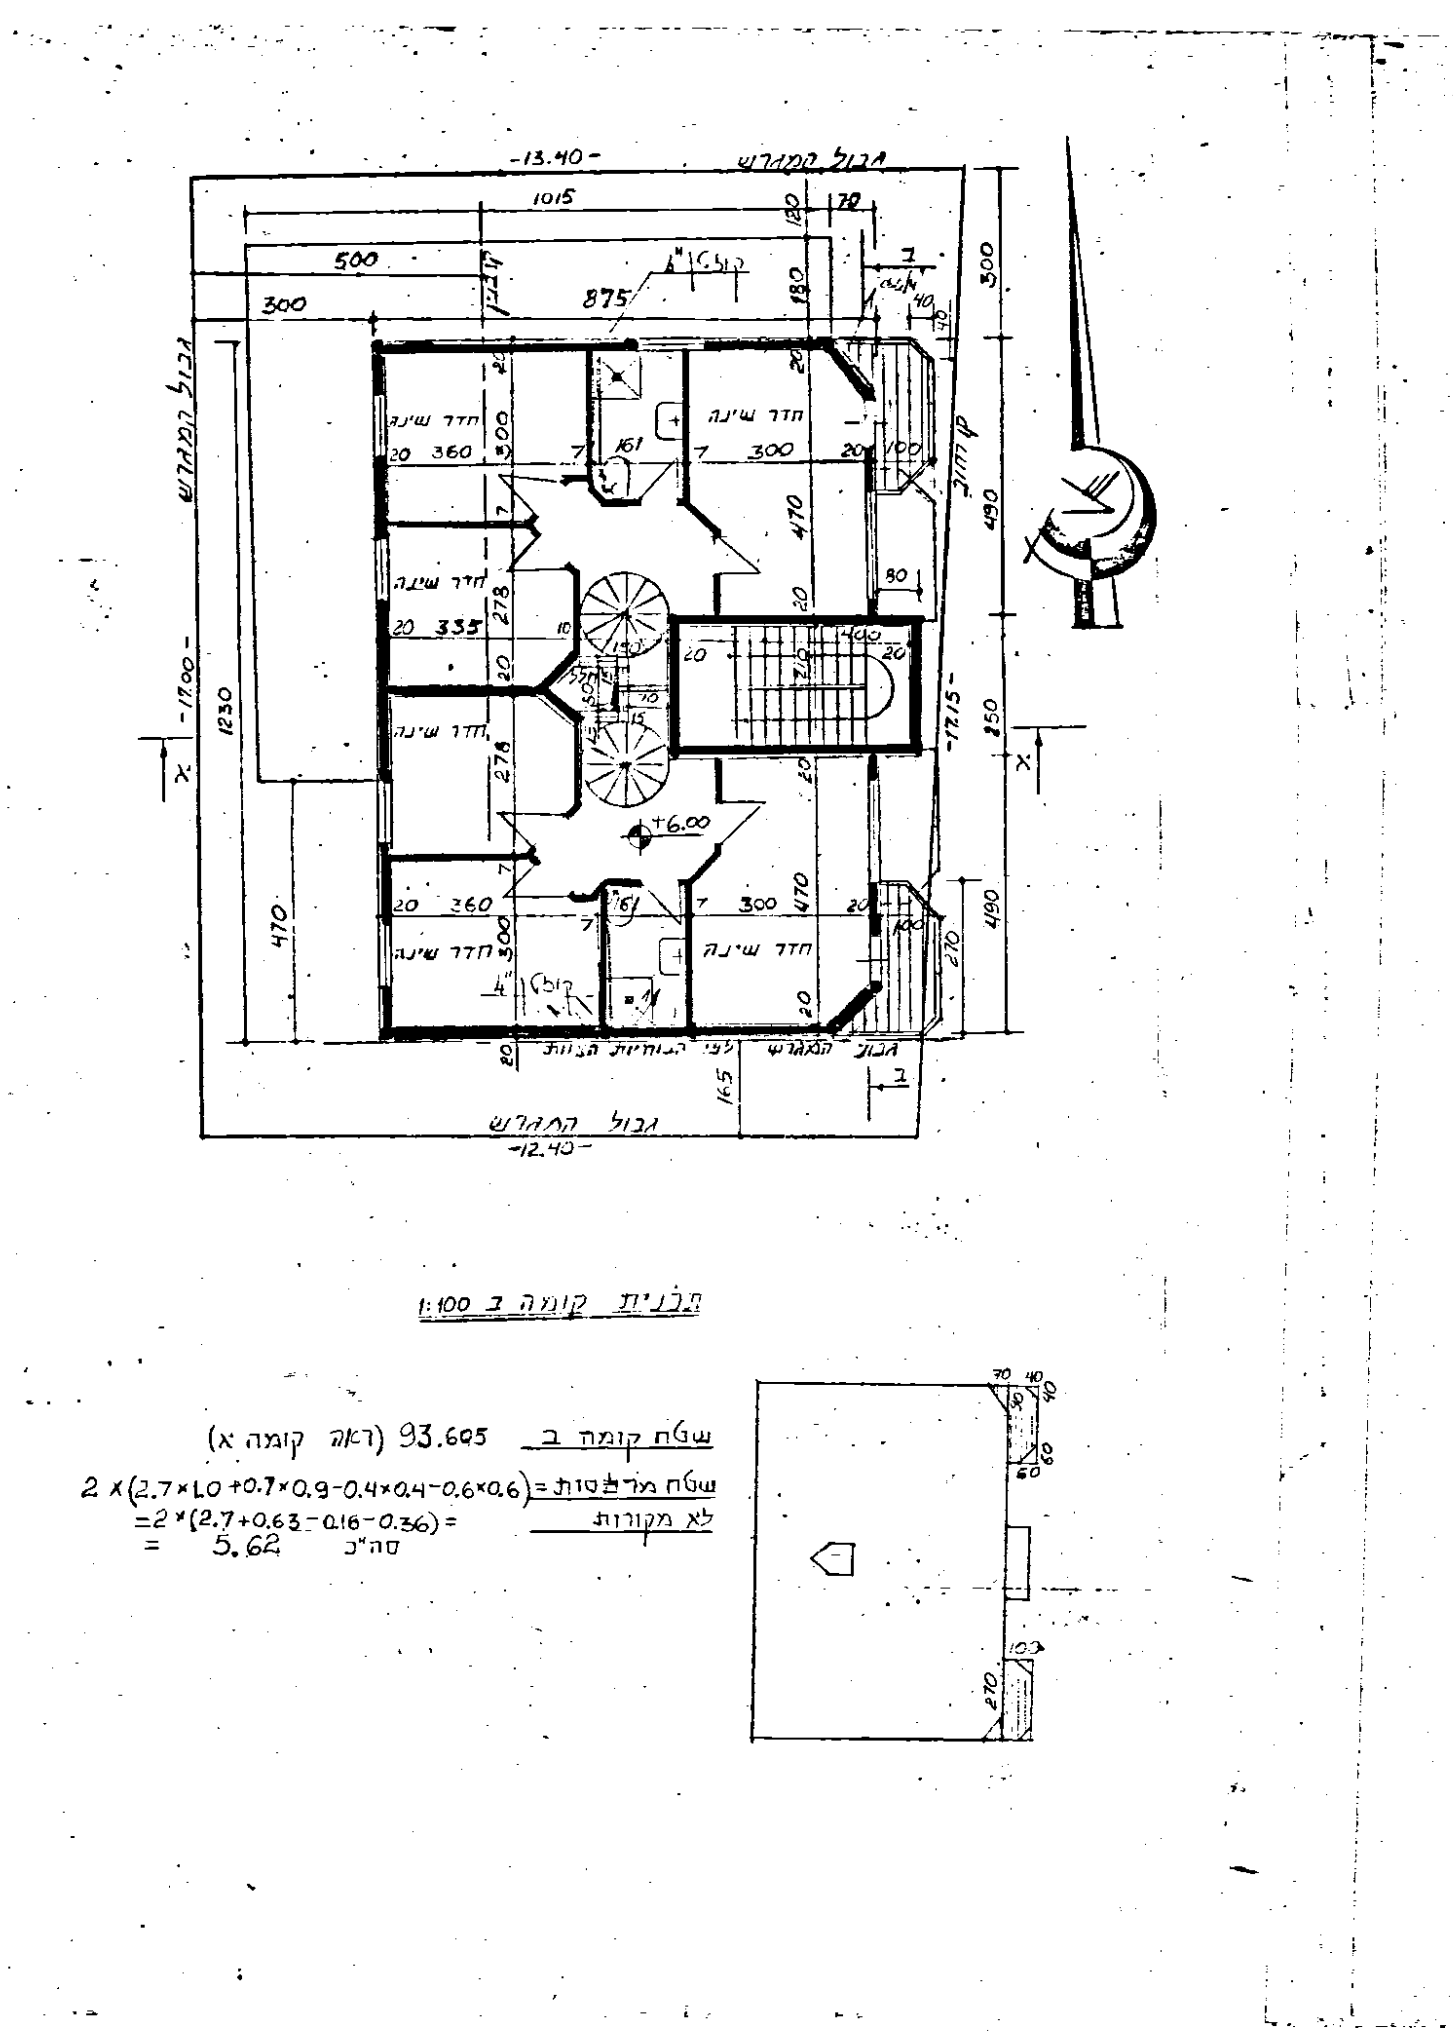
תכנית קומה ב 1:100

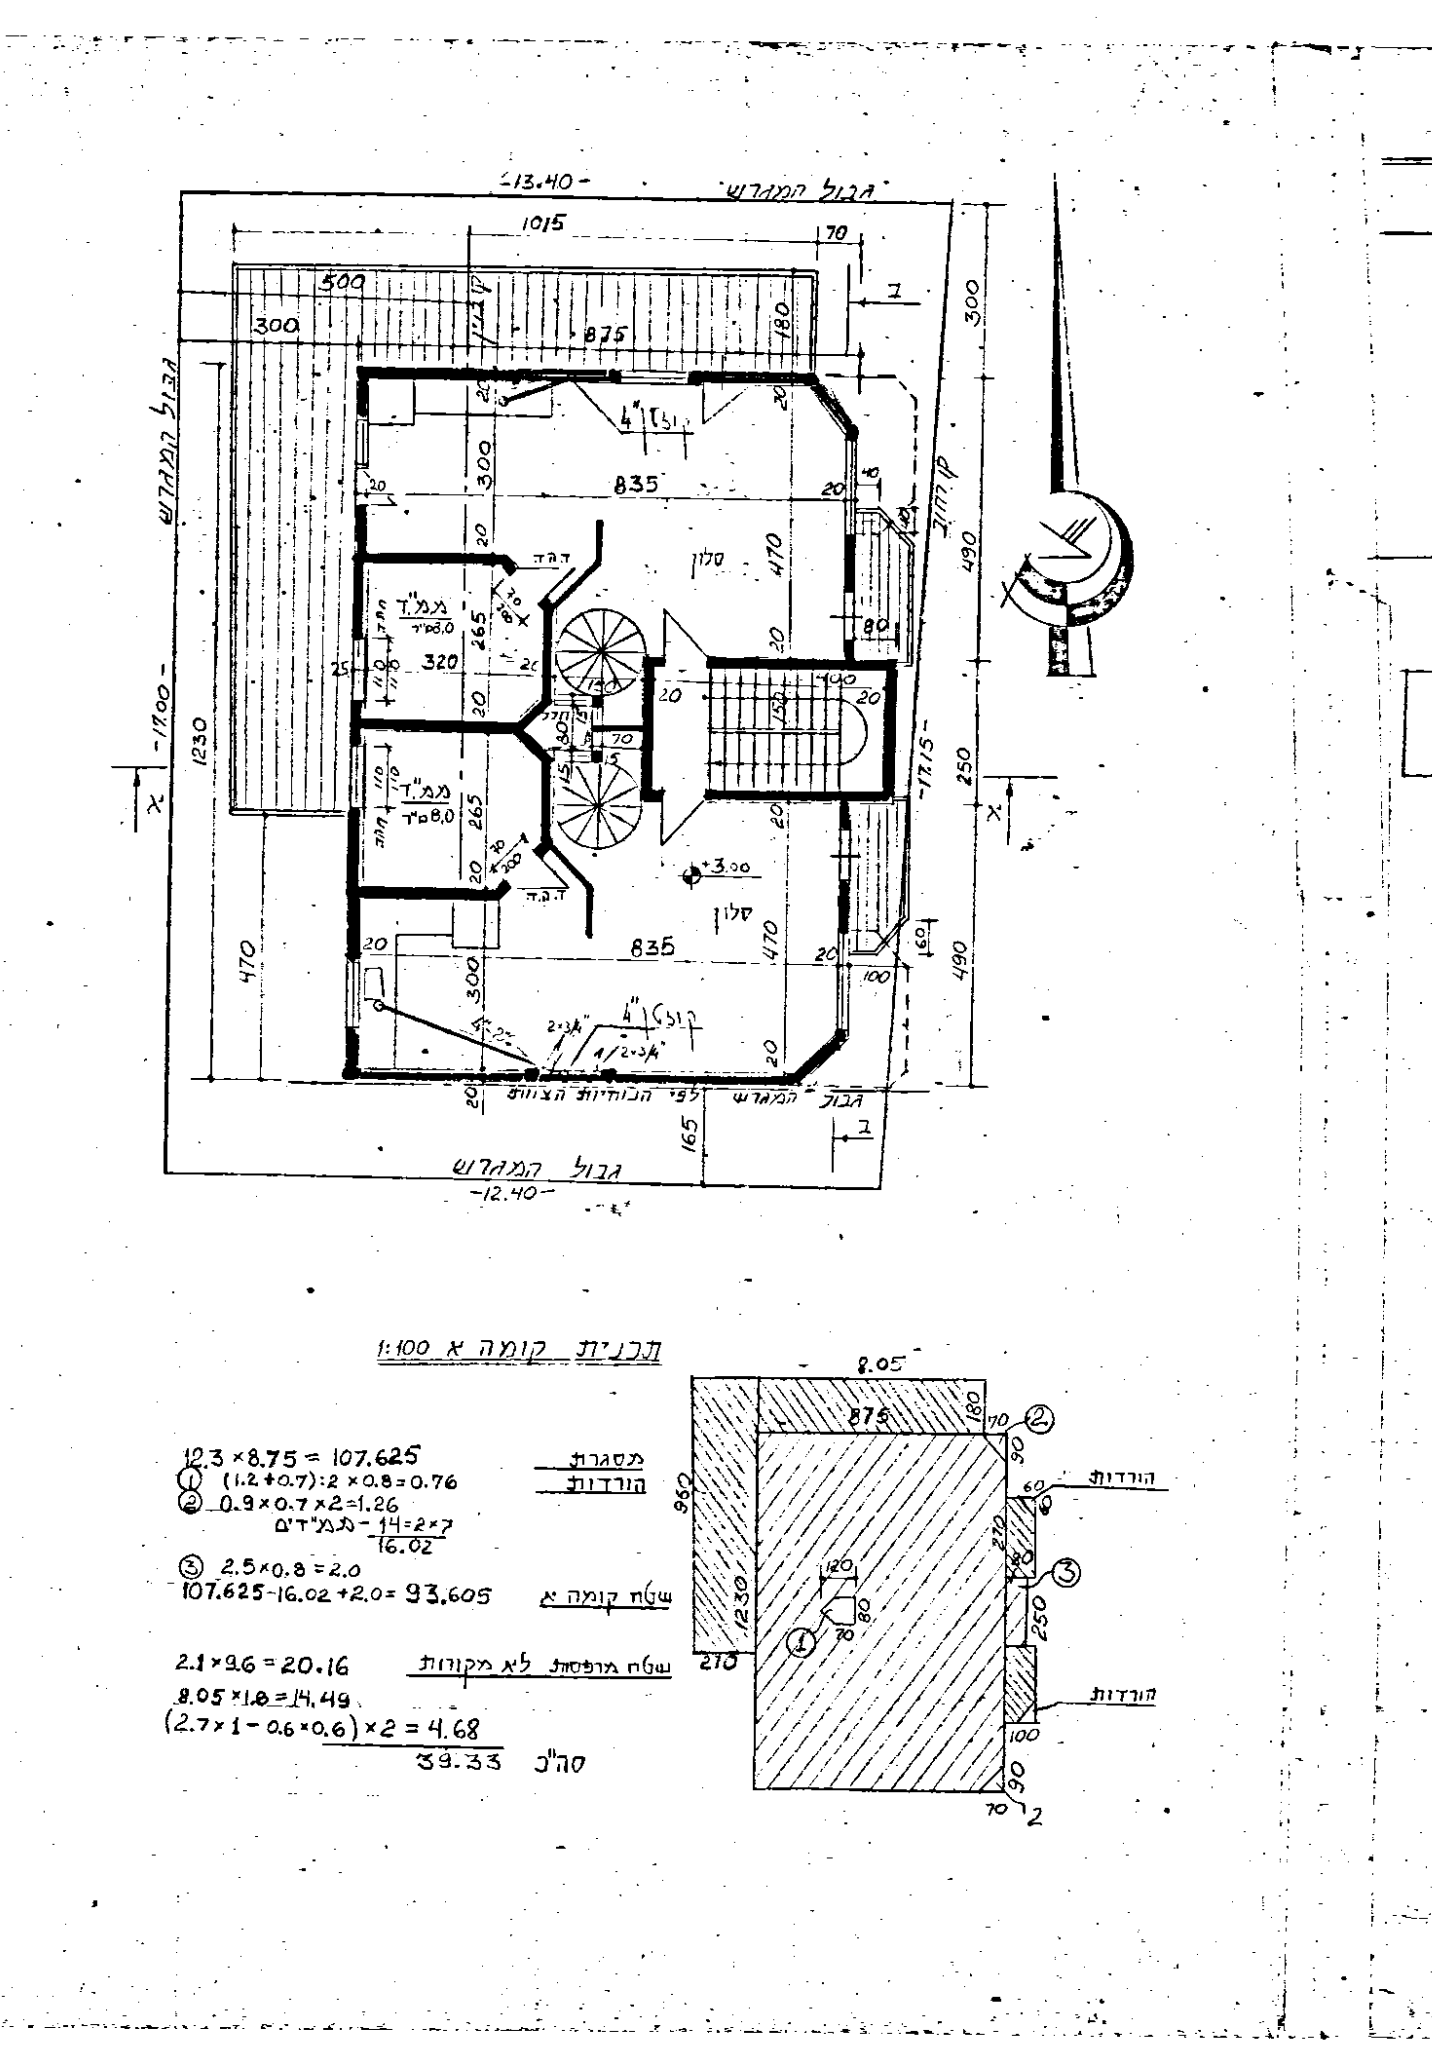
תכנית קומה א 1:100

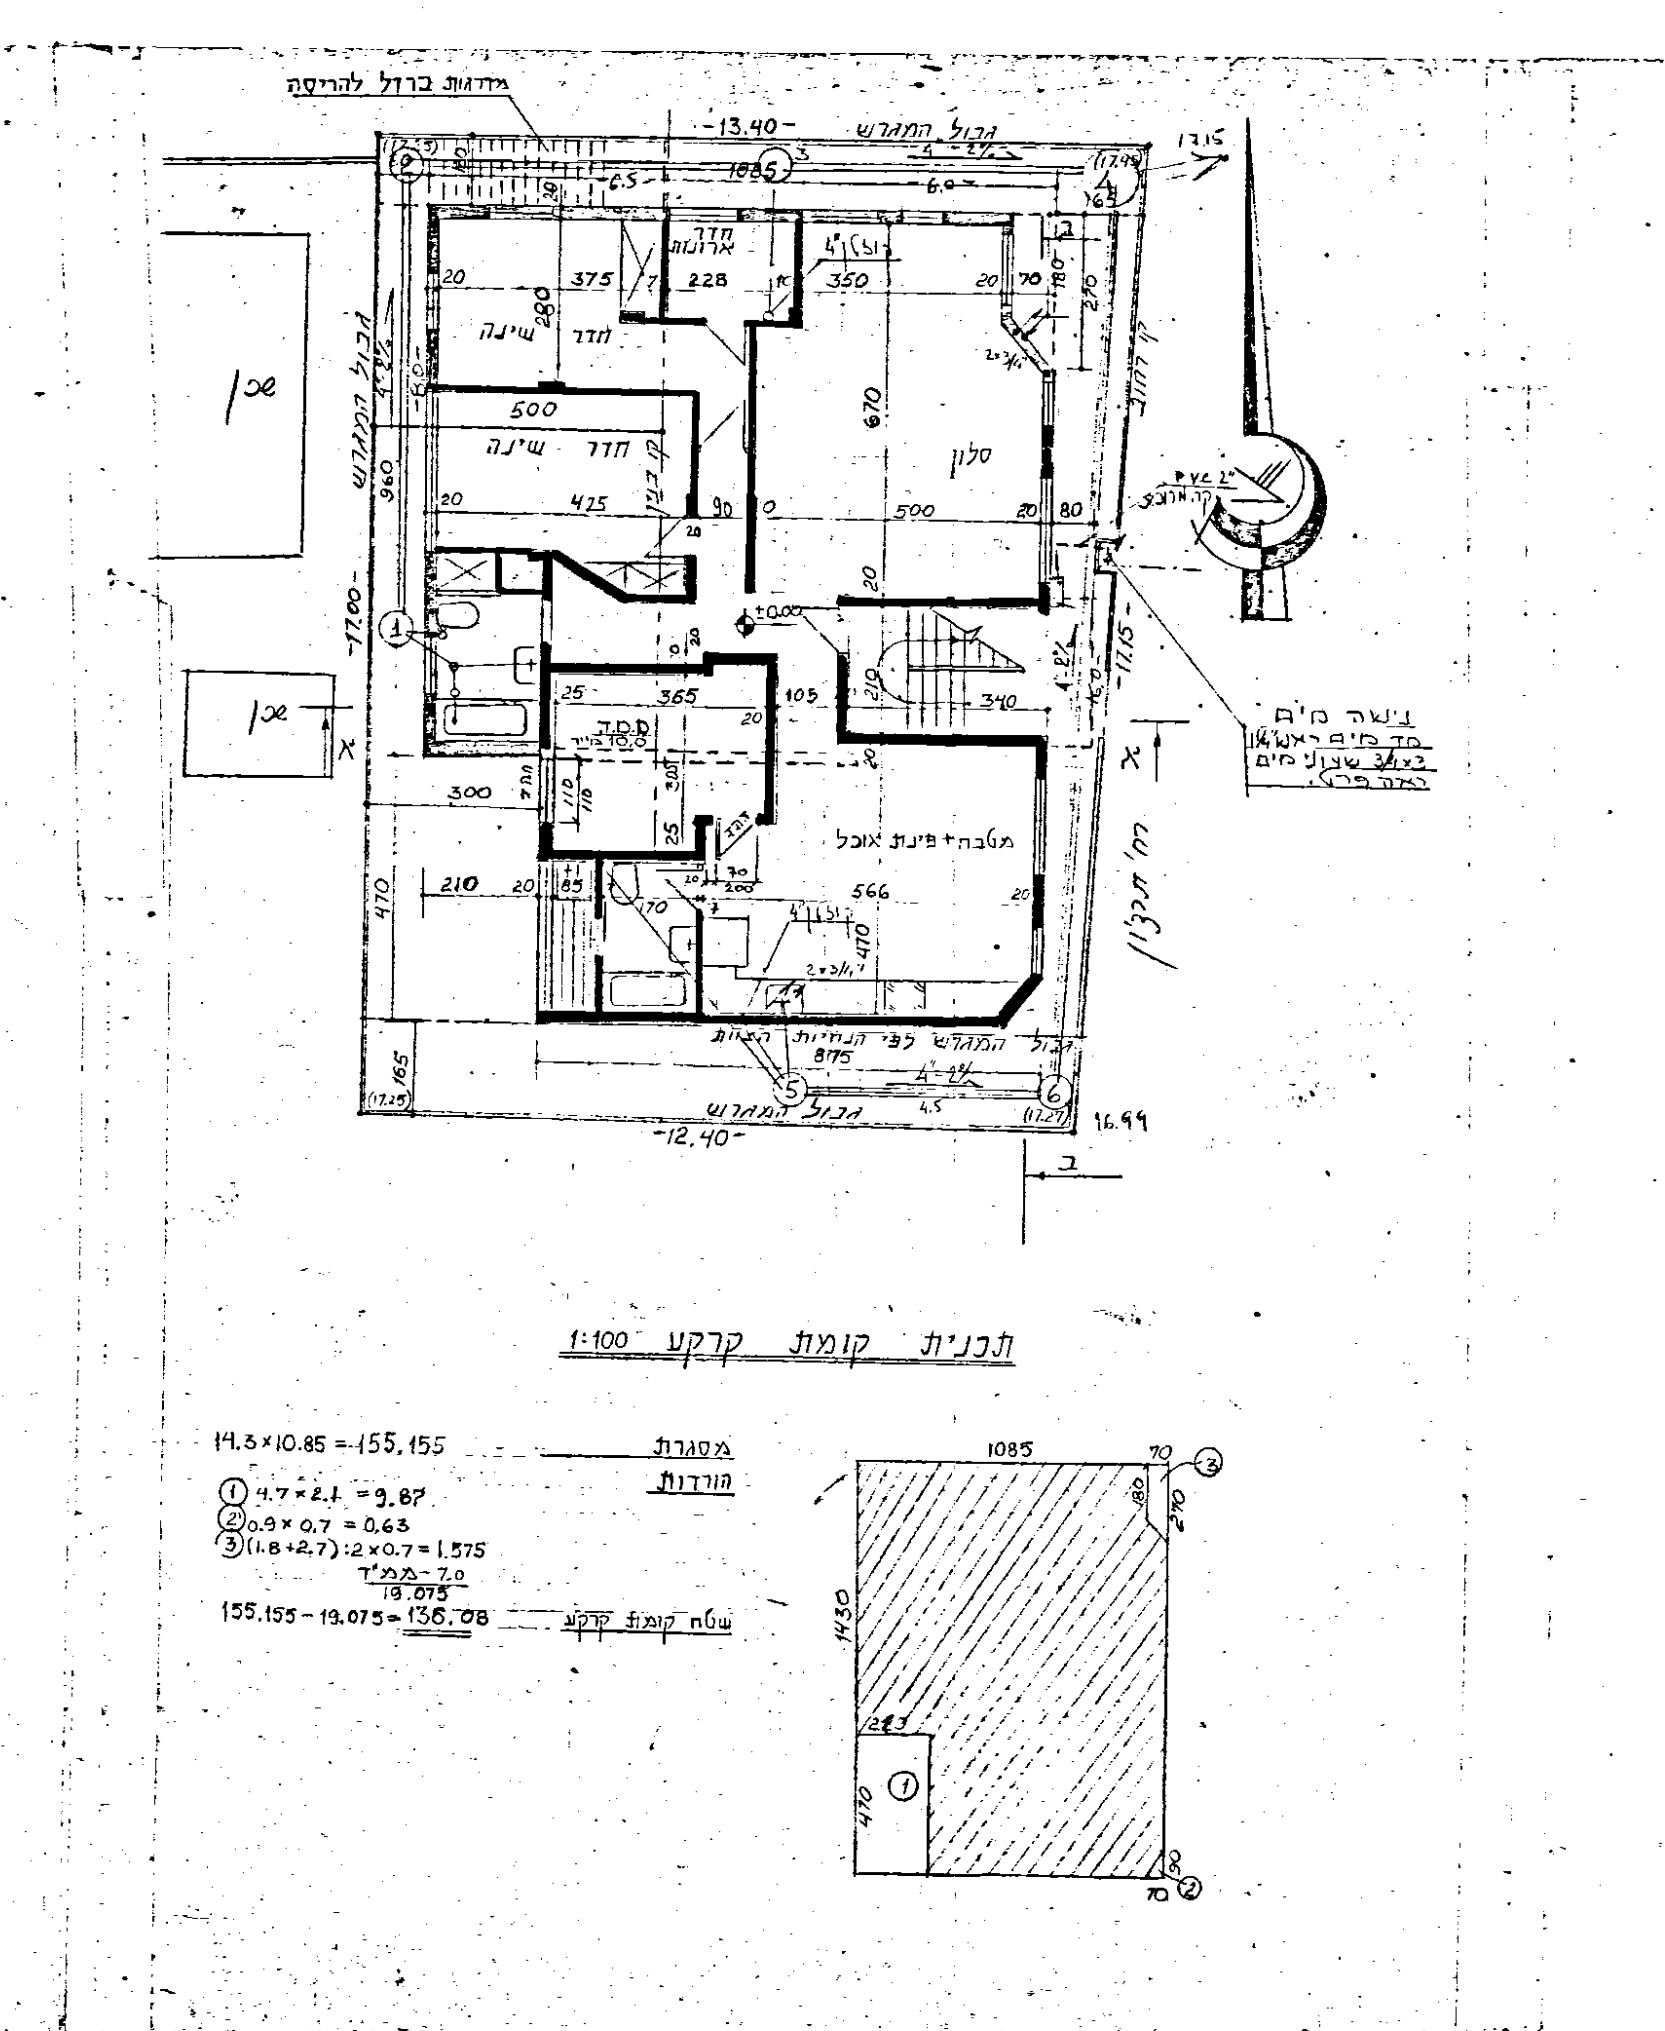
תכנית קומת קרקע 1:100

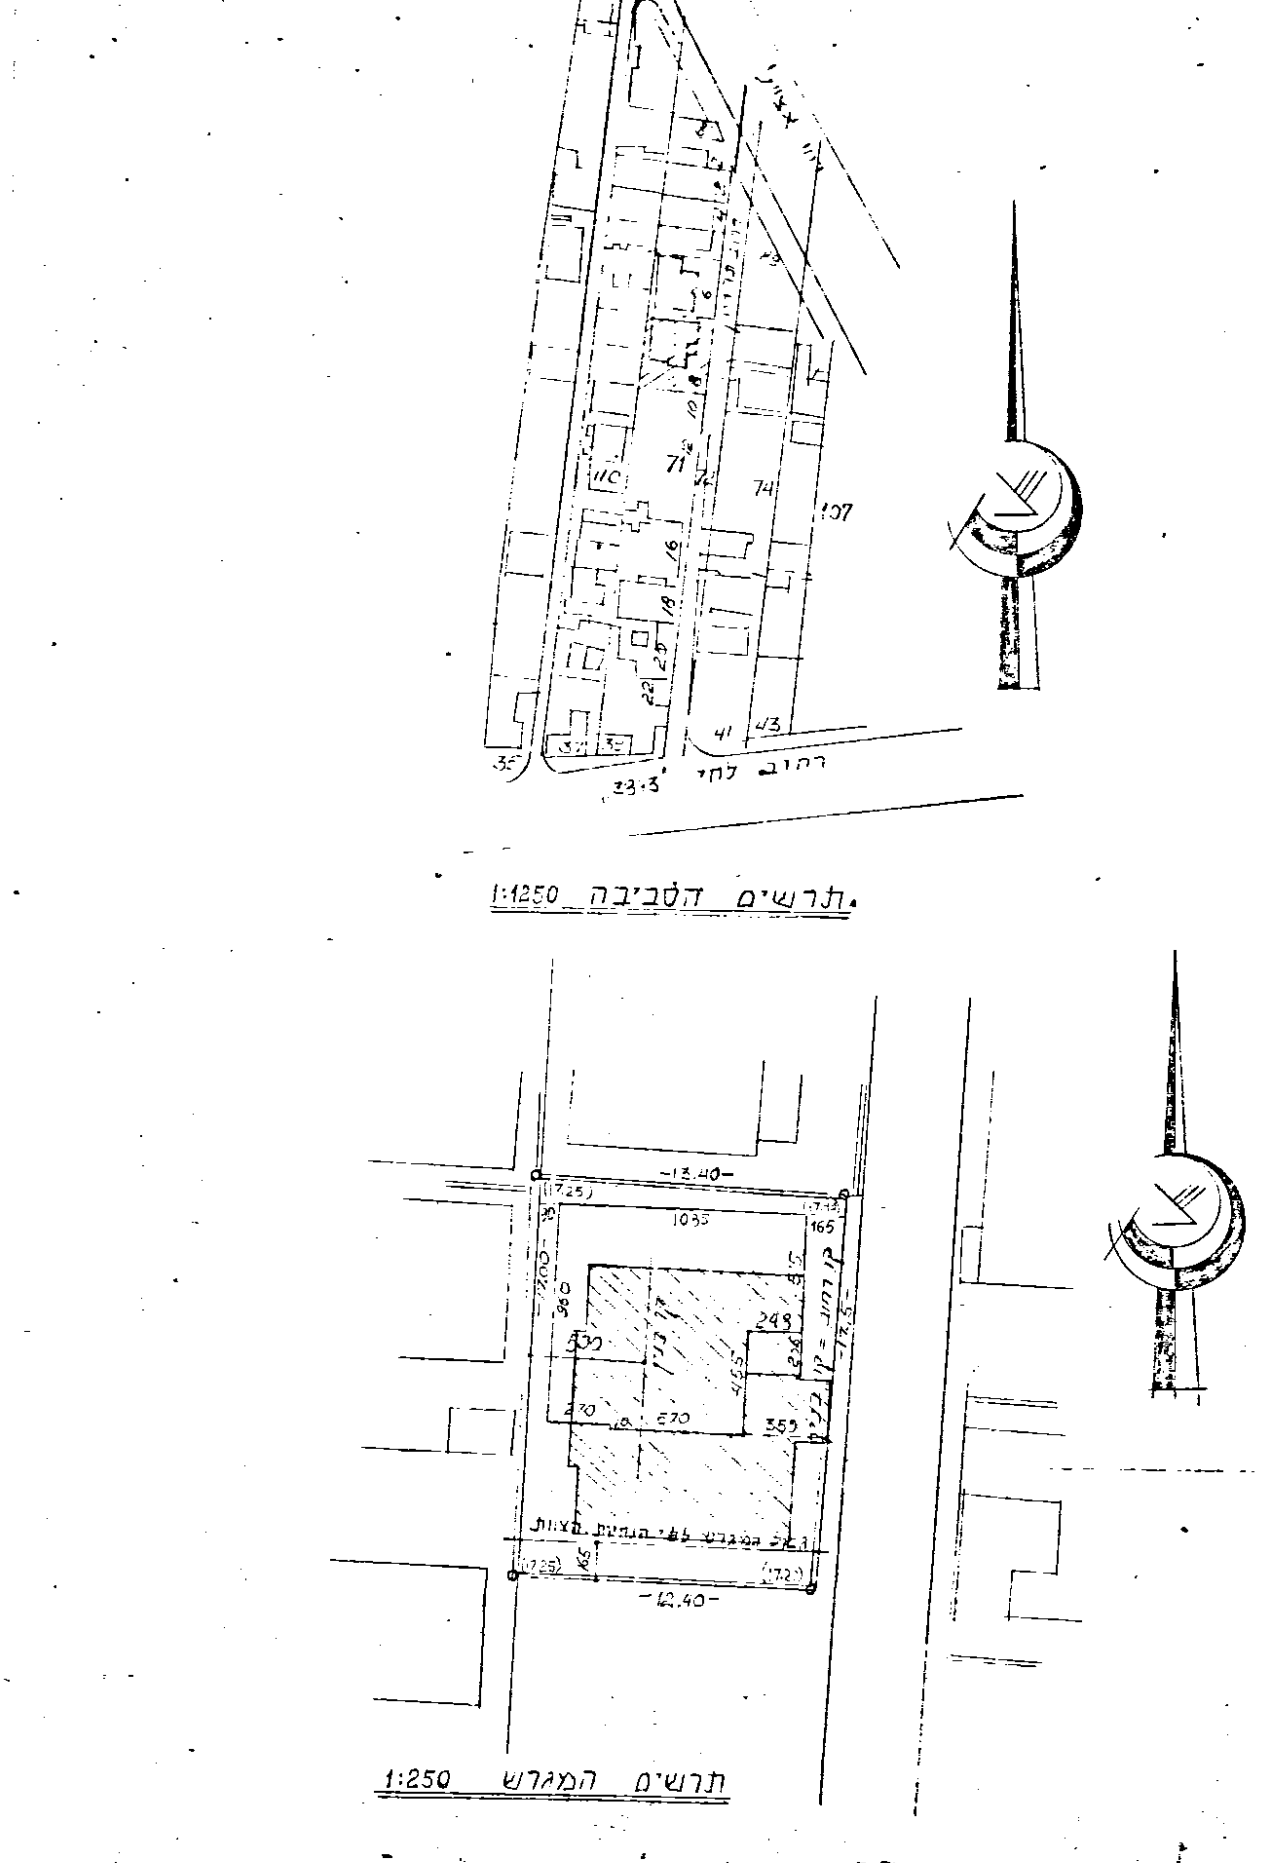
תרשים הסביבה 1:250

תרשים המגרש 1:250

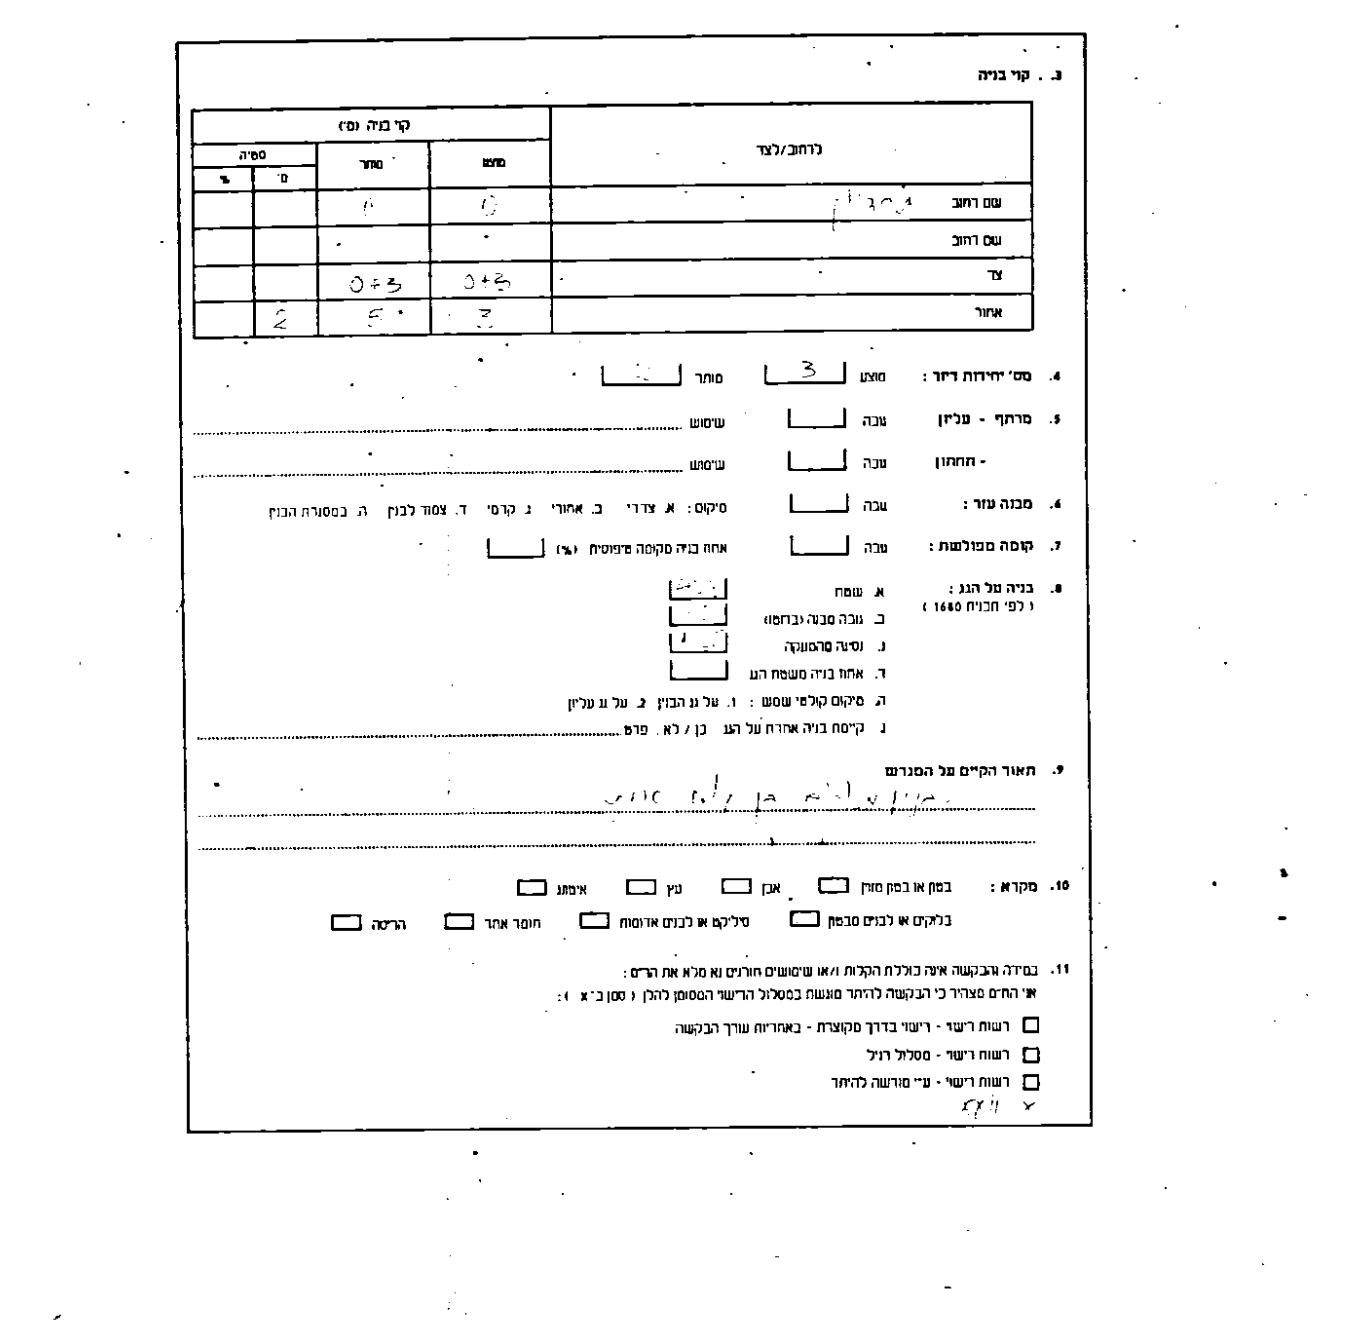

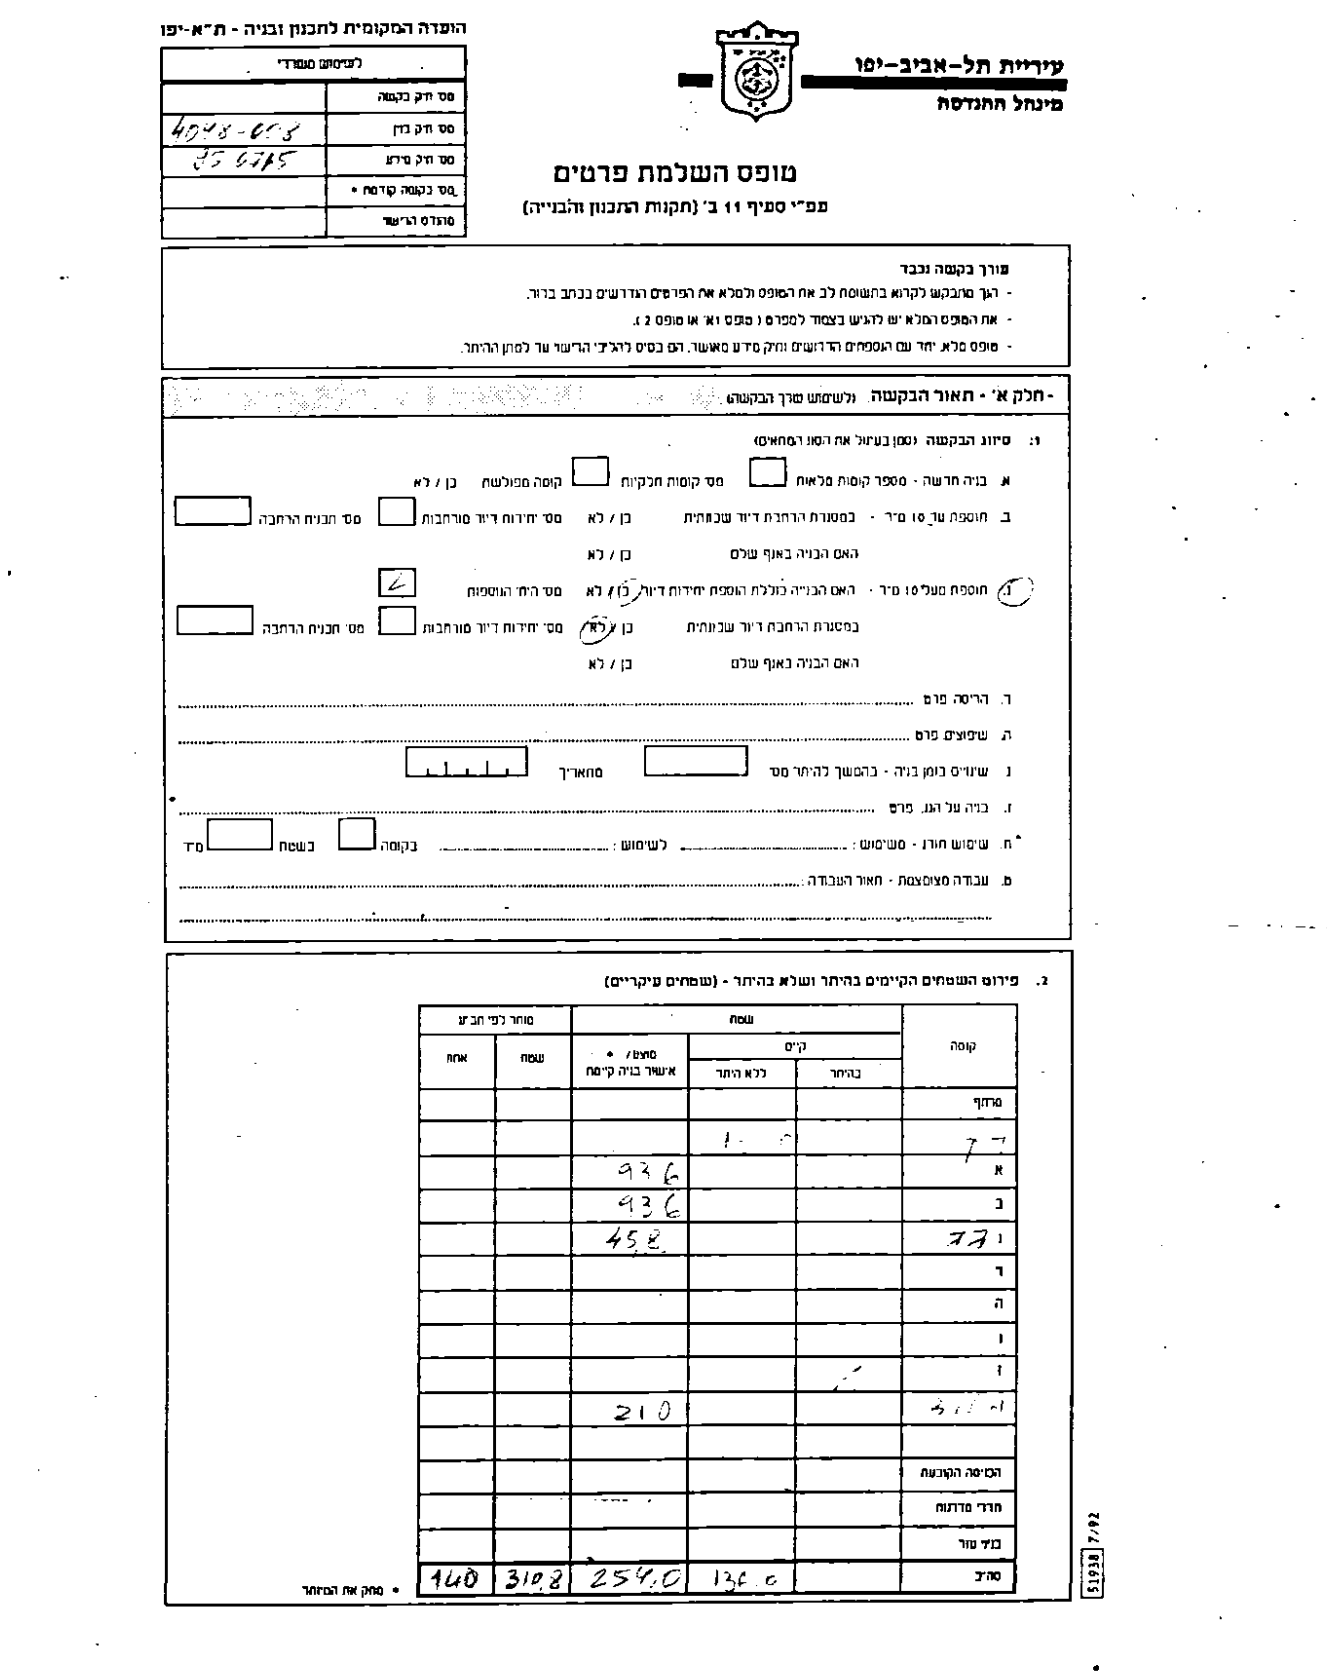

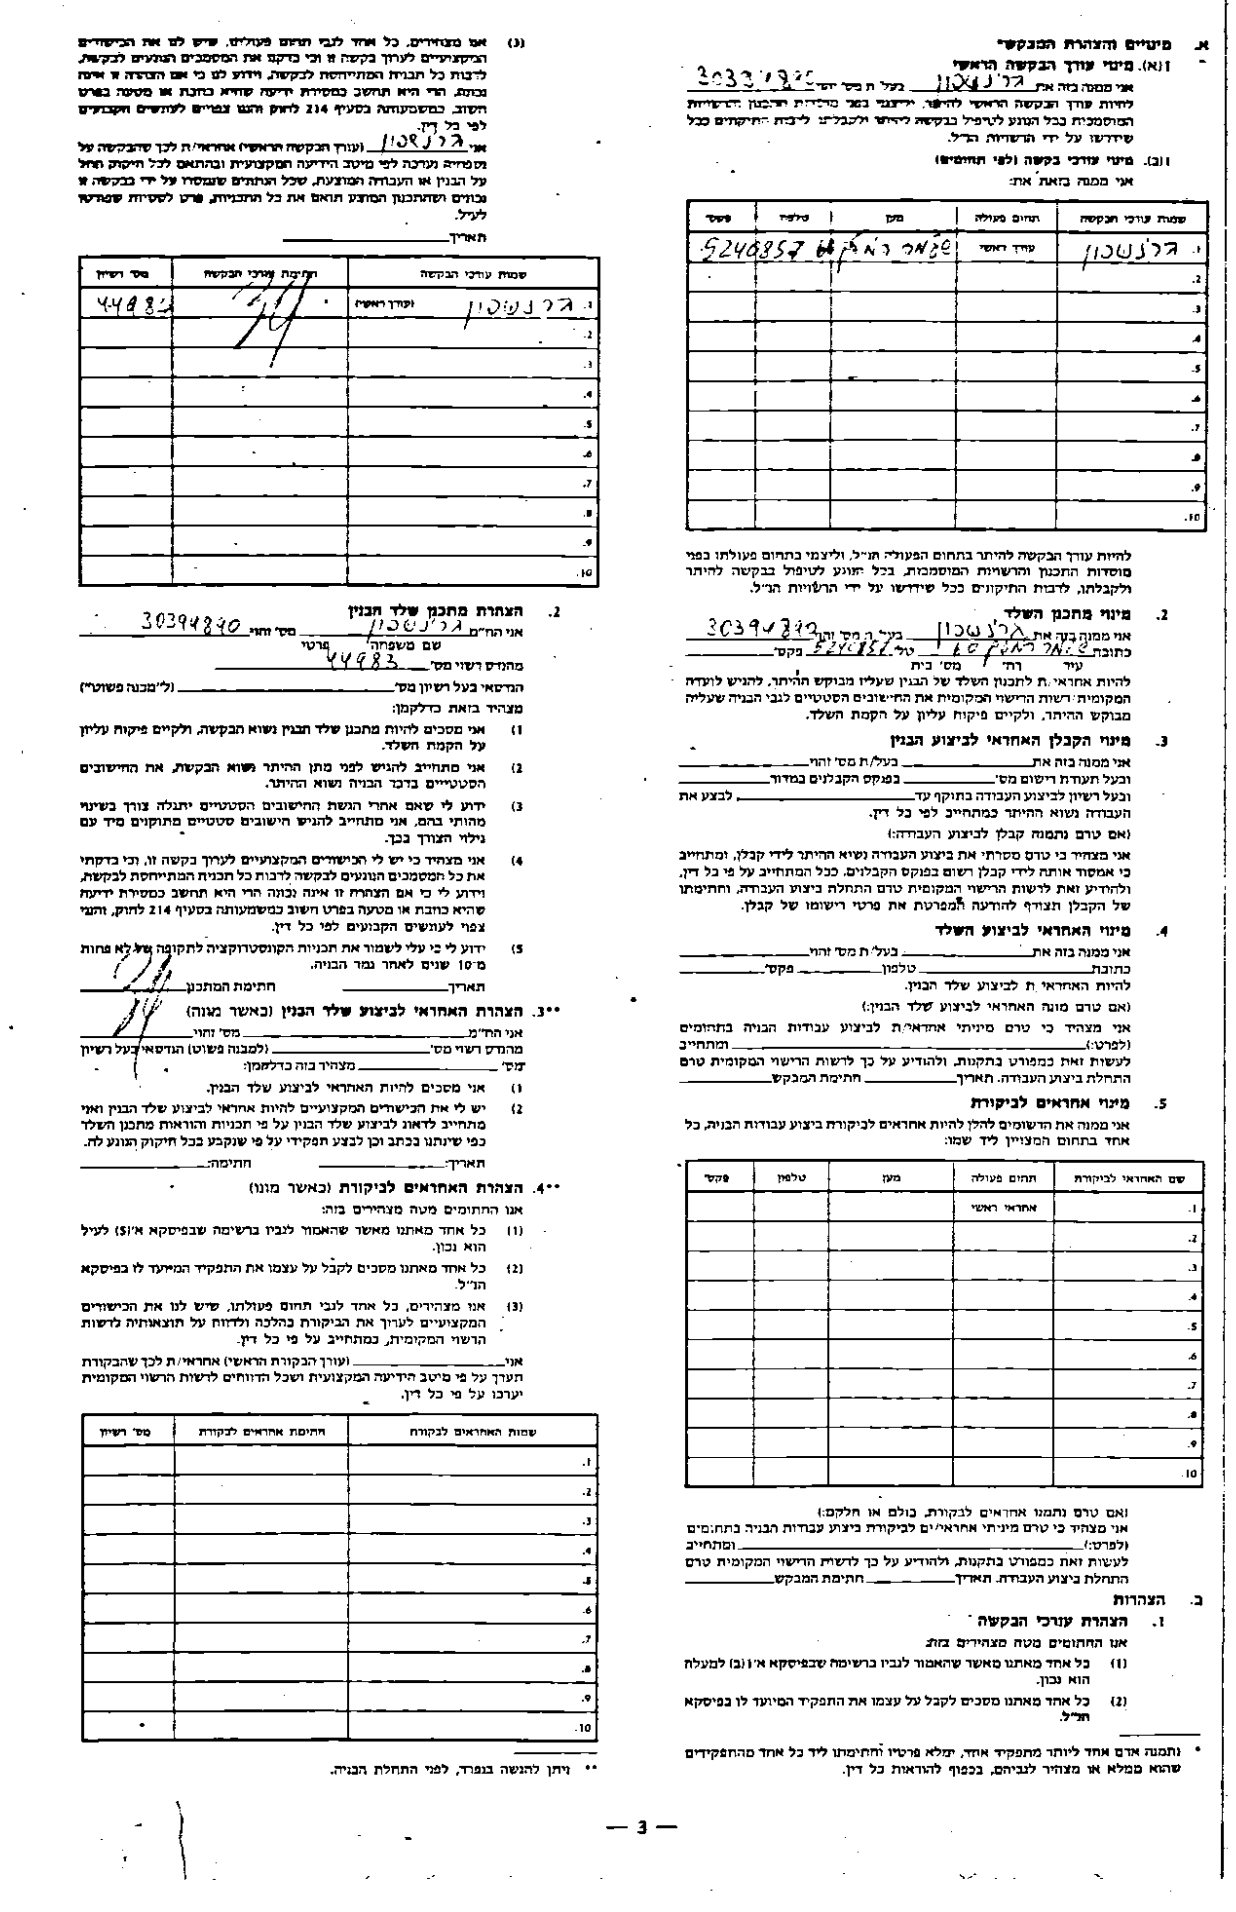

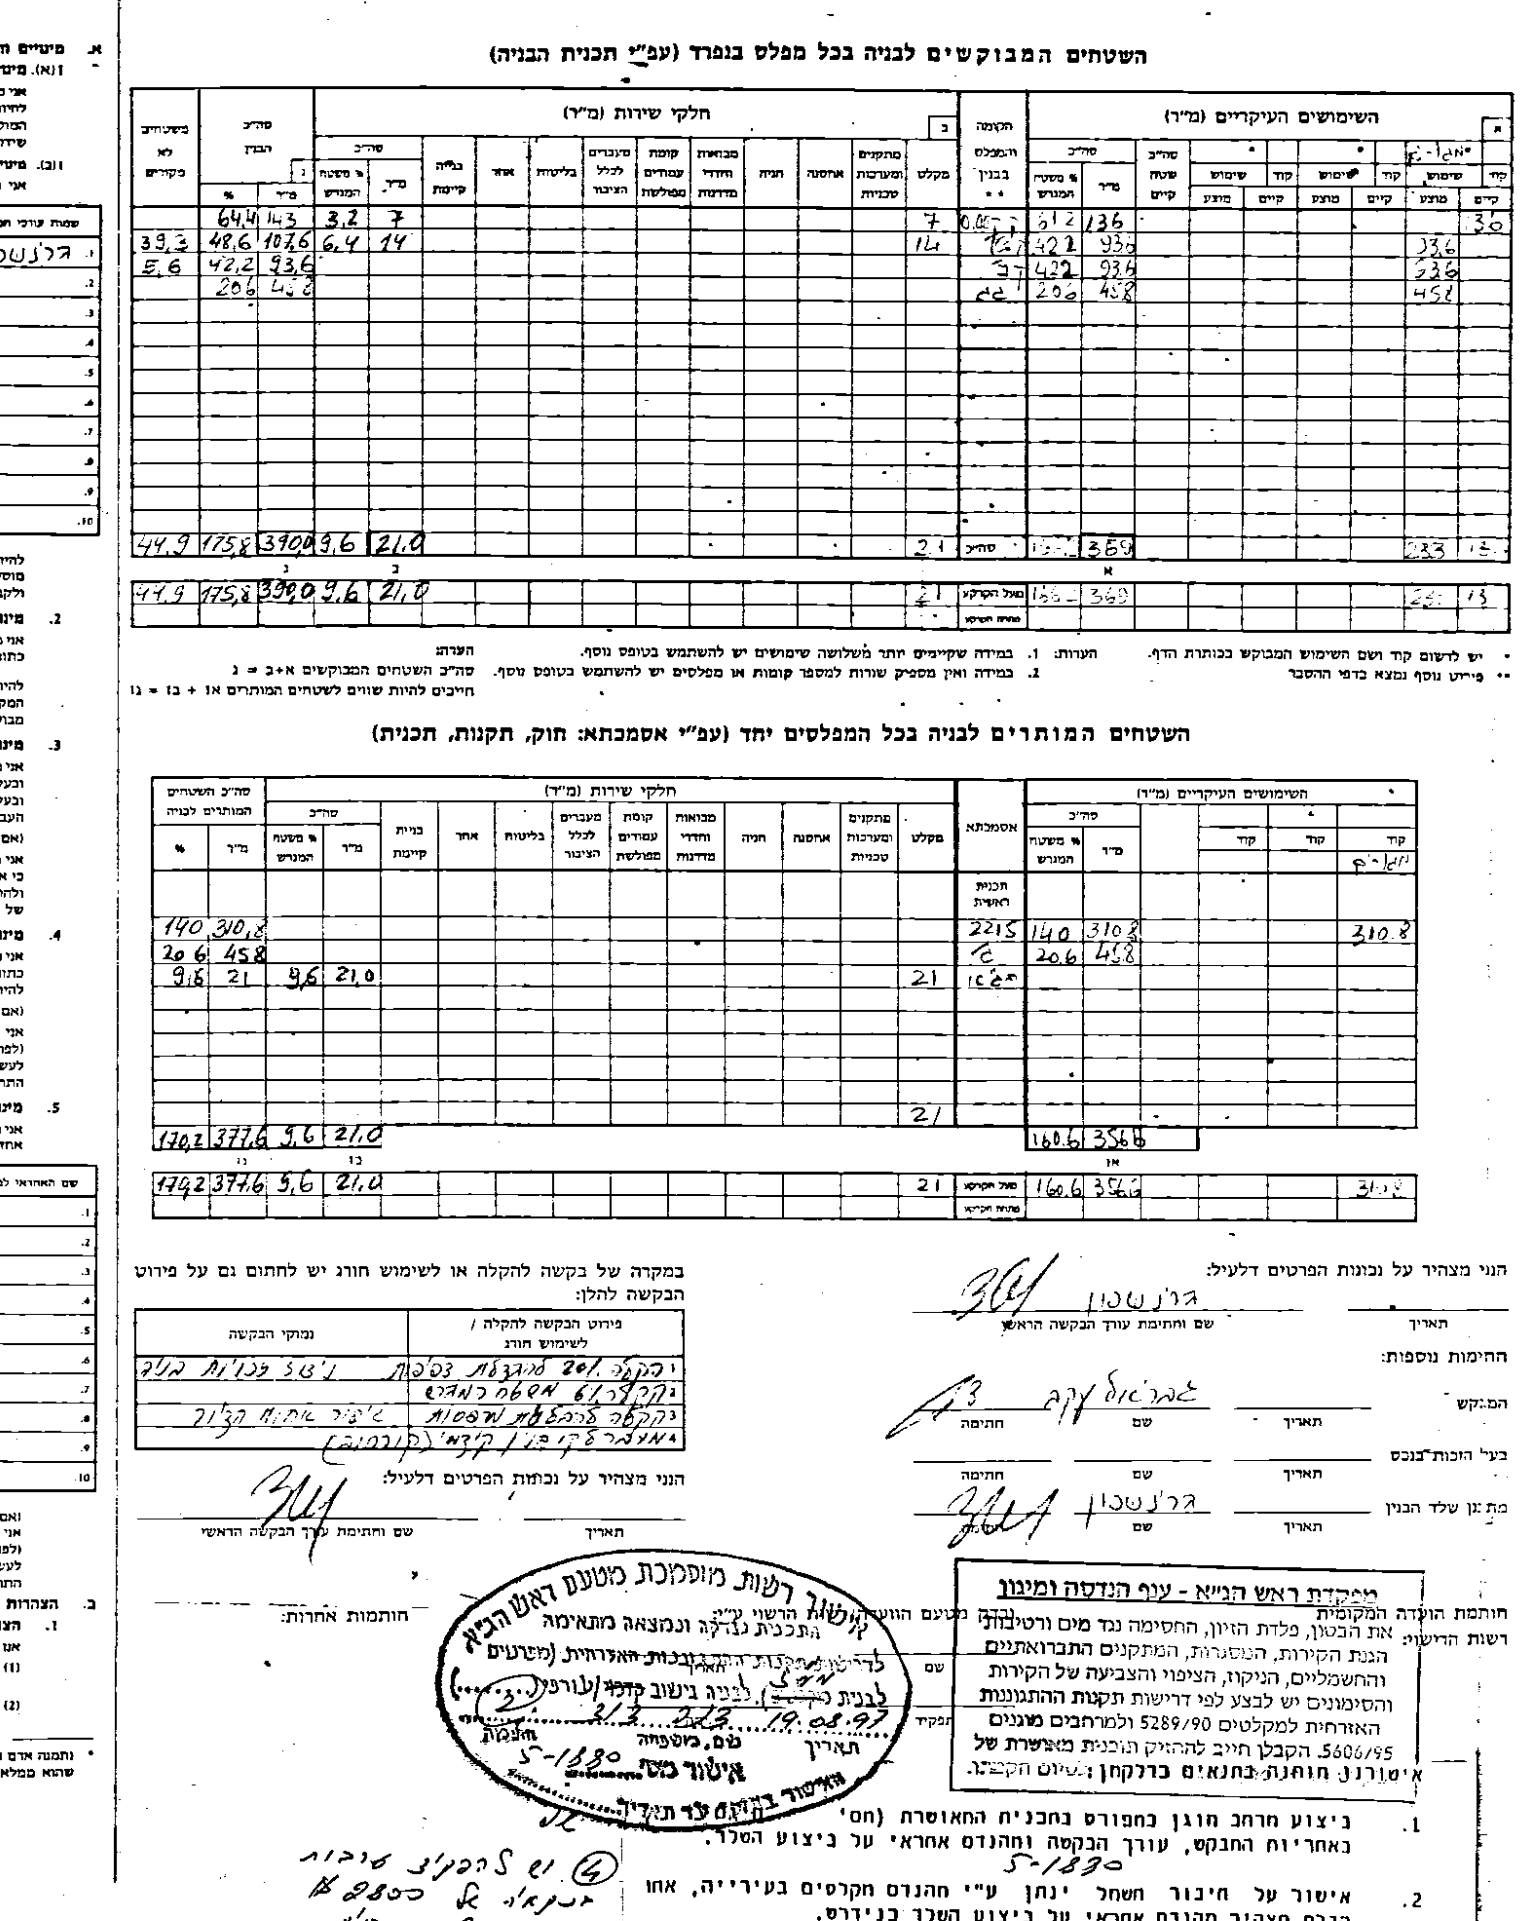

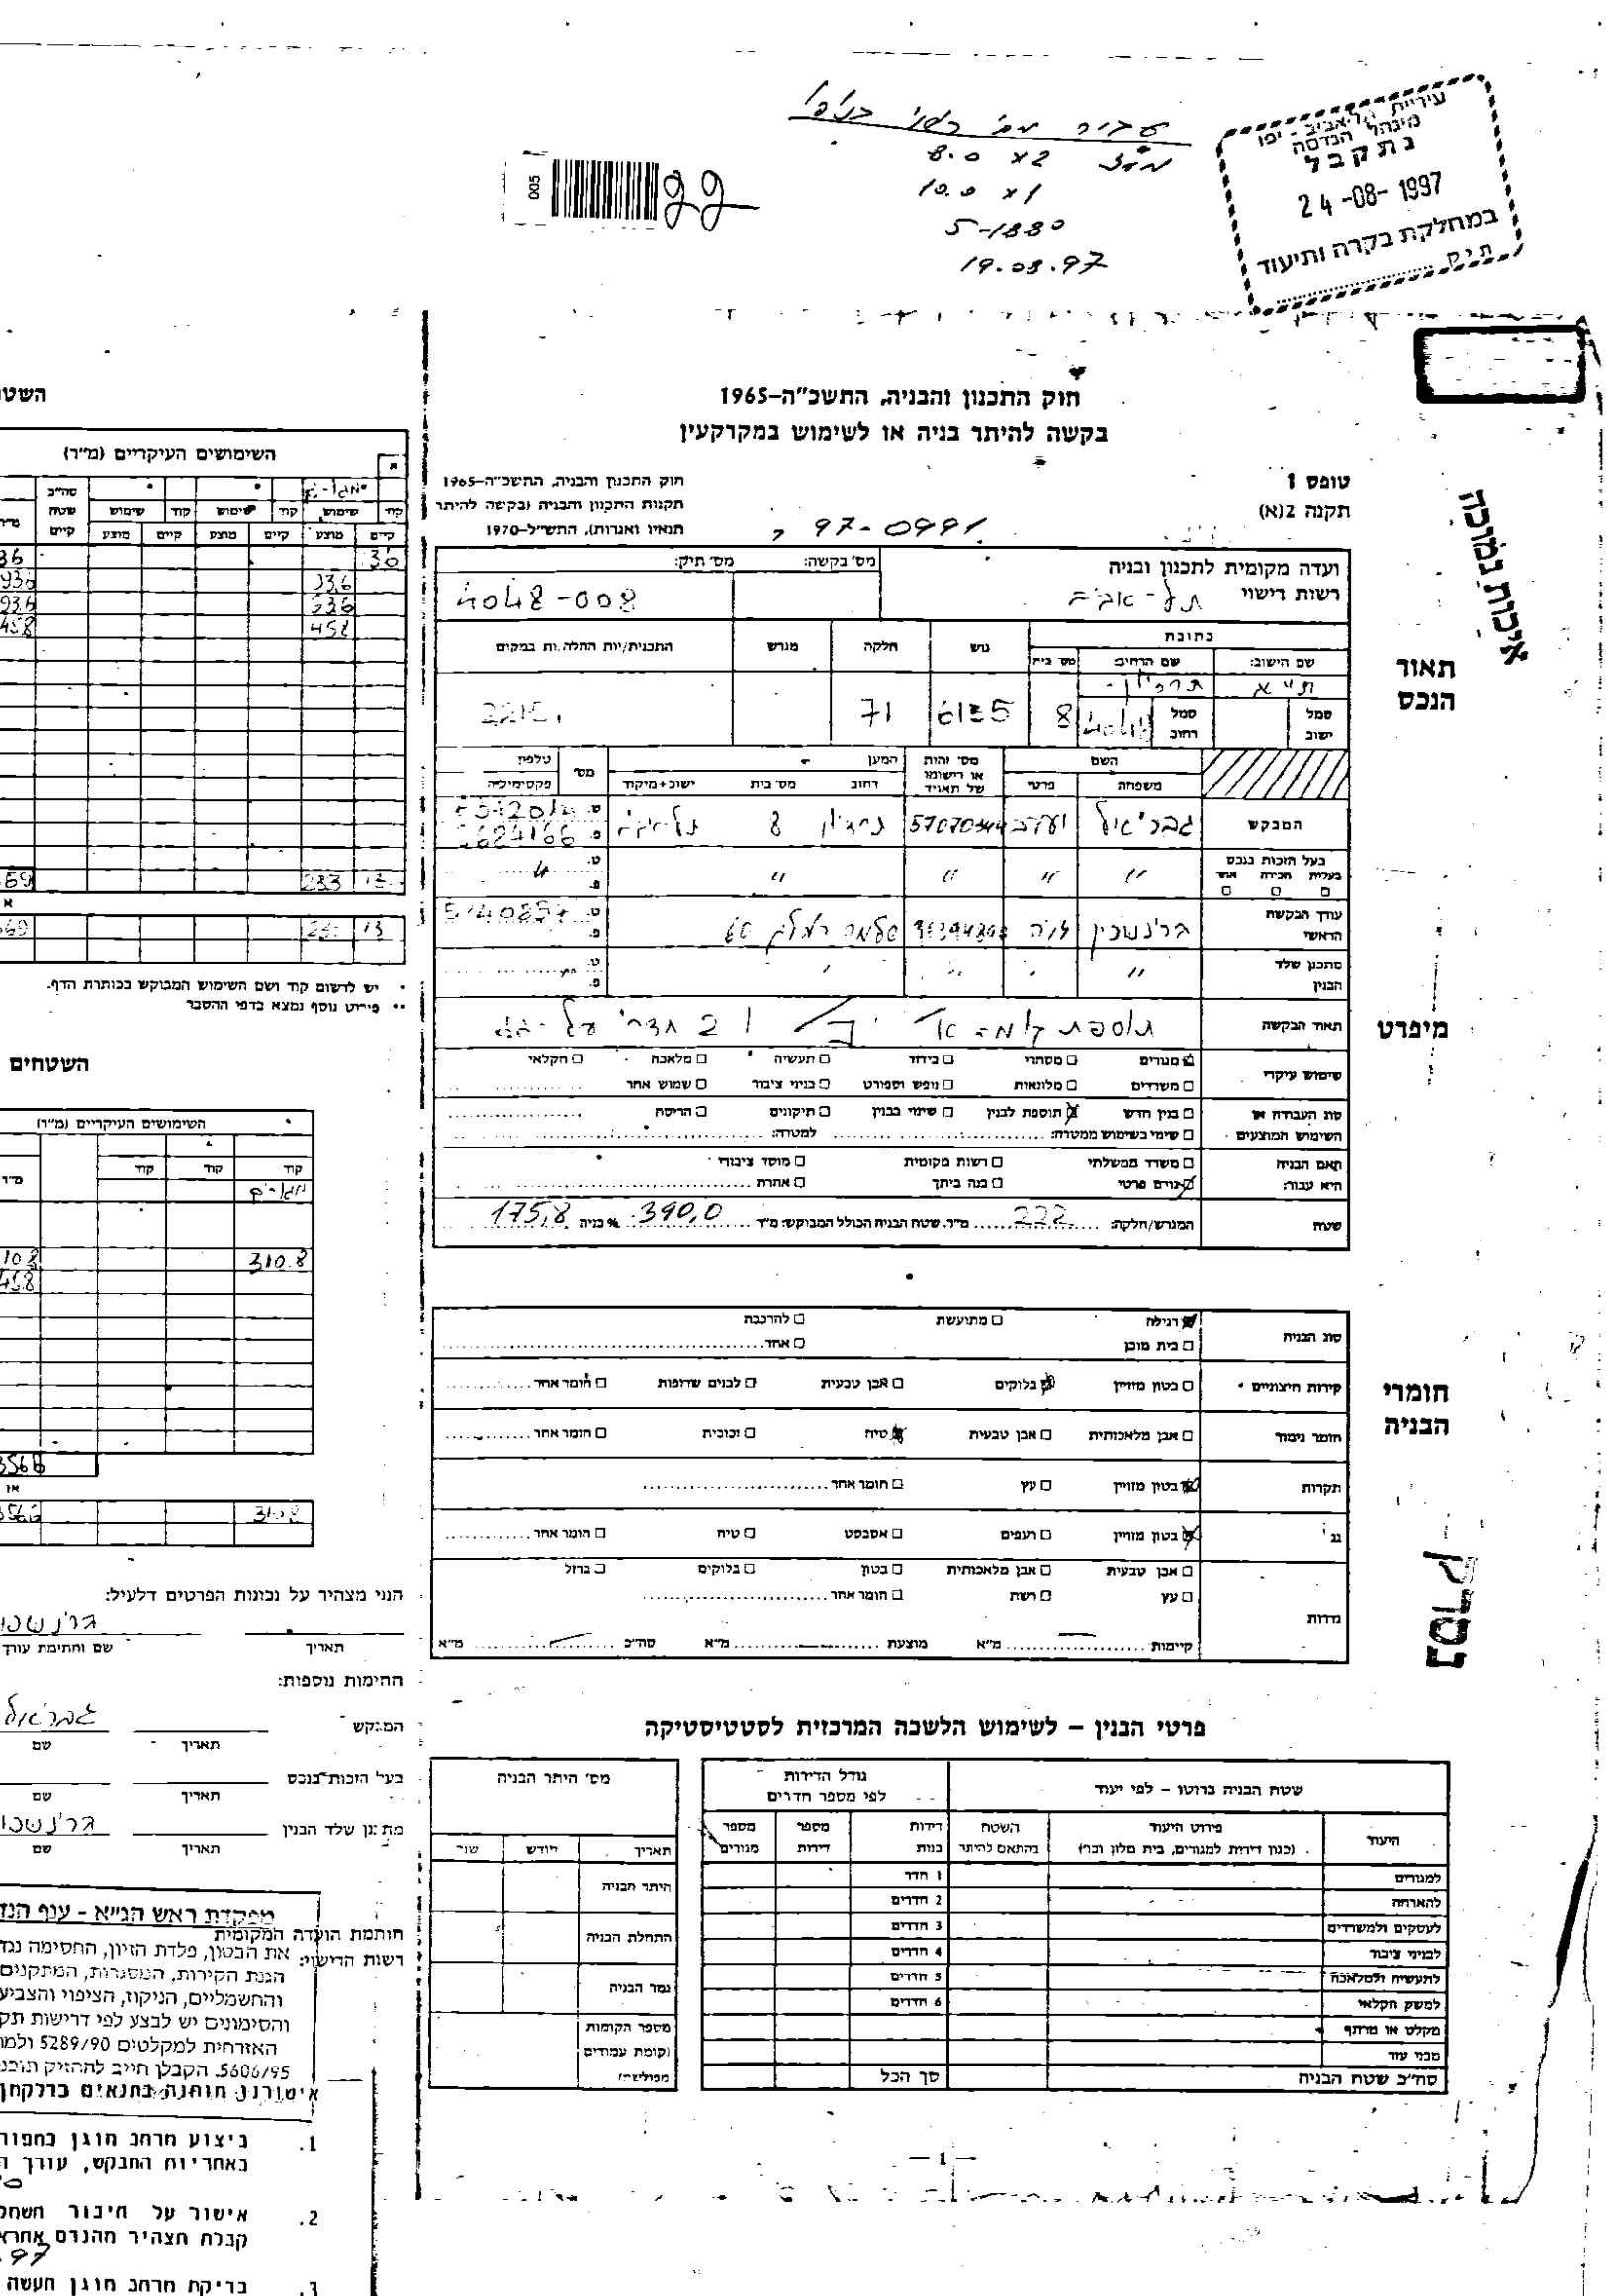

סיור עם כשר הנדסה
8.0 x2
10.0 x1
5-1880
19.08.97

עיריית תל-אביב - יפו
מינהל ההנדסה
נתקבל
24-08-1997
במחלקת בקרה ותיעוד

חוק התכנון והבניה, התשכ"ה-1965
בקשה להיתר בניה או לשימוש במקרקעין

טופס 1
תקנה 2(א)

7 97-0991

ועדה מקומית לתכנון ובניה: תל-אביב
מס' תיק: 4048-008
גוש: 6155
חלקה: 71