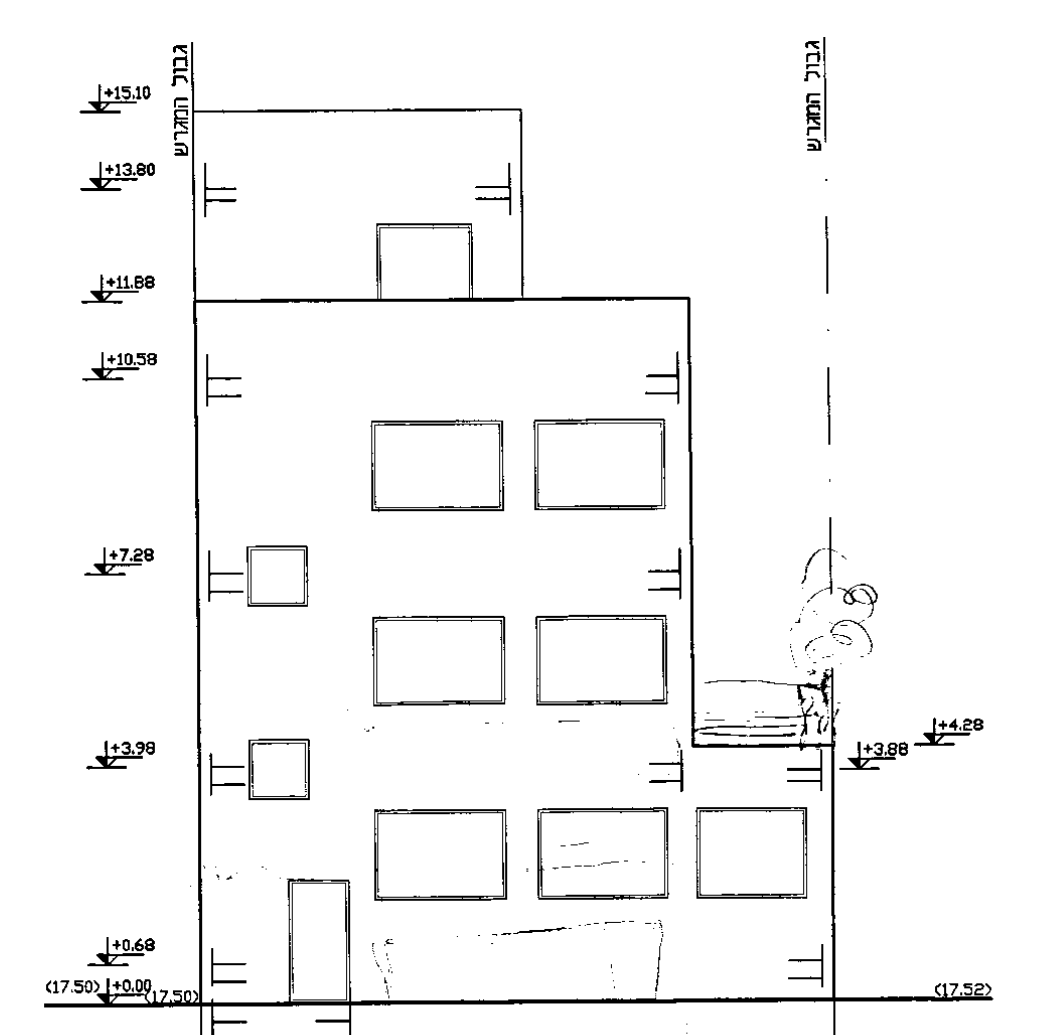
גבול המגרש
+15.10
+13.80
+11.88
+10.50
+7.20
+3.90
+0.60
±0.00
(17.50)
(17.52)

חזית מזרחית ק.מ. 1:100

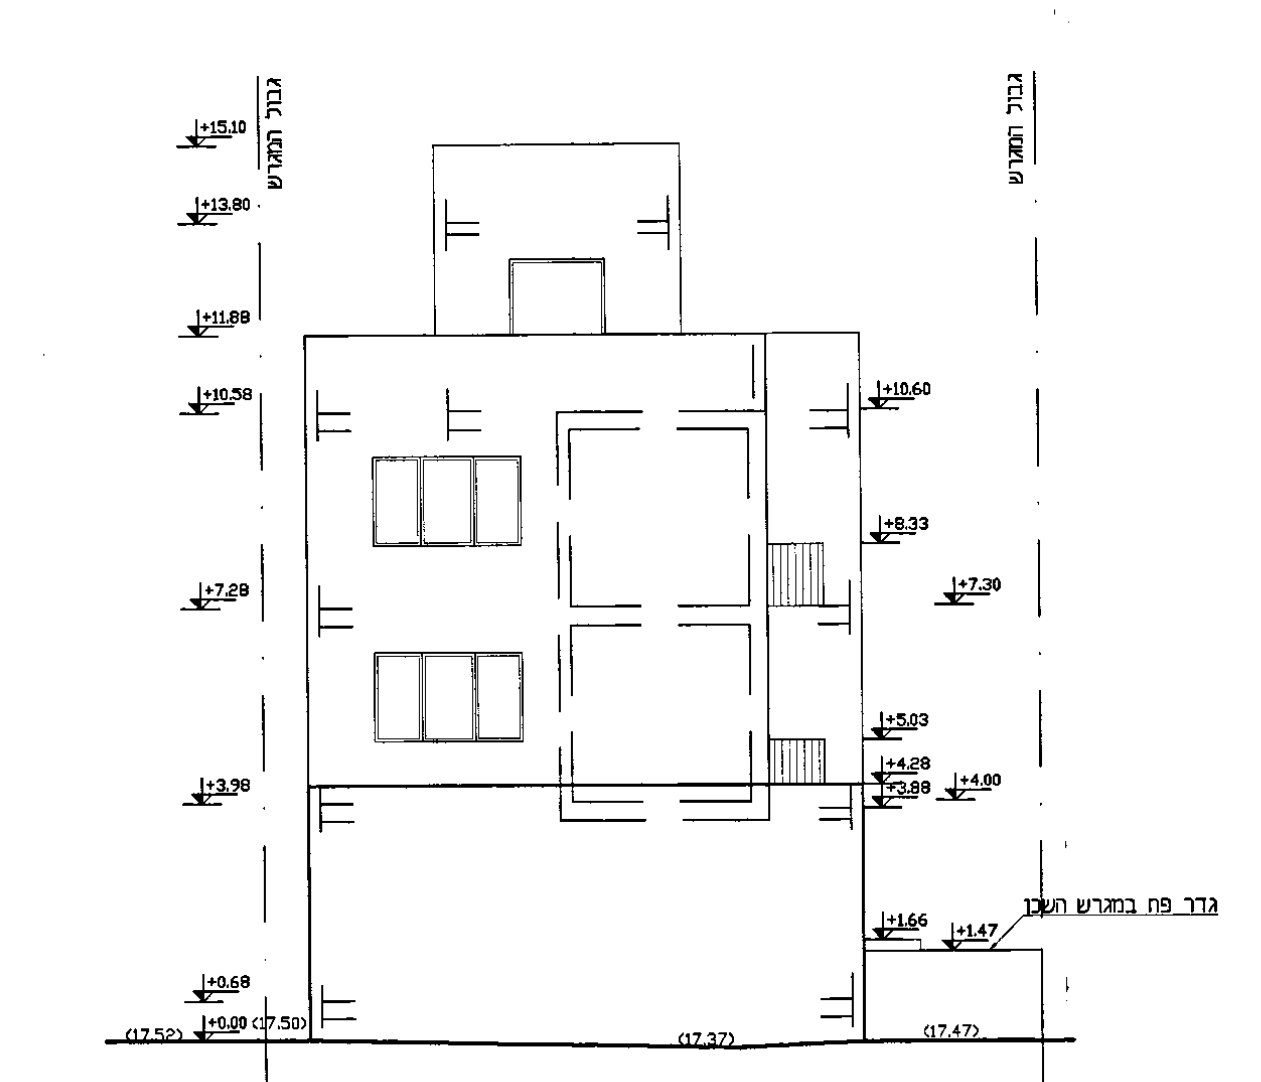
גבול המגרש
+15.10
+13.80
+11.88
+10.50
+10.60
+8.33
+7.20
+5.03
+4.28
+3.90
+1.66
+1.47
גדר פח במגרש השכן
(17.37)
(17.47)

חזית צפונית ק.מ. 1:100

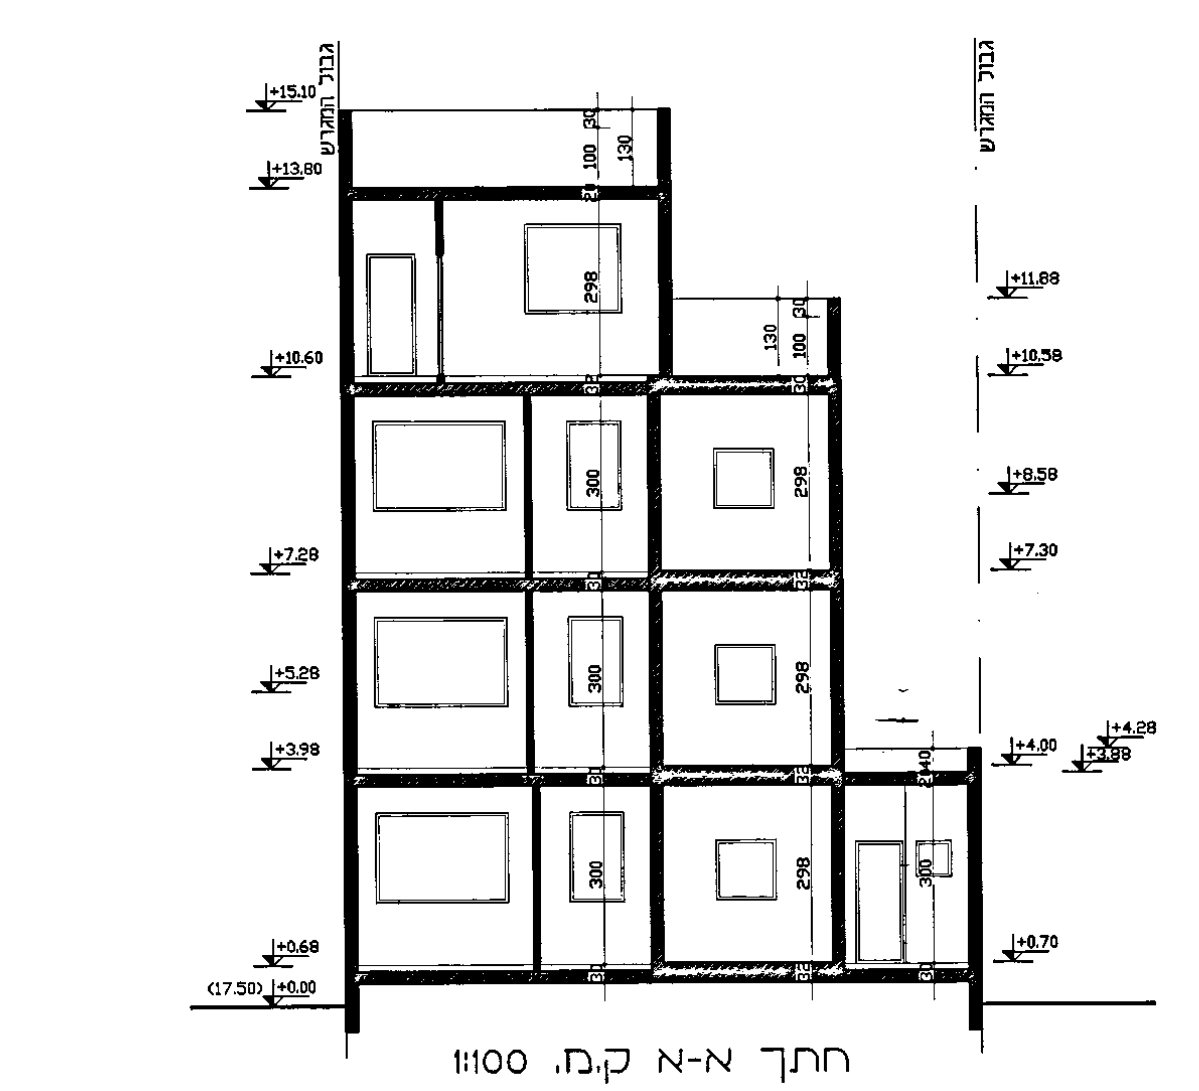
גבול המגרש
+15.10
+13.80
+11.88
+10.50
+7.20
+3.90
+0.60
300
298

חתך א-א ק.מ. 1:100

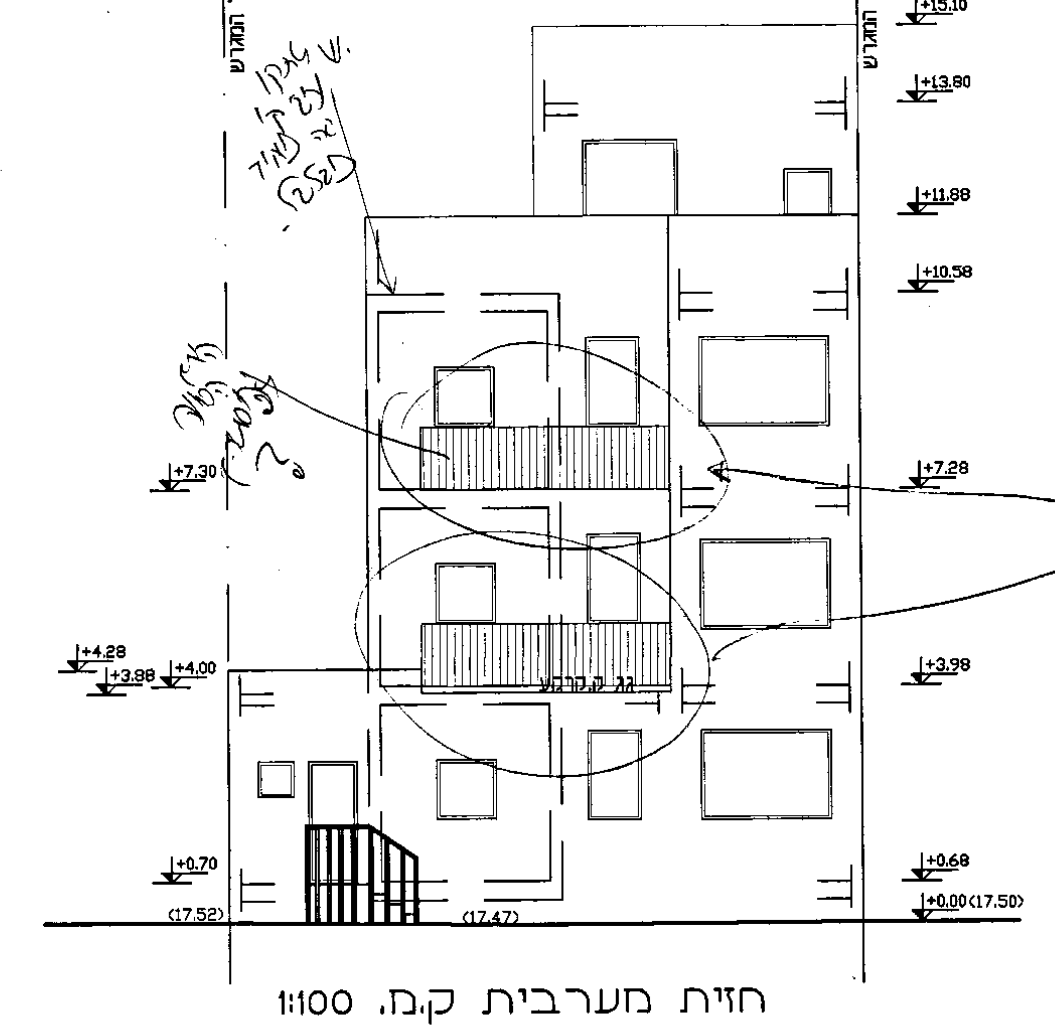
גבול המגרש
+15.10
+13.80
+11.88
+10.50
+7.20
+3.90
+0.70
±0.00
(17.50)
(17.52)
(17.47)

חזית מערבית ק.מ. 1:100

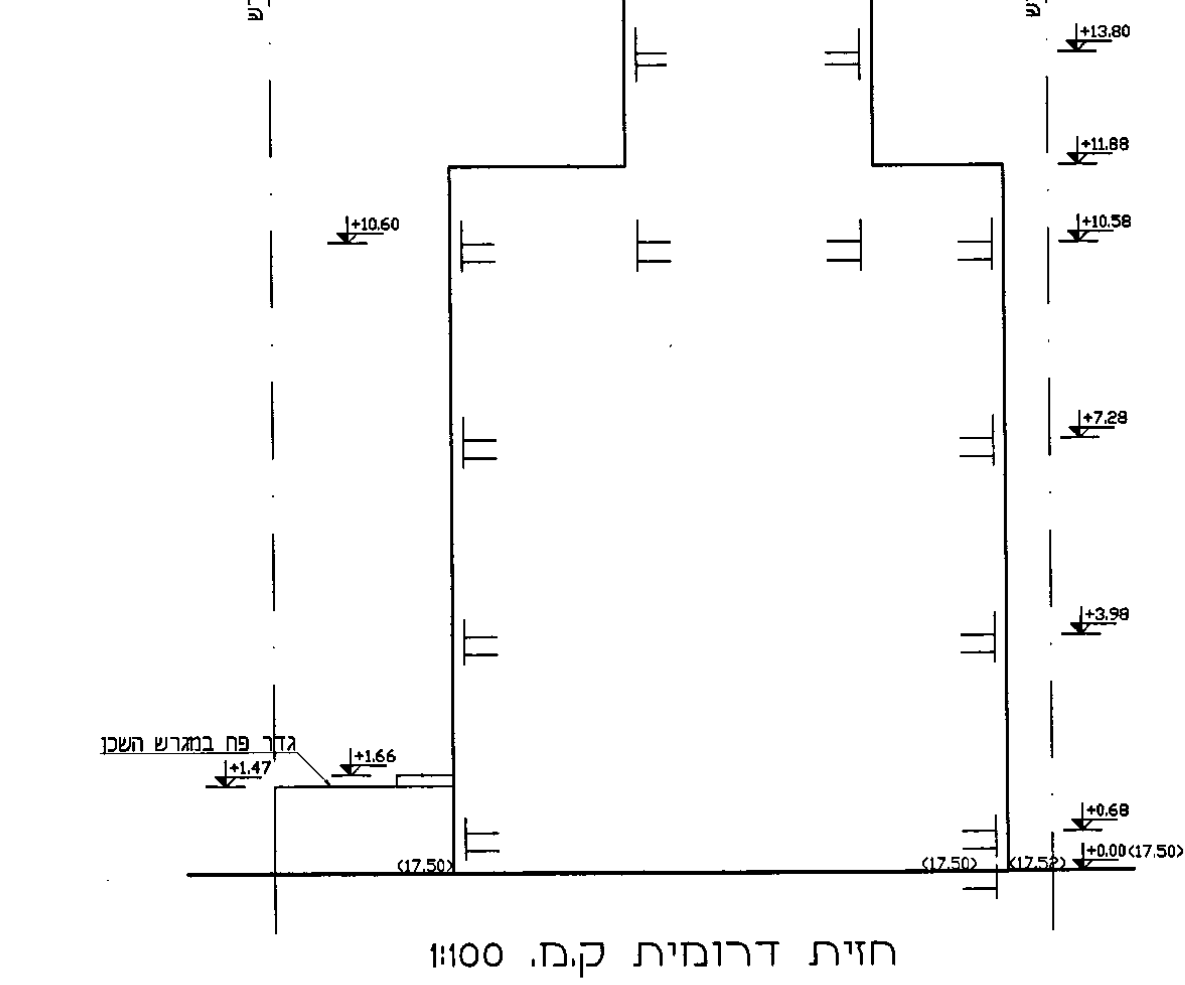
גבול המגרש
+15.10
+13.80
+11.88
+10.50
+10.60
+7.20
+3.90
+1.66
+1.47
+0.60
גדר פח במגרש השכן
(17.50)

חזית דרומית ק.מ. 1:100

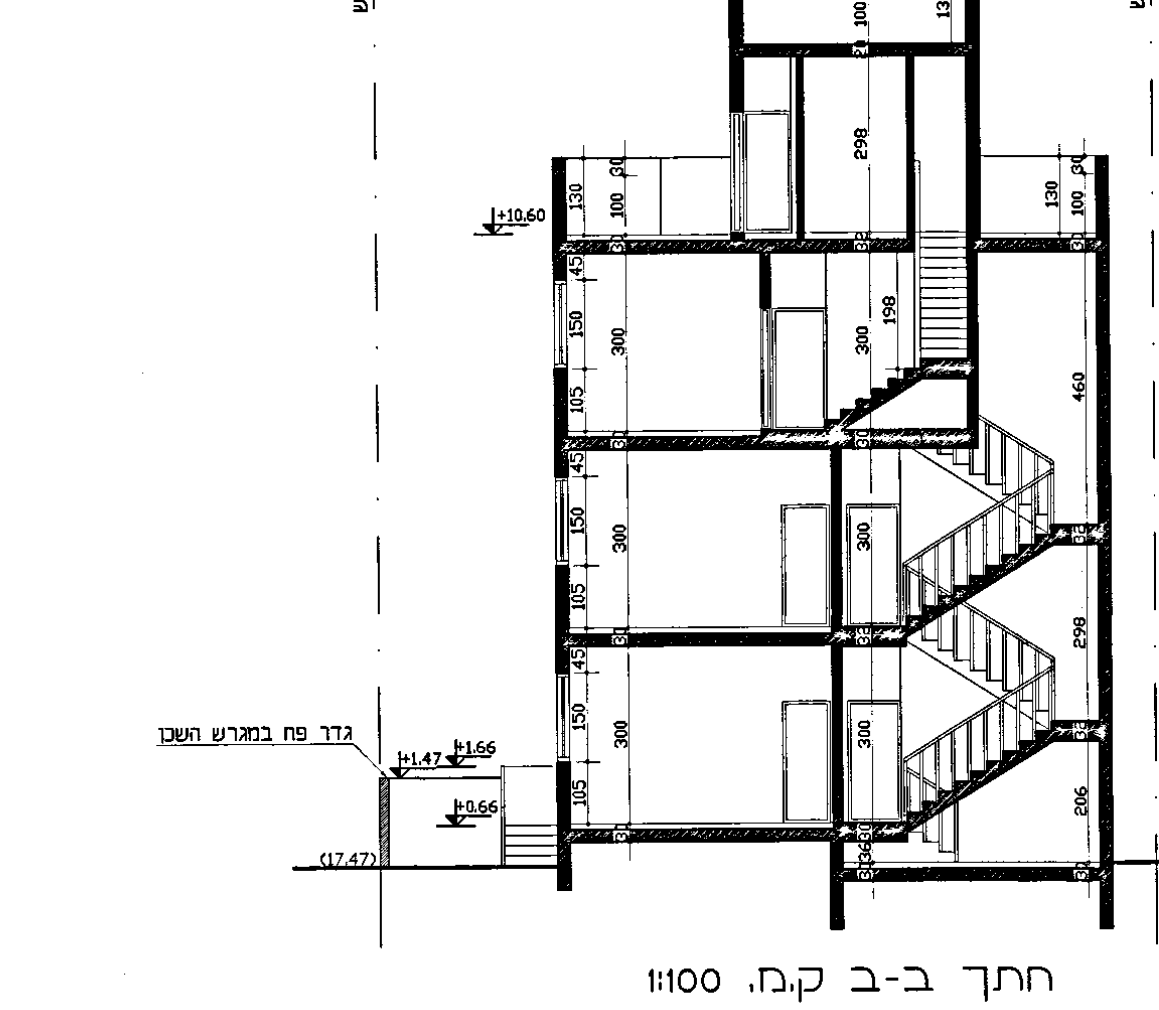
גבול המגרש
+15.10
+13.80
+11.88
+10.60
+10.50
+8.47
+7.20
+5.60
+3.90
+2.30
+0.60
+1.66
+1.47
גדר פח במגרש השכן
(17.47)
(17.50)

חתך ב-ב ק.מ. 1:100

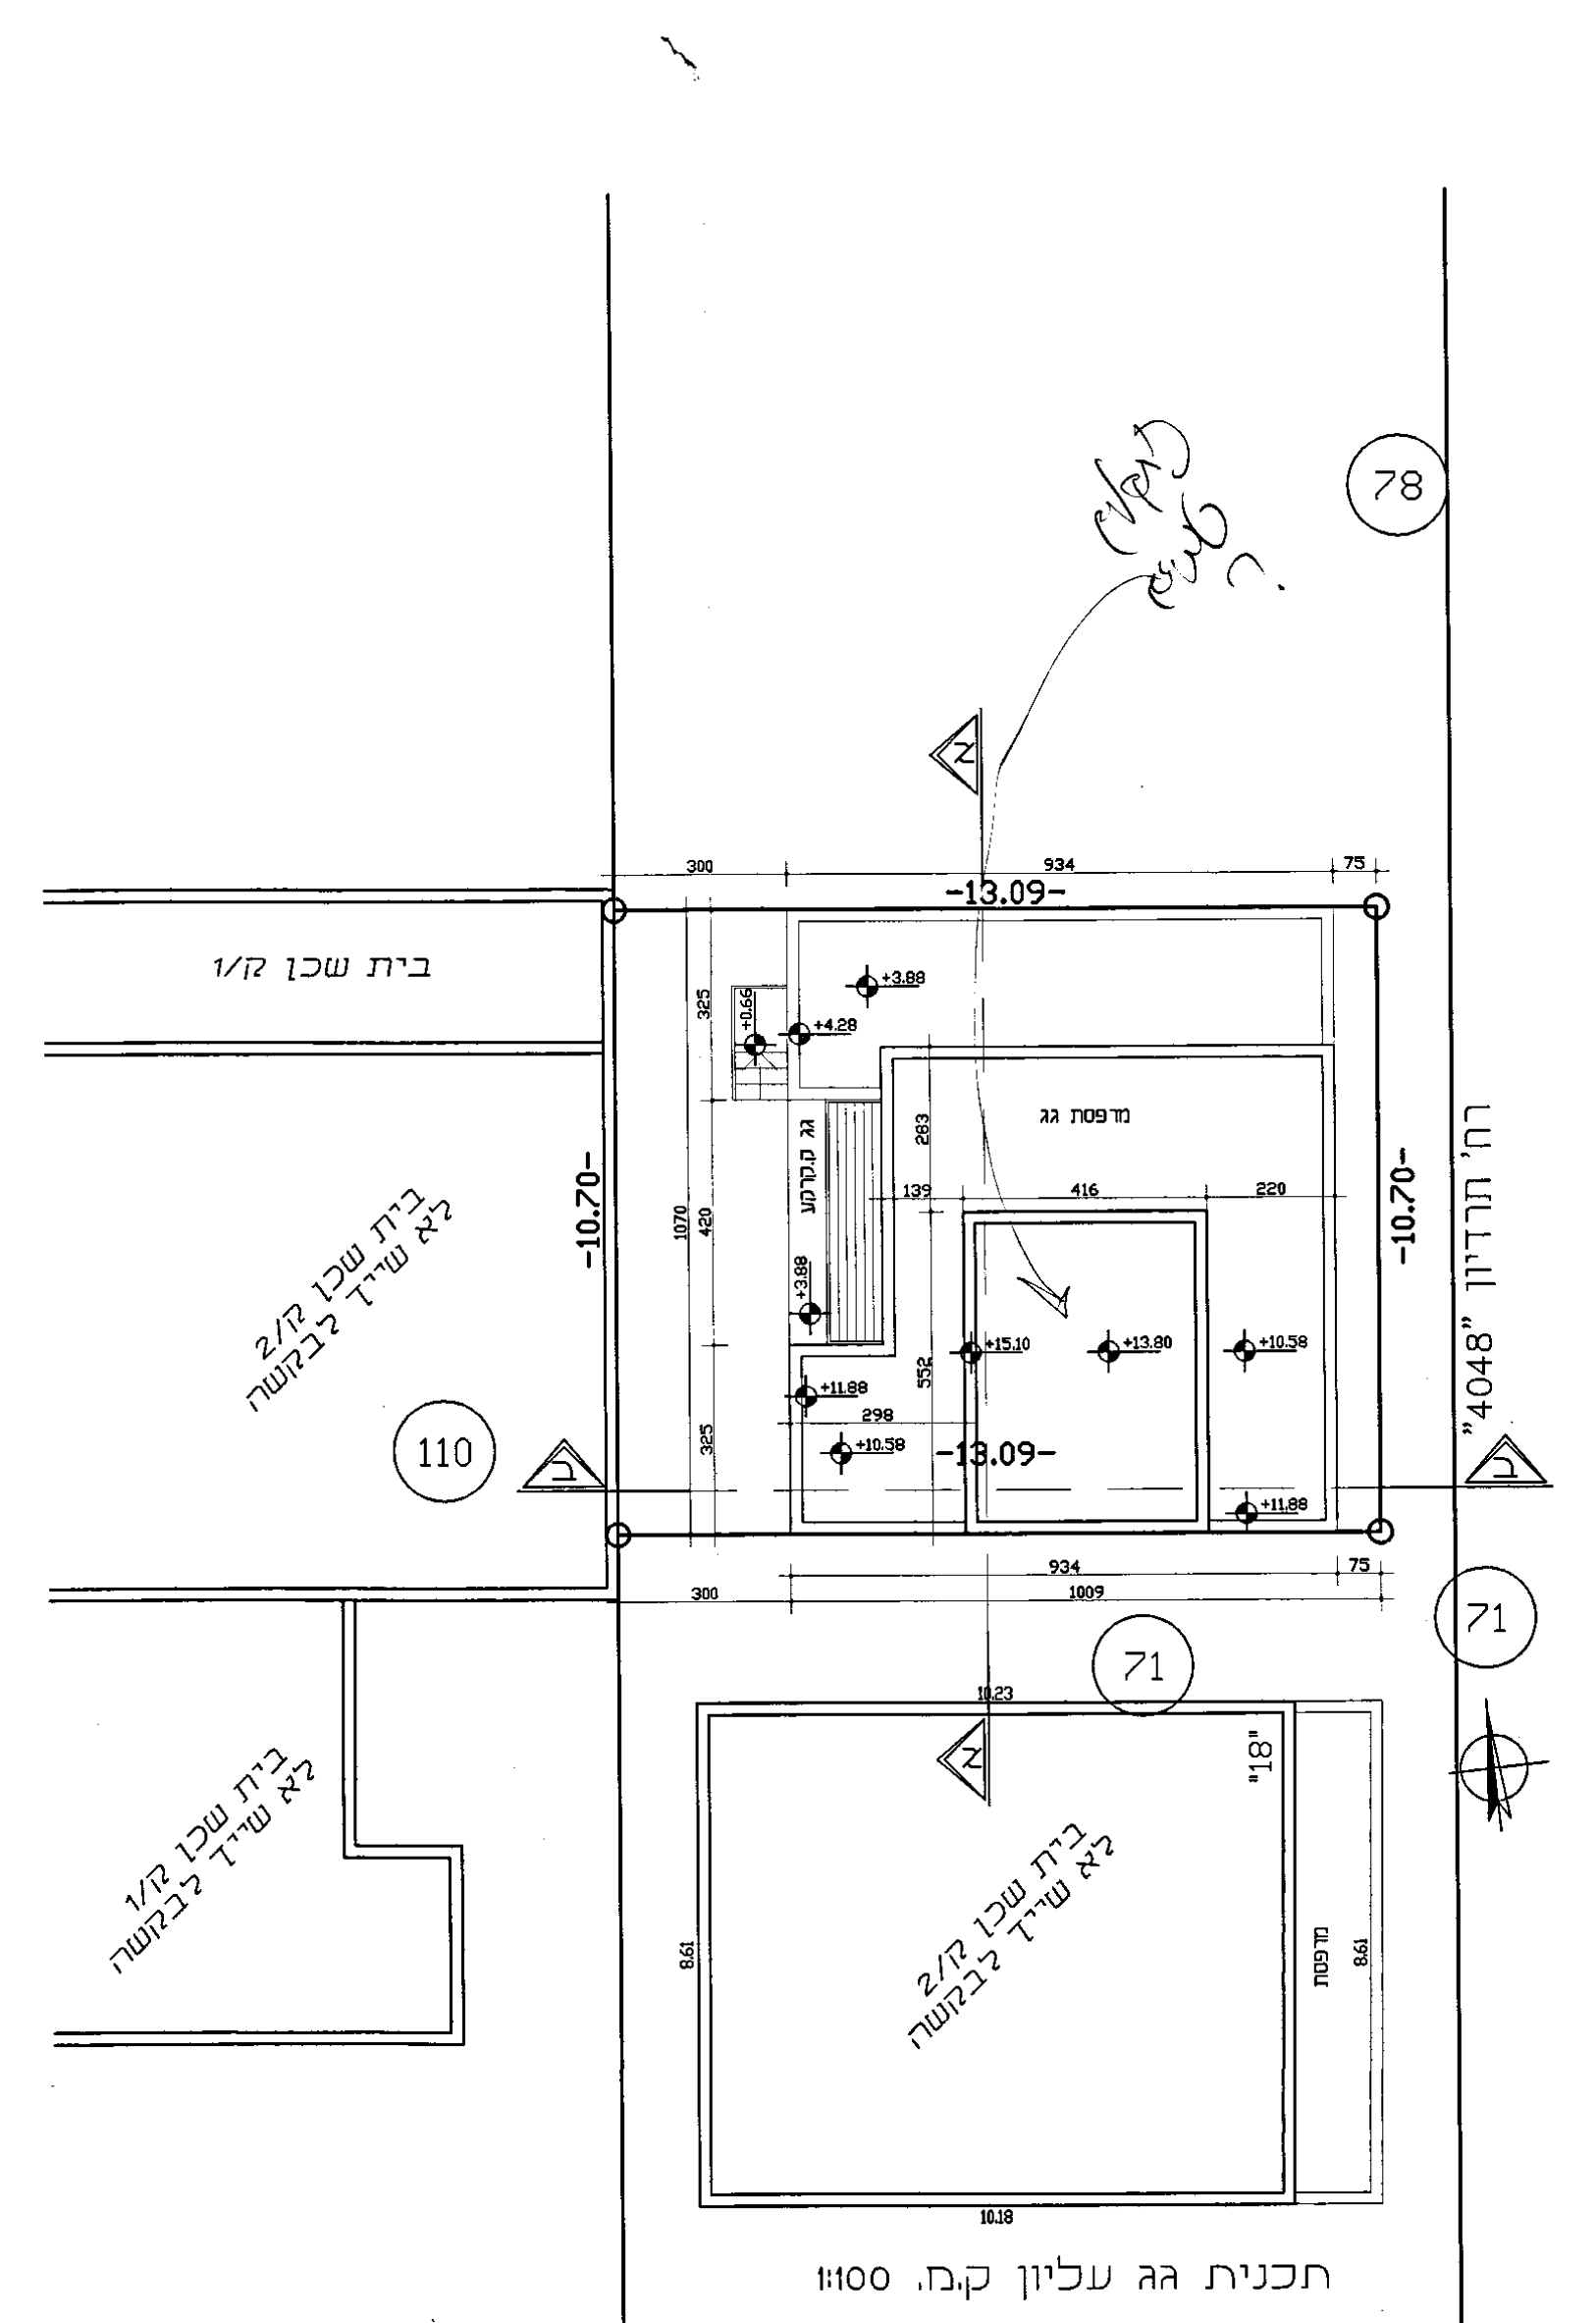
78
-13.09-
934
75
300
בית שכן ק/1
-10.70-
מרפסת גג
+13.80
+15.10
+10.50
+11.88
+4.28
+3.88
110
71
1009
בית שכן ק/2 לא שייך לבקשה
בית שכן ק/1 לא שייך לבקשה
1023
1018
"18"
מרפסת
861
רח' תרדיון "4048"

תכנית גג עליון ק.מ. 1:100

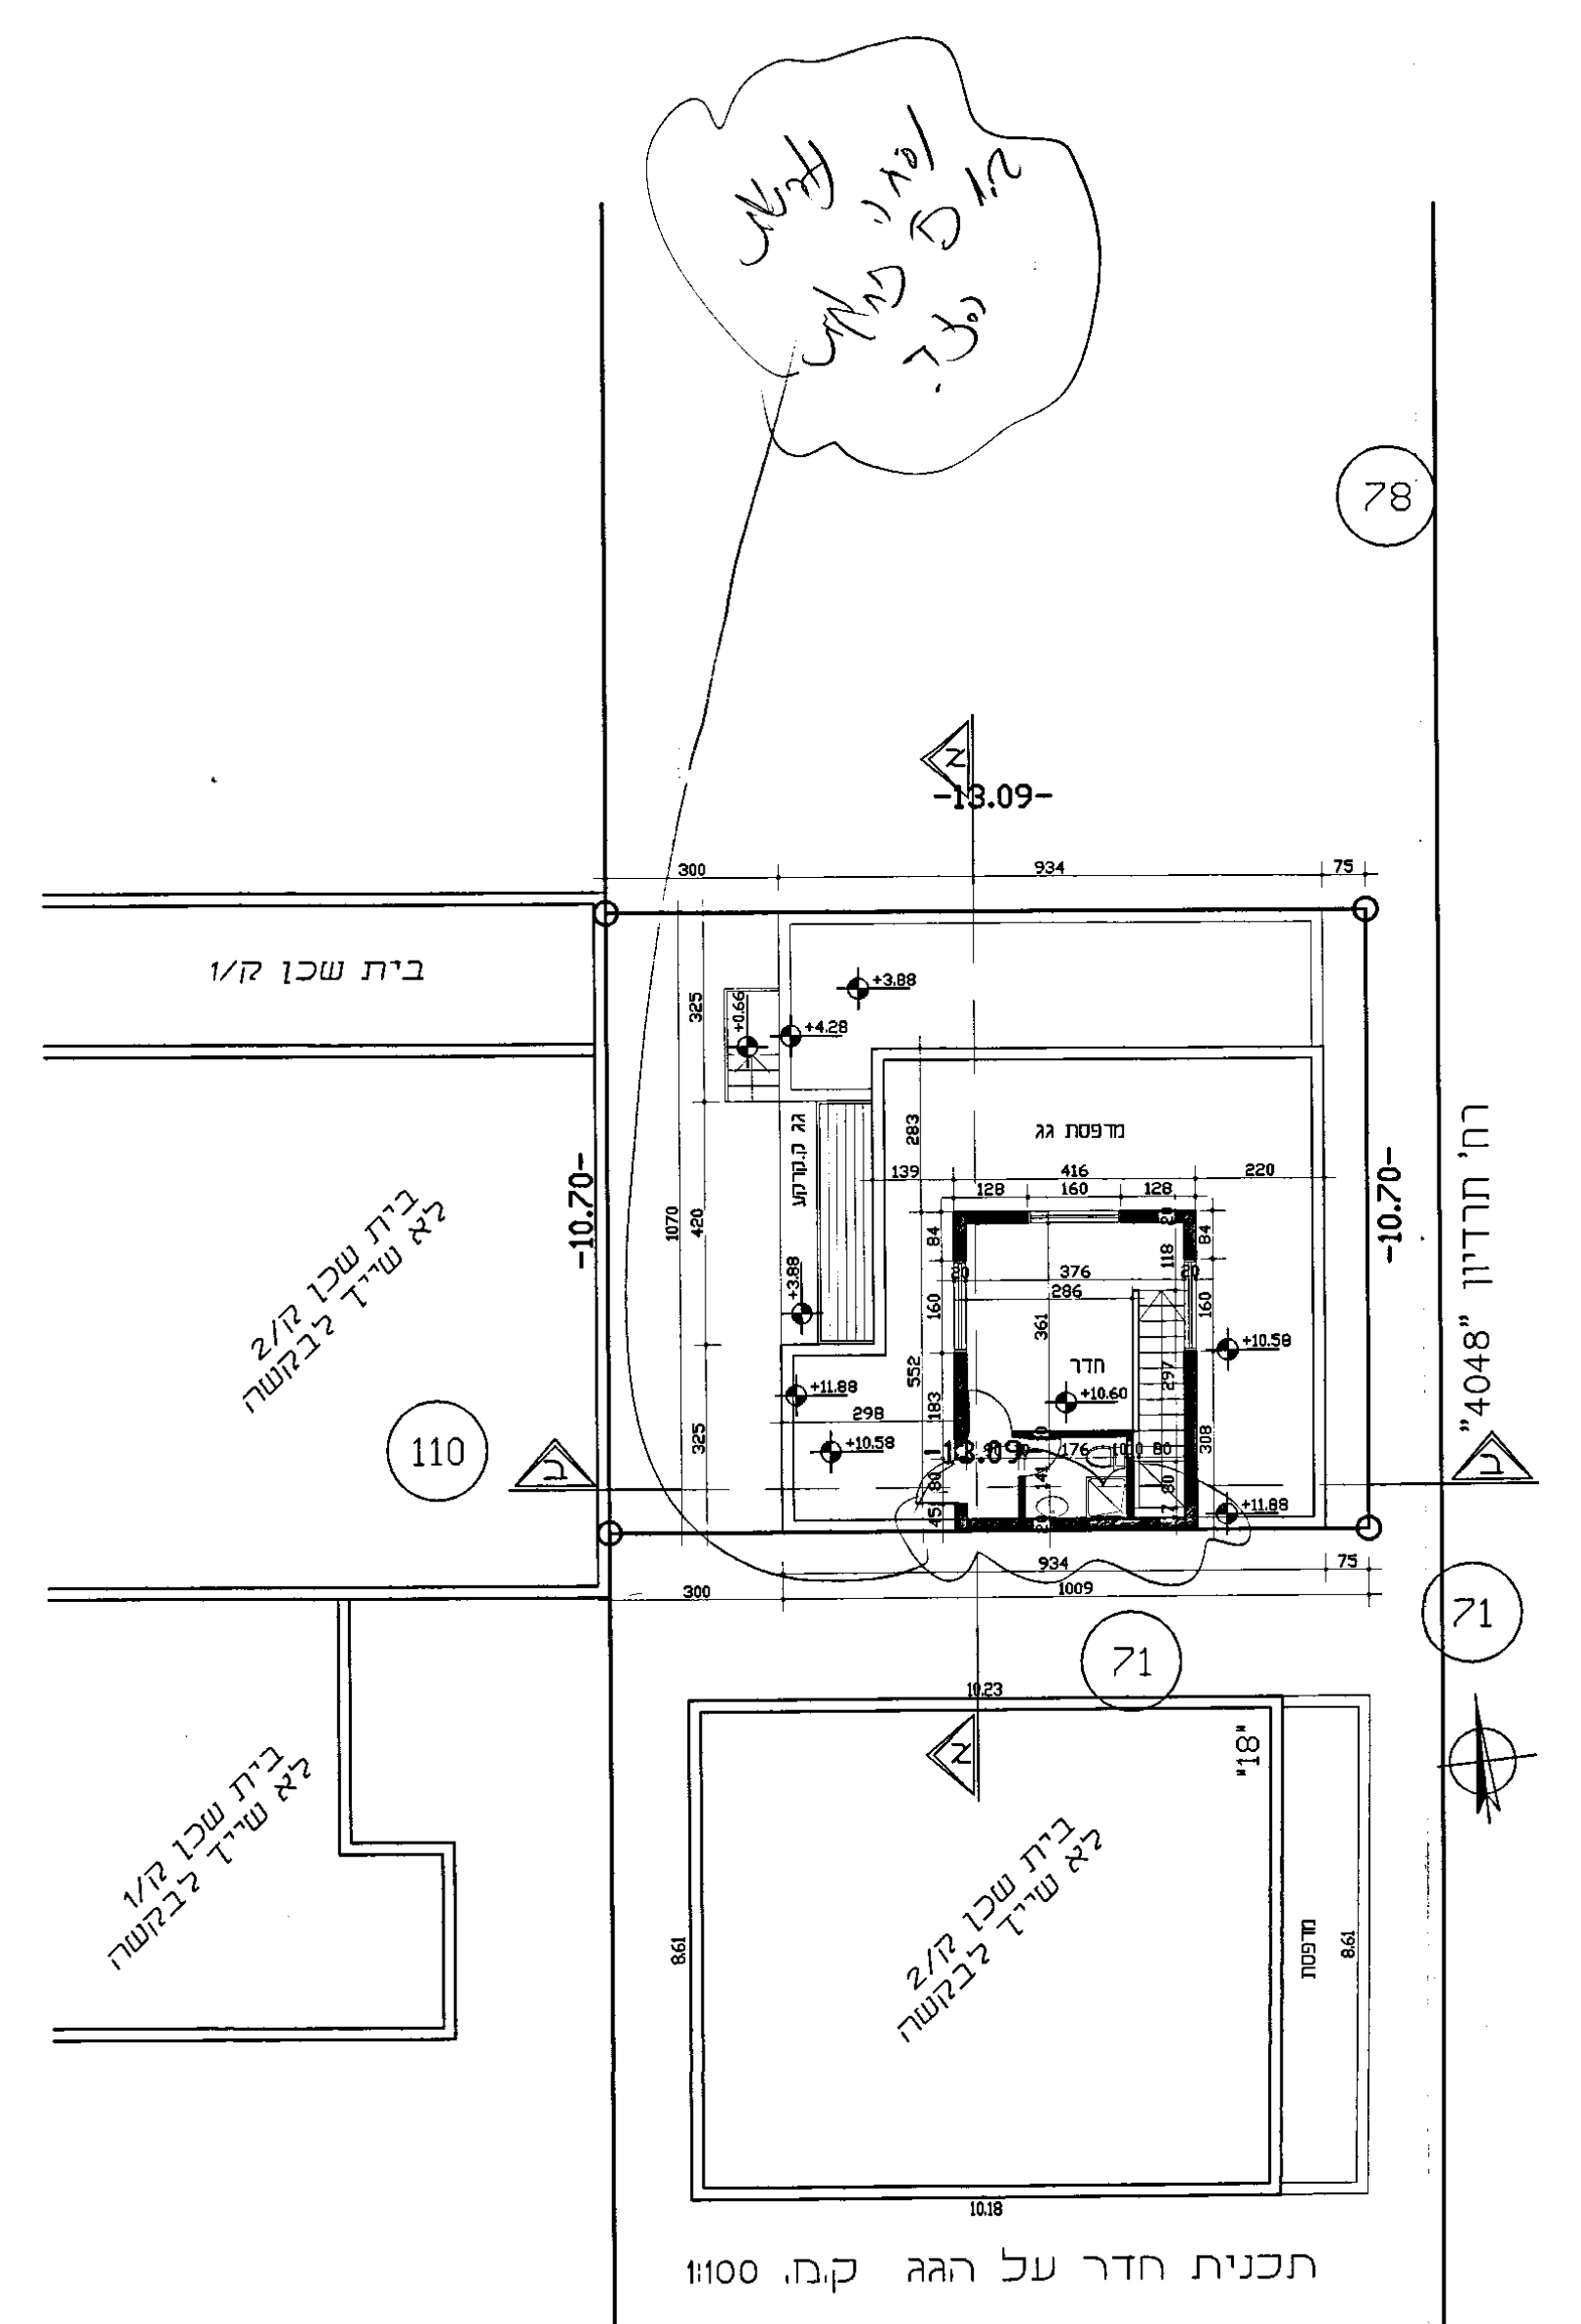
78
-13.09-
בית שכן ק/1
מרפסת גג
חדר
+10.60
+10.50
+11.88
-10.70-
110
71
בית שכן ק/2 לא שייך לבקשה
בית שכן ק/1 לא שייך לבקשה
"18"
רח' תרדיון "4048"

תכנית חדר על הגג ק.מ. 1:100

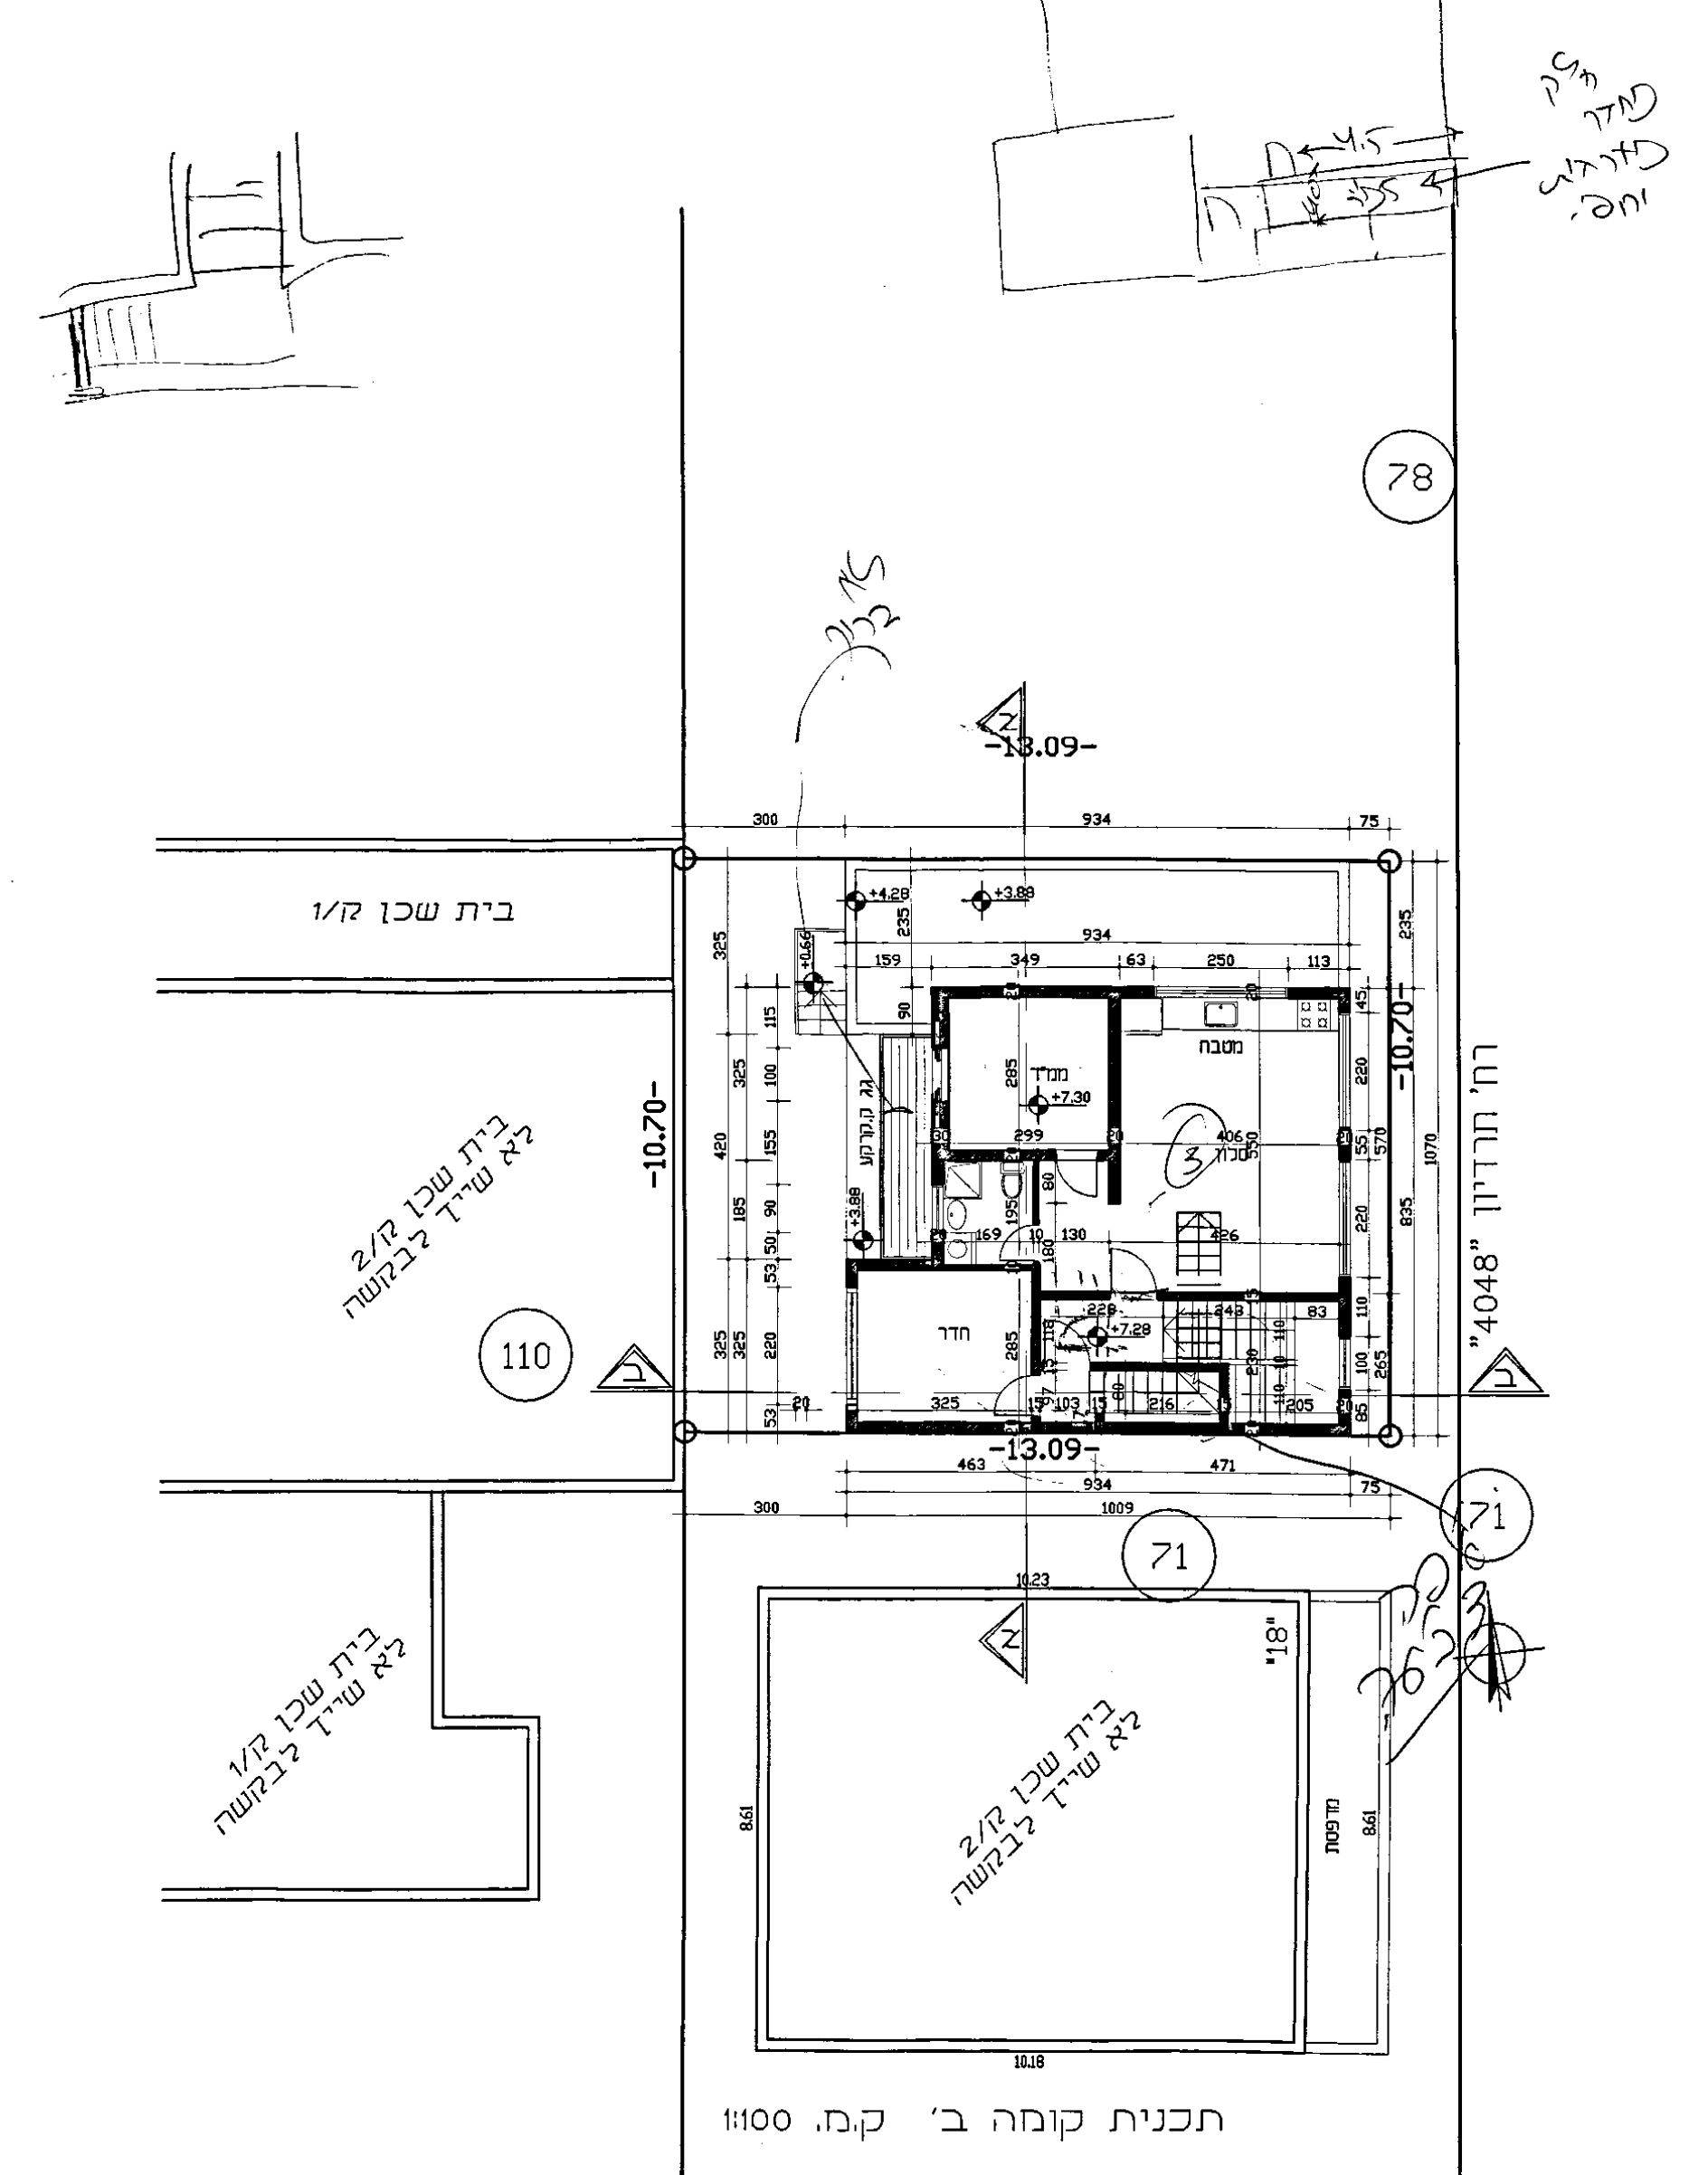
78
-13.09-
בית שכן ק/1
ממ"ד
מטבח
סלון
חדר
+7.30
+7.20
-10.70-
110
71
בית שכן ק/2 לא שייך לבקשה
בית שכן ק/1 לא שייך לבקשה
"18"
מרפסת
רח' תרדיון "4048"

תכנית קומה ב' ק.מ. 1:100

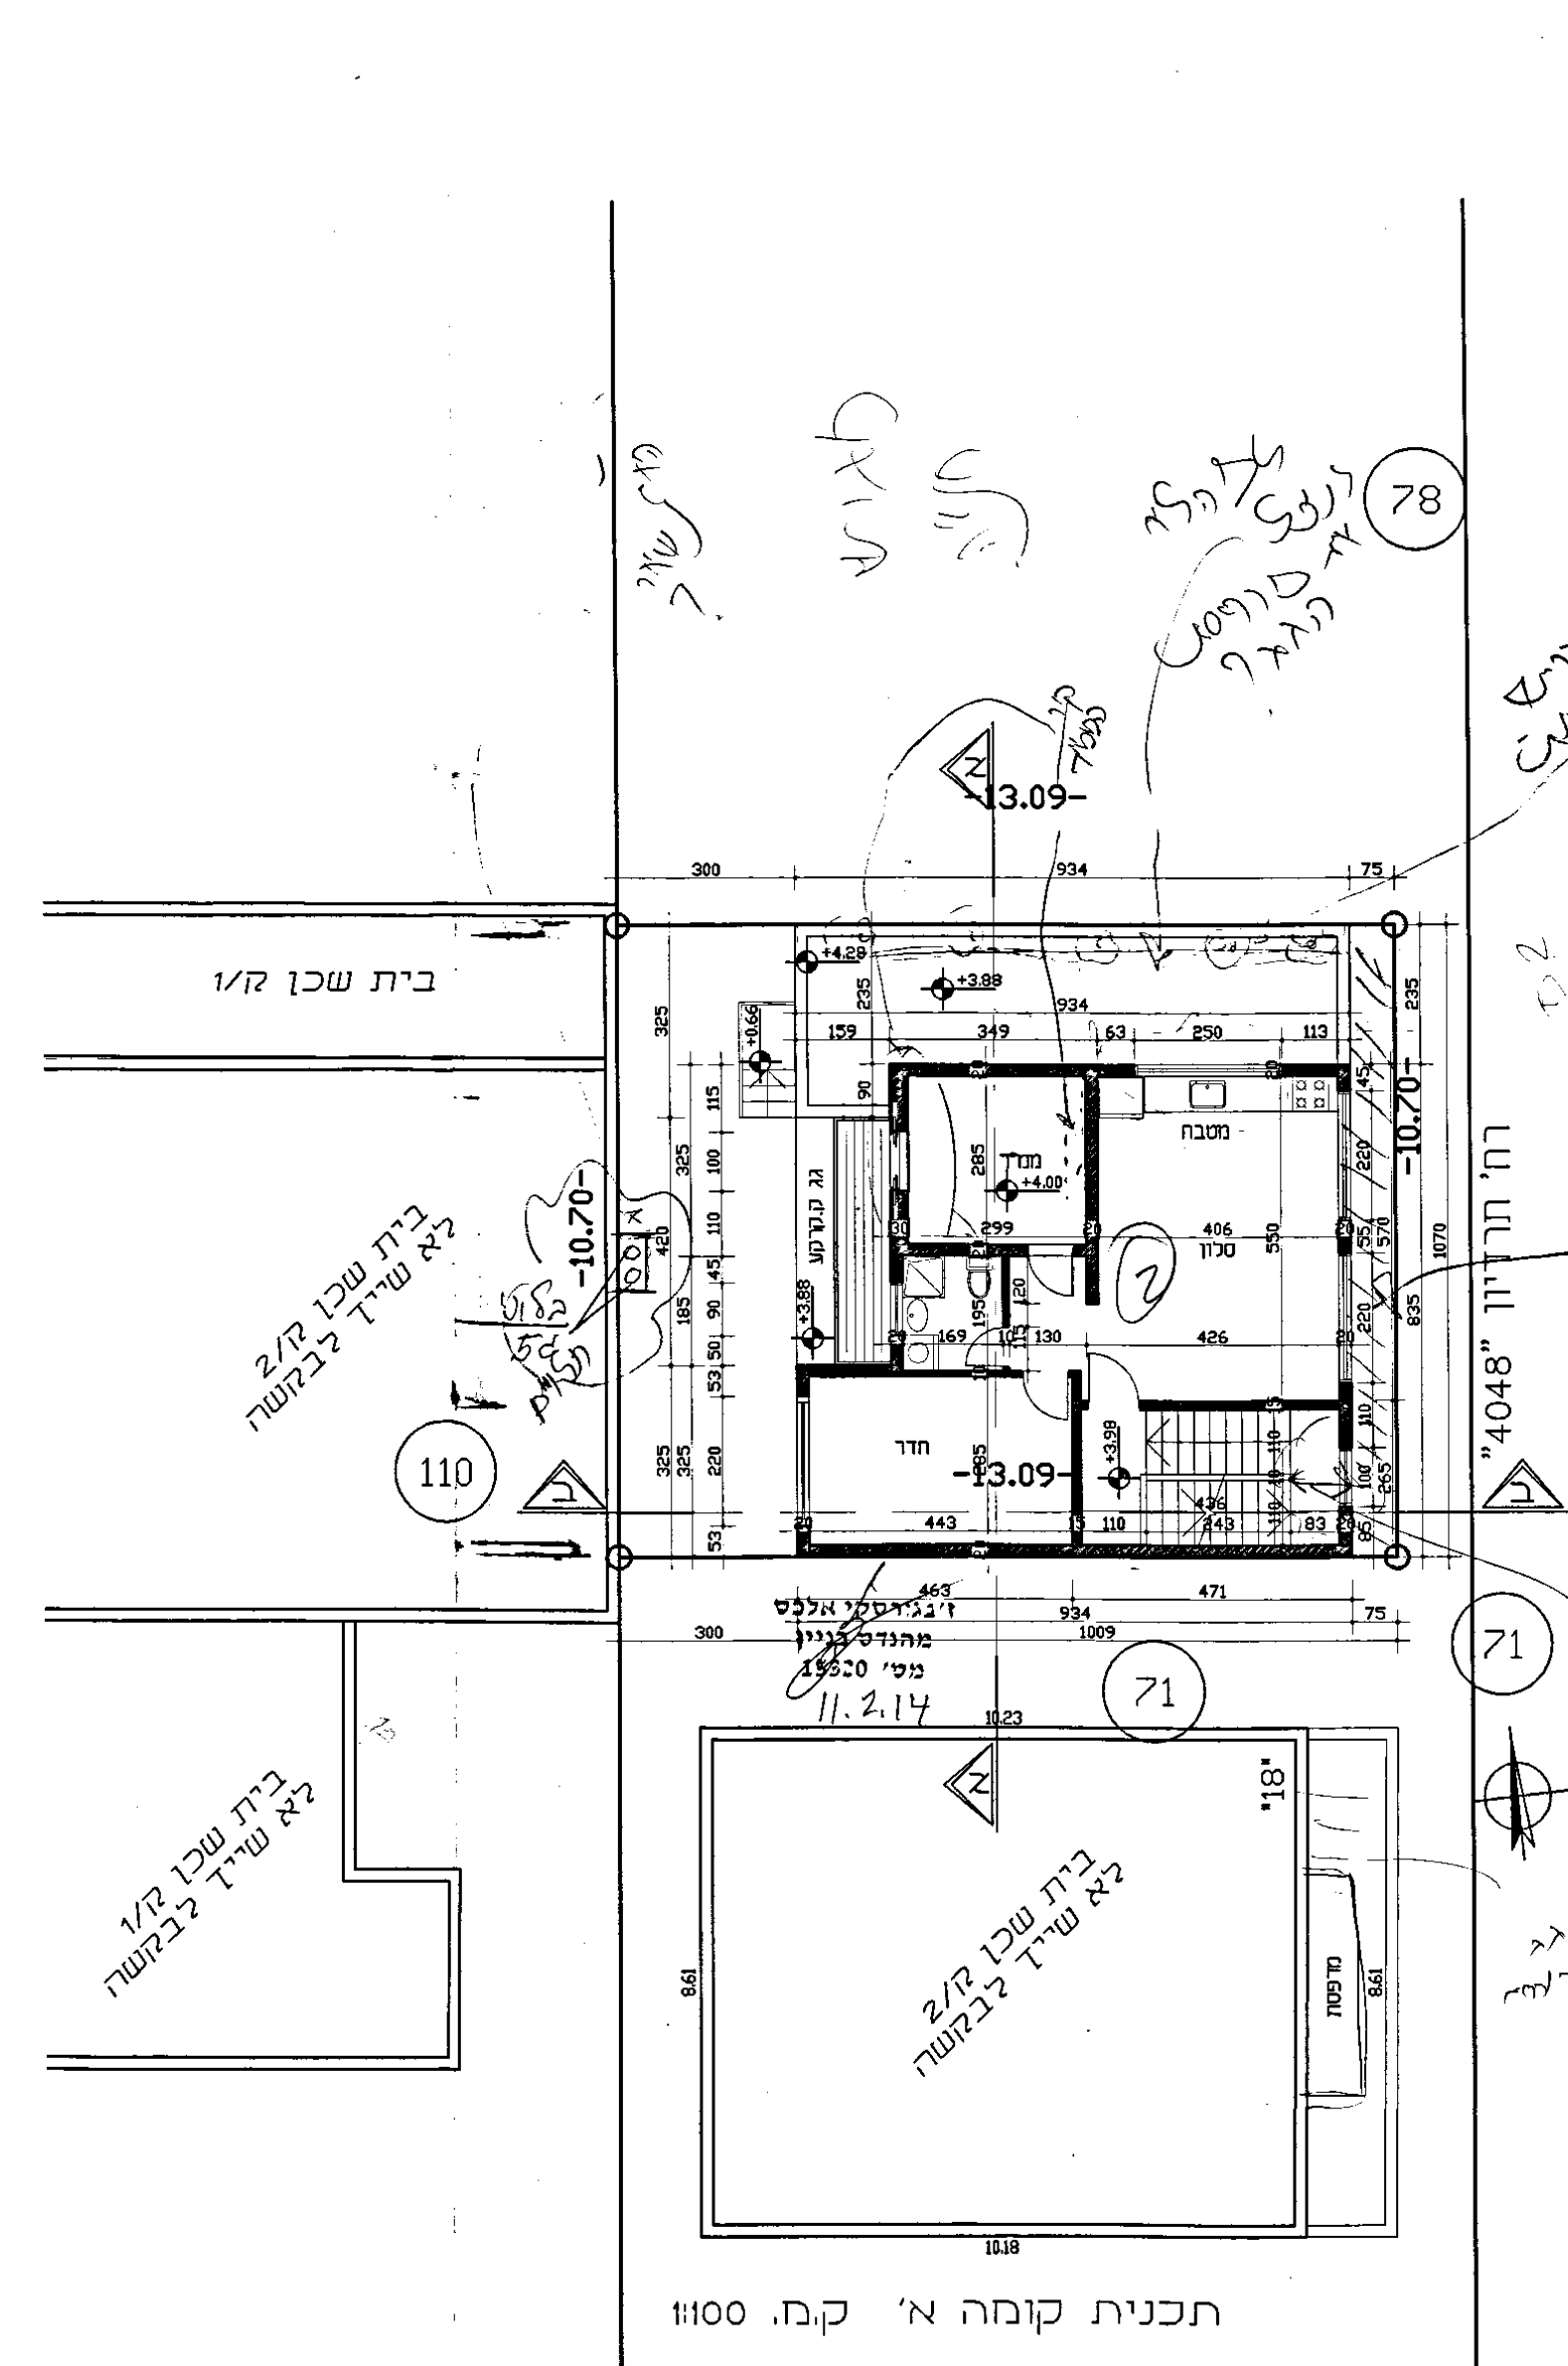
78
-13.09-
בית שכן ק/1
ממ"ד
מטבח
סלון
חדר
+4.00
-10.70-
110
71
ז'בגורסקי אלכס
מהנדס בניין
מס' 15320
11.2.14
בית שכן ק/2 לא שייך לבקשה
בית שכן ק/1 לא שייך לבקשה
"18"
מרפסת
רח' תרדיון "4048"

תכנית קומה א' ק.מ. 1:100

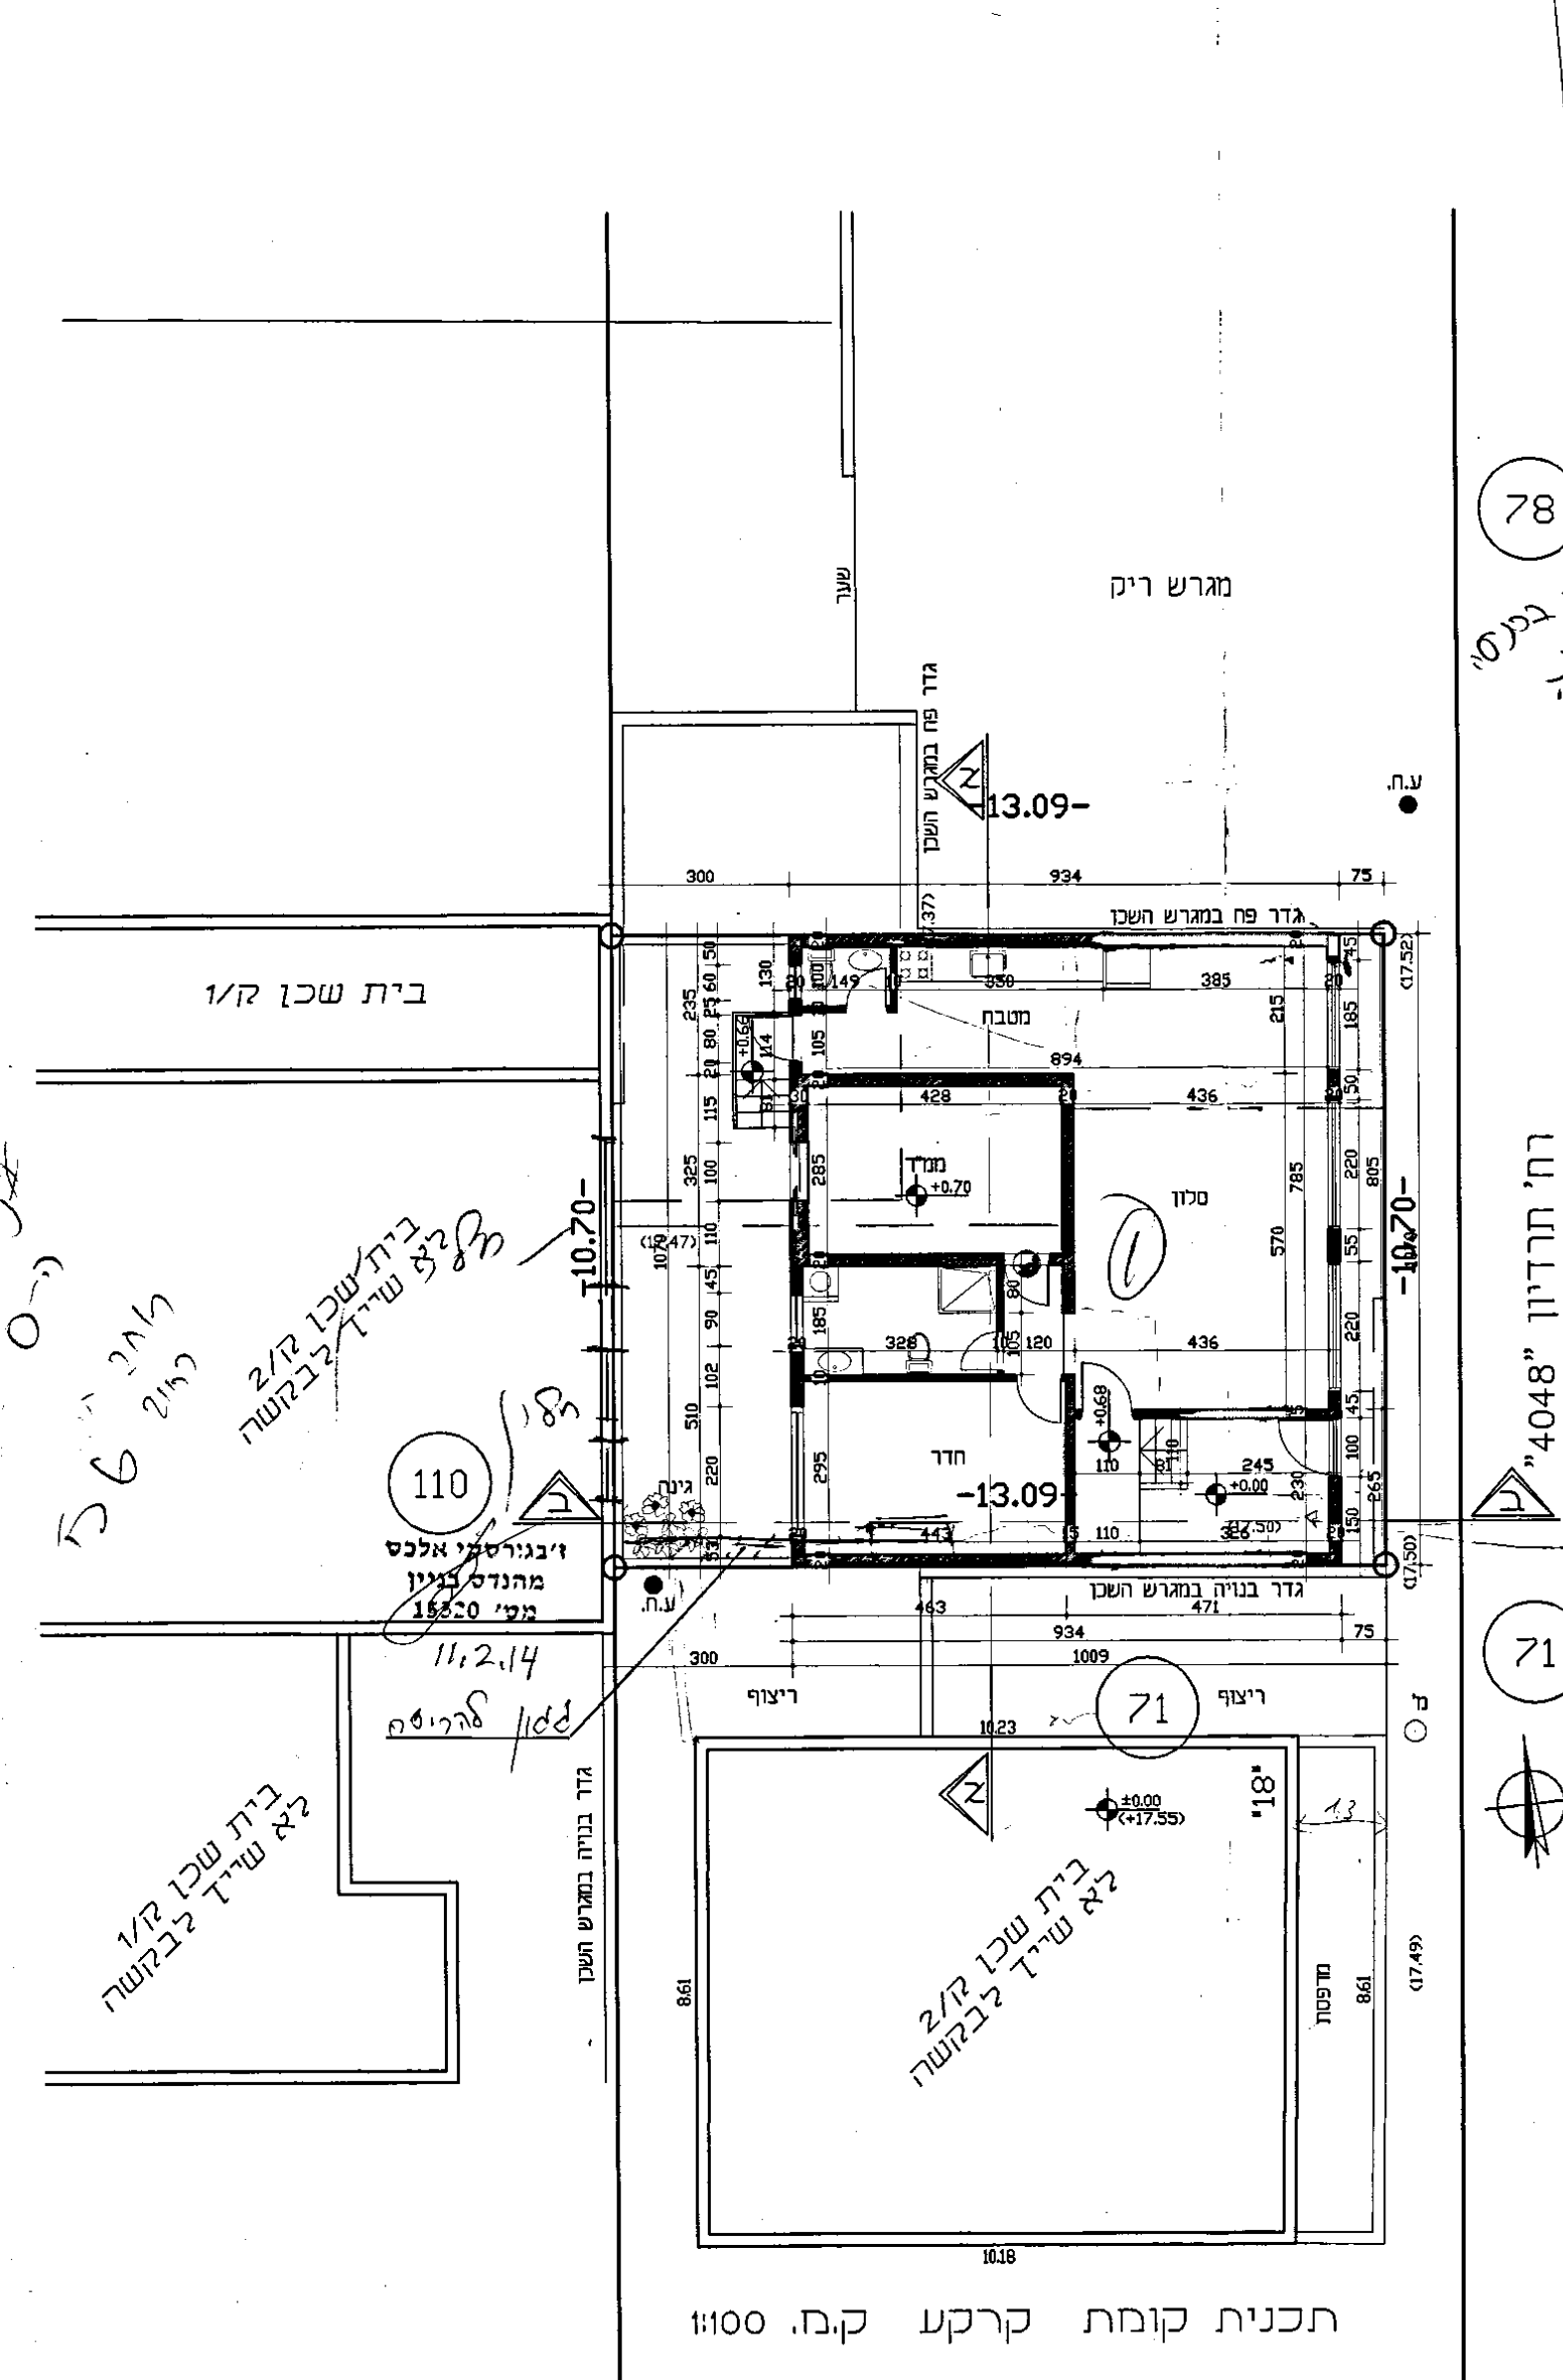
78
מגרש ריק
גדר פח במגרש השכן
-13.09-
ע.ח.
בית שכן ק/1
ממ"ד
מטבח
סלון
חדר
±0.00
-10.70-
110
71
גדר בנויה במגרש השכן
ריצוף
11.2.14
בית שכן ק/2 לא שייך לבקשה
בית שכן ק/1 לא שייך לבקשה
"18"
מרפסת
רח' תרדיון "4048"
אספלט

תכנית קומת קרקע ק.מ. 1:100

3.25x3.5 = 11.3 מ"ר

שטח דירה 3:

57.4-11.3 = 46. מ"ר

חישוב שטחים

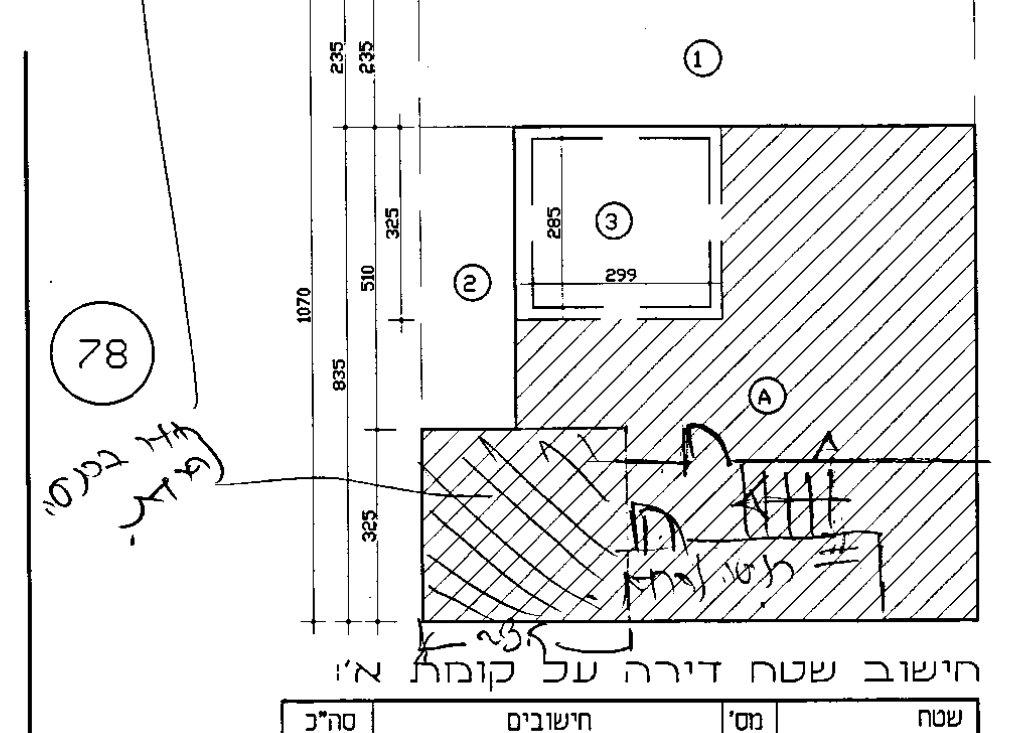
934
159
775
349
426
235
325
510
835
1070
1
2
3
285
299
A

חישוב שטח דירה על קומת א':

סה"כ מ"ר	חישובים	מס'	שטח
99.94	9.34 x 10.70	⊕	המסגרת
21.95	9.34 x 2.35	⊖	①
8.11	1.59 x 5.10	⊖	②
11.34	3.49 x 3.25	⊖	③ שטח ממ"ד
41.40	21.95 + 8.11 + 11.34		סה"כ ההורדות
58.54	99.94 - 41.40		Ⓐ שטח עיקרי

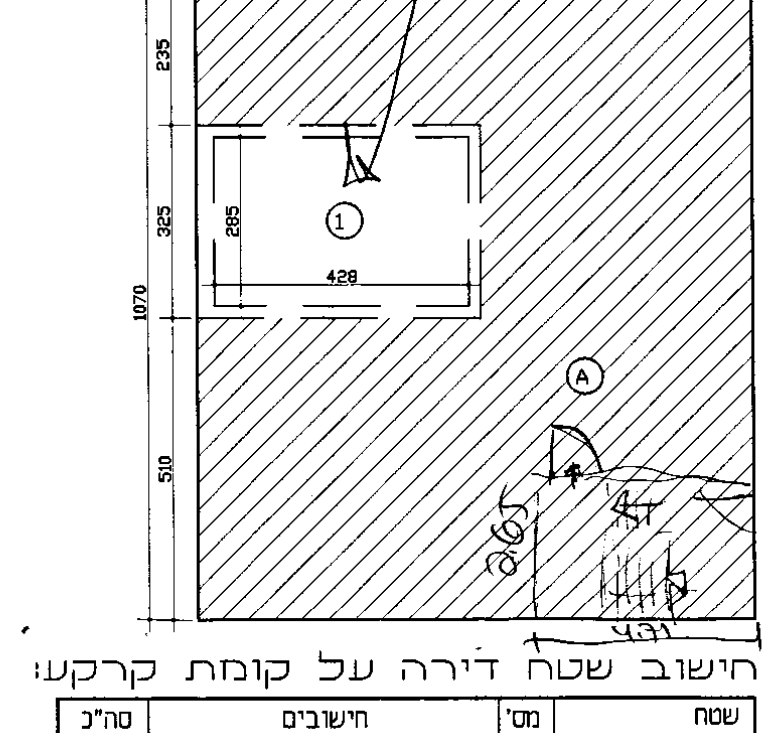
934
478
456
235
325
510
1070
285
428
1
A

חישוב שטח דירה על קומת קרקע:

סה"כ מ"ר	חישובים	מס'	שטח
99.94	9.34 x 10.70	⊕	המסגרת
12.00	12.00	⊖	① שטח ממ"ד
87.94	99.94 - 12.00		Ⓐ שטח עיקרי

2.65x4.31 = 10.484 חדר כביסה

שטח ... 87.5 מ"ר

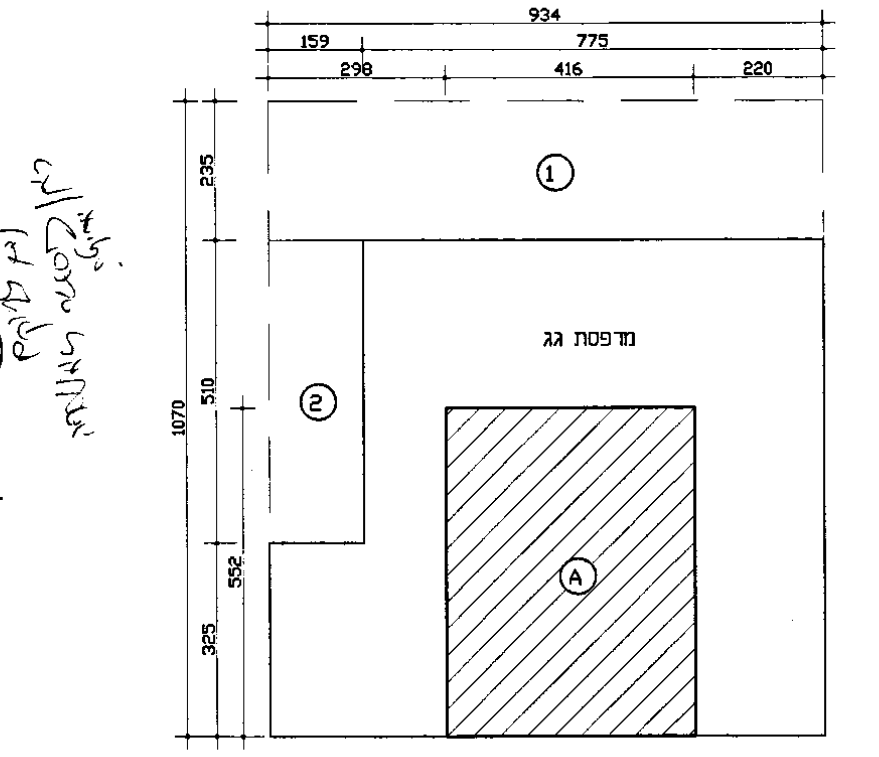
934
159
775
298
416
220
235
510
552
325
1070
1
2
מרפסת גג
A

חישוב שטח דירה בחדר על הגג:

סה"כ מ"ר	חישובים	מס'	שטח
99.94	9.34 x 10.70	⊕	המסגרת
21.95	9.34 x 2.35	⊖	①
8.11	1.59 x 5.10	⊖	②
30.06	21.95 + 8.11		סה"כ ההורדות
69.88	99.94 - 30.06		שטח גג
22.96	4.16 x 5.52		Ⓐ שטח עיקרי
46.92	69.88 - 22.96		מרפסת גג

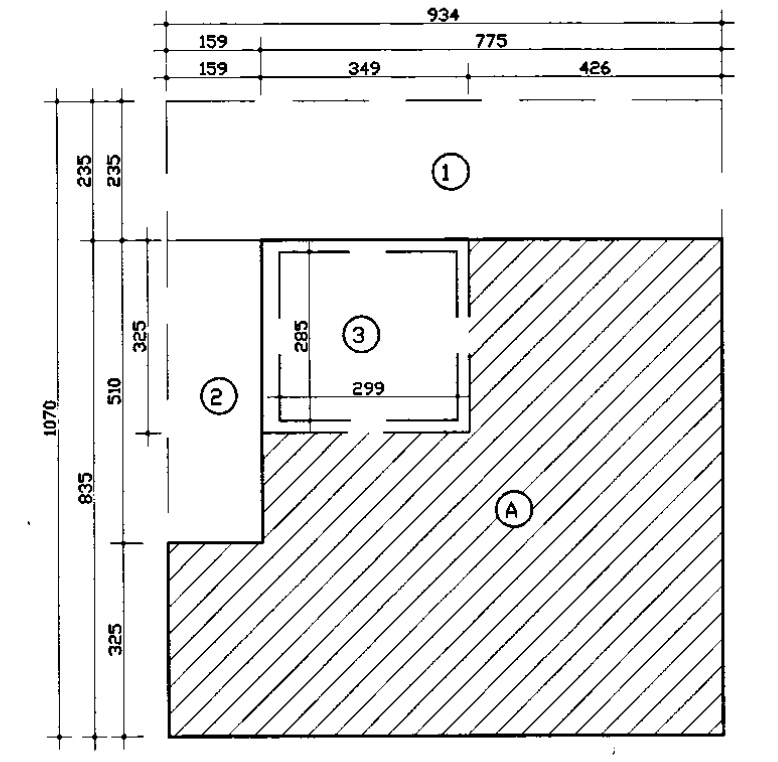
934
159
775
349
426
235
325
510
835
1070
285
299
1
2
3
A

חישוב שטח דירה על קומת ב':

סה"כ מ"ר	חישובים	מס'	שטח
99.94	9.34 x 10.70	⊕	המסגרת
21.95	9.34 x 2.35	⊖	①
8.11	1.59 x 5.10	⊖	②
11.34	3.49 x 3.25	⊖	③ שטח ממ"ד
41.40	21.95 + 8.11 + 11.34		סה"כ ההורדות
58.54	99.94 - 41.40		Ⓐ שטח עיקרי

מפה טופוגרפית

קנ"מ 1 : 250

תל-אביב
גוש : 6135
חלקה : 71 (חלק)
כתובת : רחי תרדיון, 16
הוכן עבור : כבאז תומר
מטרת המדידה: הגדרת מגרש משני עפ"י תב"ע 2215

שם הבעלים כרשום בנסח טאבו+מס' ת.ז : מלחי שמעון

שטח לפי נסח :
שטח החלקה כולה : 1.991 ד.מ.
בעלות בחלקים(כרשום בנסח טאבו) : מלחי שמעון 140/1991

בעלות במ"ר : 140
שטח מדוד(מ"ר) : 140

שטח מגרש משני : ד.מ.
שטח גריעה : ד.מ.

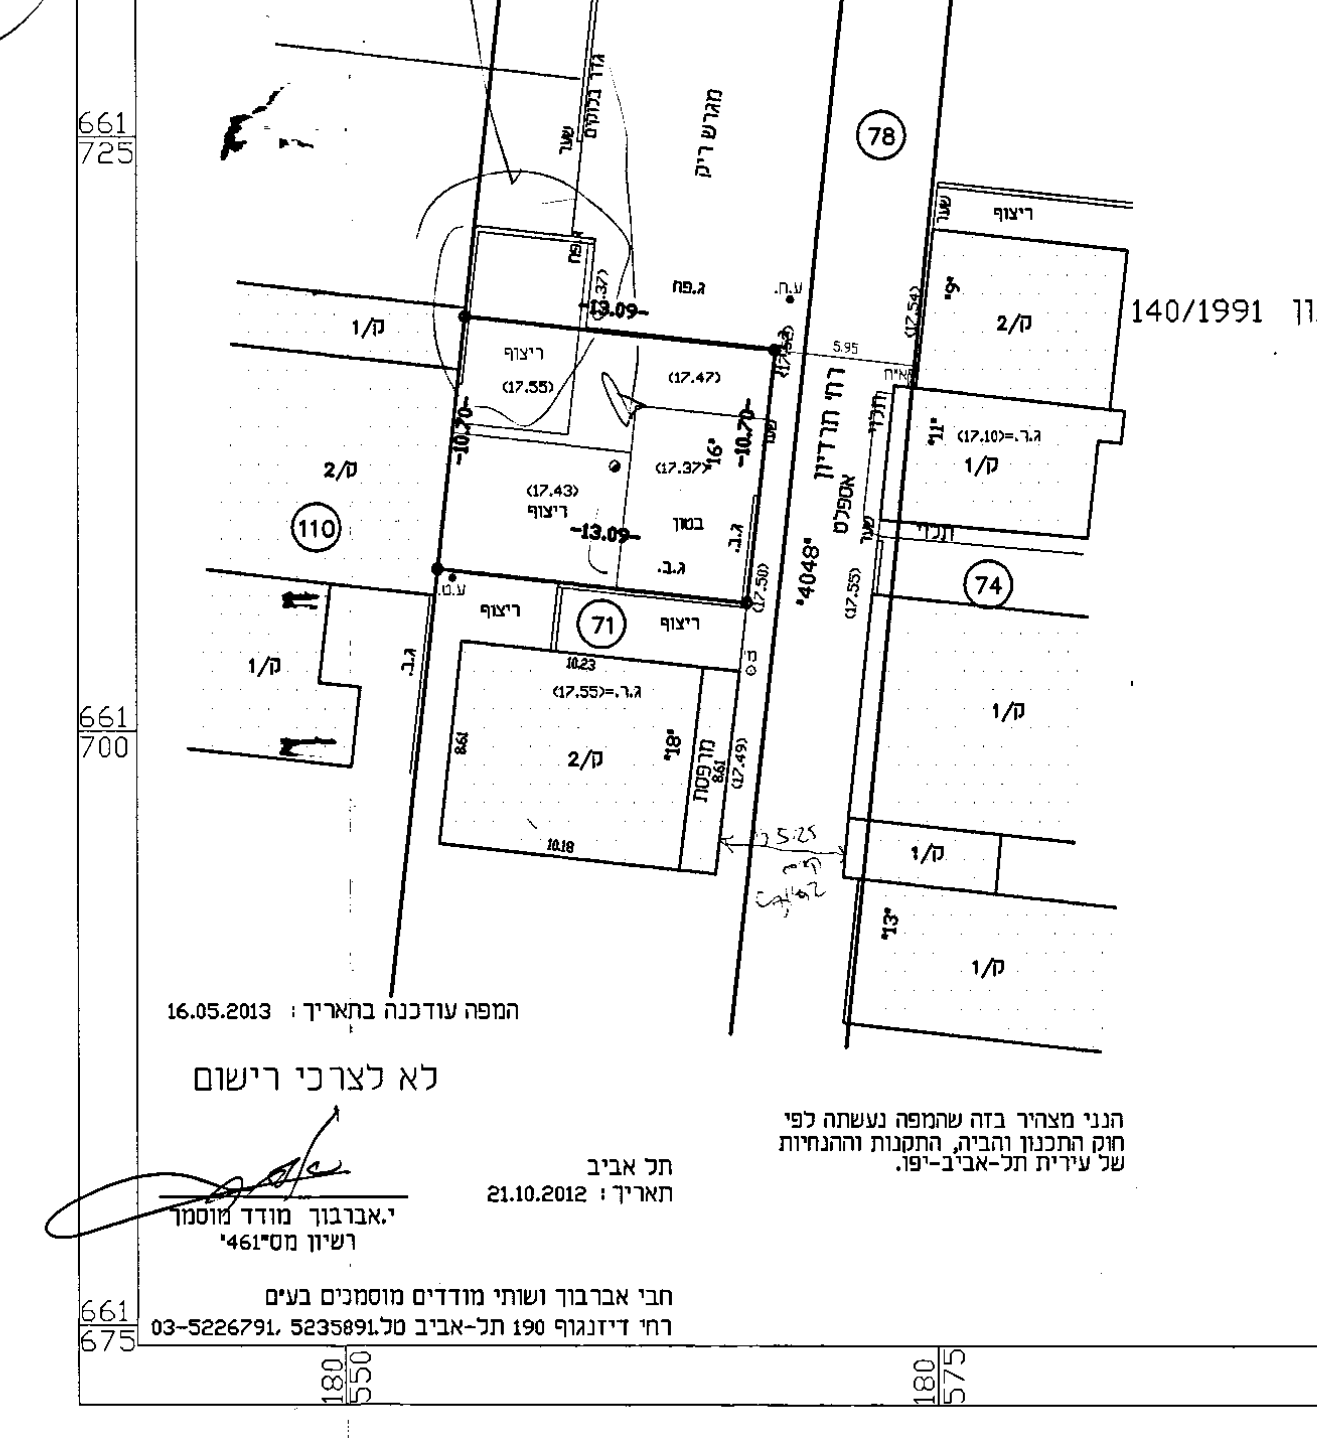
661 725
661 700
661 675
180 550
180 575
180 600
180 625
גדר במקום
שער
מגרש ריק
78
ע.ח.
ג.פח
-13.09-
-10.70-
ריצוף
(17.55)
(17.47)
(17.43)
(17.37)
בטון
"16"
110
71
74
2/ק
1/ק
רח' תרדיון "4048"
אספלט
"18"
"13"
מרפסת
10.23
10.18
8.61

המפה עודכנה בתאריך : 16.05.2013

לא לצרכי רישום

י.אברבוך מודד מוסמך
רשיון מס' 461

תל אביב
תאריך : 21.10.2012

הנני מצהיר בזה שהמפה נעשתה לפי חוק התכנון והביה, התקנות וההנחיות של עיריית תל-אביב-יפו.

חבי אברבוך ושותי מודדים מוסמכים בעים
רחי דיזנגוף 190 תל-אביב טל. 03-5226791, 5235891

תרשים הסביבה 1:1250

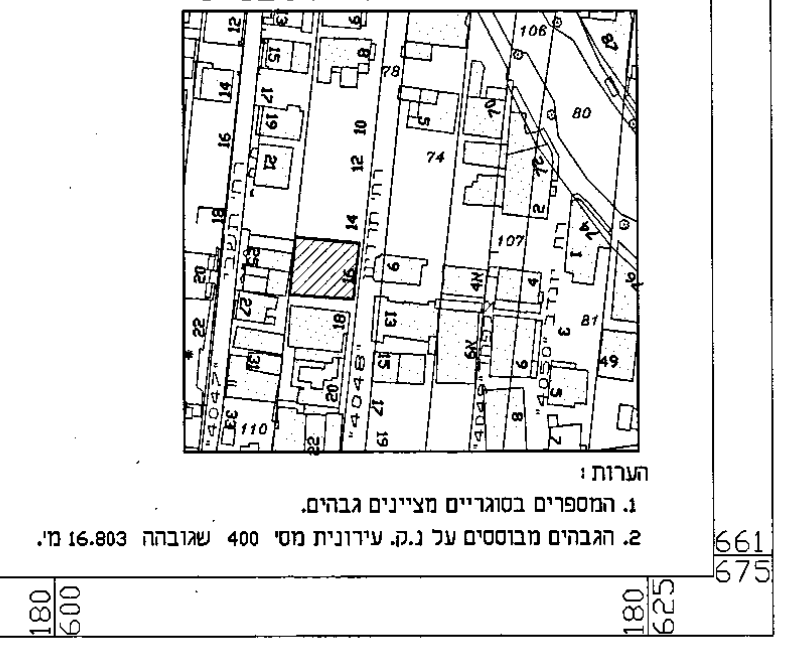
106
80
74
107
81
49
110
78
4048

הערות:
1. המספרים בסוגריים מציינים גבהים.
2. הגבהים מבוססים על נ.ק. עירונית מס' 400 שגובהה 16.803 מ'.

11/02/2014

סיכום בדיקה תחנה פיקוח בניה בקשה 20140311 לכתובת תרדיון 16

החלטת תחנה מ-11/02/2014 : תוכנית תואמת את המצב בשטח

תוכנית תואמת את המצב בשטח המבוקש טרם נהרס, טרם בנוי

מטפל: אלי פארי

פארד אלי
מפקח ראשי - מח' פקוח בנייה
מינהל הנדסה
עיריית תל-אביב-יפו

05-02-2014

22

מסמך מקור באיכות נמוכה

152381

2014-0311

נסרק

עיריית תל-אביב-יפו

מינהל ההנדסה, אגף רישוי ופיקוח על הבנייה
שדרות בן-גוריון 68 תל-אביב 64514 (פקס 5231340) טלפון 5217120, 5217045

לכבוד:
☒ הוועדה המקומית לתכנון ולבנייה
☐ רשות הרישוי המקומית

חוק התכנון והבניה, התשכ"ה-1965
תקנות התכנון והבנייה (בקשה להיתר תנאיו ואגרות) התש"ל-1970

בקשה להיתר בנייה או לשימוש במקרקעין-בניין חדש

יש להקפיד למלא את כל הפרטים בטופס הבקשה ולצרף מסמכים כמפורט ברשימת התיוג המצורפת.

טופס 1 תקנה 2(א)

מס' תיק הבניין	מס' בקשה קודמת להיתר בנייה	מס' הבקשה למידע	מתאריך
4048-016		2013-01039	02/07/2013

א. פרטי הנכס והמבקשים

הכתובת	רחוב	מס' בית	גוש	חלקה	תת חלקה	מגרש	הוראות התכניות החלות על המקום
	תרדיון	16	6135	71			2215, ג

פרטים אישיים	שם משפחה שם פרטי	שם חברה או תאגיד	מס' זהות/חברה או מס' רישום תאגיד	רחוב ומספר בית ישוב ומיקוד	מספר טלפון מספר פקס
מבקש 1	כבאז תומר נקים		024311235	תרדיון 18 ת"א-יפו	0548382700 0577519645 zivcom7@gmail.com
מבקש 2	שמאל חנה		02947371	תרדיון 18 ת"א-יפו	0548382700 zivcom7@gmail.com
מבקש 3					
בעל הזכות בנכס	כבאז תומר נקים ~~שמאל חנה~~			תרדיון 18 ~~ת"א-יפו~~	0548382700
החוכר					
עורך הבקשה הראשי	ז'בגורסקי אלכס		14687859	שבתאי 17 תל אביב-יפו	0522544457 03 9510030
מתכנן שלד הבניין	ז'בגורסקי אלכס		14687859	שבתאי 17 תל אביב-יפו	0522544457 03 9510030

ב. מהות הבקשה לבנייה חדשה

☐ הריסת מבנה קיים הכולל ____ קומות מגורים
☐ הקמת מבנה חדש הכולל: מרתף, 3 קומות וחדר על הגג
☐ מרתף/ים ☐ קומה מפולשת ☐ קומה מסחרית ל____
☒ 3 קומות מגורים ובהן 3 יחידות דיור משרדים
☐ המרתף/ים כולל/ים:
☒ מקלט ☒ מחסן ☐ חדרי עזר ☐
☒ קומת הקרקע כוללת: ☐ אולם כניסה ☐ חדר גז
☒ חדר אשפה ☐ חנויות ☐ מסעדה
☒ חדרי שירותים ☐ ☐
☒ על הגג: ☒ חדרי יציה ☐ חדרי מכונות ☐ קולטי שמש
☒ חדר מדרגות כללי ☐ פרגולה ☐
☐ בחצר: ☐ מקומות חניה ☐ גינה
☐ שטחים מרוצפים ☐ פרגולה
☐ בגבולות המגרש גדר בגובה ____ מטר
פירוט נוסף:

ג. מפרט - תיאור הבקשה

תיאור הקיים על המגרש: פרט מספר מבנים, גובהם, מקומם, ייעודם וכד' — קיים מגרש רק

שימוש עיקרי: ☒ מגורים ☐ משרדים ☐ מסחר ☐ מלונאות ☐ בידור ☐ נופש וספורט ☐ תעשיה ☐ בנין ציבורי ☐ שימוש אחר ☐ חקלאי ☐ מלאכה

סוג העבודה או השימושים המוצעים: ☐ הריסה ☒ בניין חדש

הגורם שמבוצעת בעבורו הבנייה: ☐ משרד ממשלתי ☐ רשות מקומית ☐ מוסד ציבורי ☒ גורם פרטי ☐ בנה ביתך ☐ אחר:

שטחים: שטח הבנייה הכולל המבוקש 262.66 מ"ר; שטח המגרש/החלקה 140 מ"ר; אחוזי הבנייה 187.61

ד. חומרי הבנייה

סוג הבנייה: ☒ רגילה ☐ בית מוכן ☐ מתועשת ☐ אחר
קירות חיצוניים: ☒ בטון מזוין ☐ בלוקים ☐ אבן טבעית ☐ לבנים שרופות ☐ אחר
חומרי גימור: ☐ אבן מלאכותית ☐ אבן טבעית ☒ טיח ☐ זכוכית ☐ אחר
תקרות: ☒ בטון מזוין ☐ עץ ☐ אחר
גג: ☒ בטון מזוין ☐ רעפים ☐ אסבסט ☐ טיח ☐ אחר
גדרות: ☐ אבן טבעית ☐ אבן מלאכותית ☐ בטון ☐ בלוקים ☐ ברזל ☐ עץ ☐ רשת ☐ אחר

ו. קווי בנייה

הכיוון	מוצע	מותר	במטר	ב-%
לרחוב (שם)	0,00	0,00		
לרחוב (שם)				
לצד	2,00	3,0		
לאחור	3,0	5,0		

ז. מספר יחידות דיור

אם השימוש המבוקש הוא מגורים - רשום להלן:
מספר הדירות המבוקשות: 3
מספר הדירות המותרות: 3

ה. השטחים המבוקשים לבנייה (על-פי תכנית הבנייה) והמותרים לבנייה (על-פי "אסמכתא": חוק, תקנות, תכנית) בכל מפלס בנפרד ולפי שימוש

הקומה/המפלס	מבוקש (1)	מותר (1)	מבוקש (2)	מותר (2)	מ"ר	%משטח המגרש	סך כל השטחים המותרים	ה"אסמכתא"	מקלט	מ"ר (שירות)	%משטח המגרש	מ"ר (סה"כ)	%משטח המגרש	משטחים לא מקורים
ק.קרקע +0.68	87.94	87,94			87.94	62.81		2215	12.00	12.00	8.57	99.94	71.39	
ק. א' +3.98	58.54	58,54			58.54	41.81		2215	11.34	11.34	8.10	69.88	49.91	
ק. ב' +7.28	58.54	58,54			58.54	41.81		2215	11.34	11.34	8.10	69.88	49.91	
גג +10.58	22.96	23,-			22.96	16.40		ג				22.96	16.40	
ס"ח מעל לקרקע	227.98	228,02			227.98	162.83			34.68	34.68	24.77	262.66	187.61	
ס"ח מתחת לקרקע														
סה"כ	227.98	228,02			227.98	162.83			34.68	34.68	24.77	262.66	187.61	

ט. הבקשה מוגשת לאישור

☐ הוועדה המקומית
☐ רשות הרישוי המקומית
☐ רשות הרישוי המקומית באמצעות מורשה להיתר

פירוט הבקשה להקלה / נימוקי הבקשה להקלה:
1. הקלה מקו בניין צדדי תכנוני
2. ... מפלס ...
3. הקלה 6% משטח המגרש

ח. פרטי הבנייה - לשימוש הלשכה המרכזית לסטטיסטיקה

היעוד	1
למגורים	1
להארחה	2
לעסקים ולמסחרים	3
לבנייני ציבור	4
לתעשייה ולמלאכה	5
למשק חקלאי	6
למקלט או למרתף	
למבני עזר	
סך כל שטח הבנייה	

יב. מינויים מטעם מבקש ההיתר

אני ממנה בזה את ז'בגורסקי אלכס בעל/ת מס' זהות 14687859 הרשום בסעיף א' להיות עורך הבקשה הראשי להיתר, ולייצגני לפני מוסדות התכנון והרשויות המוסמכות בכל הנוגע לטיפול בבקשה להיתר ולקבלתו, לרבות התיקונים בכל שידרשו הרשויות המוסמכות.

שם משפחה ושם פרטי	תחום פעולה	המען	מספר טלפון	מספר פקס
1.	מתכנן האינסטלציה הסניטרית			
2.				

אני ממנה בזה את ז'בגורסקי אלכס בעל/ת מס' זהות 14687859 הרשום בסע' א' להיות אחראי לתיכנון שלד הבניין שבעבורו מבוקש ההיתר, להגיש לוועדה המקומית לרשות הרישוי המקומית את החישובים לגבי הבניה שבעבורה מבוקש היתר ולפקח פיקוח עליון על הקמת השלד.

שם משפחה ושם פרטי	תחום פעולה	המען	מספר טלפון	מספר פקס
1.	אחראי ראשי			
2.				
3.				

חתימת המבקש על המינויים X

יג. הצהרות

אנו החתומים מטה מצהירים בזה:

	תאריך	שם משפחה ושם פרטי	מספר רישיון	חתימה
עורך בקשה ראשי		ז'בגורסקי אלכס	15320	
עורך בקשה 1 מתכ' האינס הסני'				
עורך בקשה 2				

אני החתום מטה ז'בגורסקי אלכס מס' זהות 14687859 מהנדס רשוי מס' 15320 מצהיר בזאת כדלקמן:

י. הצהרת עורך הבקשה הראשי

אני מצהיר על נכונות הפרטים בסעיפים א עד ס.
תאריך 11/2013 שם ז'בגורסקי א. חתימה X

יא. חתימות נוספות

	שם	תאריך	חתימה
המבקש	כבאז תומר נקים שמאל חנה	11/2013	X
בעל הזכות בנכס / בעל הנכס / החוכר	כבאז תומר נקים שמאל חנה	11/2013	
מתכנן שלד הבניין	ז'בגורסקי	11/2013	

אבנר גדי - ת"ז 024494718
מטפל בבקשה ליציאת קשר
052-2543212

נסרק