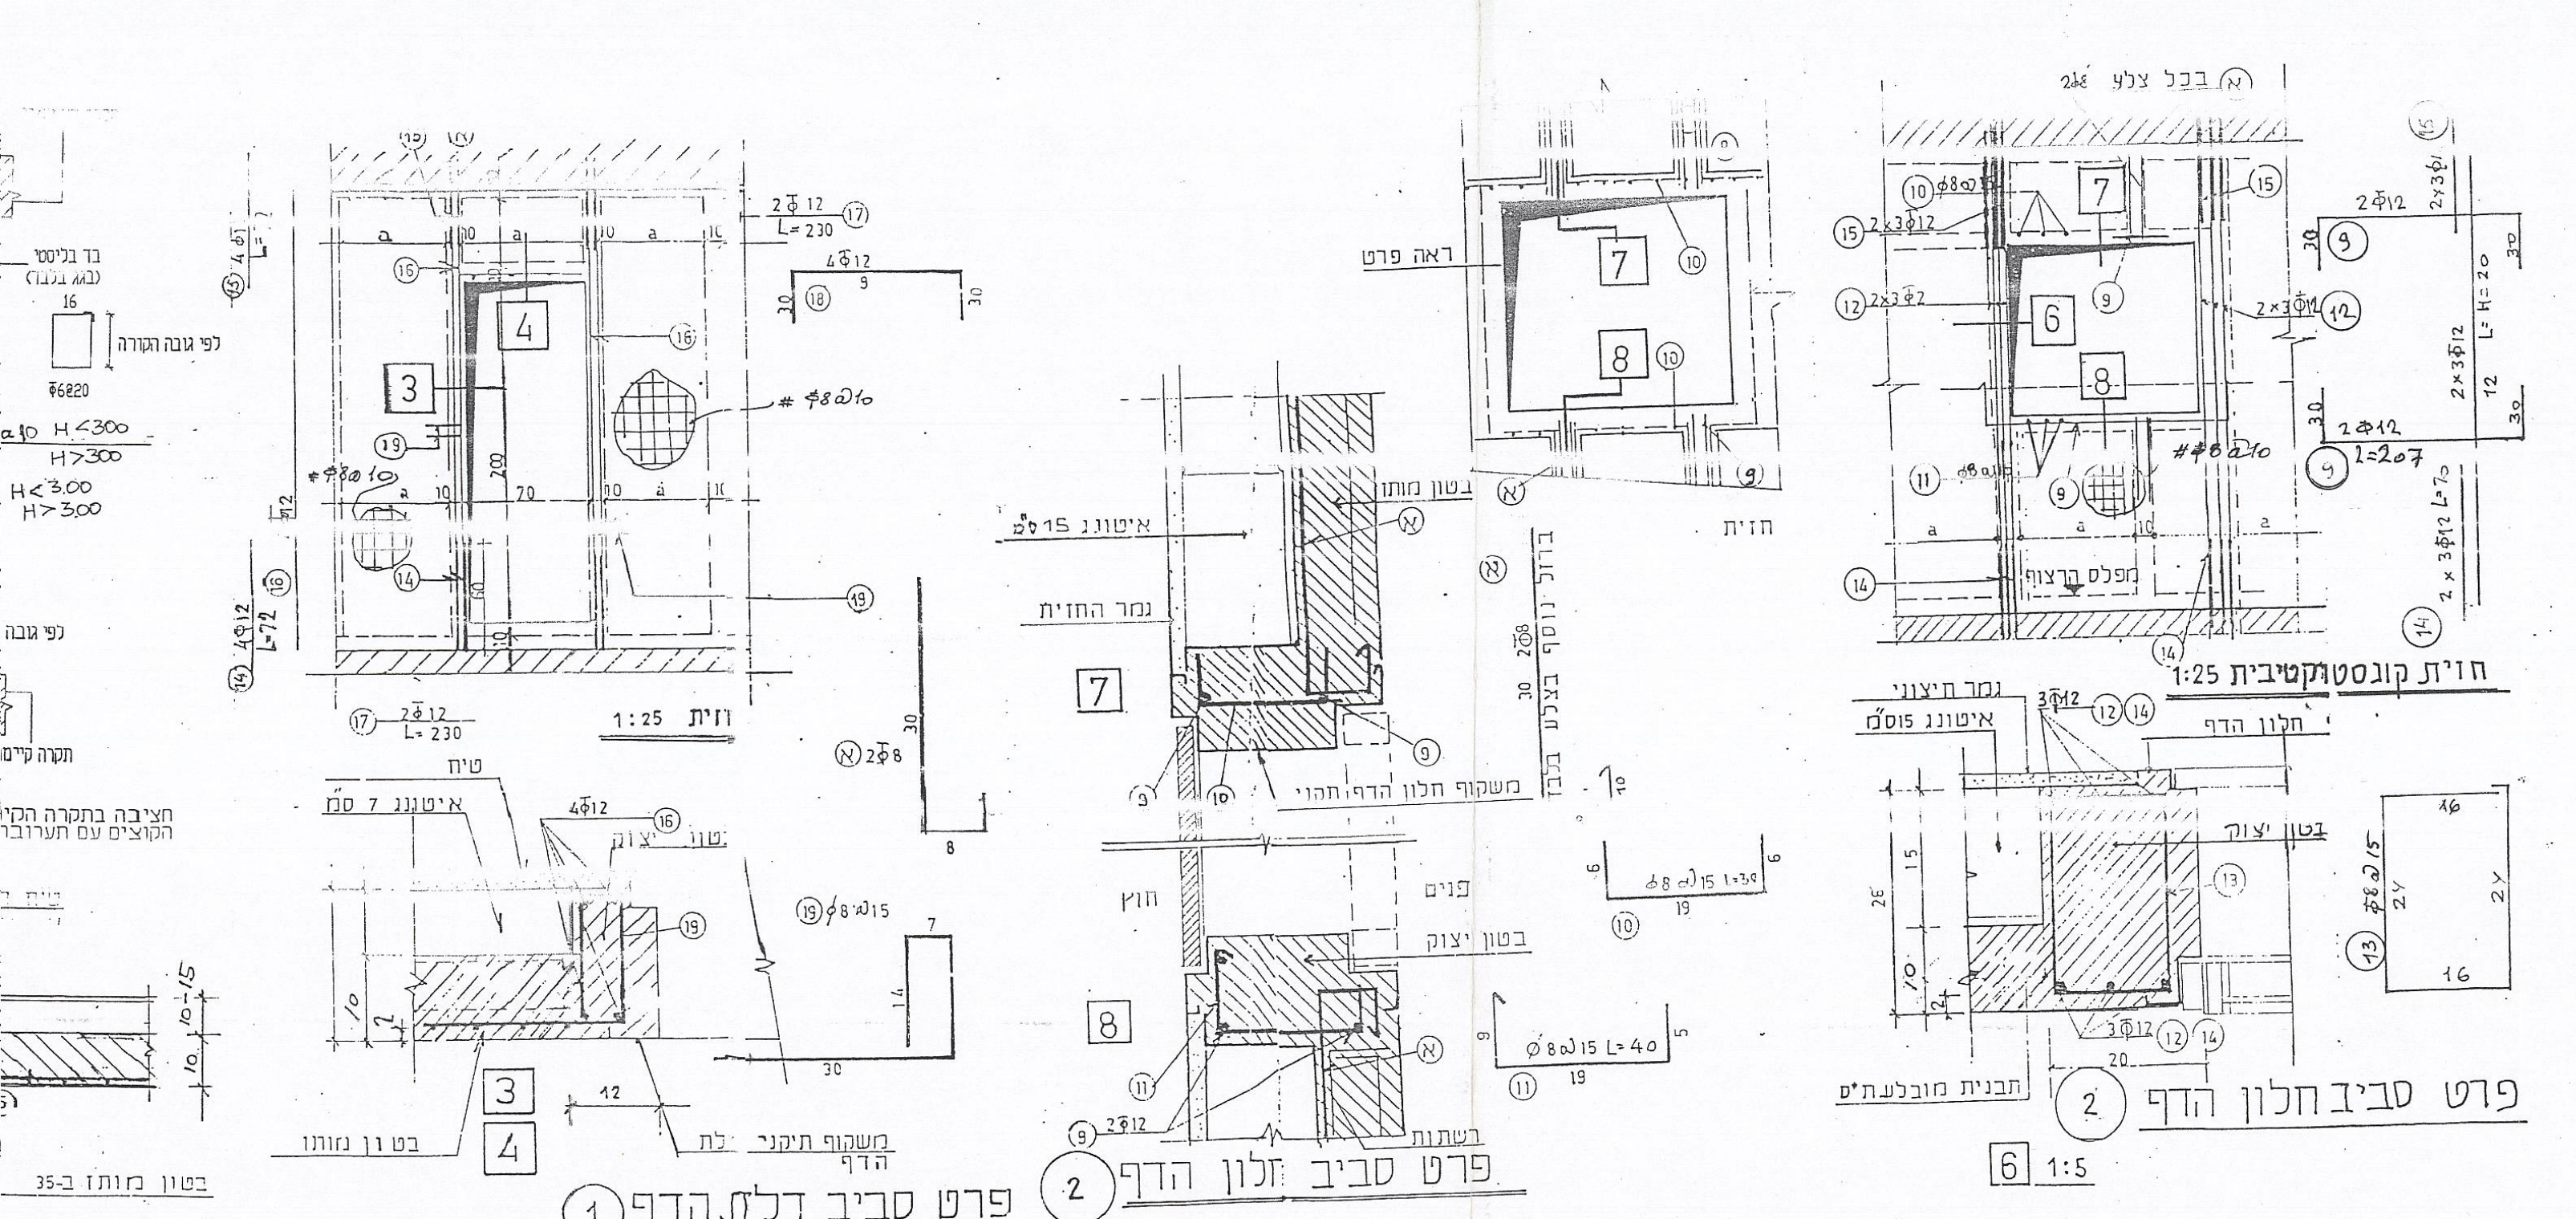

פרט סביב דלת הדף ①

פרט סביב חלון הדף ②

פרט סביב חלון הדף ②

6 1:5

פרטי קיר

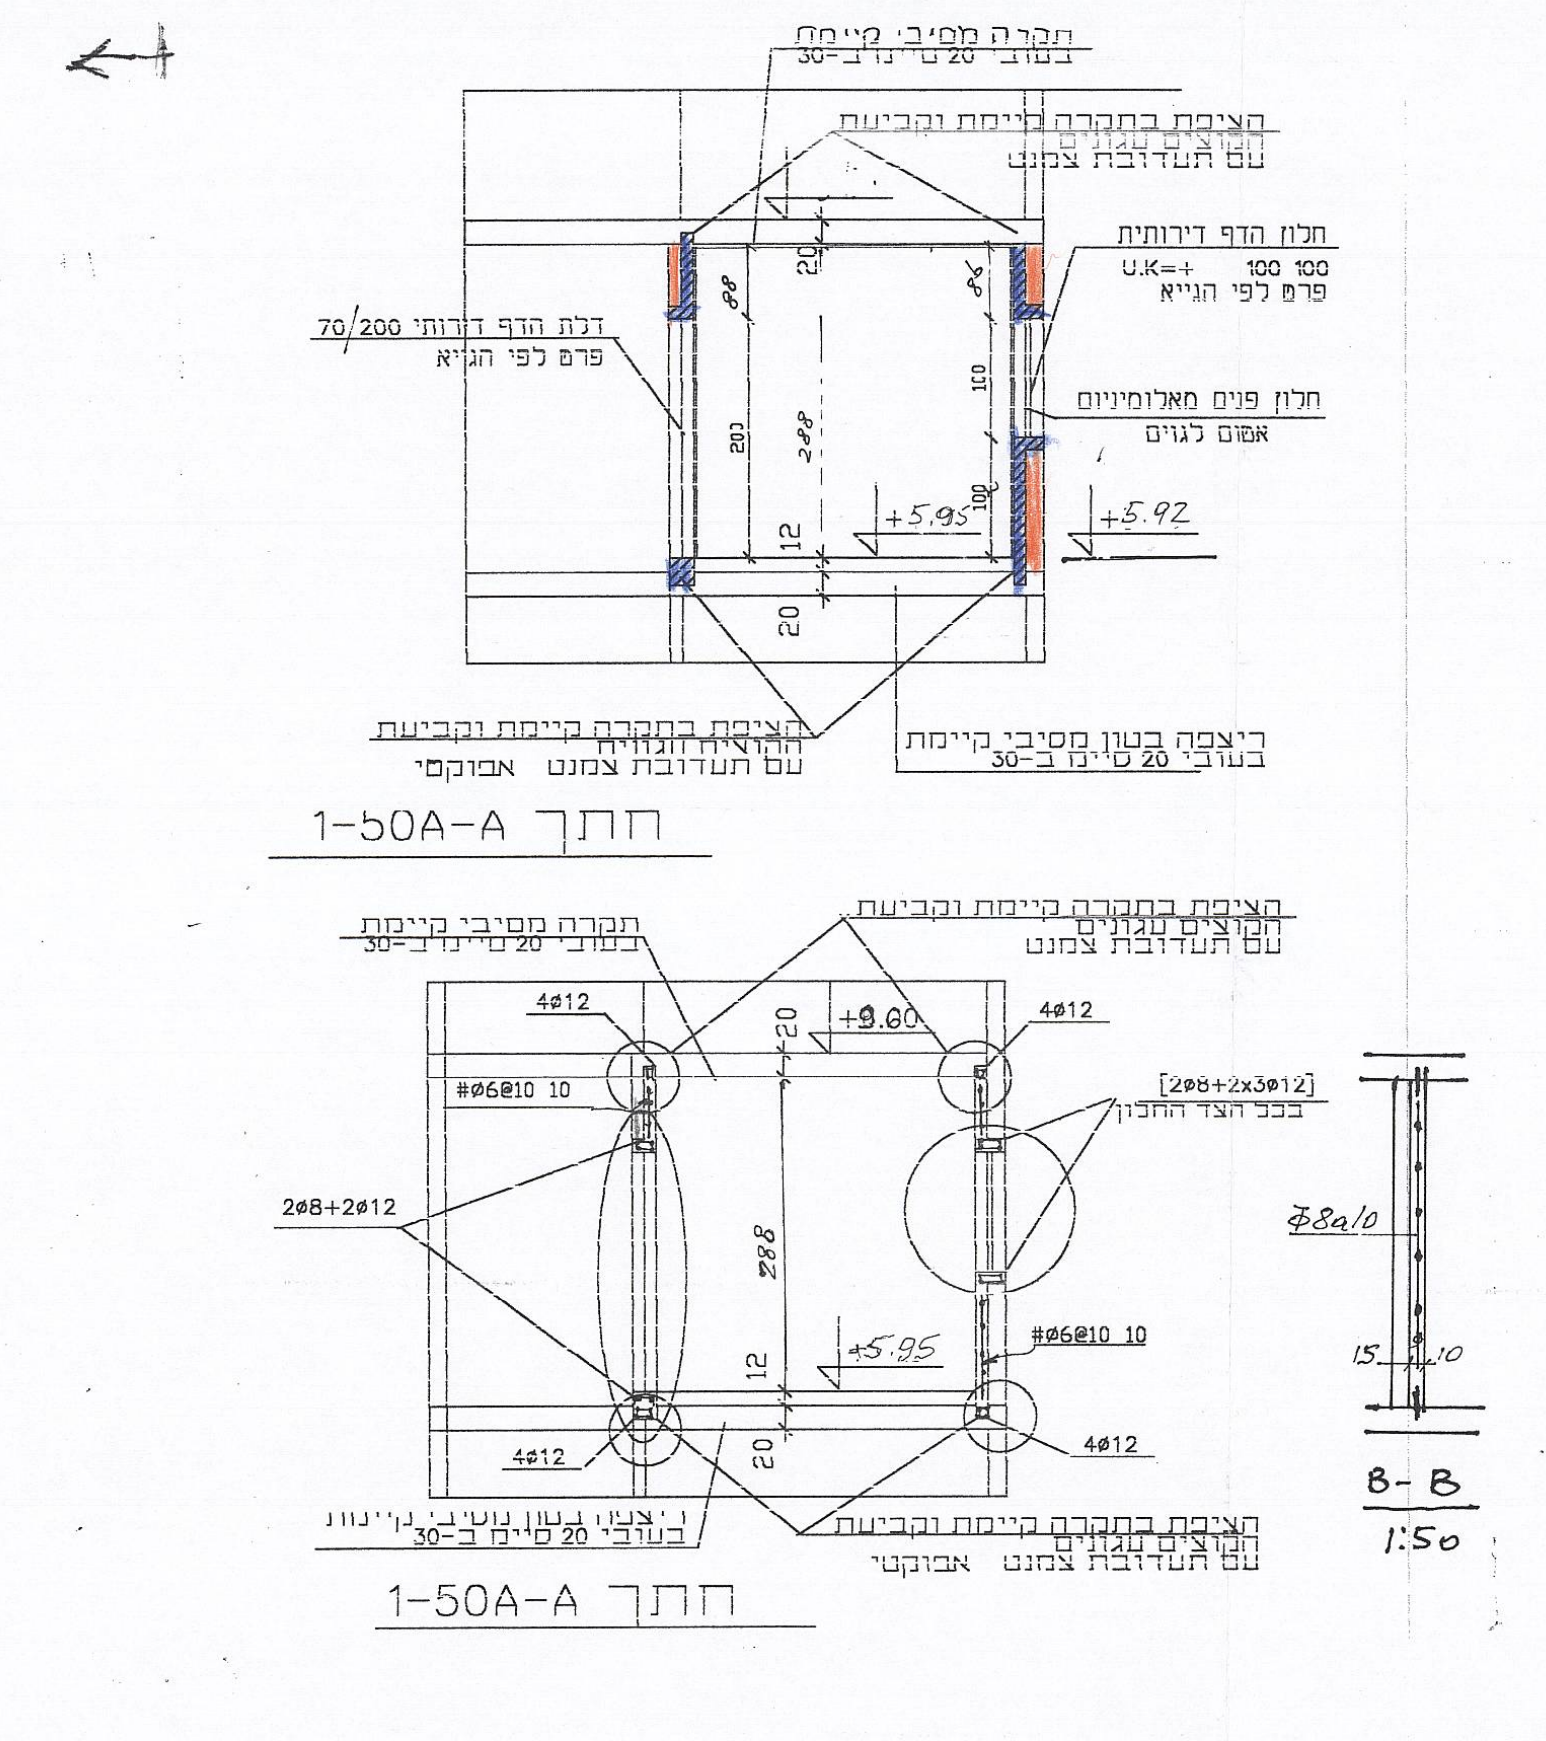

1-50A-A חתך

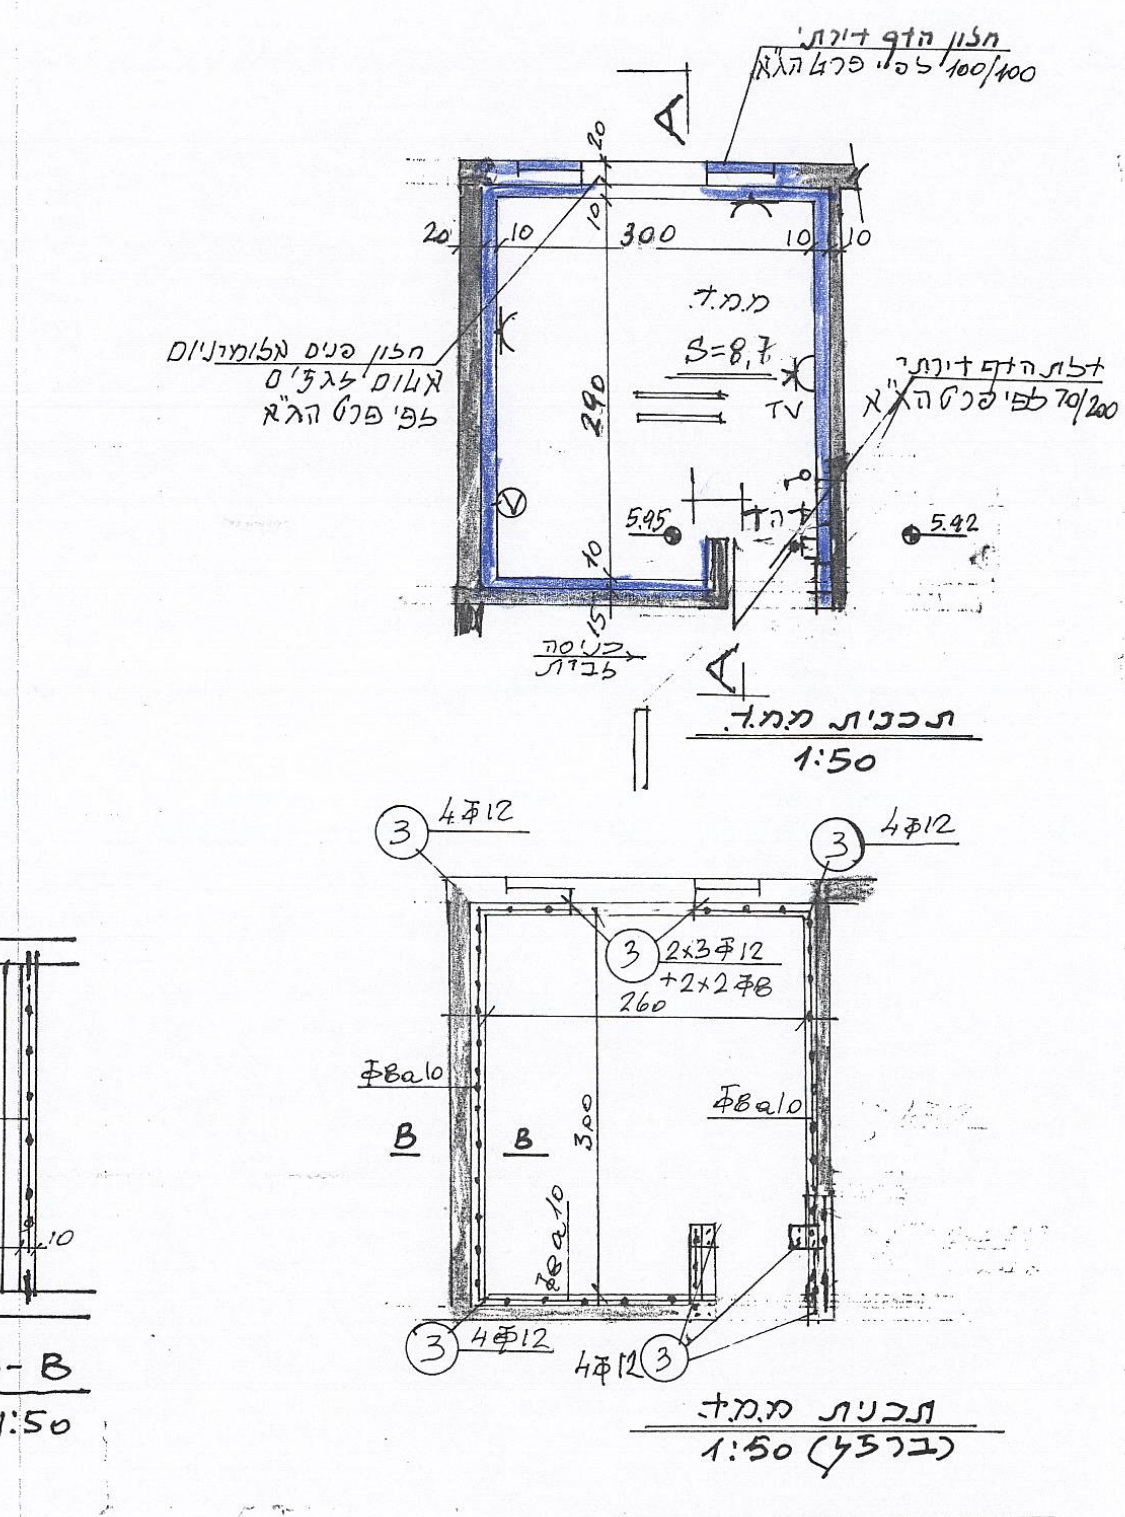

תכנית ממ"ד 1:50

	מקרא
○○	2 שקעי חשמל 220 וולט
◐	שקע מגוף חוץ
⊖	שקע מבודד
▬	גוף תאורה פלואורסנטי 2X36 וואט

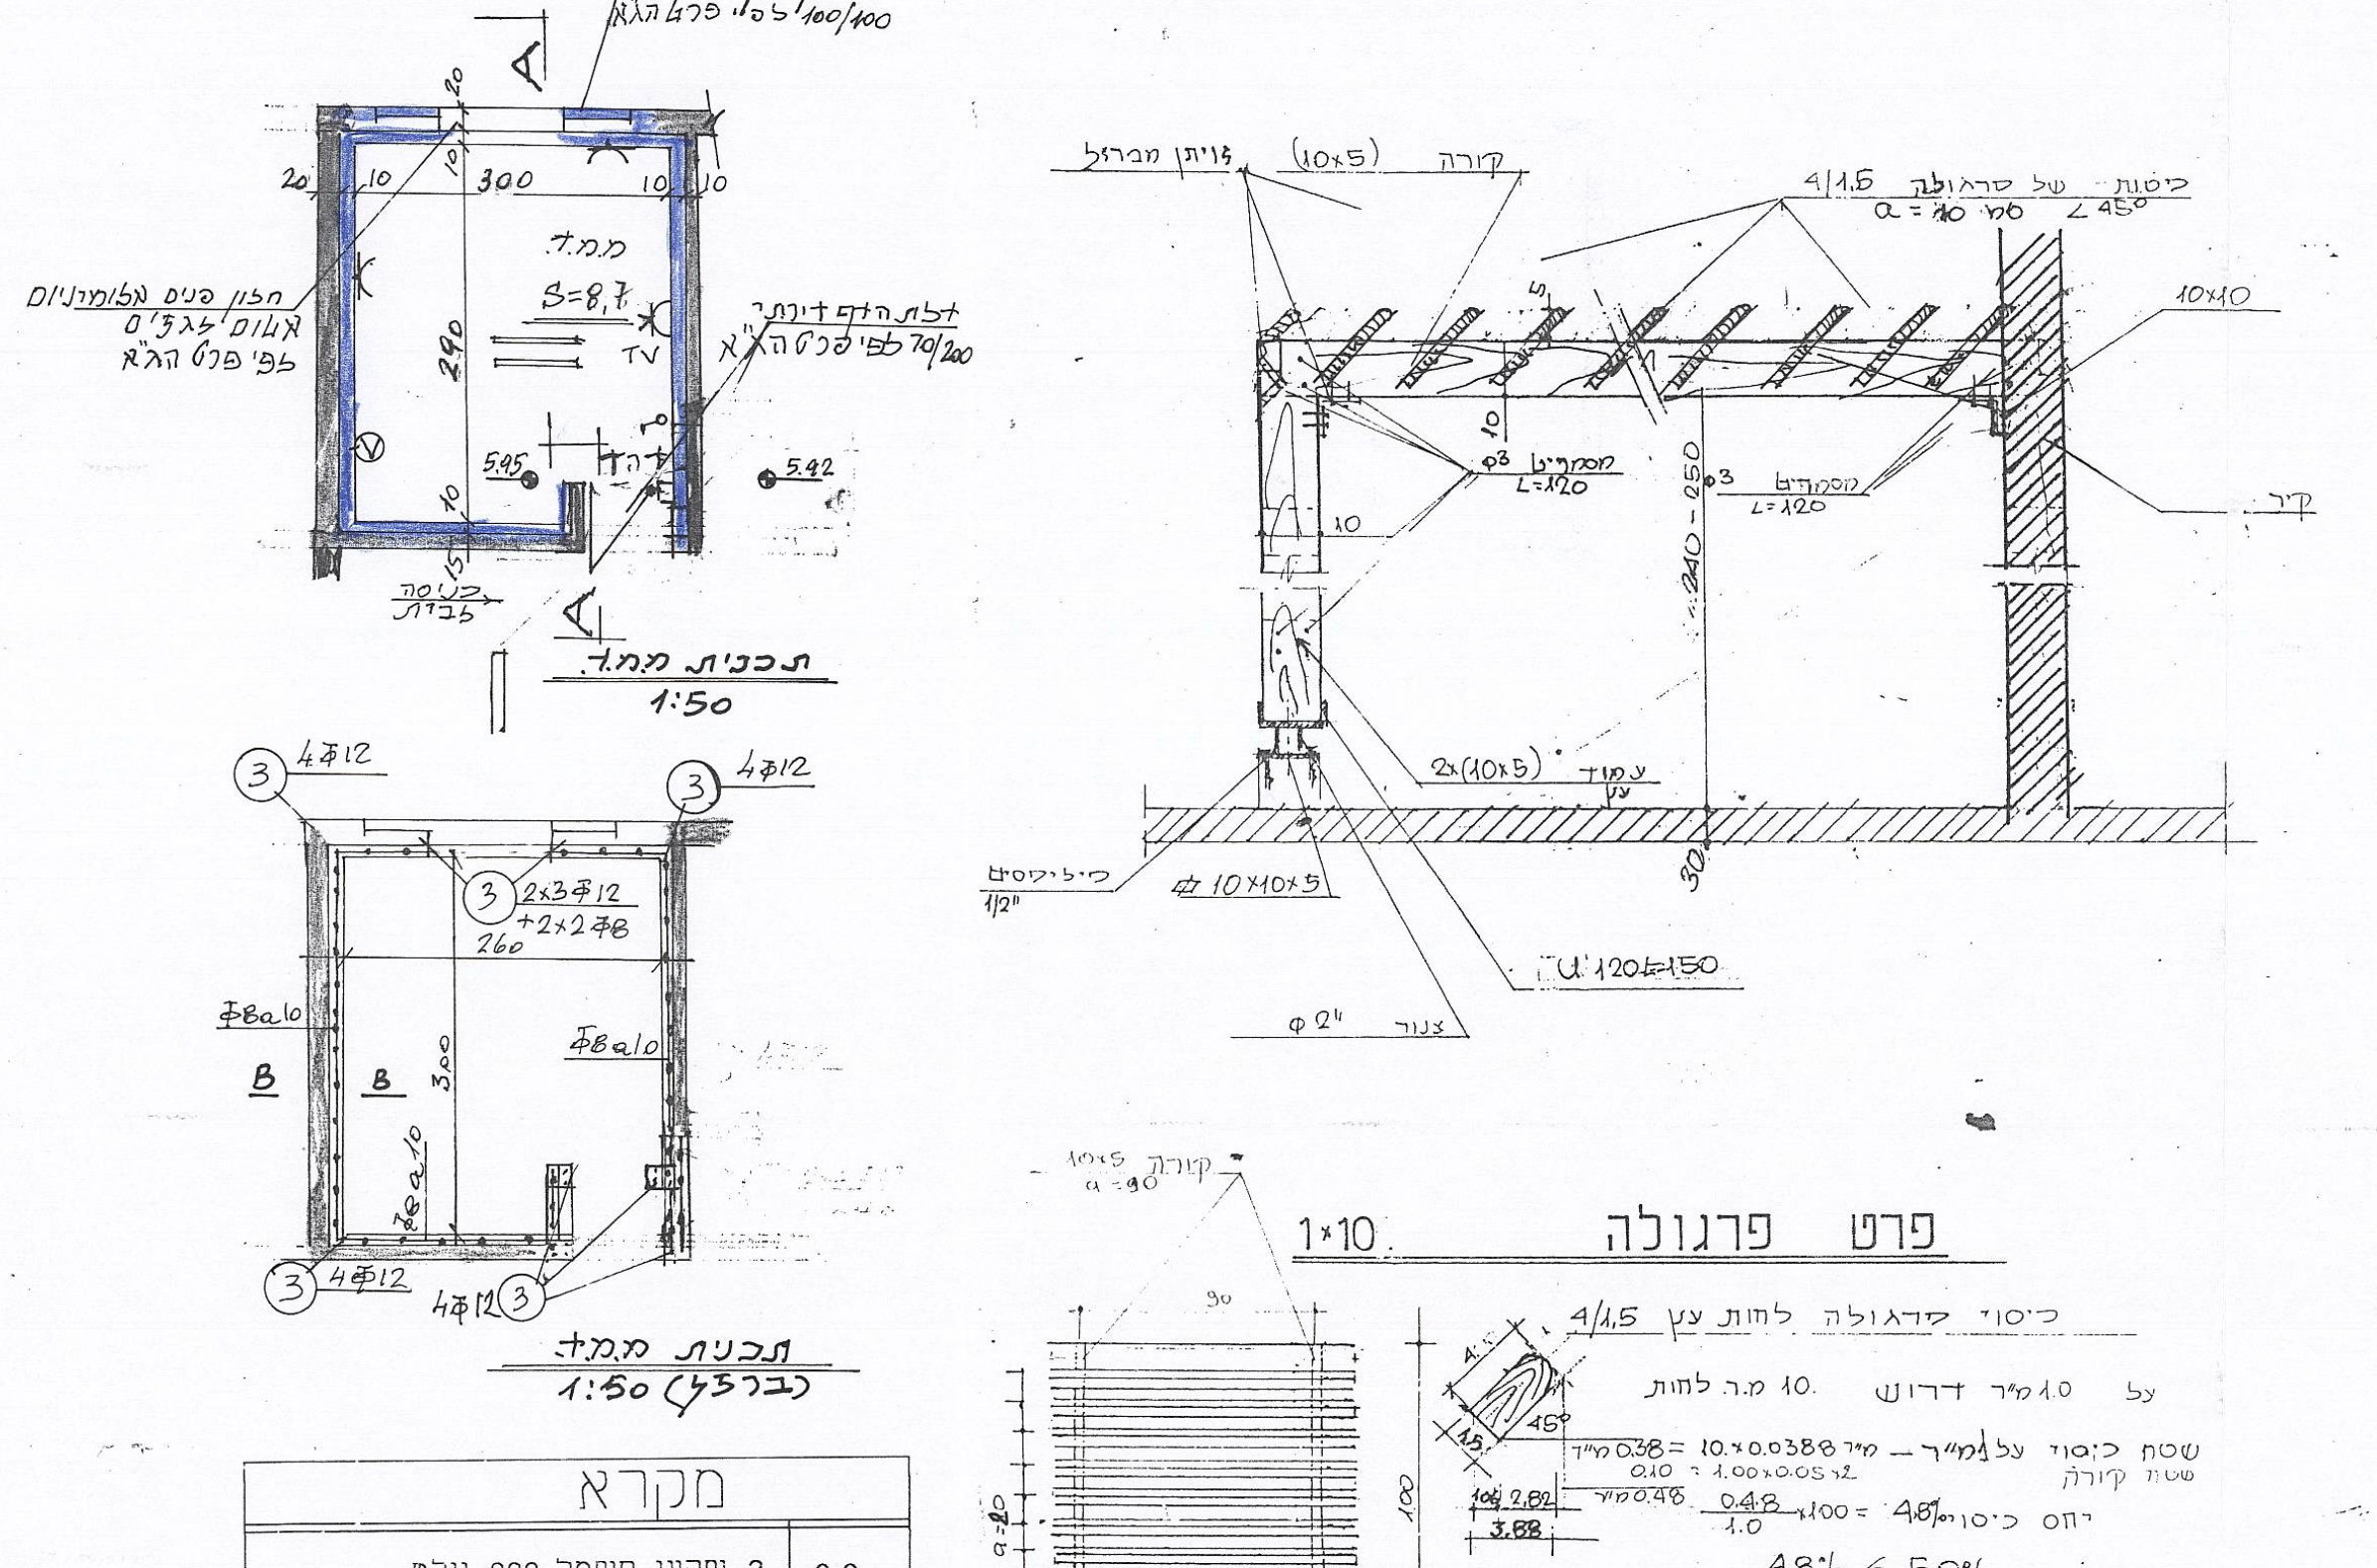

פרט פרגולה 1:10

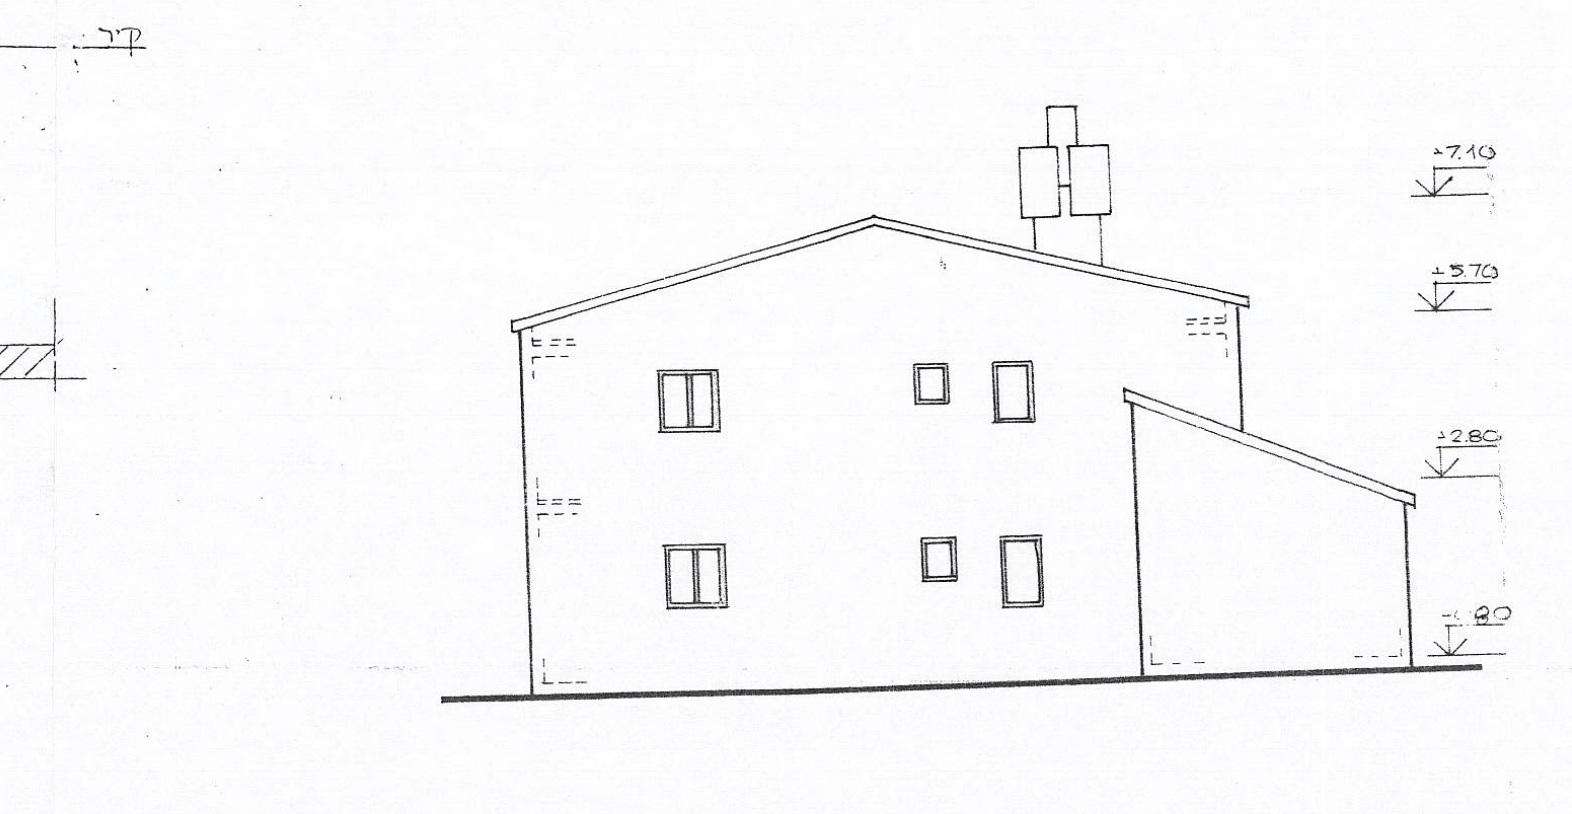

חזית דרומית חרדין 18 1:100

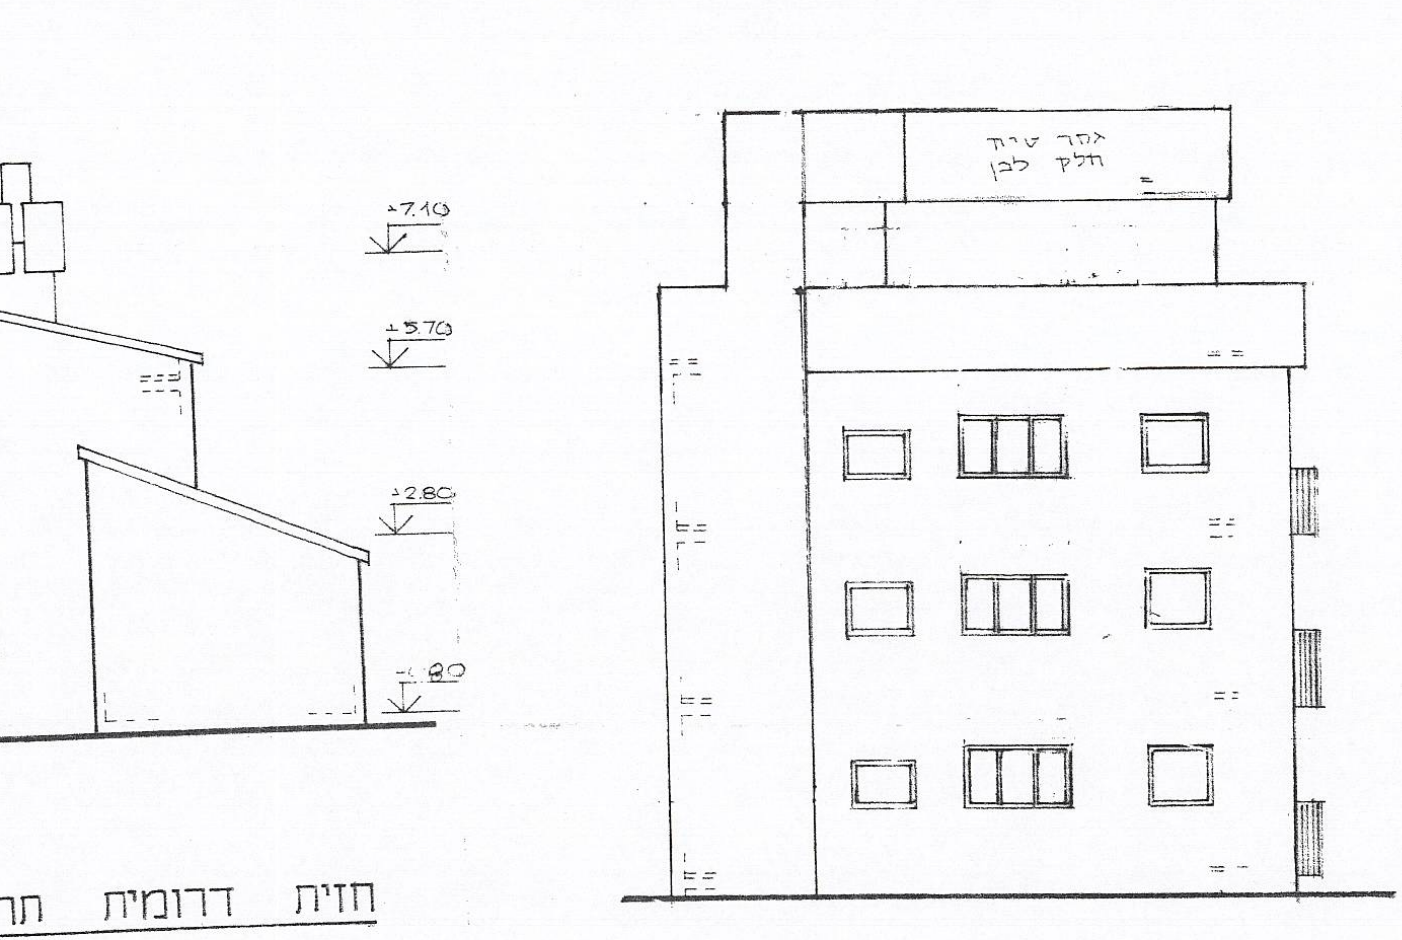

חזית צפונית 1:100

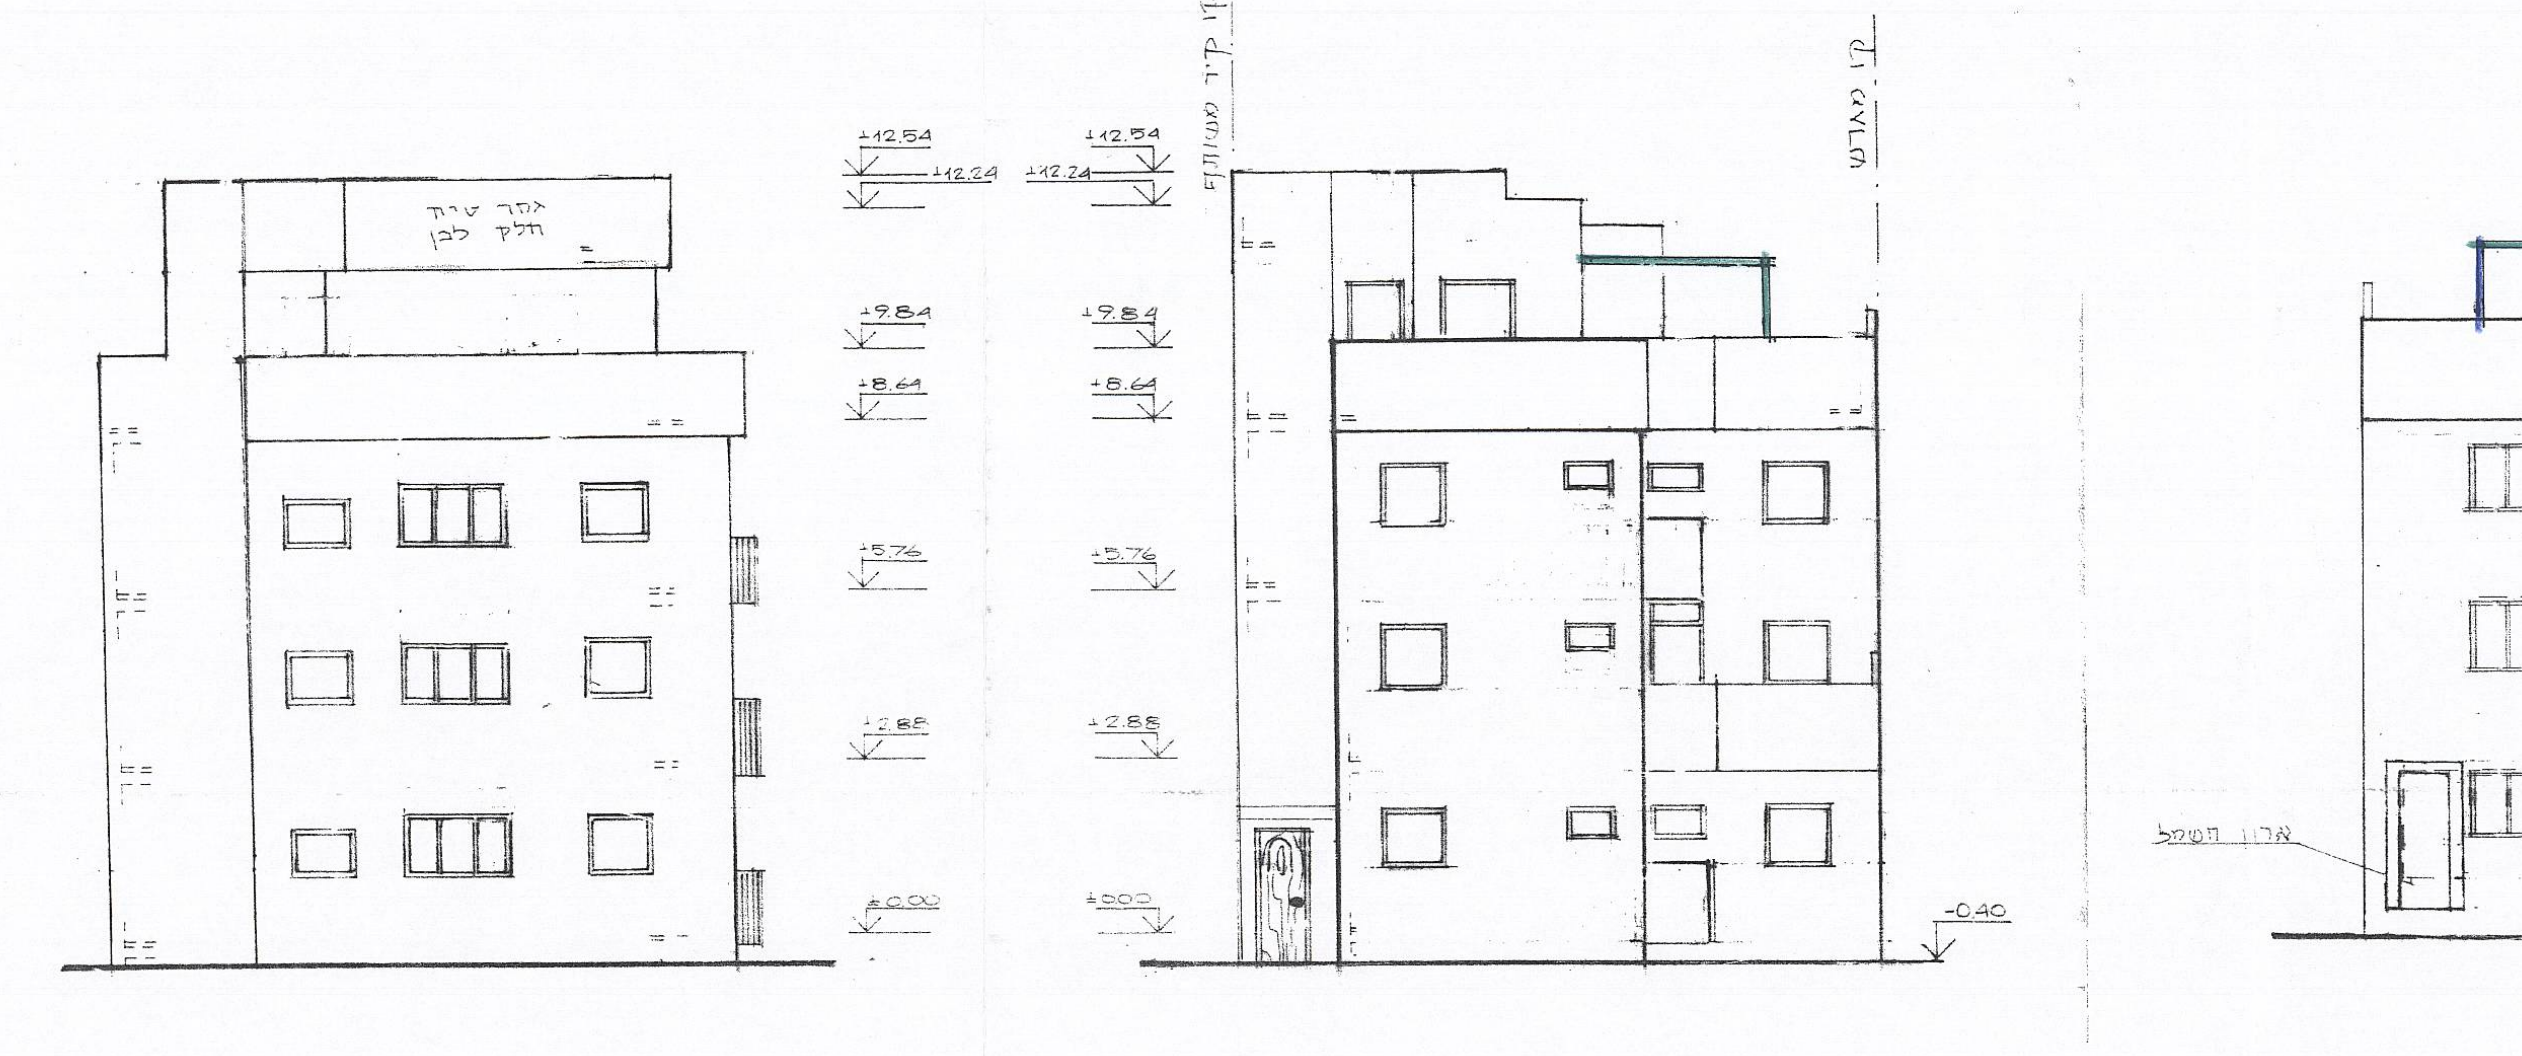

חזית מערבית 1:100

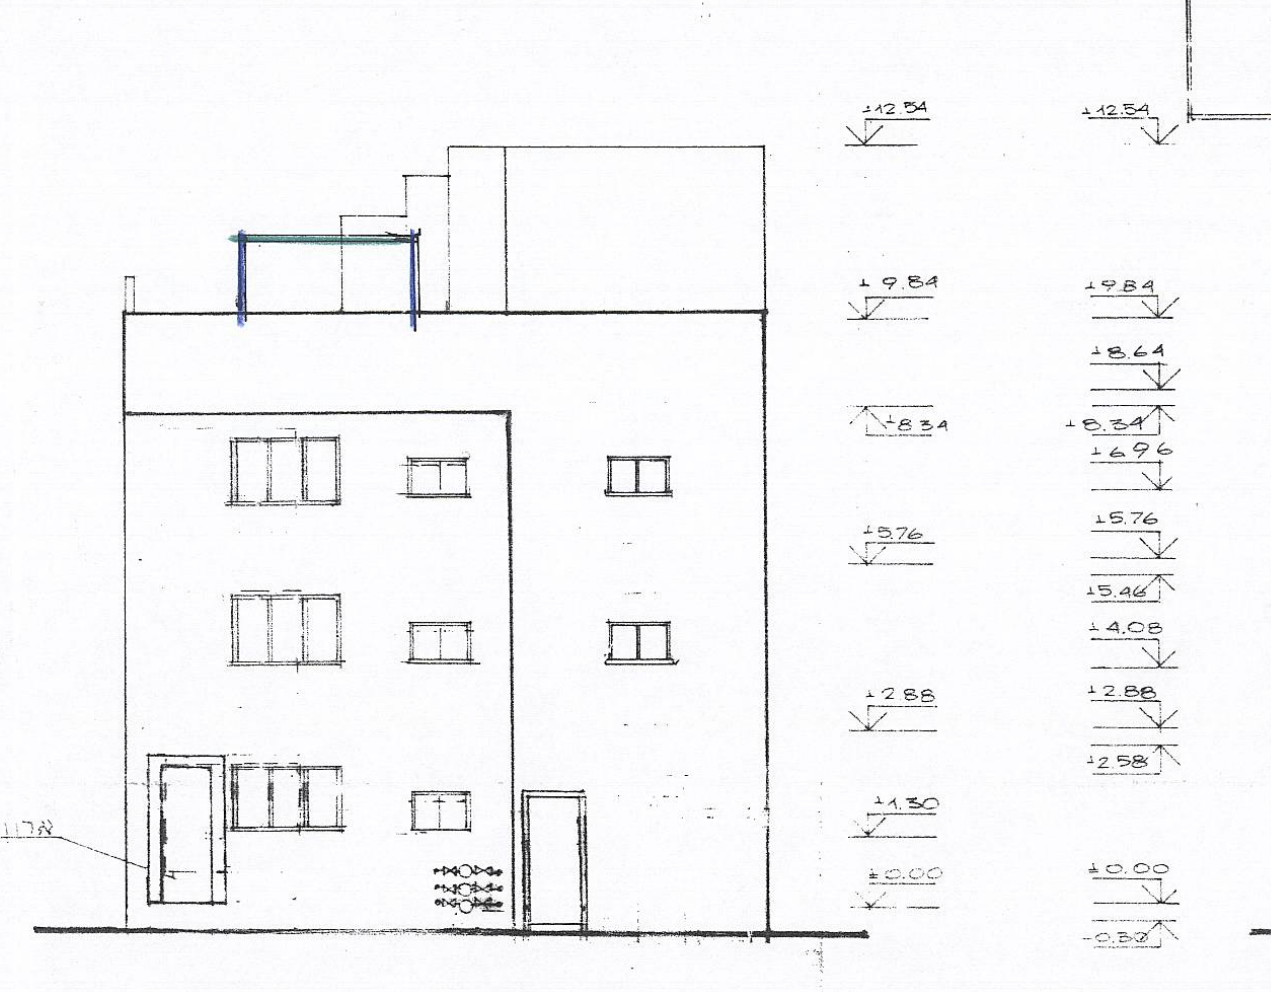

חזית מזרחית 1:100

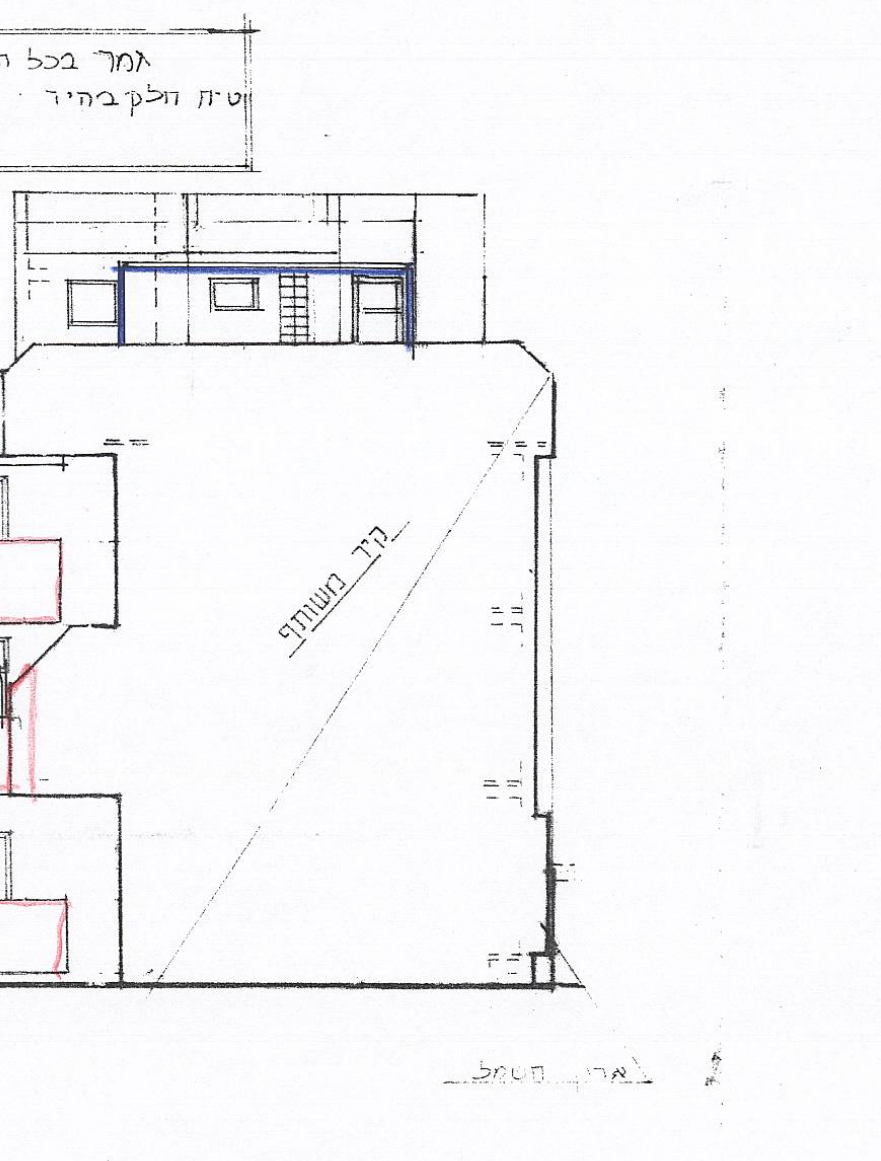

חזית דרומית 1:100

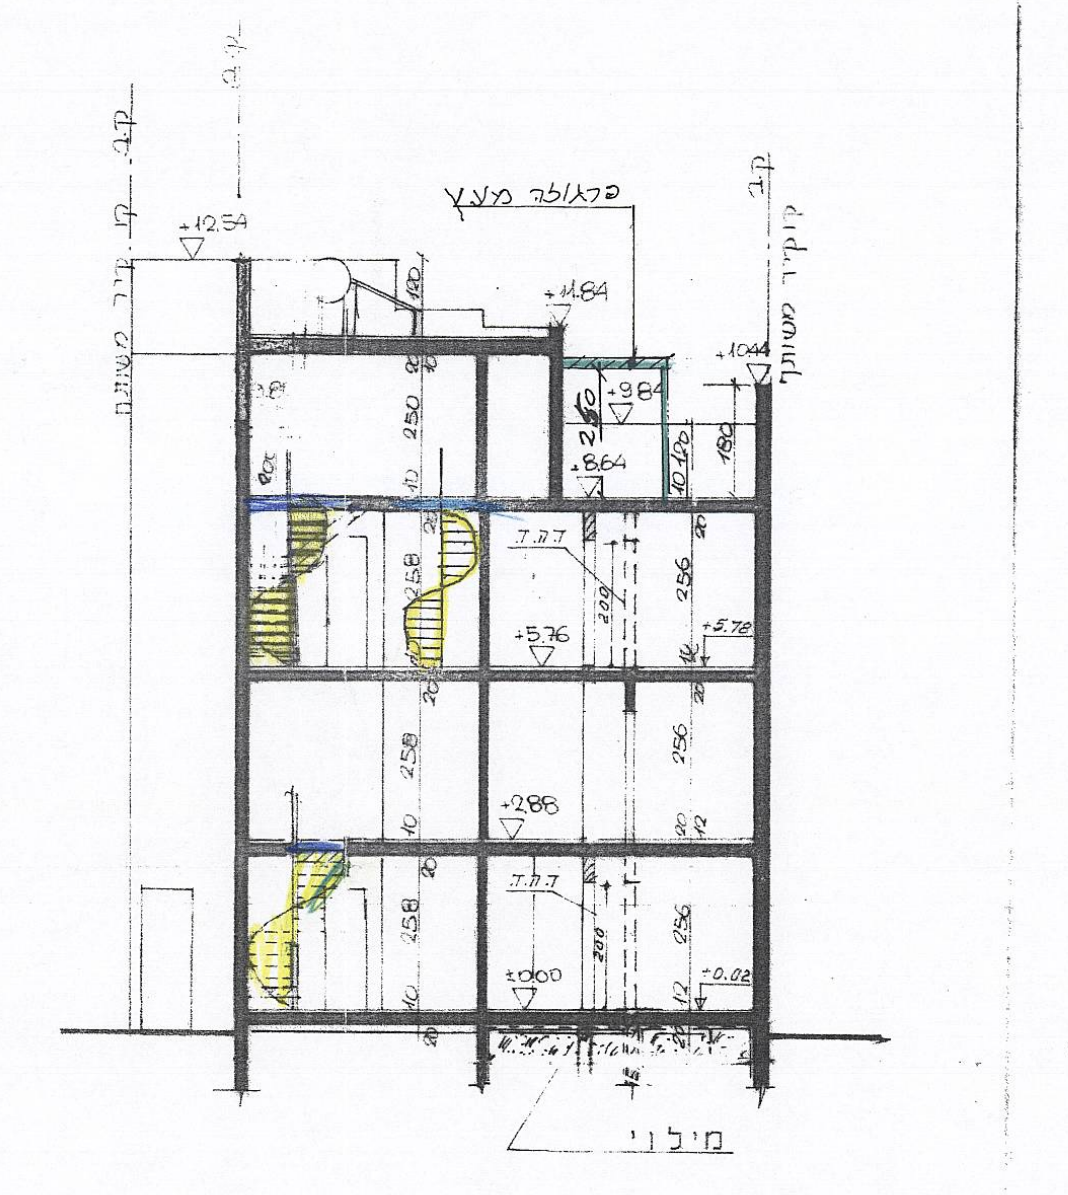

חתך ג-ג 1:100

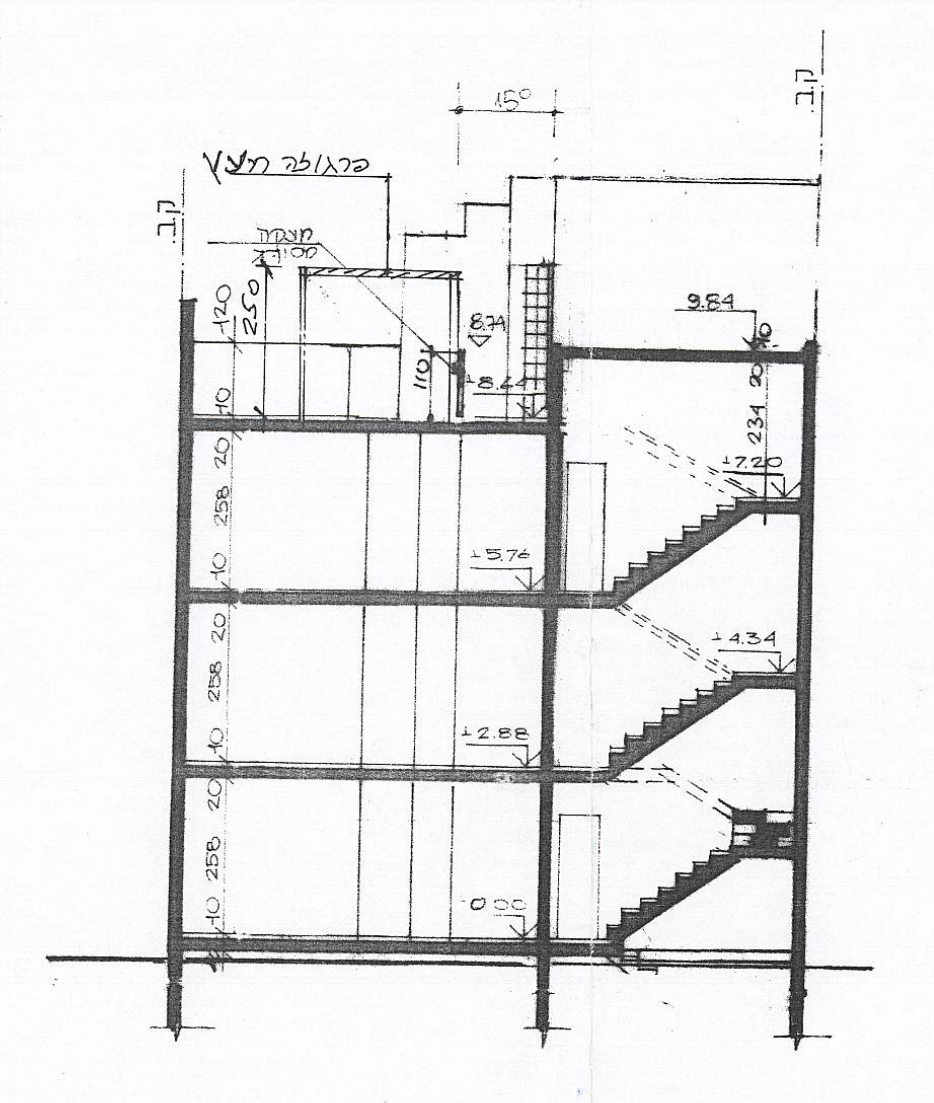

חתך ב-ב 1:100

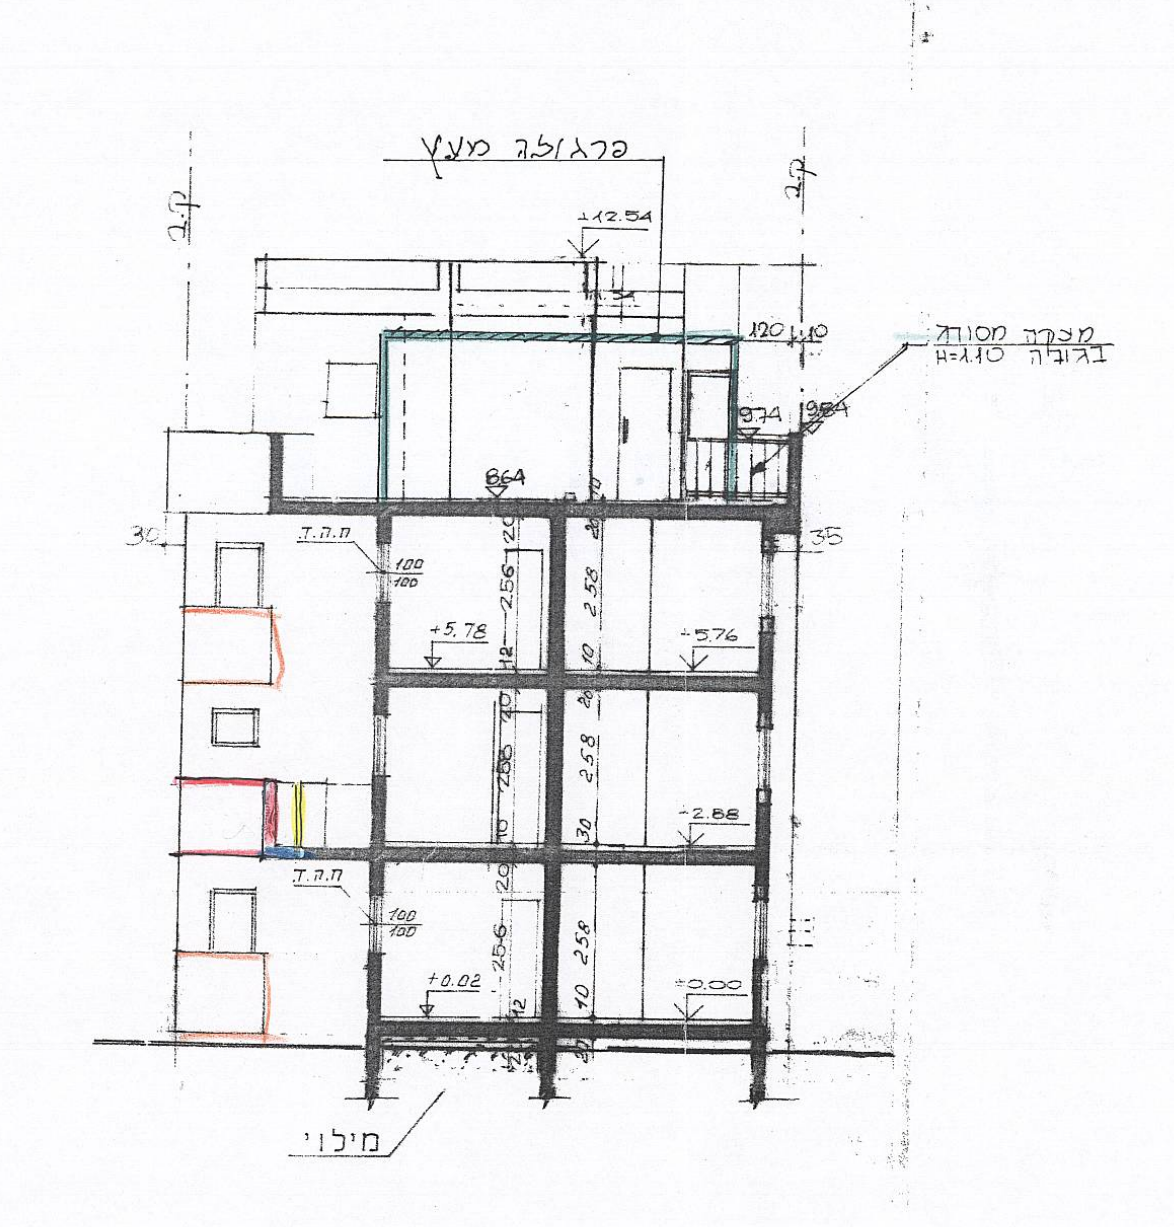

חתך א-א 1:100

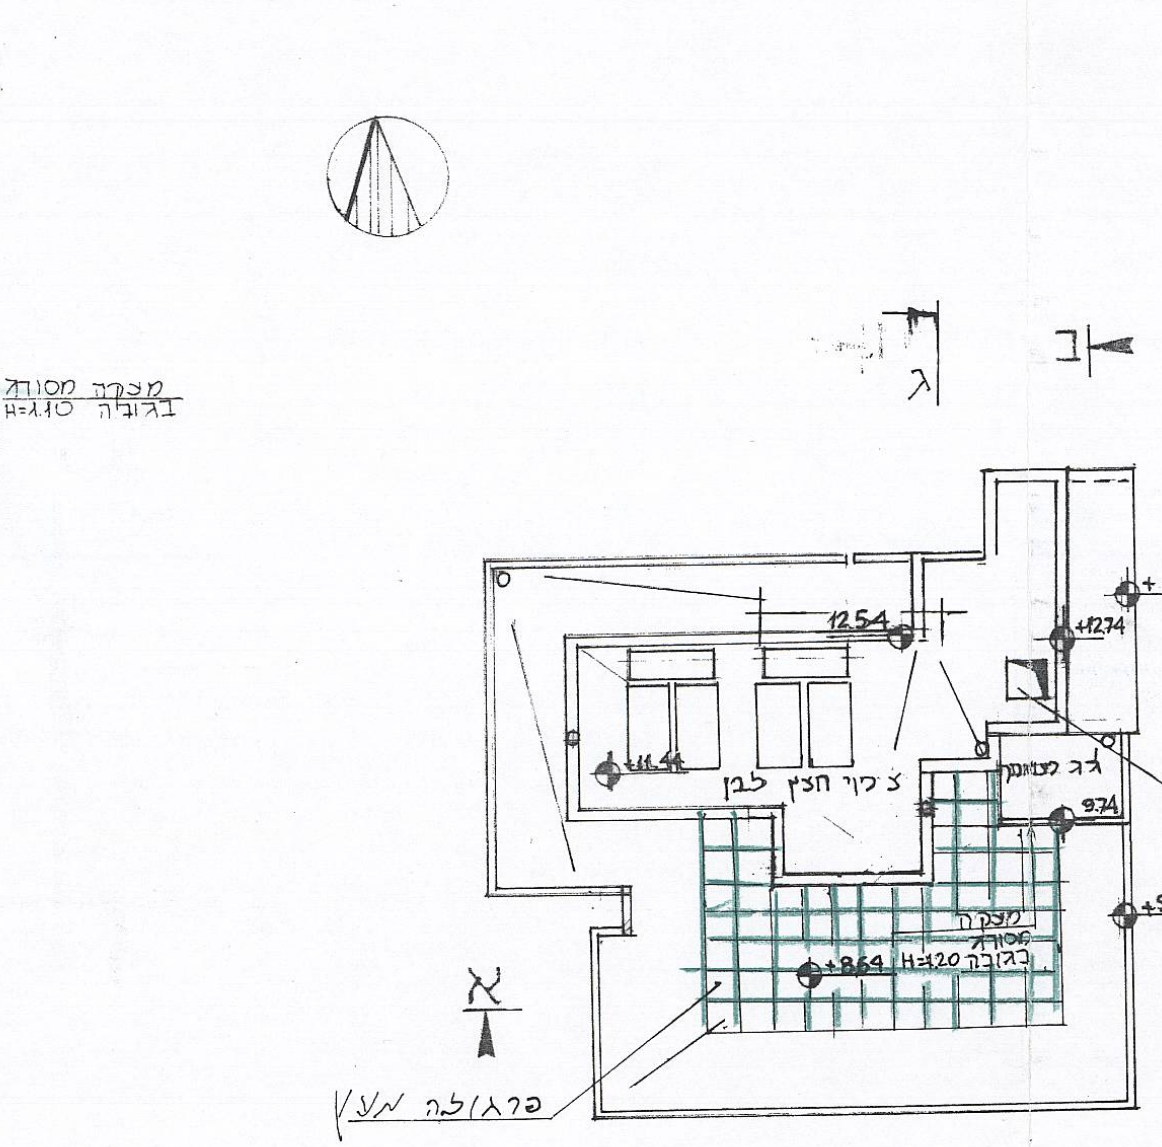

תכנית גג עליון 1:100

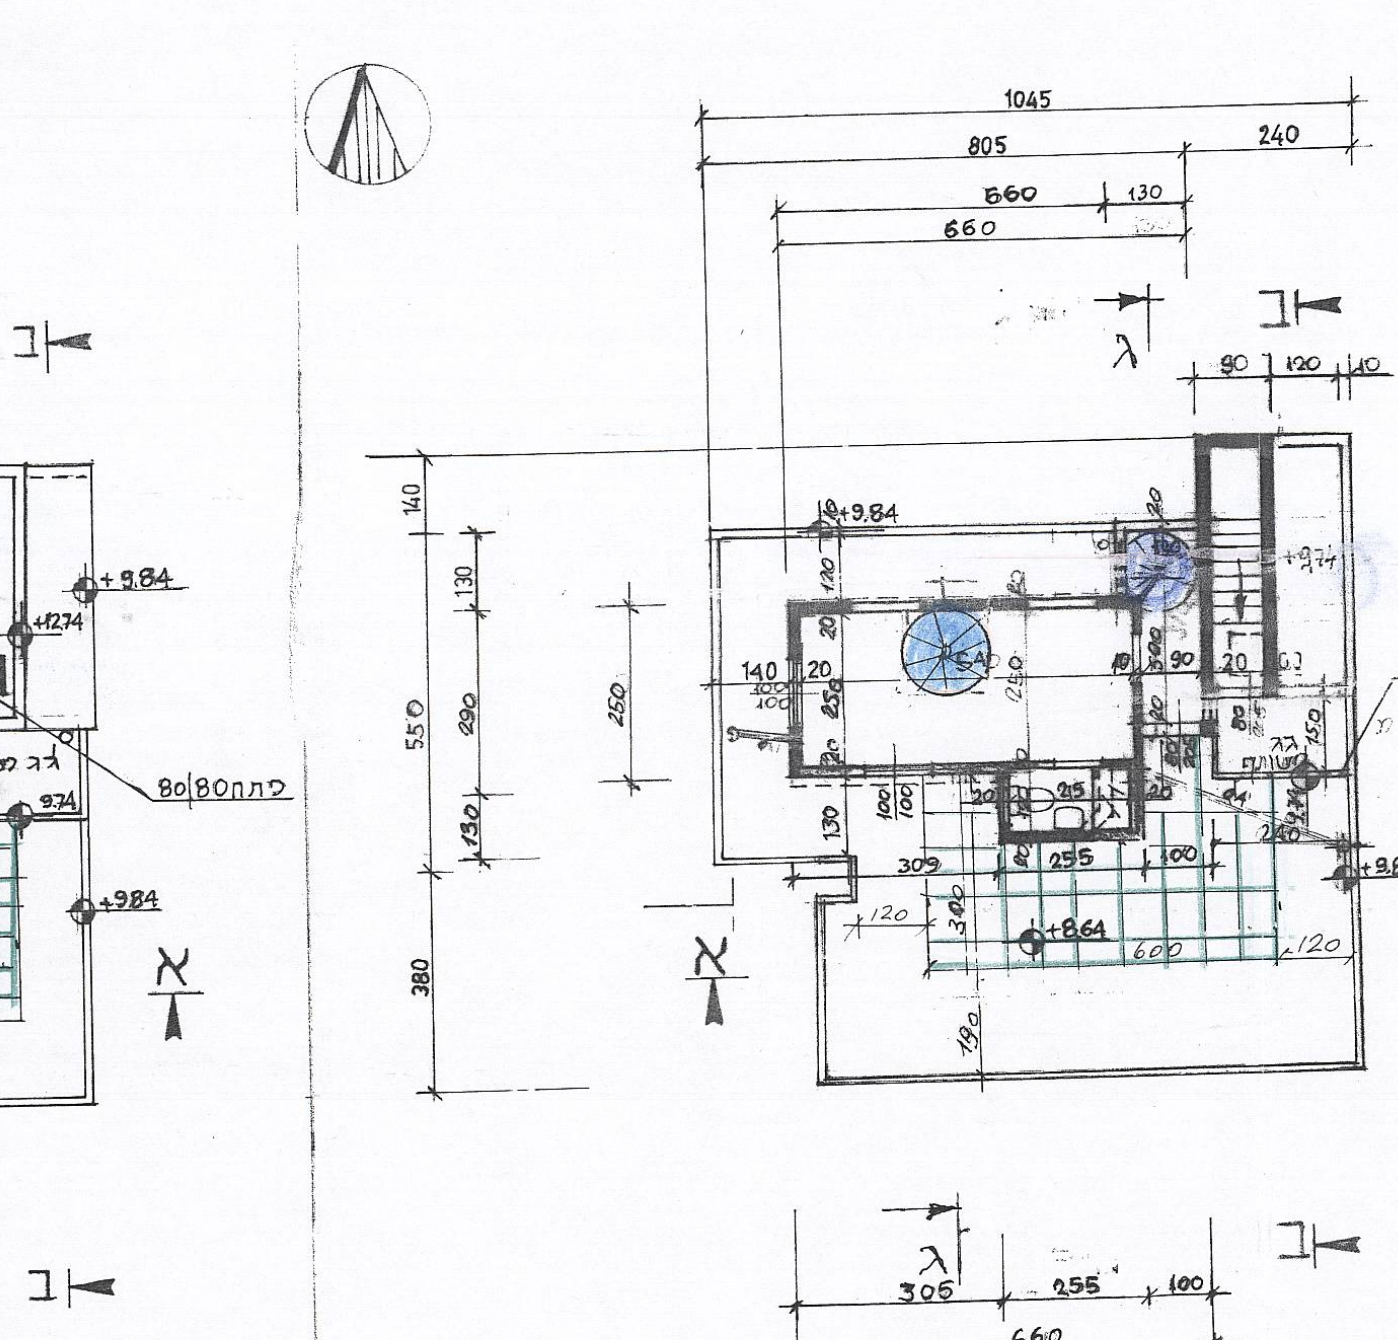

תכנית חדר על הגג 1:100

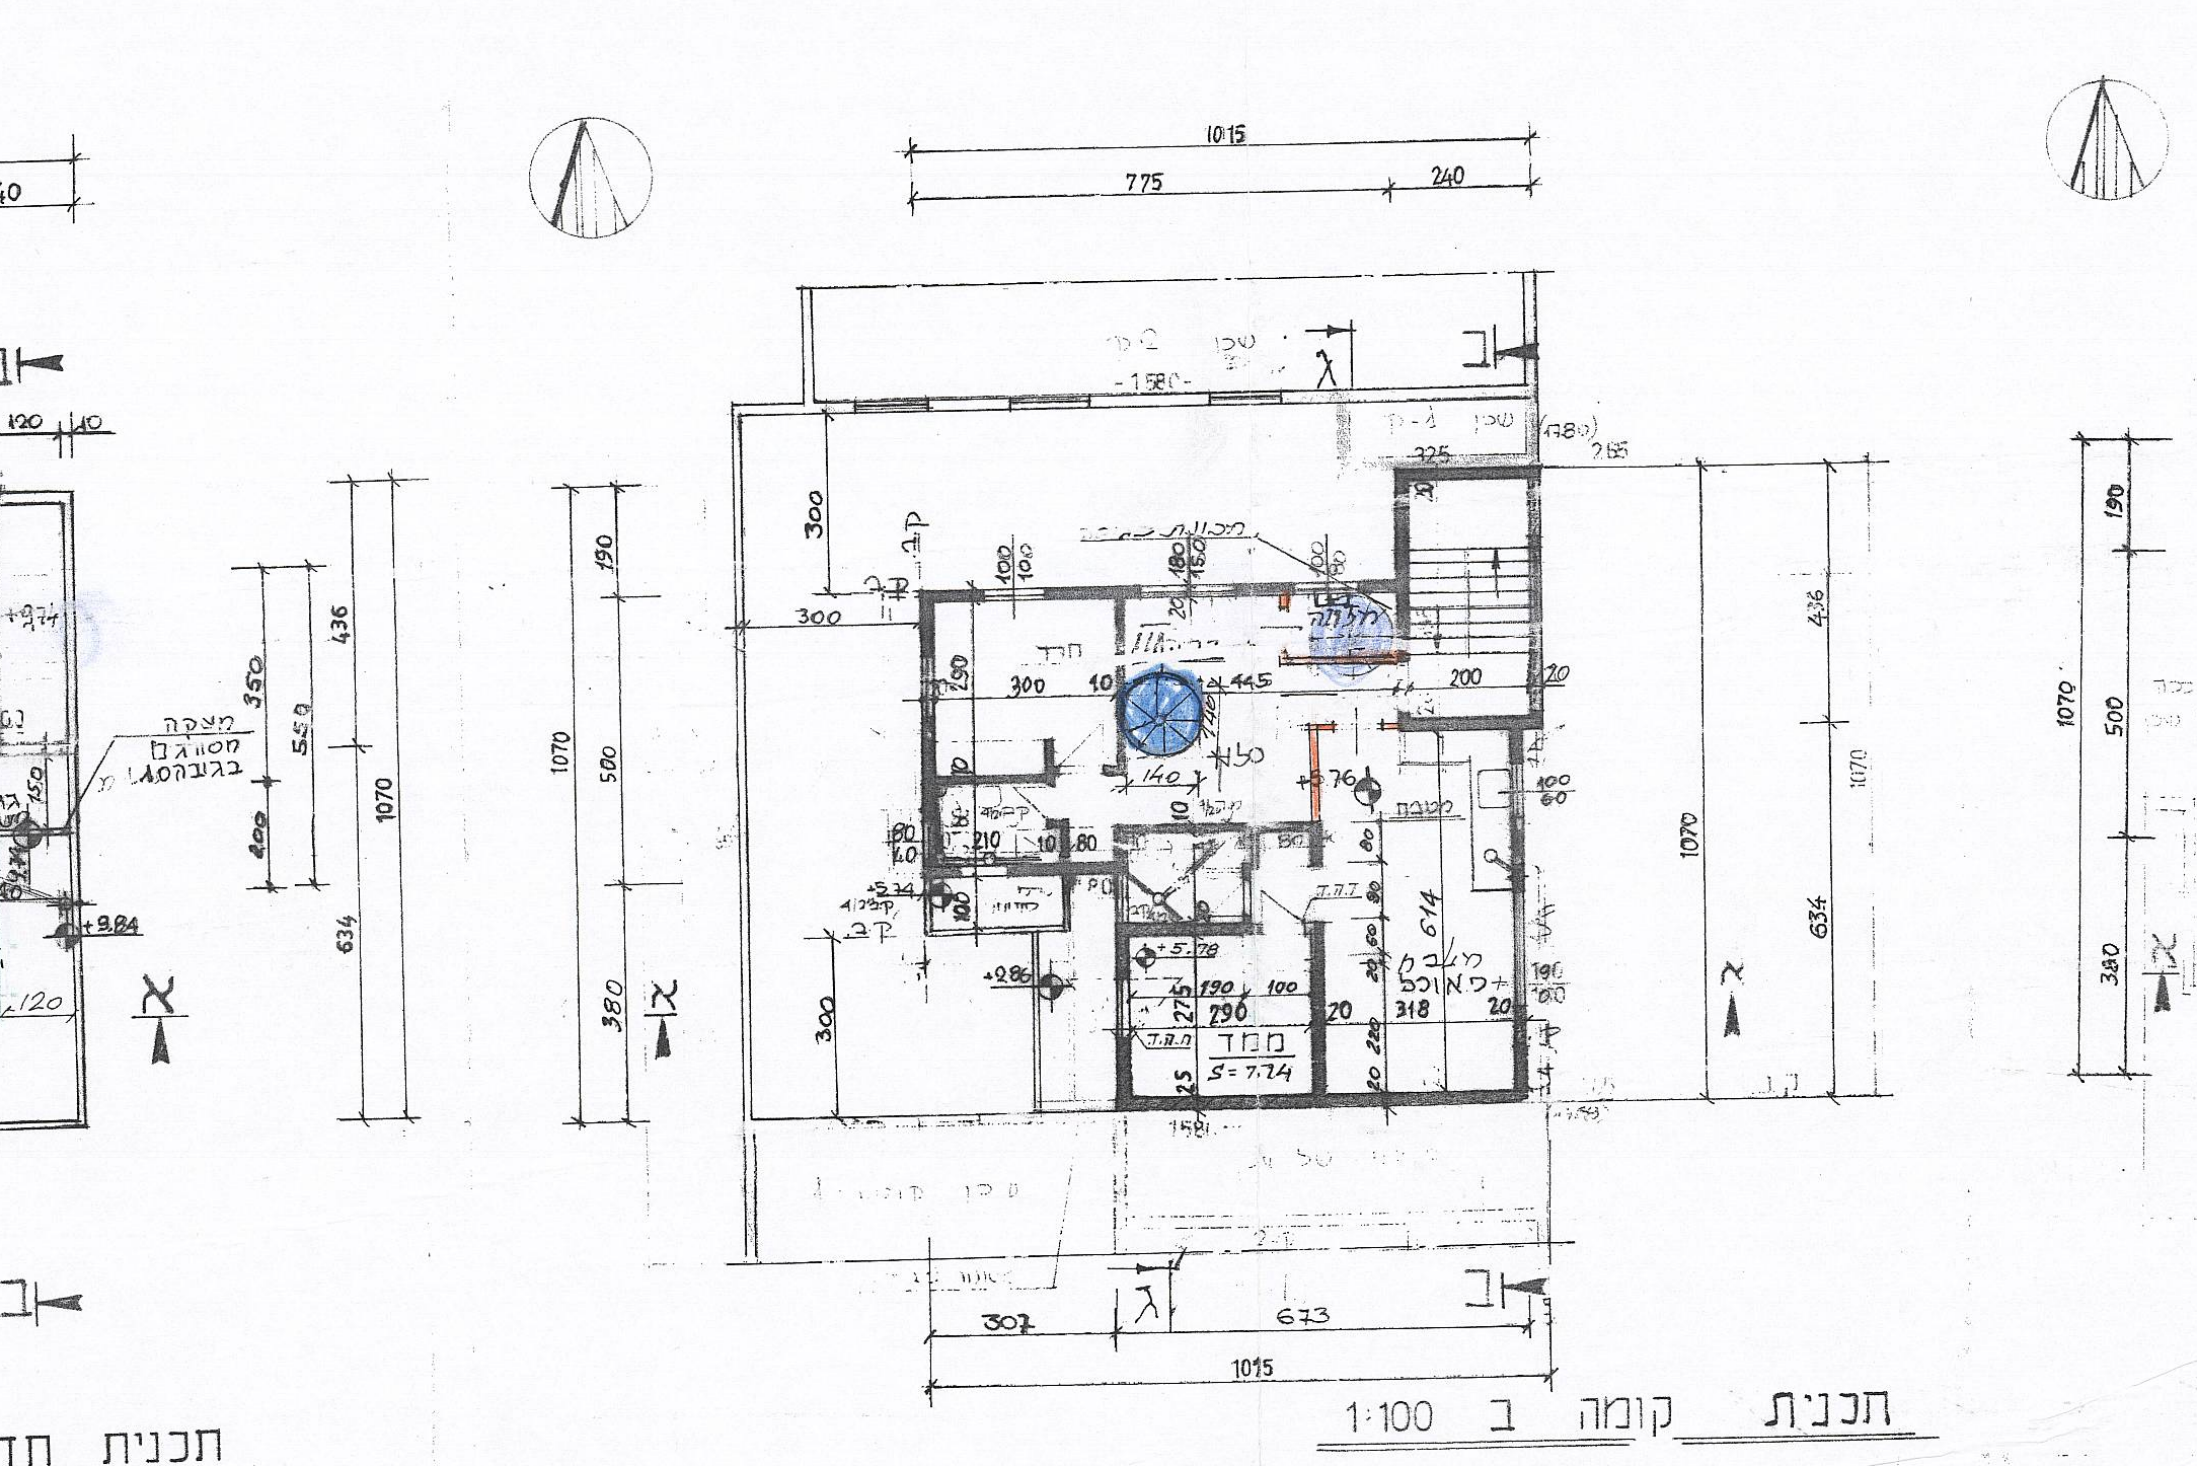

תכנית קומה ב 1:100

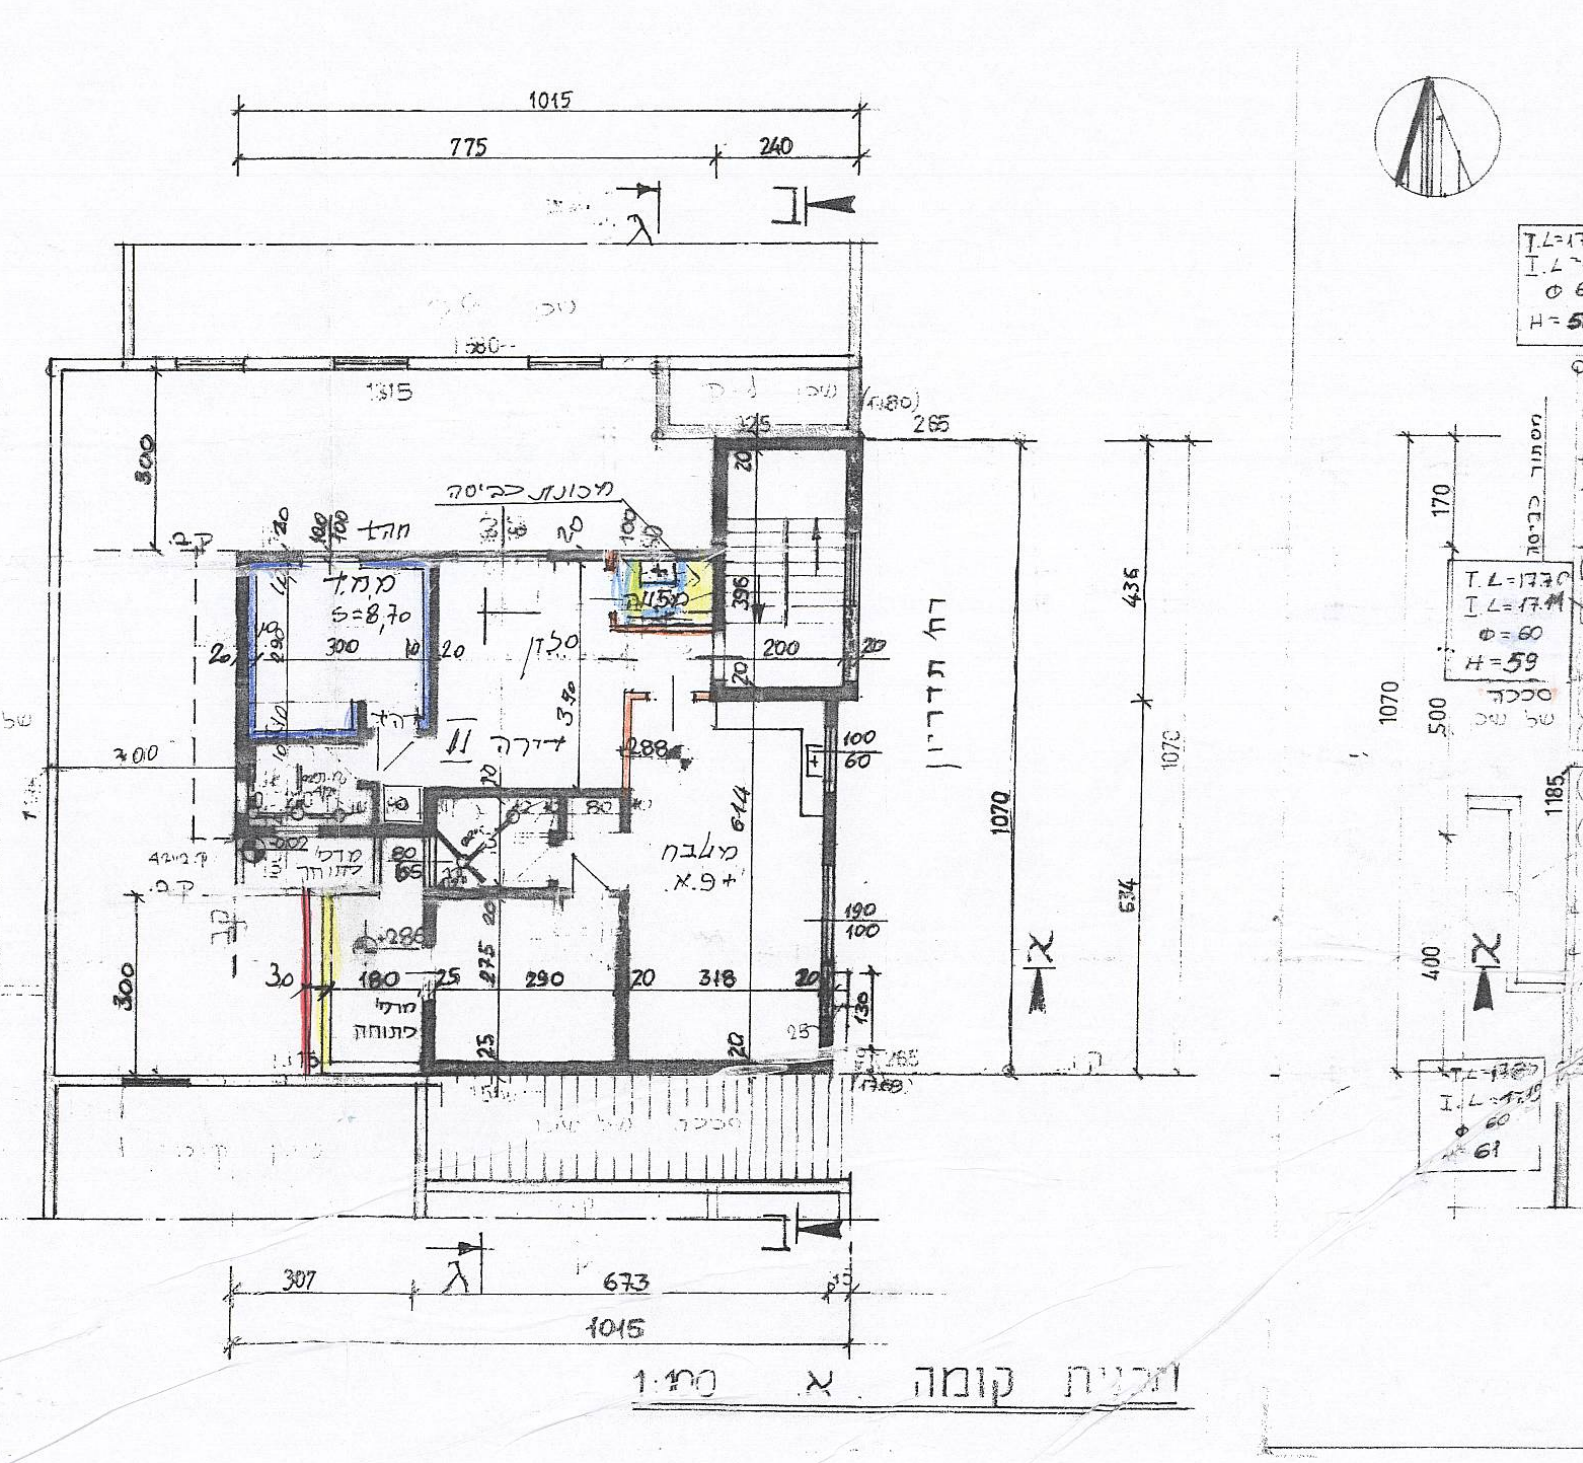

תכנית קומה א 1:100

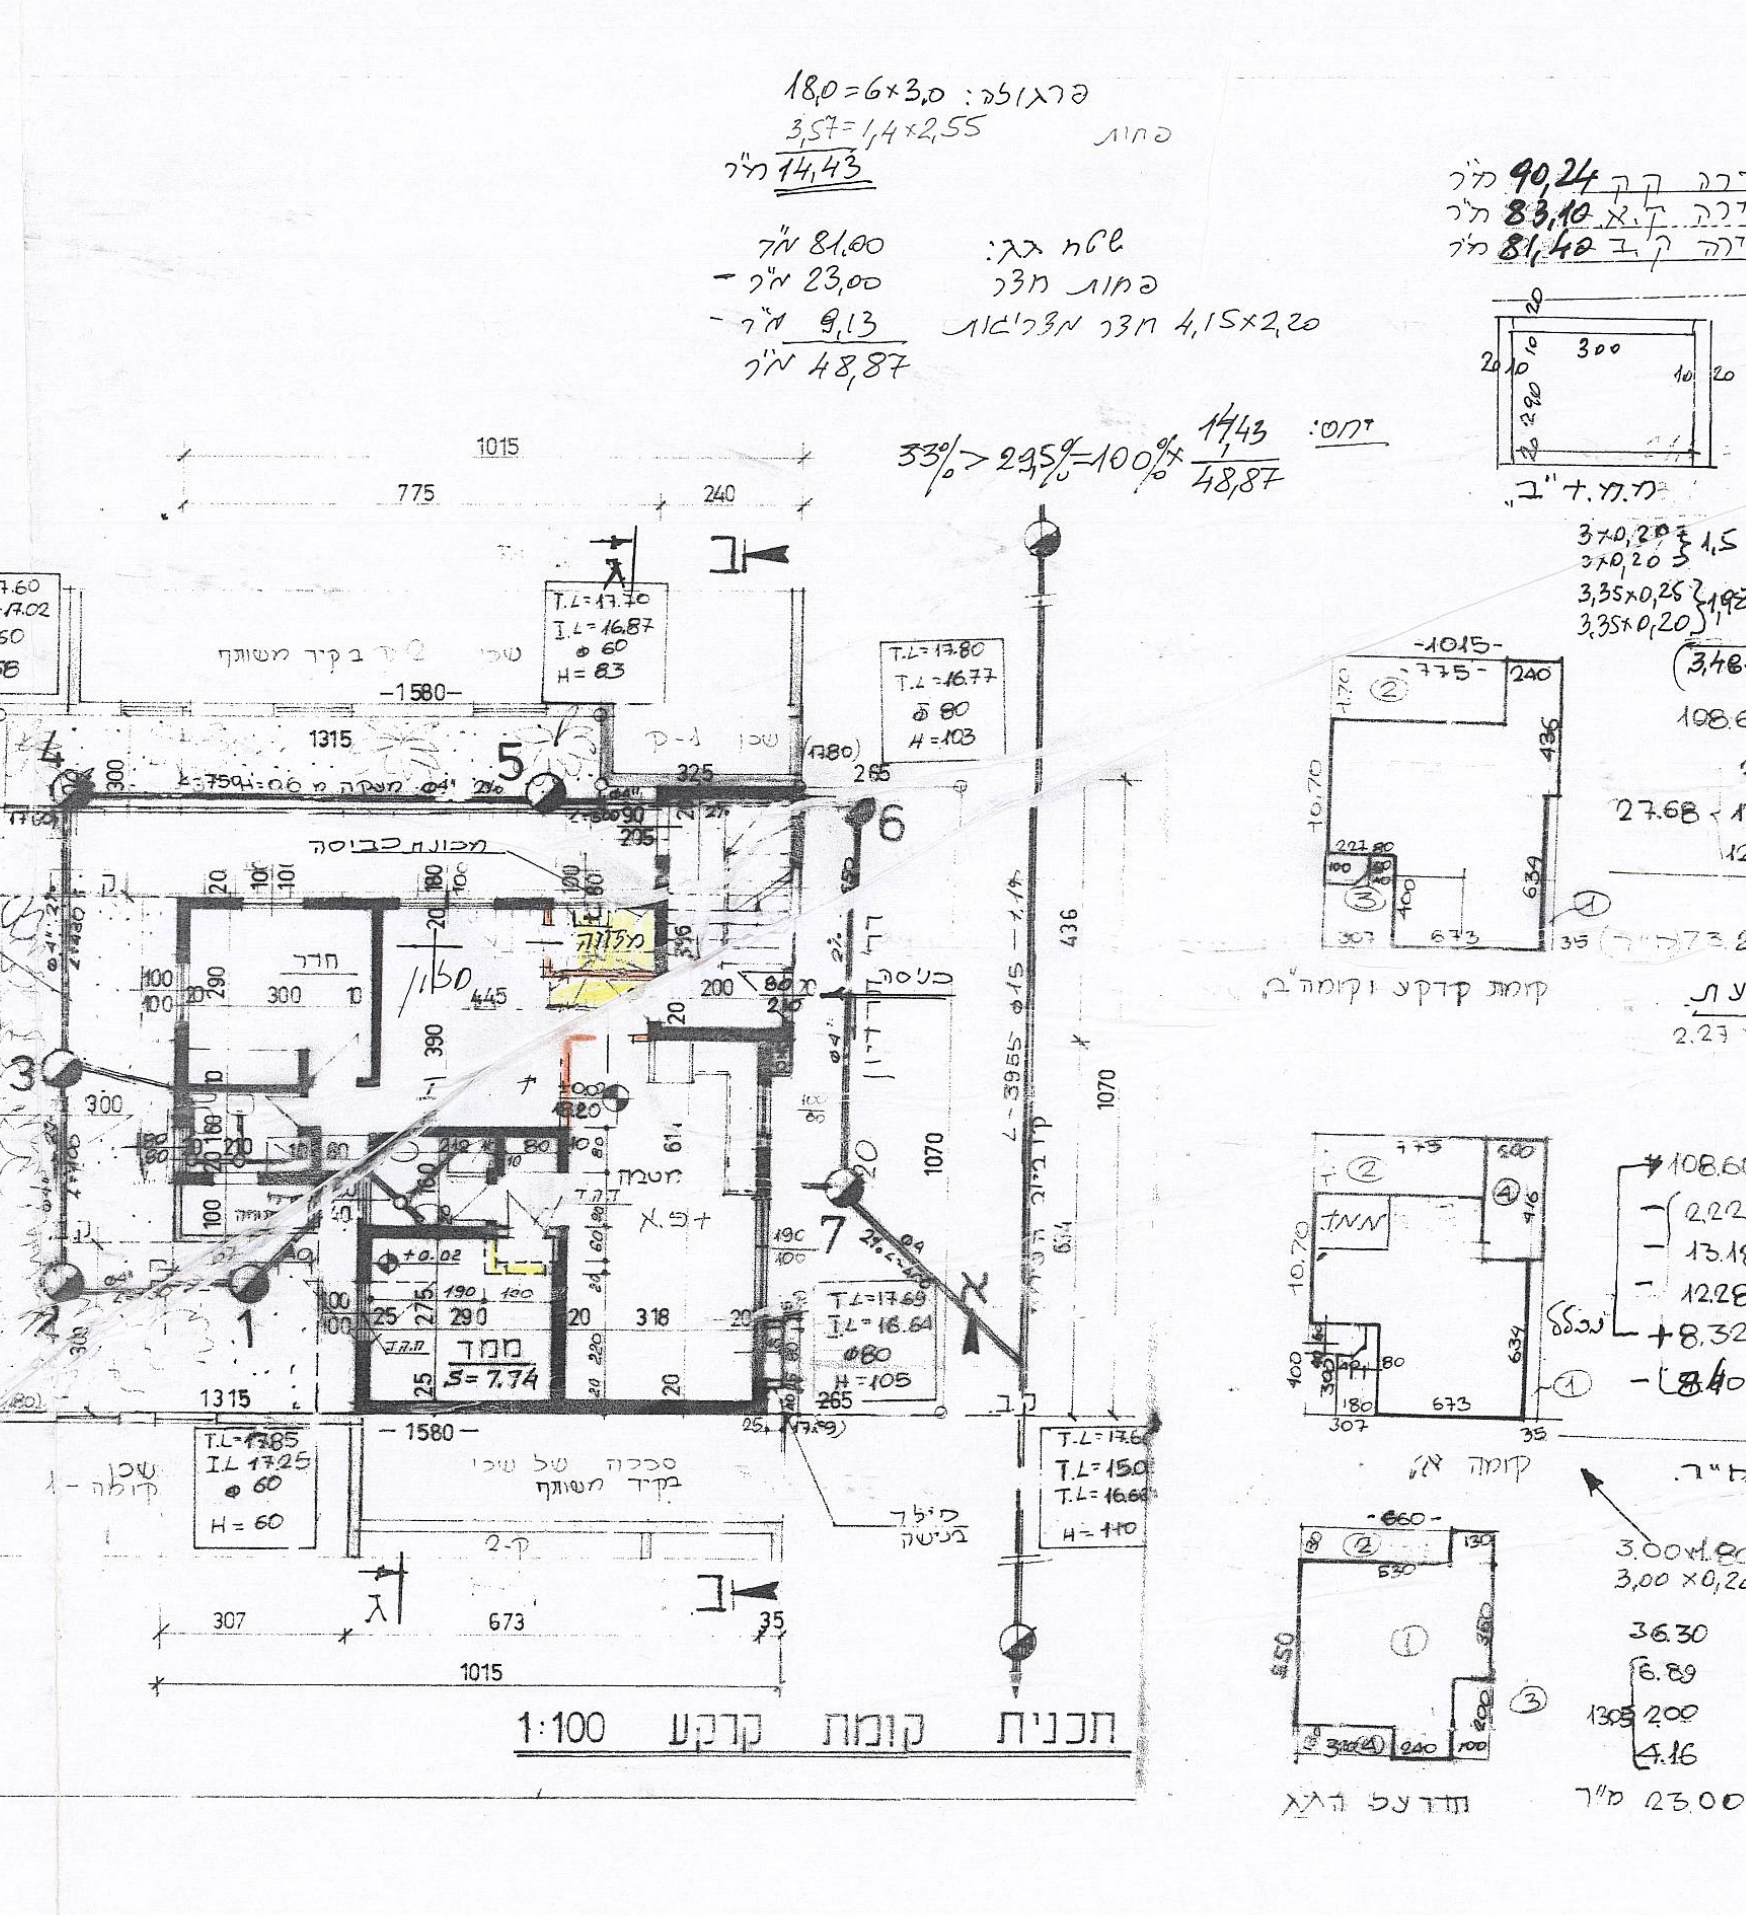

תכנית קומת קרקע 1:100

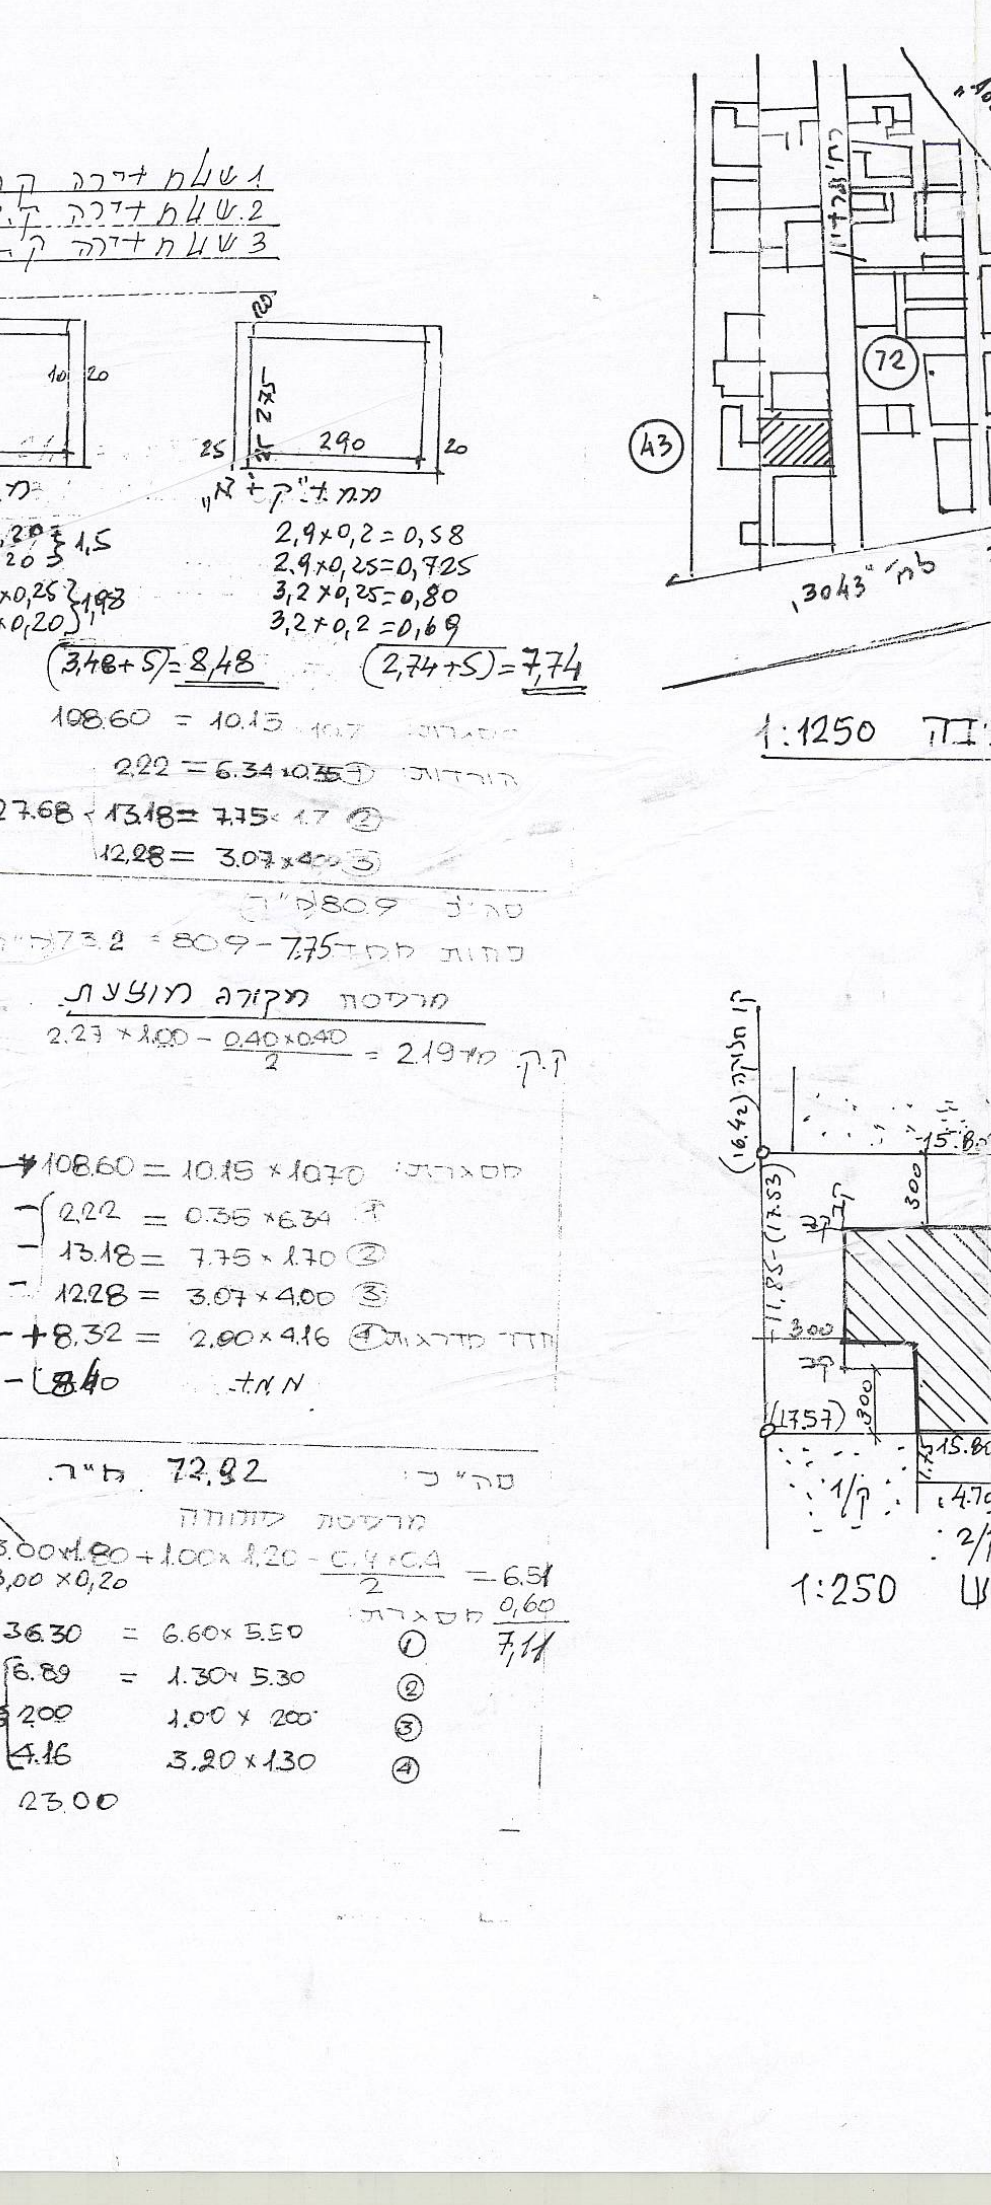

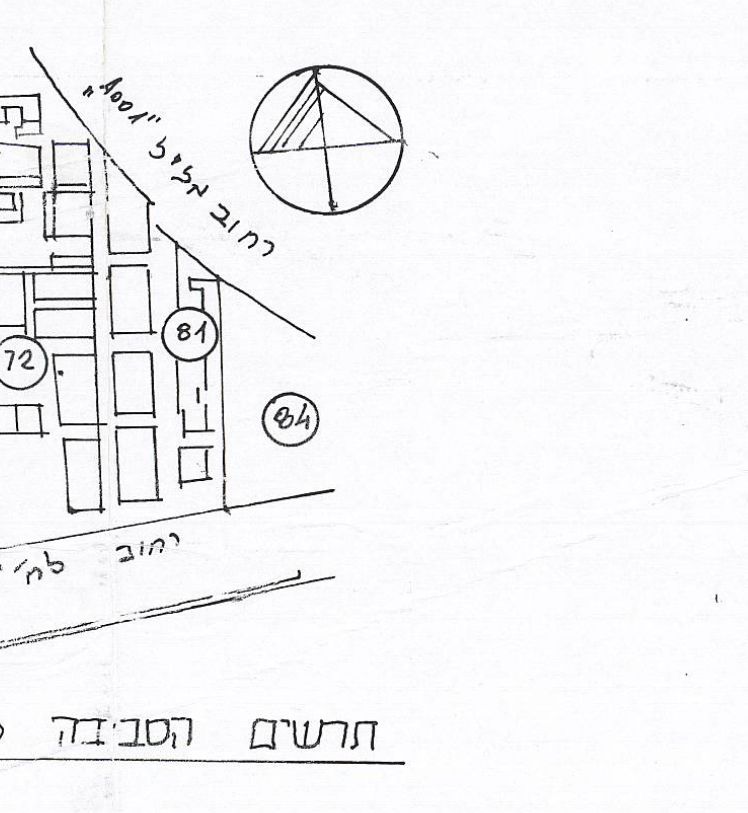

תרשים הסביבה 1:1250

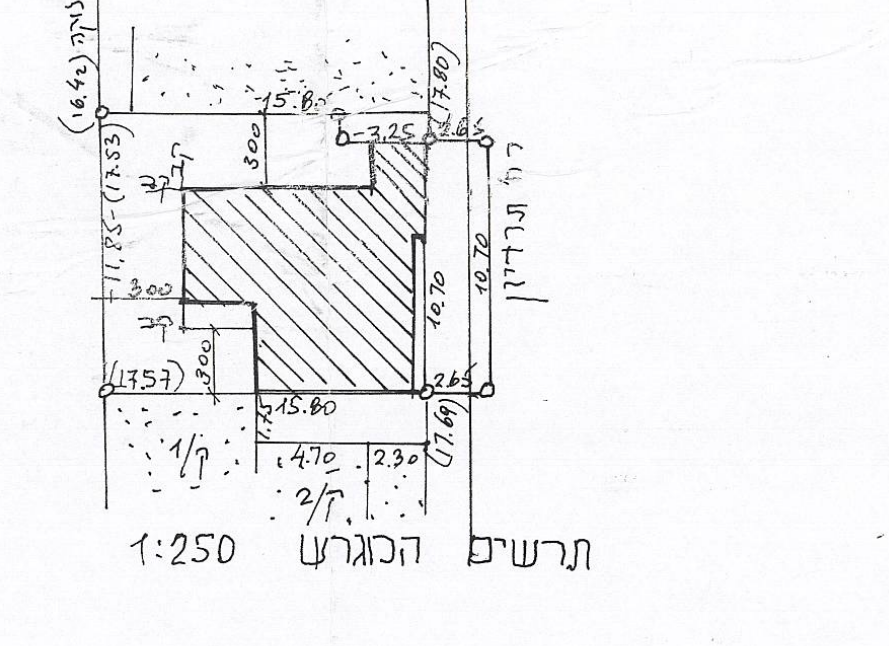

תרשים המגרש 1:250

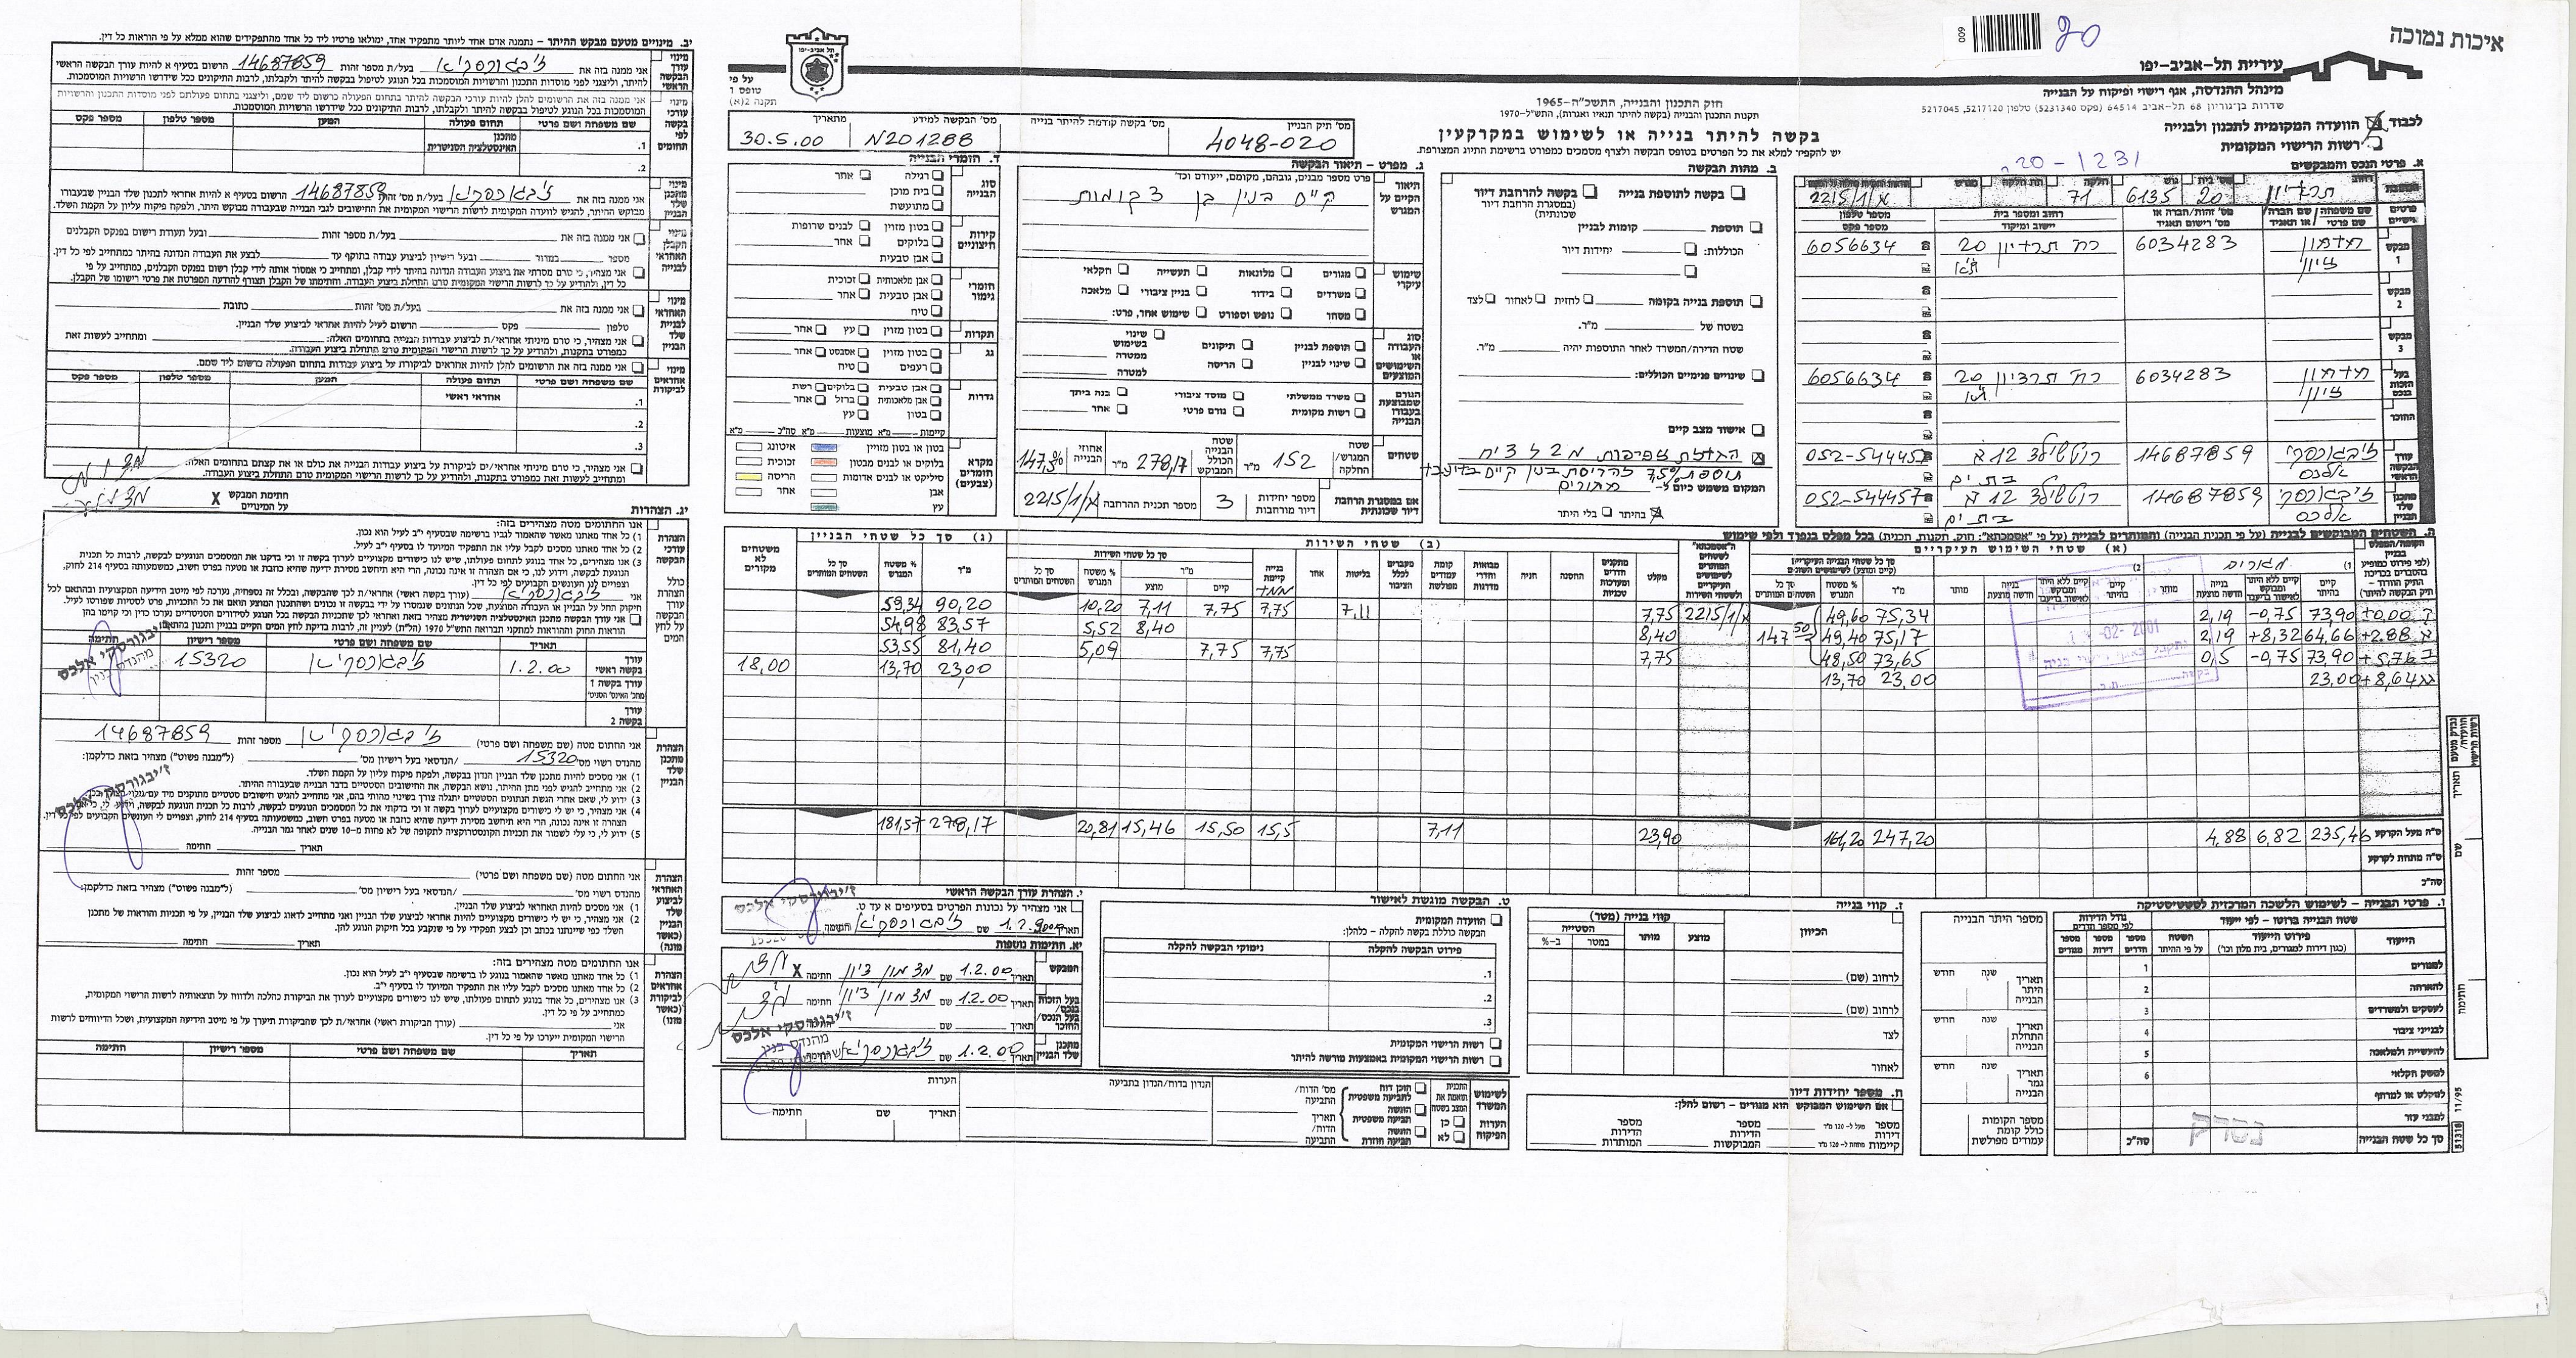

עיריית תל-אביב-יפו

איכות נמוכה

מינהל ההנדסה, אגף רישוי ופיקוח על הבנייה

חוק התכנון והבנייה, התשכ"ה-1965

בקשה להיתר בנייה או לשימוש במקרקעין

לכבוד ☒ הוועדה המקומית לתכנון ולבנייה

☐ רשות הרישוי המקומית

מס' תיק הבניין: 4048-020

מס' בקשה קודמת להיתר בנייה: N201288

תאריך: 30.5.00

תיאור הבקשה: ק"ס בנין בן 3 קומות

☒ הגדלת צפיפות מ-2 ל-3 יח'

מספר יחידות דיור מורחבות: 3

שטח המגרש: 152

שטח הבנייה הכולל המבוקש: 278.7

חרדין 20

6135

71

מבקש 1: מדמון ציון — 6034283 — רח' חרדין 20 ת"א — 6056634

בעל הזכות בנכס: מדמון ציון — 6034283 — רח' חרדין 20 ת"א — 6056634

עורך הבקשה: ז'בגונסקי אלכס — 14687859 — רוטשילד 12 א' בת-ים — 052-544457

מתכנן שלד הבניין: ז'בגונסקי אלכס — 14687859 — רוטשילד 12 א' בת-ים — 052-544457

0.00	73.90	-0.75	2.19	49.60 75.34	7.75	59.34 90.20
+2.88	64.66	+8.32	2.19	49.40 75.17	8.40	54.98 83.57
+5.76	73.90	-0.75	0.5	48.50 73.65	7.75	53.55 81.40
+8.64	23.00			13.70 23.00		13.70 23.00

15320

1.2.00

הועדה המקומית לתכנון ולבניה
למרחב תכנון תל-אביב - יפו
621026
מהנדס העיר
28.3.01

עיריית תל-אביב-יפו
מינהל ההנדסה / היתרי בניה
06.09.00
לפי תוכנית מקושרת זו
מותר להגיש תשכון.
להגיש תוכנית סניטרית..........
אחראי לאזור..........

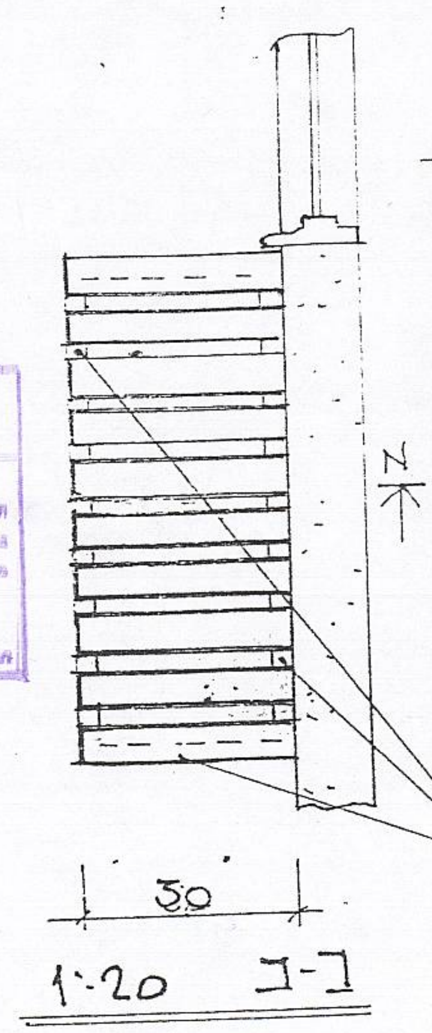

ב-ב 1:20

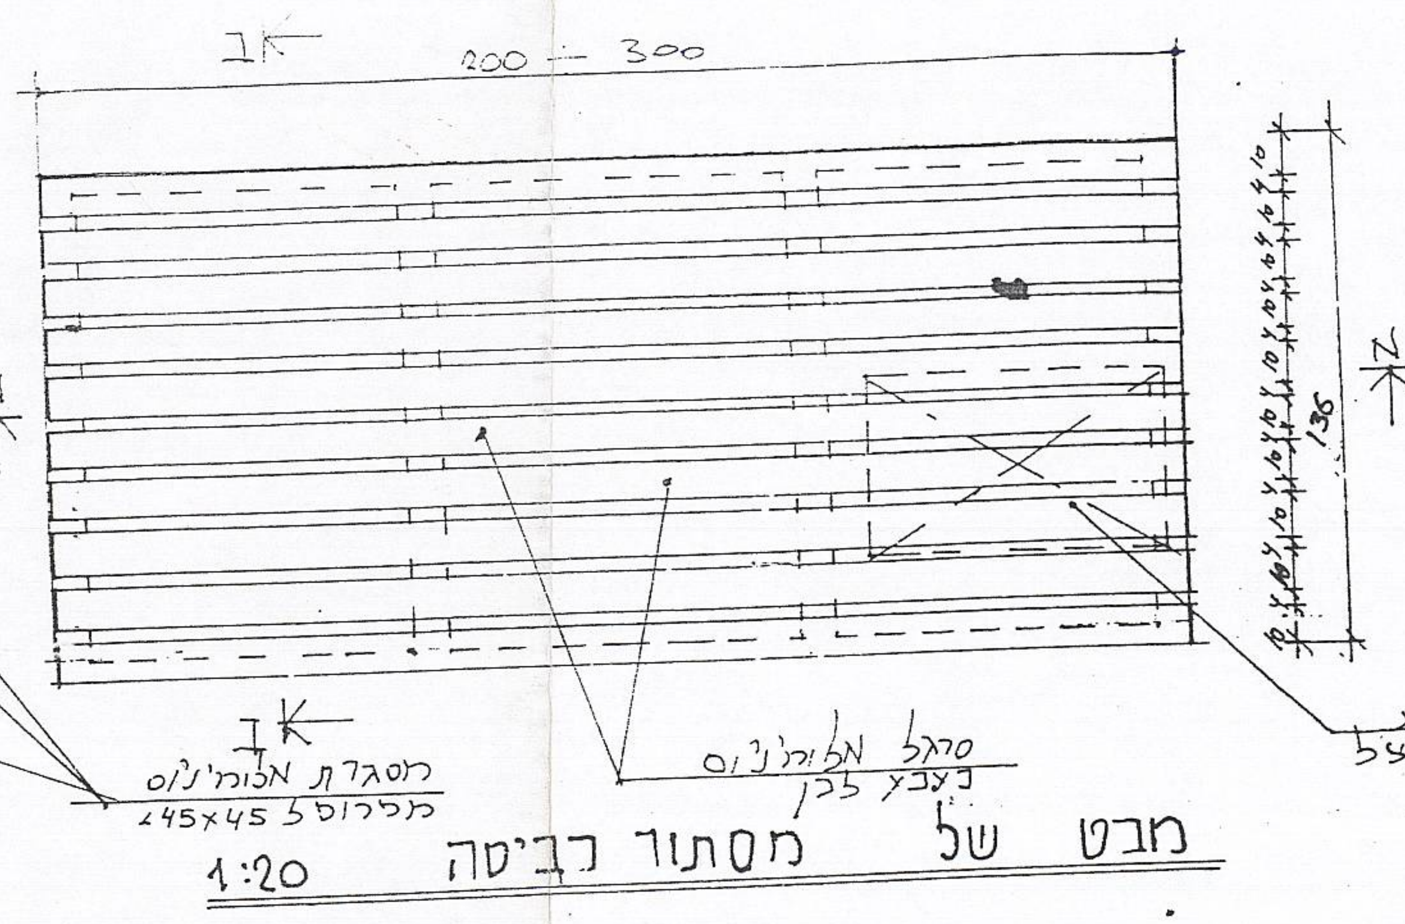

ב
200 — 300
מ
135
מ
ב
מסגרת מאלומיניום
פרופיל 45X45
סרגל אלומיניום
בצבע לבן
מיקום מנוע
מזגן מפוצל

מבט של מסתור כביסה 1:20

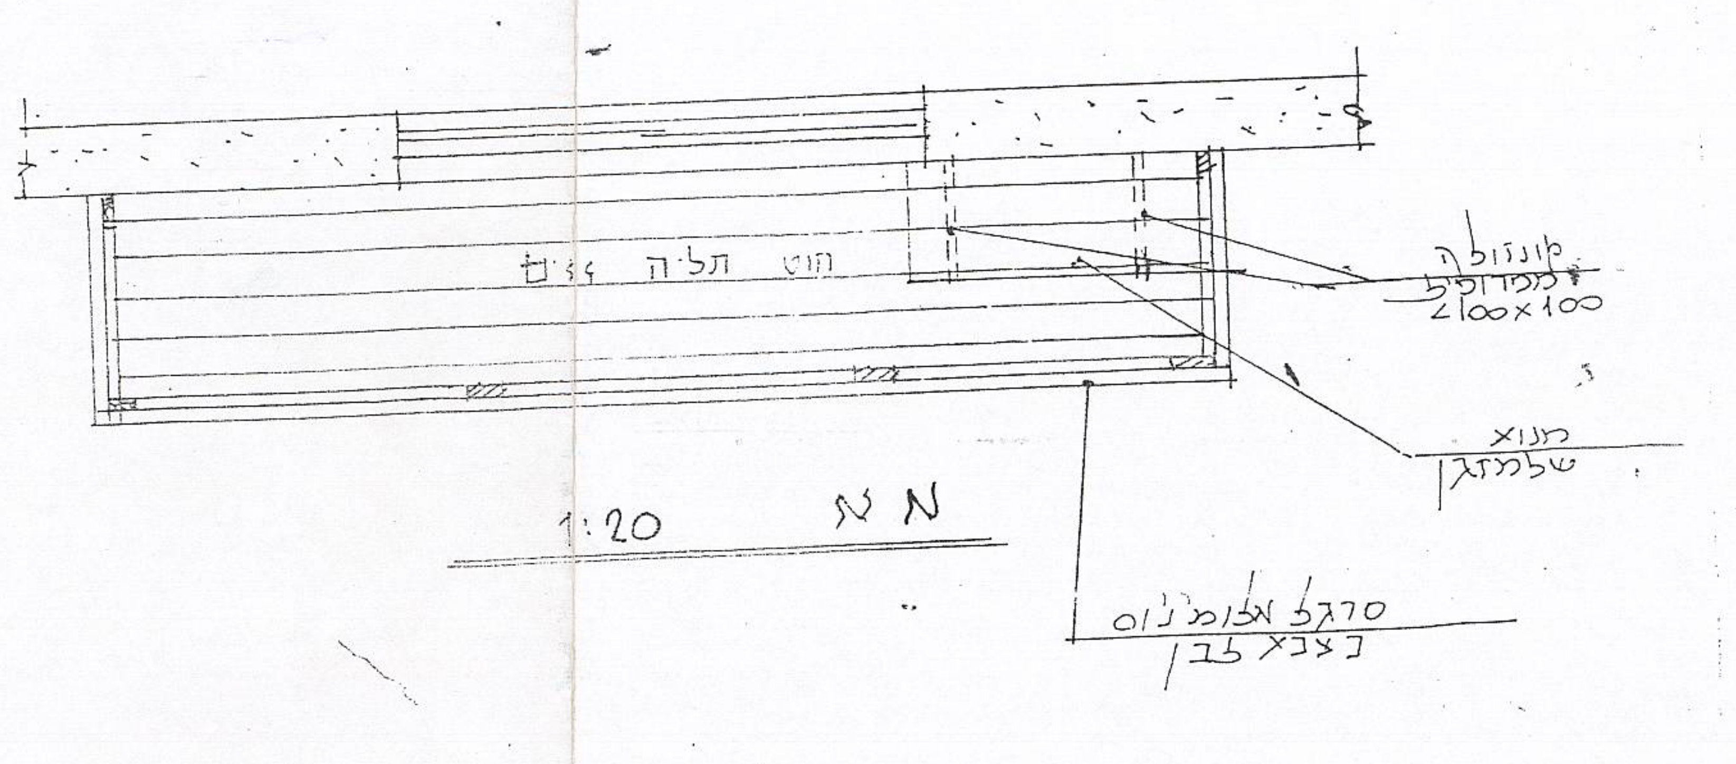

חוט תליה ניילון
קונזולה
פרופיל
100X100
מנוע
של מזגן
סרגל אלומיניום
בצבע לבן

מ מ 1:20

המרחב המוגן הקומתי יבנה בהתאם לתקנות ההתגוננות האזרחית (מפרטים לבניה מקלטים)

תיקון ; תשנ"א 1991 אשר פורסם בילקוט הפרסומים מס' 5425 מיום 3.3.1992

14.06.94

בתכנון מרחב מוגן קומתי (ממ"ק) יתקימו עקרונות יסוד אלה;

[illegible]

ללא קורות ו/או עמודים.

ב. רצפת הממ"ק קירותיו ותקרתו יהיו מישוריים וחלקים.

ג. קירות הממ"קים בבנינים רבי קומות יהיו רציפים לכל גובה הבנין, ליצירת [illegible] מוגן.

ד. יציבות המגדל המוגן של הממ"קים תובטח מפני כוחות אופקיים.

ה. העובי המזערי של חלקי הממ"ק יהיה כאמור בתקנה 208.

ו. תכנון שלד הממ"ק ייעשה בהתאם ל-ת"י 466.

ז. מידת פתח אור מיזערים לדלת כניסה יהיה 80/200 או 70/200. סוג דלת הכניסה (דלת הדף) דלת בטחון הג"א.

ח. הגנה על דלת כניסה - כמפורט בתקנות (ע"י מחיצות.

ט. מידת פתח אור לחלון 110/110 תקני לפי פרטי הג"א ובאישור רשות מוסמכת. גובה תחתית חלון מרצפת החדר לא יהיה קטן מ-1,20 מ'.

י. יש להתקין צינורות אוורור לכל 20 מ"ר שטח ממ"ק [illegible]

כ. יש להתקין מקום מוסתר עם ערכת ב"כ כימי מאושר ע"י רשות הג"א.

הבטון

הבטון בכל חלקי הממ"ק יהיה מסוג ב- 30 לפי דרישות ת"י 118.

החוזק האופיני וחוזקי תוכן הבטון , יקבע לפי ה"י 466.

הכנת הממ"ק למערכות השמל ותקשורת:

באחד מקירות הממ"ק יותקן מוביל לצורך הכנת קבל טלפון ,תיבת הסתעפות,לטלפון ונקודת טלפון, הכל לפי דרישות והנחיות חברת ה"בזק"

בכל מרחב מוגן קומתי יותקנו לפחות 2 בתי תקע לחיבור מכשיר טלוויזיה ולרדיו, ובב על כל 20 מ"ר שטח ממ"ק יותקנו ליד כל ציבור איוורור בית תקע נוסף.

מבתי התקע יוביל אלחוץ לממ"ק צינור הזנה אשר לא יפחת מ-Ø 16 מ"מ.

חיבור הקשורת לאנטנה ולרדיו יהיה צמוד לבתי התקע החשמליים.

[illegible] בכל הממ"ק עוד שני בתי תקע . חופשיים לשימוש אחר.

כל בתי התקע החשמליים יהיו בזרם רגיל של 220 וולט.

תאורת הממ"ק תהיה מתאורה פלורסנטית של שני גופי תאורה לפחות עם שני נורות של 36 ואט כל אחת.

לתאורת חירום תותקן מנורה פלורסנטית כפולה של 36 ואטx2, למשך זמן תאורה של 4 שעות

עבודות גימור

פני הדופן הפנימית של קירות זתקרת הממ"ק יהיו חלקים עם גמר יציקת הבטון, ואין לטייח אותם.

הגימור יהיה בצבע או בציפוי אקרילי אשר לא יעלה על 2 מ"מ עובי.בגוון לבן. סביב הפתחים יצבע בצבע פולט אור ברוחב 10 ס"מ בחלקו הפנימי בלבד.

לא יהיה כל ציפוי של אריחים מכל סוג שהוא בקירות הפנים של הממ"ק.

רצפת הממ"ק תרוצף באריחי מוזאיקה רגילים או קרמיקה , או לצפות עם כל חומר אחר בגון ; ססיתי פי.וי.סי או שטיח.שיפולי הריצוף יכולים להיות מהומר גמיש מסוג הציפוי אך לא מקרמיקה חרסינה או מוזאיקה וכ"ו.

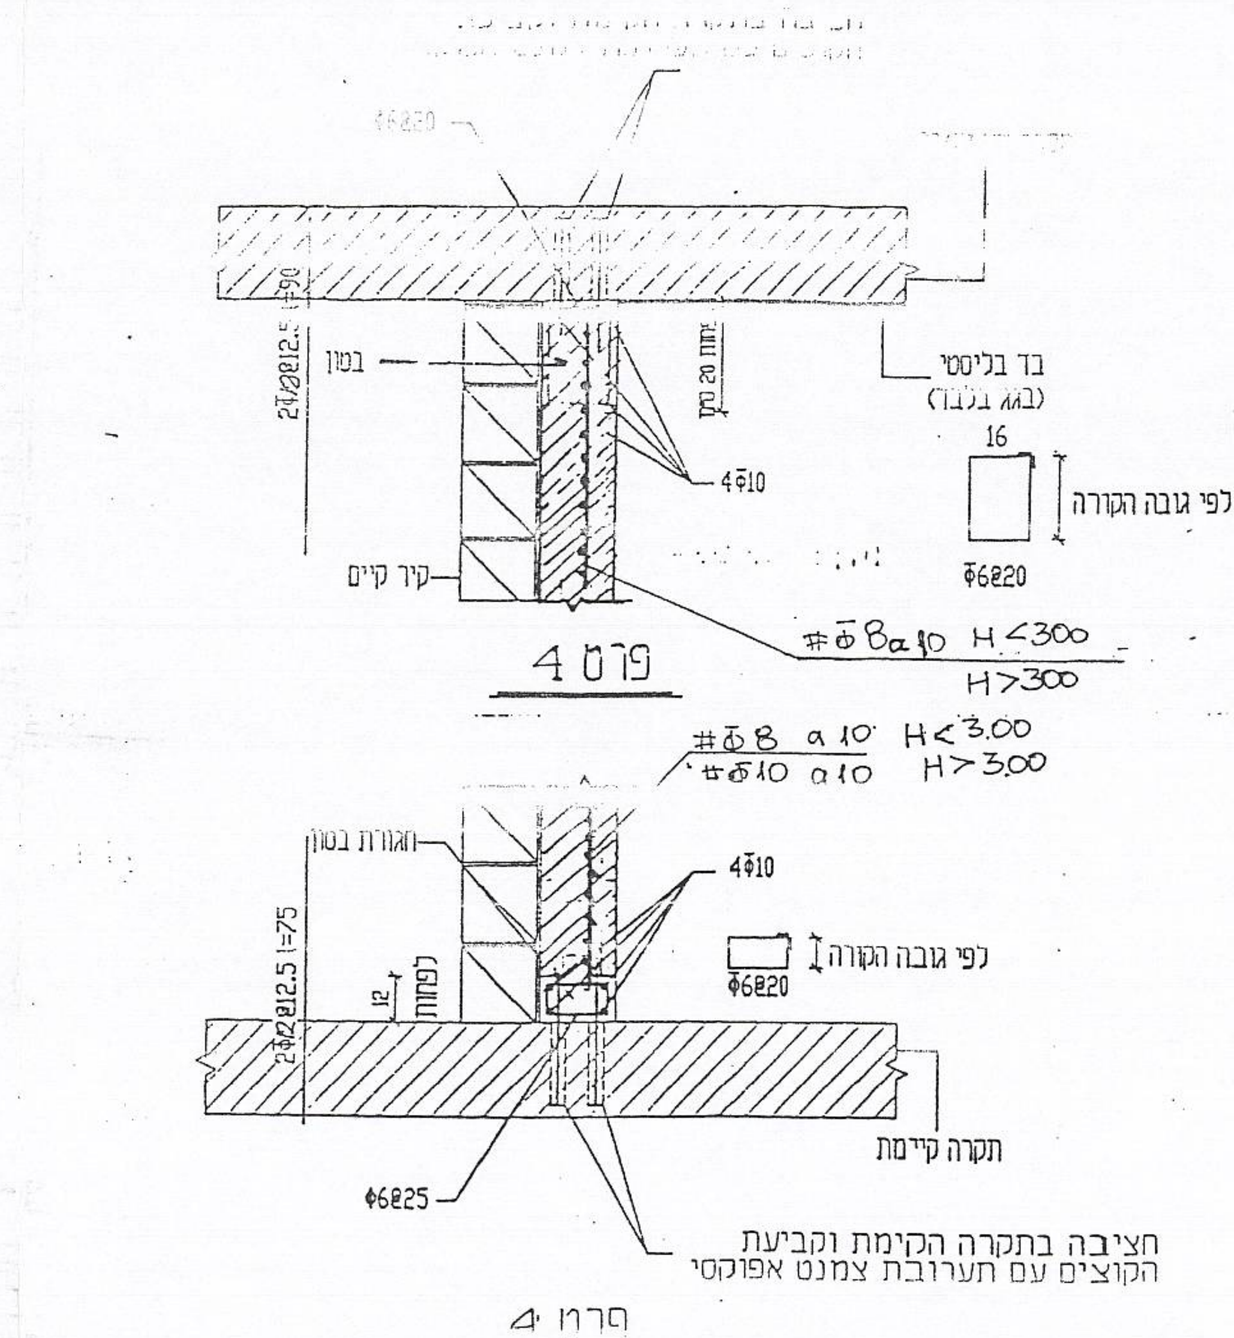

Φ6820
2Φ12@12.5 l=90
בטון
יותר מ-20 ס"מ
4Φ10
קיר קיים
בד בליסטי
(באג בלבד)
16
לפי גובה הקורה
Φ6820
#Φ8@10 H<300
H>300
#Φ8 @10 H<3.00
#Φ10 @10 H>3.00
חגורת בטון
2Φ12@12.5 l=75
לפחות
12
4Φ10
לפי גובה הקורה
Φ6820
Φ6825
תקרה קיימת
חציבה בתקרה הקימת וקביעת
הקוצים עם תערובת צמנט אפוקסי

פרט 4

פרט 4

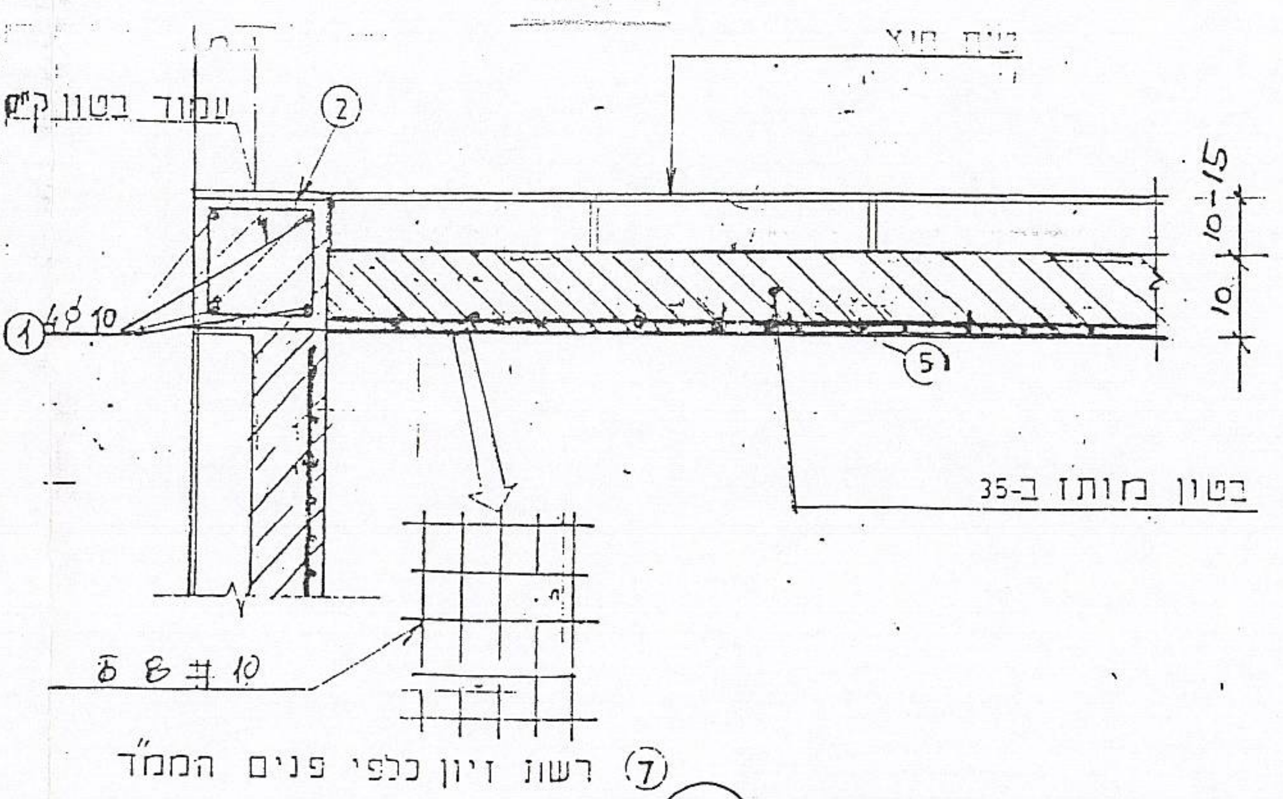

טיח חוץ
עמוד בטון קיים
②
①
4Φ10
⑤
10-15
10
10
בטון מותז ב-35
Φ8 # 10

⑦ רשות זיון כלפי פנים הממ"ד

③ פרטי קיר פנימי

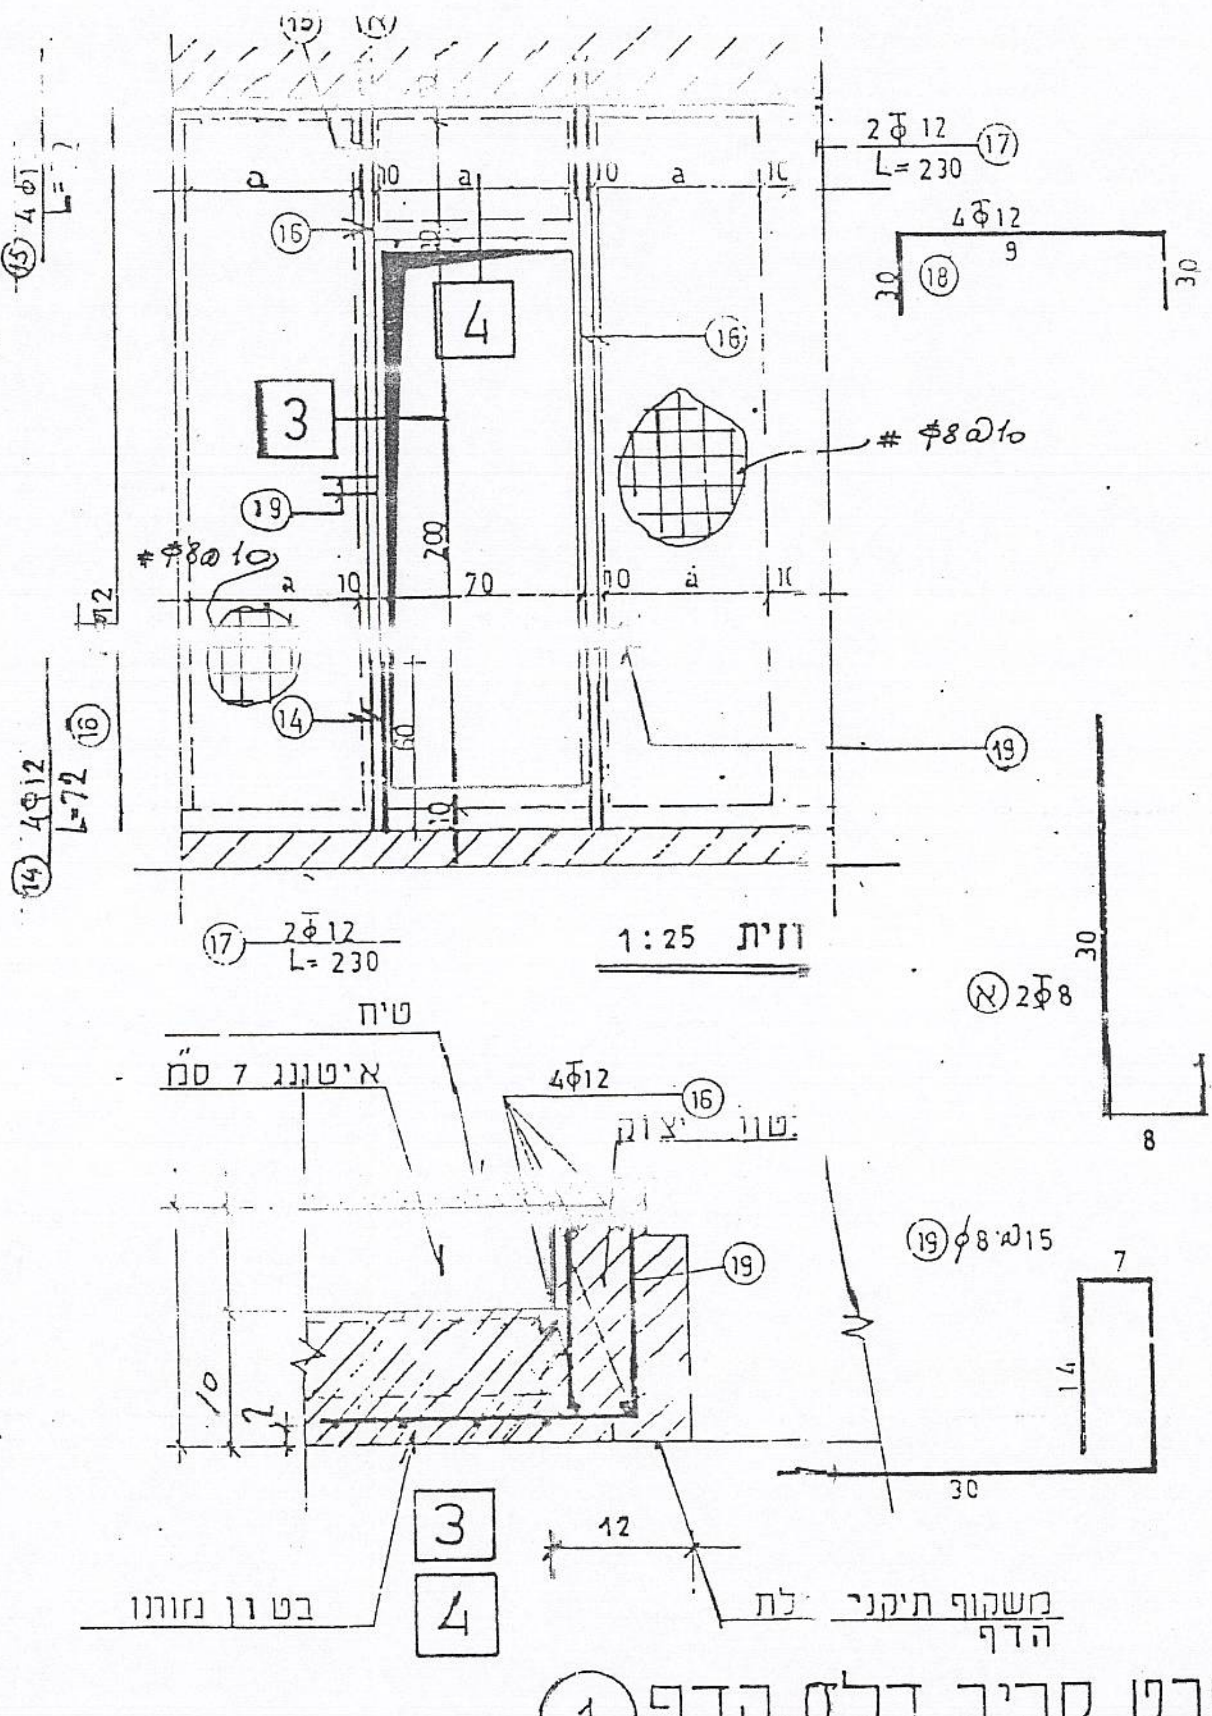

⑮ 4Φ1
L=
a
10
a
10
a
10
⑯
4
⑯
3
⑲
#Φ8@10
200
70
a
10
10
a
10
12
#Φ8@10
⑭
⑯
4Φ12
L=72
⑭
60
10
⑲
2Φ12
L=230
⑰
2Φ12
L=230
⑰
4Φ12
9
30
⑱
30
1:25 חזית
טיח
איטונג 7 ס"מ
4Φ12
⑯
בטון יצוק
⑲
10
2
3
4
בטון נזותז
12
משקוף תיקני דלת הדף
Ⓐ 2Φ8
30
8
⑲ Φ8 מ'15
7
14
30

① פרט סביב דלת הדף

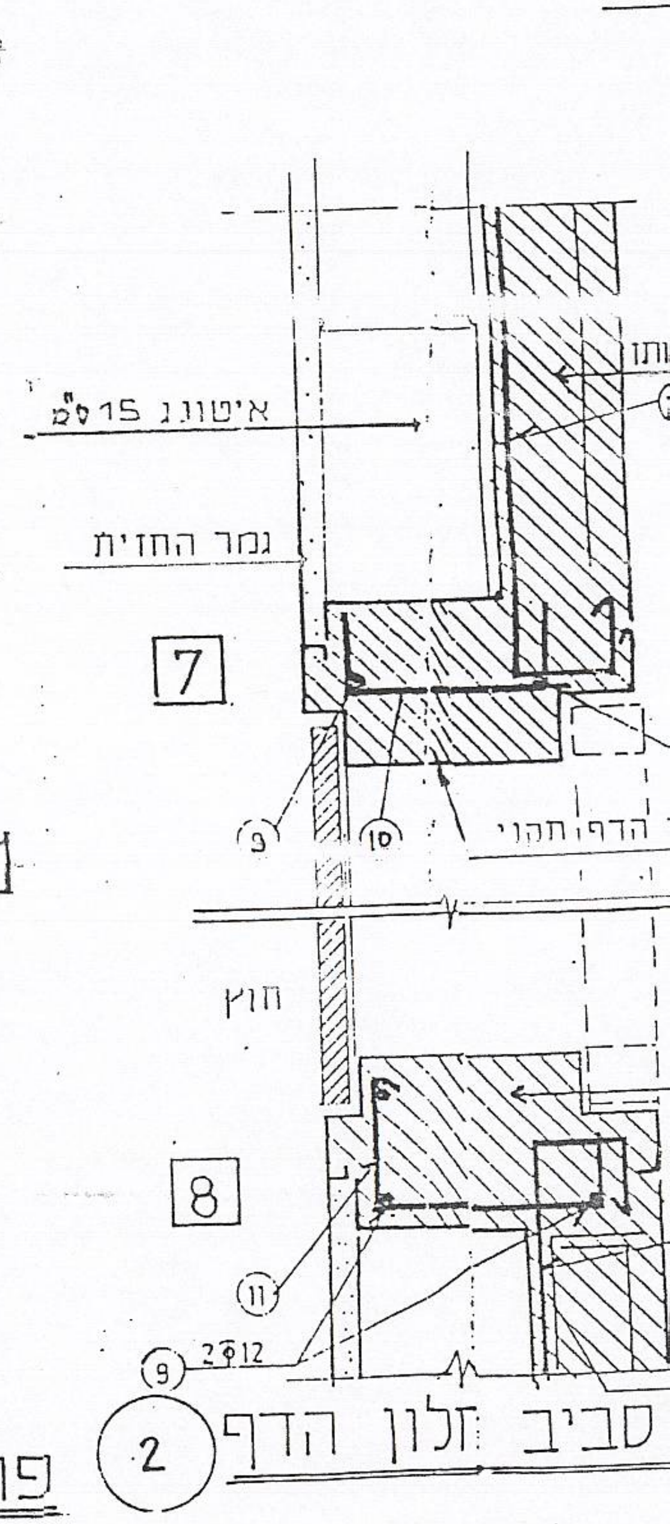

פרט
איטונג 15 ס"מ
נמר החזית
7
⑩
⑨
הדף תהוי
חוץ
8
⑪
⑨ 2Φ12

② סביב חלון הדף