סוף מסמך

20/06/2006

סיכום בדיקה - תחנה אדריכל רישוי בקשת מידע 200600146 בכתובת: אביטל 2

תיק בניין: 4062-002

החלטת תחנה מ-20/06/2006 : המלצה להיתר

ממליץ לאשר את תוספת הבניה כמבוקש.

מטפל דוד גיטמן

29/10/2006

סיכום בדיקה תחנה פיקוח בניה בקשה 20061503 לכתובת אביטל 2

החלטת תחנה מ-29/10/2006 : תוכנית תואמת את המצב בשטח

תוכנית תואמת את המצב בשטח
המבוקש בנוי במלואו

תביעות
הוגשה תביעה משפטית תיק פלילי מס' 01040007061
.01060010785

מטפל: איציק אשל

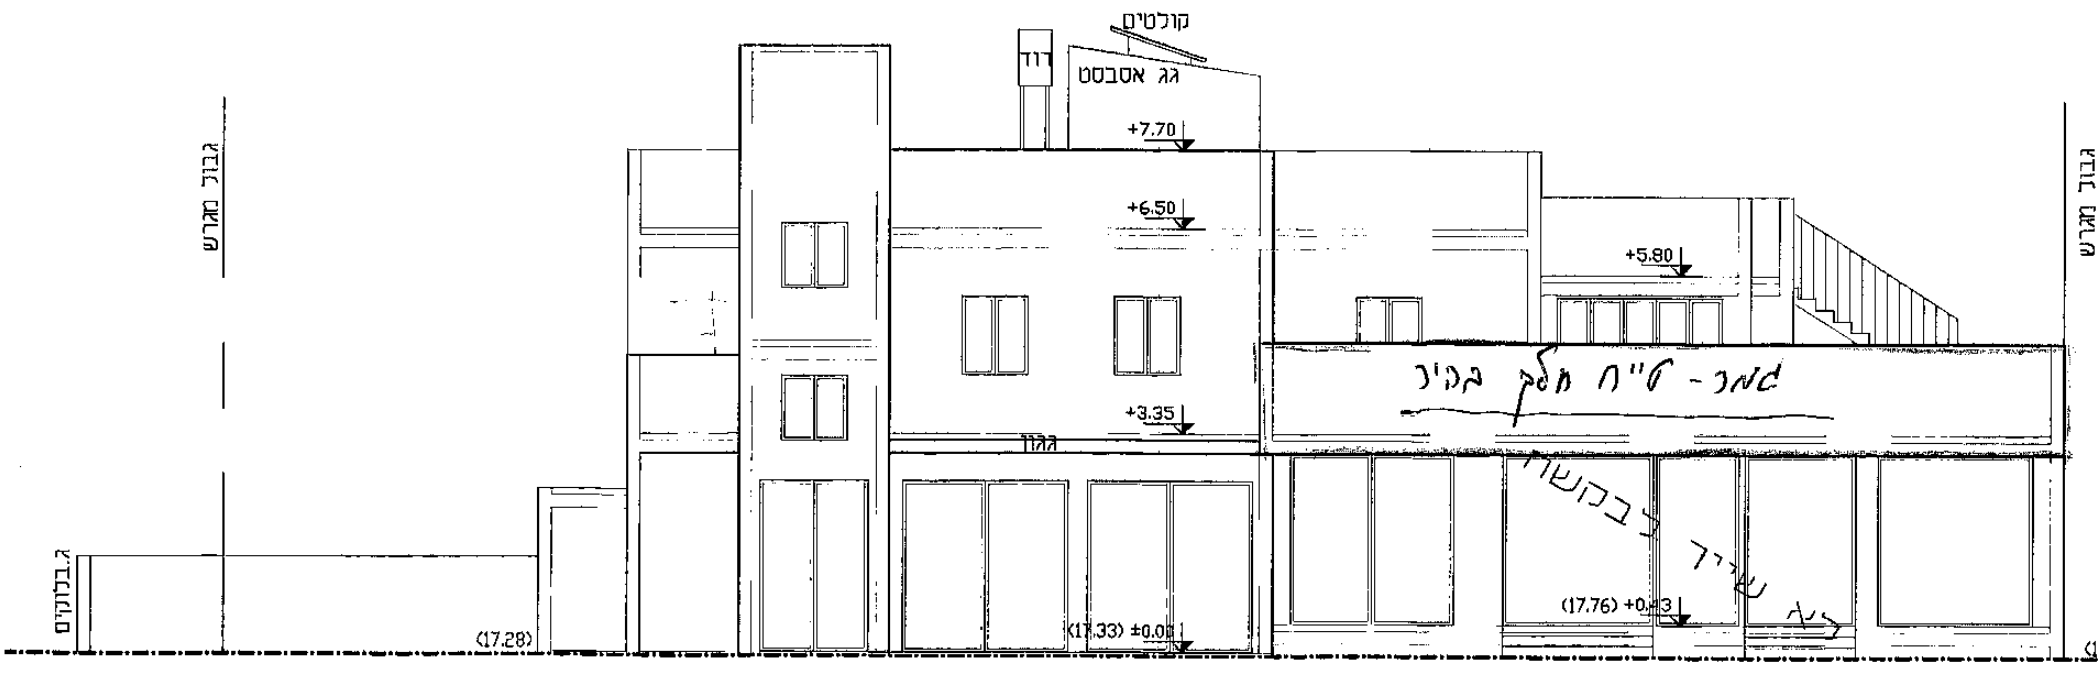

גג אסבסט
סולרים
+7.70
+6.50
+5.80
+3.35
±0.00
גבול מגרש
לא שייך לבקשה
(17.28)
(17.76)

חזית מערבית קנ"מ 1:100

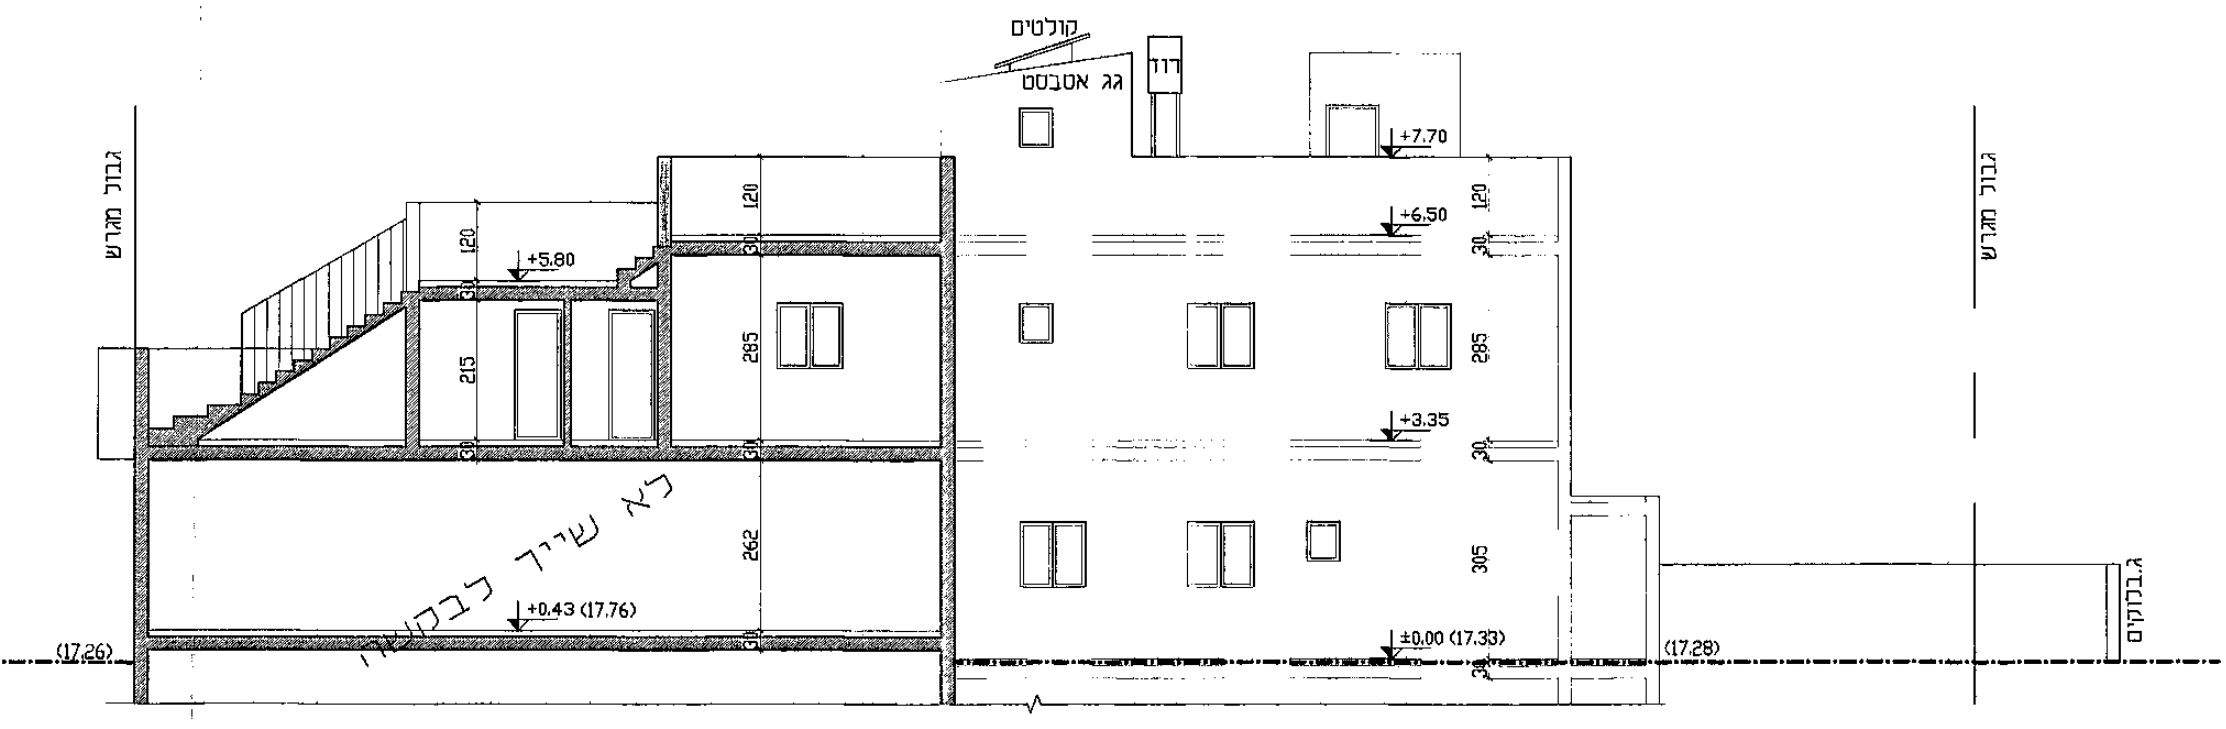

גג אסבסט
סולרים
+7.70
+6.50
+5.80
+3.35
±0.00 (17.33)
+5.43 (17.76)
גבול מגרש
לא שייך לבקשה

חתך א-א קנ"מ 1:100

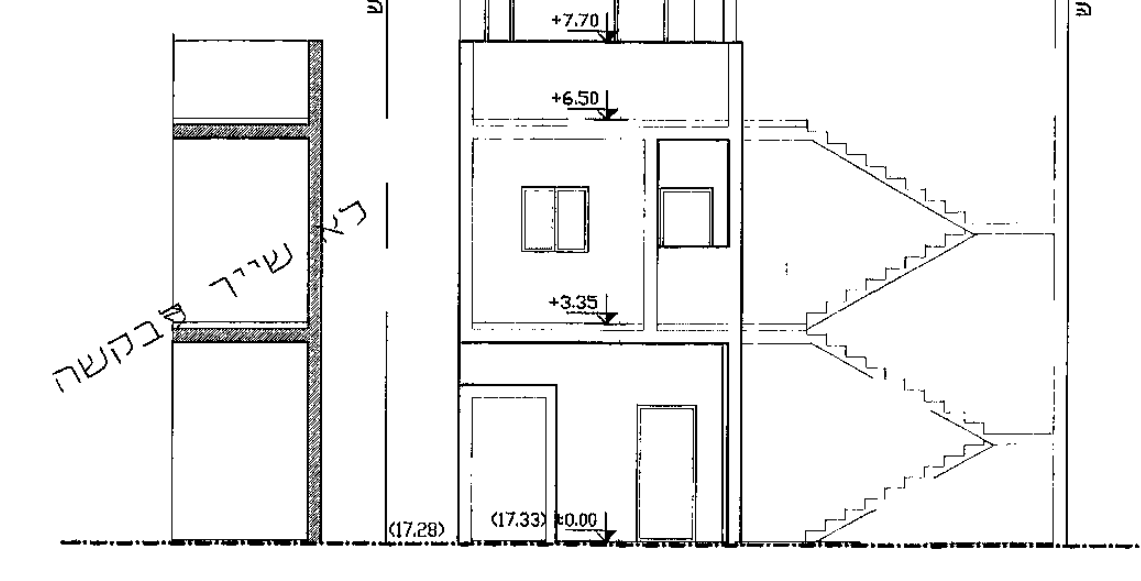

גג אסבסט
גבול מגרש
+7.70
+6.50
+3.35
±0.00
לא שייך לבקשה

חזית צפונית קנ"מ 1:100

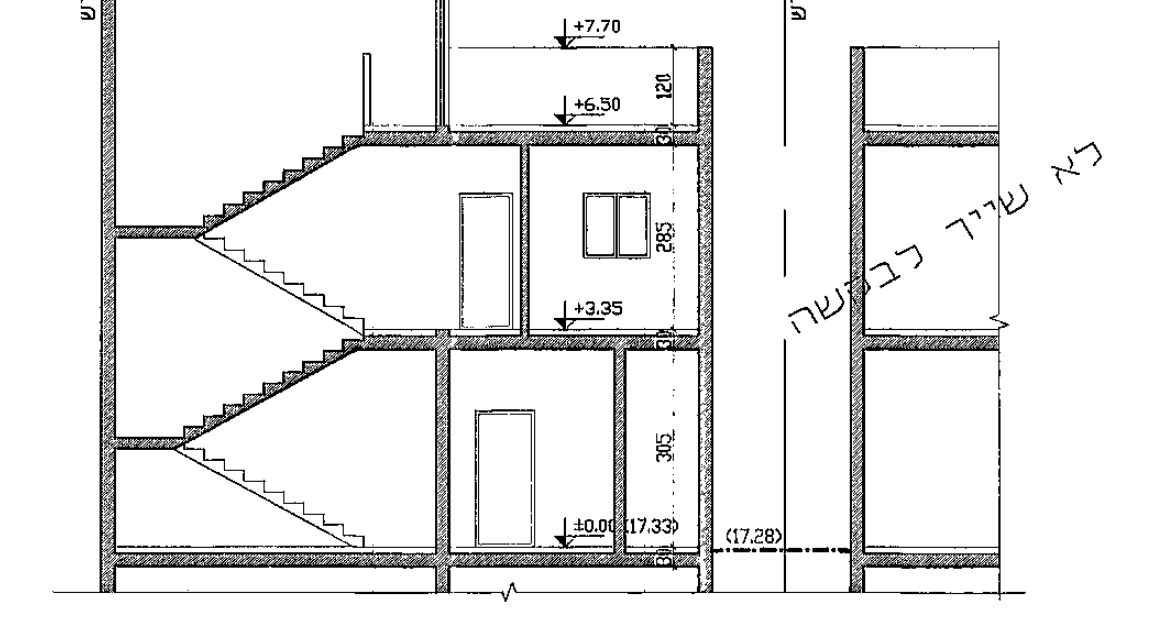

גבול מגרש
+7.70
+6.50
+3.35
±0.00
לא שייך לבקשה

חתך ב-ב קנ"מ 1:100

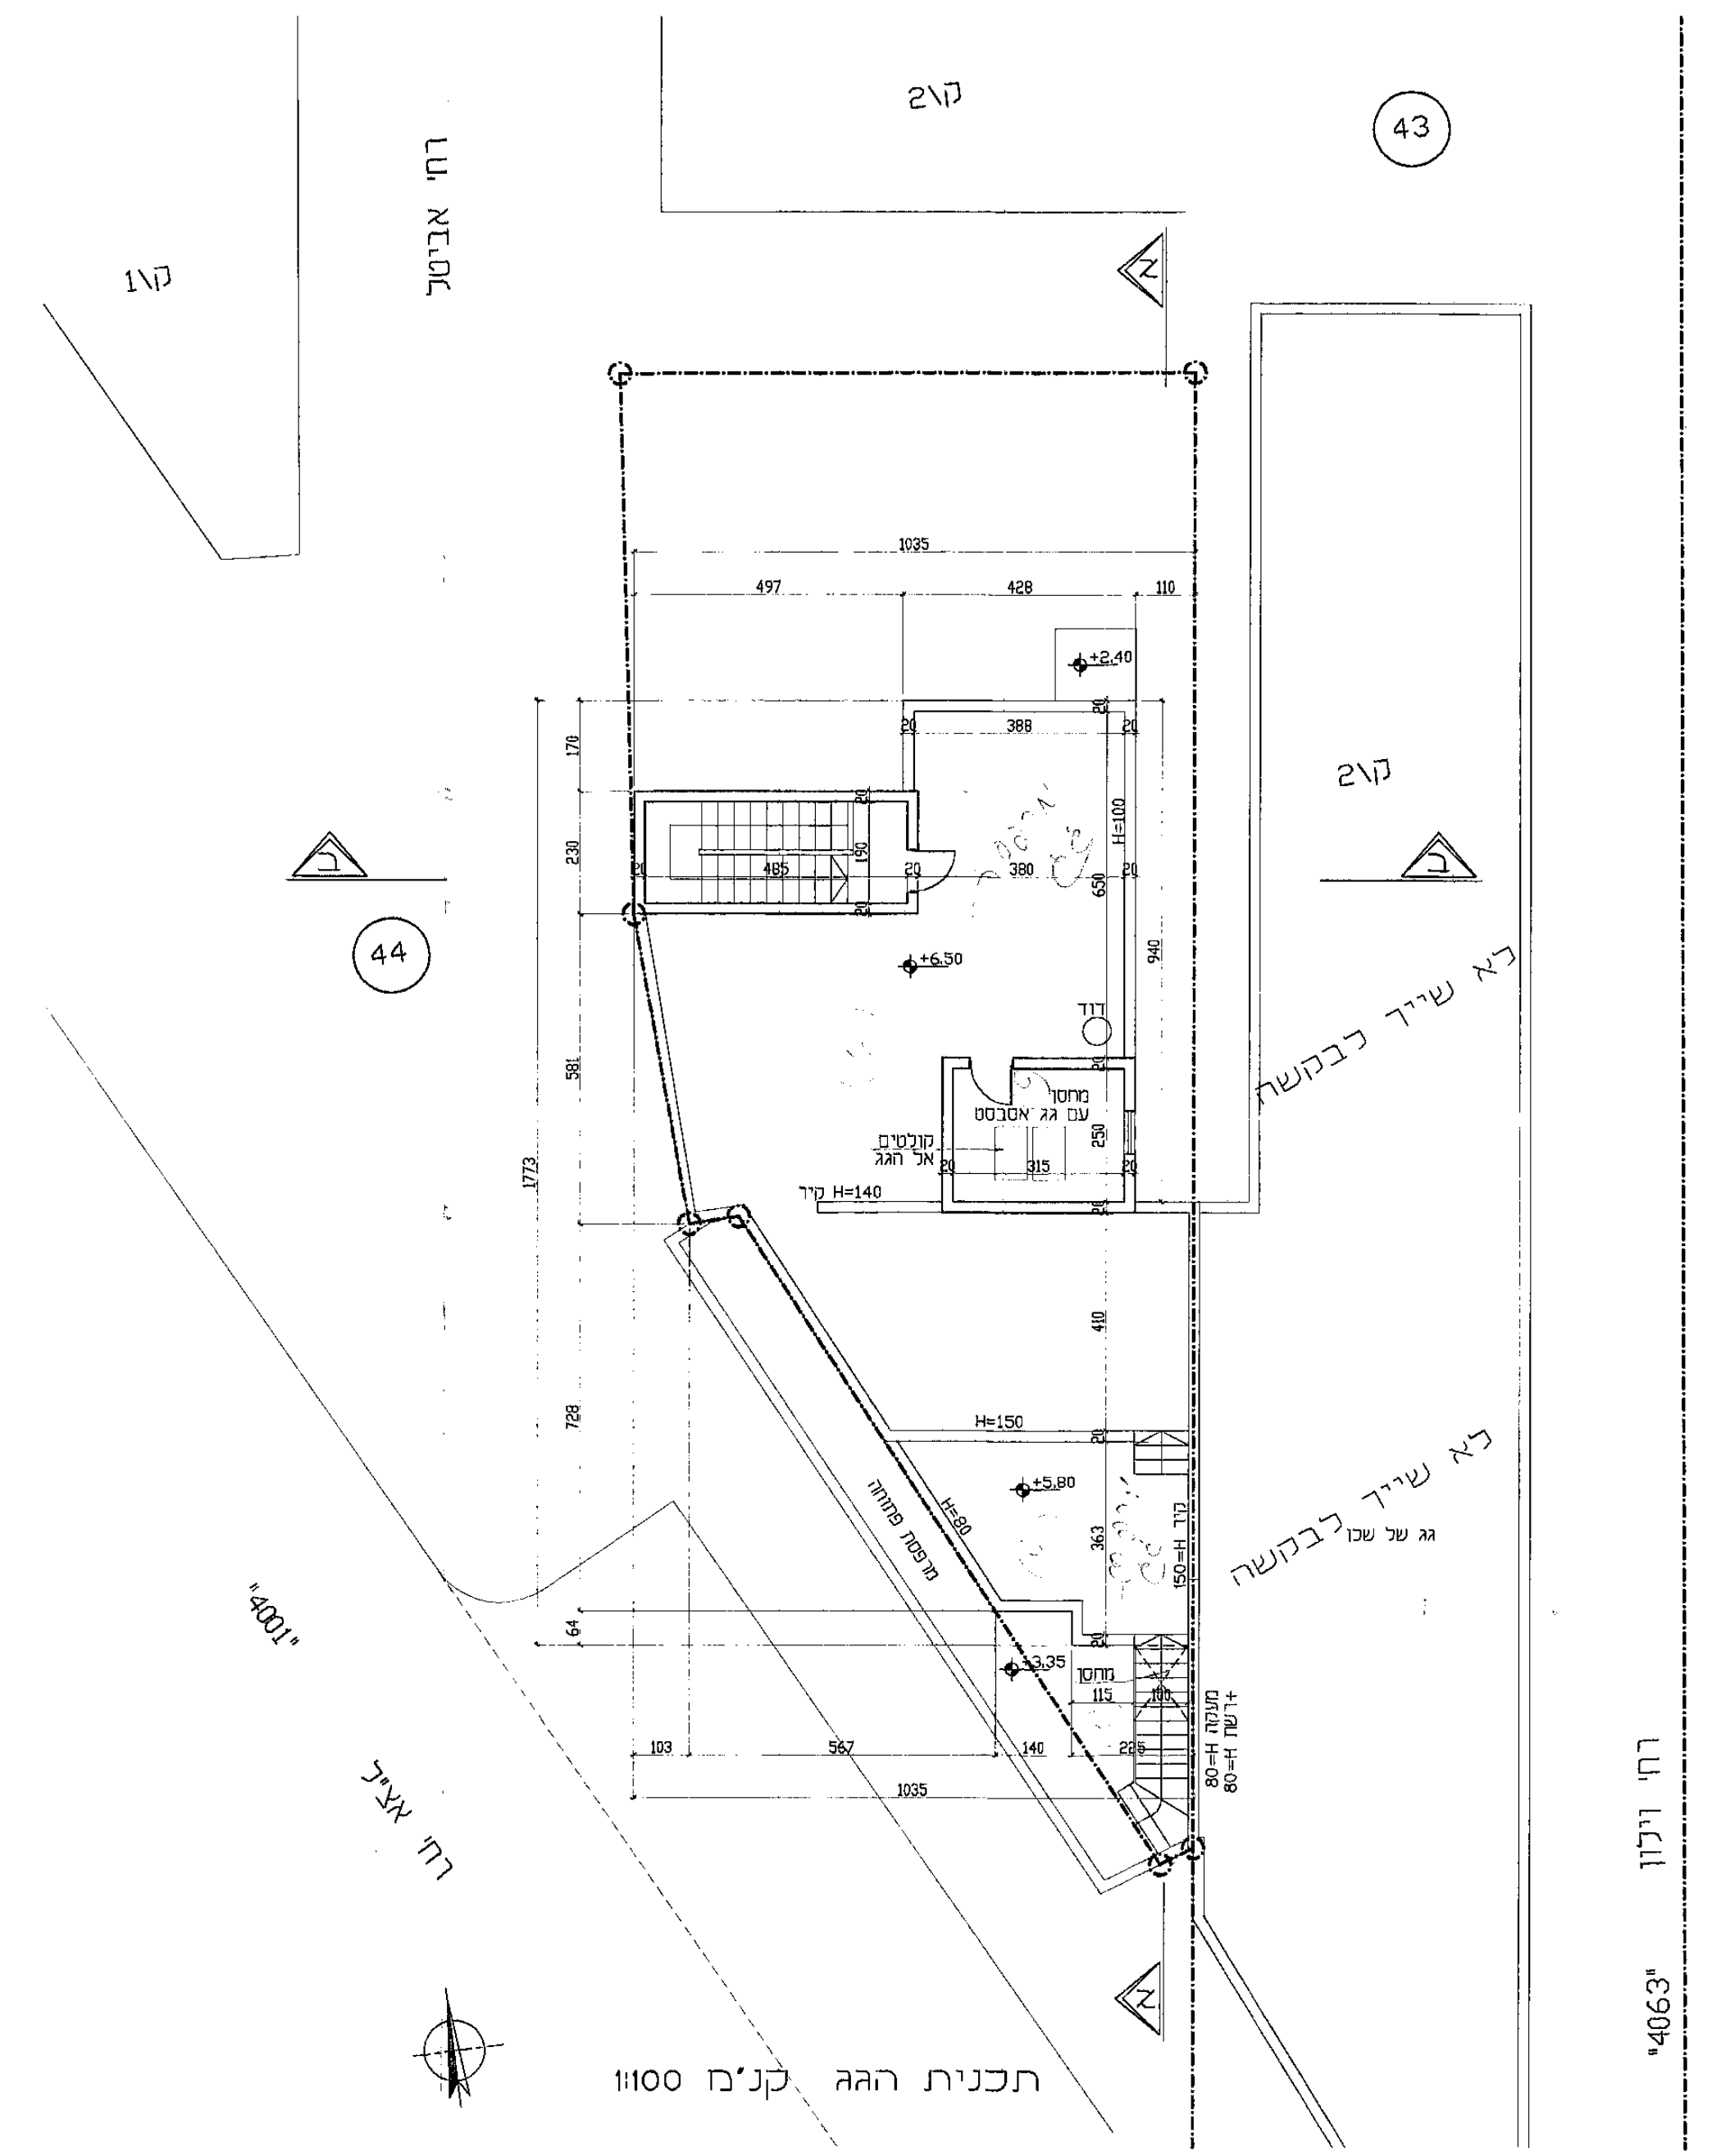

רח' אביטל
ק\1
ק\2
43
44
לא שייך לבקשה
מחסן
גג אסבסט
רח' אצ"ל
רח' ויגון
"4001"
"4063"

תכנית הגג קנ"מ 1:100

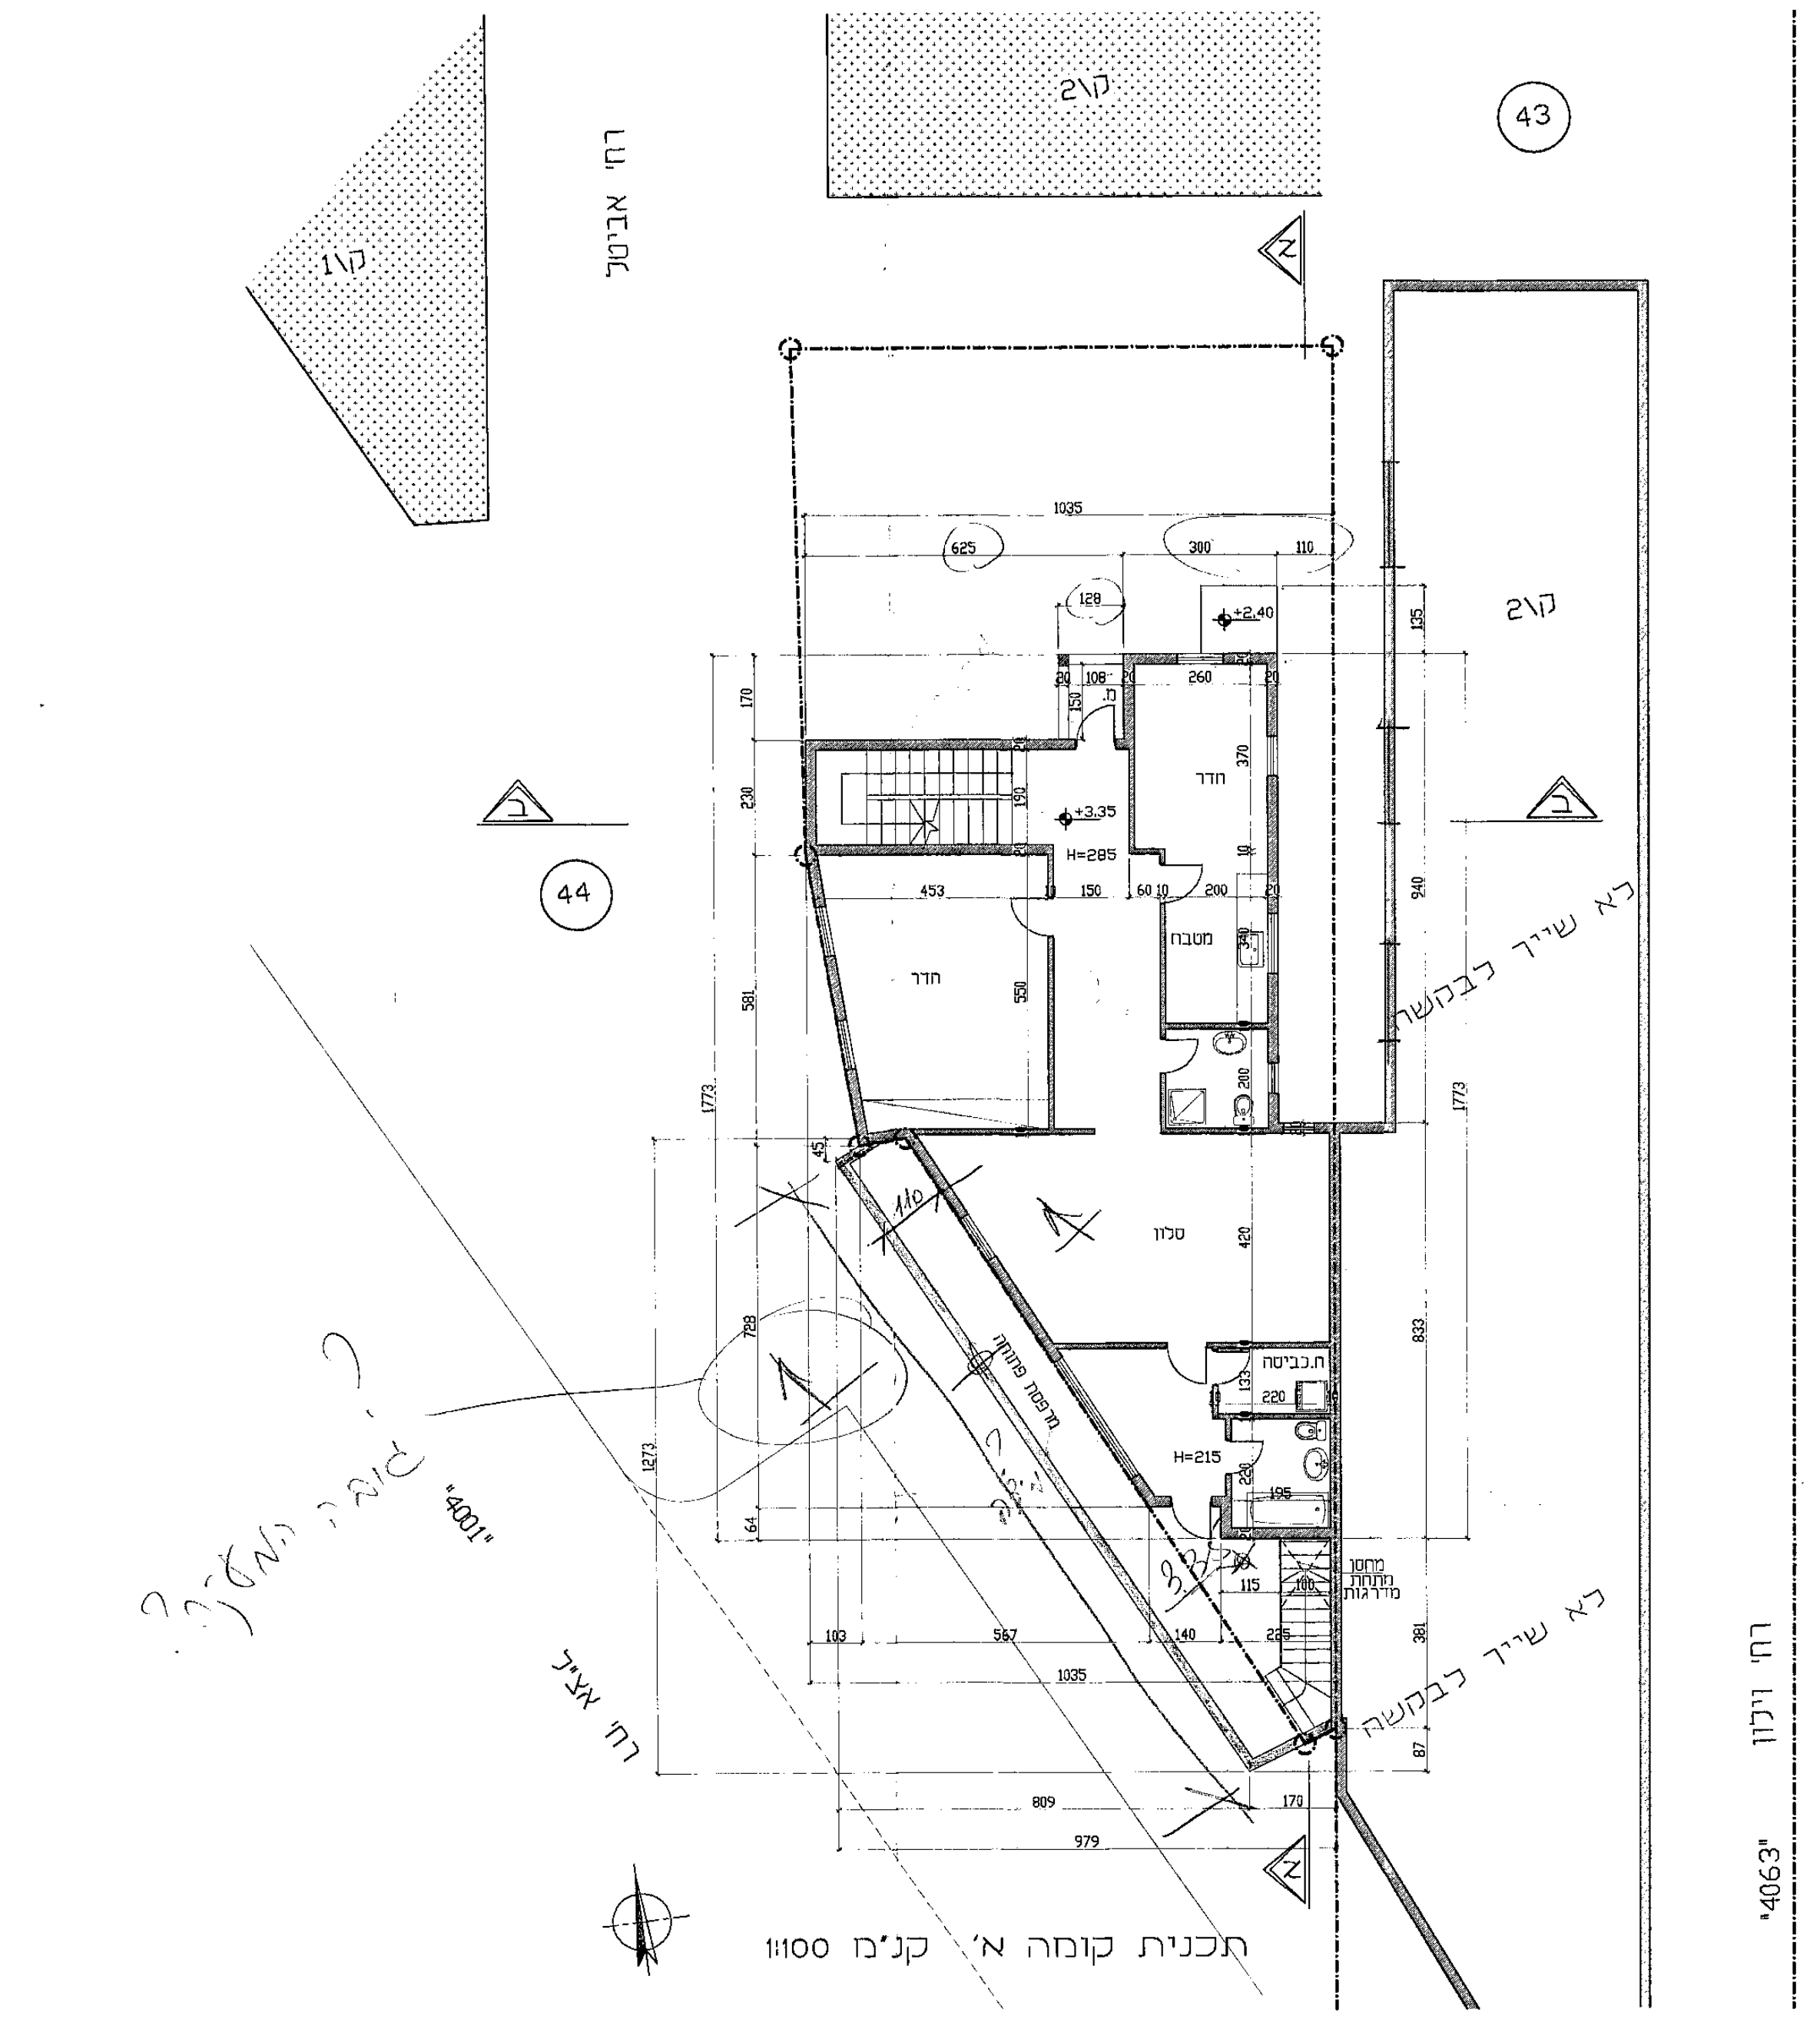

רח' אביטל
ק\1
ק\2
43
44
חדר
מטבח
סלון
לא שייך לבקשה
רח' אצ"ל
רח' ויגון
"4001"
"4063"

תכנית קומה א' קנ"מ 1:100

גומה המשך?

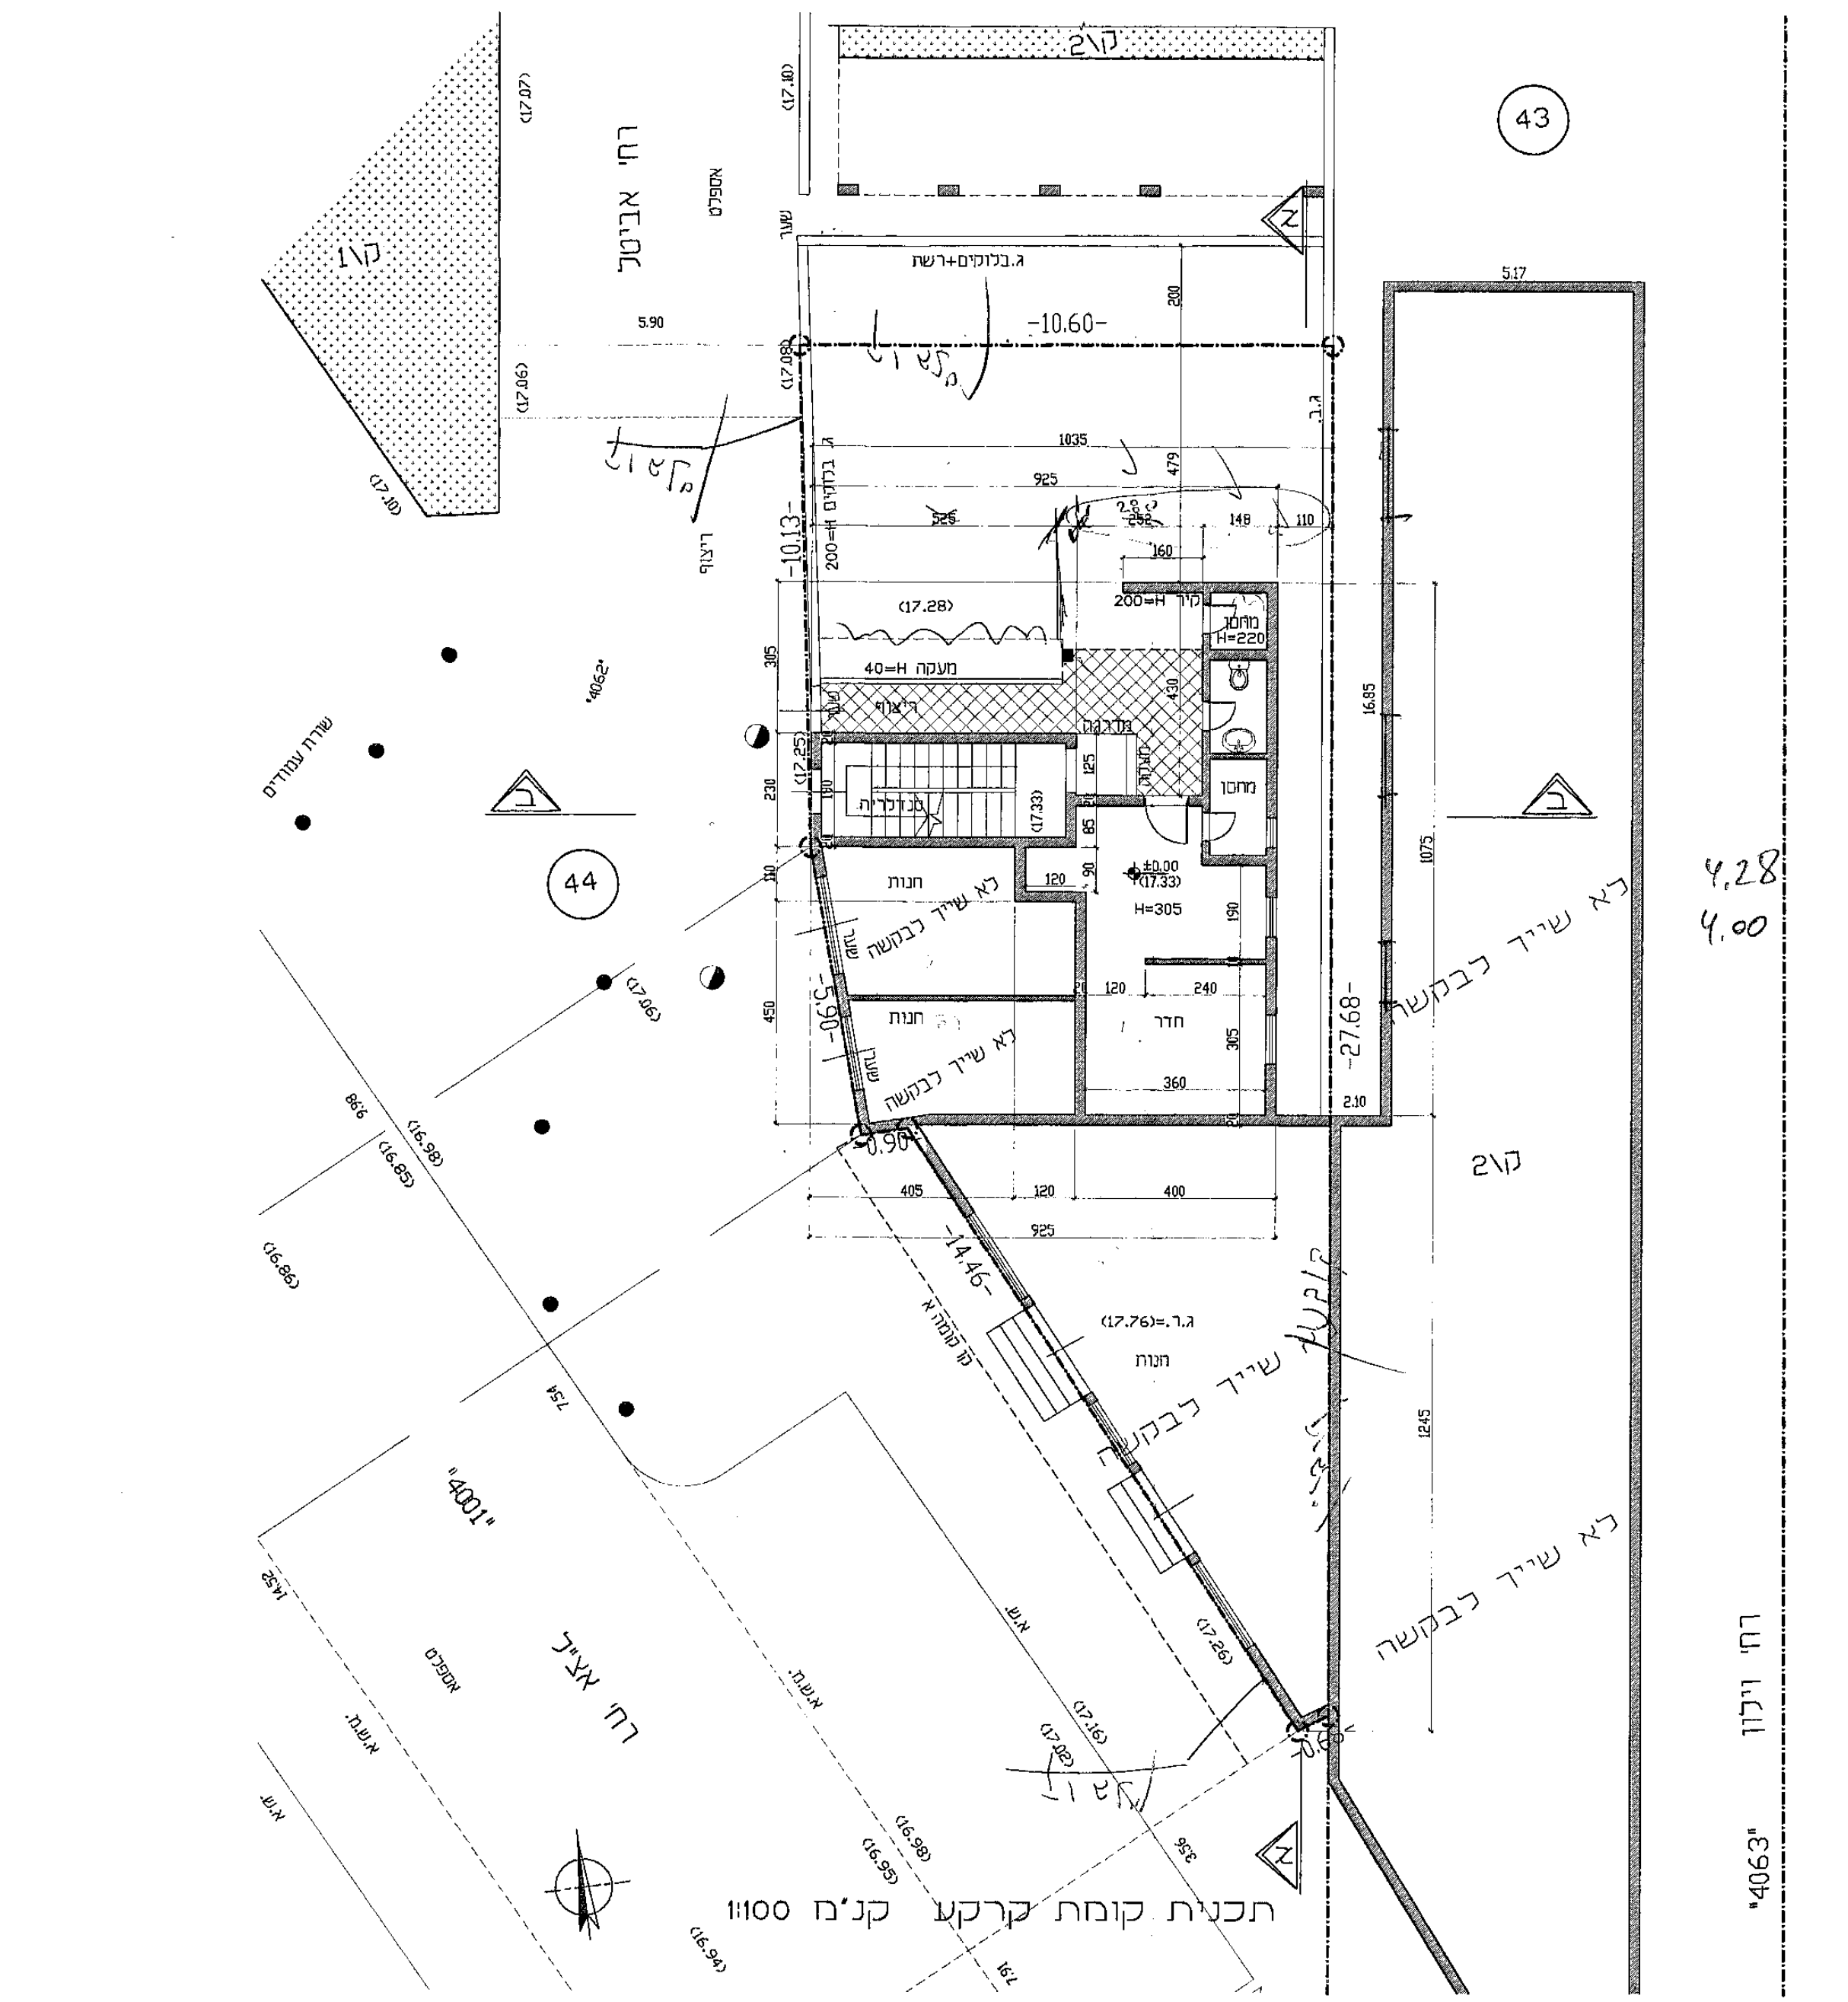

רח' אביטל
ק\1
ק\2
43
44
חנות
חדר
מחסן
לא שייך לבקשה
רח' אצ"ל
רח' ויגון
"4001"
"4063"

תכנית קומת קרקע קנ"מ 1:100

4.28
4.00

חישוב שטחים

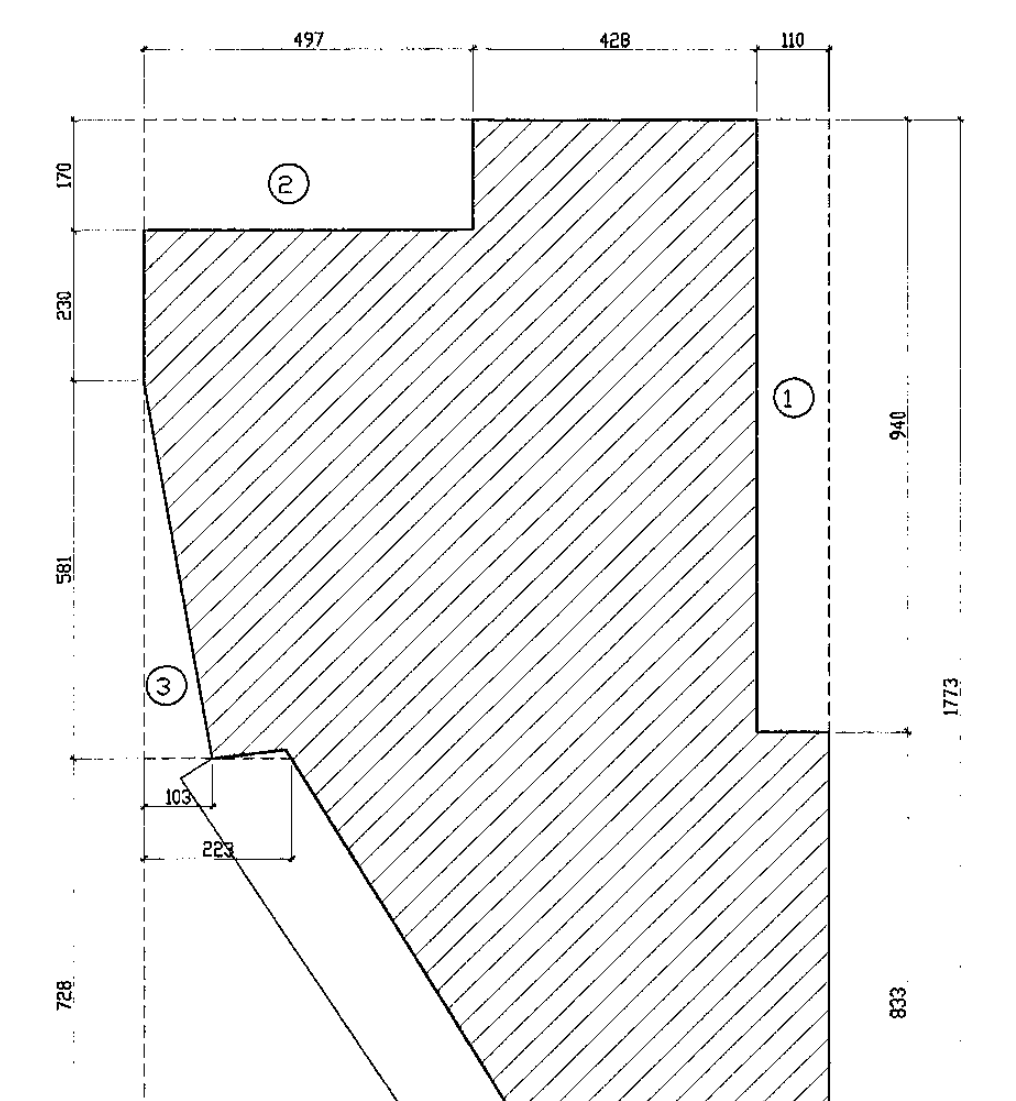

497
428
110
940
1773
1
2
3
4
5

קומה א'

שטח	מס'	חישובים	סה"כ מ"ר
המסגרת	⊕	10.35×17.73=183.50	183.50
ההורדות	⊖ ①	1.10×9.40=10.34	10.34
	⊖ ②	4.97×1.70=8.45	8.45
	⊖ ③	1.03×5.81/2=3.00	3.00
	⊖ ④	(2.23+6.69)/2×7.28=32.47	32.47
	⊖ ⑤	8.10×0.64=5.20	5.20
סה"כ ההורדות		10.34+8.45+3.00+32.47+5.20=59.46	59.46
שטח עיקרי		183.50−59.46=124.04	124.04

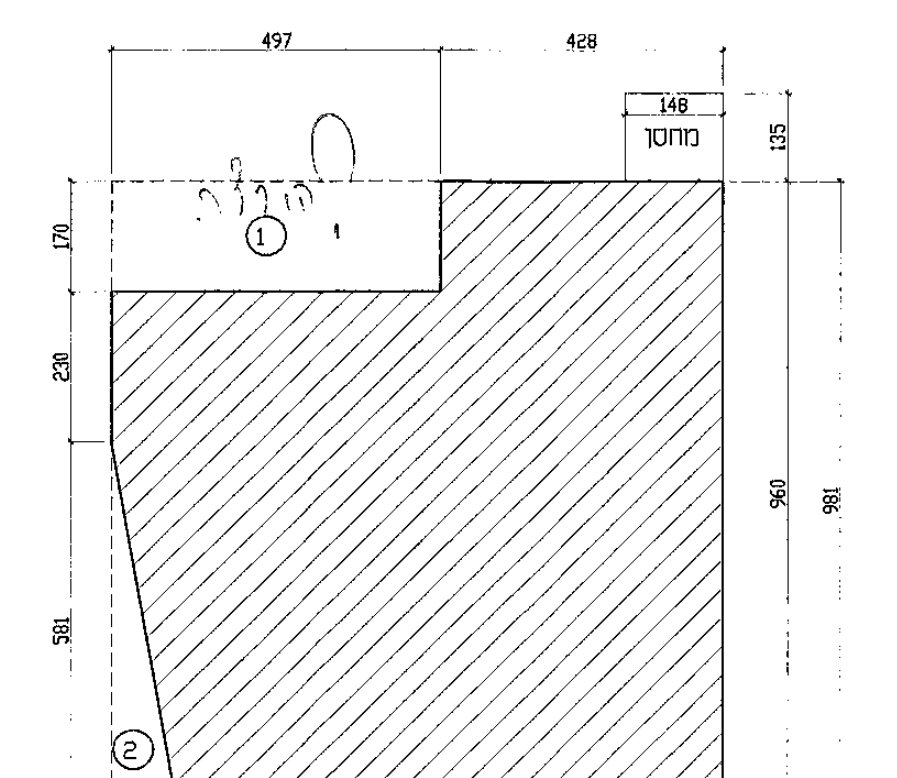

497
428
148
מחסן
135
170
230
581
960
981
103
106
716
925
1
2
3
4

קומת קרקע

שטח	מס'	חישובים	סה"כ מ"ר
המסגרת	⊕	9.25×9.81=90.74	90.74
ההורדות	⊖ ①	1.70×4.97=8.45	8.45
	⊖ ②	1.03×5.81/2=3.00	3.00
	⊖ ③	7.16×0.21=1.50	1.50
	⊖ ④	1.06×0.21/2=0.11	0.11
סה"כ ההורדות		8.45+3.00+1.50+0.11=13.06	13.06
שטח עיקרי		90.74−13.06=77.68	77.68
מחסן		1.48×1.35=2.00	2.00

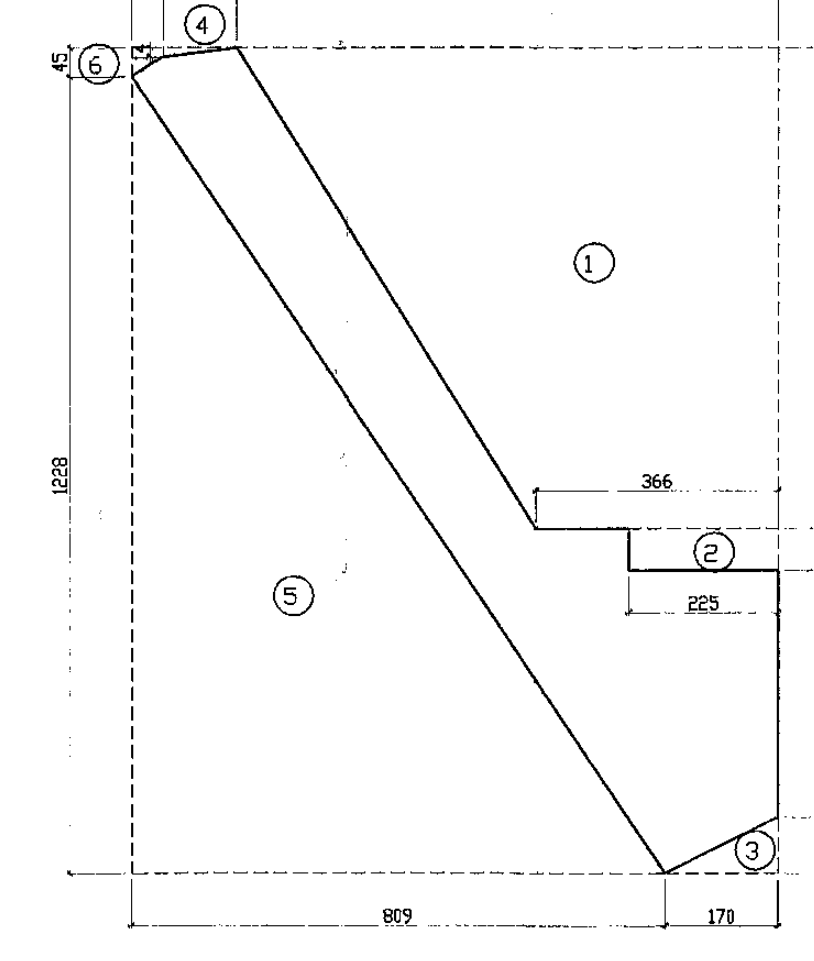

979
820
742
1273
366
225
64
381
87
1
2
3
4
5
6

מרפסת מוצעת

שטח	מס'	חישובים	סה"כ מ"ר
המסגרת	⊕	9.79×12.73=124.63	124.63
ההורדות	⊖ ①	(8.20+3.66)/2×7.42=44.00	44.00
	⊖ ②	2.25×0.64=1.44	1.44
	⊖ ③	1.70×0.87/2=0.74	0.74
	⊖ ④	0.14×1.11/2=0.08	0.08
	⊖ ⑤	12.28×8.09/2=49.67	49.67
	⊖ ⑥	(0.45+0.14)/2×0.47=0.14	0.14
סה"כ ההורדות		44.00+1.44+0.74+0.08+49.67+0.14=96.07	96.07
שטח מרפסת		124.63−96.07=28.56	28.56

תל-אביב
גוש : 6979
חלקה : 44(חלק)
כתובת : רח' אצ"ל 71 פי רח' אביטל 2
הוכן עבור : חילבה ישעיהו
מטרת המדידה : הגדרת מגרש משני עפ"י תב"ע 2215

שם הבעלים כרשום בנסח טאבו+מס' ת.ז : חילבה ישעיהו 255365

שטח לפי נסח :
שטח החלקה כולה : 11.476 ד.מ.
בעלות בחלקים(כרשום בנסח טאבו) : חילבה ישעיהו 92\11476
חילבה ישעיהו 109\11476
חילבה ישעיהו 16\11476

בעלות במ"ר : 217
שטח מדוד(מ"ר) : 217

שטח מגרש משני : ד.מ.
שטח להפקעה : ד.מ.

מפה טופוגרפית
1 : 250

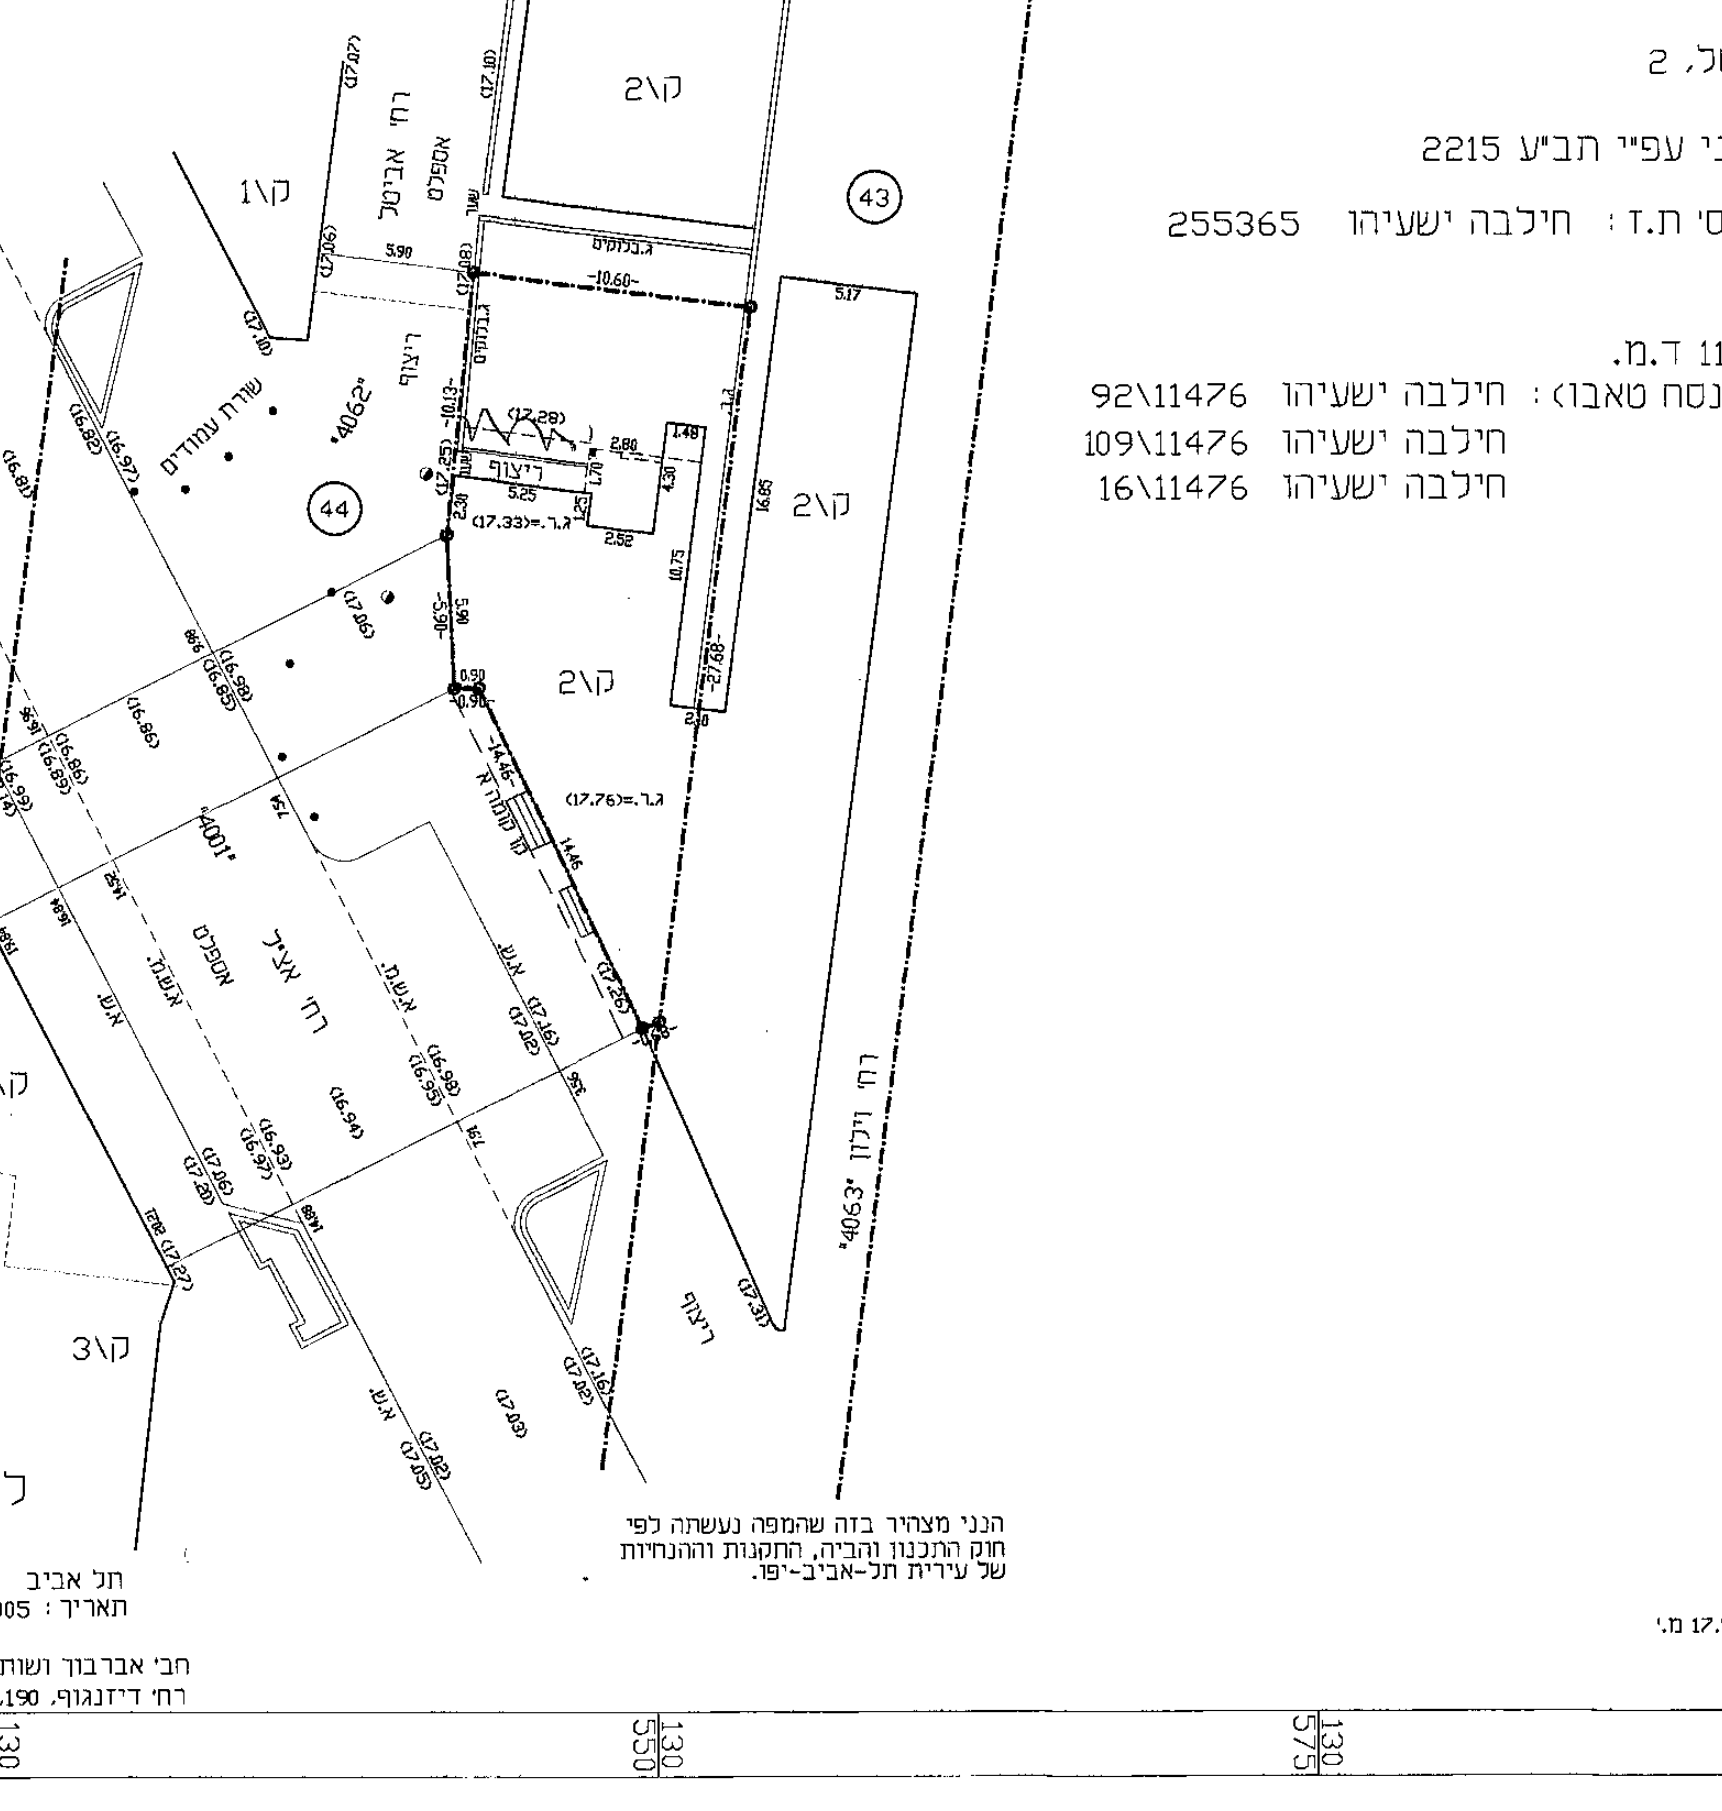

525 130
550 130
575 130
600 130
161 925
161 900
161 875
רח' אביטל
אספלט
ק\1
ק\2
43
44
45
שדרת עמודים
ריצוף
ג.בלוקים
"4062"
"4001"
רח' אצ"ל
רח' ויגון
-10.60-
(17.33)=ג.ר
(17.76)=ג.ר

לא לצרכי רישום

הנני מצהיר בזה שהמפה נעשתה לפי
חוק התכנון והביה, התקנות וההנחיות
של עיריית תל-אביב-יפו.

תל אביב
תאריך : 7.12.2005 י.אברבוך מודד מוסמך
רשיון מס' "461"
חב' אברבוך ושותי מודדים מוסמכים בע"מ
רח' דיזנגוף 190, תל-אביב טל. 03-5226791, 5235891

תרשים הסביבה 1:1250

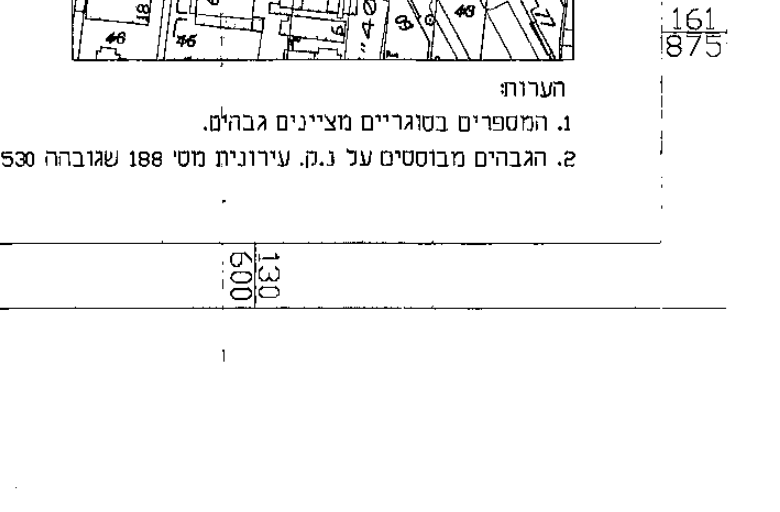

הערות:
1. המספרים בסוגריים מציינים גבהים.
2. הגבהים מבוססים על נ.ק. עירונית מס' 188 שגובהה 17.530 מ'.

- 4.28 +1.48
280
4.28

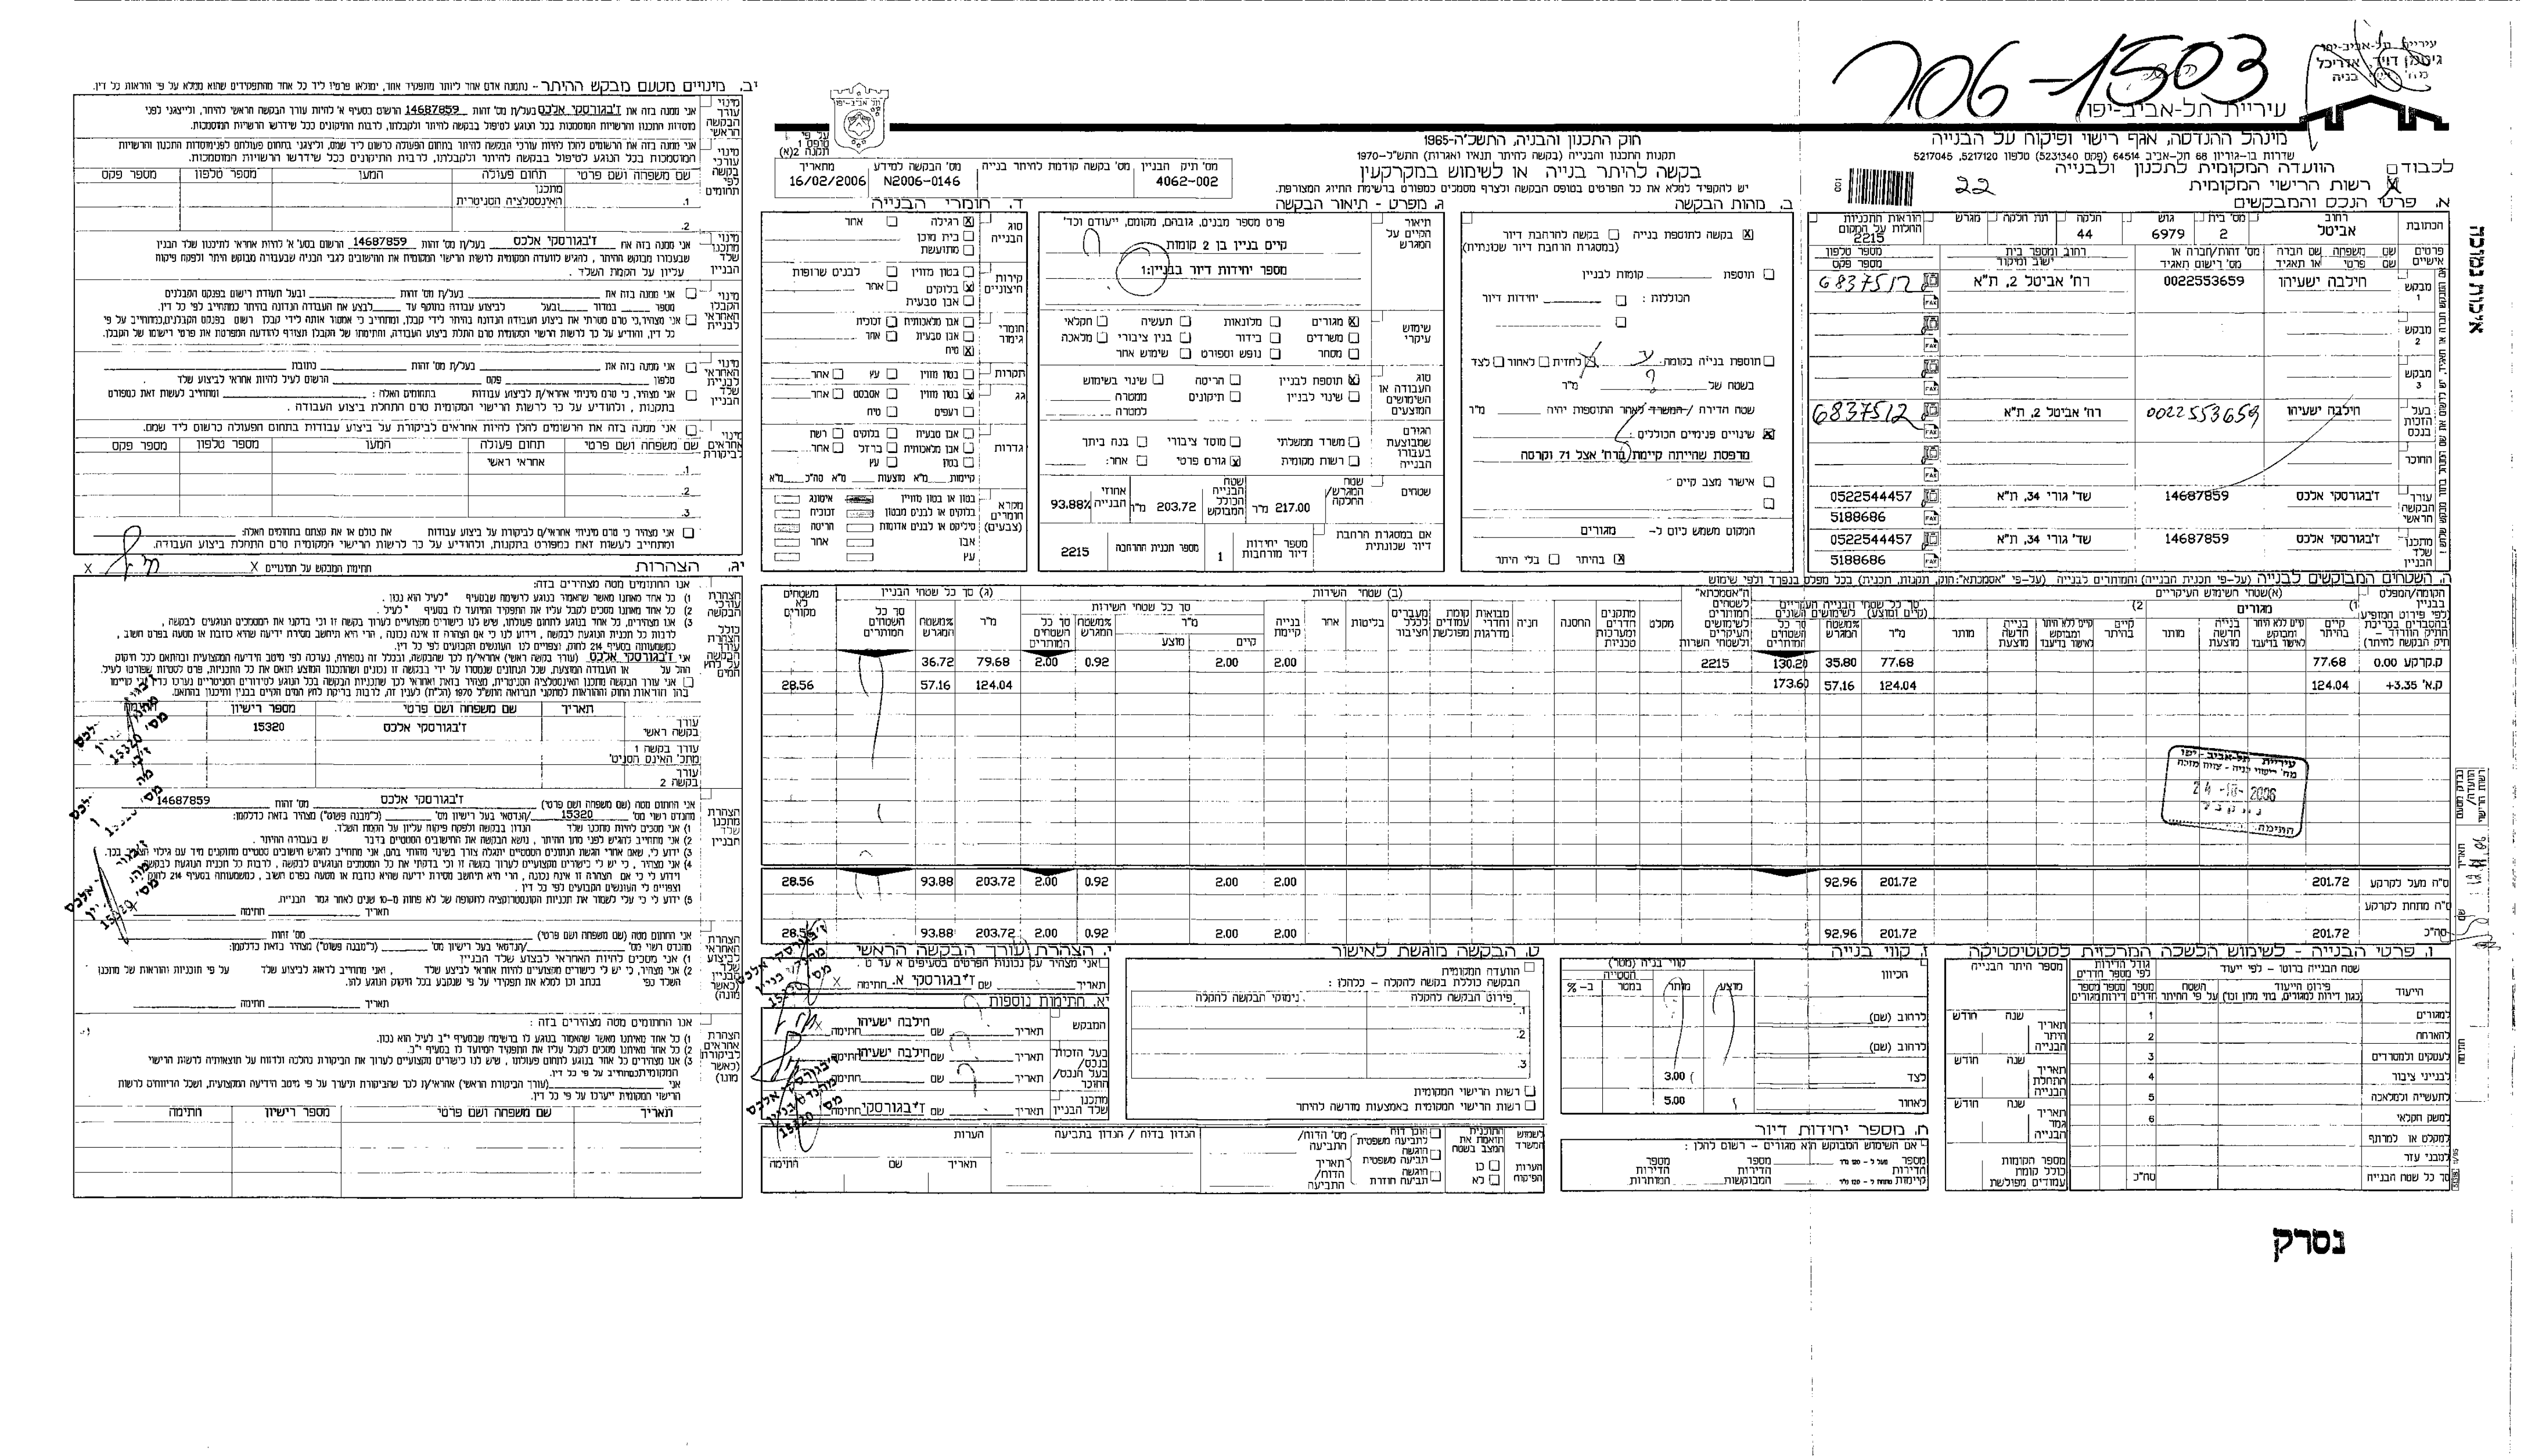

706-1503

עיריית תל-אביב-יפו
מינהל ההנדסה, אגף רישוי ופיקוח על הבנייה
שדרות בן-גוריון 68 תל-אביב 64514 (פקס 5231340) טלפון 5217120, 5217045

לכבוד
☒ הוועדה המקומית לתכנון ולבנייה
☐ רשות הרישוי המקומית

22

חוק התכנון והבניה, התשכ"ה-1965
תקנות התכנון והבנייה (בקשה להיתר תנאיו ואגרות) התש"ל-1970
בקשה להיתר בנייה או לשימוש במקרקעין
יש להקפיד למלא את כל הפרטים בטופס הבקשה ולצרף מסמכים כמפורט ברשימת התיוג המצורפת.

מס' תיק הבניין	מס' בקשה קודמת להיתר בנייה	מס' הבקשה למידע	מתאריך
4062-002		N2006-0146	16/02/2006

א. פרטי הנכס והמבקשים

	רחוב	מס' בית	גוש	חלקה	מגרש	תוכניות החלות על המקום
הכתובת	אביטל	2	6979	44		2215

	שם משפחה ושם פרטי	מס' זהות/חברה	רחוב ומספר בית, ישוב ומיקוד	מספר טלפון
מבקש 1	חילבה ישעיהו	0022553659	רח' אביטל 2, ת"א	6837512
בעל הזכות בנכס	חילבה ישעיהו	0022553659	רח' אביטל 2, ת"א	6837512
עורך הבקשה הראשי	ד'בגורסקי אלכס	14687859	שד' גורי 34, ת"א	0522544457 5188686
מתכנן שלד	ד'בגורסקי אלכס	14687859	שד' גורי 34, ת"א	0522544457 5188686

ב. מהות הבקשה
☒ בקשה לתוספת בנייה
☒ שינויים פנימיים הכוללים
מרפסת שהייתה קיימת (מרח' אצ"ל 71 וקרסה)

ג. מפרט - תיאור הבקשה
קיים בניין בן 2 קומות
מספר יחידות דיור בבניין: 1

שטח המגרש	217.00	שטח הבנייה הכולל המבוקש	203.72
אחוזי הבנייה	93.88%	מספר תכנית החרחבה	2215

ד. חומרי הבנייה

28.56	93.88	203.72	92.96	201.72

טבלת שטחים: קומת קרקע 0.00 — 77.68; קומה א' +3.35 — 124.04

נסרק