

מפה טופוגרפית

ק.מ. 1:250

26



הל-אביב-יפו שכונת התקווה

גוש 135
חלקה 44 (חלק)
רח' אביטל מס 7

לפי החלטה הועדה המקומית מיום 16.6.66
(פר' 38 ב', החלטה 22 77) - אין להחזיר
בניה בשכ' החקוה אלא חוספת בניה רק
בבנינים הקיימים ובקומות הקרקע בלבד
במקרים מיוחדים וקשים של צפיפות בדיור
עקב גידול משמחה.


הוכן בשביל חב' עזרא ובצרון בע"מ

שטח: 0.448 דונם מטר

חלוצי-יפו
יור השילוט והמסחר
אשר רחוב

רח' אביטל מס 7, 5, 15, 17


תחילת הסביבה ק.מ. 1:250

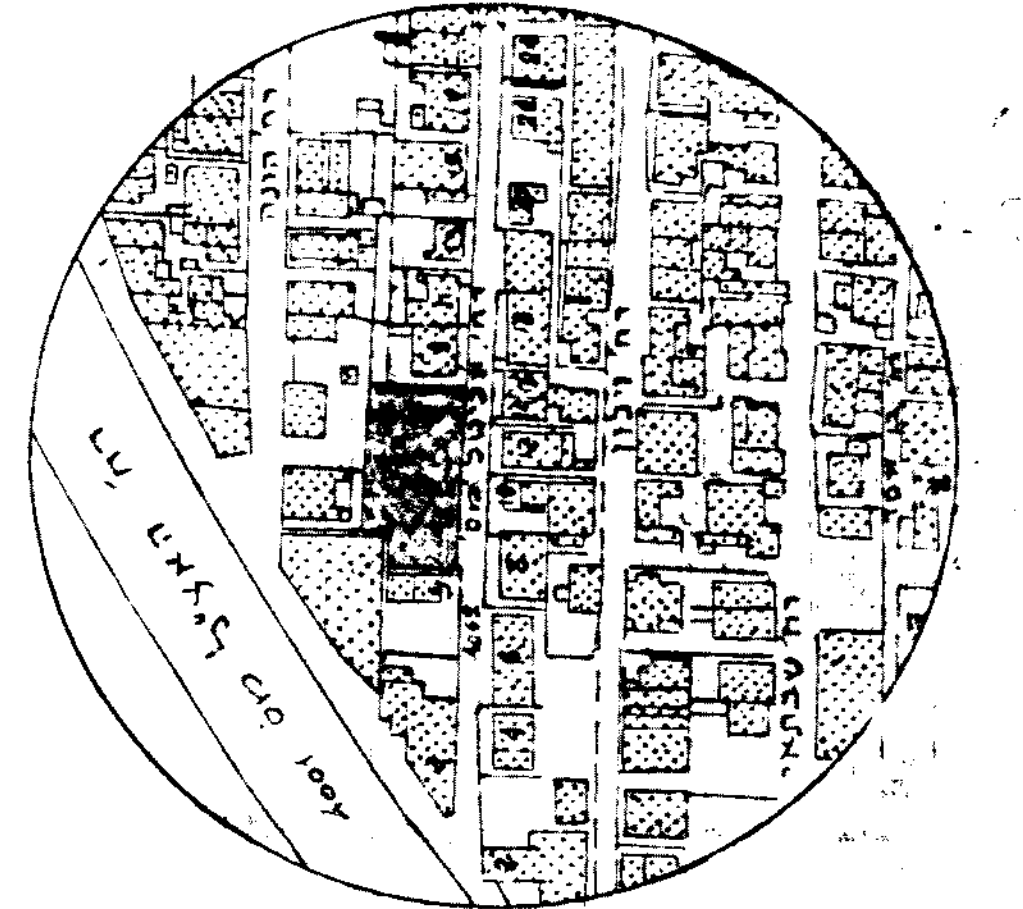

נסרק

הערות:

1. הגבהים קשורים לרשת עיזנית בנקודה 480 שגובהה 17.930.
2. המספרים בשוגרים מופיעים גבהים קיימים.
3. שטח החלקה חושב לאחר מדידת החלקה ולפי המצב הקיים.

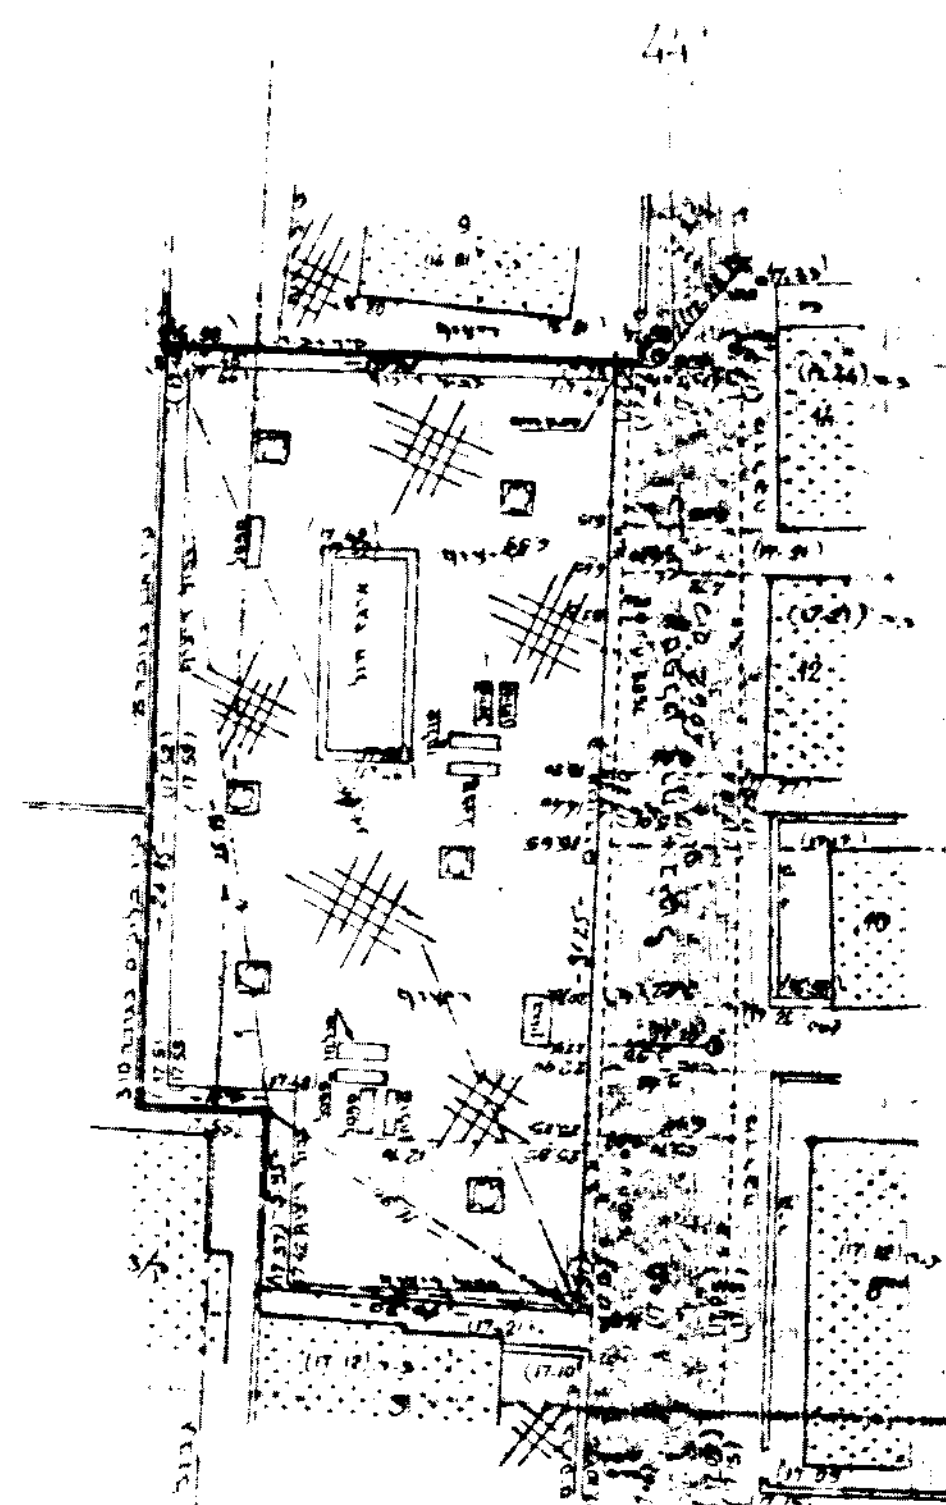

עיריית תל אביב
מנהל - מחלקת מדידות
מפה טופוגרפית
מס' 183-8
רח' אביטל מס 7, 5, 15, 17

לשכת שטח