אינסטלציה סניטרית

23

007

חוק התכנון והבניה, תשכ"ה—1965

תקנות התכנון והבניה (בקשה להיתר, תנאיו ואגרות), תש"ל—1970

טופס 2 (תקנה 2(א))

הוועדה המקומית לתכנון ולבניה: תל-אביב

מ י פ ר ט

תיק מס' 25247

א. תיאור הבנין

1. המקום: תל אביב שכונת התקווה | הרחוב: אבטל | מס' 13 | גוש 6135 | חלקה 44
2. המבקש: [illegible] יוסף | אבטל 13 ת"א
4. עורך הבקשה: [illegible] ליאון | יהלל 3 ת"א | 239968
5. המהנדס האחראי לביצוע השלד: אפרים כהן | [illegible] 11 ת"א | 452801
6. אופי הבניה: ☒ מגורים ☐ מסחר ☐ תעשיה ☐ בנין ציבורי ☐ חקלאי ☐
7. שטח המגרש/החלקה: 136.0 ... אחוז הבנים המותר: 140 %
8. מטרת הבנין: ☒ מגורים ☐ הארחה ☐ עסקים ☐ תעשיה ☐ חקלאי ☐ ציבורי ☐
9. מהות הבנין המבוקש: תוספת קומה לבנין קיים
10. תיאור העבודה המוצעת: ☐ בנין חדש ☒ תוספת לבנין קיים ☐ הריסה ☐ מקלטים ☐ שינוי בבנין ☐
11. האם הבנין הוא בגדר: ☐ מבנה ממשלתי ☐ תחנות המקורות ☐ הרשות המוסמכות

ב. היקף הבנוי

קומה	קיים	מוצע	סך הכל	אחוז הבניה
1	2	3	4	5
הבניה הקיימת	5019		5019	
א'		3869	3869	
סך הכל	5019	3869	8888	65%

ג. תשומות בבנין

הקבלן אחראי
לביצוע מערכת מי-הגשמים
בהתאם למפרט
במידע שנוהל לבקשת חיבור מים
של אגף מפעל המים - עירית תל-אביב-יפו

עירית תל-אביב-יפו
אגף מפעל המים
אישור לאספקת מים
בתוקף מיום
עד יום
חתימה

נסרק

---

2. הבניה הקיימת המוצעת לתעשיה ולמלאכה

3. הבניה המוצעת למטרות אחרות (הארחה, עסקים ומשרדים, בנייני ציבור, בנייני משק חקלאי, מטרות שונות)

4. חלקי בנין אחרים — הבניה המוצעת, שטח במ"ר

ד. חומר הבניה

ה. גדרות

ו. מקרא

הצהרות:

הנני מאשר כי הנתונים הנ"ל נכונים

התאריך 1.7.82 חתימת המבקש

התימת עורך הבקשה

התימת המהנדס האחראי לביצוע השלד

אפרים כהן מהנדס בנין

452801

[illegible] ליאון
אדריכל ובונה ערים
רח' יהלל 3 תל-אביב

אישורים של רשויות חוץ:

התימת הוועדה המקומית

עירית תל-אביב-יפו / מנהל הנדסה / אגף הרישוי

אשור מס' 200/82

נתן אשור לכלי אשפה בסוג ובמבנה שצויינו בתכניה בתנאי:

1) שיוצב 1 כלי אשפה פלסטיים 76 ליטר עם מכסה צמוד מדגם מאושר ע"י אגף התברואה, על גבי תושבות ברזל 30 ס"מ מהרצפה ו-20 ס"מ מכל קיר.

2) ברז מים ובריכה ייקבעו ע"י המתקן בעל כלי אשפה ויחוברו להספקת המים הכללית ולרשת הביוב של הבית.

3) ______

בכל מקרה של שינויים בתכנית הבניה יש לקבל אשור מחדש מאגף הרישוי על סוג, מיקום צורת ומספר כלי אשפה.

תאריך ______ חתימה ______

15 יולי 1982

לאחר גמר בניית הבנין, נא להתקשר עם מדור תכנון מתקנים במנהל ההנדסה/אגף הרישוי לשם בדיקת התנאים הנ"ל. רק לאחר ביצוע התנאים - נוכל לשחרר את הפקדון.

אין להשתמש בבטונדה לפחי אשפה

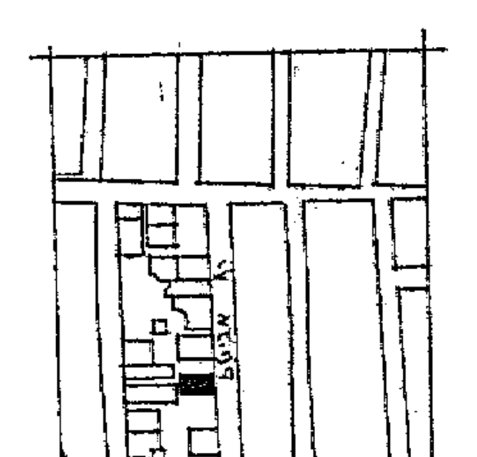

1 : 2500 תרשים סביבה

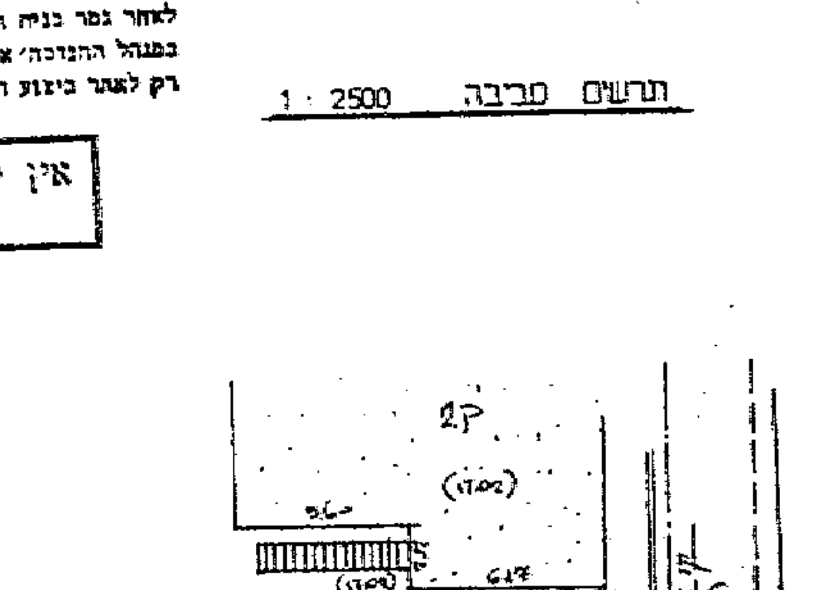

1 : 250 תרשים מגרש

עירית תל-אביב-יפו
16-08-1982

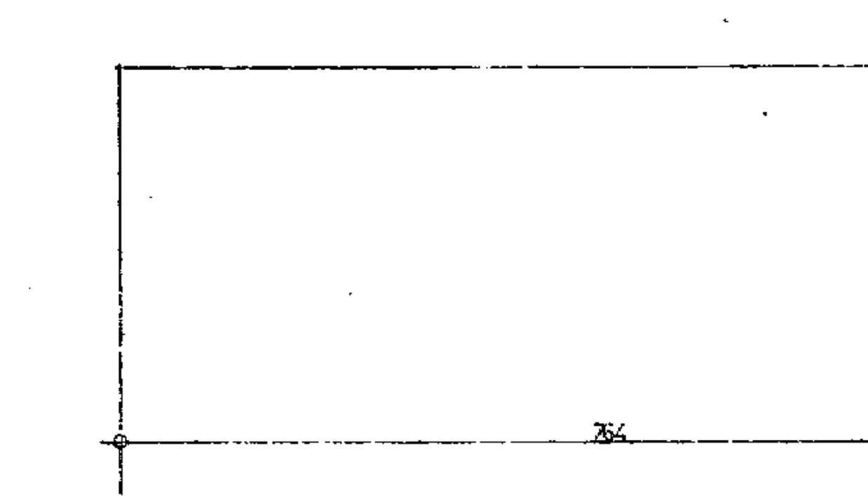

חישוב קומת קרקע - קיימת

שטח דירה קיימת
764 · 657 — 5019 נטו

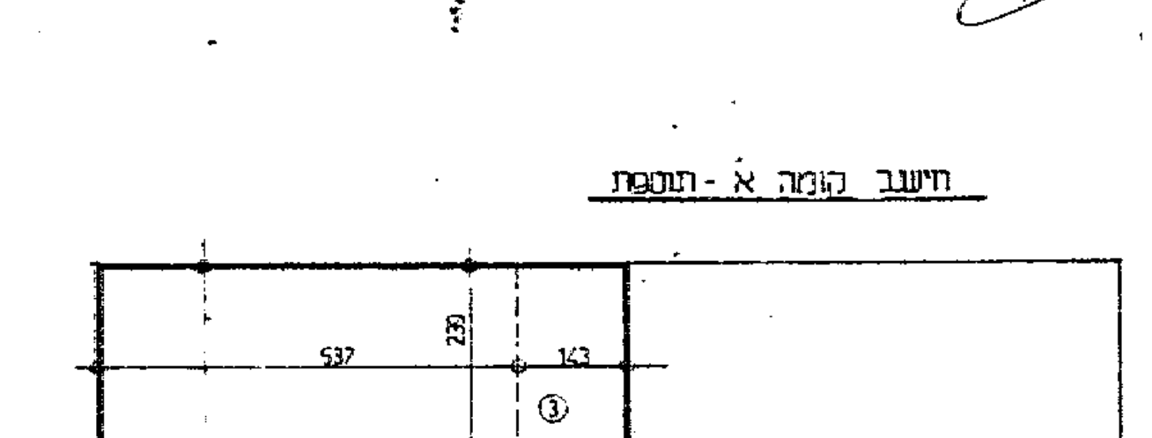

חישוב קומה א' - תוספת

שטח תוספת
① 657 · 537 — 3528
③ 239 · 143 — 341
3869 נטו

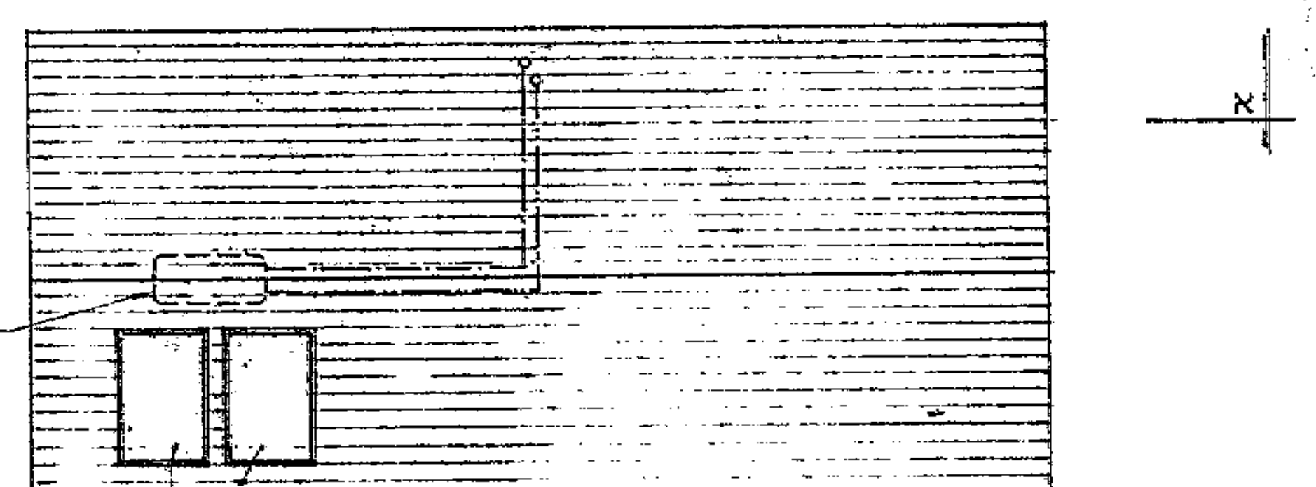

תכנית גג 1:100

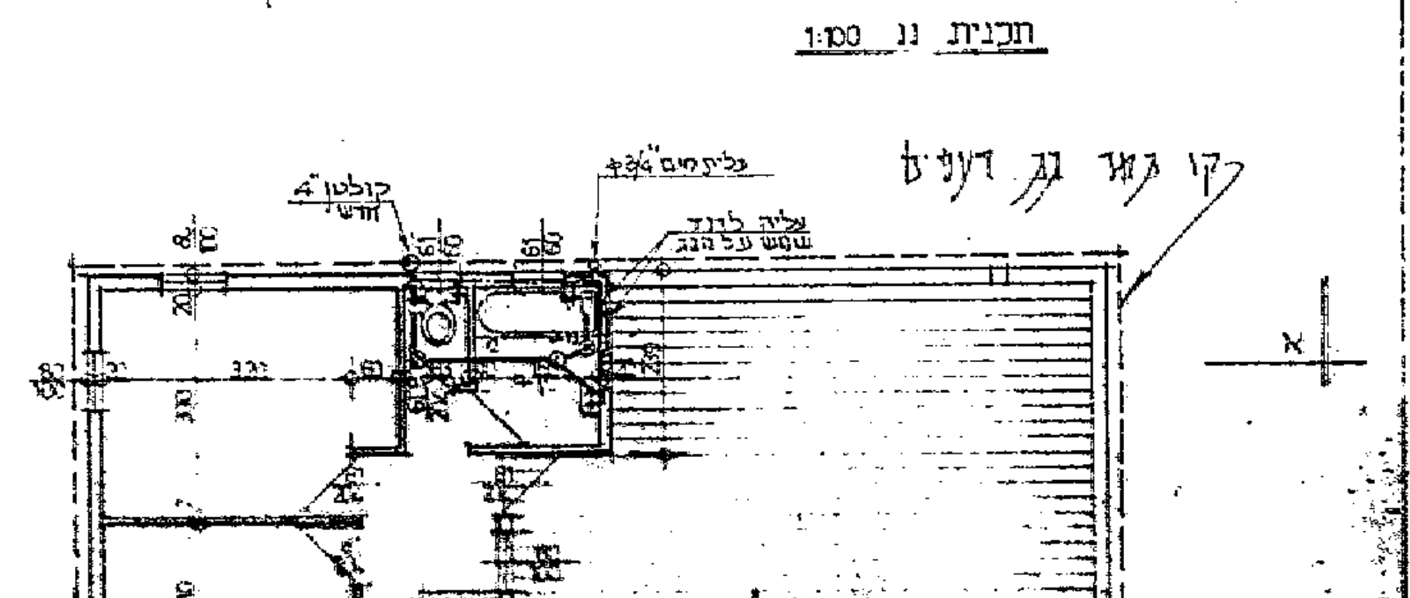

תכנית קומה א' 1:100 (מוצע)

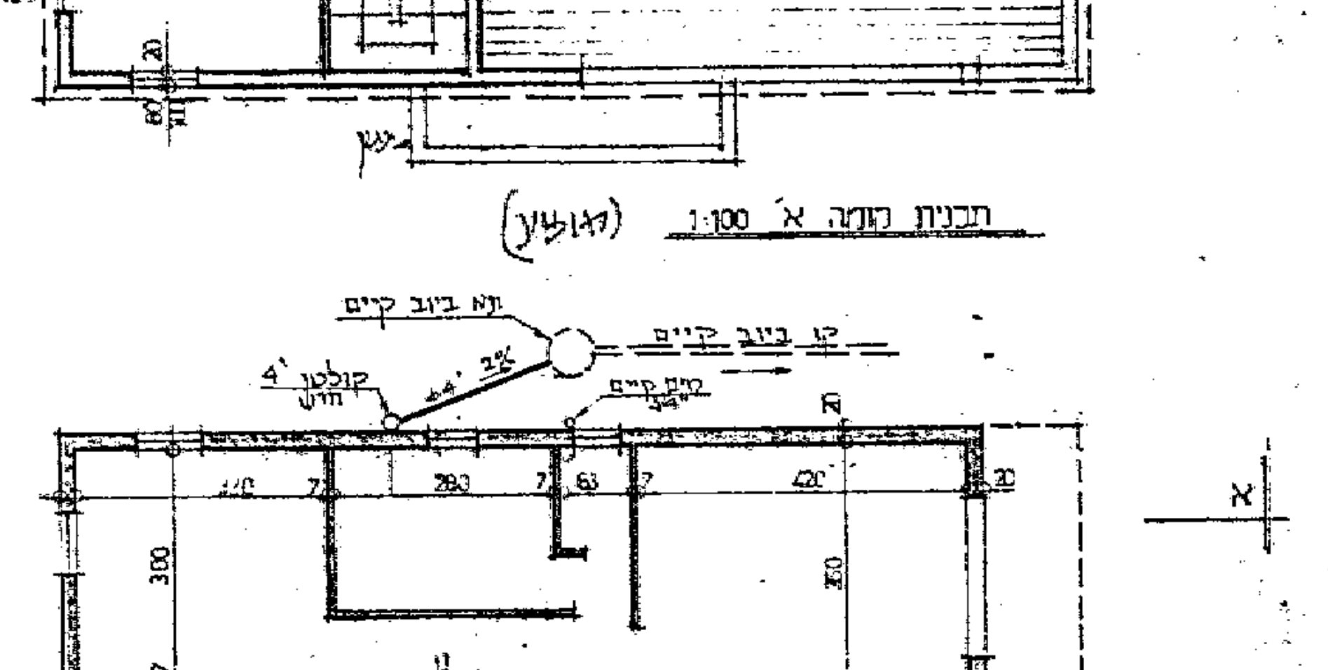

תכנית קומת קרקע 1:100 (קיים)

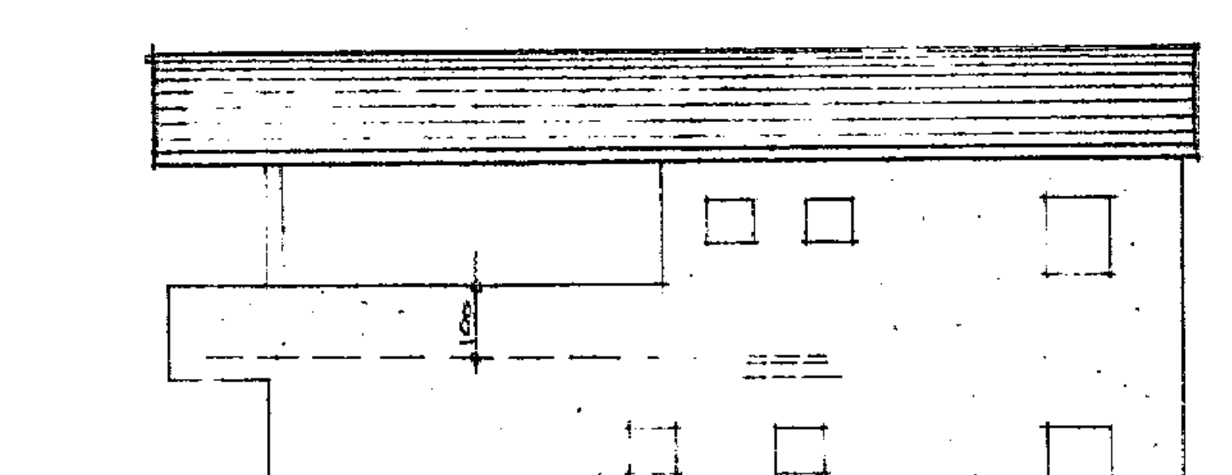

חזית אחורית 1:100

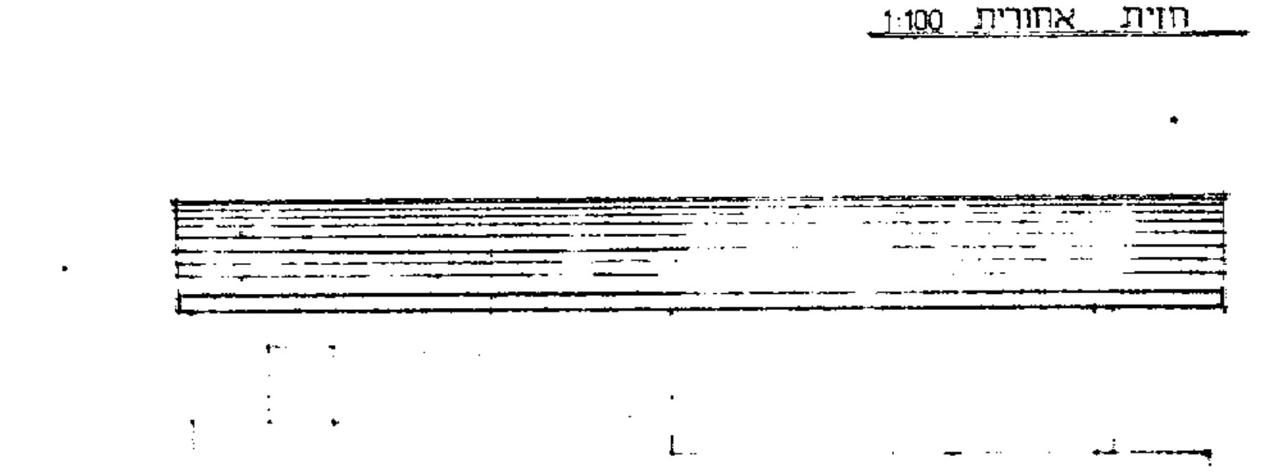

חזית כניסה 1:100

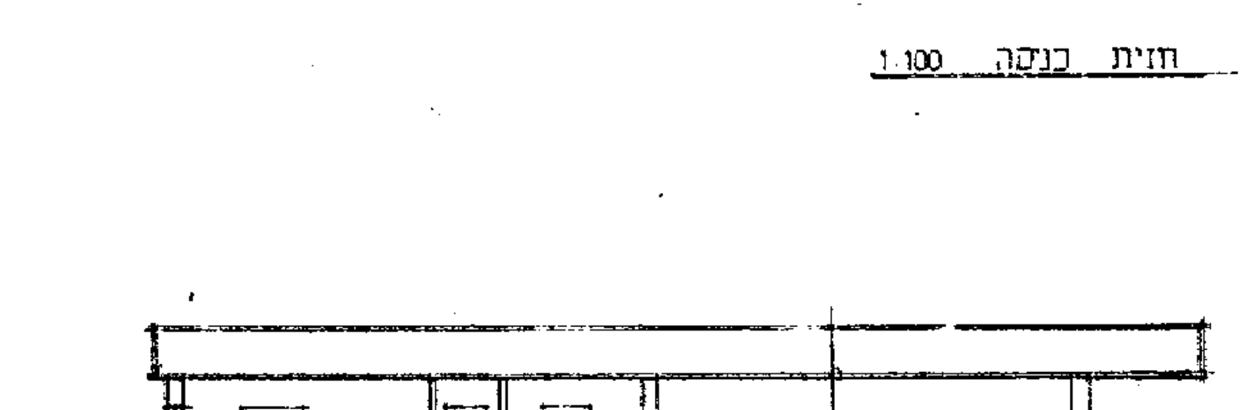

חתך א'-א' 1:100

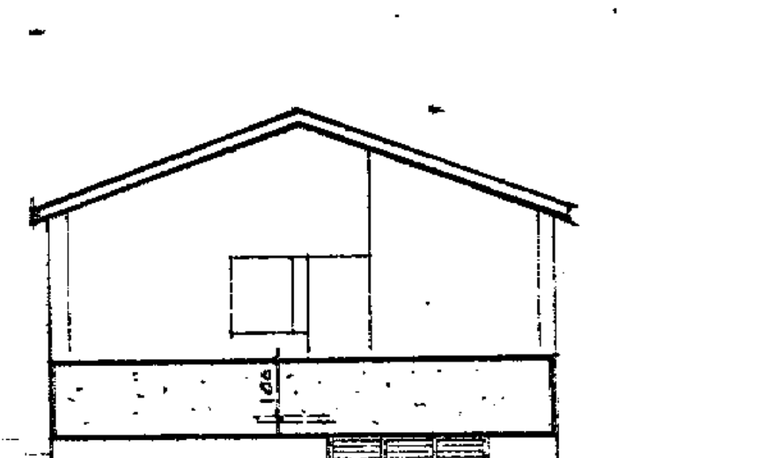

חזית צדדית - מזרחית 1:100

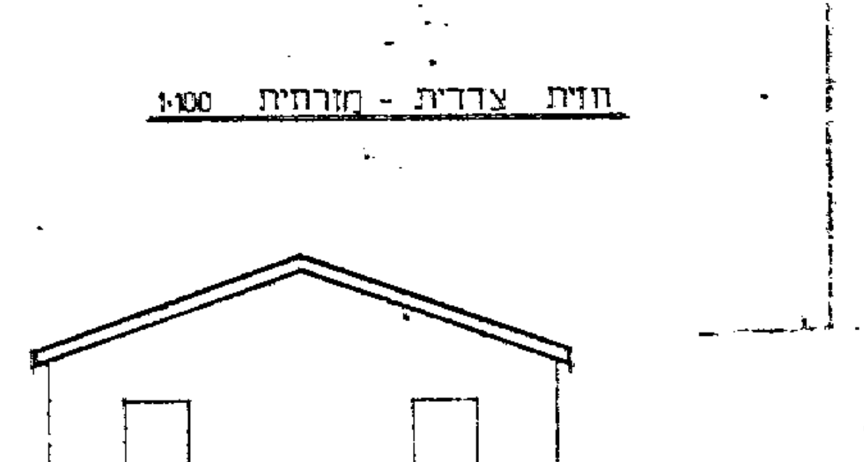

חזית צדדית - מערבית 1:100

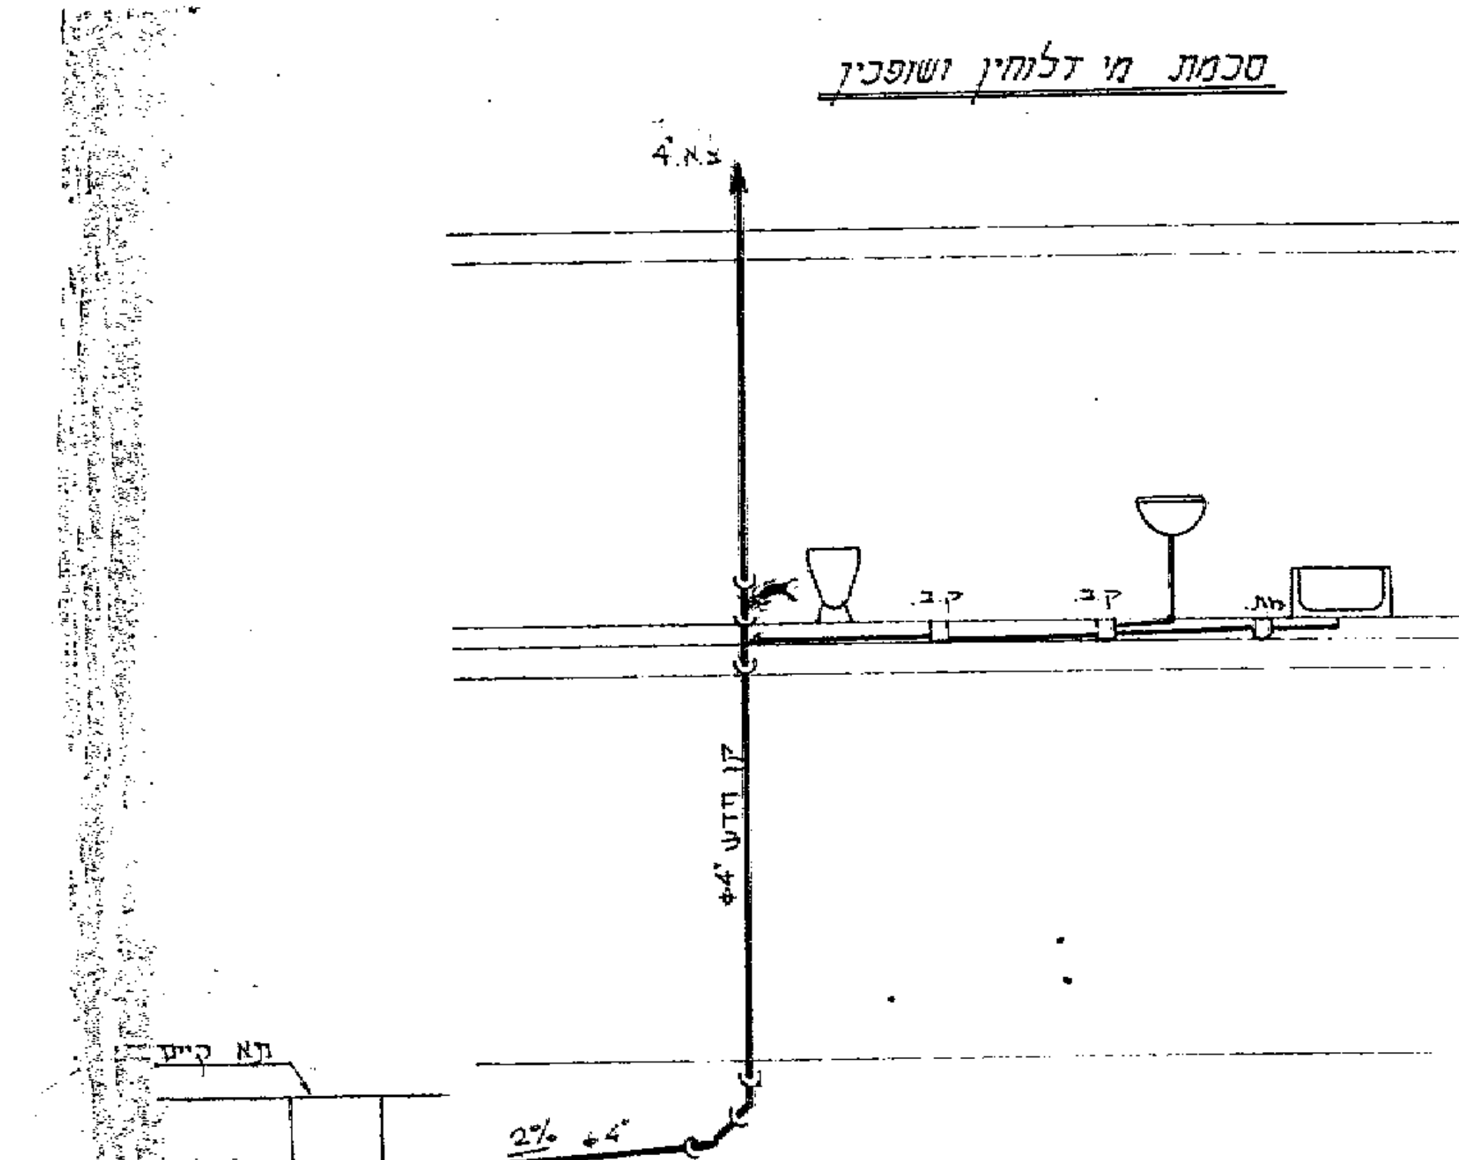

סכמת מי דלוחין ושופכין

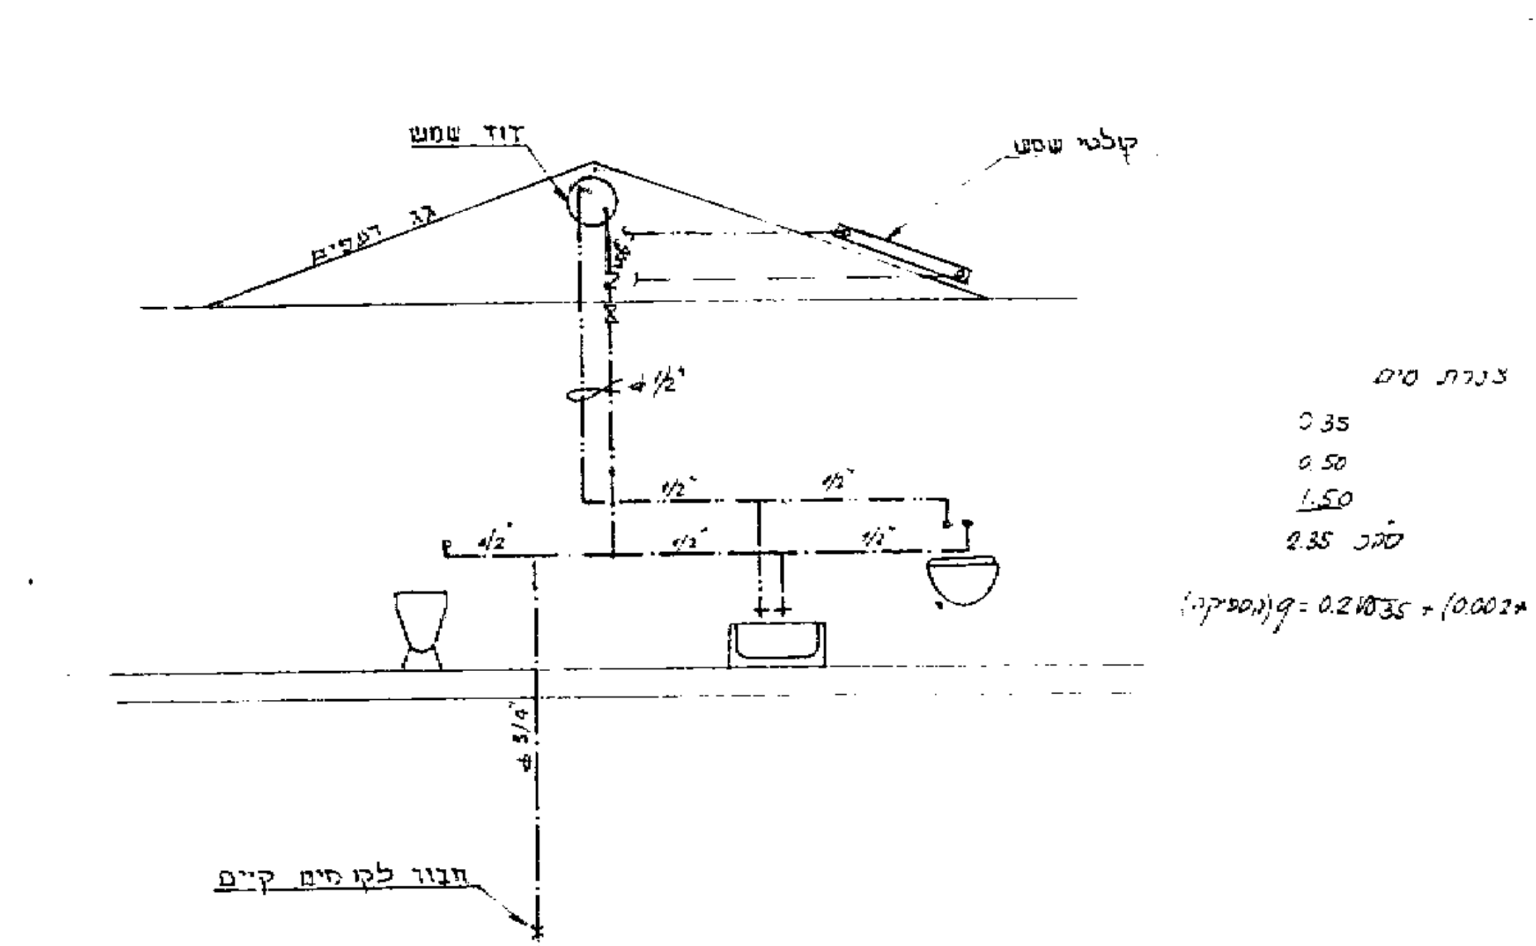

חשוב צנרת מים
1 קערה 0.35
1 כ"ר 0.50
1 אמבטיה 1.50
סה"כ 2.35
q (הספקה) = 0.2√2.35 + (0.002 × 2.35) = 0.3113 ℓ/sec

סכמת מים קרים וחמים

עירית תל-אביב-יפו
15 -07- 1982

עירית תל-אביב-יפו
21 -07- 1982

סוף מסמך