





מחוז תל-אביב
נפה תל-אביב יפו
מקום תל-אביב
גוש 6435 חלקה 44 מגרש 1
כתובת רח' אביטל 13
הוכן בשביל עובדיה יוסף
שטח החלקה כולה במ"ר : 11476
בעלות בחלקים: 125/11476
בעלות במ"ר: 125
שטח מדוד במ"ר 125
שטח מגרש משנה במ"ר 125
שטח לגריעה במ"ר
שטח מגרש שיוקצה במ"ר 125
מסרת המדידה הגדרת מגרש משני


תרשים סביבה קנ"מ 1:2500

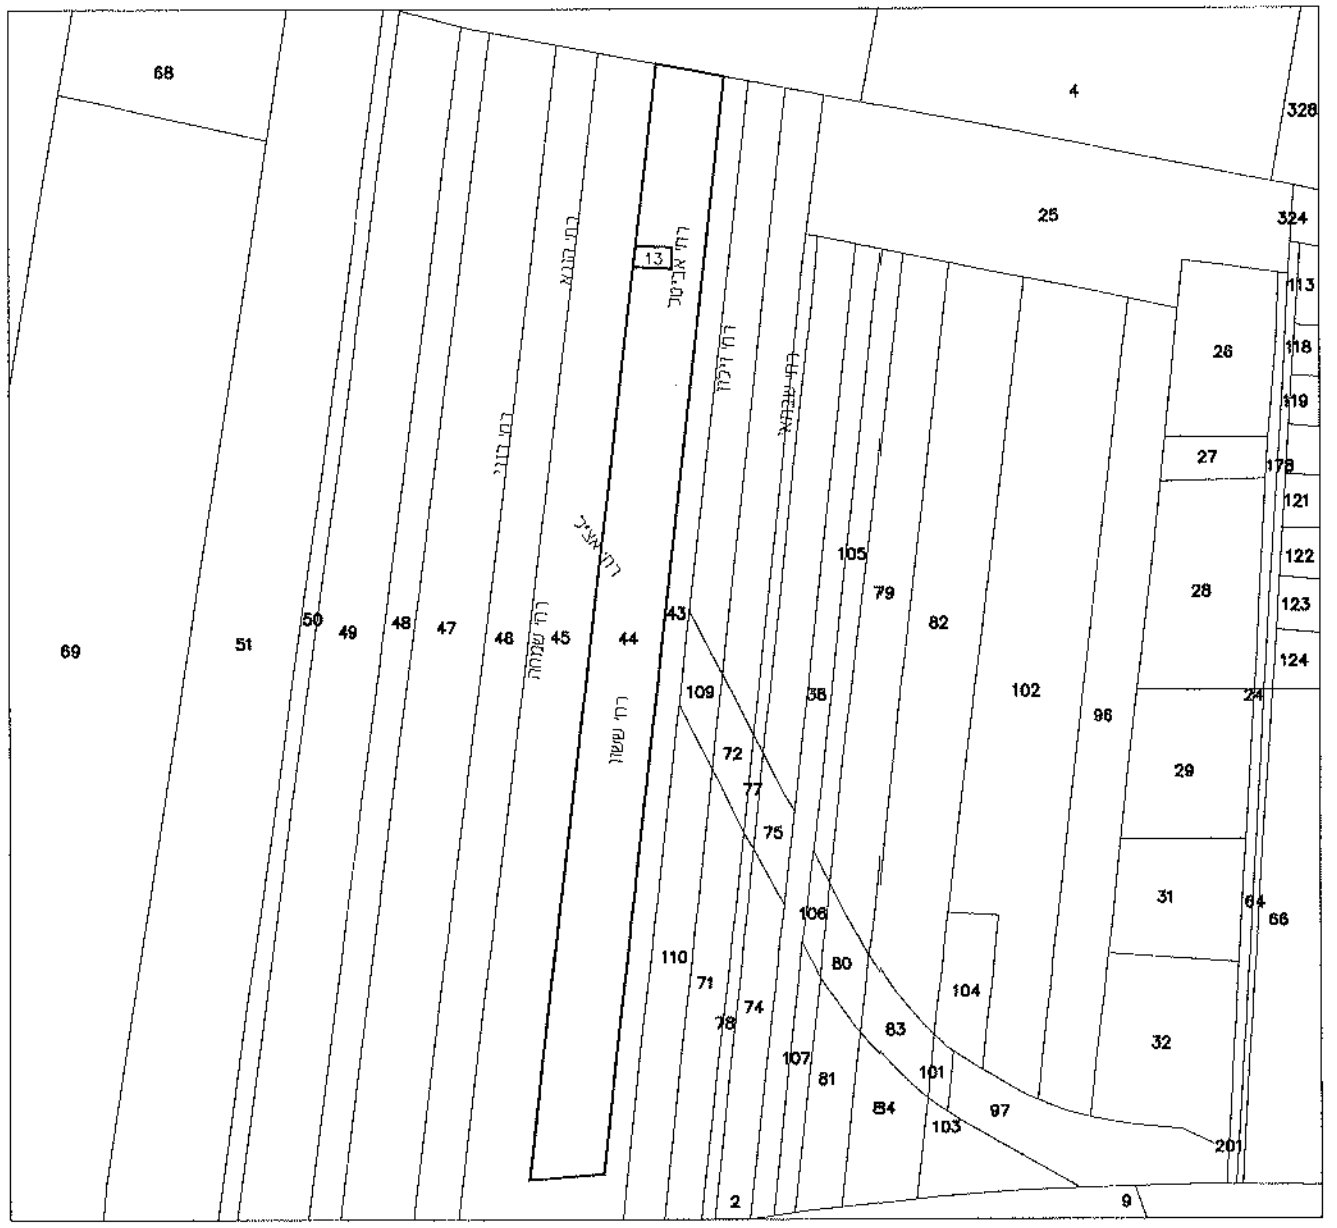

קנה מידה 1 : 250

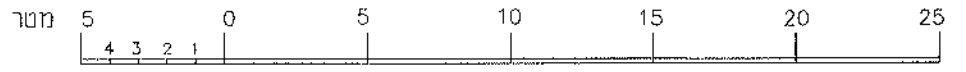

למעט טאם

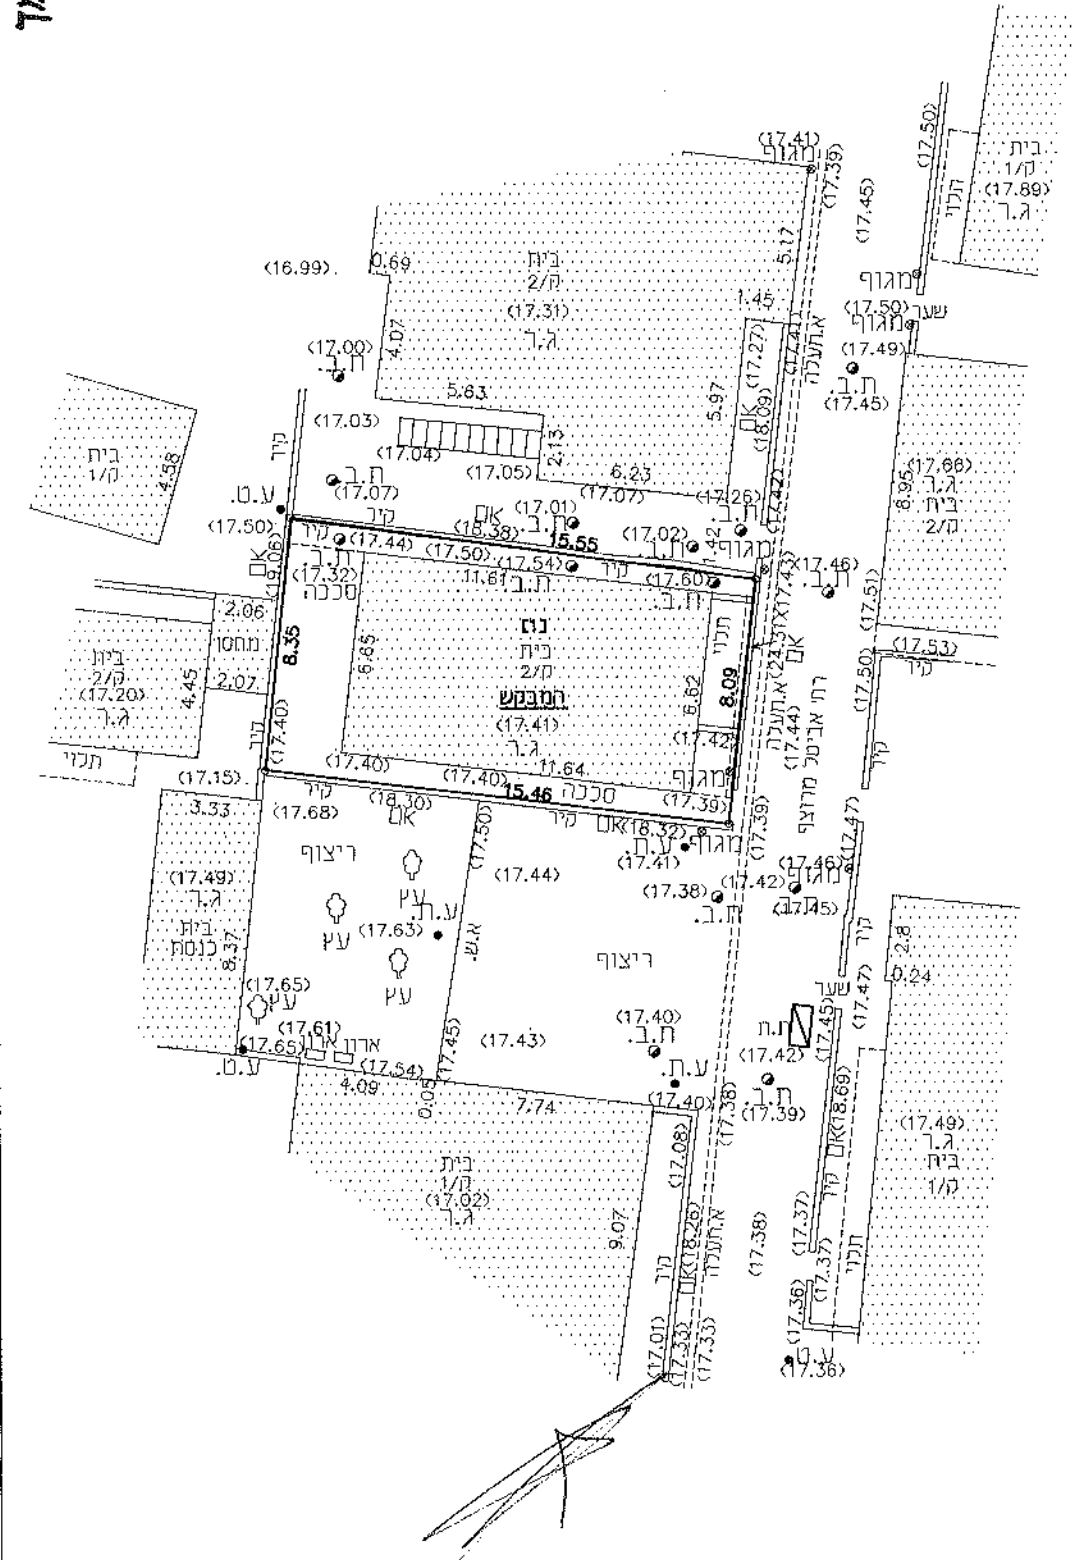

לא לצרכי רישום

אני מאשר בזה כי מפה זו היא העתק נכון של המפה הטופוגרפית שהכנתי על סמך מדידה שהסתיימה ביום 14.06 שנת 2011 וכל הפרטים שצוינו במפה הם מדויקים ודרגתה היא א', המפה בוצעה בהתאם לתקנות המודדים (מדידה ומיפוי) התשנ"ח-1998.

מסארוה חוסאם - מודד מוסמך מ.ר. 894
מייבנה משולש 40400 טל. 0522-650723
09-7990140 טלפ. 09-7996748
הנדסת מדידות
EMAIL-MHME.D@BEZEQINT.net

הערות
המפה מבוססת על מפת גוש רישום 6034
הגברים קשורים לנקודה עירונית 188 שגובהה 17.530

שטח	מחוז	מחוז	מחוז
0/00	תל-אביב	תל-אביב	תל-אביב
016648	28/10/1980	מכר לפי צו	מכר לפי צו
017144	04/11/1980	מכר	מכר
016501	29/10/1981	מכר ללא תחורה	מכר ללא תחורה
005296	12/03/1982	ירושלם	ירושלם
008933	26/05/1982	מכר לפי צו	מכר לפי צו
003609	24/02/1983	מכר	מכר
013579	03/08/1983	מכר	מכר

4061
37.41

איגוד הנדסאים