הועדה המקומית לתכנון ובניה
למרחב תכנון תל-אביב - יפו
בהתאם לסעיף 14/ב לתקנות התכנון והבניה
(בקשה להיתר, תנאיו ואגרות) תש"ל-1970,
הריני לאשר כי לספח זה צורף היתר בניה/שימוש
מס' 20-0621
מיום .... ומהווה חלק בלתי נפרד ממנו
.... מהנדס העיר
.... תאריך 28.07.2020

19-0024

סוף המסמך

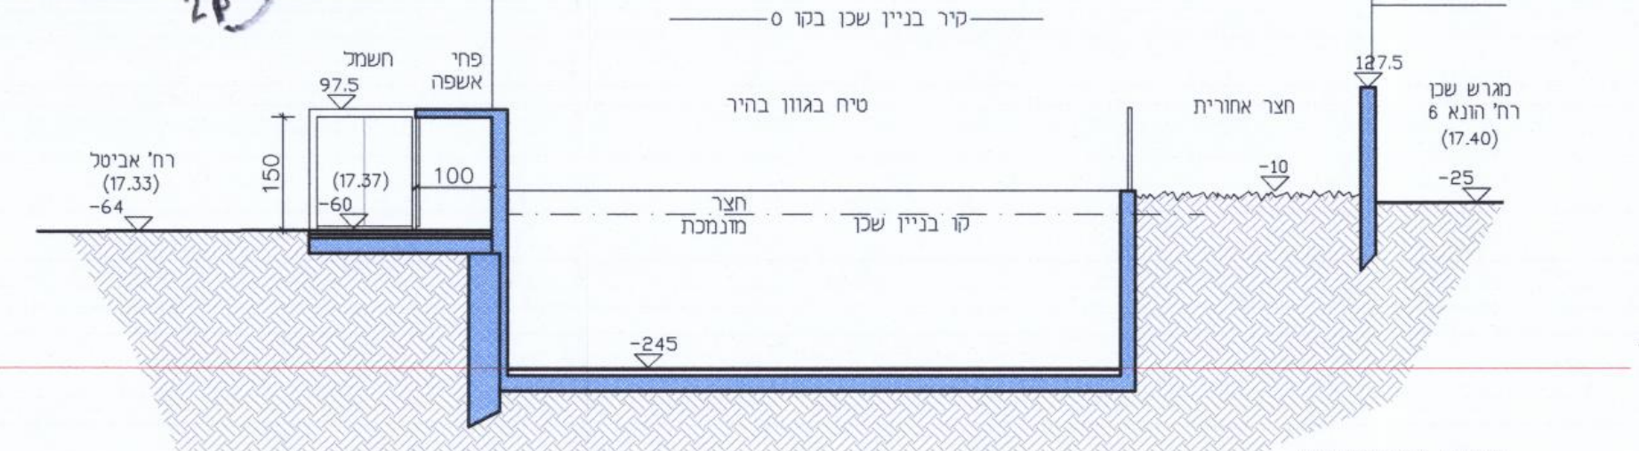

גדר דרומית

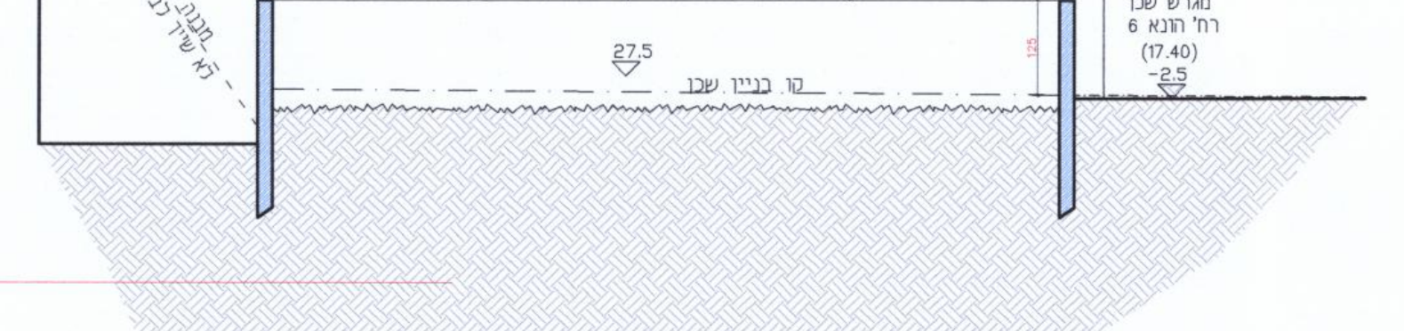

גדר מערבית

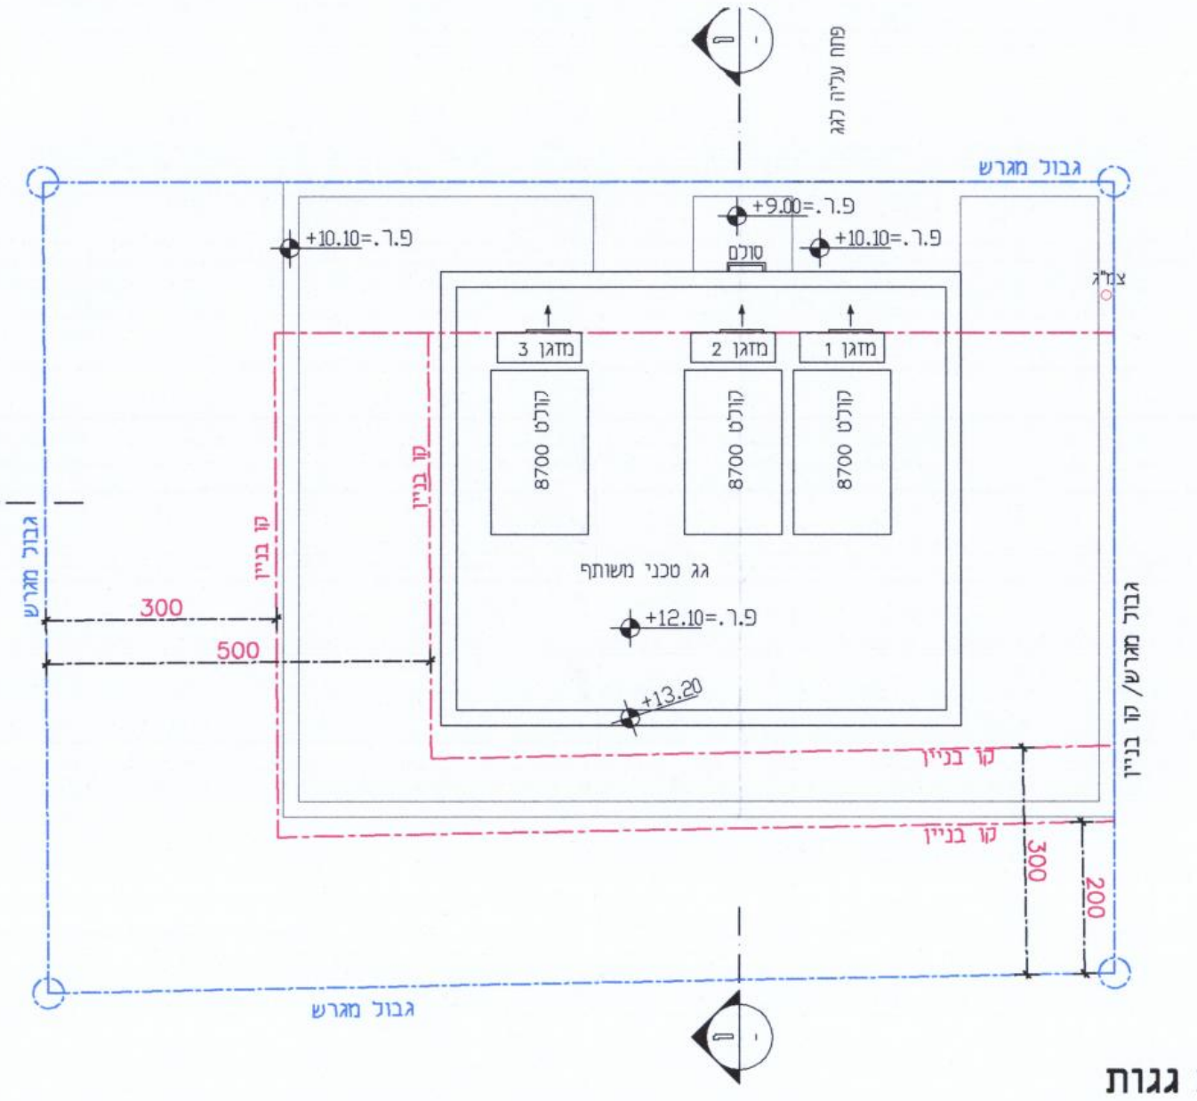
תכנית גגות

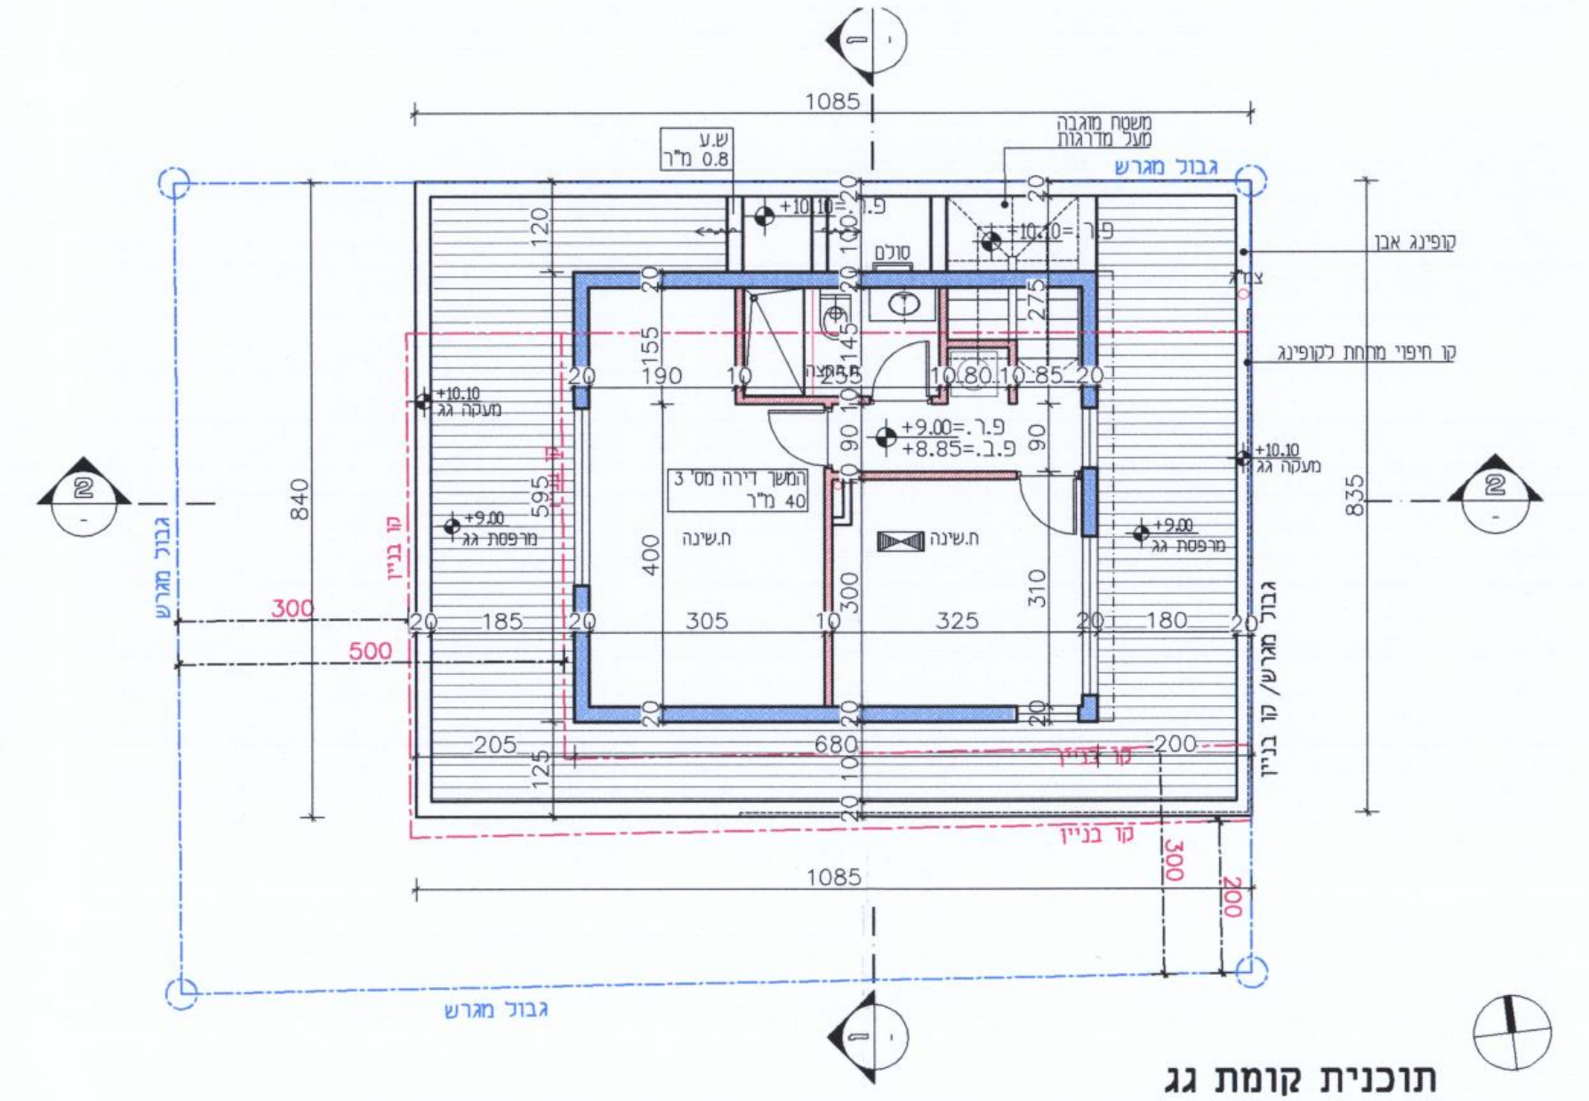
תוכנית קומת גג

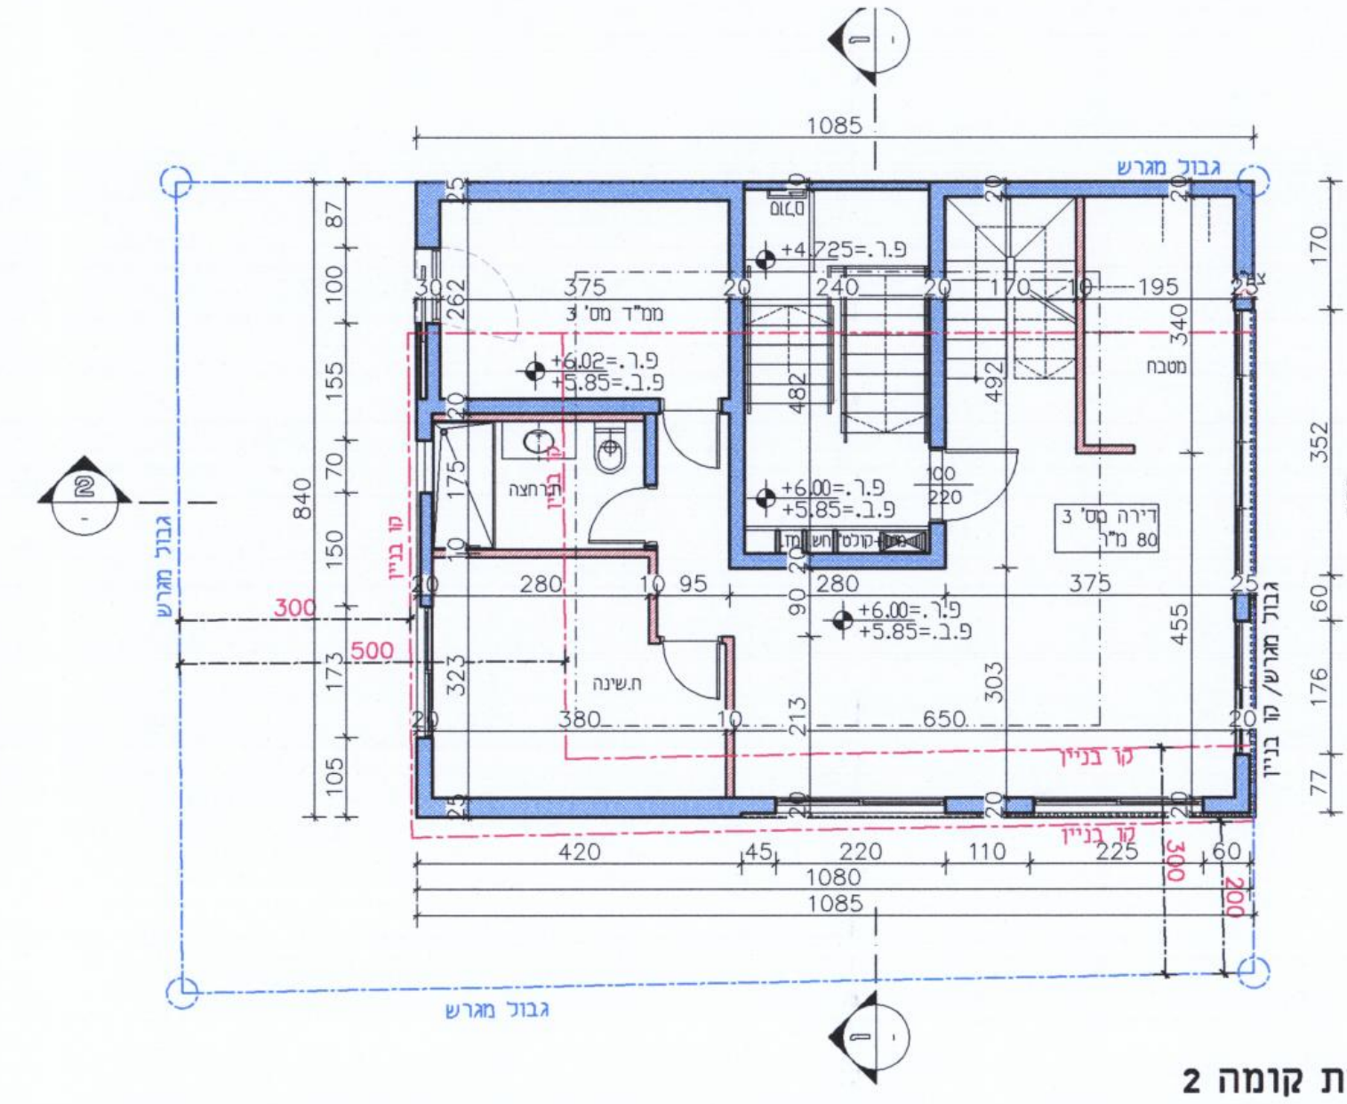
תכנית קומה 2

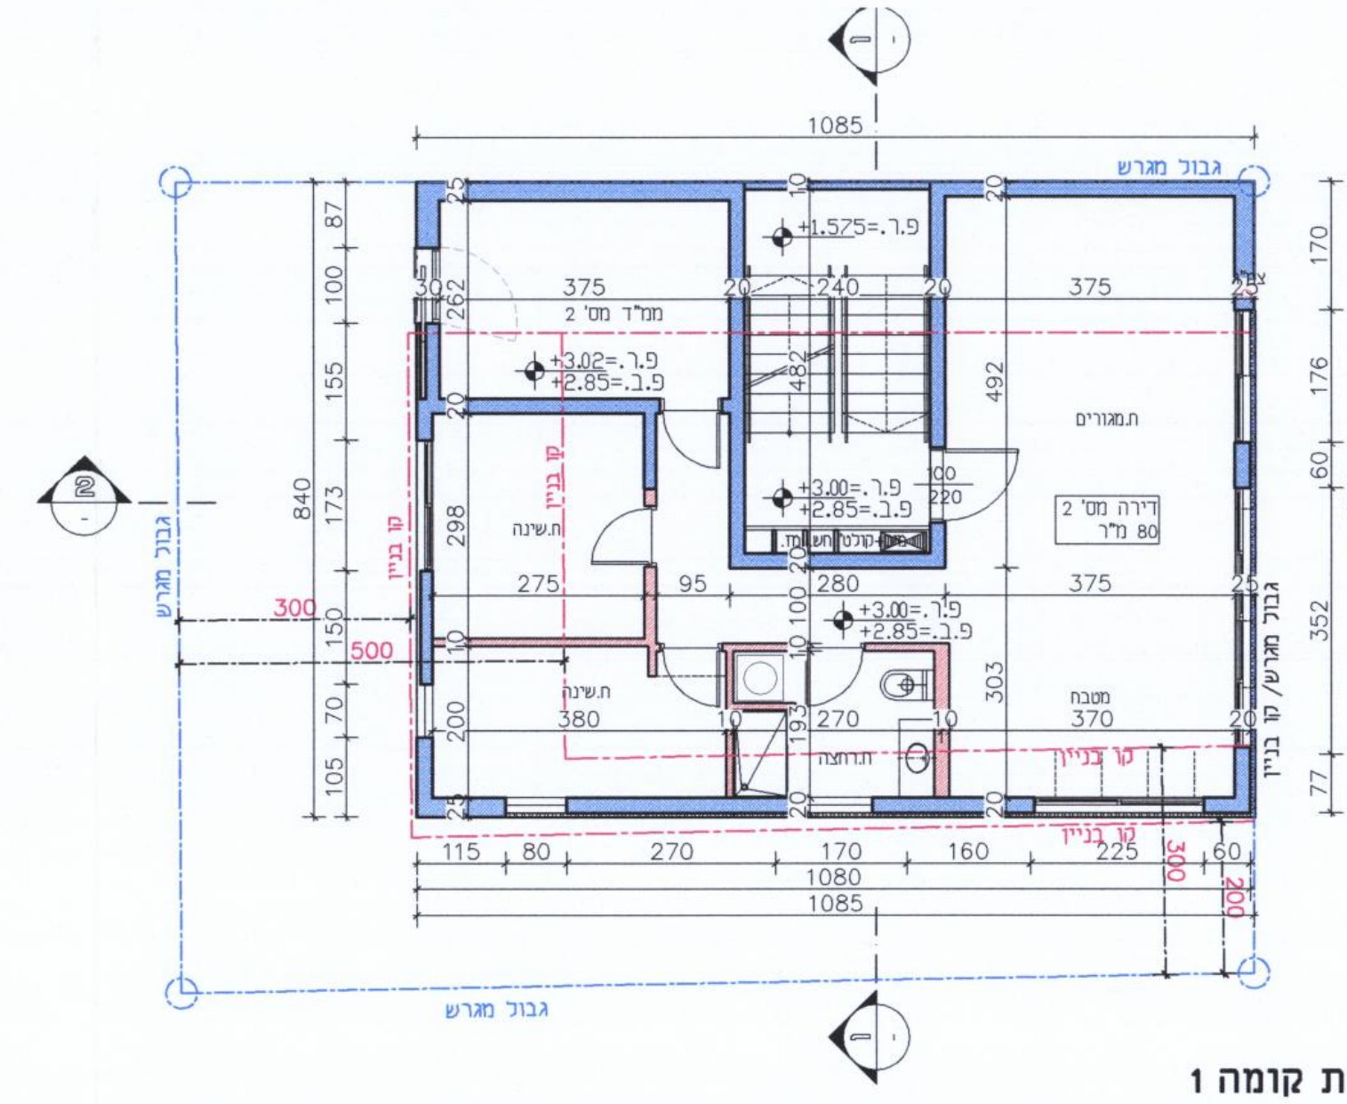
תוכנית קומה 1

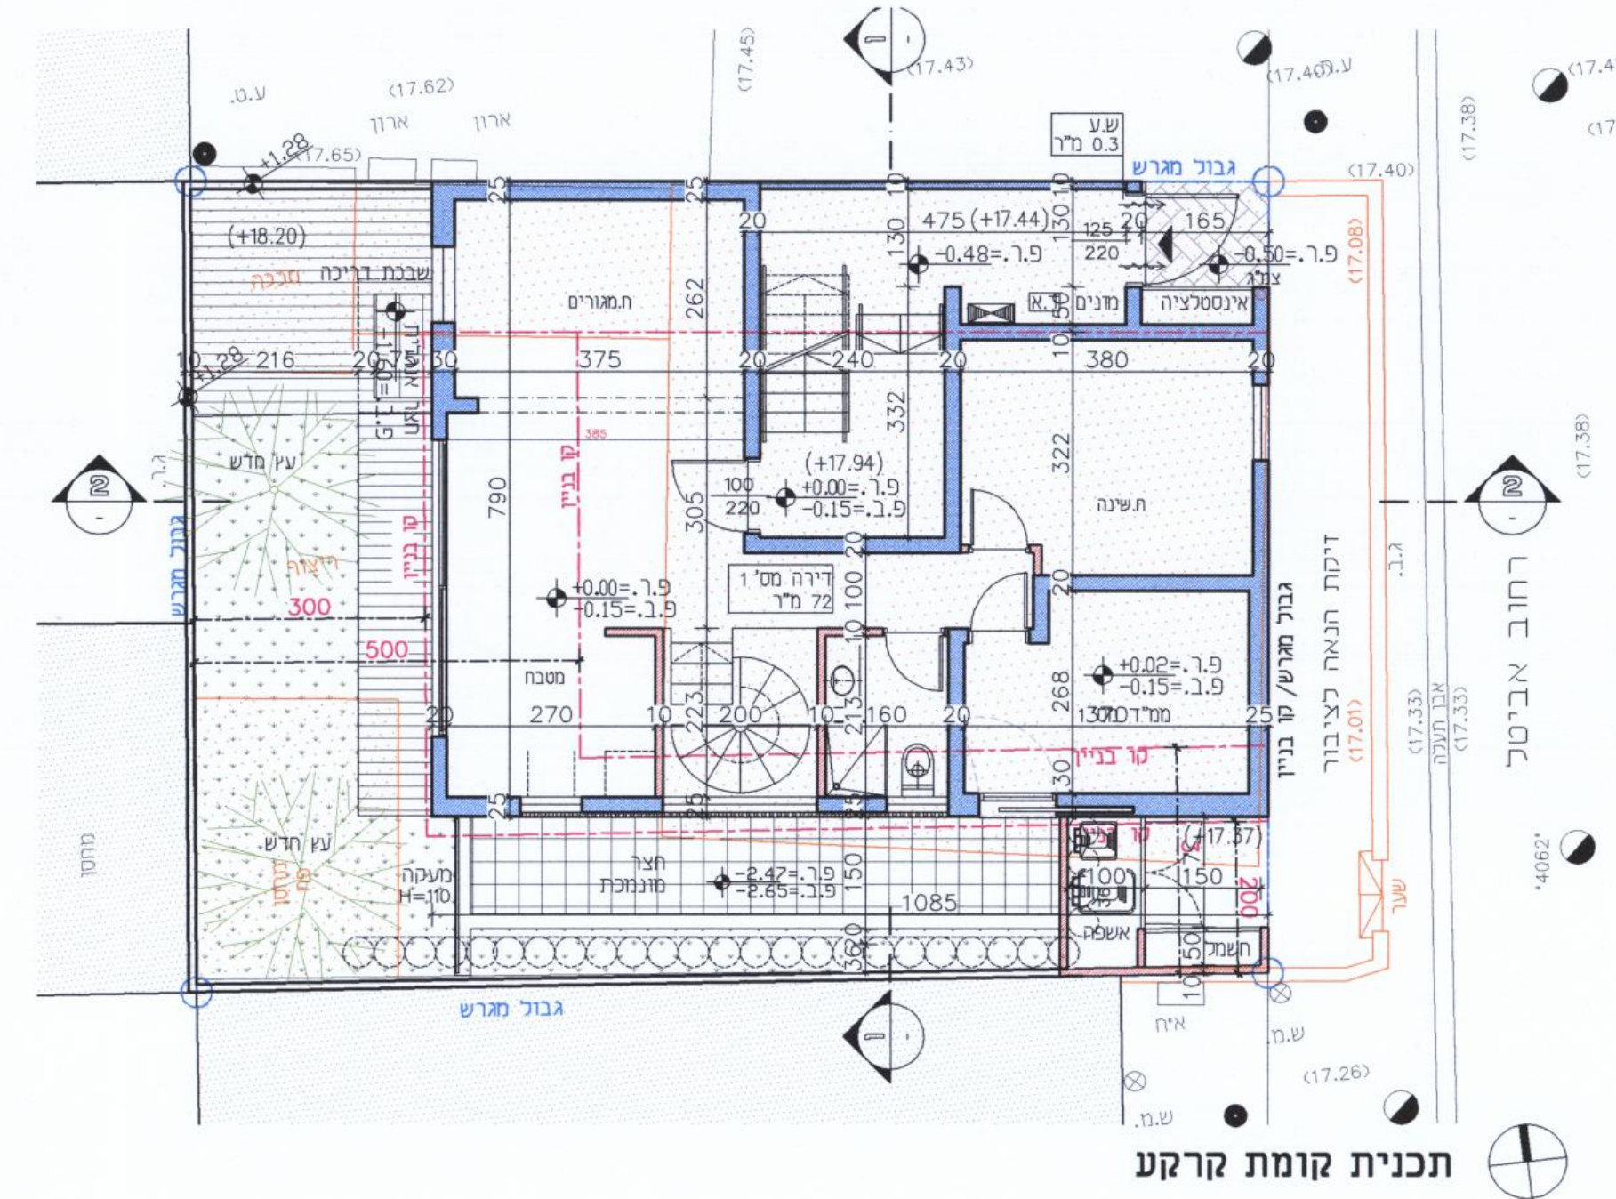
תכנית קומת קרקע

חישוב מספר עצים לנטיעה

תכסית בניין =	83
שטח המגרש = (ראה חישובי שטחים)	120
מפתח 1 עץ לכל 50 מ"ר	(120-83)/50=0.74
סה"כ מספר עצים בוגרים לנטיעה =	1

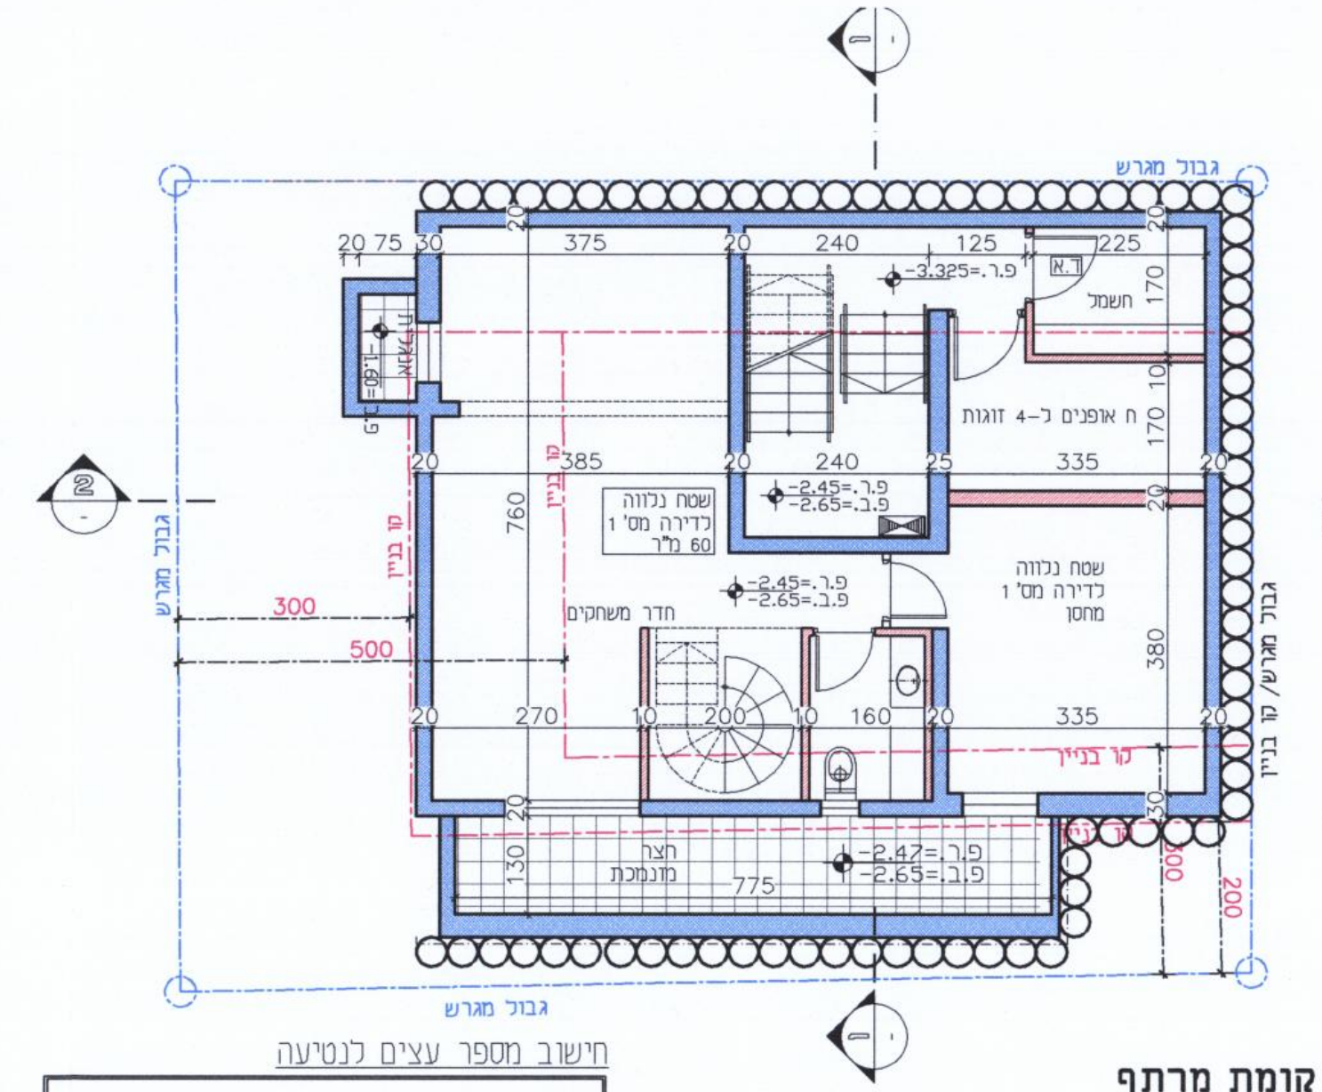
תכנית קומת מרתף

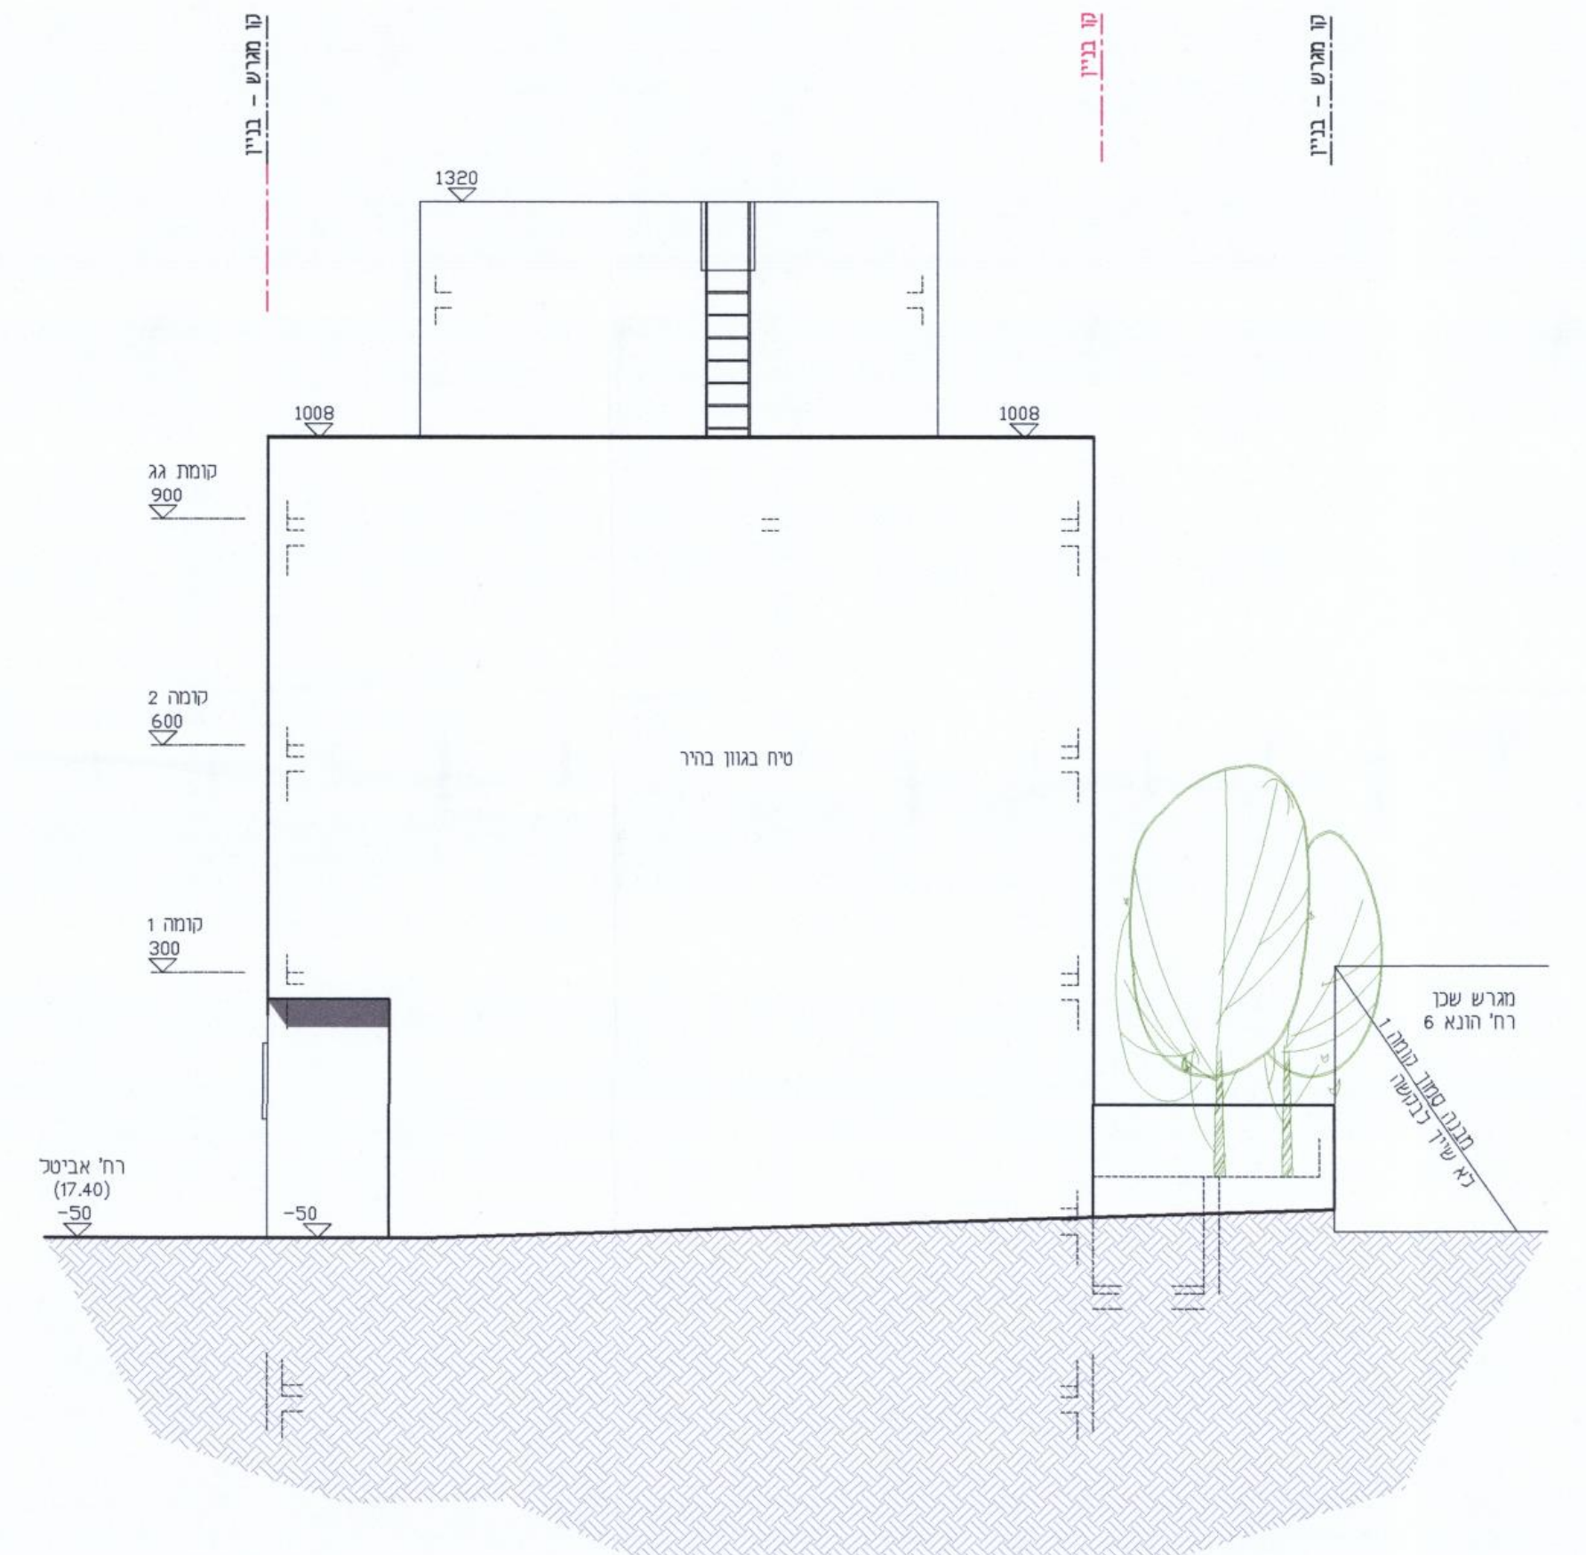
חזית צפונית - קיר בקו 0

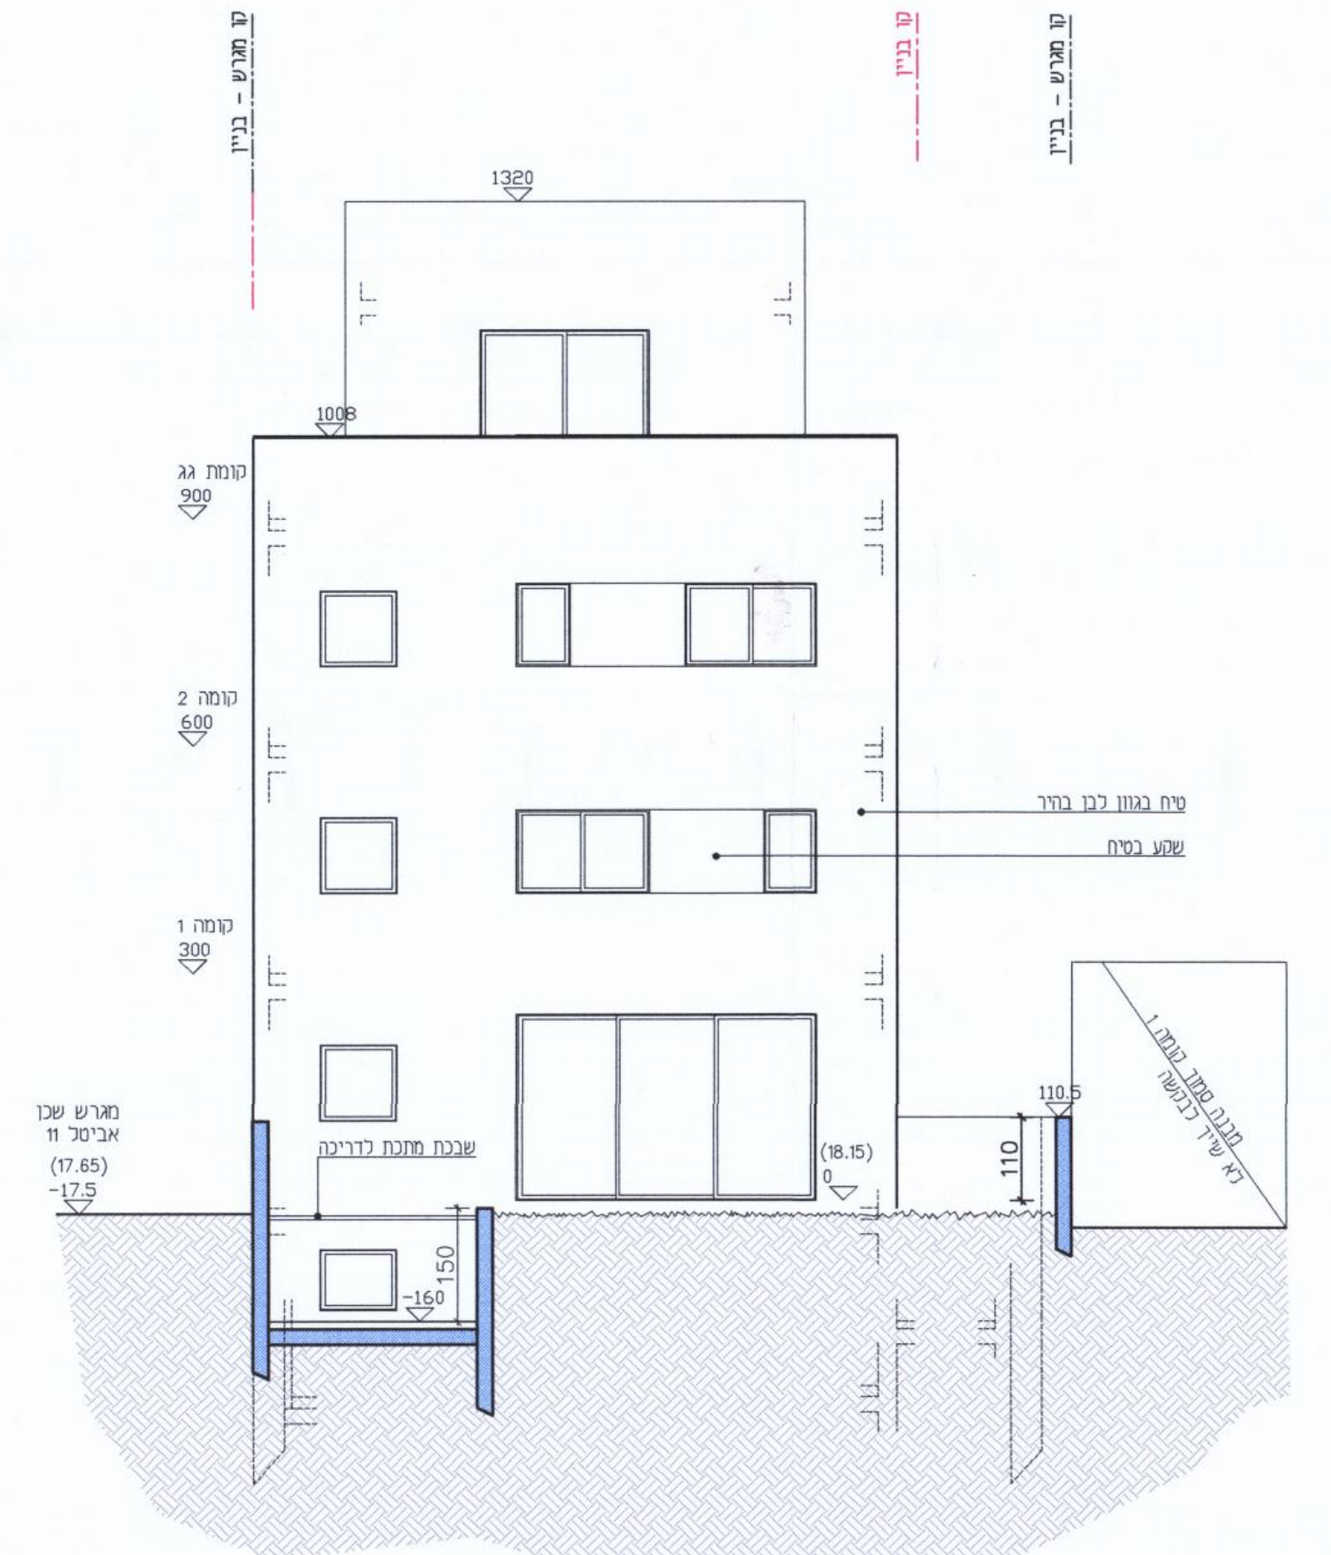
חזית מערבית

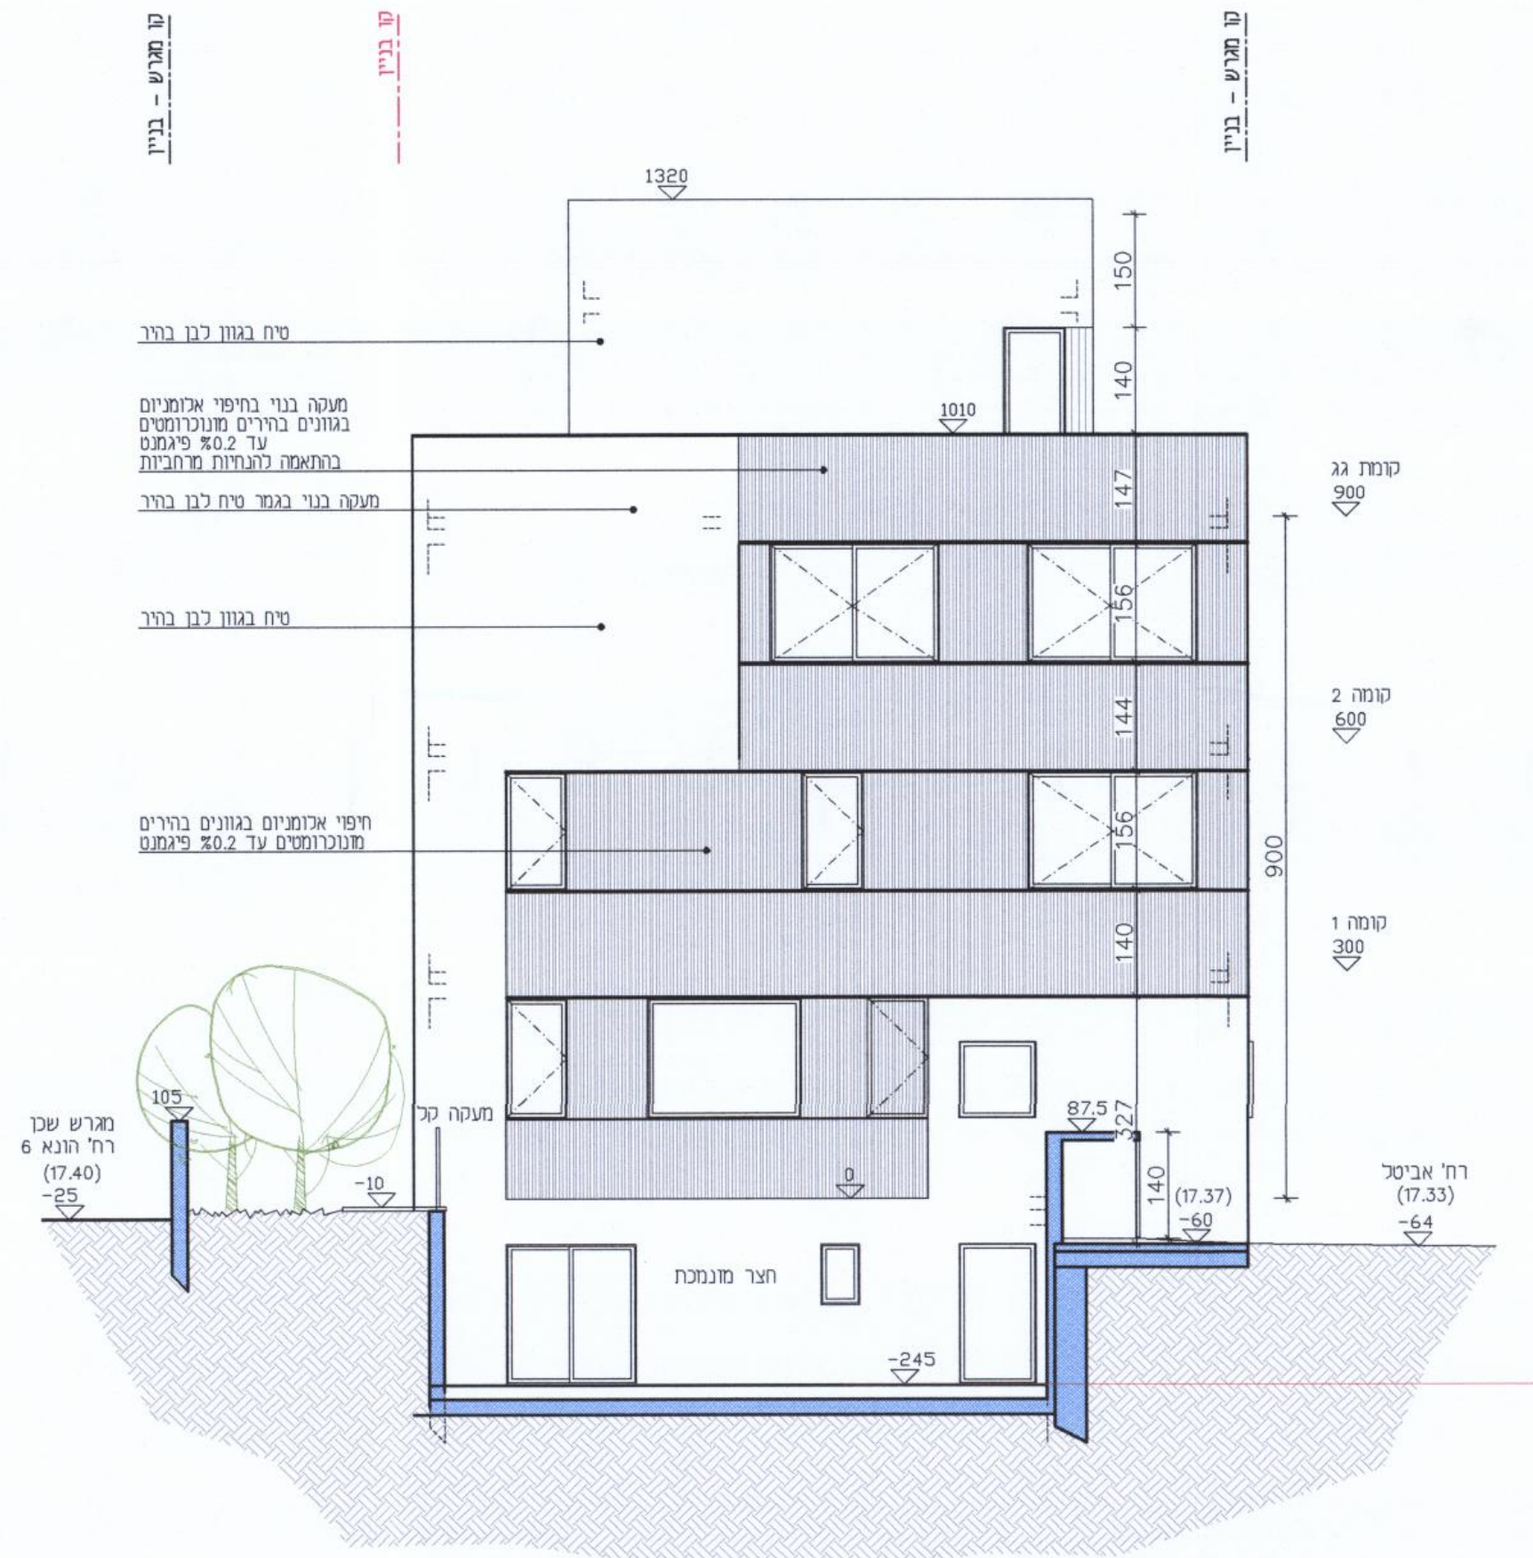
חזית דרומית

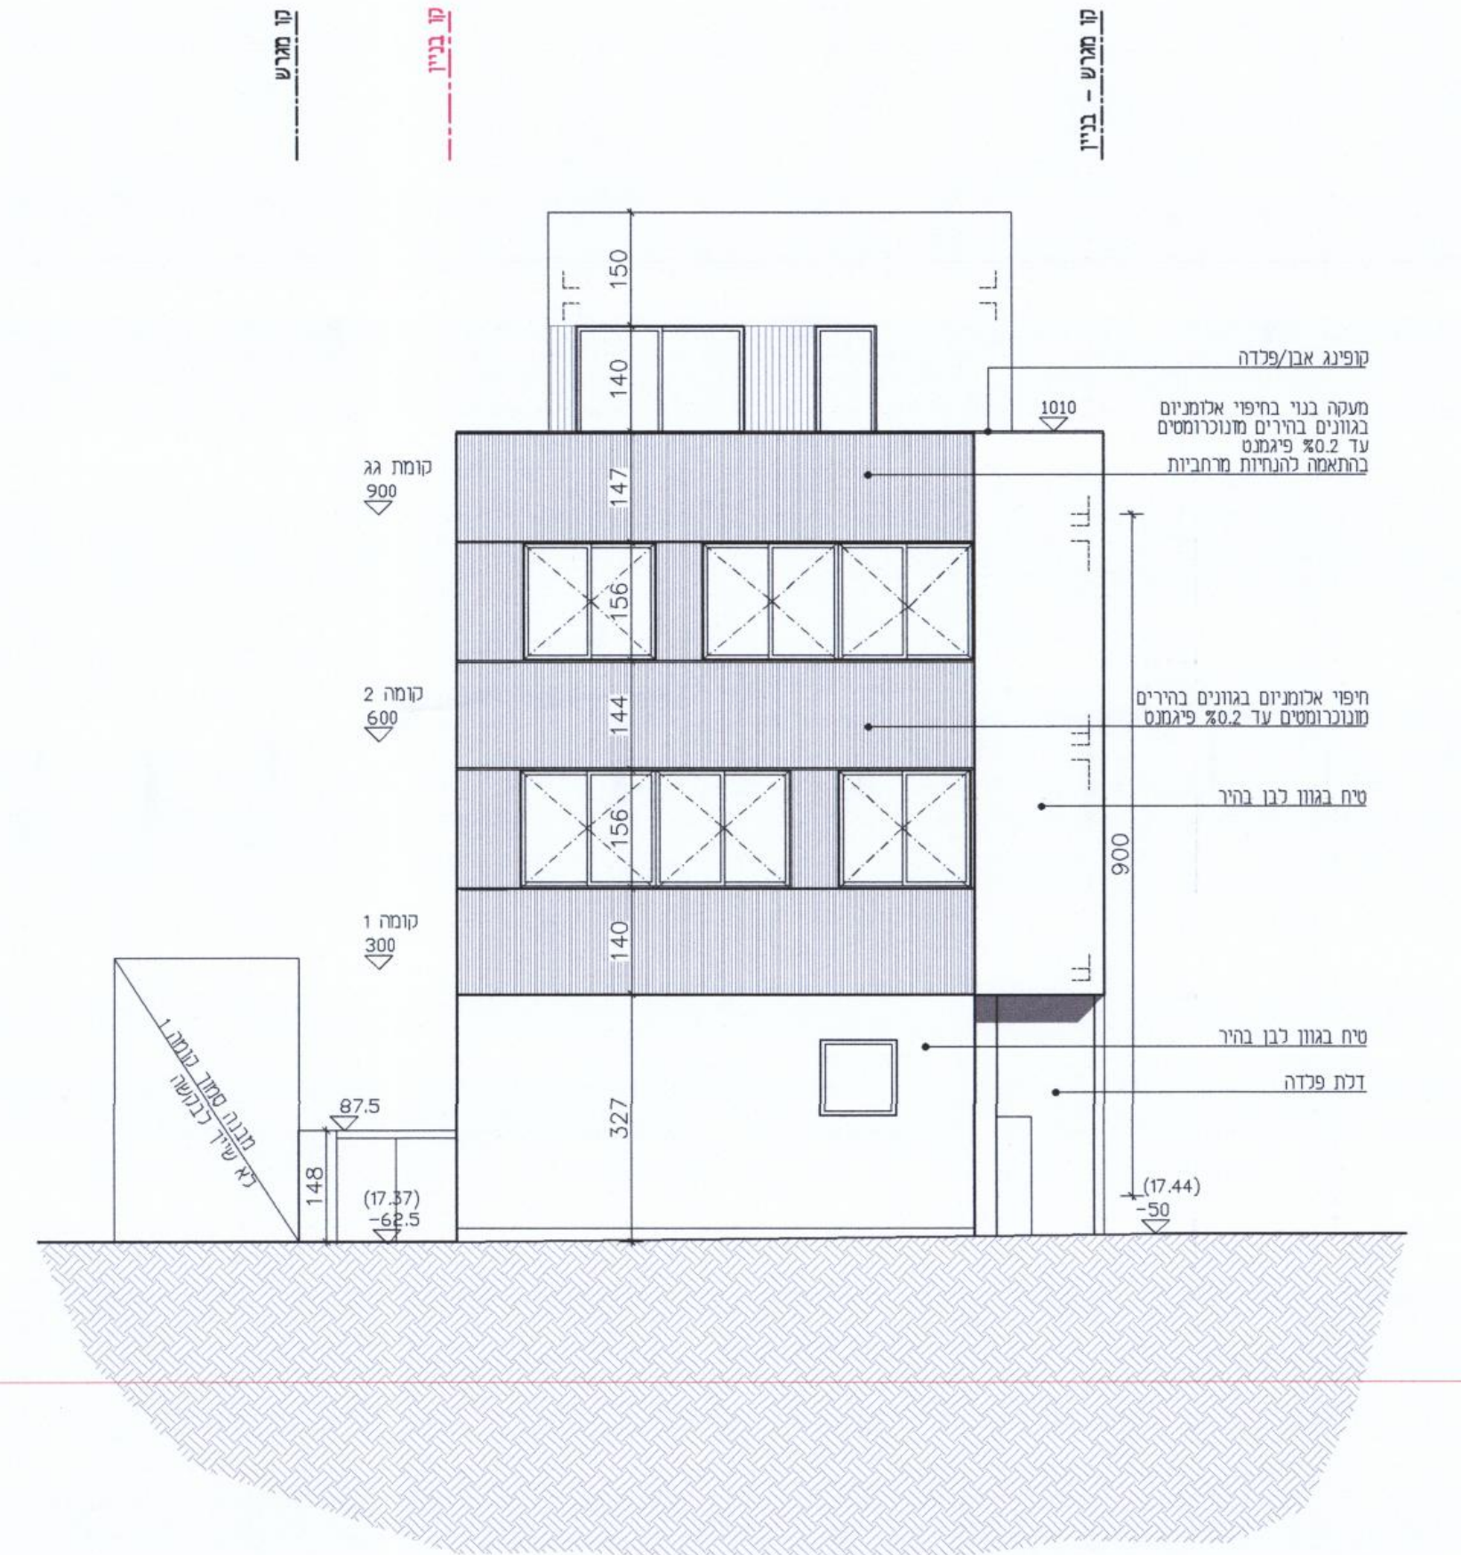
חזית מזרחית - רחוב אביטל

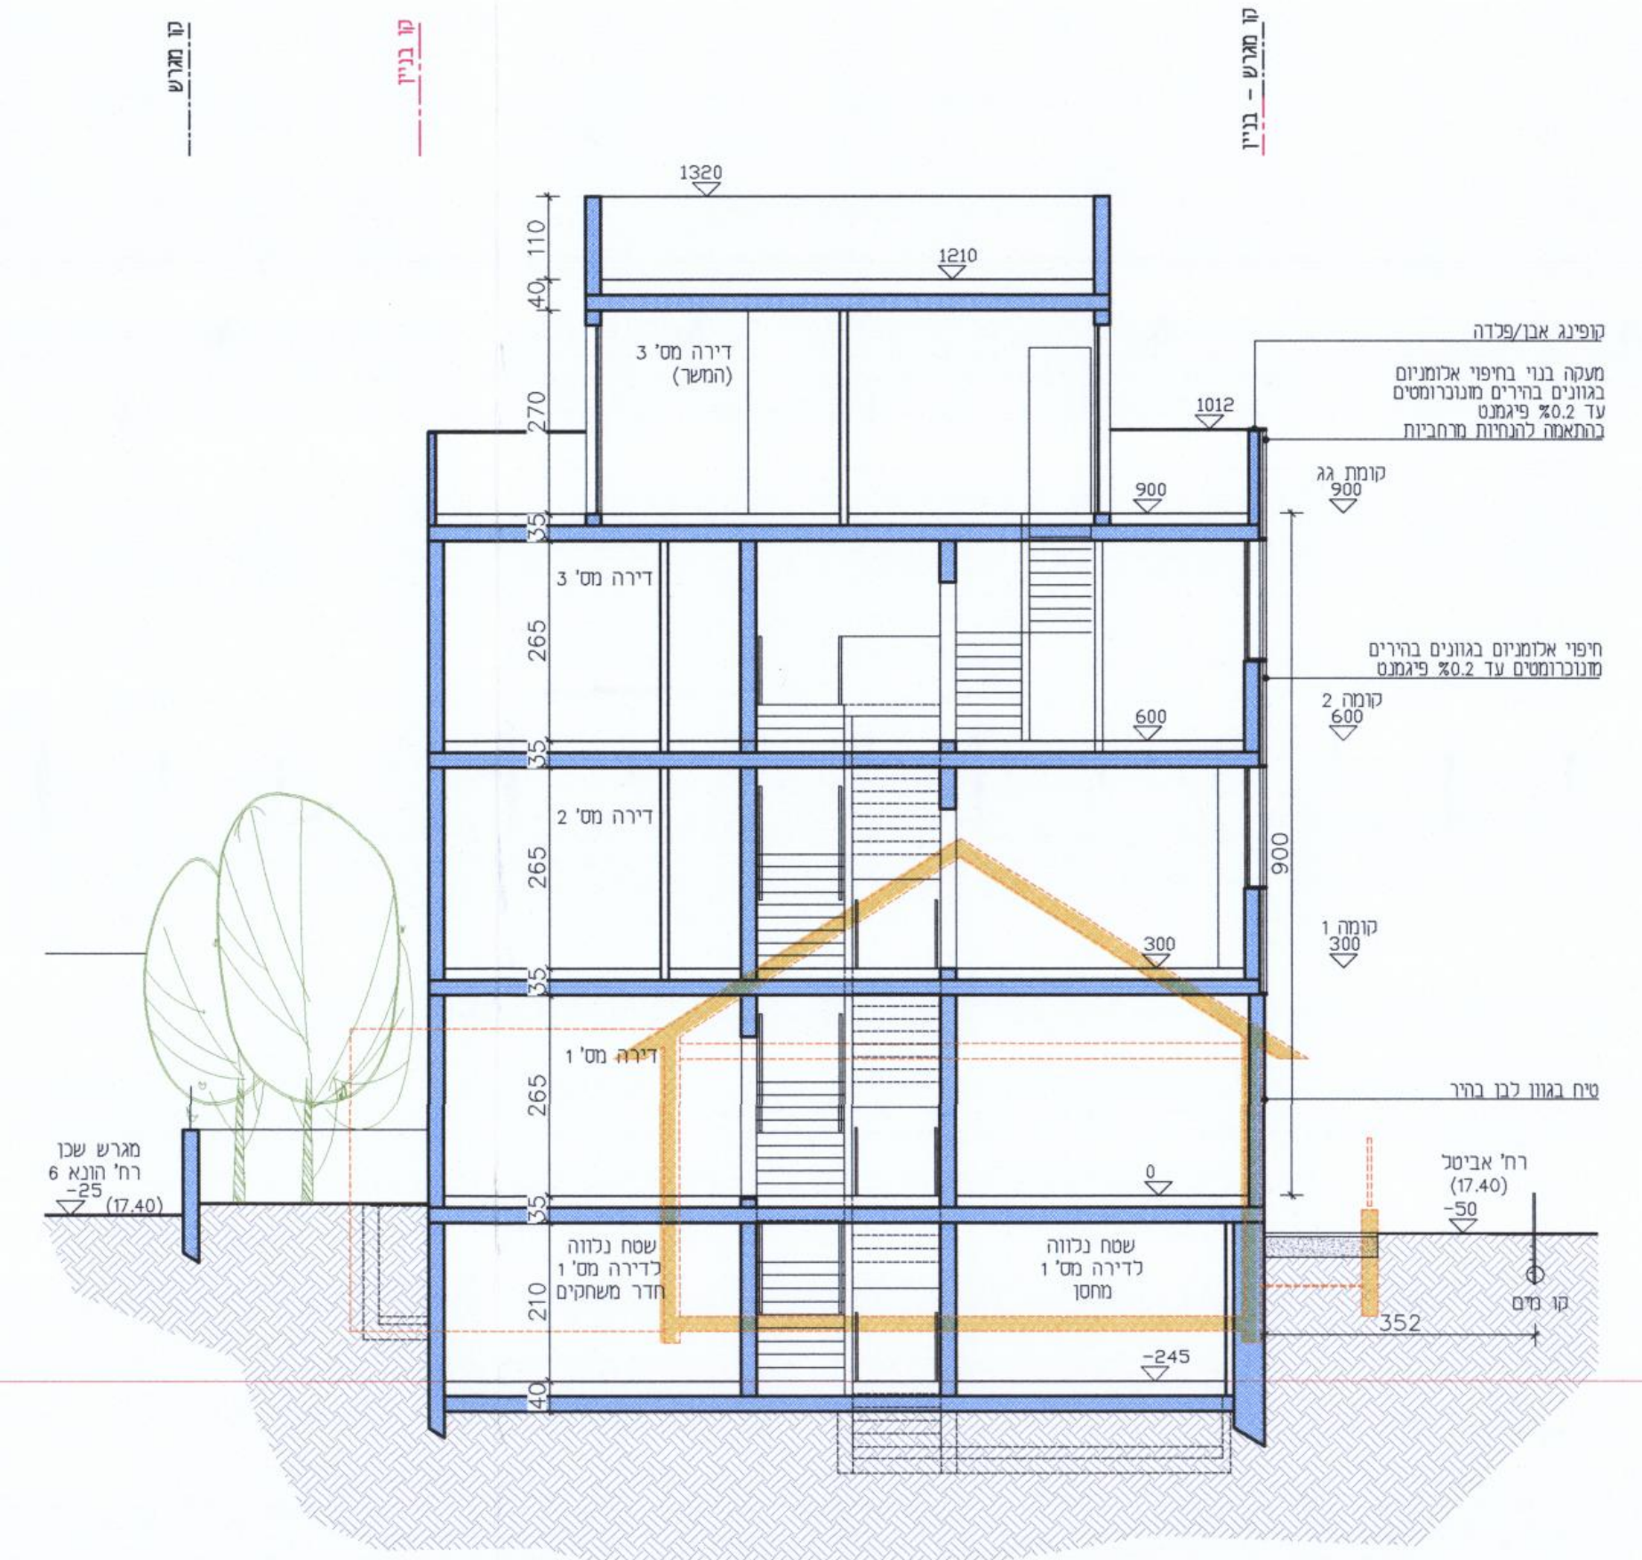
חתך 2-2

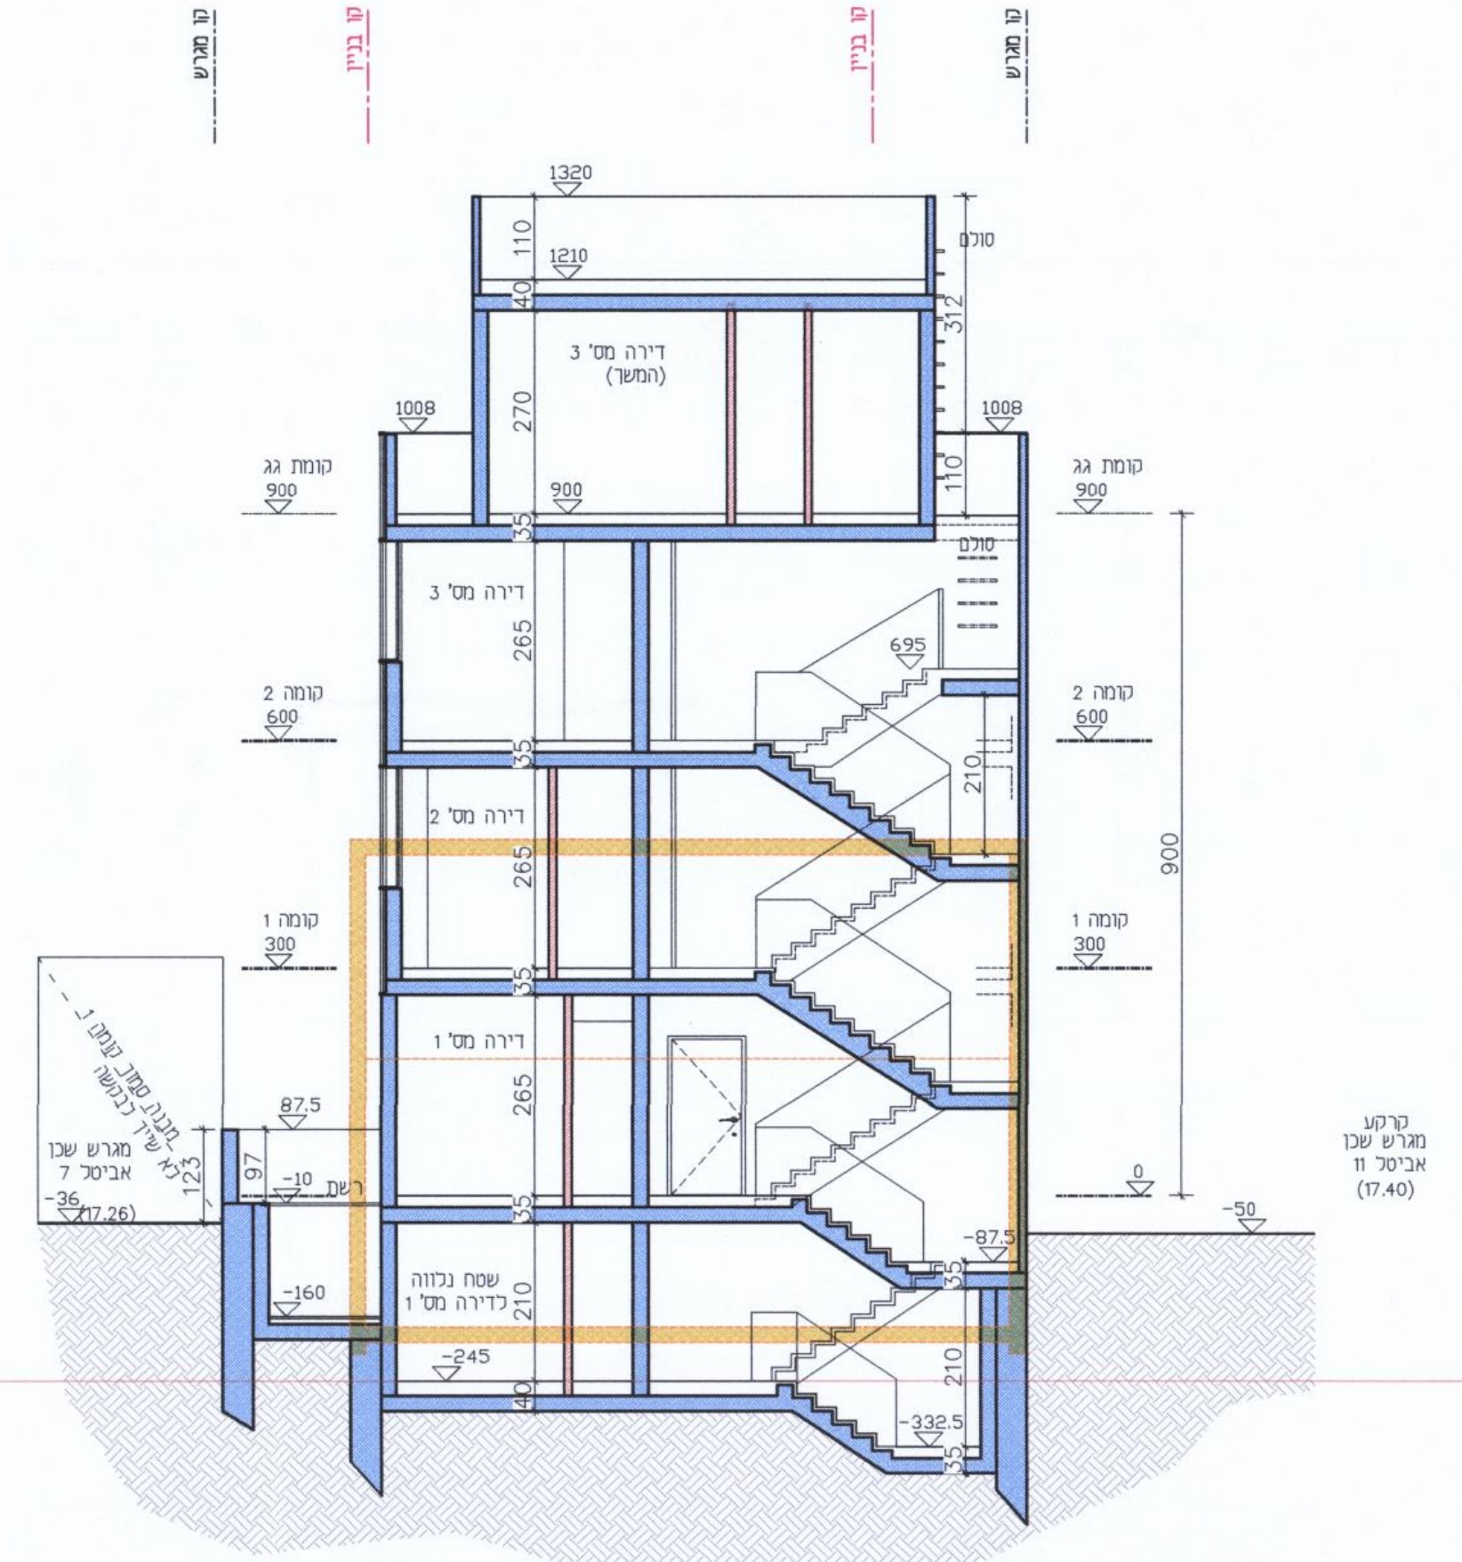
חתך 1-1

מפה טופוגרפית
1 : 250

תל-אביב
גוש : 6135
כתובת : רח' אביטל, 9
מהות הבקשה : בניה חדשה
חלקות : 44, 45 (חלקים)
שם הבעלים כרשום בנסח טאבו+מסי ת.ז :

חלקה	שם הבעלים	מסי ת.ז.	שטח חלקה כולה	בעלות בחלקים	בעלות במ"ר	שטח מדוד במ"ר
44	כהן כרמלה	5240639	11.476	3729/3718224	11.50	109.85
	כהן כרמלה	5240639		5311/619704	98.35	
45	קלב צבי	023574437	9.821	307/19642	153.50	37.70
					263.35	147.54

בעלות במ"ר : 263.35
שטח מדוד(מ"ר) : 147.54

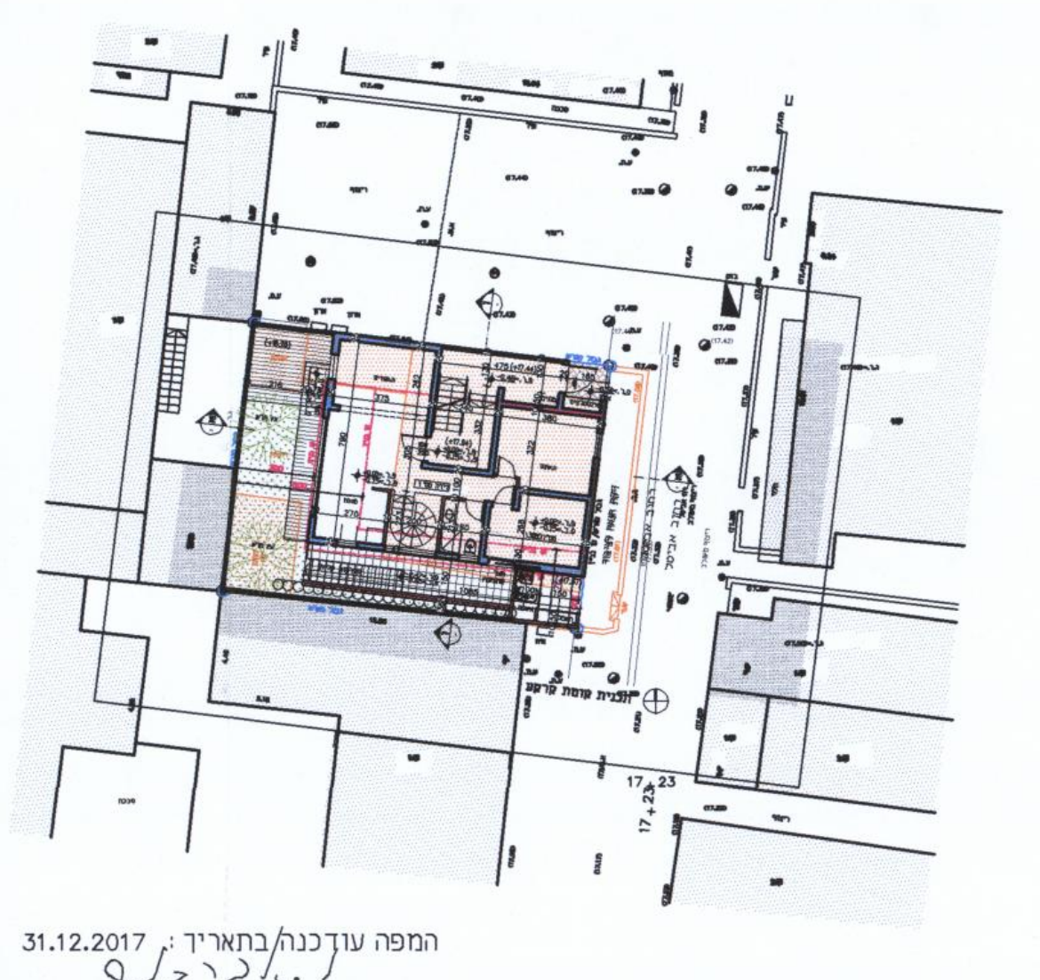

המפה עודכנה בתאריך : 31.12.2017

לא לצרכי רישום

י.אברבוך מודד מוסמך
רשיון מסי "461"

תל אביב
תאריך : 11.12.2016

הנני מצהיר בזה שהמפה נעשתה לפי חוק התכנון והביה, התקנות וההנחיות של עירית תל-אביב-יפו.

חבי אברבוך י.ת. בע"מ
רח' דיזנגוף, 190, ת"א טל. 03-5226791, 5235891

מקרא

ע.ח.	עמוד חשמל
ע.ט.	עמוד טלפון
ע.ת.	עמוד תאורה
א.ש.	אבן שפה
א.גן	אבן גן
א.ח. א.חשמל	ארון חשמל
ק/2	מבנה 2 קומות
ב.ש.	ברז שרפה
ג.ר.=(19.06)	גובה רצפה
מגוף	שעון מים
(3.57)	גובה קרקע
מ'	שוחת מים
ת.ב.	שוחת ביוב
ניקוז	שוחת ניקוז
בזק	תקשורת
	עצים
64	מספר חלקה
-69.53-	גבול החלקה
	גבול גוש
קו בניין 2.00 מ'	קו בניין

תרשים הסביבה 1:1250

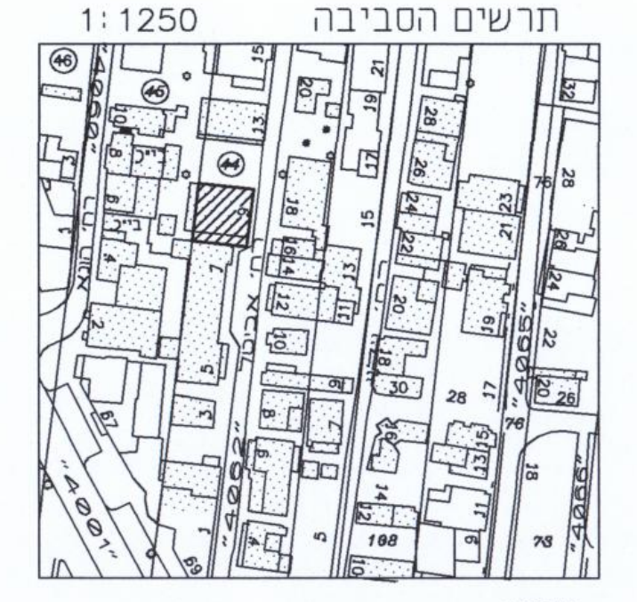

הערות :
1. המספרים בסוגריים מציינים גבהים.
2. הגבהים מבוססים על נ.ק. עירונית מסי 188 שגובהה 17.530 מ'.

נסרק

20

007

פרטי הבקשה להיתר:
מספר פנייה 12420
כתובת: אביטל 9
תאריך הדפסה: 16/06/2020

תצהיר

אני החתום/ה מטה הררי תומר
בעל/ת ת.ז. 062855119
מצהיר/ה כי :

1. ביום 27/05/2018 הגשתי לעיריית תל אביב קבצי המחשב במסגרת הגשת בקשה להיתר בניה בפניה שמספרה 12420
2. את הקבצים הנ"ל, המפורטים ברשימה להלן, חתמתי בעצמי בחתימתי האלקטרונית.
3. רשימת הקבצים :

100_AVTL.dwfx
100_AVTL.dwfx
150_AVTL.dwg
1500_avtl_HITHAIVUTTASHLUM.pdf
1500_avtl_ishur.jpg
1500_avtl_tnua.dwf
1600_avtl_nspahmigun.jpg
1800_avtl.dwfx
1800_avtl_elect.pdf
1800_avtl_leter.jpg
2100_IMG_8947.JPG
2100_IMG_8948.JPG
2200_avtl_tabu_p20.PDF
2200_avtl_tabu_p31.PDF
2200_P20.jpg
2200_P26.jpg
2200_TZ_EDI.jpg
2200_TZ_NOAM.pdf
2380_avtl_1.pdf
2380_avtl_2.pdf
2380_avtl_3.pdf
2600_avtl_nezakim.pdf
400_avtl_biuv.dwf
450_avtl_water.zip
500_avtl_1.dwfx
501_avtl_btihut.dwf
5100_avtl.pdf
5100_avtl_2.pdf
5100_avtl_h.pdf
5200_avtl_ashpa.dwfx
5500_avtl_1.jpg
5500_avtl_2.jpg
5500_avtl_3.jpg
5800_avtl_takana27.dwfx
600_avtl.dwfx
8000_avtl_oganim.pdf
901_avital 9.pdf

4. השוותי בין התכנית המצויה בקבצים הנ"ל לבין התכנית המצויה בגיליון הנייר עליו מודבק תצהיר זה ומצאתי כי התכנית זהה בשניהם (בקבצים ובנייר).

שם: תומר הררי תאריך: 1/7/20 חתימה: אדריכל תומר הררי מ.ר. 20998871

פניה 12420 תאריך יצירה 16.06.2020 בקשה 19-0024

עיריית תל-אביב-יפו
מינהל הנדסה
אגף רישוי ופיקוח על הבניה

חוק התכנון והבניה התשכ"ה- 1965
תקנות התכנון והבניה (בקשה להיתר תנאיו ואגרות) התש"ל - 1970
על פי טופס 1 תקנה 2(א)

א. פרטי הנכס והמבקשים

בקשת מידע: 2018-01431
תיק בניין: 4062-009

כתובת
רחוב אביטל
בית 9
גוש/חלקה: 44/6135
שטח מגרש/חלקה: 147.00 מ"ר
שטח בניה מבוקש: 381.88 מ"ר
אחוז בניה: 259.78

תכניות החלות על המקום והן מקור לשטחים מבוקשים
2215
1א2215
ג/3א
הקלה: 6% הקלה
ע1

פרטים אישיים	שם משפחה שם פרטי שם חברה או תאגיד	רחוב / מספר בית ישוב מיקוד
מבקש	כהן נועם יואל	ביל"ו 47 תל אביב - יפו 6425605
בעל זכות בנכס	כהן נועם יואל	ביל"ו 47 תל אביב - יפו 6425605
בעל זכות בנכס	כהן אדמונד	נחום הנב"א 12 תל אביב - יפו 6350314
עורך ראשי	הררי תומר	החשמל 11 תל אביב - יפו 6618905
מתכנן שלד	מזרחי תמיר	המלאכה 2 רעננה 4366101

ב. מהות הבקשה

סוג הבקשה
בניה חדשה / בניין מגורים לא גבוה (עד 13 מ')

שימוש
מגורים
ממ"ד/ממ"ק/מקלט-שטח עיקרי
מרתפים
מבואות וחדרי מדרגות

ג. מפרט תאור הבקשה

פירוט המבוקש במרתפים
מרתף אחד בלבד
חדרי עזר

פירוט המבוקש בקומת הקרקע
אחר: מגורים

פירוט המבוקש בקומות
כמות קומות מגורים: 3
כמות יח"ד מבוקשות: 3

פירוט המבוקש על הגג
חדרי יציאה

פירוט המבוקש בחצר
גינה
גדר בגבולות מגרש בגובה (מטר): 1.5

ד. חומרי הבנייה

סוג הבניה
רגילה

קירות חיצוניים
בטון מזוין
בלוקים

חומרי גימור
טיח
אחר: חיפוי אלומיניום

תקרות
בטון מזוין

גג
בטון מזוין

גדרות
אחר: טיח

מקרא חומרים (צבעים)
בטון או בטון מזוין: כחול
בלוקים או לבנים: אדום
עץ: חום
זכוכית: סגול
הריסה: צהוב
בניה קיימת: אפור

ו. קווי בנייה

לרחוב אביטל מוצע: 0
לצד מוצע: 0
לאחור מוצע: 3 מותר: 5 סטייה במטר: 2 סטייה באחוז: 40
לצד 2 מוצע: 2 מותר: 3 סטייה במטר: 1 סטייה באחוז: 33.33

ז. מספר יחידות דיור

מספר יחידות הדיור הקיימות: 1
מספר יחידות הדיור לביטול/הריסה: 1
מספר יחידות הדיור המבוקשות ששטחן עד 120 מ"ר: 2
מספר יחידות הדיור המבוקשות ששטחן מעל 120 מ"ר: 1
מספר יחידות הדיור המותרות: 3

ח. פרטי הבנייה - לשימוש הלשכה המרכזית לסטטיסטיקה

שטח הבניה ברוטו לפי היעוד
למגורים: מגורים שטח: 381.87
סך כל שטחי הבניה: 381.87

גודל הדירות לפי מספר חדרים
חדר 4: מספר דירות: 2
חדר 5: מספר דירות: 1
סה"כ מספר דירות: 3

ט. הבקשה מוגשת לאישור

הקלות מאושרות – ראו החלטת הוועדה

ה. השטחים המבוקשים (על-פי תכני תכנית הבנייה) והמותרים לבנייה

(על-פי "אסמכתא" : חוק, תקנות, תכניות) בכל מפלס בנפרד ולפי שימוש

מבנה	הקומה	מפלס	מגורים מבוקש	ממ"ד/ממ"ק/מקלט שטח עיקרי מבוקש	מבואות וחדרי מדרגות מבוקש	ממ"ד/ממ"ק/מקלט שטח שירות לשמוש מגורים מבוקש	מעברים מבואות וחדרי מדרגות לשמוש מגורים מבוקש	עובי קירות ממ"ד/ממ"ק/מקלט לשימוש מגורים מבוקש	שטח תת קרקעי נלווה מבוקש	עיקרי: סה"כ	עיקרי: % משטח המגרש	אסמכתא: תכנית ראשית/אחר	שירות: סה"כ	שירות: % משטח המגרש	סה"כ קומה: עיקרי+שירות	סה"כ קומה: % משטח המגרש	סה"כ קומה: שטחים לא מקורים
		±0.00 = +17.40															
1	מרתף -1	-3.15					26.6700		55.2051			ע1	81.8751	55.70	81.8751	55.70	
1	קרקע 0	0.00	53.4640		15.9180	8.9610		3.1020		69.3820	47.20	2215 1א2215	12.0630	8.21	81.4450	55.40	
1	קומה 1	3.15	64.5890	0.9109	11.8080	8.8346		3.2025		77.3079	52.59	2215 1א2215	12.0371	8.19	89.3450	60.78	
1	קומה 2	6.30	64.5890	0.9109	11.8080	8.8346		3.2025		77.3079	52.59	(הקלה) 6% הקלה 2215 1א2215	12.0371	8.19	89.3450	60.78	
1	קומה 3	9.45	39.8650							39.8650	27.12	ג/3א			39.8650	27.12	49.4800
	מתחת לקרקע						26.67		55.21				81.88	55.70	81.88	55.70	
	מעל הקרקע		222.51	1.82	39.53	26.63		9.51		263.86	179.50		36.14	24.58	300.00	204.08	49.48
	סה"כ		222.51	1.82	39.53	26.63	26.67	9.51	55.21	263.86	179.50		118.01	80.28	381.88	259.78	49.48

י. הצהרת עורך הבקשה הראשי

אני מצהיר על נכונות הפרטים בסעיפים א עד ט

תאריך 1/7/20 שם: הררי תומר חתימה: אדריכל תומר הררי מ.ר. 20998871

יא. חתימות נוספות

תפקיד	שם	תאריך	חתימה
מבקש	כהן נועם יואל		
בעל זכות בנכס	כהן נועם יואל		
בעל זכות בנכס	כהן אדמונד	29.6.2020	
מתכנן שלד	מזרחי תמיר		תמיר מזרחי מהנדס בניין ת.פ. 5214845

לתשומת לב החותם על תכנית הבקשה להיתר

1) אין לחתום על תכנית הבקשה להיתר, אלא אם היא חלק מהדפסה רציפה (גרמוקשה / הרמוניקה) בנייר הכוללת את טופס1(פרטים ונתונים מילוליים ומספריים של הבקשה להיתר, חתום בחותמת מים של עיריית תל אביב) תרשים חישוב השטחים(חתום בחותמת מים של עיריית תל אביב) ותכנית הבקשה להיתר (תכניות, חתכים, חזיתות וכד').

2) לאחר שתפתח בקשת רישוי במחלקת רישוי בניה תשלח אליך הודעה עם מספר הבקשה להיתר. לאחר קבלתה, עליך להכנס לתיק הבניין בגנזך ההנדסה האינטרנטי באתר עיריית תל אביב ולוודא שהתכנית הנוכחית עליה חתמת כאן זהה למסמכי הבקשה להיתר כפי שהם מופיעים בתיק הבניין האינטרנטי.

יב. מינויים מטעם מבקש ההיתר

מינוי עורך הבקשה הראשי

אני ממנה בזה את הררי תומר בעל/ת מס' זהות 062855119 הרשום בסעיף א לדיות עורך הבקשה הראשי להיתר, ולייצגני לפני מוסדות התיכנון והרשויות המוסמכות בכל הנוגע לטיפול בבקשה להיתר ולקבלתו, לרבות התיקונים ככל שידרשו הרשויות המוסמכות.

מינוי עורכי בקשה לפי תחומים

אני ממנה את הרשומים להלן להיות עורכי הבקשה להיתר בתחום הפעולה כרשום ליד שמם, ולייצגני בתחום פעולתו לפני מוסדות התכנון והרשויות המוסמכות בכל הנוגע לטיפול בבקשה להיתר ולקבלתו, לרבות התיקונים ככל שידרשו הרשויות המוסמכות.

שם משפחה שם פרטי	תחום פעילות	המען	פרטי התקשרות
.1			
.2			
.3			

מינוי מתכנן שלד הבניין

אני ממנה בזה את מזרחי תמיר בעל/ת מס' זהות 035804335 הרשום בסעיף א לדיות אחראי לתכנון שלד הבניין שבעבורו מבוקש ההיתר, להגיש לוועדה המקומית לרשות הרישוי המקומית את החישובים לגבי הבניין שבעבורו מבוקש היתר ולפקח פיקוח עליון על הקמת השלד.

מינוי הקבלן האחראי לבנייה

☐ אני ממנה בזה את ________ בעל/ת מס' זהות ________ ובעל תעודת רישום בפנקס קבלנים מספר ________ בסיווג ________ ובעל רישיון לביצוע עבודה בתוקף עד ________ לבצע את העבודה הנדונה בהיתר בהתחייב לפי כל דין.

☐ אני מצהיר, כי טרם מסרתי את ביצוע העבודה הנדונה בהיתר לידי קבלן, ומתחייב למסור אותה לידי קבלן רשום בפנקס הקבלנים, בהתחייב על פי כל דין, ולהודיע על כך לרשות הרישוי המקומית טרם התחלת ביצוע העבודה, וחתימתו של הקבלן תצורף להודעה המפרטת את פרטי רישומו של הקבלן.

מינוי האחראי לבניית שלד הבניין

☐ אני ממנה בזה את ________ בעל/ת מס' זהות ________ כתובת ________ טלפון ________ מייל ________ הרשום לעיל להיות אחראי לביצוע שלד הבניין.

☐ אני מצהיר, כי טרם מיניתי אחראי/ת לביצוע עבודות הבנייה בתחומים אלה: ________ ומתחייב לעשות זאת כמפורט בתקנות, ולהודיע על כך לרשות הרישוי המקומית טרם התחלת ביצוע העבודה.

מינוי אחראים לביקורת

☐ אני ממנה בזה את הרשומים להלן להיות אחראים לביקורת על ביצוע עבודות בתחום הפעולה כרשום ליד שמם

שם משפחה שם פרטי	תחום פעילות	המען	פרטי התקשרות
.1			
.2			
.3			

אני מצהיר כי טרם מיניתי אחראי/ת לביקורת על ביצוע עבודות הבנייה את כולם או את קצתם בתחומים האלה: ________ ומתחייב לעשות זאת כמפורט בתקנות, ולהודיע על כך לרשות הרישוי המקומית טרם התחלת ביצוע העבודה.

חתימת המבקש על המינויים ________

יג. הצהרות

הצהרת עורכי הבקשה כולל הצהרות עורך הבקשה על לחץ המים

אנו החתומים מטה מצהירים בזה:
1) כל אחד מאתנו מאשר שהאמור בנוגע לרשימה שבסעיף י"ב לעיל הוא נכון.
2) כל אחד מאתנו מסכים לקבל עליו את התפקיד המיועד לו בסעיף י"ב לעיל.
3) אנו מצהירים, כל אחד בנוגע לתחום פעולתו, שיש לנו כישורים מקצועיים לערוך בקשה זו וכי בדקנו את המסמכים הנודעים לבקשה, לרבות כל תכנית הנוגעת לבקשה, וידוע לנו כי אם הצהרה זו אינה נכונה, הרי היא תיחשב מסירת ידיעה שהיא כוזבת או מטעה בפרט חשוב, כמשמעותה בסעיף 214 לחוק, וצפויים לנו העונשים הקבועים לפי כל דין.

אני הררי תומר (עורך בקשה ראשי) אחראי/ת לכך שהבקשה, ובכלל זה נספחיה, נערכה לפי מיטב הידיעה המקצועית ובהתאם לכל חיקוק החל על הבניין או העבודה המוצעת, שכל הנתונים שנמסרו על ידי בבקשה זו נכונים ושהתכנון המוצע תואם את כל התכניות, פרט לסטיות שפורטו לעיל.

☐ אני עורך הבקשה מתכנן האינסטלציה הסניטרית, מצהיר בזאת ואחרי לכך שתכניות הבקשה בכל הנוגע לסידורים הסניטריים נערכו כדין וכי קויימו בהן הוראות החוק וההוראות למתקני תברואה התש"ל 1970 (הל"ת) לעניין זה, לרבות בדיקת לחץ המים הקיים בבניין ותיכנון המתקנים

	תאריך	שם משפחה שם פרטי	מספר רישיון	חתימה
עורך ראשי		הררי תומר	20998871	אדריכל תומר הררי מ.ר. 20998871

הצהרת מתכנן שלד הבניין

אני החתום מטה מזרחי תמיר מס' זהות 035804335 מהנדס רשוי מס' 548405 או הנדסאי בעל רישוי מס' ________ ("מבנה פשוט") מצהיר בזאת כדלקמן:
1) אני מסכים להיות מתכנן שלד הבניין הנדון בבקשה ולפקח פיקוח עליון על הקמת השלד.
2) כל אחד מאתנו מסכים לקבל עליו את התפקיד המיועד לו בסעיף י"ב לעיל.
3) ידוע לי, שאם אחרי הגשת הנתונים הסטטיים יתגלה צורך בשינוי מהותי בהם, אני מתחייב להגיש חישובים סטטיים מתוקנים מיד עם גילוי הצורך בכך.
4) אני מצהיר, כי יש לי כישורים מקצועיים לערוך בקשה זו וכי בדקתי את כל המסמכים הנוגעים לבקשה, לרבות כל תכנית הנוגעת לבקשה, וידוע לי כי אם הצהרה זו אינה נכונה, הרי היא תיחשב מסירת ידיעה שהיא כוזבת או מטעה בפרט חשוב, כמשמעותה בסעיף 214 לחוק, וצפויים לי העונשים הקבועים לפי כל דין.
5) ידוע לי כי עלי לשמור את תכנית הקונסטרוקציה לתקופה של לא פחות מ10- שנים לאחר גמר הבניה.

תאריך 30/6/20 חתימה

הצהרת האחראי לביצוע שלד הבניין (כאשר מונה)

אני החתום מטה (שם משפחה ושם פרטי) ________ מס' זהות ________ מהנדס רשוי מס' ________ או הנדסאי בעל רישוי מס' ________ ("מבנה פשוט") מצהיר בזאת כדלקמן:
1) אני מסכים להיות האחראי לבצוע שלד הבניין.
2) אני מצהיר, כי יש לי כישורים מקצועיים להיות אחראי לבצוע שלד הבניין, ואני מתחייב לדאוג לביצוע שלד הבניין על פי תוכניות והוראות של מתכנן השלד כפי שיינתנו בכתב וכן למלא את תפקידי על פי שנקבע בכל חיקוק הנוגע להן.

תאריך ________ חתימה ________

הצהרת אחראים לביקורת (כאשר מונו)

אנו החתומים מטה מצהירים בזה:
1) כל אחד מאיתנו מאשר שהאמור בנוגע לו ברשימה שבסעיף י"ב לעיל הוא נכון.
2) כל אחד מאיתנו מסכים לקבל עליו את התפקיד המיועד לו בסעיף י"ב.
3) אנו מצהירים כל אחד בנוגע לתחום פעולתו, שיש לנו כישורים מקצועיים לעדוך את הביקורת כהלכה ולדווח על תוצאותיה לרשות הרישוי המקומית, כמתחייב כל פי כל דין.
אני ________ (עורך הביקורת הראשי) אחראי/ת לכך שהביקורת תיערך על פי מיטב הידיעה המקצועית, ושכל הדיווחים לרשות הרישוי המקומית ייערכו על פי כל דין.

תאריך	שם משפחה שם פרטי	מספר רישיון	חתימה
/ /			
/ /			
/ /			
/ /			