מסמך סופי

D:\Documents and Settings\Massuri 01\My Documents\Doc&DWG on Massuri01\DWG2007\bnia\ויליון 9\agasa7.dwg, 17/06/2009 12:49:32, DesignJet 750C C3196A-anat.pc3

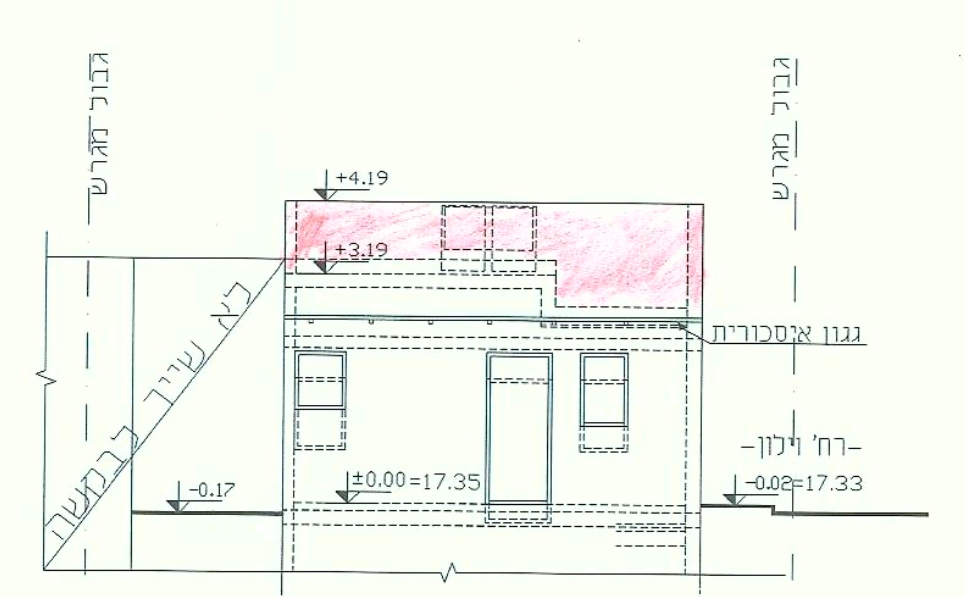
גבול מגרש
גבול מגרש
+4.19
+3.19
גגון אסכורית
לא שייך בבקשה
-רח' וילון-
±0.00=17.35
-0.17
-0.08=17.33

חזית דרומית ק.מ. 1:100

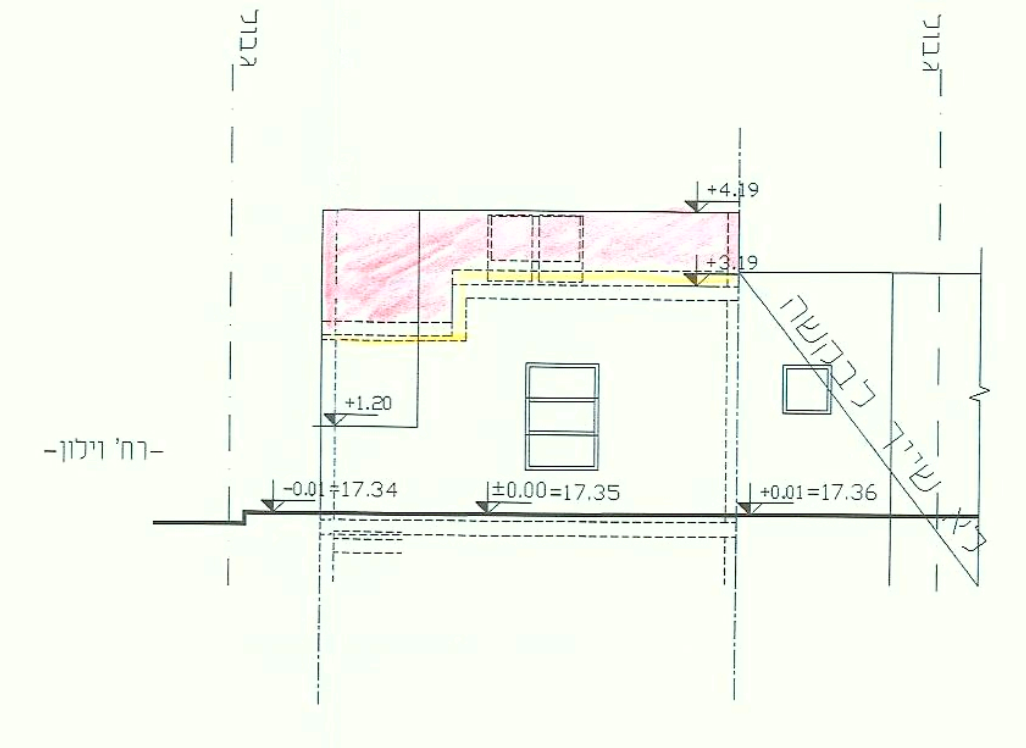
גבול מגרש
גבול מגרש
+4.19
+3.19
+1.20
-רח' וילון-
-0.01=17.34
±0.00=17.35
+0.01=17.36
לא שייך בבקשה

חזית צפונית ק.מ. 1:100

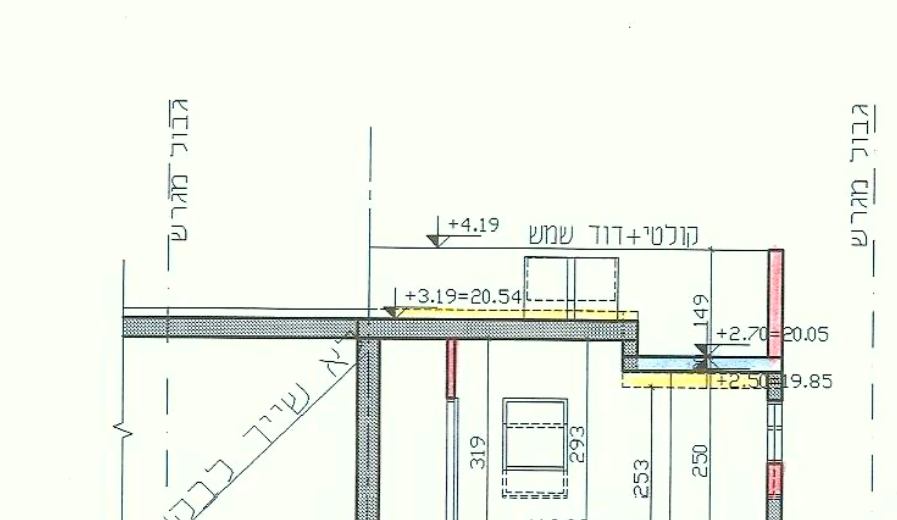
גבול מגרש
גבול מגרש
+4.19
קולטי+דוד שמש
+3.19=20.54
+2.70=20.05
+2.50=19.85
319
293
253
250
-0.26=17.09
±0.00=17.35
-רח' וילון-
+3.19=17.28
לא שייך בבקשה

חתך א-א ק.מ. 1:100

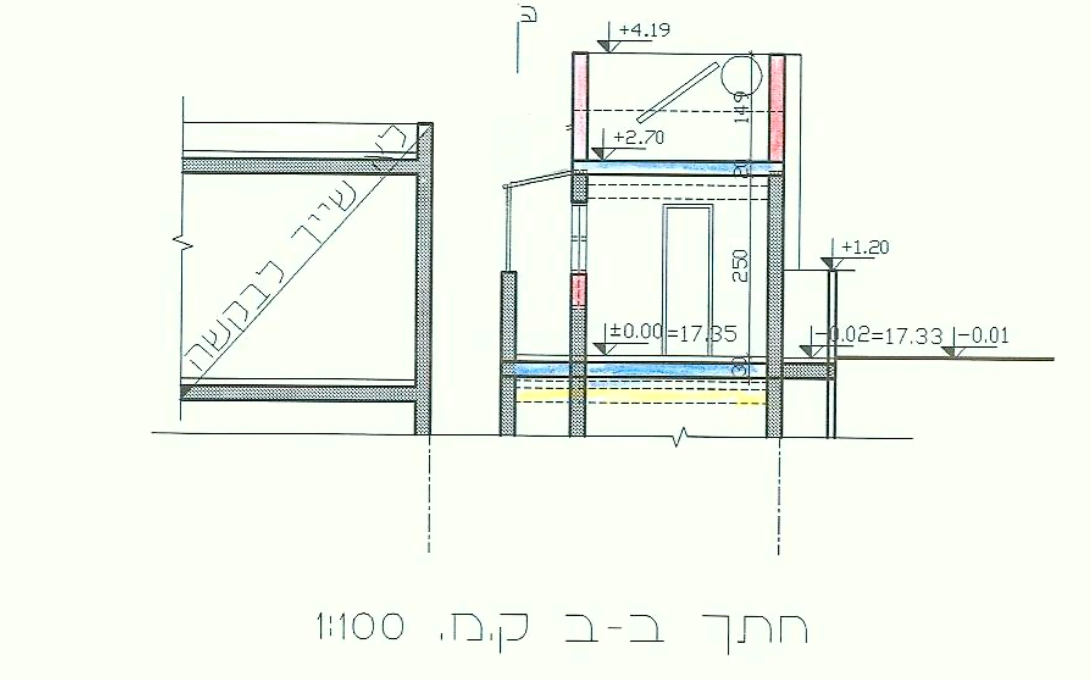
גבול מגרש
+4.19
+2.70
250
±0.00=17.35
+1.20
-0.02=17.33
-0.01
לא שייך בבקשה

חתך ב-ב ק.מ. 1:100

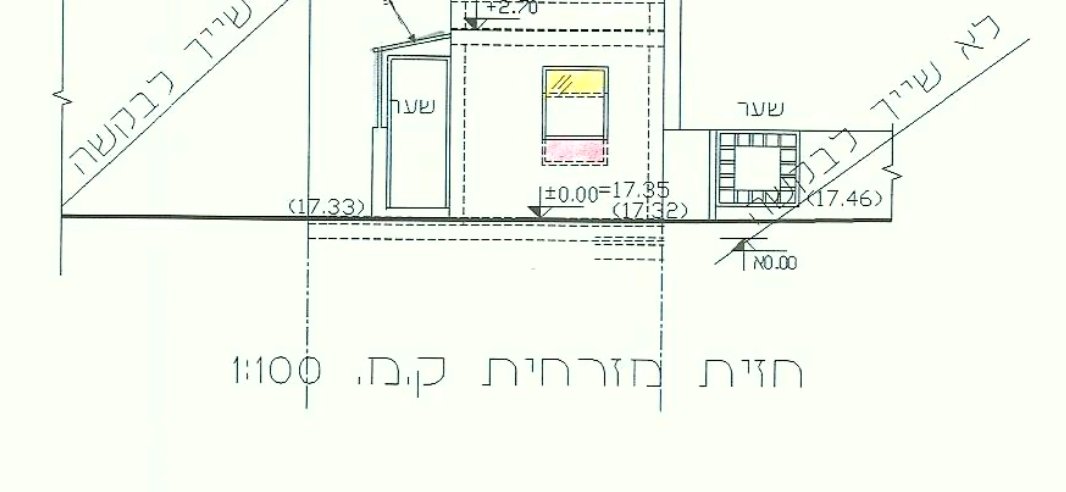
גגון אסכורית
+4.19
+3.19
+2.70
שער
שער
(17.33)
±0.00=17.35
(17.32)
(17.46)
±0.00
לא שייך בבקשה

חזית מזרחית ק.מ. 1:100

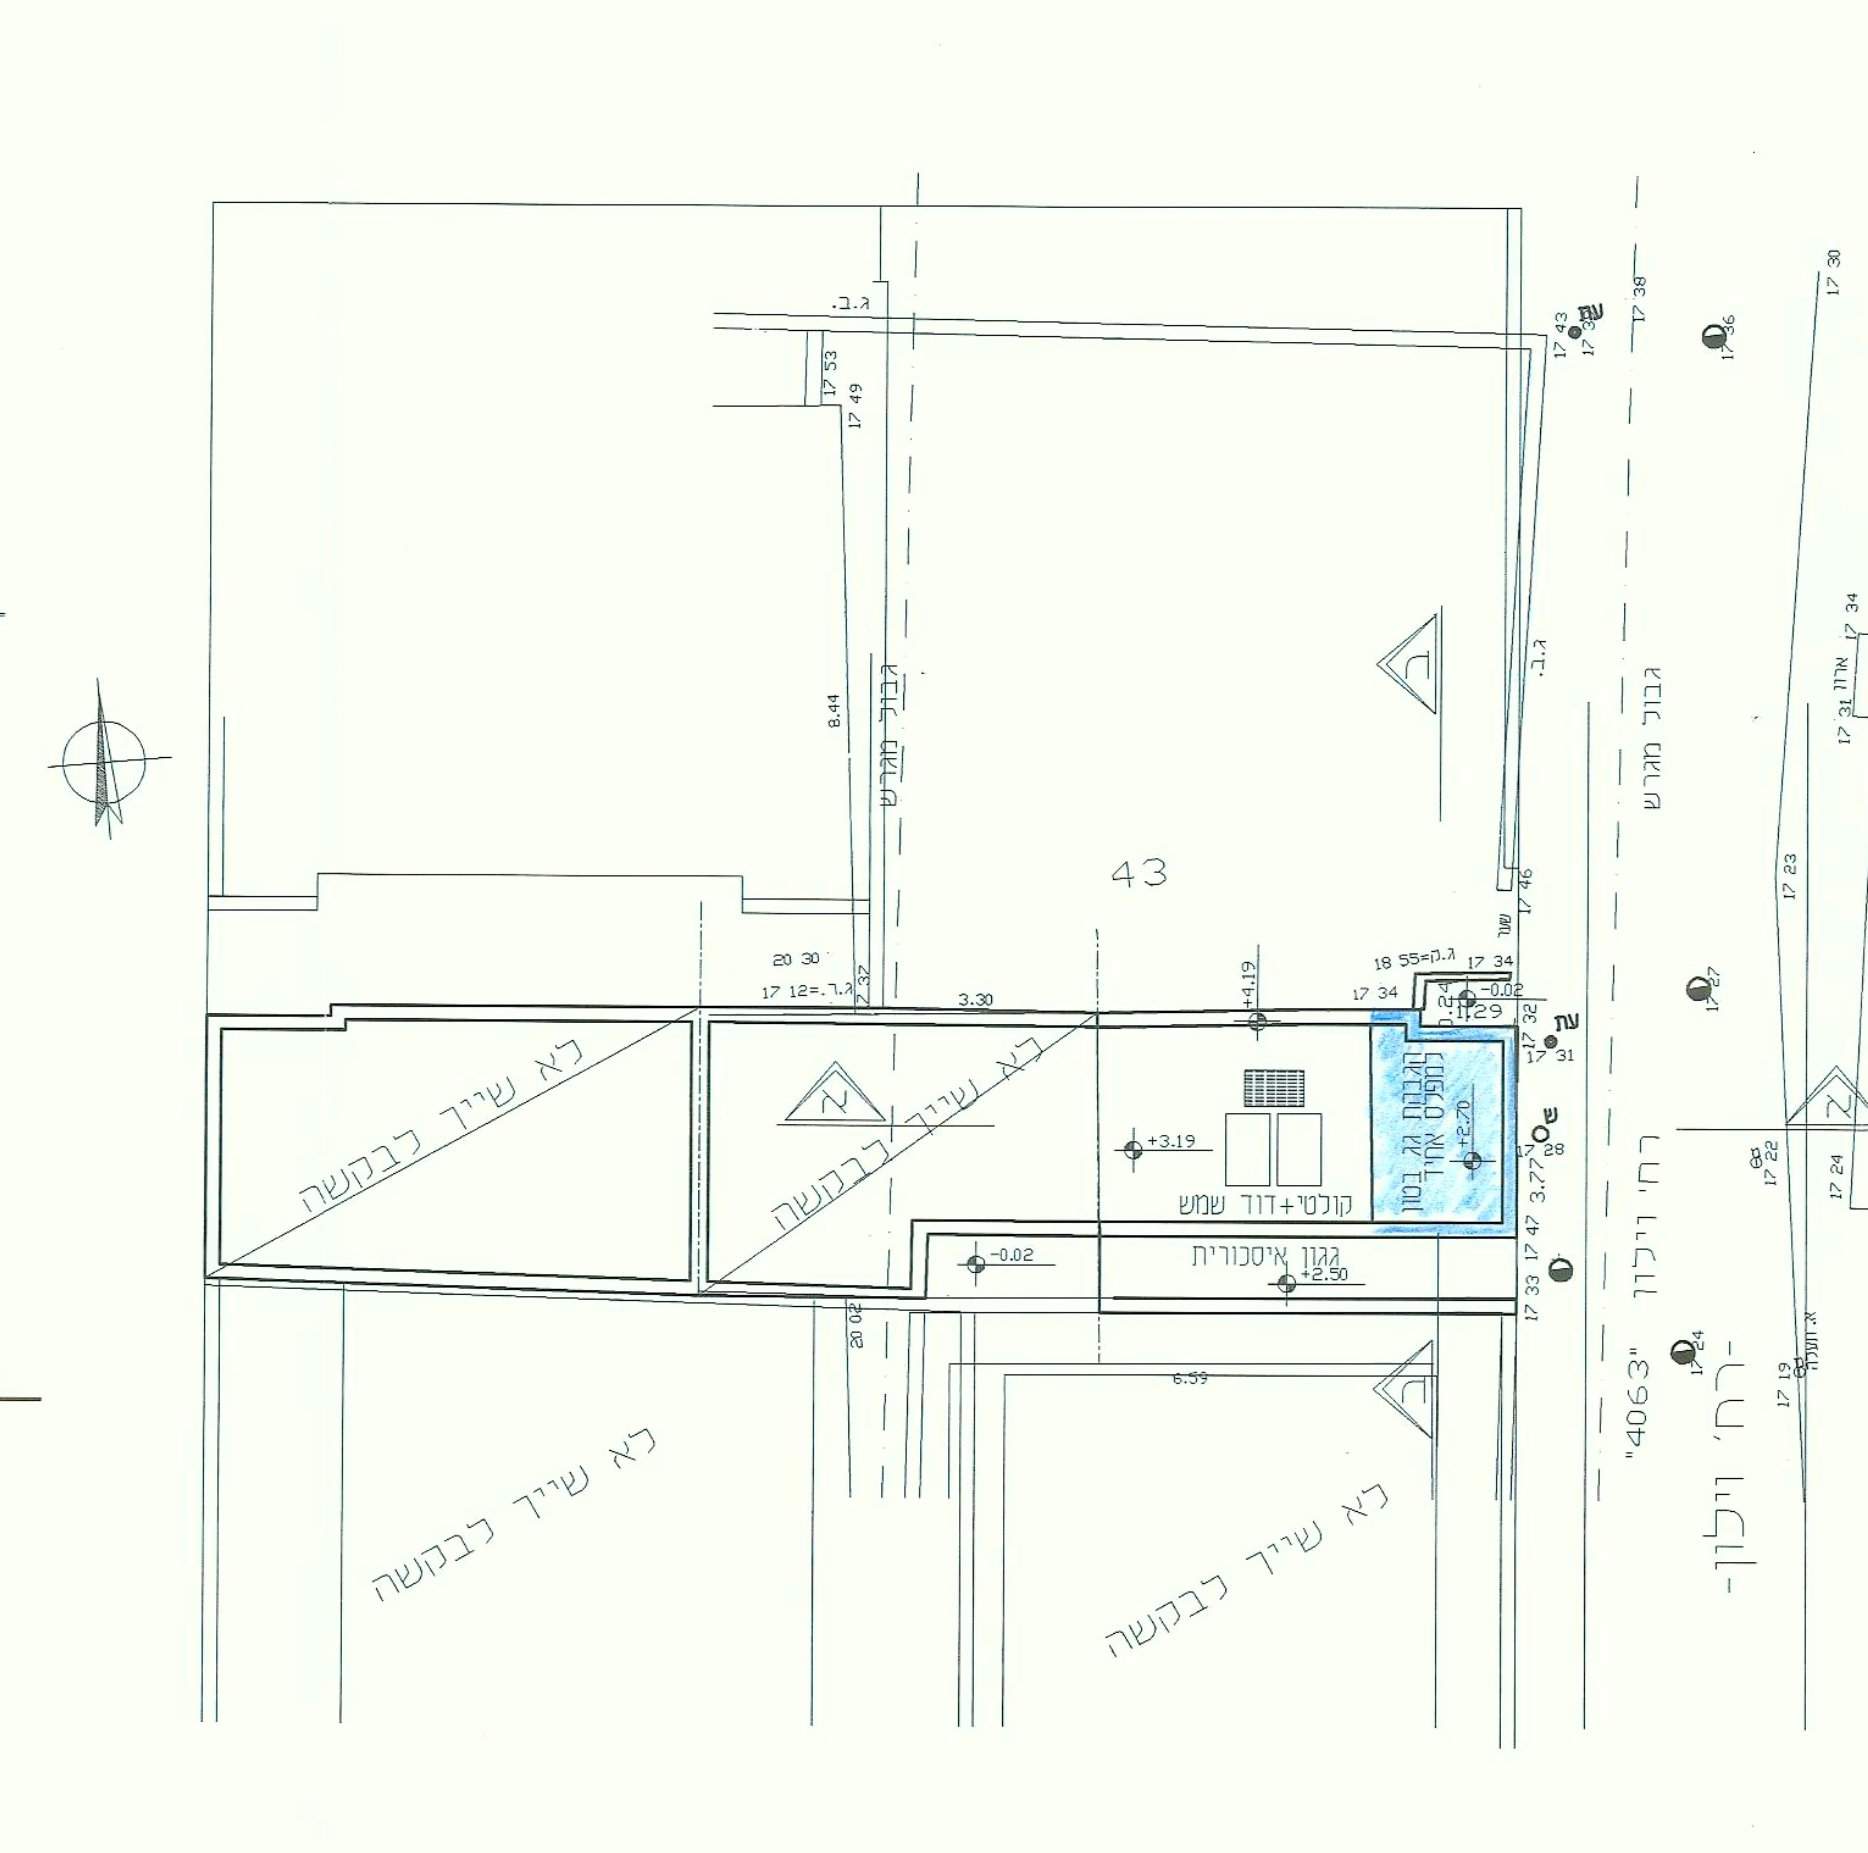
ג.ב.
17.53
17.49
8.44
גבול מגרש
43
20.30
17.12=ג.ג
3.30
+4.19
+3.19
18.55=ג.ג
17.34
הגבהת גג מעקה קיים בטון
קולטי+דוד שמש
גגון אסכורית
-0.02
+2.50
לא שייך בבקשה
רח' וילון
"4063"
30
6.59
גבול מגרש

תכנית הגג ק.מ. 1:100

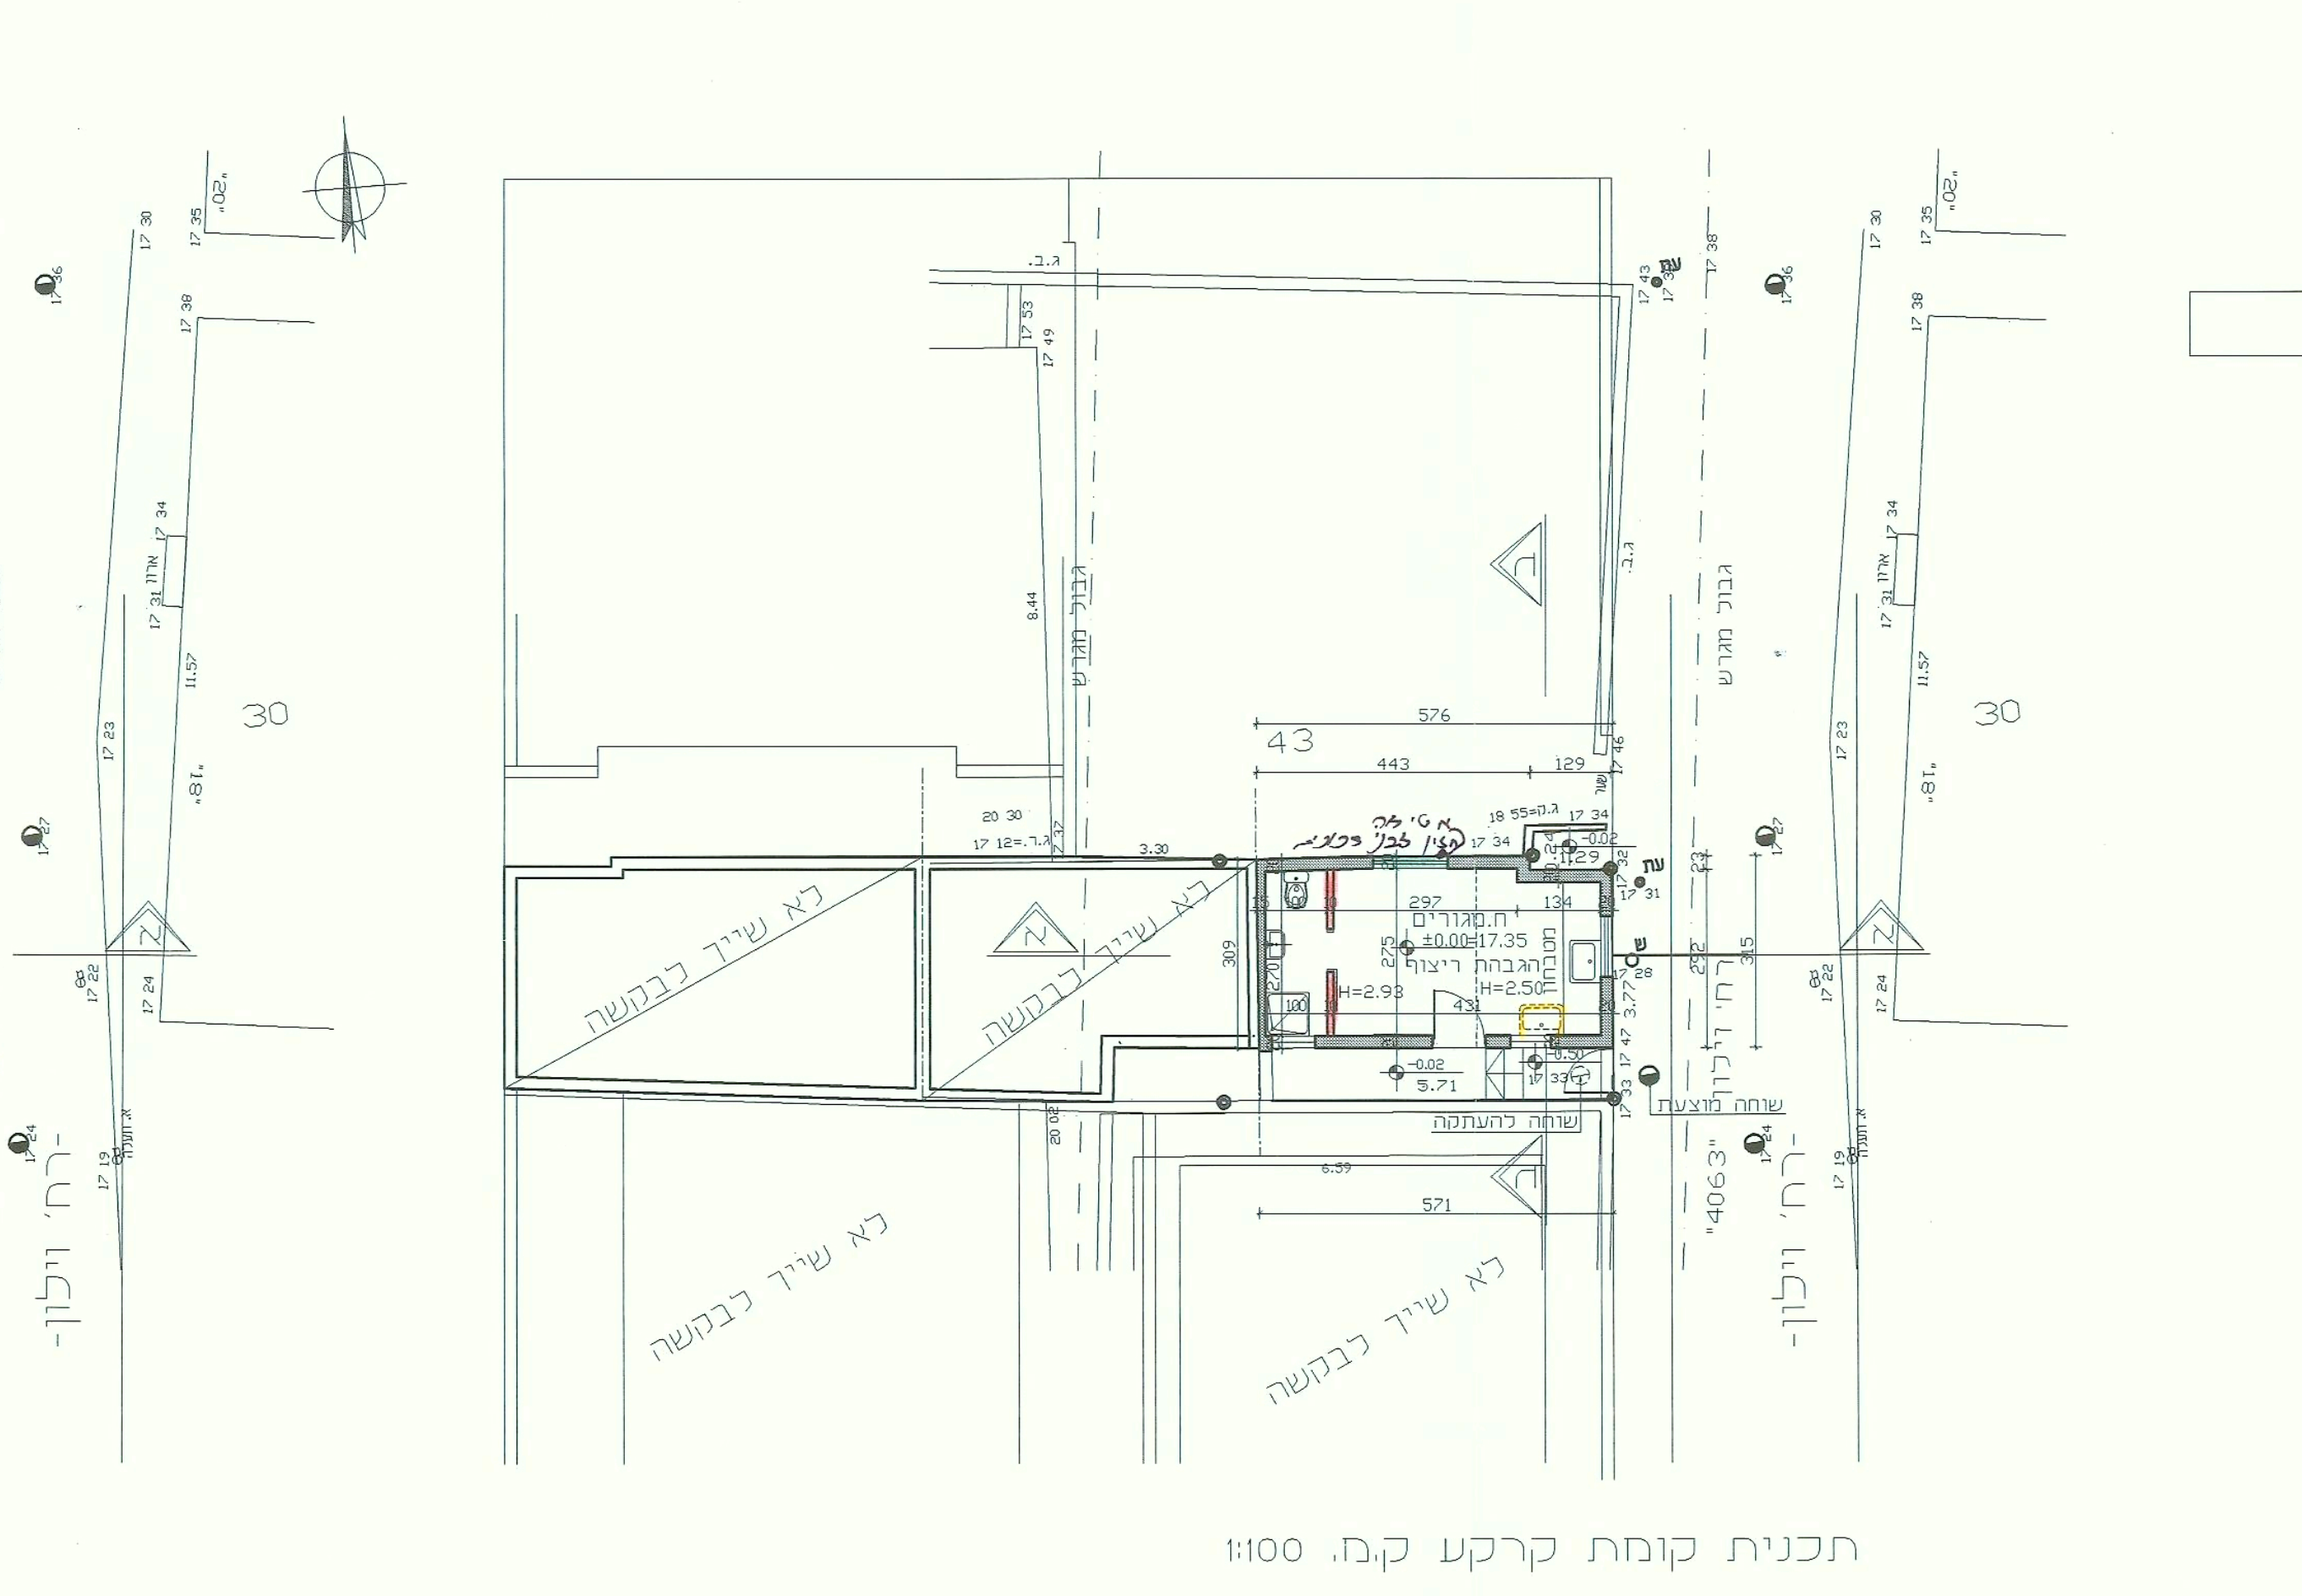
43
576
443
129
ח.מגורים
±0.00=17.35
הגבהת ריצוף
H=2.93
H=2.50
297
134
309
-0.02
5.71
571
שוחה להעתקה
לא שייך בבקשה
-רח' וילון-
"4063"
30
11.57

תכנית קומת קרקע ק.מ. 1:100

חישוב שטחים

קומת קרקע-קיים

סה"כ שטח וקיים: 22.30 מ"ר

TA\TA9C.PRJ

מפה טופוגרפית

קנה מידה 1:100

תל אביב
גוש : 6135
חלקה : 43 (חלק)
כתובת : רח' וילון, 9

מטרת המפה : הגדרת מיגרש משני ע"פ תב"ע 2215
שם הבעלים : בזיליאנסקי שוטה ת.ז. 310546783

שטח לפי נסח : שטח החלקה כולה : 11476מ"ר
בעלות בחלקים(כלפי נסח) 22\11476
בעלות במ"ר: 22
שטח מדוד : 22 מ"ר

שטח מגרש משני:
שטח לגריעה:

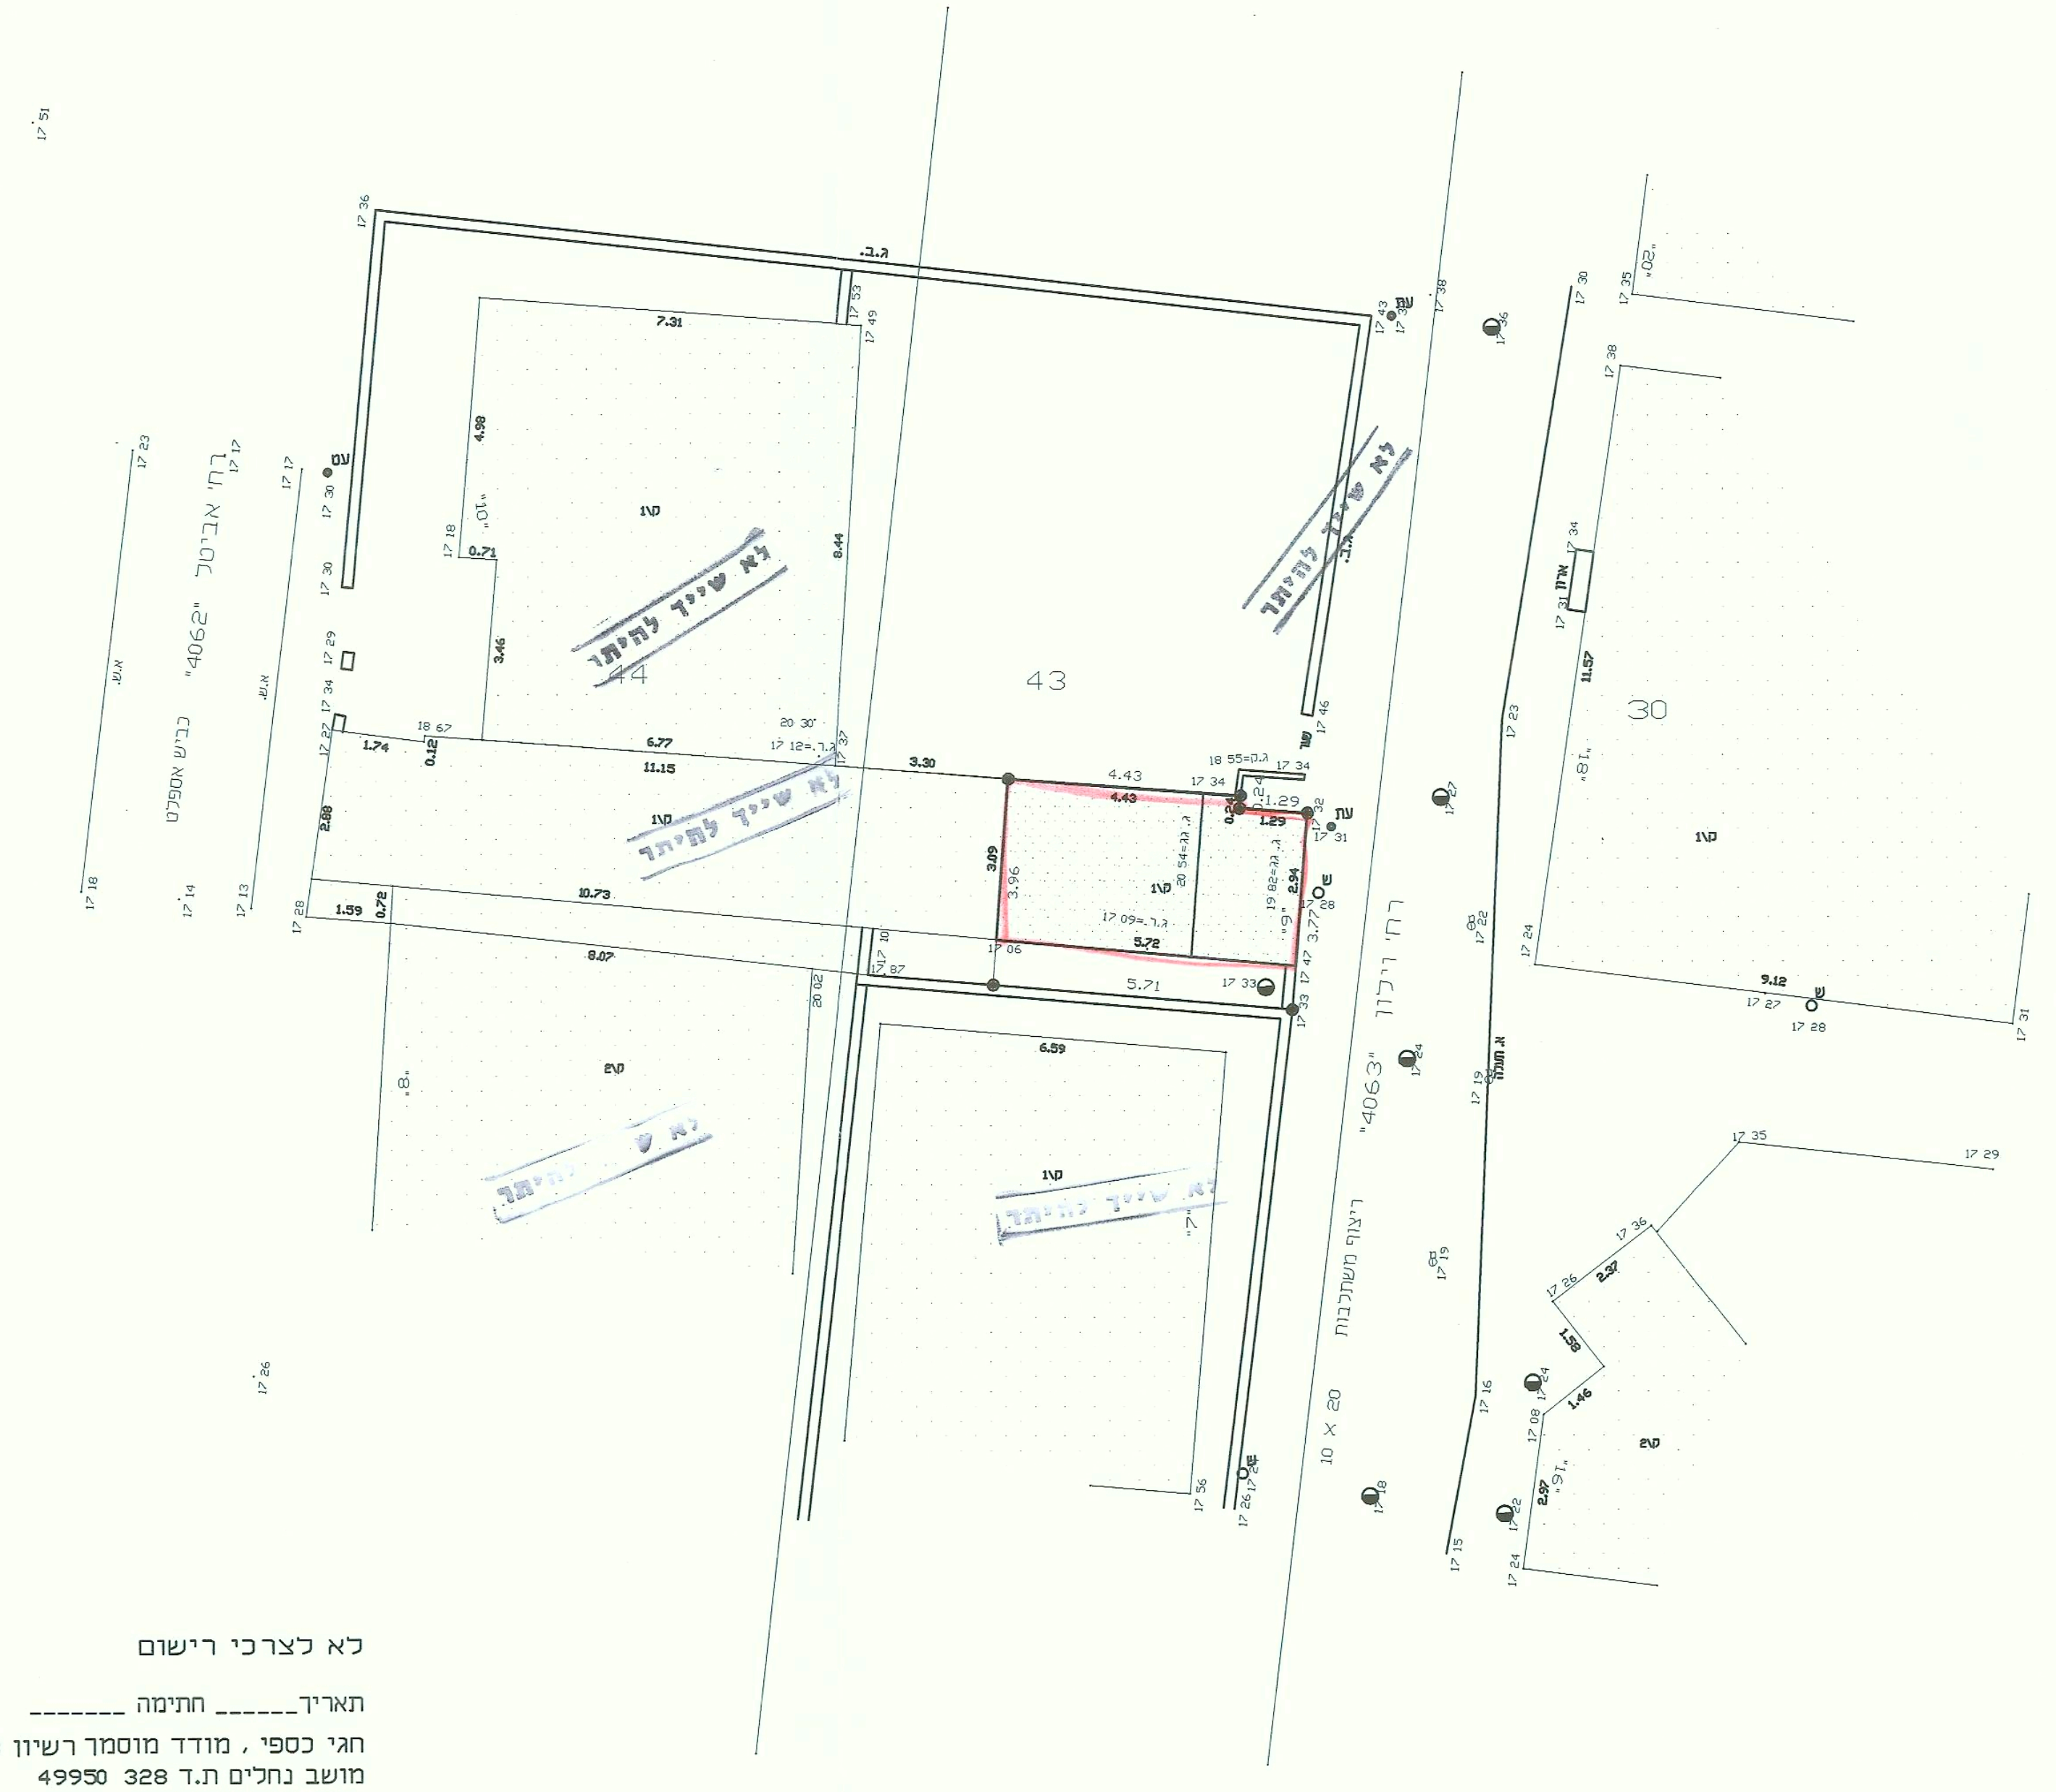
44
43
30
7.31
4.43
3.30
5.71
5.72
6.59
6.77
10.73
11.15
8.07
רח' אביטל
"4062"
כביש אספלט
רח' וילון
"4063"
ריצוף משתלבות
10 X 20
לא שייך להיתר
לא שייך להיתר
לא שייך להיתר
לא שייך להיתר
לא שייך להיתר
161 980
161 970
161 960
161 950
540 130
550 130
560 130
570 130
580 130
590 130
600 130

תרשים סביבה 1:1000

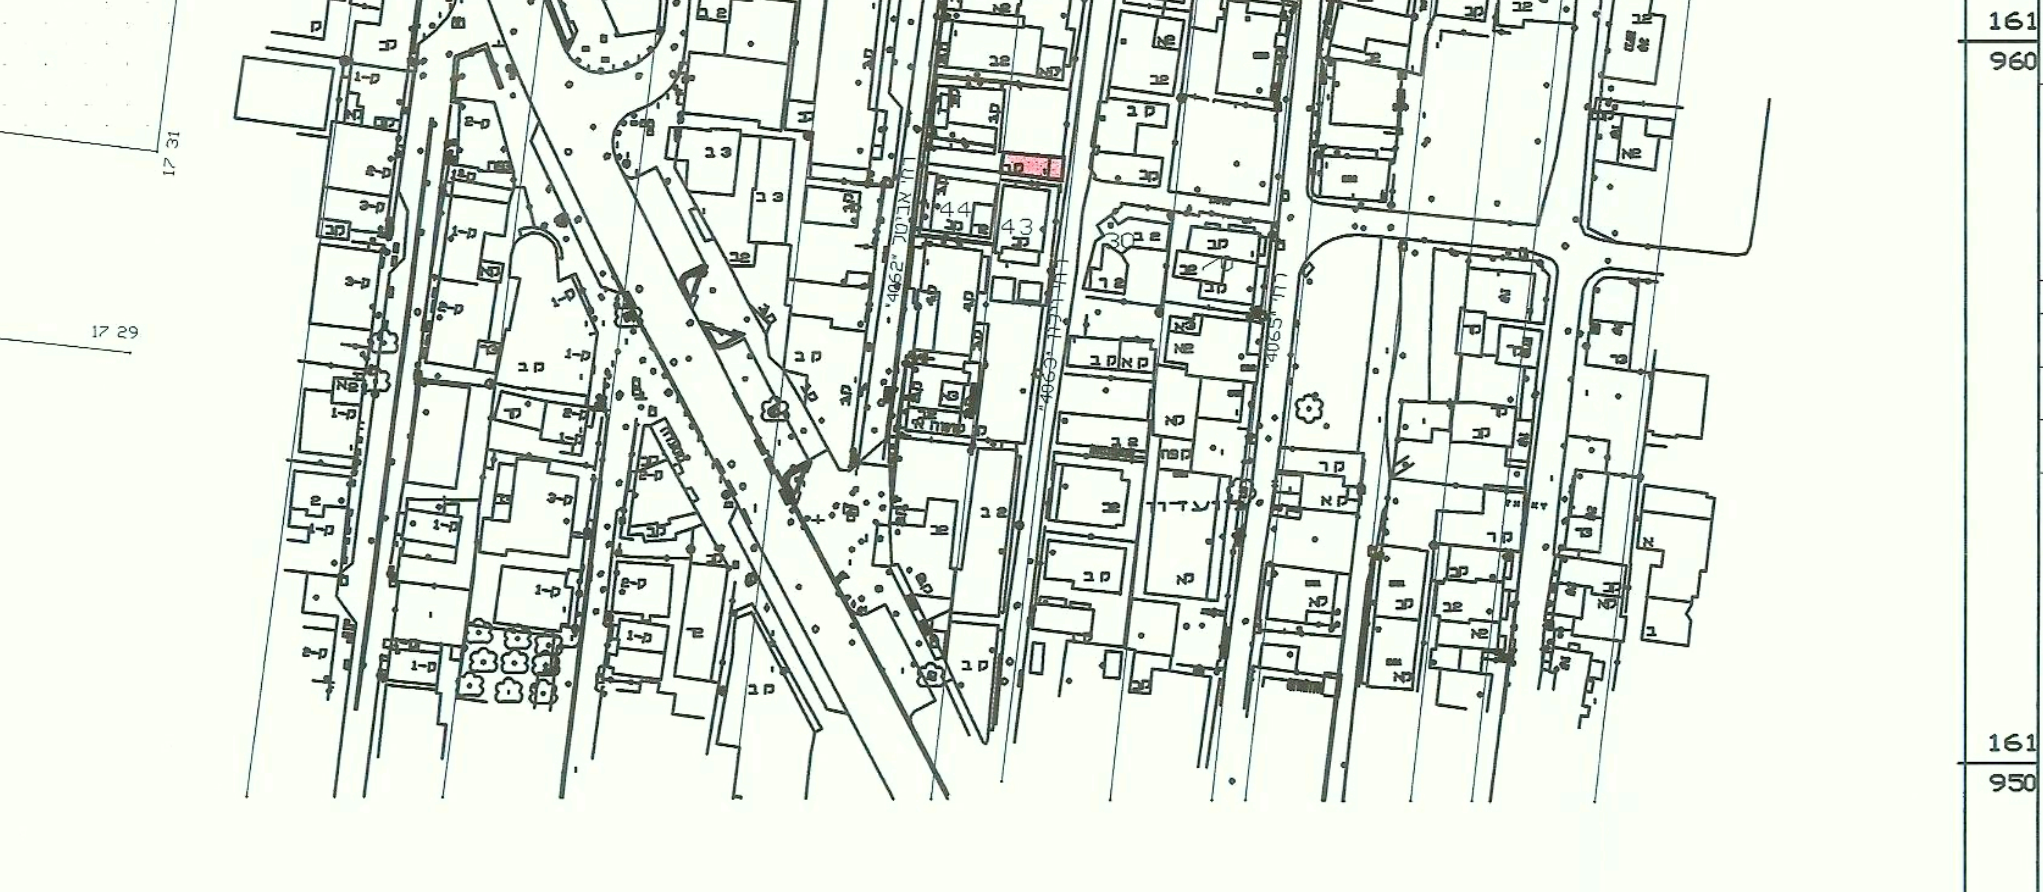

לא לצרכי רישום

תאריך______ חתימה _______
חגי כספי , מודד מוסמך רשיון 623
מושב נחלים ת.ד 328 49950
טל. 03-9326020

7-07-1750

עיריית תל-אביב-יפו
מ"ה רישוי בניה - עזרה מרכז
30 -06- 2009
נתקבל
חתימה

20

תכנית מעודכנת: 03.11.08
תכנית מעודכנת: 17.06.09

עיריית תל-אביב-יפו

מינהל ההנדסה, אגף רישוי ופיקוח על הבנייה
שדרות בן-גוריון 68 תל-אביב 64514 (פקס 5231340) טלפון 5217120, 5217045

חוק התכנון והבנייה, התשכ"ה-1965
תקנות התכנון והבנייה (בקשה להיתר תנאיו ואגרות) התש"ל-1970

בקשה להיתר בנייה או לשימוש במקרקעין

יש להקפיד למלא את כל הפרטים בטופס הבקשה ולצרף מסמכים כמפורט ברשימת התיוג המצורפת.

לכבוד
☐ הוועדה המקומית לתכנון ולבנייה
☒ רשות הרישוי המקומית

מס' תיק הבניין: 647-022
מס' בקשה קודמת להיתר בנייה: 2007-02848

א. פרטי הנכס והמבקשים

הכתובת	רחוב	מס' בית	גוש	חלקה	תת חלקה	מגרש	הוראות התכניות החלות על המקום
	וילון	9	6135	44			

פרטים אישיים	שם משפחה ושם פרטי	מס' זהות/חברה	רחוב ומספר בית / ישוב ומיקוד	מספר טלפון / מספר פקס
מבקש 1	בזיליאנסקי שוטה	310546783	וילון 9, ת"א	052-2456492
מבקש 2				
מבקש 3				
בעל הזכות בנכס	בזיליאנסקי שוטה	310546783	וילון 9, ת"א	052-2456492
החוכר				
עורך הבקשה הראשי	ענת מסורי	023769052	מצדה 4, ת"א	052-2454861 03-5291910
מתכנן שלד הבניין	ד'בגורסקי אלכס	14687859	שד' גורי 34, ת"א	0522544457 5188686

ב. מהות הבקשה

☐ בקשה לתוספת בנייה ☐ בקשה להרחבת דיור (במסגרת הרחבת דיור שכונתית)

☐ תוספת ____ קומות לבניין
הכוללת ☐ ____ יחידות דיור
☐
☐ תוספת בנייה בקומה ____ ☐ לחזית ☐ לאחור ☐ לצד
בשטח של ____ מ"ר
שטח הדירה / המשרד לאחר התוספת יהיה ____ מ"ר
☒ שינויים פנימיים הכוללים: שינויים ללא תוספת שטח
הגבהת מעקה גג בטון להסתרת קולטים, ואיחוד מפלס הרצפה
הנחת גג אסכורית לגג בטון
☒ אישור מצב קיים
☐
המקום משמש כיום כ- מגורים
☒ בהיתר ☐ בלי היתר

ג. מפרט - תיאור הבקשה

תיאור הקיים על המגרש: קיים בניין בן קומה 1
מספר יחידות דיור בבניין: 1

שימוש עיקרי: ☒ מגורים ☐ מלונאות ☐ תעשיה ☐ חקלאי ☐ משרדים ☐ בידור ☐ בנין ציבורי ☐ מלאכה ☐ מסחר ☐ נופש וספורט ☐ שימוש אחר

סוג העבודה והשימושים המבוקשים: ☐ תוספת לבניין ☐ הריסה ☐ שינוי בשימוש ☐ שינוי לבניין ☒ תיקונים ☐ ממטרה / למטרה

הגורם שבעבורו תבוצע הבנייה: ☐ משרד ממשלתי ☐ מוסד ציבורי ☐ בנה ביתך ☐ רשות מקומית ☒ גורם פרטי ☐ אחר

שטחים: שטח המגרש/החלקה 22 מ"ר

ד. חומרי הבנייה

סוג הבנייה: ☒ רגילה ☐ בית מוכן ☐ מתועשת ☐ אחר
קירות חיצוניים: ☒ בטון מזוין ☒ בלוקים ☐ אבן טבעית ☐ טיח ☐ לבנים שרופות ☐ אחר
חומרי גימור: ☐ אבן מלאכותית ☐ זכוכית ☐ אבן טבעית ☒ טיח
תקרות: ☒ בטון מזוין ☐ עץ ☐ אחר
גג: ☒ בטון מזוין ☐ עץ ☐ אסבסט ☐ אחר
גדרות: ☐ אבן טבעית ☒ בלוקים ☐ רשת ☐ אבן מלאכותית ☐ ברזל ☐ אחר ☐ בטון

ה. השטחים המבוקשים לבנייה

לא תוספת שטח

ו. פרטי הבנייה - לשימוש הלשכה המרכזית לסטטיסטיקה

ז. קווי בנייה

ח. מספר יחידות דיור

ט. הבקשה מוגשת לאישור

☐ הוועדה המקומית
הבקשה כוללת בקשה להקלה - כדלהלן:
☐ רשות הרישוי המקומית
☐ רשות הרישוי המקומית באמצעות מורשה להיתר

י. הצהרת עורך הבקשה הראשי

אני מצהיר על נכונות הפרטים בסעיפים א עד ט.
תאריך ______ שם מסורי ענת חתימה X

יא. חתימות נוספות

	שם	חתימה	תאריך
המבקש	בזיליאנסקי שוטה		
בעל הזכות בנכס/בעל הנכס/החוכר	בזיליאנסקי שוטה		
מתכנן שלד הבניין	ד'בגורסקי אלכס		

יב. מינויים מטעם מבקש ההיתר

אני ממנה בזה את מסורי ענת בעל/ת מס' זהות 023769052 הרשום בסעיף א' להיות עורך הבקשה הראשי.

אני ממנה בזה את ד'בגורסקי אלכס בעל/ת מס' זהות 14687859 הרשום בסעיף א' להיות מתכנן שלד הבניין.

יג. הצהרות

	תאריך	שם משפחה ושם פרטי	מספר רישיון	חתימה
עורך בקשה ראשי		מסורי ענת	17824	
עורך בקשה 1				
עורך בקשה 2				

אני החתום מטה ד'בגורסקי אלכס מס' זהות 14687859
מהנדס רשוי מס' 15320

הכנת תכנית: 17.10.2007

מינהל ההנדסה
אגף העתק
חתימה

הוועדה המקומית לתכנון ולבנייה
090587
09 -07- 2009
מהנדס העיר