


איכות ייחודה

בקשה מספר: 2004-003394 רחוב אביב 16 תל אביב 61340

- המספרים בסוגריים מציינים גרים.
- הגבהים המרביים על נק. עירונית מס' 188 שגובהה 17.530 מ'.

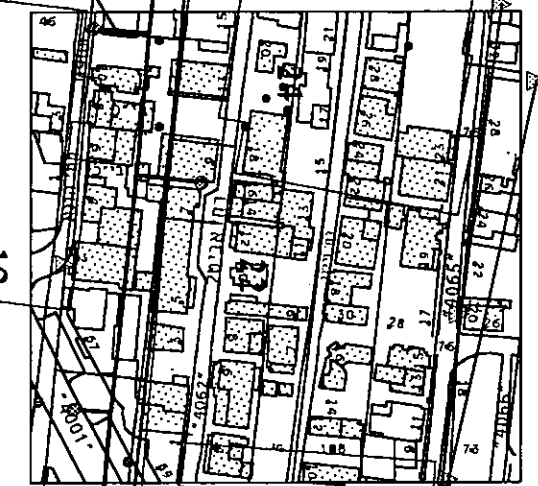

תריסים הסביבה 1250:

שטח מגרש משני
שטח להפקעה: ד.מ.

שטח (דוד) מ"ר: 100
בעלות במ"ר:

שטח העליקה כולה: 11.476 ד.מ.
בעלות בחלקים) כרשום בנסח טאבו) מחוזי דוד
בנגיאט אלברט 113/22952

שטח לפי נסח:


שם הבעלים כרשום בנסח טאבו+מס' ת.ז: מחוזי דוד 87728
בנגיאט אלברט 4179612/9

כתובת: רח' אביטל, 16, 14
הוכן עבור: מחוזי דוד ומנגיאט אלברט
מטרת המדידה: היתר בניה

חלקה: 44 (חלק)

גוש: 6135

תל-אביב 32

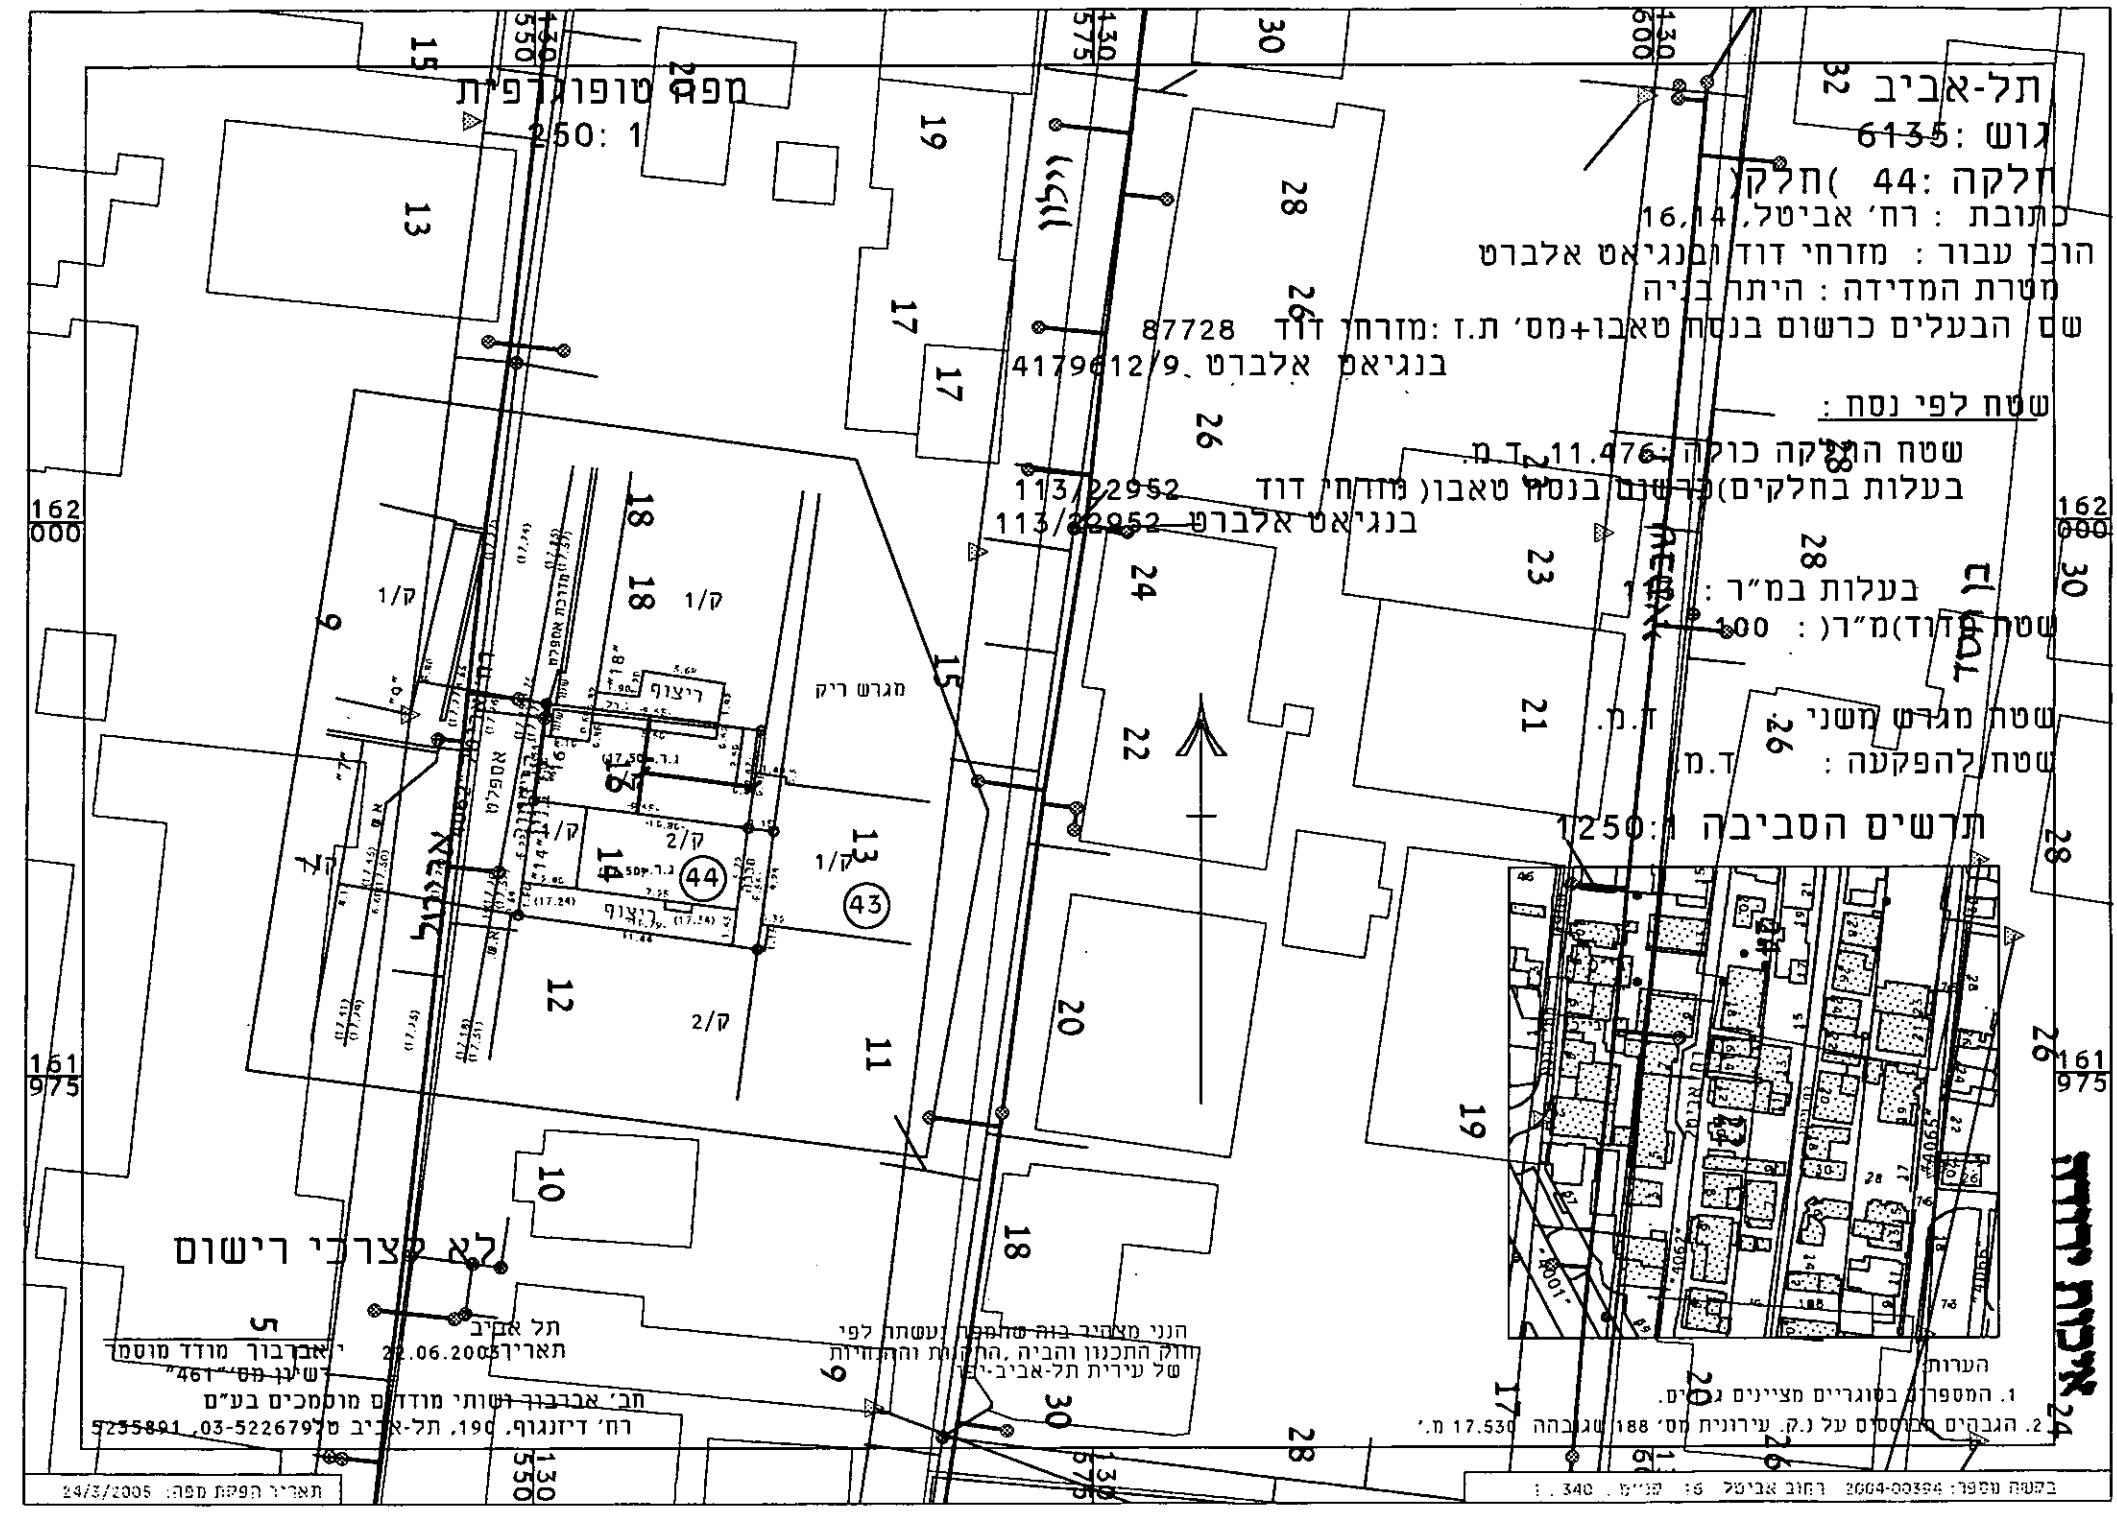

הנני מצהיר בזה שהמפרט נעשה לפי
חוק התכנון והבניה, החוקות וההחלטות
של עיריית תל-אביב-יפו

לא מצרכי רישום

תל אביב
תאריך: 22.06.2005
י. אברבור מודד מוסמך
ש.ג.מ. 461
חב' אברבור ושותי מודדים מוסמכים בע"מ
רח' דיוגוף, 190, תל-אביב טל' 522679, 03-5255891