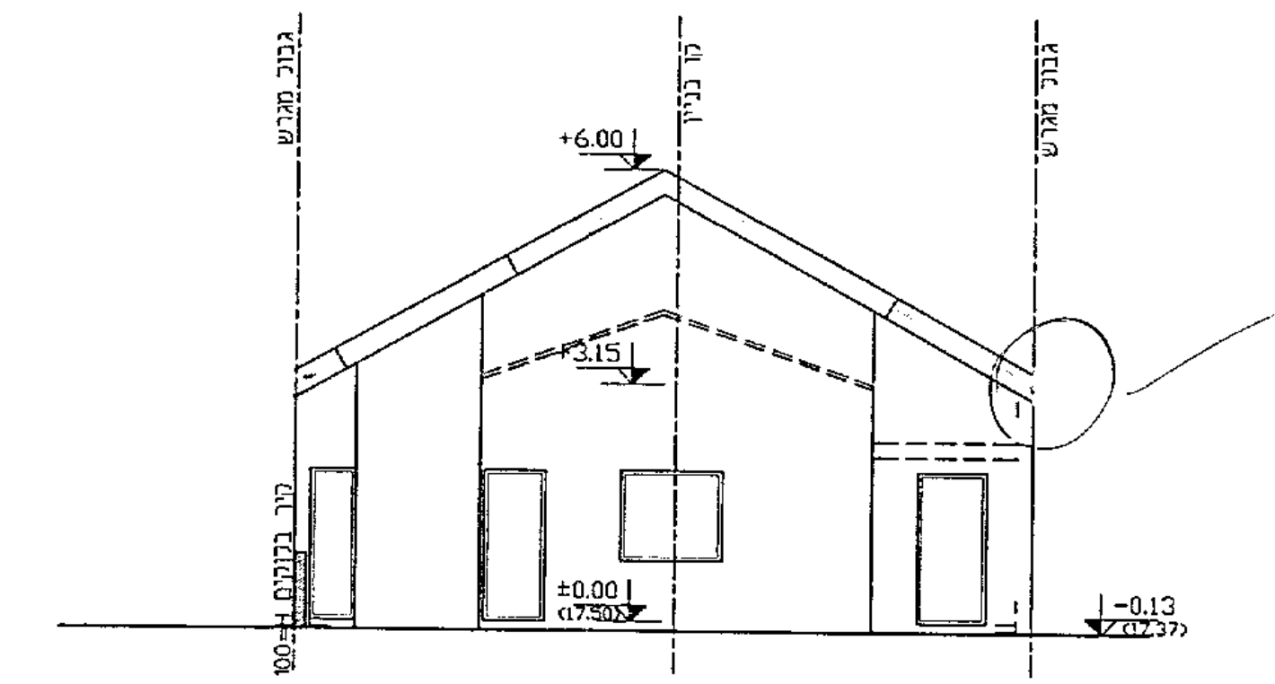
גבול מגרש
קו בניין
+6.00
+3.15
±0.00
(17.50)
-0.13
(17.37)
קיר בלוקים H=100
9

חזית צפונית קנ"מ 1:100

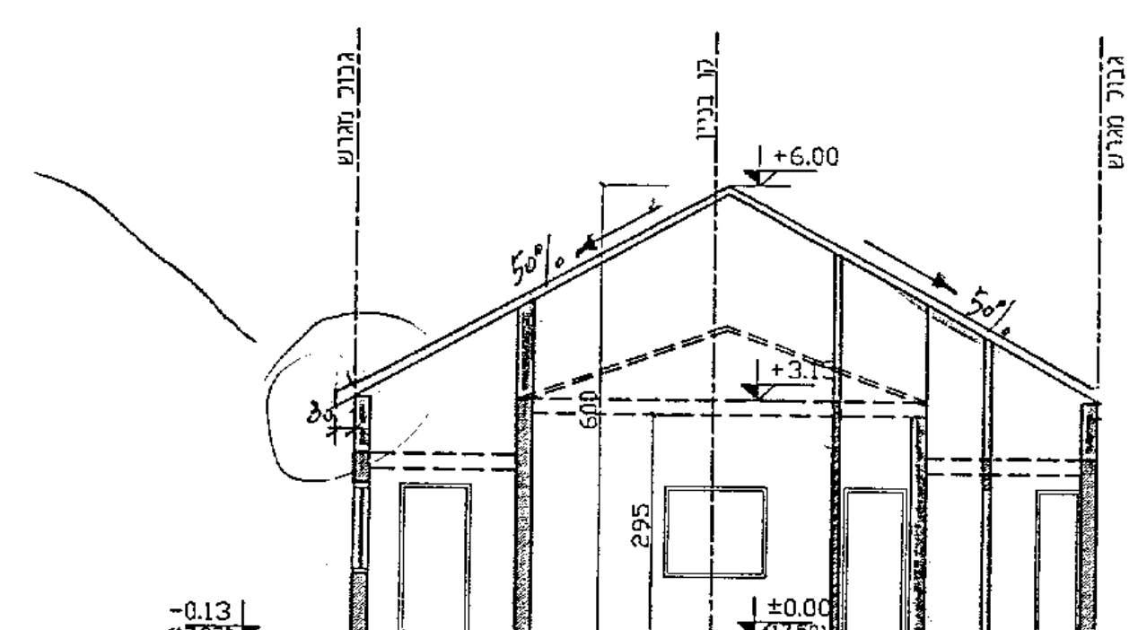
גבול מגרש
קו בניין
+6.00
+3.15
50%
600
295
±0.00
(17.50)
-0.13
(17.37)

חתך א-א קנ"מ 1:100

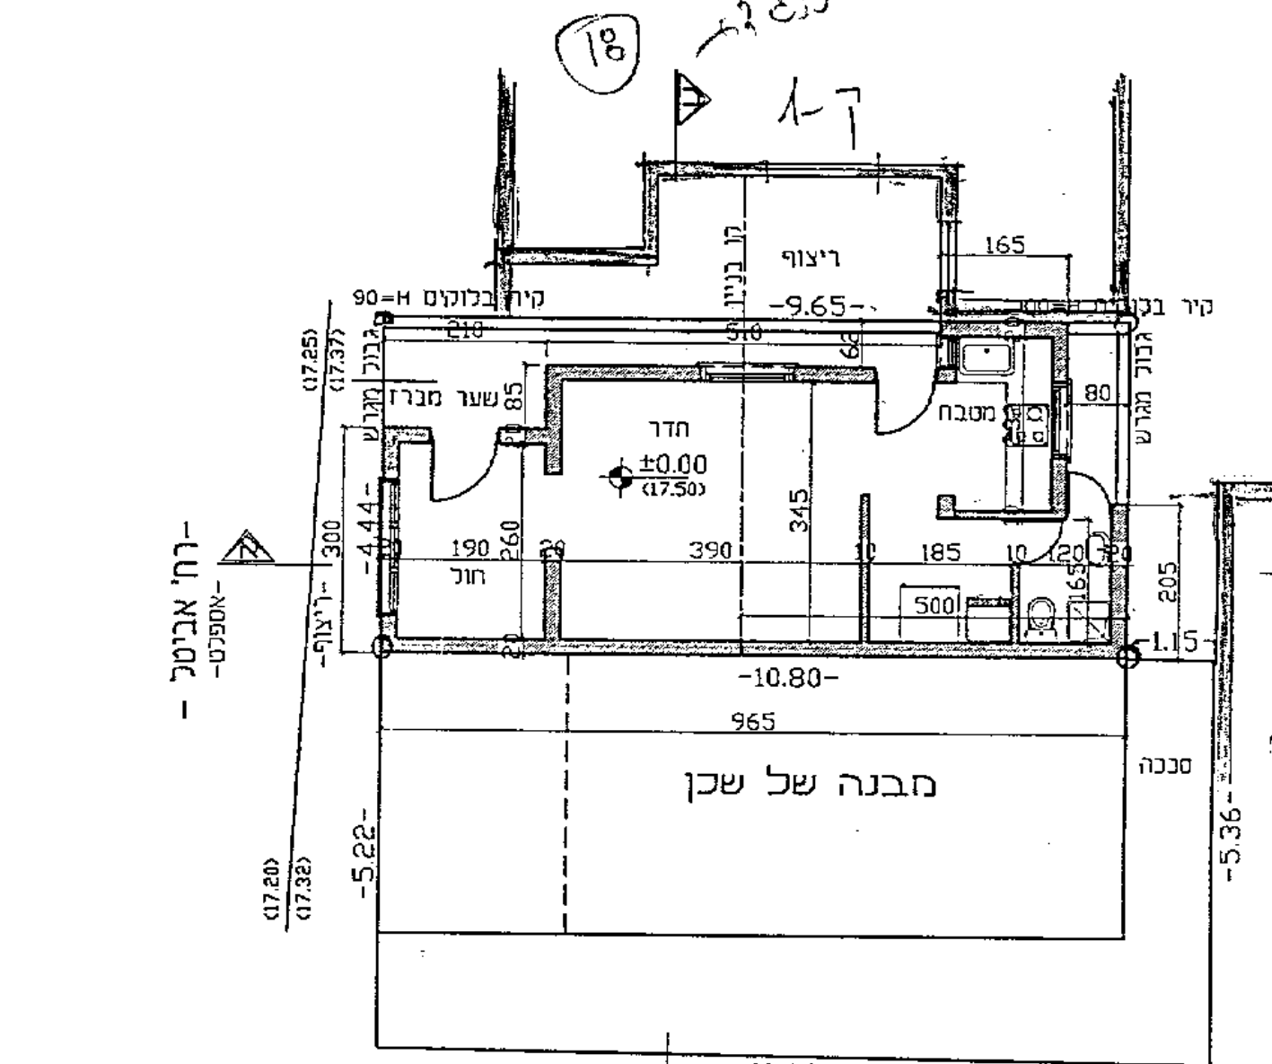
18
ק-1
ריצוף
-9.65-
165
קיר בלוקים H=90
חדר
±0.00
(17.50)
שער מברזל
מטבח
חול
190
390
345
185
500
-10.80-
965
-4.44-
-5.22-
-5.36-
1.15
מבנה של שכן
סככה
רח' אביטל
-אספלט-
-11.44-

תכנית קומת קרקע קנ"מ 1:100

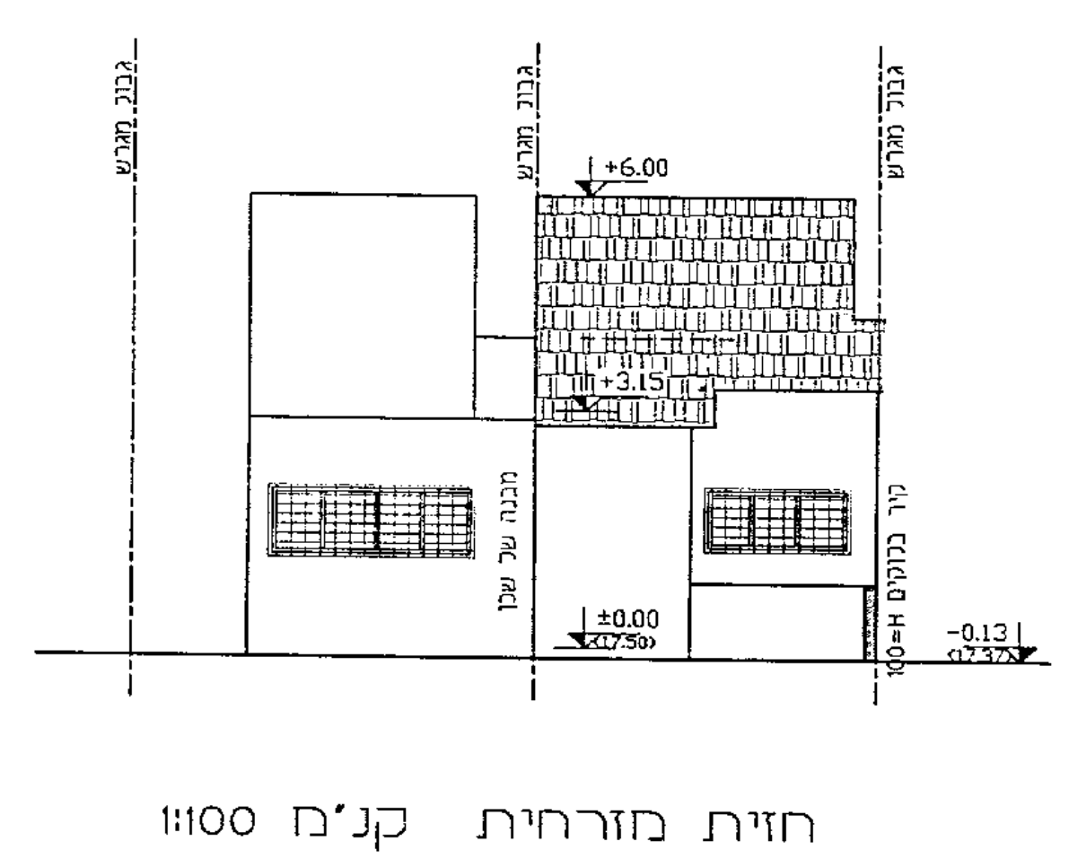
גבול מגרש
+6.00
+3.15
±0.00
(17.50)
-0.13
(17.37)
מבנה של שכן
קיר בלוקים H=100

חזית מזרחית קנ"מ 1:100

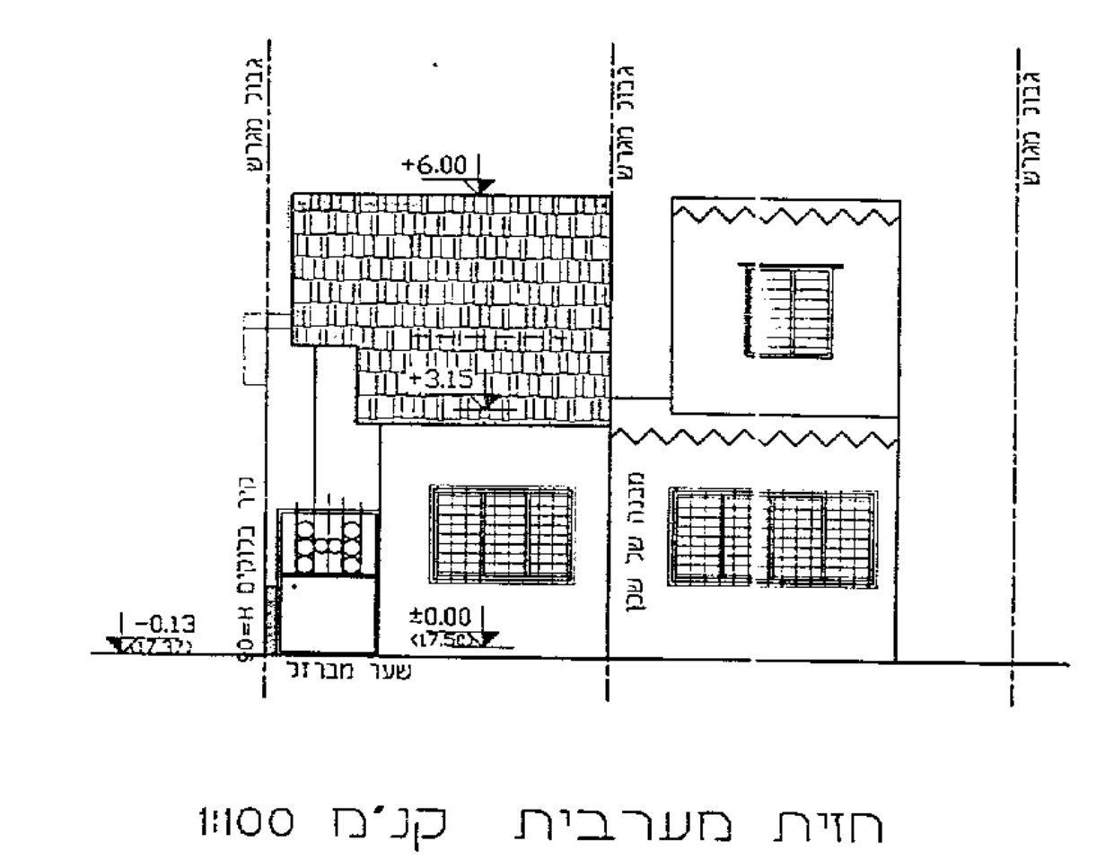
גבול מגרש
+6.00
+3.15
±0.00
(17.50)
-0.13
(17.37)
קיר בלוקים H=90
שער מברזל
מבנה של שכן

חזית מערבית קנ"מ 1:100

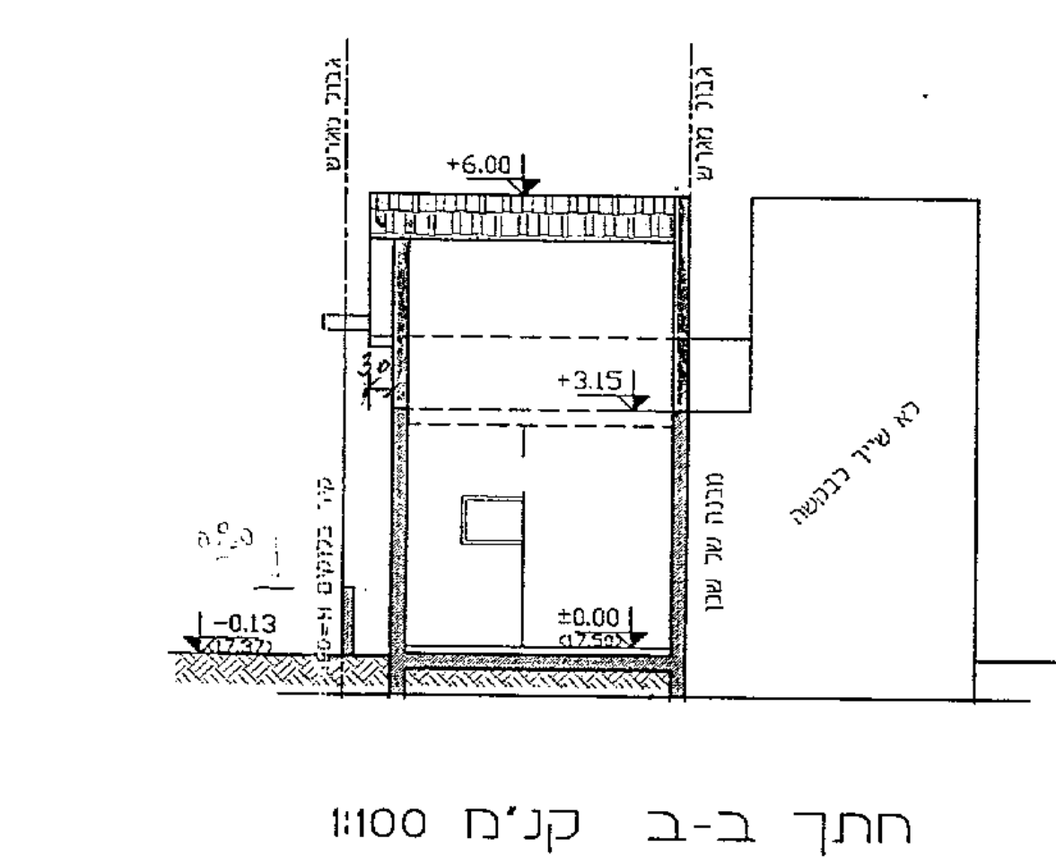
גבול מגרש
קו בניין
+6.00
+3.15
±0.00
(17.50)
-0.13
(17.37)
קיר בלוקים
מבנה של שכן
לא שייך לבקשה

חתך ב-ב קנ"מ 1:100

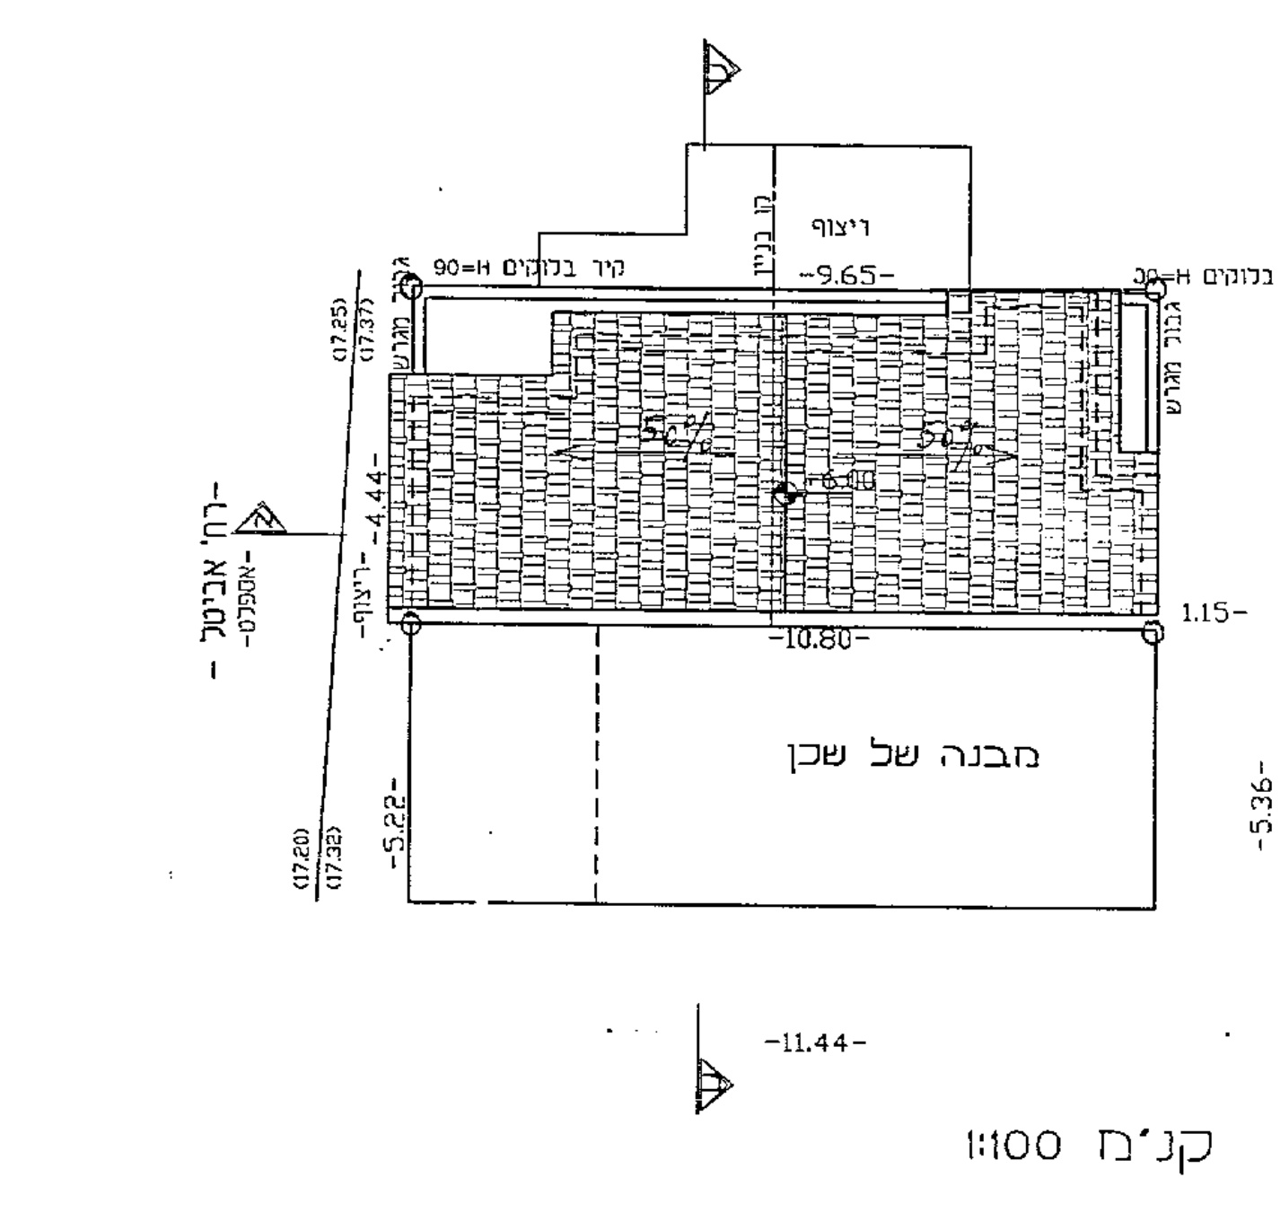
ריצוף
קו בניין
-9.65-
קיר בלוקים H=90
50%
+6.00
-4.44-
1.15
-10.80-
מבנה של שכן
-5.22-
-5.36-
רח' אביטל
-אספלט-
-11.44-

תכנית גג קנ"מ 1:100

חישוב שטחים

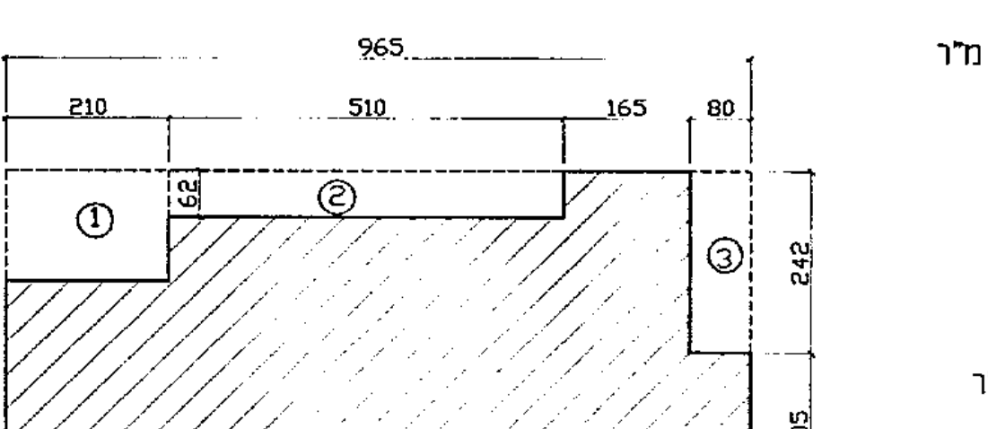
965
210
510
165
80
147
300
447
62
242
205
①
②
③

המסגרת: 43.13=4.47•9.65 מ"ר

ההורדות:
1) 3.09=1.47•2.10 מ"ר
2) 3.16=0.62•5.10 מ"ר
3) 1.94=2.42•0.80 מ"ר
סה"כ ההורדות: 8.19 מ"ר
סה"כ שטח דירה: 34.94 מ"ר

- סימון גבולות המגרש
- צבע
- שיפוע
- סימון הבלוק של הגג

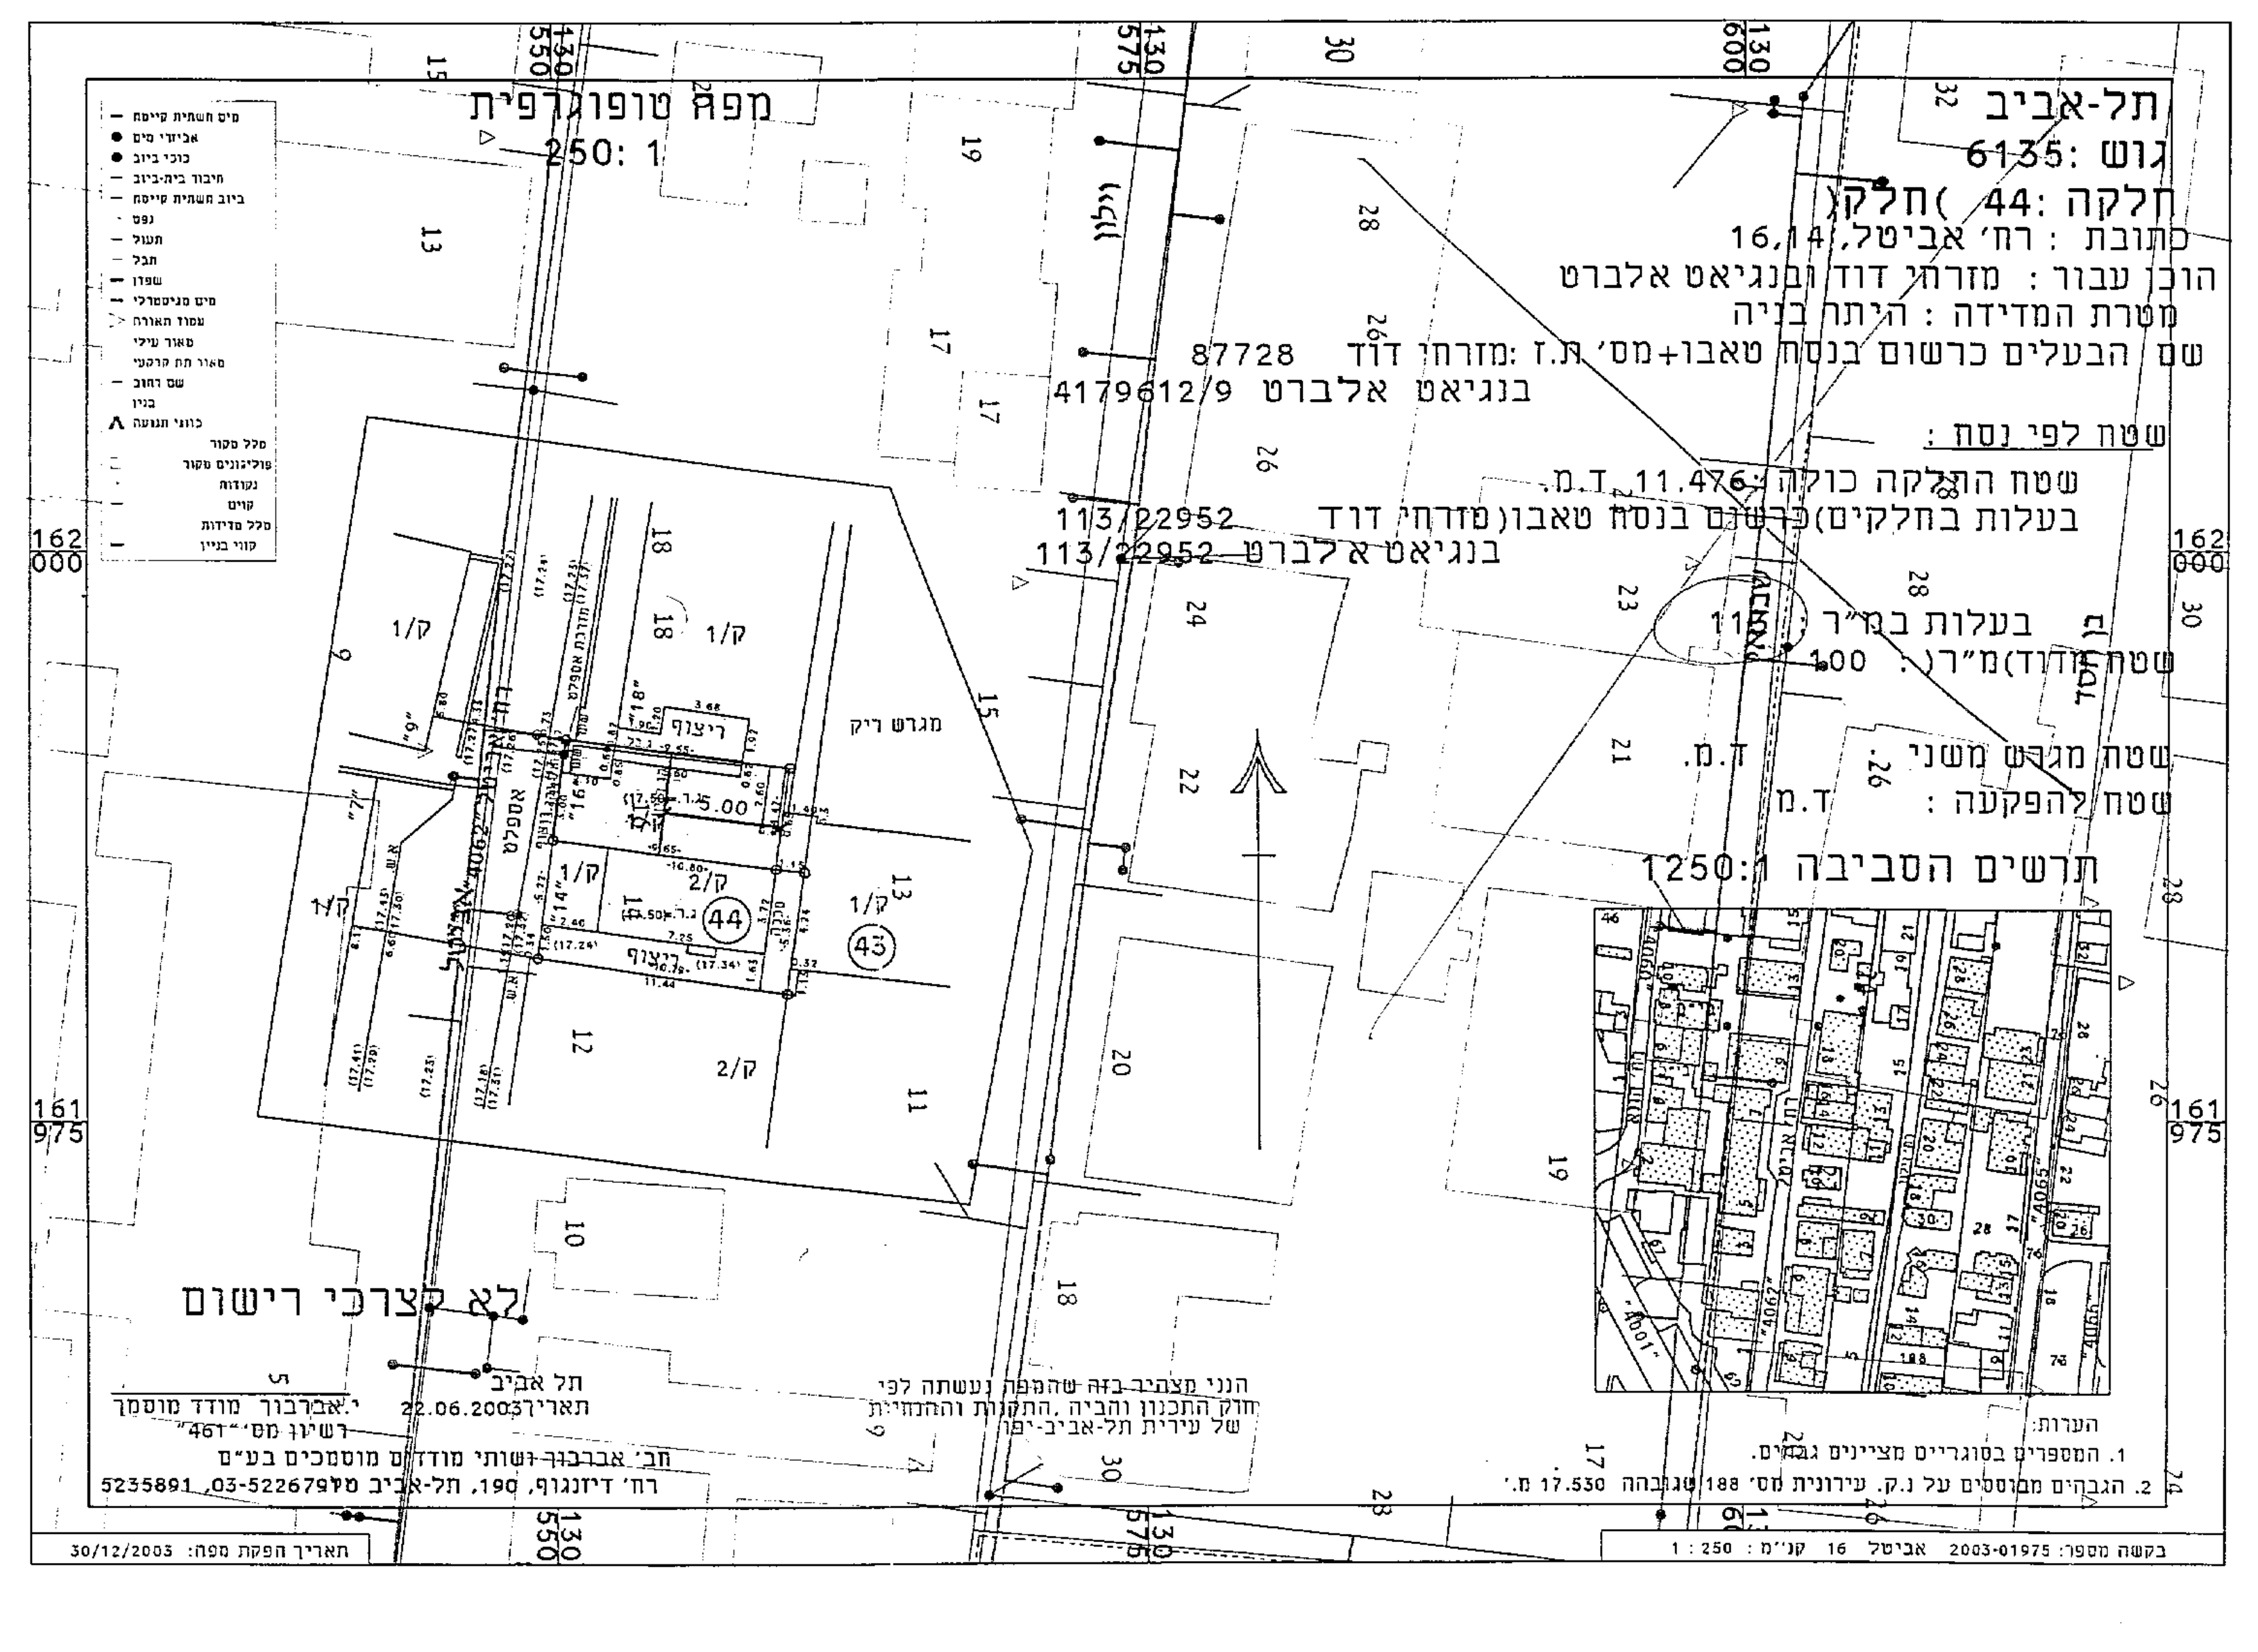
מפה טופוגרפית
1:250
1/ק
2/ק
ריצוף
מגרש ריק
44
43
12
13
18
24
22
20
26
28
17
19
10
11
30
162 000
161 975
130 550
130 575
130 600

תל-אביב
גוש: 6135
חלקה: 44 חלק
כתובת: רח' אביטל 16,14
הוכן עבור: מזרחי דוד ובנגיאט אלברט
מטרת המדידה: היתר בניה
שם הבעלים כרשום בנסח טאבו+מס' ת.ז: מזרחי דוד 87728
בנגיאט אלברט 4179612/9

שטח לפי נסח:
שטח החלקה כולה: 11.476 ד.מ.
בעלות בחלקים(כרשום בנסח טאבו): מזרחי דוד 113/22952
בנגיאט אלברט 113/22952
בעלות במ"ר: 113
שטח(מדוד)מ"ר: 100
שטח מגרש משני: ד.מ.
שטח להפקעה: ד.מ.

תרשים הסביבה 1:1250

לא לצרכי רישום

תל אביב
תאריך: 22.06.2003
י. אברבוך מודד מוסמך
רשיון מס' "461"
חב' אברבוך ושות' מודדים מוסמכים בע"מ
רח' דיזנגוף 190, תל-אביב טל. 03-5226799, 5235891

הנני מצהיר בזה שהמפה נעשתה לפי חוק התכנון והבניה, התקנות וההנחיות של עיריית תל-אביב-יפו

הערות:
1. המספרים בסוגריים מציינים גבהים.
2. הגבהים מבוססים על נ.ק. עירונית מס' 188 שגובהה 17.530 מ'.

תאריך הפקת מפה: 30/12/2003 | בקשה מספר: 2003-01975 אביטל 16 קנ"מ: 1 : 250

ד"מ מפה מתוזנת
אין קו

הגשה 21

עיריית תל-אביב-יפו
מינהל ההנדסה, אגף רישוי ופיקוח על הבנייה
שדרות בן-גוריון 68 תל-אביב 64514 (פקס 5231340) טלפון 5217120, 5217045

חוק התכנון והבניה, התשכ"ה-1965
תקנות התכנון והבניה (בקשה להיתר תנאיו ואגרות) התש"ל-1970
בקשה להיתר בנייה או לשימוש במקרקעין
יש להקפיד למלא את כל הפרטים בטופס הבקשה ולצרף מסמכים כמפורט ברשימת התיוג המצורפת.

על פי טופס 1 תקנה 2(א)

מס' תיק הבניין	מס' בקשה קודמת להיתר בנייה	מס' הבקשה למידע	מתאריך
4062-016		N2003-1975	01/01/04

לכבוד
☒ הוועדה המקומית לתכנון ולבנייה
☐ רשות הרישוי המקומית

2005-0925

א. פרטי הנכס והמבקשים

הכתובת	רחוב	מס' בית	גוש	חלקה	תת חלקה	מגרש	הוראות התכניות החלות על המקום
	אביטל	16	6135	44			ג 2215

פרטים אישיים	שם משפחה / שם פרטי	מס' זהות/חברה או מס' רישום תאגיד	רחוב ומספר בית ישוב ומיקוד	מספר טלפון / מספר פקס
מבקש 1	מזרחי דוד	87728	אביטל 16 ת"א	
מבקש 2				
מבקש 3				
בעל הזכות בנכס	מזרחי דוד	87728	אביטל 16 ת"א	
החוכר				
עורך הבקשה הראשי	ז'בגורסקי אלכס	14687859	רח' רוטשילד 12 בת-ים	9510030 6837771
מתכנן שלד הבניין	ז'בגורסקי אלכס	14687859	רח' רוטשילד 12 בת-ים	052-544457

ב. מהות הבקשה
☒ בקשה לתוספת בנייה ☒ בקשה להרחבת דיור (במסגרת הרחבת דיור שכונתית)
☐ תוספת ____ קומות לבניין
הכוללות: ☐ ____ יחידות דיור
☐ תוספת בנייה בקומה ____ ☐ לחזית ☐ לאחור ☐ לצד
בשטח של ____ מ"ר
שטח הדירה / המשרד לאחר התוספות יהיה ____ מ"ר
☐ שינויים פנימיים הכוללים: החלפת הגג הקיים מרעפים לרעפים+הגבהת הגג הקיים
☐ אישור מצב קיים
המקום משמש כיום ל- מגורים
☒ בהיתר ☐ בלי היתר

ג. מפרט - תיאור הבקשה
תיאור הקיים על המגרש: קיים בניין בן 1 קומות
1 יח דיור
שימוש עיקרי: ☒ מגורים ☐ משרדים ☐ מסחר ☐ מלונאות ☐ בידור ☐ נופש וספורט ☐ תעשיה ☐ בנין ציבורי ☐ שימוש אחר ☐ חקלאי ☐ מלאכה
סוג העבודה או השימושים המוצעים: ☐ תוספת לבניין ☐ שינוי לבניין ☐ הריסה ☐ תיקונים ☐ שינוי בשימוש ממטרה ____ למטרה ____
הגורם שמבוצעת בעבורו הבנייה: ☐ משרד ממשלתי ☐ רשות מקומית ☐ מוסד ציבורי ☒ גורם פרטי ☐ בנה ביתך ☐ אחר
שטחים: שטח המגרש/החלקה ~~56.50~~ 43 מ"ר | שטח הבנייה הכולל המבוקש 34.94 מ"ר | אחוזי הבנייה 61.81
אם במסגרת הרחבת דיור שכונתית: מספר יחידות דיור מורחבות 1 | מספר תכנית ההרחבה ג 2215

ד. חומרי הבנייה
סוג הבנייה: ☒ רגילה ☐ בית מוכן ☐ מתועשת ☐ אחר
קירות חיצוניים: ☐ בטון מזוין ☒ בלוקים ☐ אבן טבעית ☐ לבנים שרופות ☐ אחר
חומרי גימור: ☐ אבן מלאכותית ☐ אבן טבעית ☒ טיח ☐ זכוכית ☐ אחר
תקרות: ☒ בטון מזוין ☐ עץ ☐ אחר
גג: ☐ בטון מזוין ☒ רעפים ☐ אסבסט ☐ טיח ☐ אחר
גדרות: ☐ אבן טבעית ☐ אבן מלאכותית ☐ בטון ☐ בלוקים ☐ ברזל ☐ עץ ☐ רשת ☐ אחר
קיימות ____ מ"א מוצעות ____ מ"א סה"כ ____ מ"א

ה. השטחים המבוקשים לבנייה (על-פי תכנית הבנייה) והמותרים לבנייה (על-פי "אסמכתא": חוק, תקנות, תכניות) בכל מפלס בנפרד ולפי שימוש

הקומה/המפלס בבניין	קיים בהיתר	(1) מגורים: מ"ר	ה"אסמכתא" לשטחים המותרים	סך כל שטחי הבנייה העיקריים: מ"ר	%משטח המגרש	סך כל השטחים המותרים	(ג) סך כל שטחי הבנייה: מ"ר	%משטח המגרש	סך כל השטחים המותרים
ק.קרקע	0.00	34.94	ג 2215	34.94	61.84	33.90	34.94	61.81	33.90
סה"כ מעל לקרקע		34.94		34.94	61.8	33.90	34.94	61.81	33.90
סה"כ מתחת לקרקע									
סה"כ		34.94		34.94	61.8	33.90	34.94	61.81	33.90

ז. קווי בנייה

הכיוון		מוצע	מותר
לרחוב (שם)	אביטל	0.00	0.00
לרחוב (שם)			
לצד		0.00	0.00
לאחור		0.80	5.00

ט. הבקשה מוגשת לאישור
☐ הוועדה המקומית
☐ רשות הרישוי המקומית
☐ רשות הרישוי המקומית באמצעות מורשה להיתר

י. הצהרת עורך הבקשה הראשי
אני מצהיר על נכונות הפרטים בסעיפים א עד ס.
תאריך 12/12/04 שם ז'בגורסקי א. חתימה X

יא. חתימות נוספות

	שם	תאריך
המבקש	מזרחי דוד	12/12/04
בעל הזכות בנכס	מזרחי דוד	12/12/04
מתכנן שלד הבניין	ז'בגורסקי	12/12/04

כן ☒
הערות: טרם קני
תאריך 11.1.05

יב. מינויים מטעם מבקש ההיתר
אני ממנה בזה את ז'בגורסקי אלכס בעל/ת מס' זהות 14687859 הרשום בסעיף א' להיות עורך הבקשה הראשי להיתר, ולייצגני לפני מוסדות התכנון והרשויות המוסמכות בכל הנוגע לטיפול בבקשה להיתר ולקבלתו, לרבות התיקונים ככל שידרשו הרשויות המוסמכות.

שם משפחה ושם פרטי	תחום פעולה	המען	מספר טלפון	מספר פקס
1.	מתכנן האינסטלציה הסניטרית			
2.				

אני ממנה בזה את ז'בגורסקי אלכס בעל/ת מס' זהות 14687859 הרשום בסעיף א' להיות אחראי לתכנון שלד הבניין שבעבורו מבוקש ההיתר, להגיש לוועדה המקומית לרשות הרישוי המקומית את החישובים לגבי הבניה שבעבורה מבוקש היתר ולפקח פיקוח עליון על הקמת השלד.

שם משפחה ושם פרטי	תחום פעולה	המען	מספר טלפון	מספר פקס
1.	אחראי ראשי			
2.				
3.				

חתימת המבקש על המינויים X

יג. הצהרות

	שם משפחה ושם פרטי	מספר רישיון	תאריך
עורך בקשה ראשי	ז'בגורסקי אלכס	15320	
עורך בקשה 1 מתכ' האינס הסניט'			
עורך בקשה 2			

אני החתום מטה ז'בגורסקי אלכס מס' זהות 14687859 מהנדס רשוי מס' 15320

ז'בגורסקי אלכס מהנדס בניין מס' 15320

ח. פרטי הבנייה - לשימוש הלשכה המרכזית לסטטיסטיקה
ח. מספר יחידות דיור

מסמך
נכתב