

תל-אביב  
גוש 6135

חלקה: (חלק) 44

כתובת: רח' אביטל 17

הוכן עבור: הבעלים

מהות הבקשה: היתר בניה

שם הבעלים כרשום בנסח טאבומס+ ת.ז.:

שטח לפי נסח:

בעלות בחלקים (כרשום בנסח טאבו):


בעלות במ"ר: 190.08

שטח מדוד (מ"ר): 135

שטח מגרש משנה: מ"ר

אביאסף

תרשום הסביבה 1 : 1250

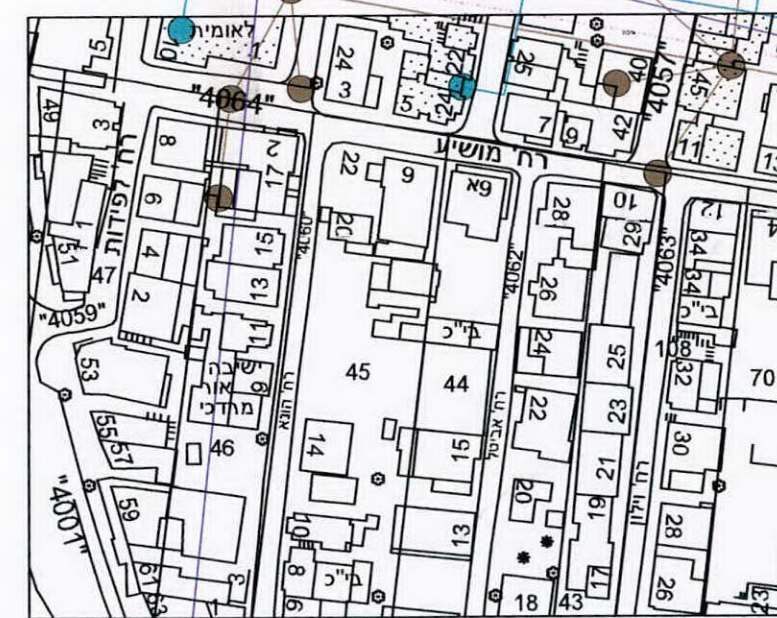

הערות:

המספרים בסוגריים מציינים גבהים 1.


הגבהים מבוססים על נק. עירונית מס' 187 שגובהה 17.594 מ'.

בקשה מספר: 2012-00924 אביטל 17 קנ"מ : 1:250

| חלקה | שם הבעלים      | מס' ת.ז.  | שטח חלקה כולה | בעלות בחלקים | בעלות במ"ר |
|------|----------------|-----------|---------------|--------------|------------|
| 44   | בבלי יפה       | 3049583   | 11,476.00     | 157/1101696  | 1.635      |
|      | מזרחי אסתר     | 5057369   |               | 157/1101696  | 1.635      |
|      | מזרחי מרדכי    | 5408886   |               | 157/1101696  | 1.635      |
|      | מזרחי מלי      | 5276468   |               | 157/1101696  | 1.635      |
|      | מזרחי אברהם    | 479299    |               | 157/252472   | 7.14       |
|      | אבויריש אביבה  | 479301    |               | 157/252472   | 7.14       |
|      | סמוכה עדינה    | 479300    |               | 157/252472   | 7.14       |
|      | מזרחי יוסף     | 479302    |               | 157/252472   | 7.14       |
|      | מזרחי עובדיה   | 479303    |               | 157/252472   | 7.14       |
|      | מזרחי יצחק     | 479304    |               | 157/252472   | 7.14       |
|      | מזרחי יהודה    | 479305    | 11,476.00     | 157/252472   | 7.14       |
|      | ברסמן טוב מרים | 479306    |               | 157/252472   | 7.14       |
|      | אברהם רחל      | 5050232   |               | 157/252472   | 7.14       |
|      | נחום דליה      | 5201009   |               | 157/252472   | 7.14       |
|      | מזרחי יחזקאל   | 307794958 |               | 157/1147600  | 21         |
|      | מכסין ילנה     | 307232645 |               | 42/11476     | 42         |
|      | סורל רוג'ר     | 312326810 |               | 469/45904    | 42         |
|      | גבריאל אלון    |           |               |              |            |



מפה טופוגרפית  
קנ"מ 1 : 250

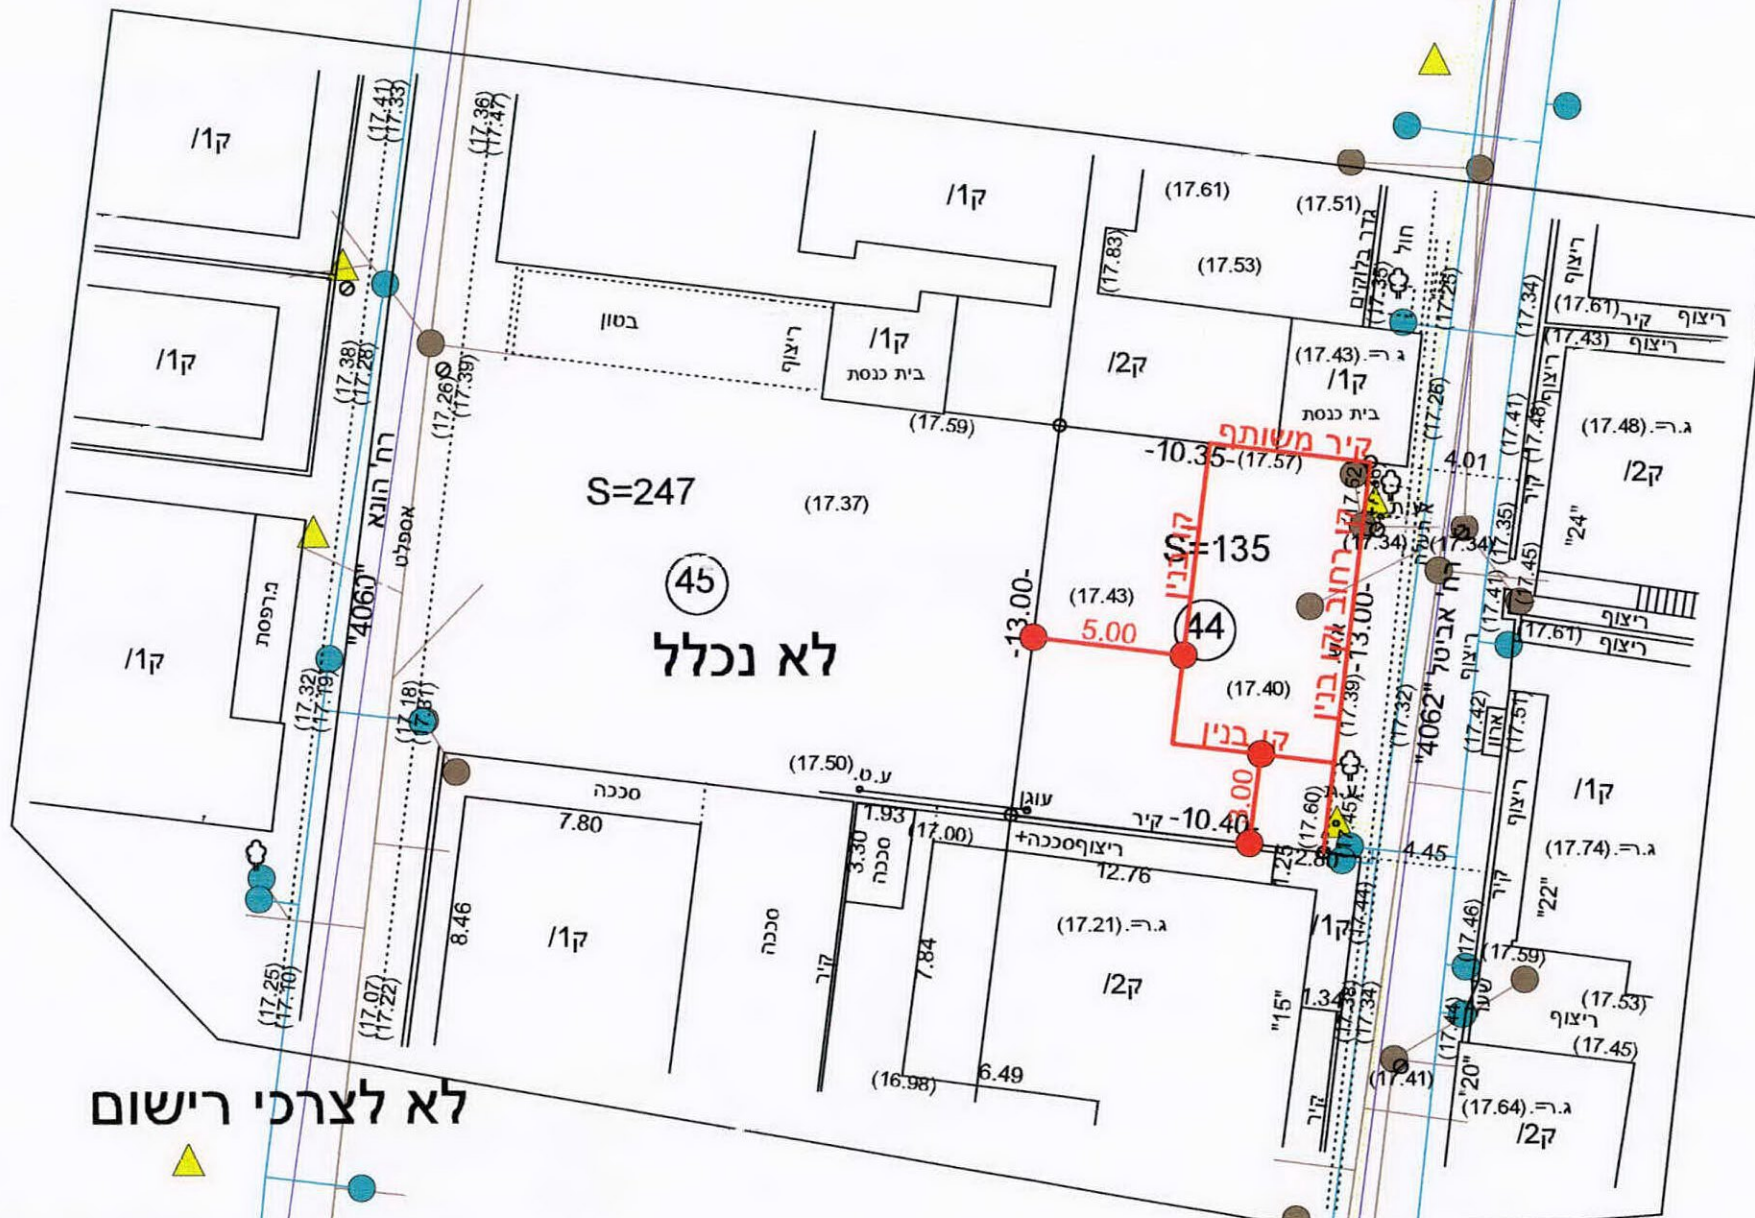

הנני מצהיר בזה שהמפה נעשתה לפי חוק התכנון והבניה התקנות וההנחיות של עיריית תל-אביב-יפו.

לא לצרכי רישום

י. אברבך

תאריך: 29.04.12 מודד מוסמך מס' רשיון 461

חברת אברבך י. ת. בע"מ.

רחוב דיזנגוף 190 ת"א, טל': 035235891

ME-שן: שהקרוז @ זשישה מילרסקי: 035226791