

איכות נמוכה

מ-93-354-1273
15.8.93
26



מנהל ההנדסה / אגף תכנון ובנין ערים
מח' שרותי בנין ערים - מדור המידע

הערות למפה טופ' / מצבית

גוש - 6135 חלקה - 44
מס' תיק מידע 1273-92

31	רח' 3672-לוד
50-60	רח' 4001-אביטל
69	רח' 4001-אצ"ל
	רח' 4046-יטון
	רח' 4062-אביטל
8.0	רוחב דרך-8.0
6-8	רח' 4064-מושיע

יעוד בתוקף - אזור מגורים ב
תכניות בתוקף - 2215
הערות - רחוב 4062-אביטל ברוחב 4-8 מ' קו בנין 0.
קו בנין צדדיים 3 מ' או 0 (קירות משותפים).
קו בנין אחורי 5 מ' גובה הבנין 3 קומות.
אחוזי הבניה הכוללים 140%, תכנית קרקע מירבית
60% מרתף לפי תכנית ע'.
הצפיפות 10 דירות לדונם.
אין לגבות היטל השבחה היות והשבונה הוכרזה
כשכונת שקום, הסדר המגרש יעשה במסגרת הסדר כללי
של השכונה.
יש לתאם את התכנון עם צוות מזרח באגף תב'ע.

חתימה
15.8.93
חתימה
11.8.93

עיריית תל אביב-יפו / מנהל הנדסה
מחלקת התכנון והנדסה

אישור תוכנית
מס' 1062
רחוב
מס' 1608.93
תאריך

עיריית תל אביב-יפו
מנהל בנין והנדסה / אגף עבודות שיפוריות
מחלקת מדידות

חתימה
חתימה
תאריך 1608.93

מס' חשבונית (לצורך חשבוניות בנין)
מאושר (ונבע) מ: מס' (גרפי)
מאושר (ונבע) מ: מס' (גרפי)
מאושר (ונבע) מ: מס' (גרפי)

כאן העולה מידע על קיום



תל-אדיר

גוש: 6135
חלקה: 44 (חלק)

שטח: 0.282 דק (לפי שטח) 0.250 דק (כדור)

זהות העקשה: דנית גדר
הוכן עקור: לוי מזל

מדידה טופוגרפית
ק"מ 1:250

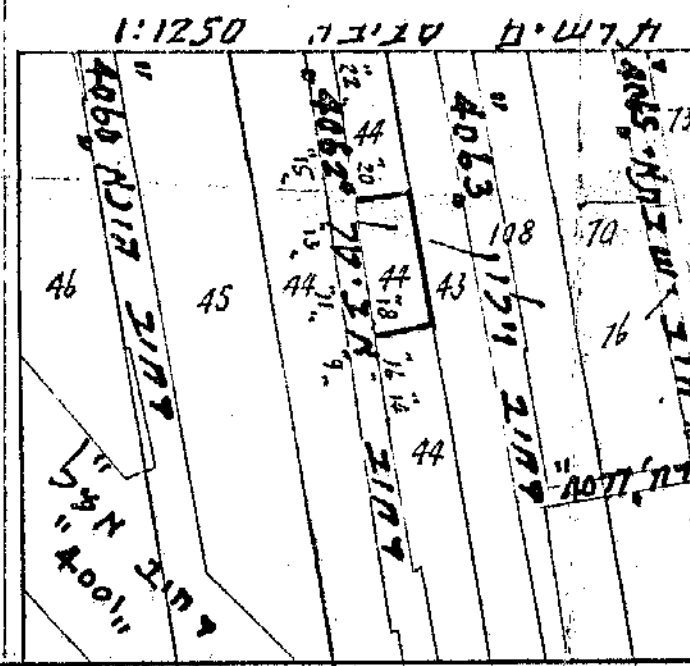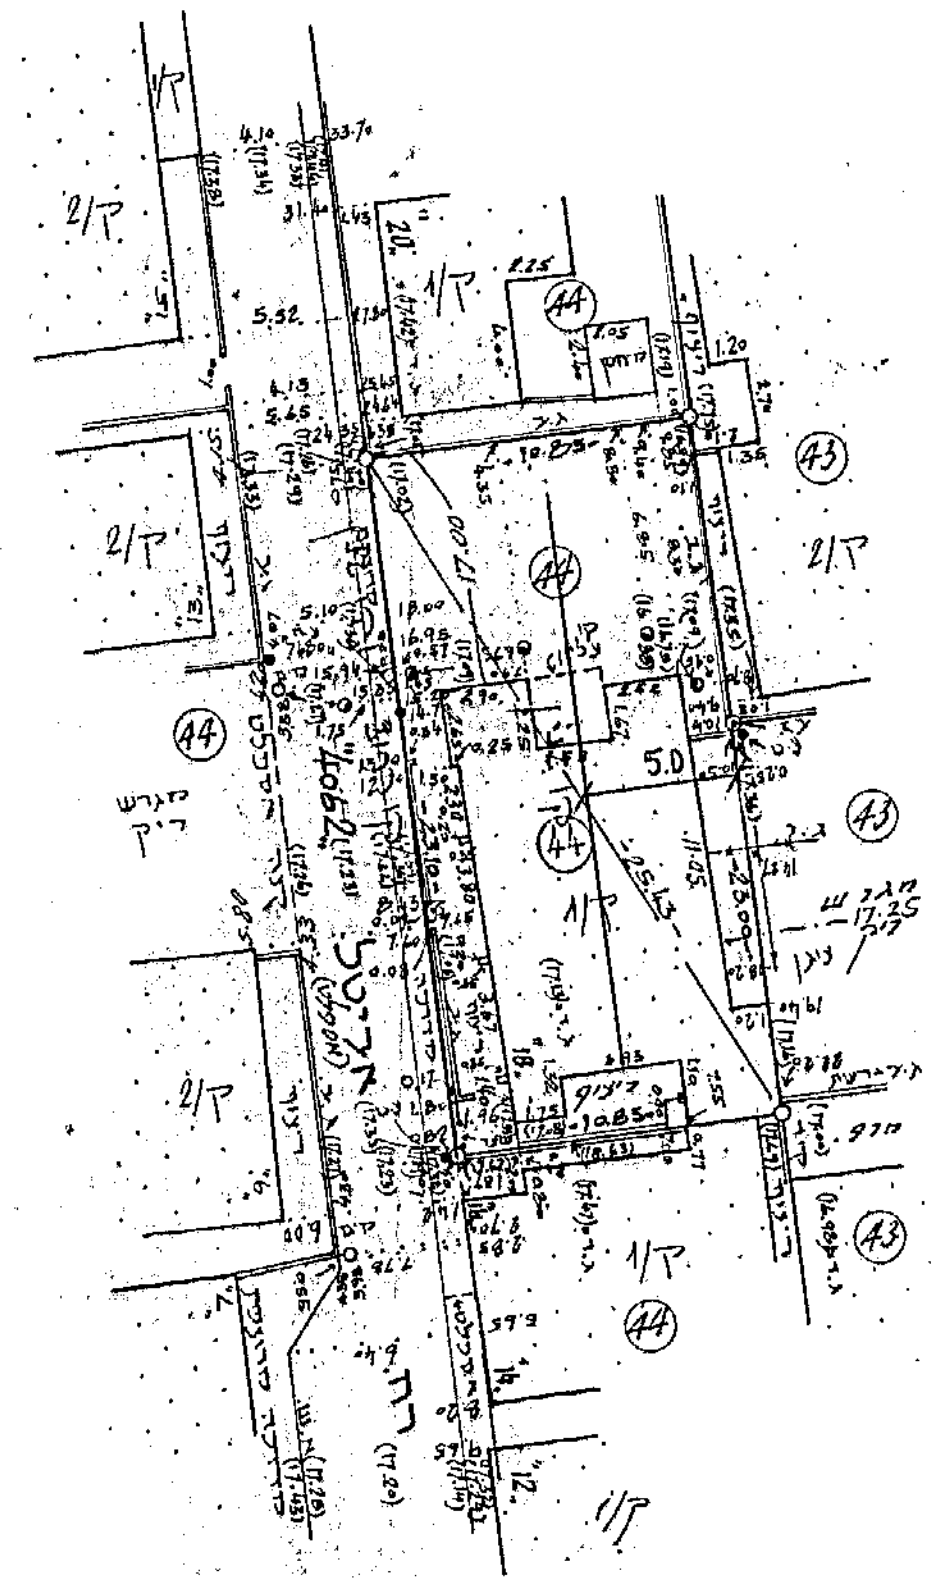

לא לערכי הישום

הנני מצהיר כי זוהי שהספה נעשית לפי חוק התכנון
והצננה, התקנות וההנחיות של עיריית תל-אדיר-יפו.

גדעתיים 4.11.92
דוד מוסקד

שבתא הפנר - מודד מוסקד, B.A. ושיון מס' 484
רחוק כנעלסון וצו גרעתיים, טל' 6736082-03

הערות:
1. הסכרים שאריות הם גרדים
2. האגדה מוסקד על זק 43 = 17.638 דק
3. בגבולות וקבעו 22 מסגרי הקיים