

מ"פ-93-354
15.8.93



מנהל התנדוטה / אגף תכנון ובנין ערים
מח' שרונה בנין ערים - מדור המידע

הערות למפה טופ' / מצבית

גוש - 6135 חלקה - 44
מס' תיק מידע 1273-92

31	רח' 3671-לוד
58-60	רח' 4001-אצ"ל
69	רח' 4001-אצ"ל
	רח' 4046-שולן
	רח' 4062-אביטל
	רח' 4064-מושיע

יעוד בתוקף - אזור מגורים ב
תכניות בתוקף - 2215

הערות - רחוב 4062-אביטל ברוחב 4-8 מ' קו בנין 0.
קו בנין צדדיים 3 מ' (קירות משותפים).
קו בנין אחורי 5 מ' גובה הבנין 3 קומות,
אחוזי הבניה הכוללים 140%, תכנית קרקע מירבית
60% מרתף לפי תכנית ע'.
הצפיפות 10 דירות לדונם.
אין לגבות היטל השבחה תיות והשכונה הוכרזה
כשכונת שקום. הסדר המגרש יעשה במסגרת הסדר כללי
של השכונה.
יש לתאם את התכנון עם צוות מזרח באגף תב"ע.

חתימה
חתימה
חתימה
מנהל מדור המידע
15.8.93
11.8.93

עריכת תל-אביב-יפו / מינהל תכנון
אישור
רחוב אביטל
רחוב
רחוב
רחוב
תאריך 16.08.93

עיריית תל-אביב-יפו
מינהל תכנון והשכונות / אגף עבודות עיבודיות
פנקס תכנון
חתימה
חתימה
תאריך 16.08.93

ט"ח הפקעה (לצורך חשוב זכויות בנין)
מאושר (ת"ב) () מ"מ (גרפי)
י"ע (ת"ב) () מ"מ (גרפי)
כאמ"ל ע"פ חוק המ"ל

תל-אביב

גוש: 6135


חלקה: 44 (חלק)

שטח: 0.262 הא' (לפי שטח) 0.250 הא' (כדור)

זהות העקשה: דנית גדר

הוכן ע"ד: לוי מזל

דעה טוכוורכית
ק"מ 1:250

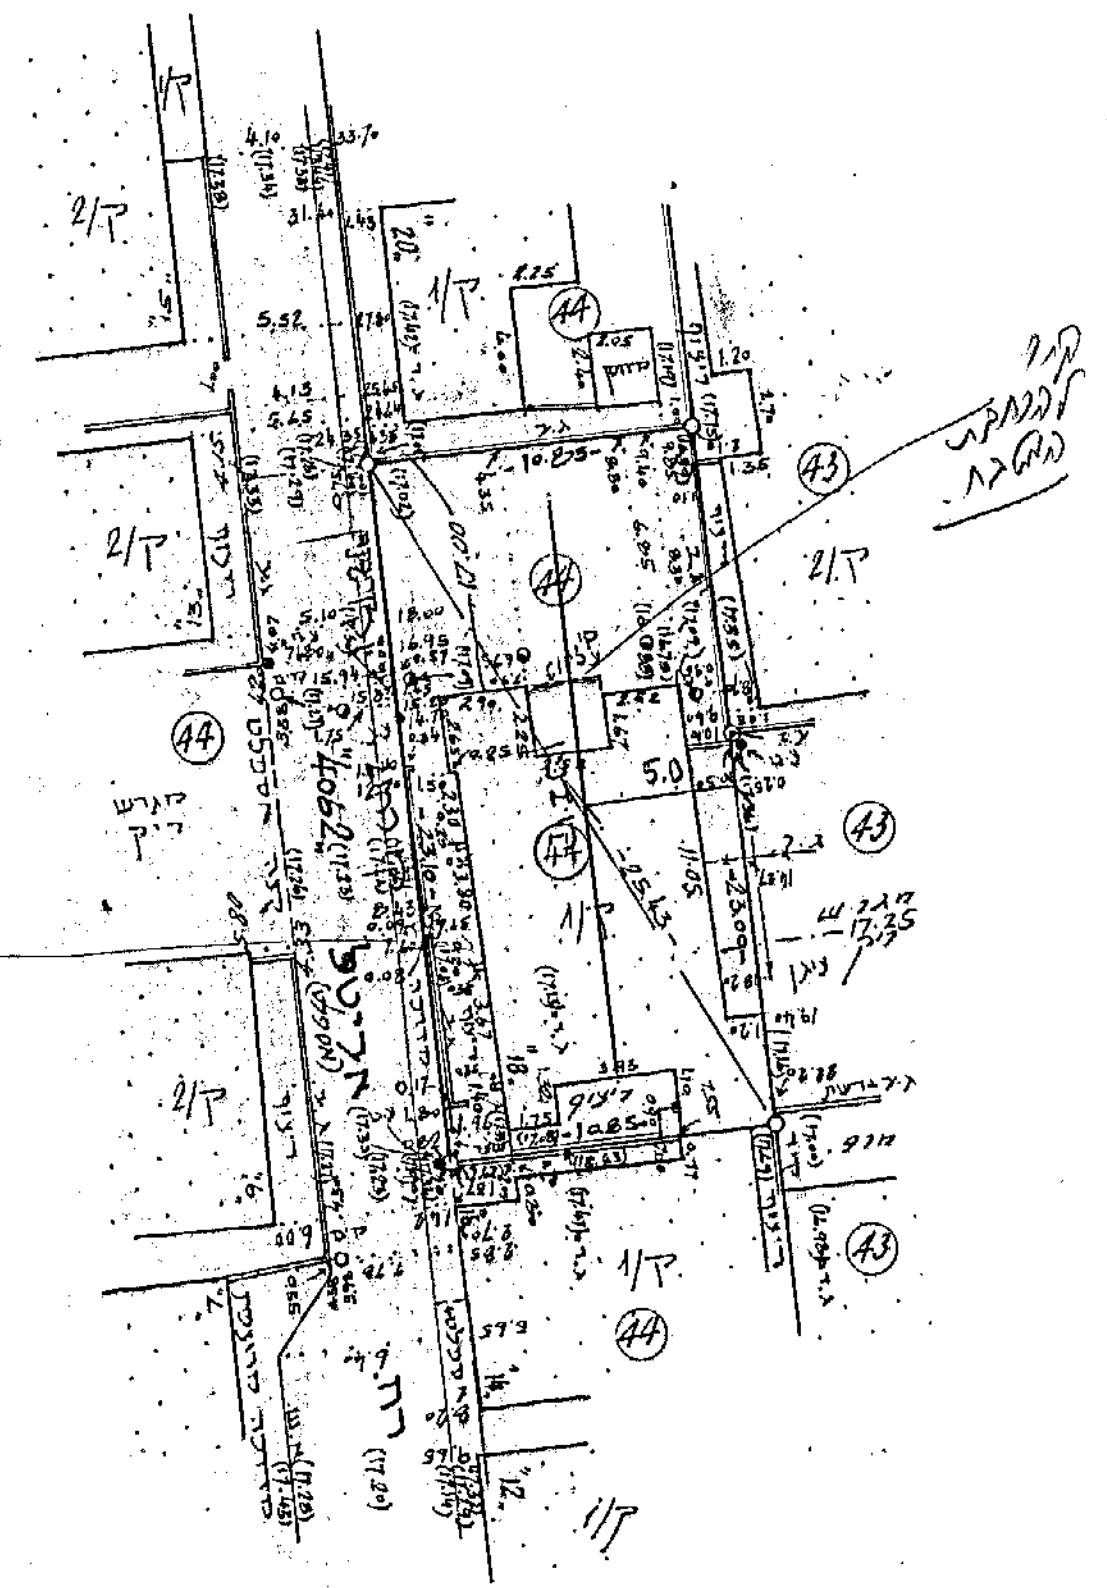

אחוזי הבניה
9 אח' אחוזים

לא לערכי רישום

הנני מצהיר דעה שהספה נעשית לפי חוק התכנון
והבניה, התקנות וההנחיות של עיריית תל-אביב-יפו.

גדעתיים 4.11.92
דוד מוסק

שבחאי הפנו - מודד מוסק, B.A., רשיון מס' 484
רחוב כנעלסון 130 גבעתיים, טל' 6736083-03

- הערות:
- המספרים בסוגריים הם ג'הים
 - האגדה מוסקס על כק 413 = 17.638 ד'
 - הגבולות נקבעו 22. המצב הק"מ

