לתיק 796-1652

22

חוק התכנון והבניה, התשכ"ה-1965

בקשה להיתר בניה או לשימוש במקרקעין

טופס 1
תקנה 2(א)

חוק התכנון והבניה, התשכ"ה-1965
תקנות התכנון והבניה (בקשה להיתר תנאיו ואגרות), התש"ל-1970

[redacted]

ועדה מקומית לתכנון ובניה / רשות רישוי	
מס' בקשה	96-1652
מס' תיק	4062-020

תאור הנכס

שם הישוב	שם הרחוב	מס' בית	גוש	חלקה	מגרש	התכנית/יות החלה/ות במקום
	סוכות	20	6135	45		2215

	משפחה	פרטי	מס' זהות	המען	טלפון
המבקש	שניר	[illegible]	5919884 6952772	סוכות 20	291011
בעל הזכות בנכס	"	"	"	"	"
עורך הבקשה הראשי	הרכשפון	[illegible]	30394840	שלמה המלך 60	5240857
מתכנן שלד הבנין	"	"	"	"	"

מיפרט

תאור הבקשה: שינוים בבמן בניה

129.1 — 134.21 — 104.0

תומרי הבניה

השטחים המבוקשים לבניה בכל המפלסים

קוד	מצב			סה"כ מ"ר	% משטח המגרש	הקומה
מגורים	49.72		49.72	45.72	47.8	±0.00
	48.94		48.94	48.94	47.1	+2.90
	22.11	0.26	22.11	22.36	21.5	+5.6
סה"כ	120.73	0.26	120.73	120.66	46.4	

השטחים המותרים לבניה בכל המפלסים

מגורים — 22.15 — 116.4 — 120.73 — 120.73

עיריית תל-אביב-יפו
מינהל ההנדסה

טופס השלמת פרטים

4062-020
96-1734

שינוים בבמן הבניה

קרקע 55.94
55.94
22.36
134.34

מפקדת ראש הג"א – ענף הנדסה ומיגון

המקלט/ממ"ד, בטון, פלדת הזיון, החסימה נגד מים ורטיבות, הגנת הקירות, המסגרות, המתקנים התברואתיים והחשמליים, הניקוז, הציפוי והצביעה של הקירות והסימונים יש לבצע לפי דרישות תקנות ההתגוננות האזרחית במקלטים

08.12.96

5-1666

אישורנו מותנה בתנאים כדלקמן:

1. ביצוע מרחב מוגן במפורט בתכנית המאושרת (חס' חיום) באחריות המבקש, עורך הבקשה והמהנדס אחראי על ביצוע השלד.
2. אישור על חיבור השלד ינתן ע"י מהנדס מקלטים בעירייה, אחרי קבלת תצהיר מהנדס אחראי על ביצוע השלד כנדרש.
3. בדיקה מרחב מוגן תעשה בשני שלבים: בהלך הבניה, ובגמר הבניה.

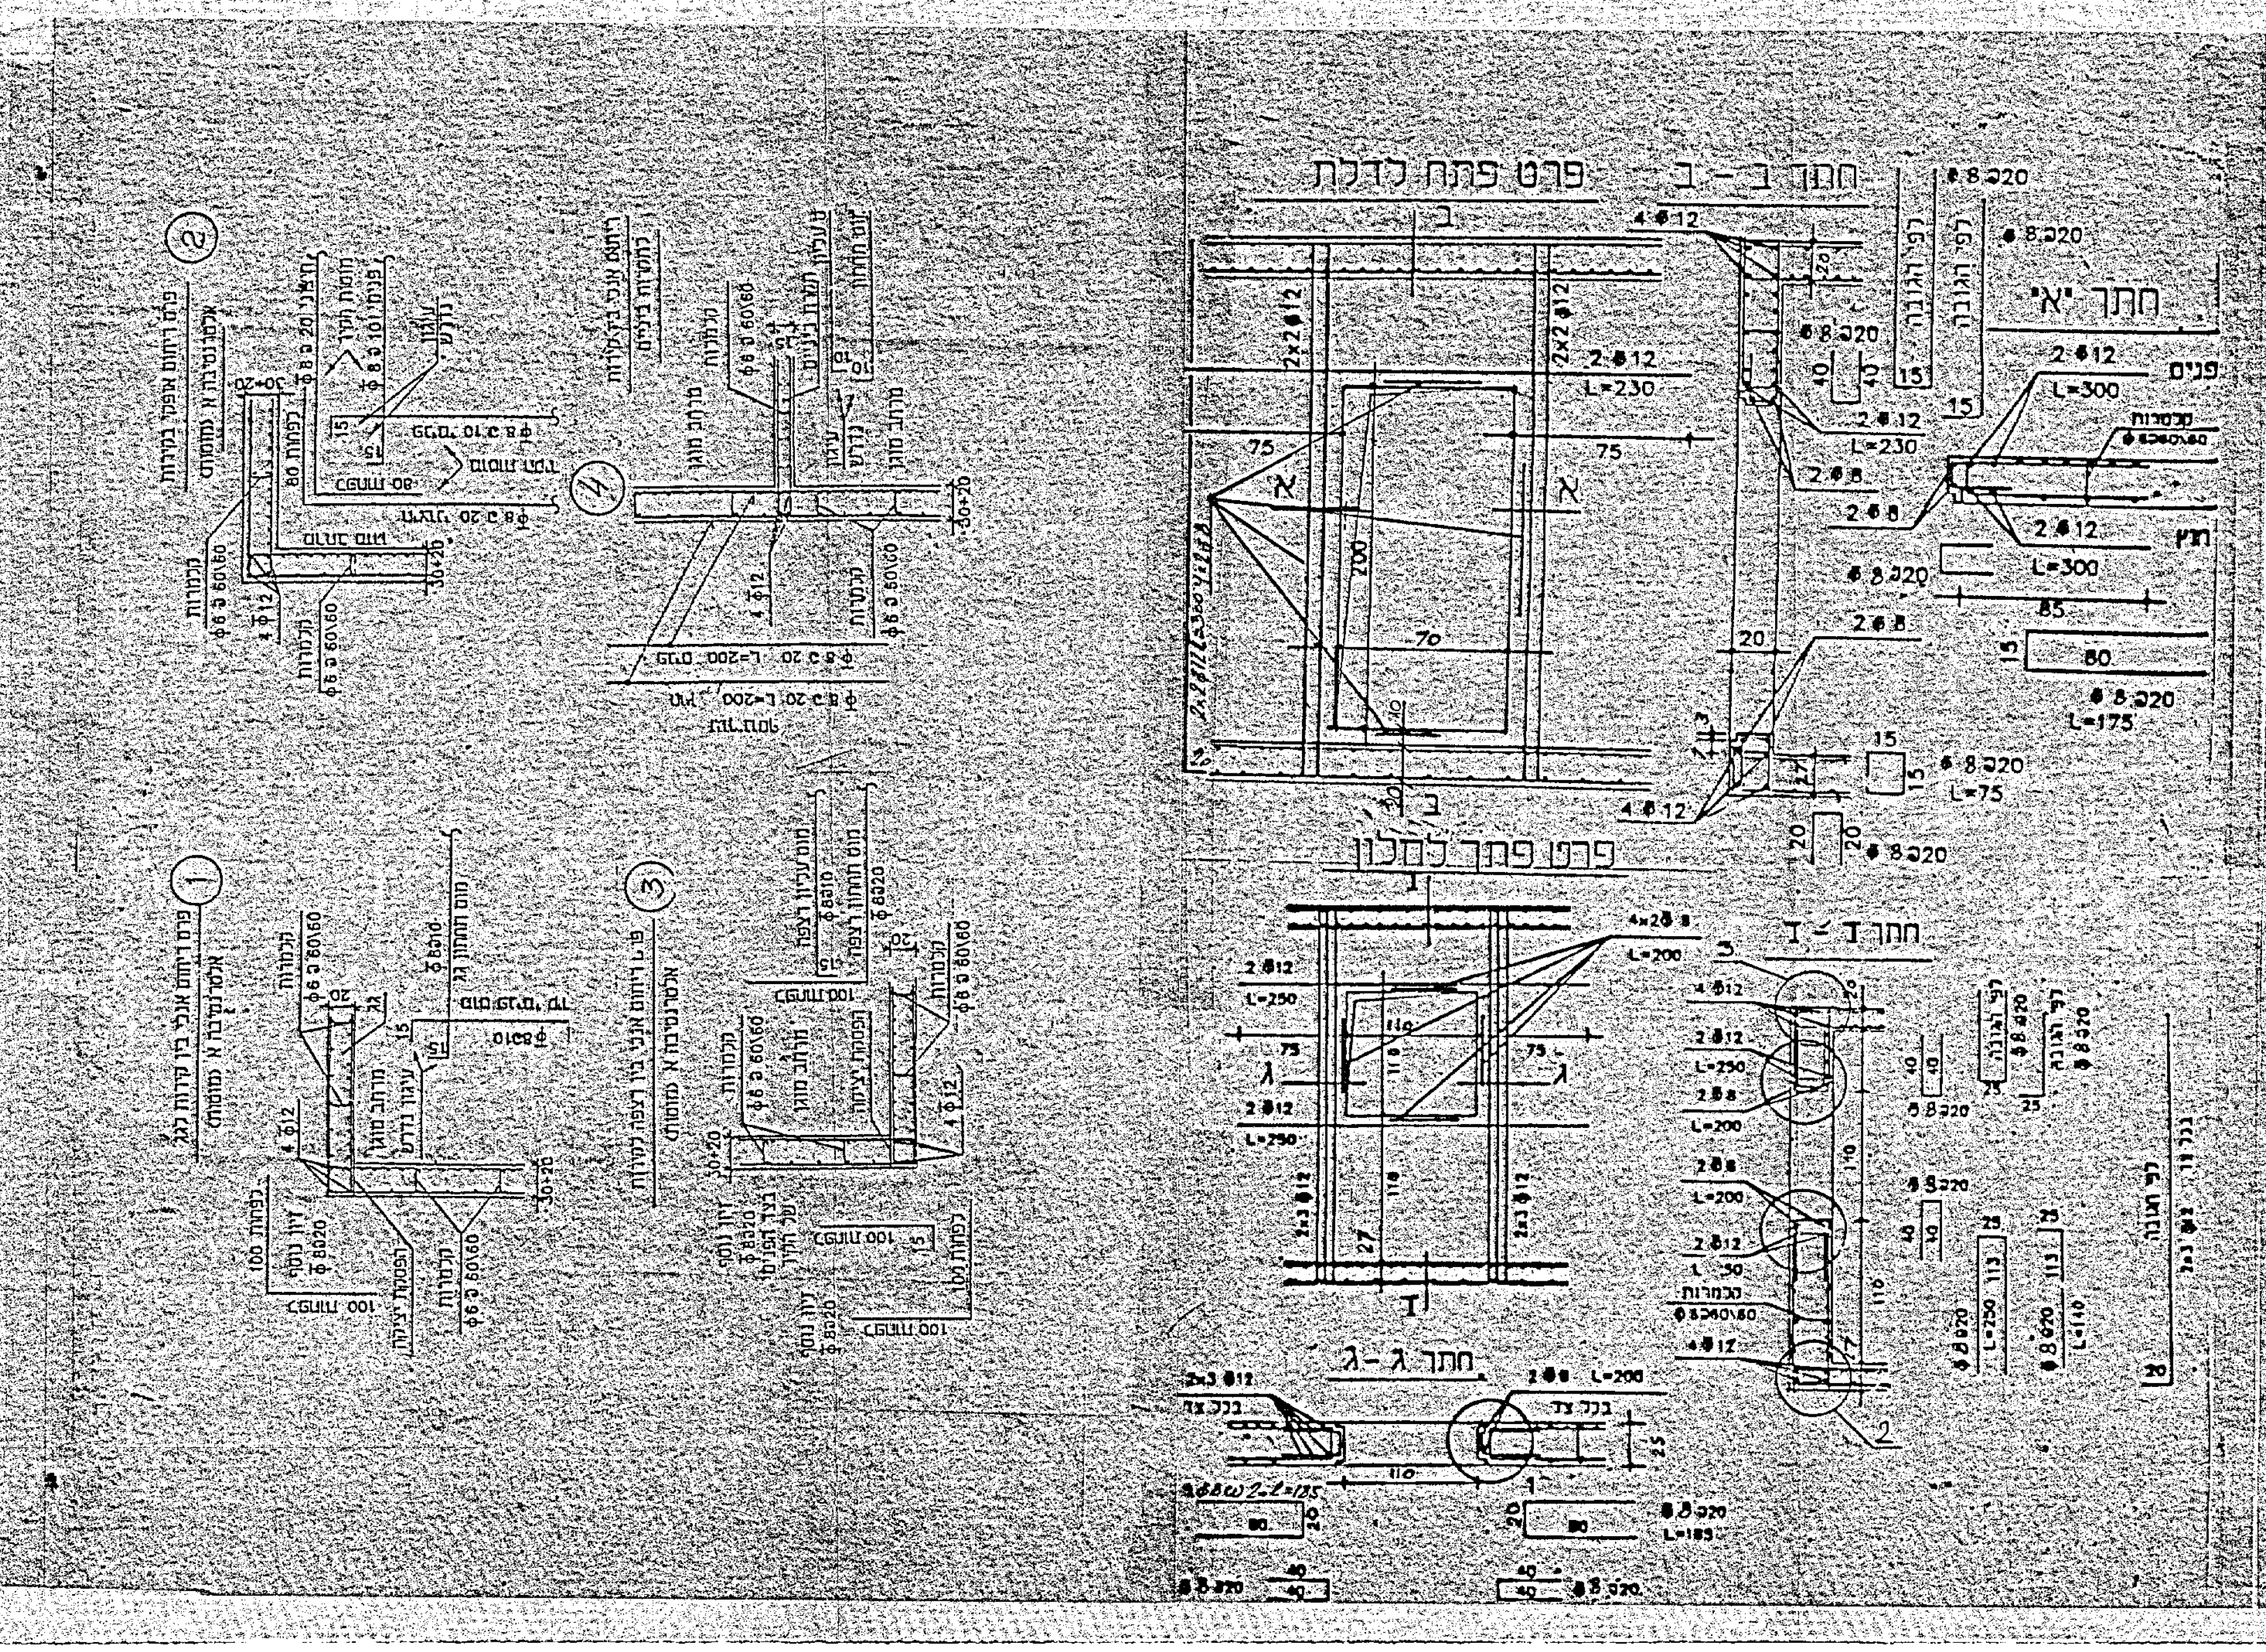

פרט פתח לדלת
חתך ב-ב
חתך "א"
פרט פתח למכון
חתך ד-ד
חתך ג-ג

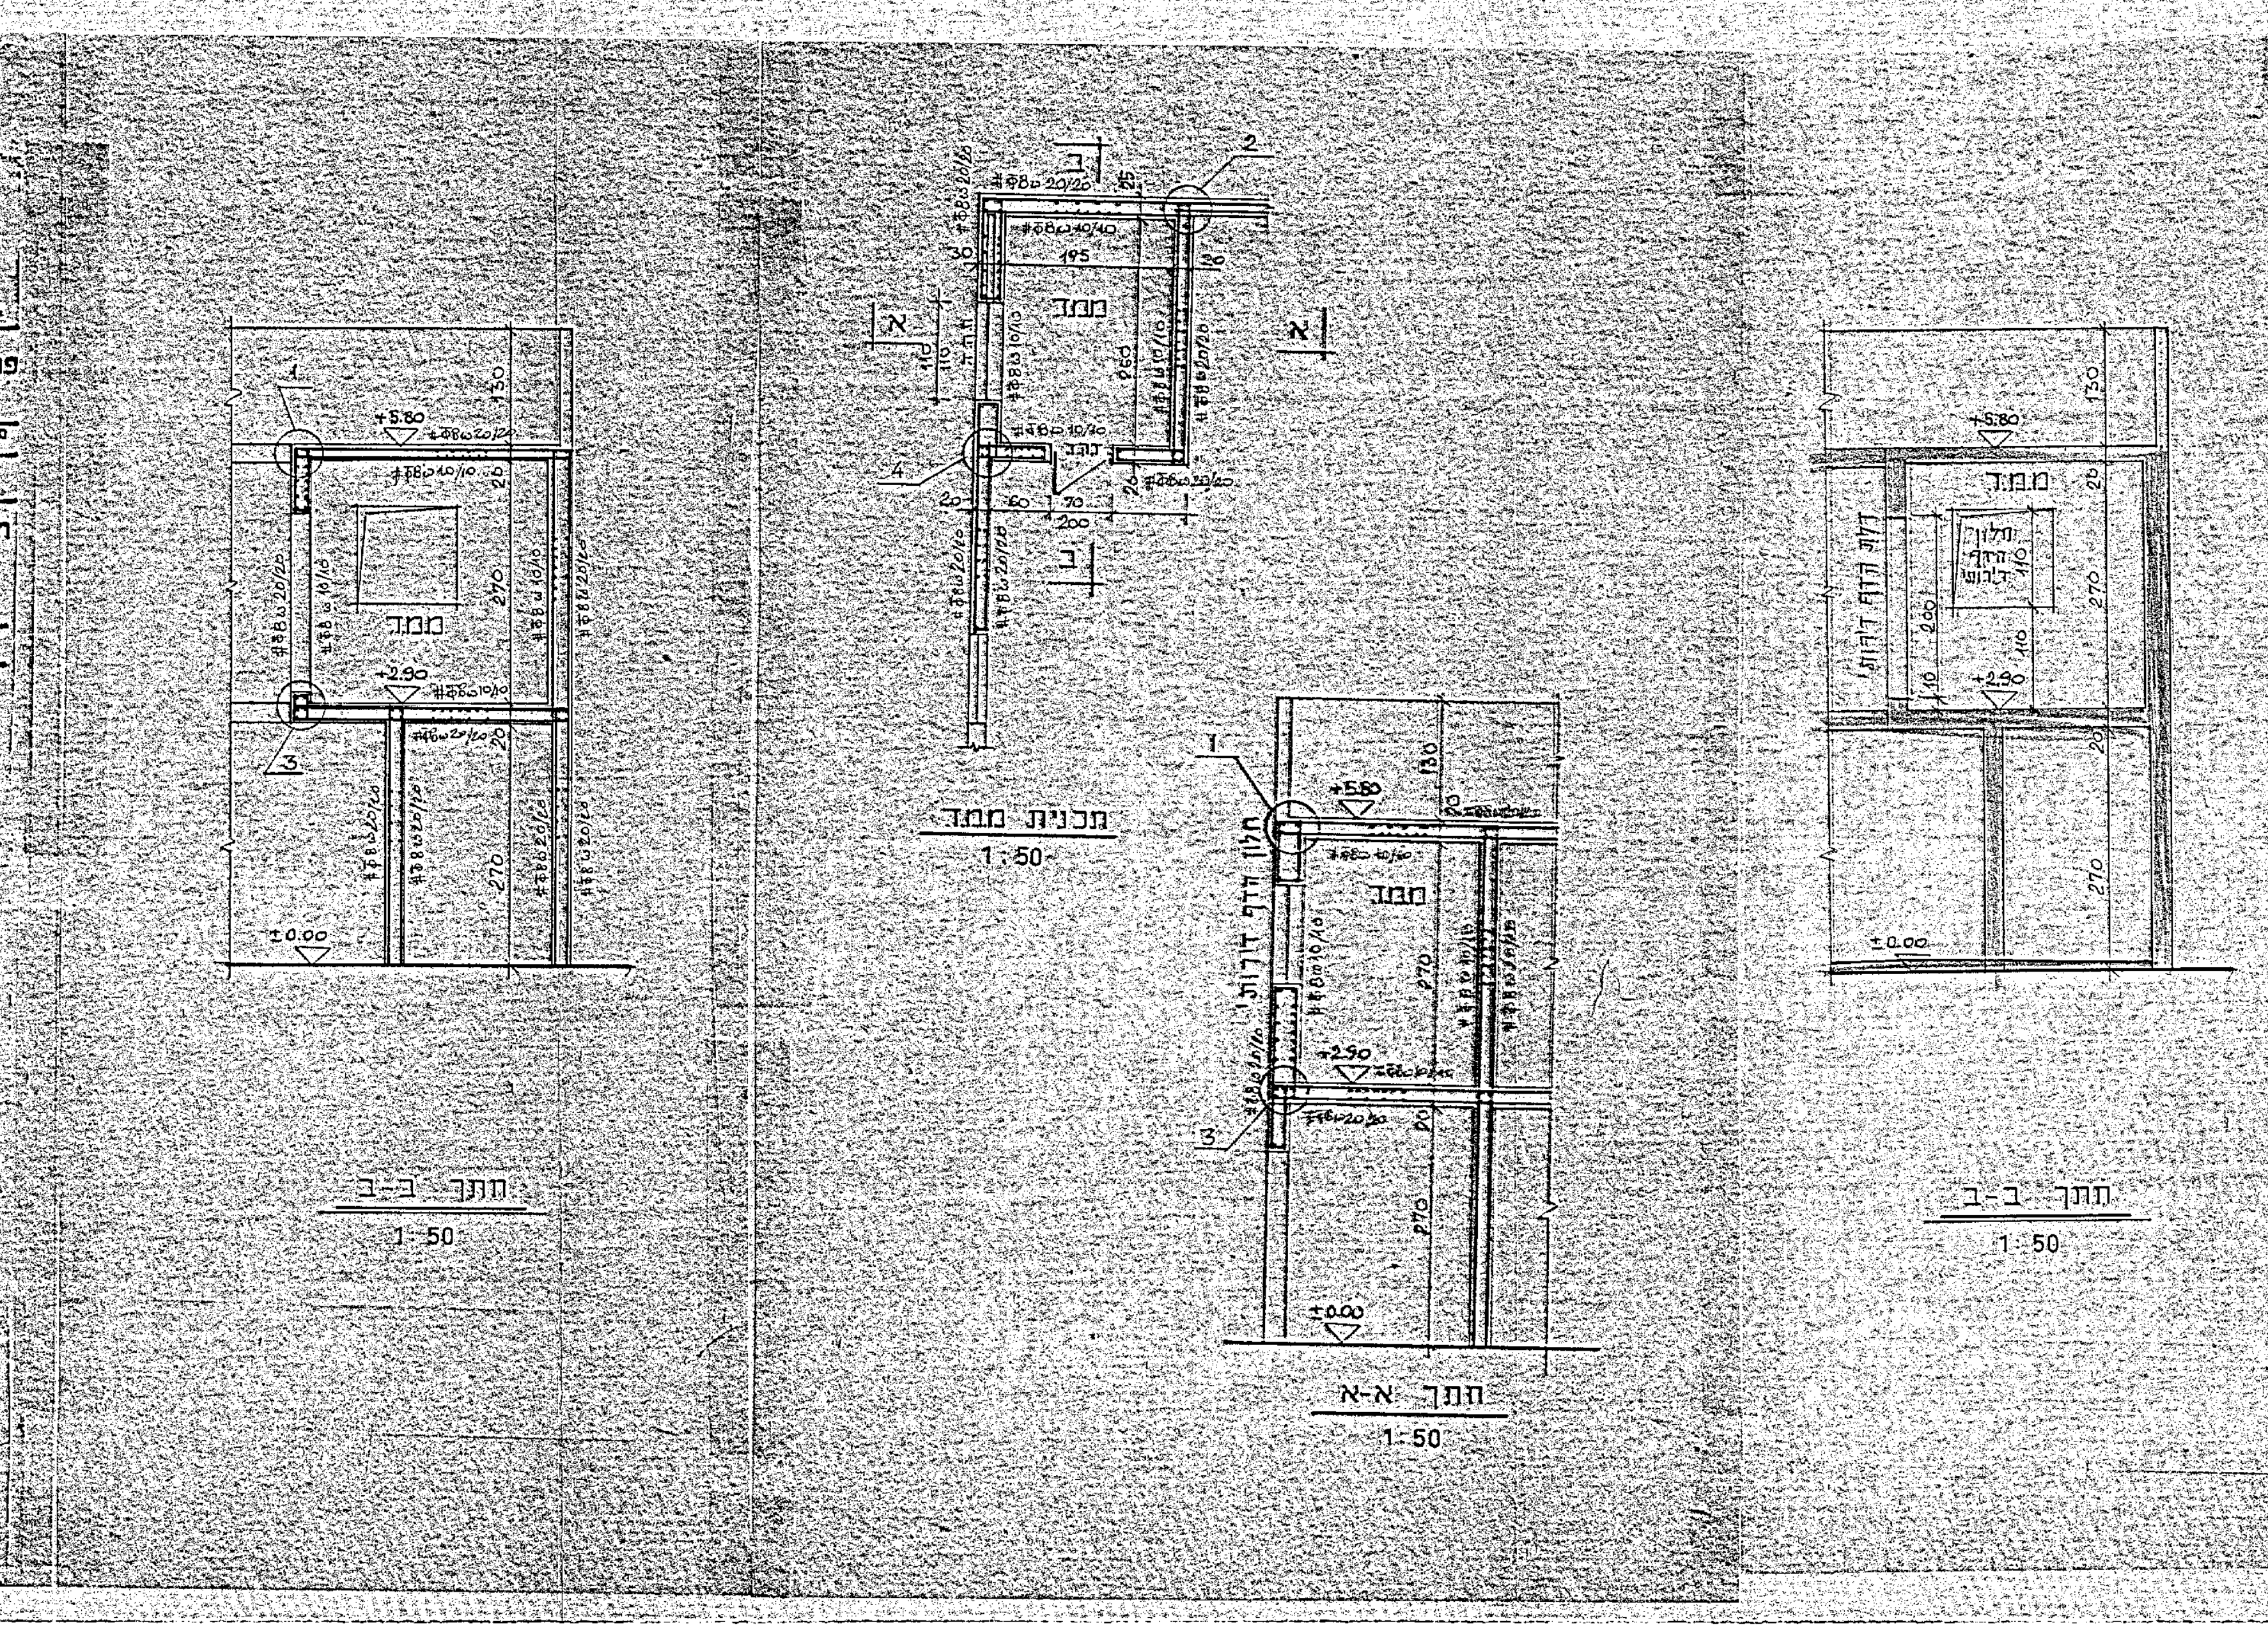

ממ"ד
תכנית ממ"ד
1:50
חתך ב-ב
1:50
חתך א-א
1:50

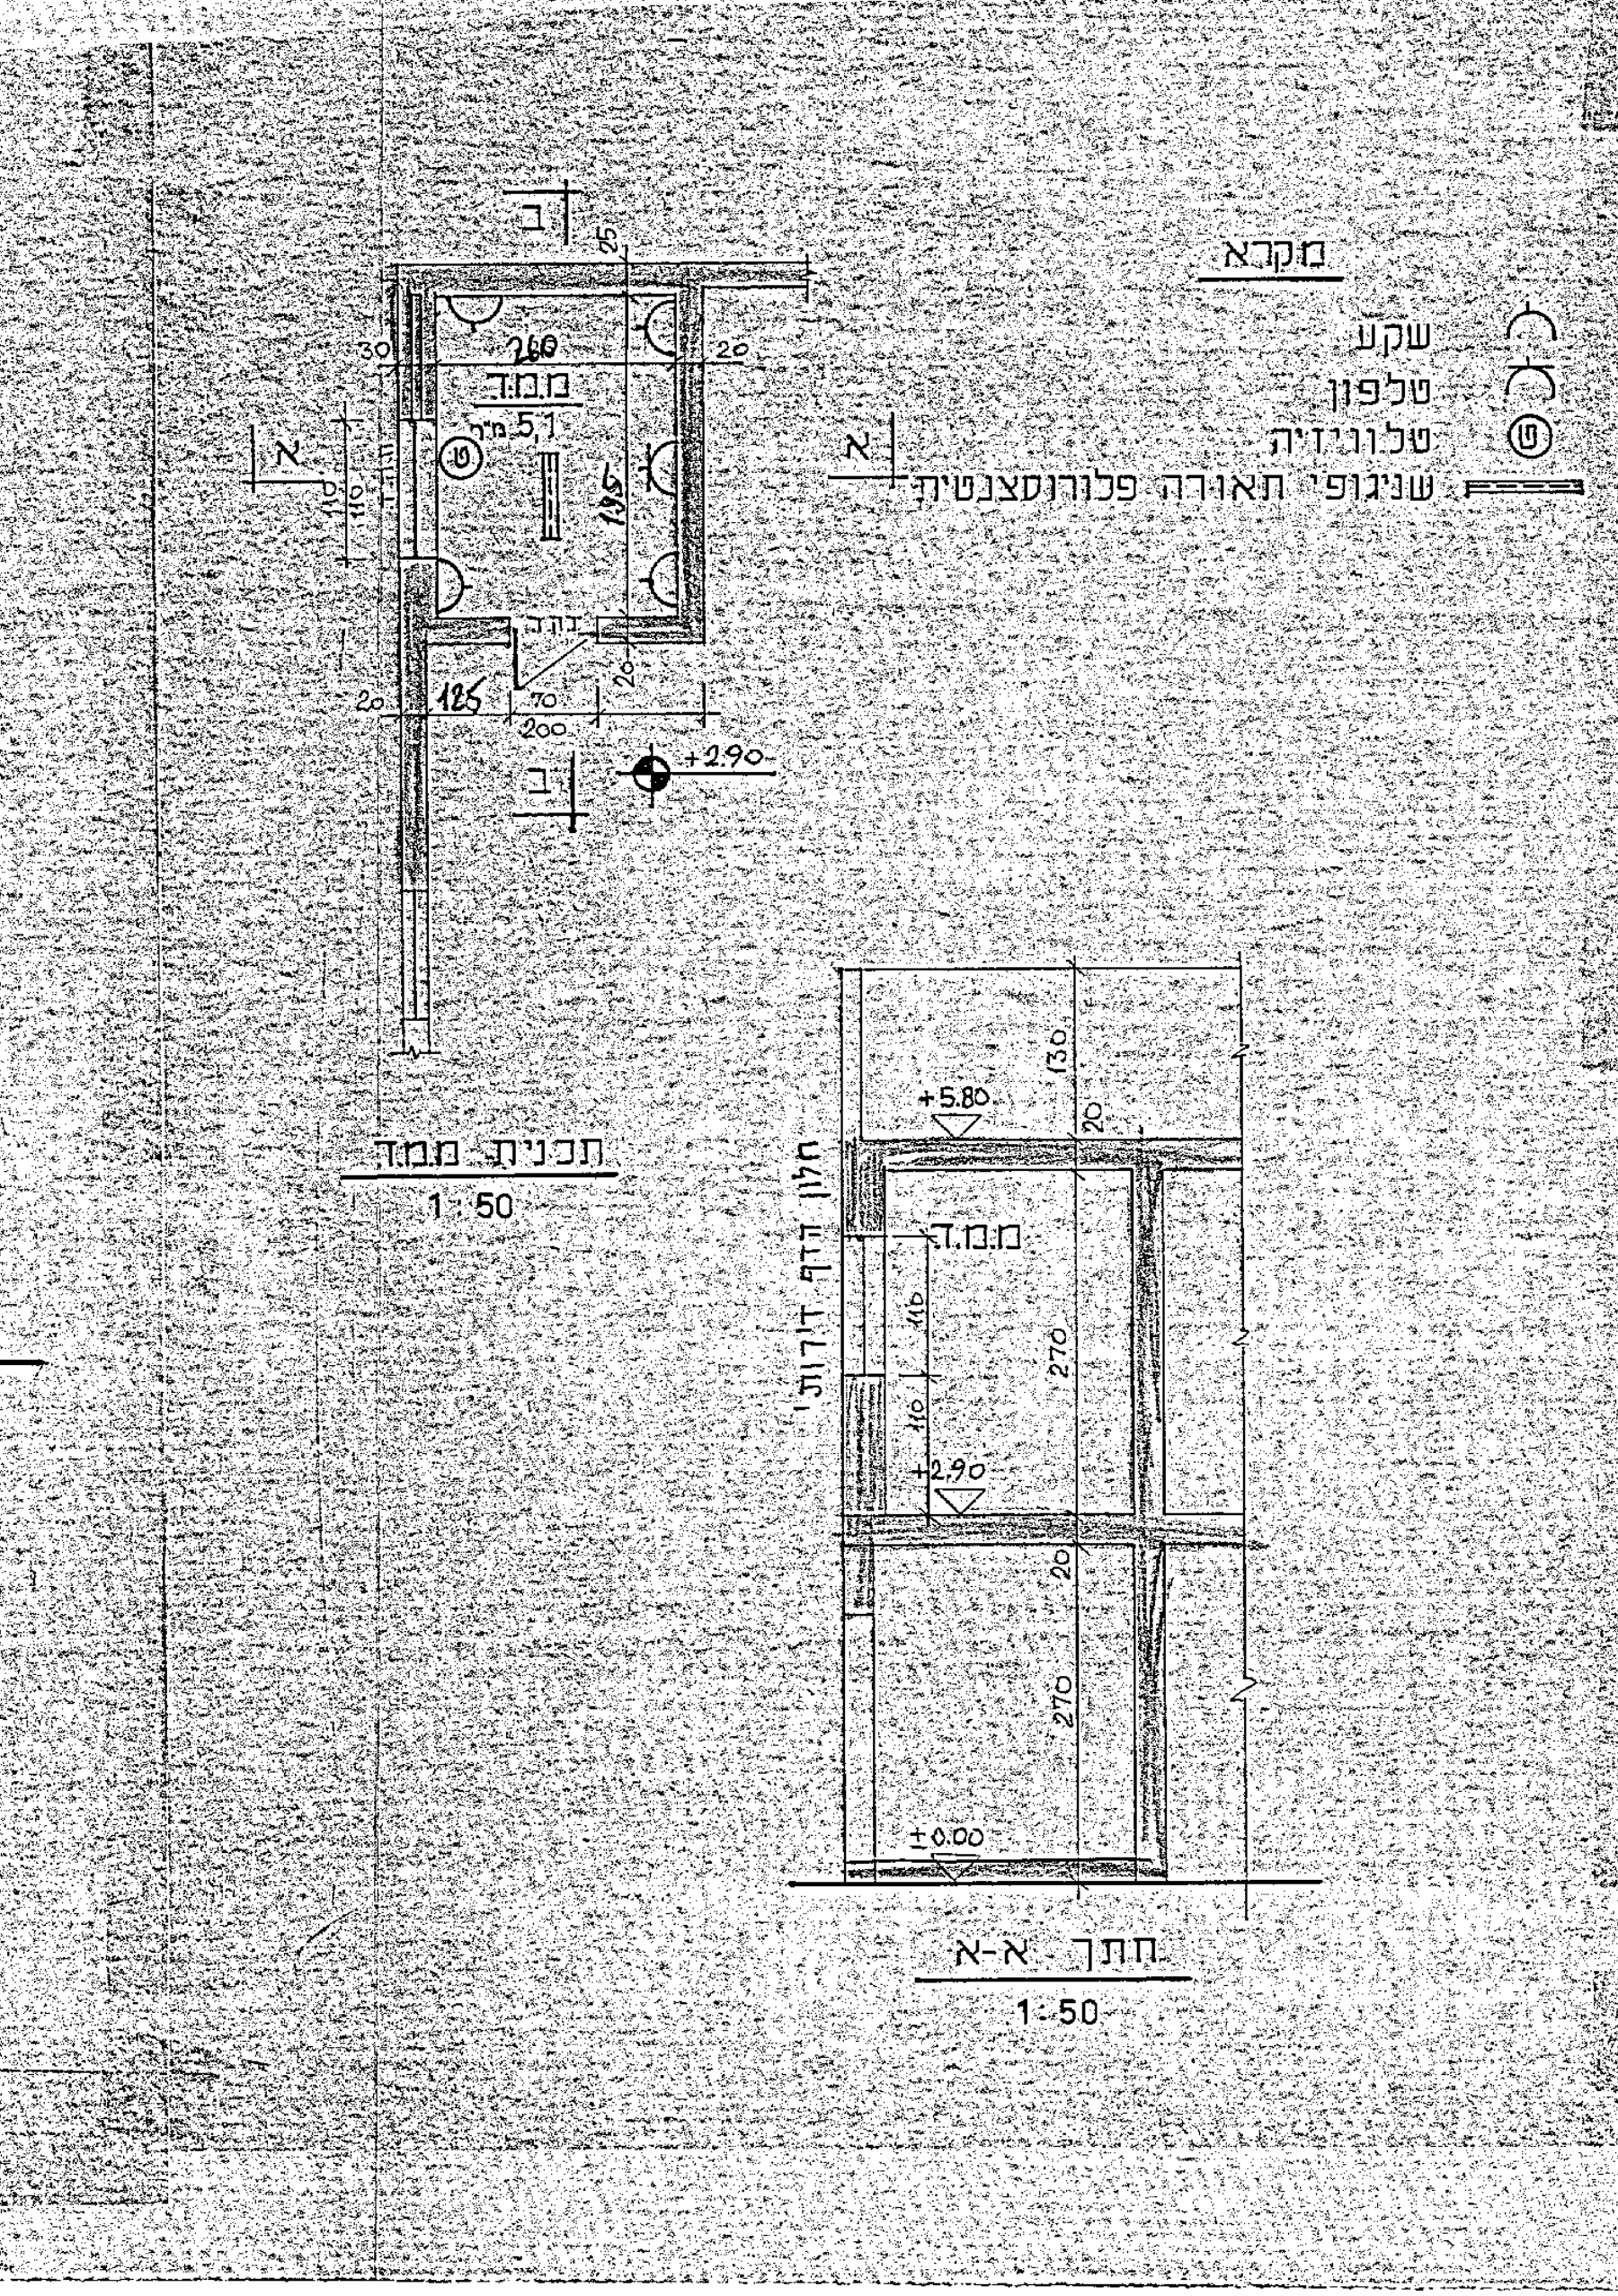

ממ"ד
מקרא
שקע
טלפון
טלוויזיה
שנגופי תאורה פלורוסצנטית
תכנית ממ"ד
1:50
חתך א-א
1:50
חתך ב-ב
1:50

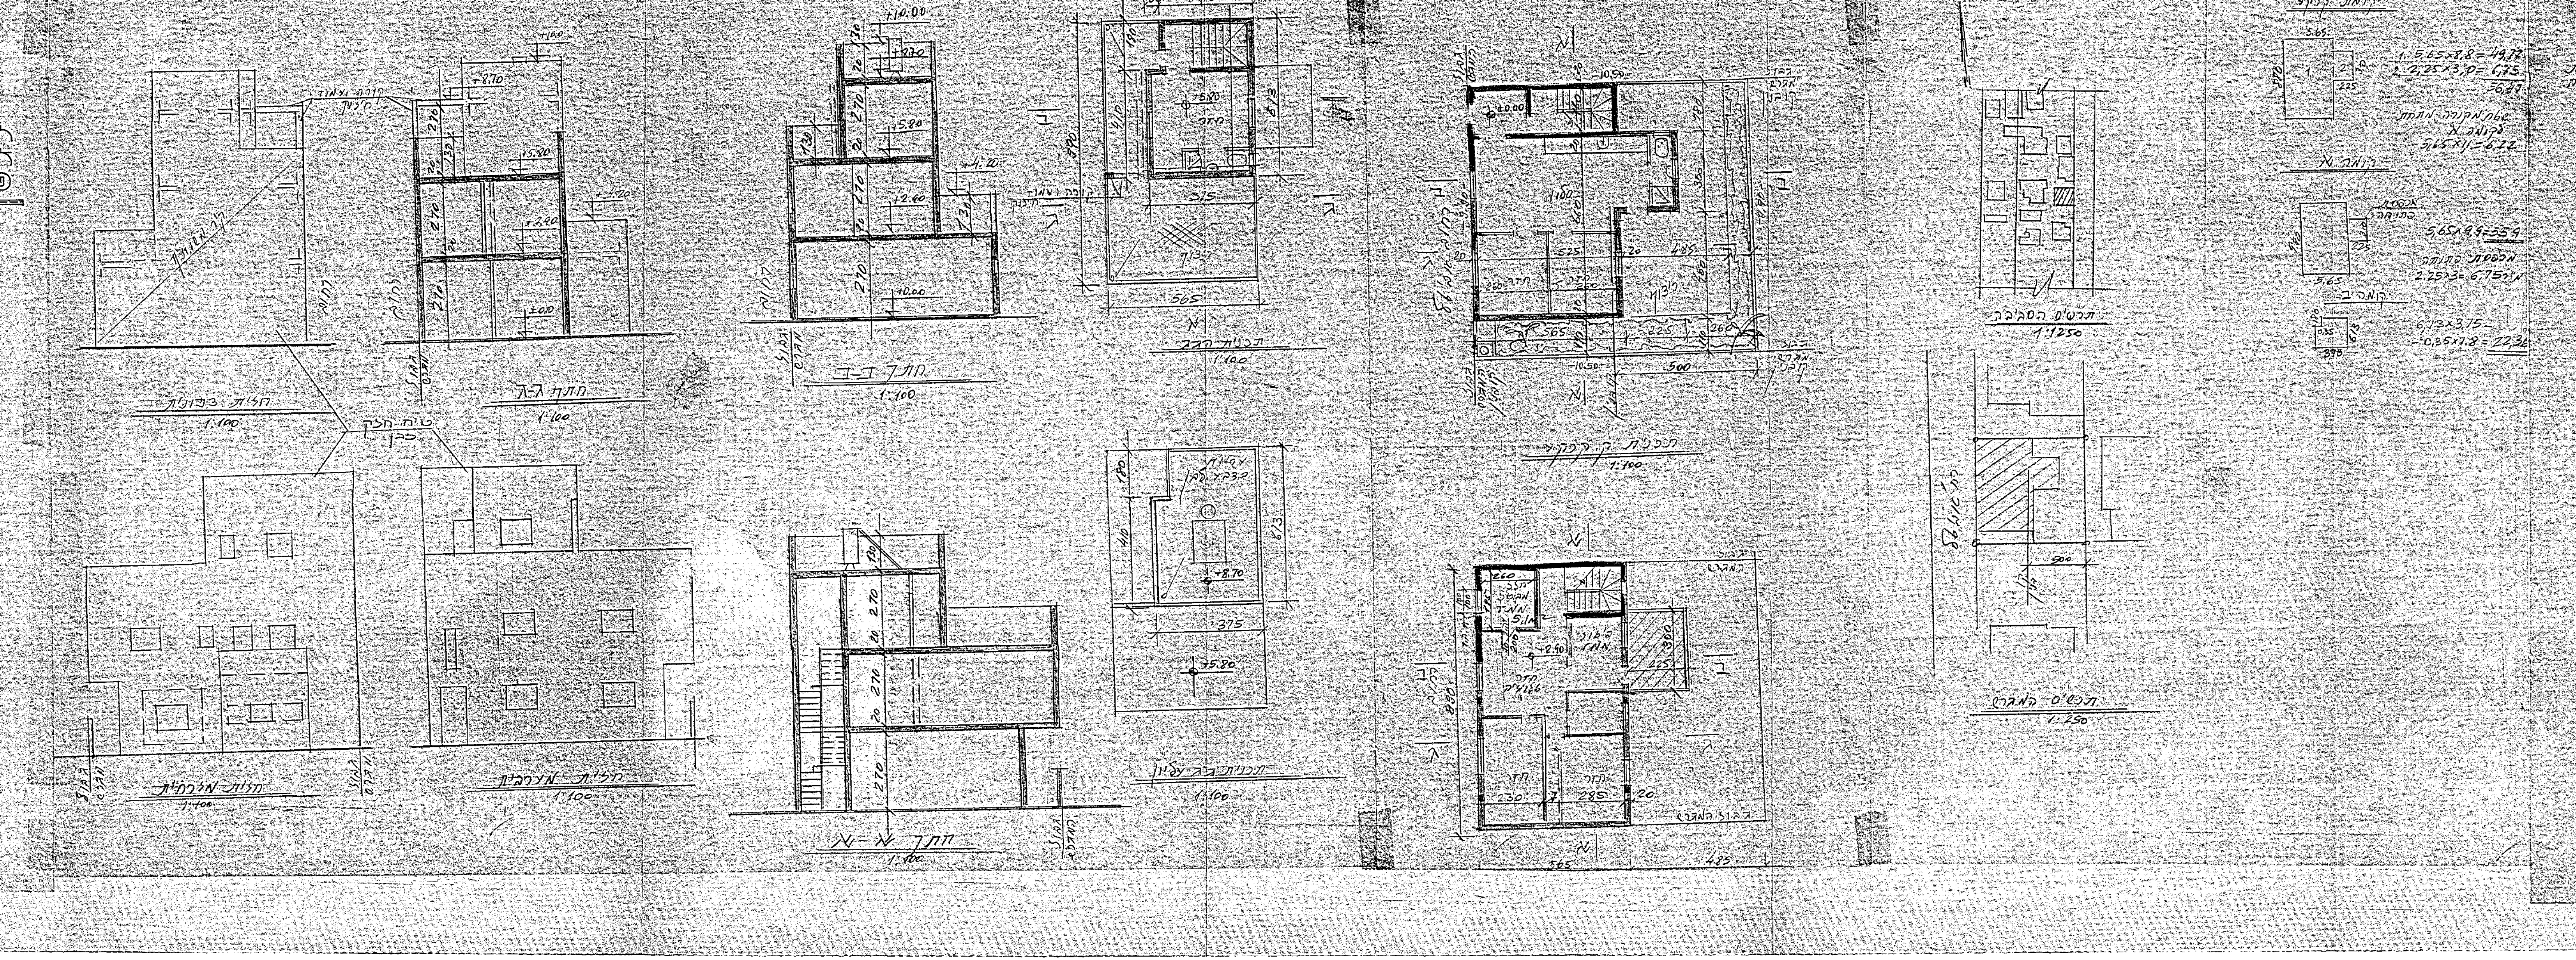

חזית צפונית
1:100
חתך ג-ג
1:100
חתך ב-ב
1:100
תכנית גג
1:100
תכנית ק. קרקע
1:100
חזית מזרחית
1:100
חזית מערבית
1:100
חתך א-א
1:100
תכנית ק. עליון
1:100
תרשים הסביבה
1:250
תרשים המגרש
1:250