004

20

פרטי הבקשה להיתר:
מספר פנייה: 16162
כתובת: אביטל 21
תאריך הדפסה: 06/07/2020

נסרק

תצהיר

אני החתום/ה מטה פדרמן אליה
בעל/ת ת.ז. 051656841
מצהיר/ה כי :

1. ביום 25/08/2019 הגשתי לעיריית תל אביב קבצי המחשב במסגרת הגשת בקשה להיתר בניה בפניה שמספרה 16162

2. את הקבצים הנ"ל, המפורטים ברשימה להלן, חתמתי בעצמי בחתימתי האלקטרונית.

3. רשימת הקבצים :

- 100_GAG.dwf
- 150_AVITAL GAG.dwg
- 1600_1.pdf
- 1600_11.jpg
- 1600_2.pdf
- 1600_22.jpg
- 1600_3.jpg
- 1600_33.jpg
- 1600_4.jpg
- 1600_5.jpg
- 1600_6.jpg
- 1600_7.pdf
- 1600_migun.pdf
- 1600_PTOR MIGUN.pdf
- 1600_PTOR.signed
- 1600_טופס תקינות וטופס פטור.pdf
- 1652_PTOR.signed
- 2100_1.jpg
- 2100_11 (1).jpg
- 2100_11 (2).jpg
- 2100_11 (3).jpg
- 2100_2.jpg
- 2100_3.jpg
- 2100_4.jpg
- 2100_5.jpg
- 2100_6.jpg
- 2100_7.jpg
- 2200_nesach mesuman.pdf
- 2200_nesachadkanu.pdf
- 2200_rishaion.pdf
- 2200_taz dolev.pdf
- 2200_taz tsach.pdf
- 2320_SRIKA and hagasha.dwfx
- 2360_avital.pdf
- 2360_pirsum musha.pdf
- 2360_telenechasim.pdf
- 2380_AVITAL 21.pdf
- 2400_SHOVAR.pdf
- 500_avital esh.dwfx
- 500_avital esh.pdf
- 500_GAG 2.pdf
- 500_GAG.pdf
- 501_AVITAL 21 NISPACH BETICHUT.dwf
- 501_GAG 2.pdf
- 501_GAG.pdf
- 501_GALAELONIM.pdf
- 501_KIBUY (2).pdf
- 501_MABADA (1).pdf
- 501_MAYM.pdf
- 5330_AVITAL.pdf
- 600_new.dwfx
- 900_avital.pdf
- 900_rishionot.pdf

4. השוותי בין התכנית המצויה בקבצים הנ"ל לבין התכנית המצויה בגיליון הנייר עליו מודבק תצהיר זה ומצאתי כי התכנית זהה בשניהם (בקבצים ובנייר).

פדרמן אליה אדריכל ובונה ערים ת.ר. 33662	6.7.20	
	תאריך	חתימה

פניה 16162
תאריך יצירה 06.07.2020
בקשה 20-0378
TEL AVIV YAFO תל אביב יפו

עיריית תל־אביב-יפו
מינהל הנדסה
אגף רישוי ופיקוח על הבנייה

חוק התכנון והבניה התשכ"ה- 1965
תקנות התכנון והבניה (בקשה להיתר תנאיו ואגרות) התש"ל - 1970
על פי טופס 1 תקנה 2(א)

א. פרטי הנכס והמבקשים

בקשת מידע: 2018-00922
תיק בניין: 4062-021

כתובת
רחוב אביטל
בית 21
גוש/חלקה: 44/6135
שטח מגרש/חלקה: 147.00 מ"ר
שטח בניה מבוקש: 22.97 מ"ר
אחוז בניה: 15.63

תכניות החלות על המקום והן מקור לשטחים מבוקשים
תקנה: 3ג

פרטים אישיים	שם משפחה שם פרטי שם חברה או תאגיד	רחוב / מספר בית ישוב מיקוד
מבקש	נקב צח יצחק	ארבע ארצות 12 תל אביב - יפו 6248614
מבקש	לדרמן דולב	המרגנית 4 רמת גן 5258404
בעל זכות בנכס	נקב צח יצחק	ארבע ארצות 12 תל אביב - יפו 6248614
בעל זכות בנכס	לדרמן דולב	המרגנית 4 רמת גן 5258404
עורך ראשי	פדרמן אליה	רבנו ניסים גאון 30 אלעד 40800
מתכנן שלד	חן אילה	הגאון אליהו 17 רמת גן 5236486

ב. מהות הבקשה

סוג הבקשה
מסלול מקוצר / תוספת בנייה על הגג למבנה מגורים

שימוש
מגורים

ג. מפרט תאור הבקשה

פירוט המבוקש לתוספת

הרחבת דיור
מספר יח"ד מורחבות: 1
שטח דירה/משרד לאחר תוספת (מ"ר): 23.00
כיוון התוספת: לאחור
כיוון התוספת: לצד
תוספת אחרת: תוספת לחדר על הגג לפי 3ג
שימוש המקום כיום: בהיתר בניין מגורים בן 3 קומות ובו 2 דירות מגורים

פירוט המבוקש לתוספת בניה בקומת הגג
כיוון התוספת: לאחור
כיוון התוספת: לצד
שטח ניצול חלל הגג (מ"ר): 23
הדירה, לרבות הבנייה על הגג קיימת בהיתר משנת: 2017
השימוש בתוספת המבוקשת: למגורים
גובה המבנה הקיים (מטר): 13.3
נסיגה מהמעקה מצד אחד (מטר): 1.2
נסיגה מהמעקה מצד שני (מטר): 1.2

הגורם עבורו מתבצעת העבודה
גורם פרטי

ד. חומרי הבנייה

סוג הבניה
רגילה

קירות חיצוניים
בלוקים

חומרי גימור
טיח

תקרות
בטון מזוין

גג
בטון מזוין

גדרות
בלוקים

מקרא חומרים (צבעים)
בטון או בטון מזוין: כחול
בלוקים או לבנים: אדום
עץ: חום
זכוכית: סגול
הריסה: צהוב
בניה קיימת: אפור

ו. קווי בנייה

ז. מספר יחידות דיור

מספר יחידות הדיור הקיימות: 2
מספר יחידות הדיור לביטול/הריסה:
מספר יחידות הדיור המבוקשות ששטחן עד 120 מ"ר: 2
מספר יחידות הדיור המבוקשות ששטחן מעל 120 מ"ר:
מספר יחידות הדיור המותרות: 2

ח. פרטי הבנייה - לשימוש הלשכה המרכזית לסטטיסטיקה

שטח הבניה ברוטו לפי היעוד
למגורים: 1 שטח: 23.00
סך כל שטחי הבניה: 23.00

גודל הדירות לפי מספר חדרים
חדר 1: מספר דירות: 1 מספר מגורים: 2
סה"כ מספר דירות: 1
סה"כ מספר מגורים: 2

ט. הבקשה מוגשת לאישור

ה. השטחים המבוקשים (על-פי תכני תכנית הבנייה) והמותרים לבנייה

(על-פי "אסמכתא" : חוק, תקנות, תכניות) בכל מפלס בנפרד ולפי שימוש

מבנה	הקומה	מפלס	מגורים בהיתר	מגורים מבוקש	עיקרי: סה"כ	עיקרי: % משטח המגרש	אסמכתא: תכנית ראשית/ אחר	סה"כ קומה: עיקרי+שירות	סה"כ קומה: % משטח המגרש	סה"כ קומה: שטחים לא מקורים
1	קומה 3	0.00	4.3377	18.6352	22.9728	15.63	(תקנה) 3ג	22.9728	15.63	35.3803
	מתחת לקרקע									
	מעל הקרקע		4.34	18.64	22.97	15.63		22.97	15.63	35.38
	סה"כ		4.34	18.64	22.97	15.63		22.97	15.63	35.38

י. הצהרת עורך הבקשה הראשי

אני מצהיר על נכונות הפרטים בסעיפים א עד ט

תאריך 6 / 7 / 20 שם: פדרמן אליה חתימה

יא. חתימות נוספות

תפקיד	שם	תאריך	חתימה
מבקש	נקב צח יצחק	6.7.20	צנ
מבקש	לדרמן דולב	"	
בעל זכות בנכס	נקב צח יצחק	"	צנ
בעל זכות בנכס	לדרמן דולב	"	
מתכנן שלד	חן אילה	"	

לתשומת לב החותם על תכנית הבקשה להיתר:

1) אין לחתום על תכנית הבקשה להיתר, אלא אם היא חלק מהדפסה רציפה (גרמוקשה / הרמוניקה) בנייר הכוללת את טופס1(פרטים ונתונים מילוליים ומספריים של הבקשה להיתר, חתום בחותמת מים של עיריית תל אביב) תרשים חישוב השטחים(חתום בחותמת מים של עיריית תל אביב) ותכנית הבקשה להיתר (תכניות, חתכים, חזיתות וכד').

2) לאחר שתפתח בקשת רישוי במחלקת רישוי בניה תשלח אליך הודעה עם מספר הבקשה להיתר. לאחר קבלתה, עליך להכנס לתיק הבניין בגנזך ההנדסה האינטרנטי באתר עיריית תל אביב ולוודא שהתכנית הנוכחית עליה חתמת כאן זהה למסמכי הבקשה להיתר כפי שהם מופיעים בתיק הבניין האינטרנטי.

יב. מינויים מטעם מבקש ההיתר

מינוי עורך הבקשה הראשי

אני ממנה בזה את פדרמן אליה בעל/ת מס' זהות 051656841 הרשום בסעיף א להיות עורך הבקשה הראשי להיתר, וליצגני לפני מוסדות התיכנון והרשויות המוסמכות בכל הנוגע לטיפול בבקשה להיתר ולקבלתו, לרבות התיקונים ככל שידרשו הרשויות המוסמכות.

מינוי עורכי בקשה לפי תחומים

אני ממנה את הרשומים להלן להיות עורכי הבקשה להיתר בתחום הפעולה כרשום ליד שמם, וליצגני בתחום פעולתו לפני מוסדות התכנון והרשויות המוסמכות בכל הנוגע לטיפול בבקשה להיתר ולקלתו, לרבות התיקונים ככל שידרשו הרשויות המוסמכות.

	שם משפחה שם פרטי	תחום פעילות	המען	פרטי התקשרות
1.	אליה פדרמן	אדריכל	רבנו ניסים גאון 30 אלעד	052-2948324
2.				
3.				

מינוי מתכנן שלד הבניין

אני ממנה בזה את חן אילה בעל/ת מס' זהות 052015443 הרשום בסעיף א להיות אחראי לתכנון שלד הבניין שבעבורו מבוקש ההיתר, להגיש לוועדה המקומית לרשות הרישוי המקומית את החישובים לגבי הבניין שבעבורה מבוקש היתר ולפקח פיקוח עליון על הקמת השלד.

מינוי הקבלן האחראי לבנייה

☐ אני ממנה בזה את ______ בעל/ת מס' זהות ______ ובעל תעודת רישום בפנקס קבלנים מספר ______ במדור ______ ובעל רישיון לביצוע עבודה בתוקף עד ______ לבצע את העבודה הנדונה בהיתר כמתחייב לפי כל דין.

☒ אני מצהיר, כי טרם מסרתי את ביצוע העבודה הנדונה בהיתר לידי קבלן, ומתחייב למסור אותה לידי קבלן רשום בפנקס הקבלנים, כמתחייב על פי כל דין, ולהודיע על כך לרשות הרישוי המקומית טרם התחלת ביצוע העבודה, וחתימתו של הקבלן תצורף להודעה המפרטת את פרטי רישומו של הקבלן.

מינוי האחראי לבניית שלד הבניין

☐ אני ממנה בזה את ______ בעל/ת מס' זהות ______ כתובת ______ טלפון ______ מייל ______ הרשום לעיל להיות אחראי לביצוע שלד הבניין.

☒ אני מצהיר, כי טרם מיניתי אחראי/ת לביצוע עבודות הבנייה בתחומים אלה: שלד ובנייה ומתחייב לעשות זאת כמפורט בתקנות, ולהודיע על כך לרשות הרישוי המקומית טרם התחלת ביצוע העבודה.

מינוי אחראים לביקורת

☐ אני ממנה בזה את הרשומים להלן להיות אחראים לביקורת על ביצוע עבודות בתחום הפעולה כרשום ליד שמם

	שם משפחה שם פרטי	תחום פעילות	המען	פרטי התקשרות
1.				
2.				
3.				

אני מצהיר כי טרם מיניתי אחראי/ת לביקורת על ביצוע עבודות הבנייה את כולם או את קצתם בתחומים האלה: שלד ובנייה
ומתחייב לעשות זאת כמפורט בתקנות, ולהודיע על כך לרשות הרישוי המקומית טרם התחלת ביצוע העבודה.

חתימת המבקש על המינויים צנ

יג. הצהרות

הצהרות עורכי הבקשה כולל הצהרות עורך הבקשה על לחץ המים

אנו החתומים מטה מצהירים בזה:
1) כל אחד מאתנו מאשר שהאמור בנוגע לרשימה שבסעיף י"ב לעיל הוא נכון.
2) כל אחד מאתנו מסכים לקבל עליו את התפקיד המיועד לו בסעיף י"ב לעיל.
3) אנו מצהירים, כל אחד בנוגע לתחום פעולתו, שיש לנו כישורים מקצועיים לערוך בקשה זו וכי בדקנו את המסמכים הנודעים לבקשה, לרבות כל תכנית הנוגעת לבקשה, וידוע לנו כי אם הצהרה זו אינה נכונה, הרי היא תיחשב מסירת ידיעה שהיא כוזבת או מטעה בפרט חשוב, כמשמעותה בסעיף 214 לחוק, וצפויים לנו העונשים הקבועים לפי כל דין.

אני פדרמן אליה (עורך בקשה ראשי) אחרי/ת לכך שהבקשה, ובכלל זה נספחיה, נערכה לפי מיטב הידיעה המקצועית ובהתאם לכל חיקוק החל על הבניין או העבודה המוצעת, שכל הנתונים שנמסרו על ידי בבקשה זו נכונים ושהתכנון המוצע תואם את כל התכניות, פרט לסטיות שפורטו לעיל.

☐ אני עורך הבקשה מתכנן האינסטלציה הסניטרית, מצהיר בזאת ואחרי לכך שתכניות הבקשה בכל הנוגע לסידורים הסניטריים נערכו כדין וכי קויימו בהן הוראות החוק וההוראות למתקני תברואה התש"ל 1970 (הל"ת) לעניין זה, לרבות בדיקת לחץ המים הקיים בבניין ותיכנון בהתאם.

	תאריך	שם משפחה שם פרטי	מספר רישיון	חתימה
עורך ראשי	6.7.20	פדרמן אליה	33662	

הצהרת מתכנן שלד הבניין

אני החתום מטה חן אילה מס' זהות 052015443
מהנדס רשוי מס' 20678
או הנדסאי בעל רישוי מס' ______ ("למבנה פשוט") מצהיר בזאת כדלקמן:
1) אני מסכים להיות מתכנן שלד הבניין הנדון בבקשה ולפקח פיקוח עליון על הקמת השלד.
2) כל אחד מאתנו מסכים לקבל עליו את התפקיד המיועד לו בסעיף י"ב לעיל.
3) ידוע לי, שאם אחרי הגשת הנתונים הסטטיים יתגלה צורך בשינוי מהותי בהם, אני מתחייב להגיש חישובים סטטיים מתוקנים מיד עם גילוי הצורך בכך.
4) אני מצהיר, כי יש לי כישרים מקצועיים לערוך בקשה זו וכי בדקתי את כל המסמכים הנוגעים לבקשה, לרבות כל תכנית הנוגעת לבקשה, וידוע לי כי אם הצהרה זו אינה נכונה, הרי היא תיחשב מסירת ידיעה שהיא כוזבת או מטעה בפרט חשוב, כמשמעותה בסעיף 214 לחוק, וצפויים לי העונשים הקבועים לפי כל דין.
5) ידוע לי כי עלי לשמור את תכנית הקונסטרוקציה לתקופה של לא פחות מ10- שנים לאחר גמר הבניה.

תאריך 6.7.20 חתימה

הצהרת האחראי לביצוע שלד הבניין (כאשר מונה)

אני החתום מטה (שם משפחה ושם פרטי) ______ מס' זהות ______
מהנדס רשוי מס' ______ או הנדסאי בעל רישוי מס' ______ ("למבנה פשוט")
מצהיר בזאת כדלקמן:
1) אני מסכים להיות האחראי לבצוע שלד הבניין.
הבניין על פי תוכניות והוראות של מתכנן השלד כפי שיינתנו בכתב וכן למלא את תפקידי על פי שנקבע בכל חיקוק הנוגע להן.
2) אני מצהיר, כי יש לי כישרים מקצועיים להיות אחראי לבצוע שלד הבניין, ואני מתחייב לדאוג לביצוע שלד
תאריך ______ חתימה ______

הצהרת אחראים לביקורת (כאשר מונו)

אנו החתומים מטה מצהירים בזה:
1) כל אחד מאיתנו מאשר שהאמור בנוגע לו ברשימה שבסעיף י"ב לעיל הוא נכון.
2) כל אחד מאיתנו מסכים לקבל עליו את התפקיד המיועד לו בסעיף י"ב.
3) אנו מצהירים כל אחד בנוגע לתחום פעולתו, שיש לנו כישורים מקצועיים לערוך את הביקורת כהלכה ולדווח על תוצאותיה לרשות הרישוי המקומית, כמתחייב כל פי כל דין.
אני ______ (עורך הביקורת הראשי) אחראי/ת לכך שהביקורת תיערך על פי מיטב הידיעה המקצועית, ושכל הדיווחים לרשות הרישוי המקומית ייערכו על פי כל דין.

תאריך	שם משפחה שם פרטי	מספר רישיון	חתימה
___ / ___ / ___			
___ / ___ / ___			
___ / ___ / ___			
___ / ___ / ___			

שטחי מיגון ומרפסות בדירה

הקומה	מבנה	מפלס	דירה	עיקרי	ממ"ד/ ממ"ק/ מקלט עיקרי	ממ"ד/ ממ"ק/ מקלט שירות	ממ"ד/ ממ"ק/ מקלט קירות	סה"כ עיקרי שירות	סה"כ עיקרי שירות לדירה	גזוזטרה	מרפסת לא מקורה
קומה 3	1	0.00	2	18.6352				18.6352	18.6352		30.9237
מתחת לקרקע											
מעל הקרקע				18.64				18.64	18.64		30.92
סה"כ				18.64				18.64	18.64		30.92
שטח ממוצע									18.64		

אסמכתאות לקומות

מבנה	הקומה	מפלס	סוג	שטח	תב"ע \ הסבר	תיאור נוסף
1	3	0.00	תקנות התכנון והבניה	22.9728	3ג	

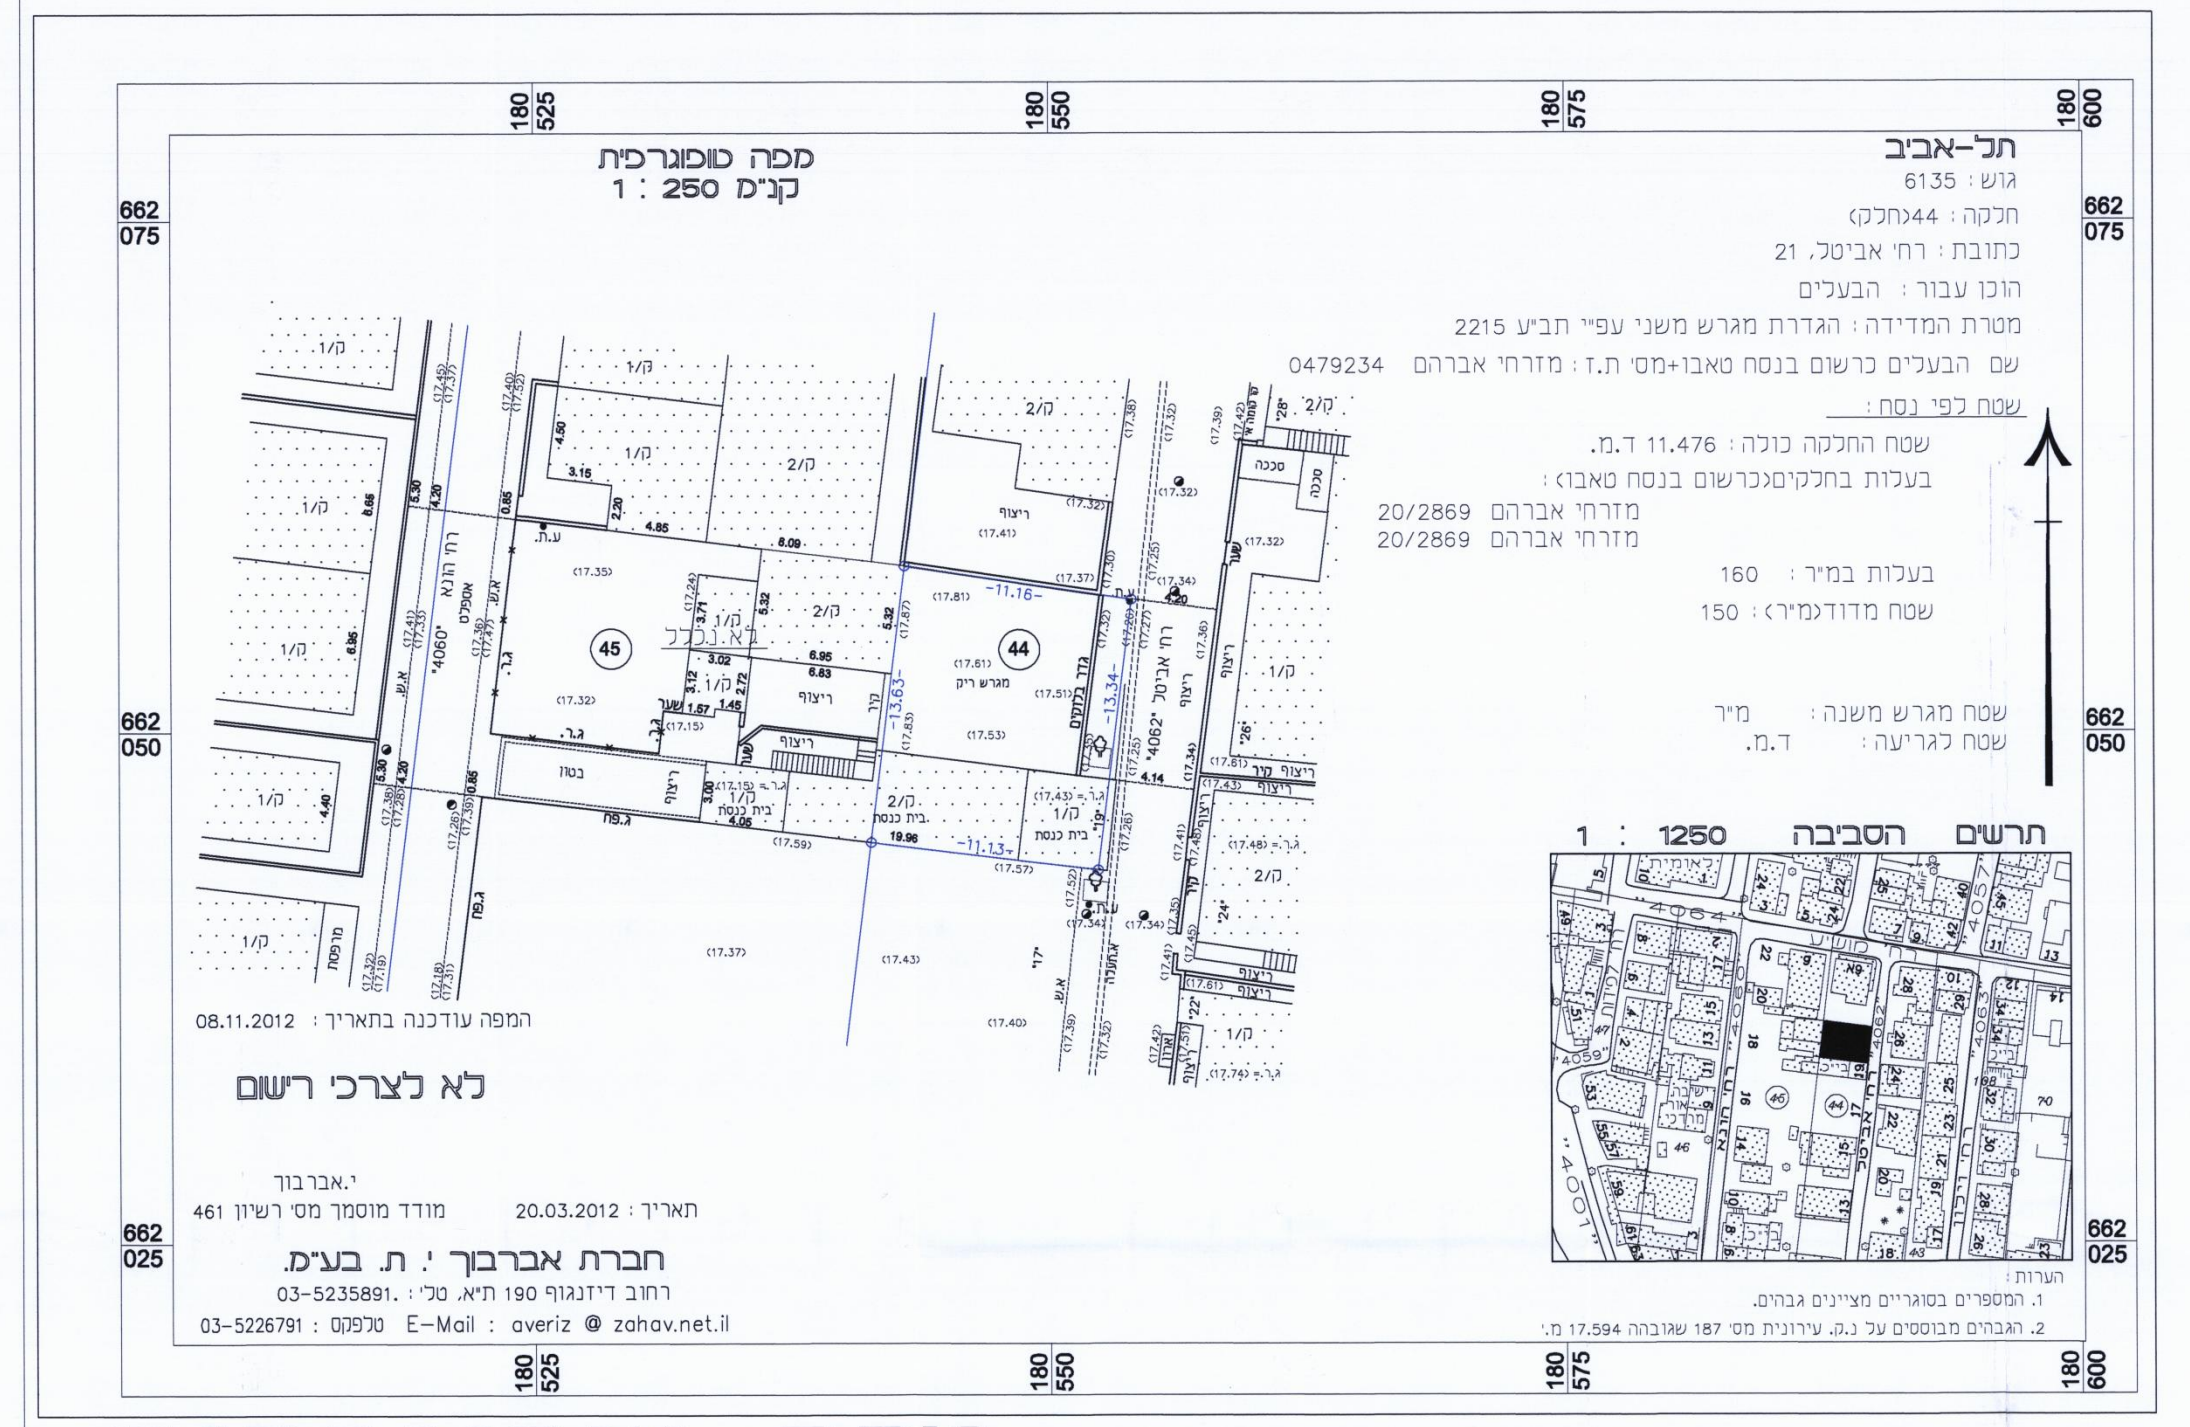
מפה טופוגרפית
קנ"מ 1 : 250
תל-אביב
גוש : 6135
חלקה : 44(חלק)
כתובת : רח' אביטל 21
הוכן עבור : הבעלים
מטרת המדידה : הגדרת מגרש משני עפ"י תב"ע 2215
שם הבעלים כרשום בנסח טאבו+מס' ת.ז : מזרחי אברהם 0479234
שטח לפי נסח
שטח החלקה כולה : 11.476 ד.מ.
בעלות בחלקים(כרשום בנסח טאבו)
מזרחי אברהם 20/2869
מזרחי אברהם 20/2869
בעלות במיר : 160
שטח מדוד(מ"ר) : 150
שטח מגרש משנה : מ"ר
שטח לגריעה : ד.מ.
תרשים הסביבה 1 : 1250
המפה עודכנה בתאריך : 08.11.2012
לא לצרכי רישום
י.אברבוך
מודד מוסמך מס' רשיון 461
תאריך : 20.03.2012
חברת אברבוך י. ת. בע"מ.
רחוב דיזנגוף 190 ת"א. טל': 03-5235891.
03-5226791 : טלפקס E-Mail : overiz @ zahov.net.il

מפה טופוגרפית

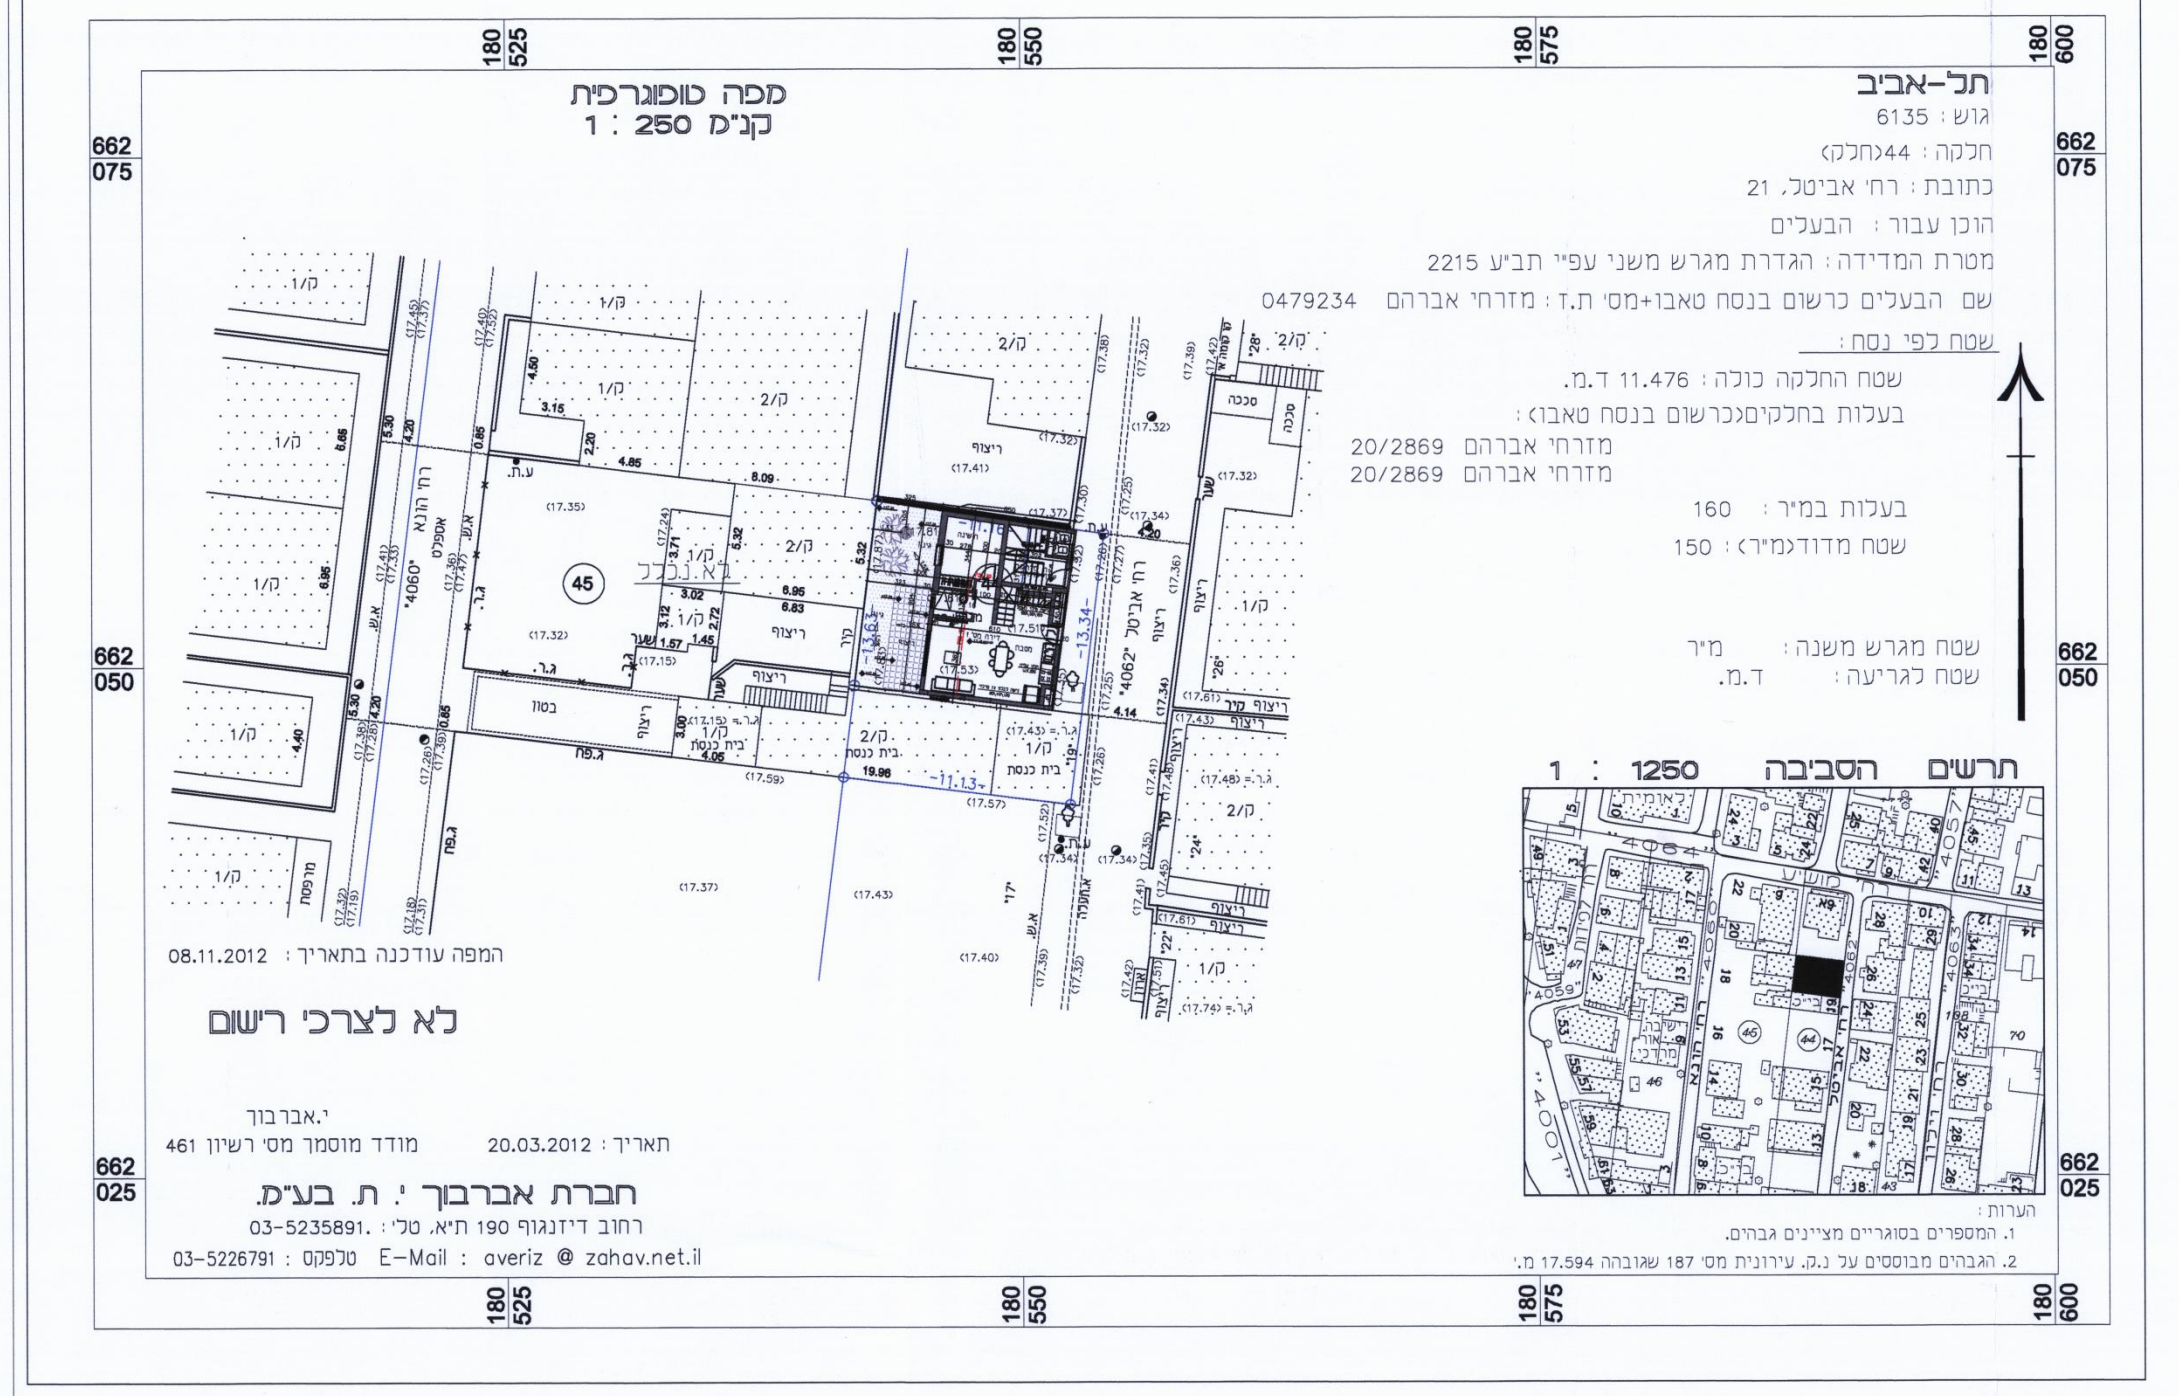
מפה טופוגרפית
קנ"מ 1 : 250
תל-אביב
לא לצרכי רישום
חברת אברבוך י. ת. בע"מ.

תוכנית העמדה

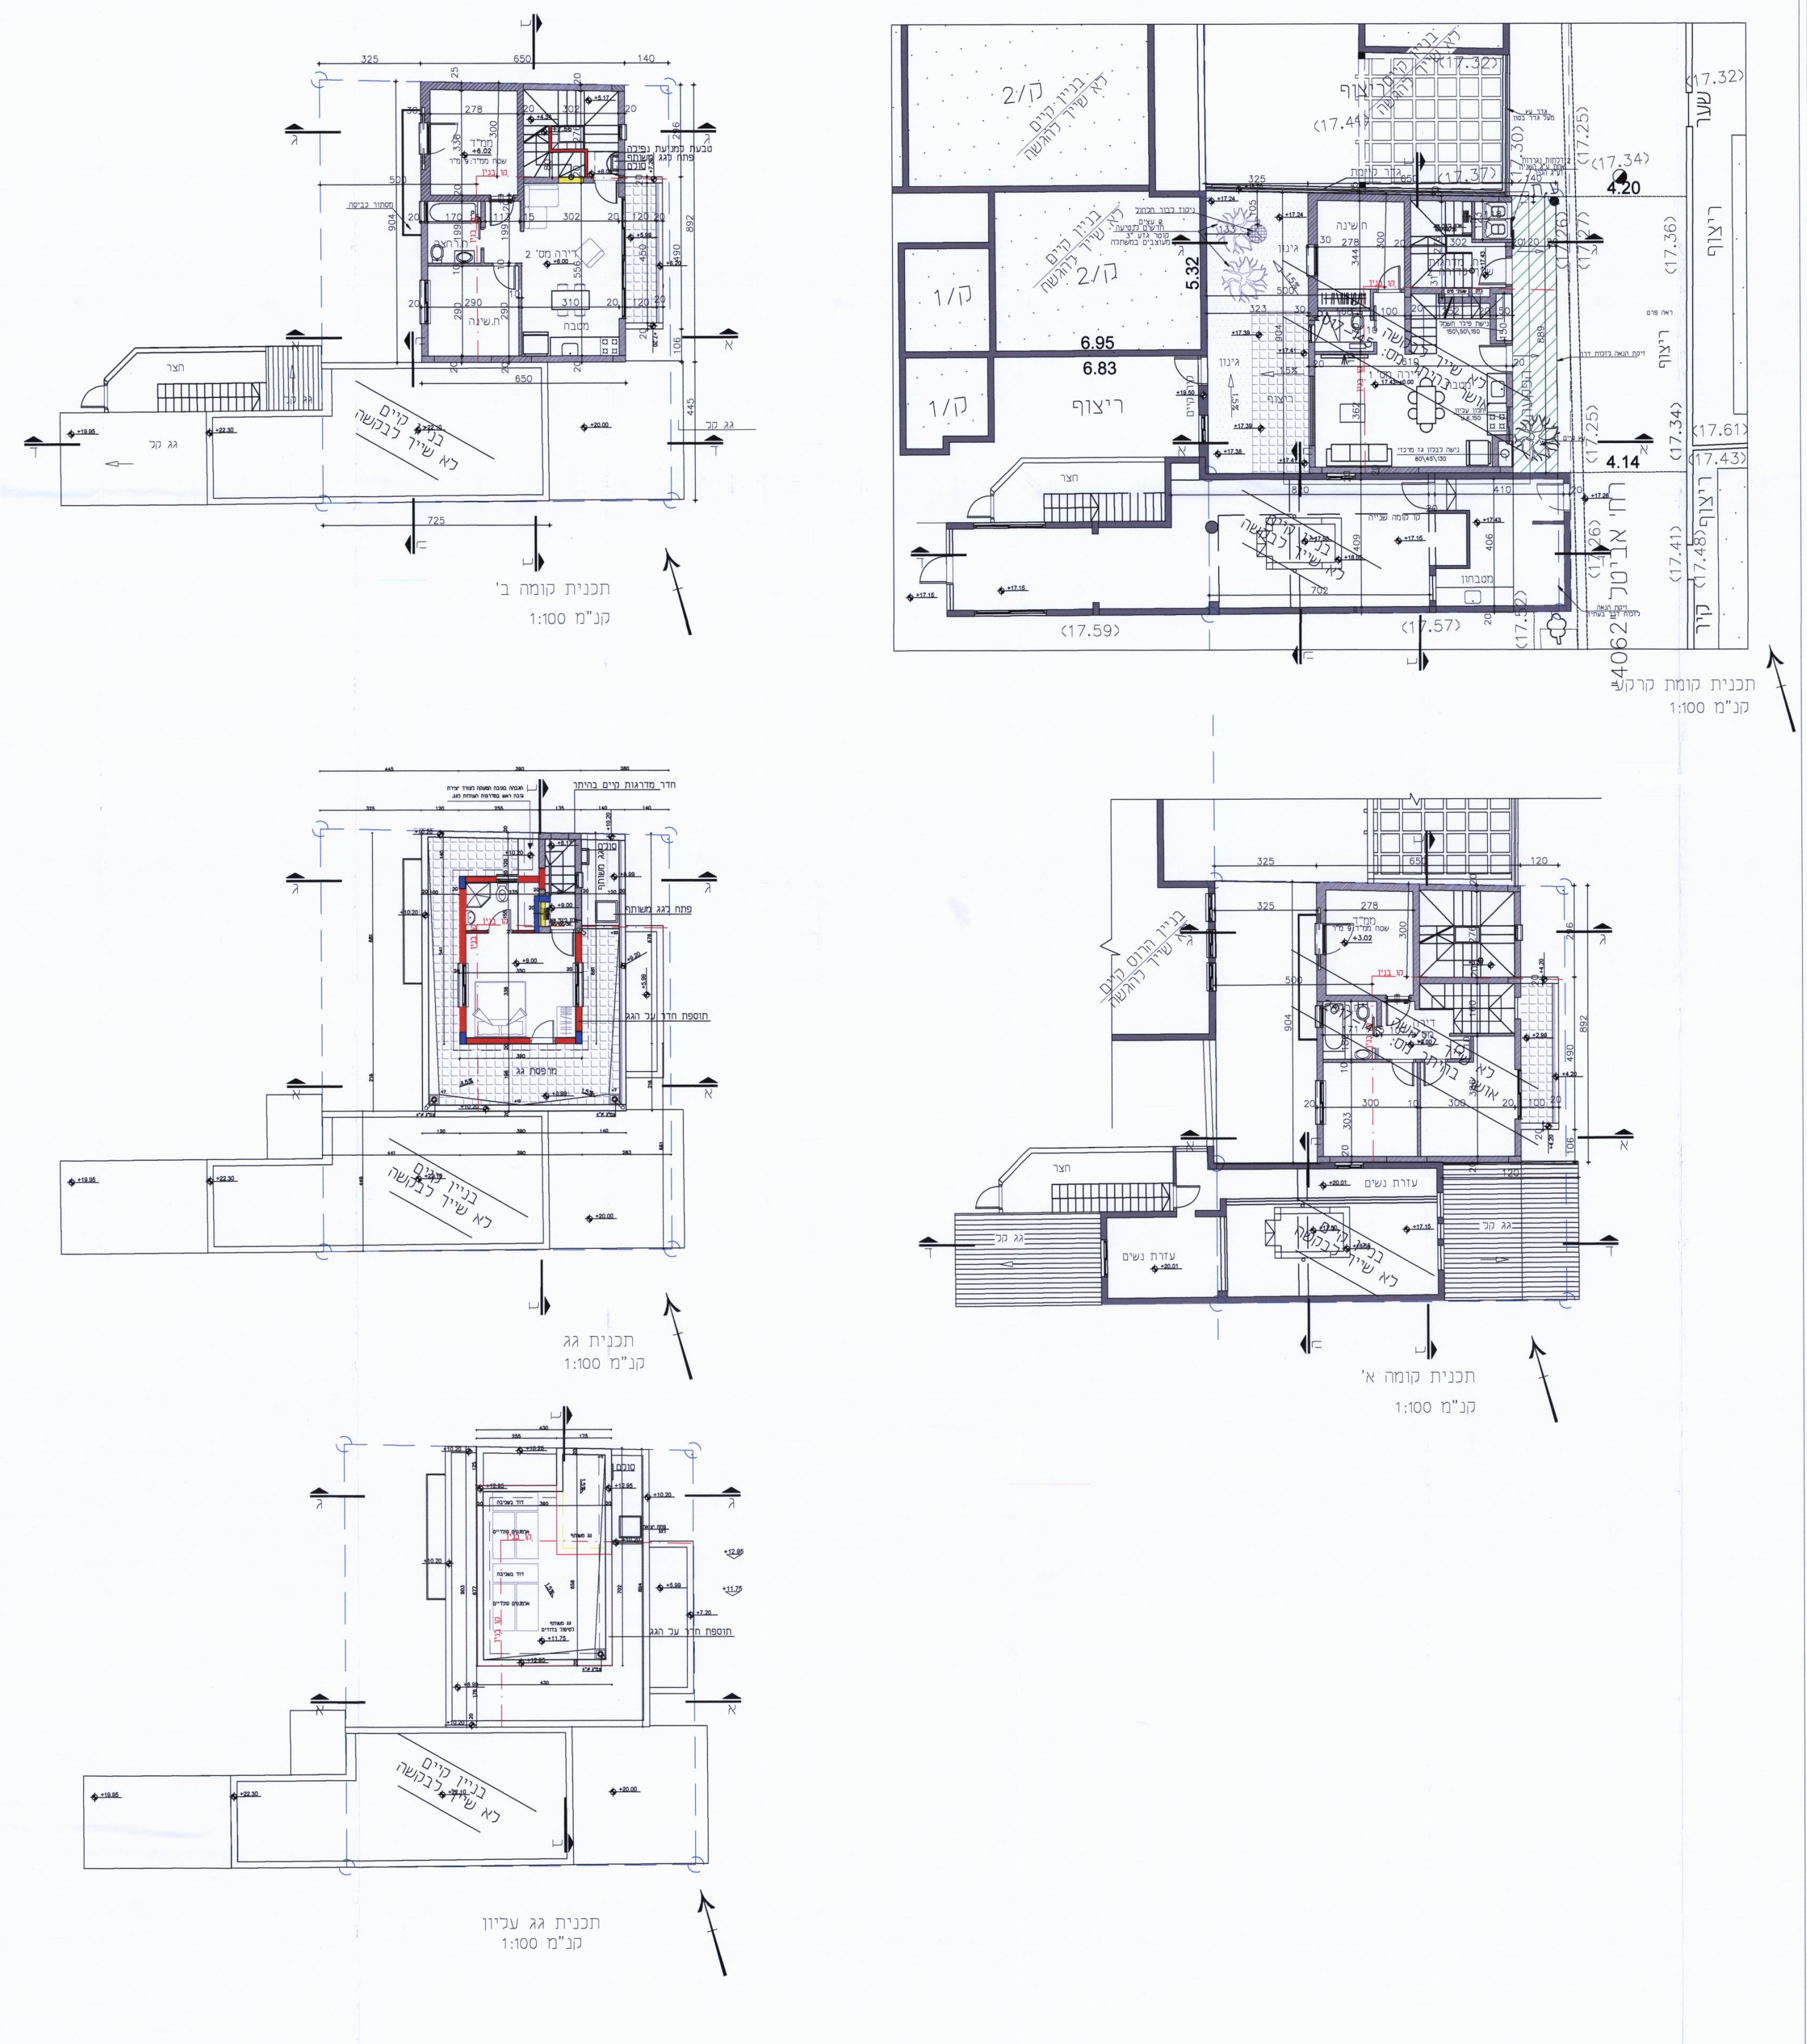
תכנית קומת קרקע
קנ"מ 1:100
תכנית קומה א'
קנ"מ 1:100
תכנית קומה ב'
קנ"מ 1:100
תכנית גג
קנ"מ 1:100
תכנית גג עליון
קנ"מ 1:100
ריצוף
רח' אביטל
6.95
6.83
4.20
4.14
5.32
בניין קיים לא שייך לבקשה

תוכניות

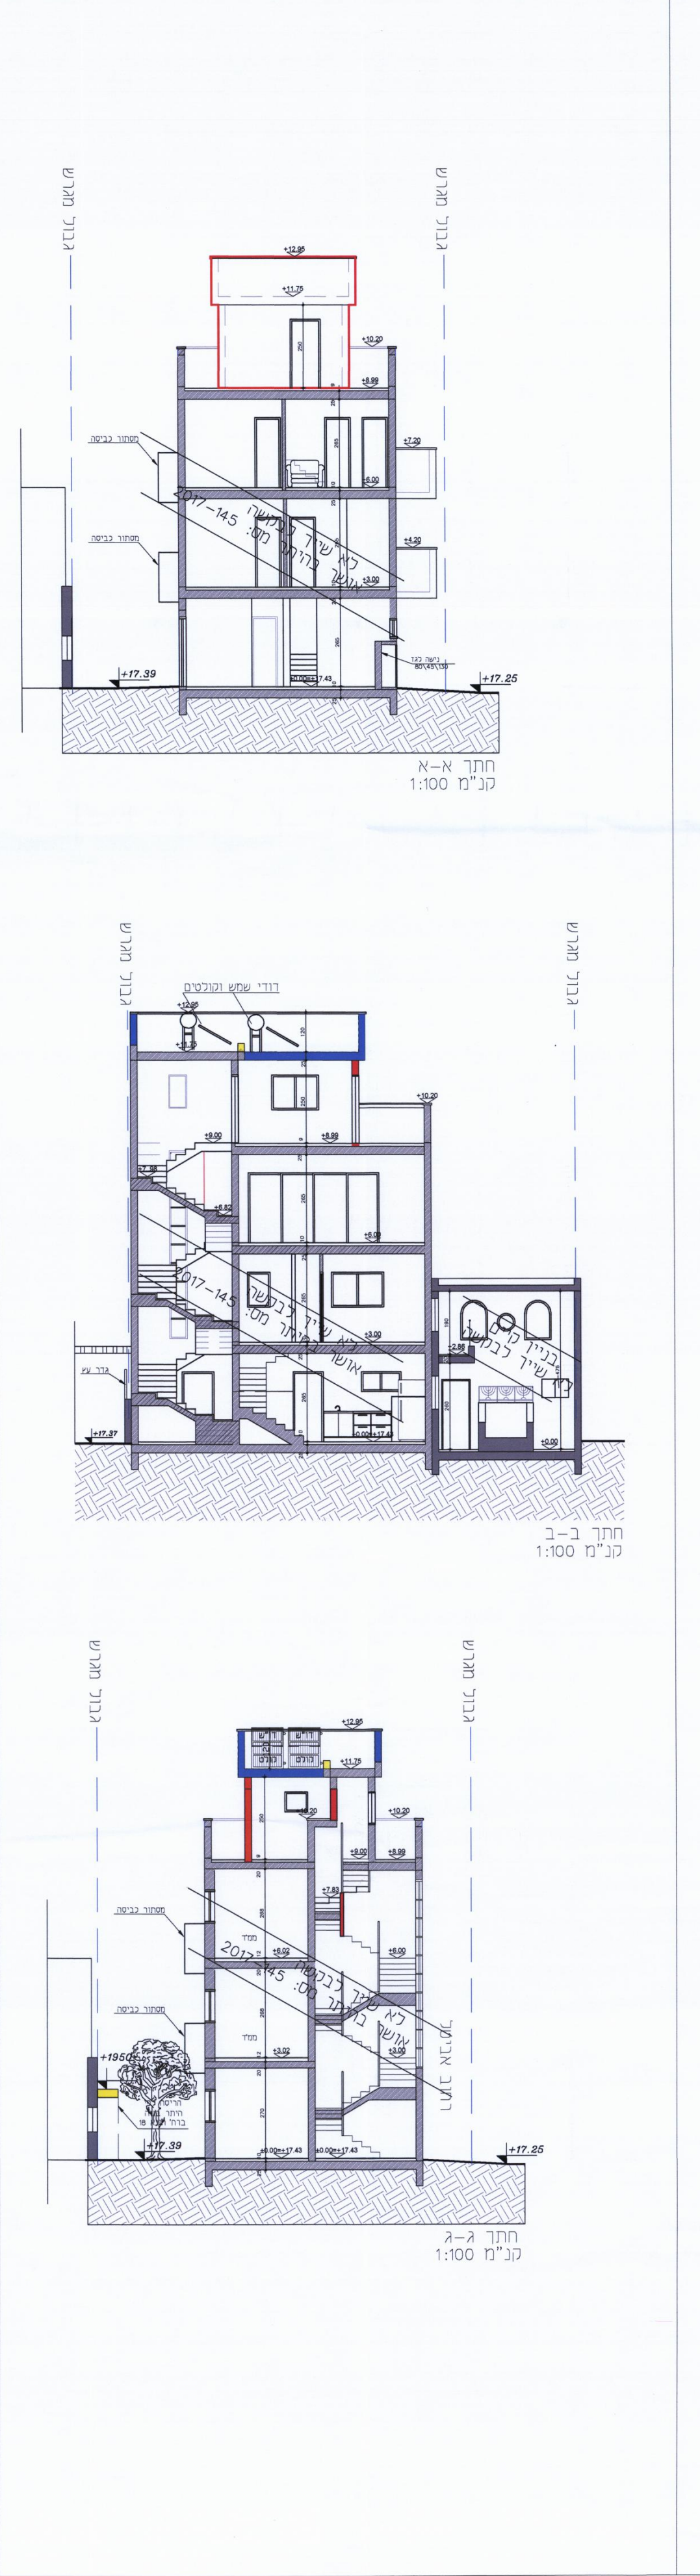
חתך א-א
קנ"מ 1:100
חתך ב-ב
קנ"מ 1:100
חתך ג-ג
קנ"מ 1:100
לא שייך לבקשה אושר בהיתר מס: 2017-145

חתכים

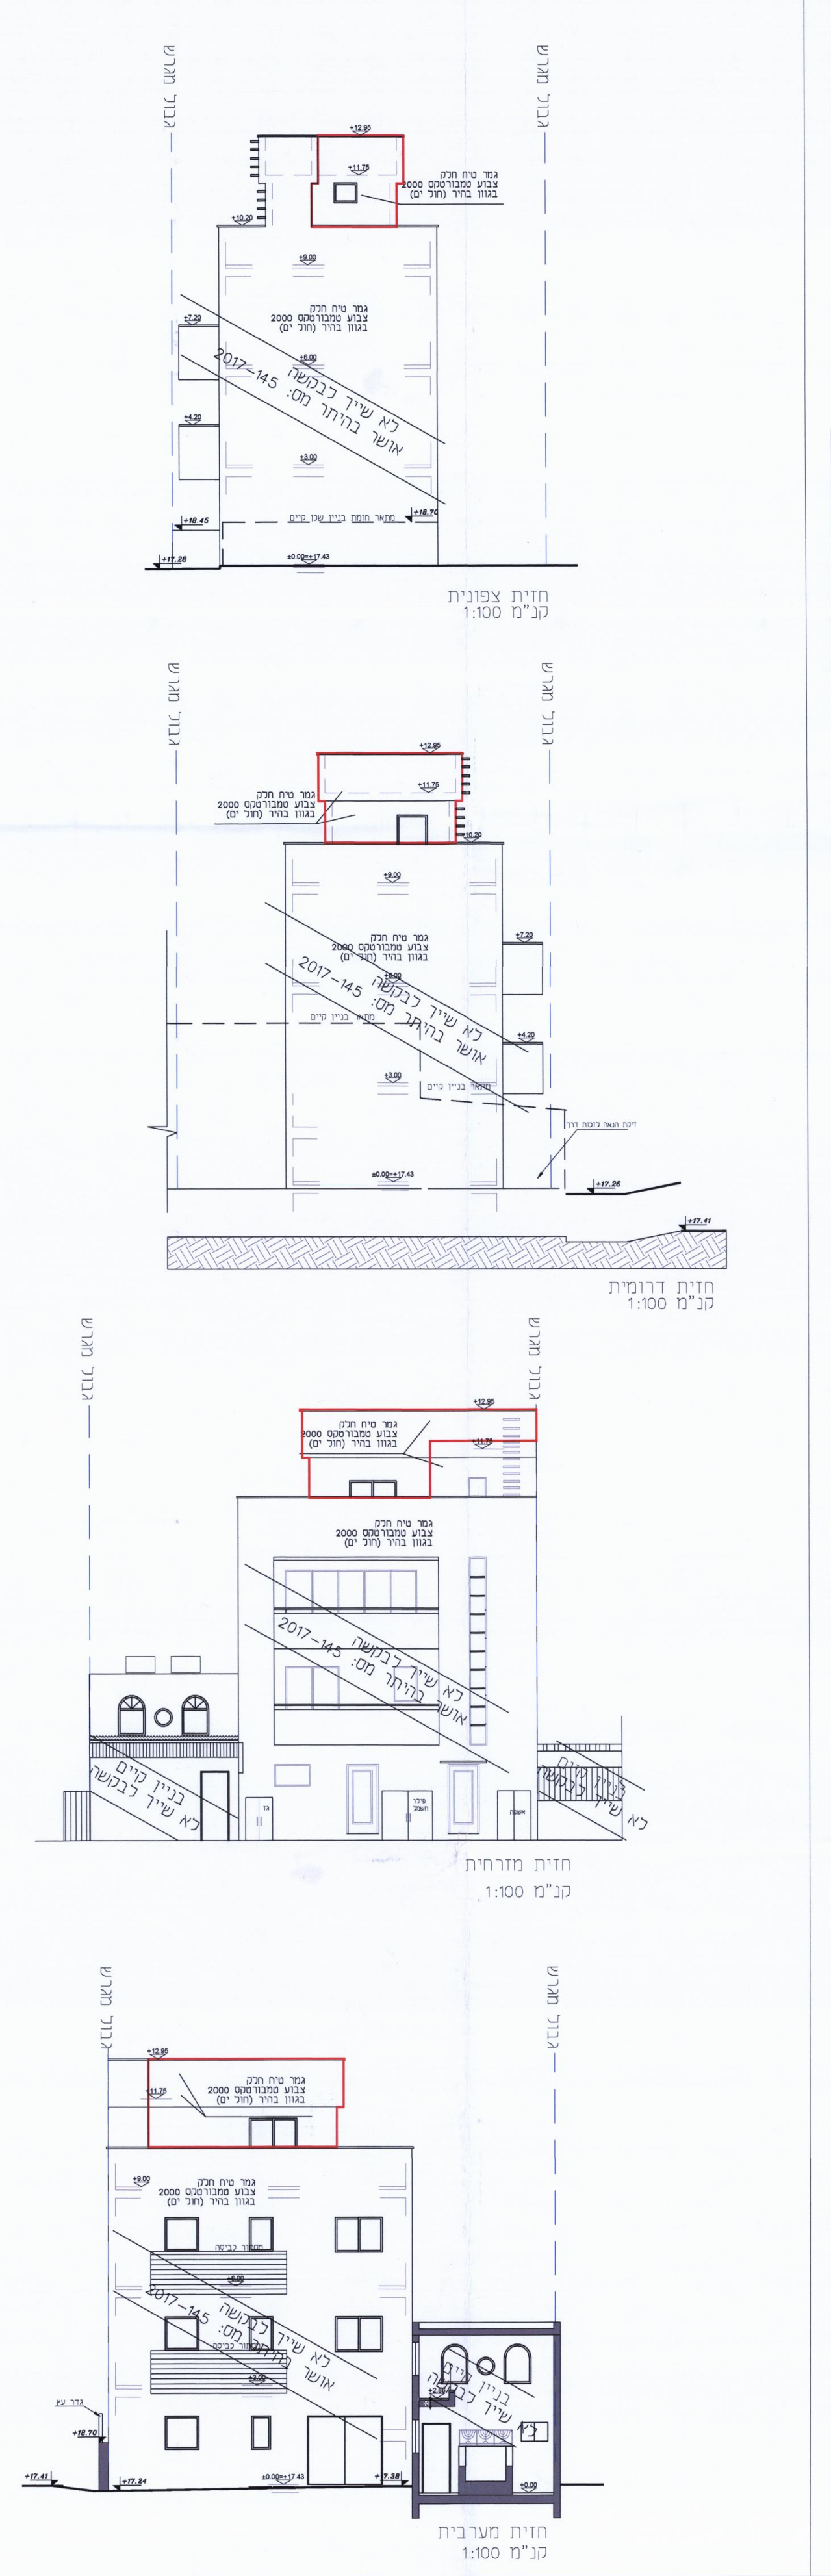
חזית צפונית
קנ"מ 1:100
חזית דרומית
קנ"מ 1:100
חזית מזרחית
קנ"מ 1:100
חזית מערבית
קנ"מ 1:100
גמר טיח חלק צבוע מתבורטקס 2000 בגוון בהיר (חול ים)
לא שייך לבקשה אושר בהיתר מס: 2017-145

חזיתות

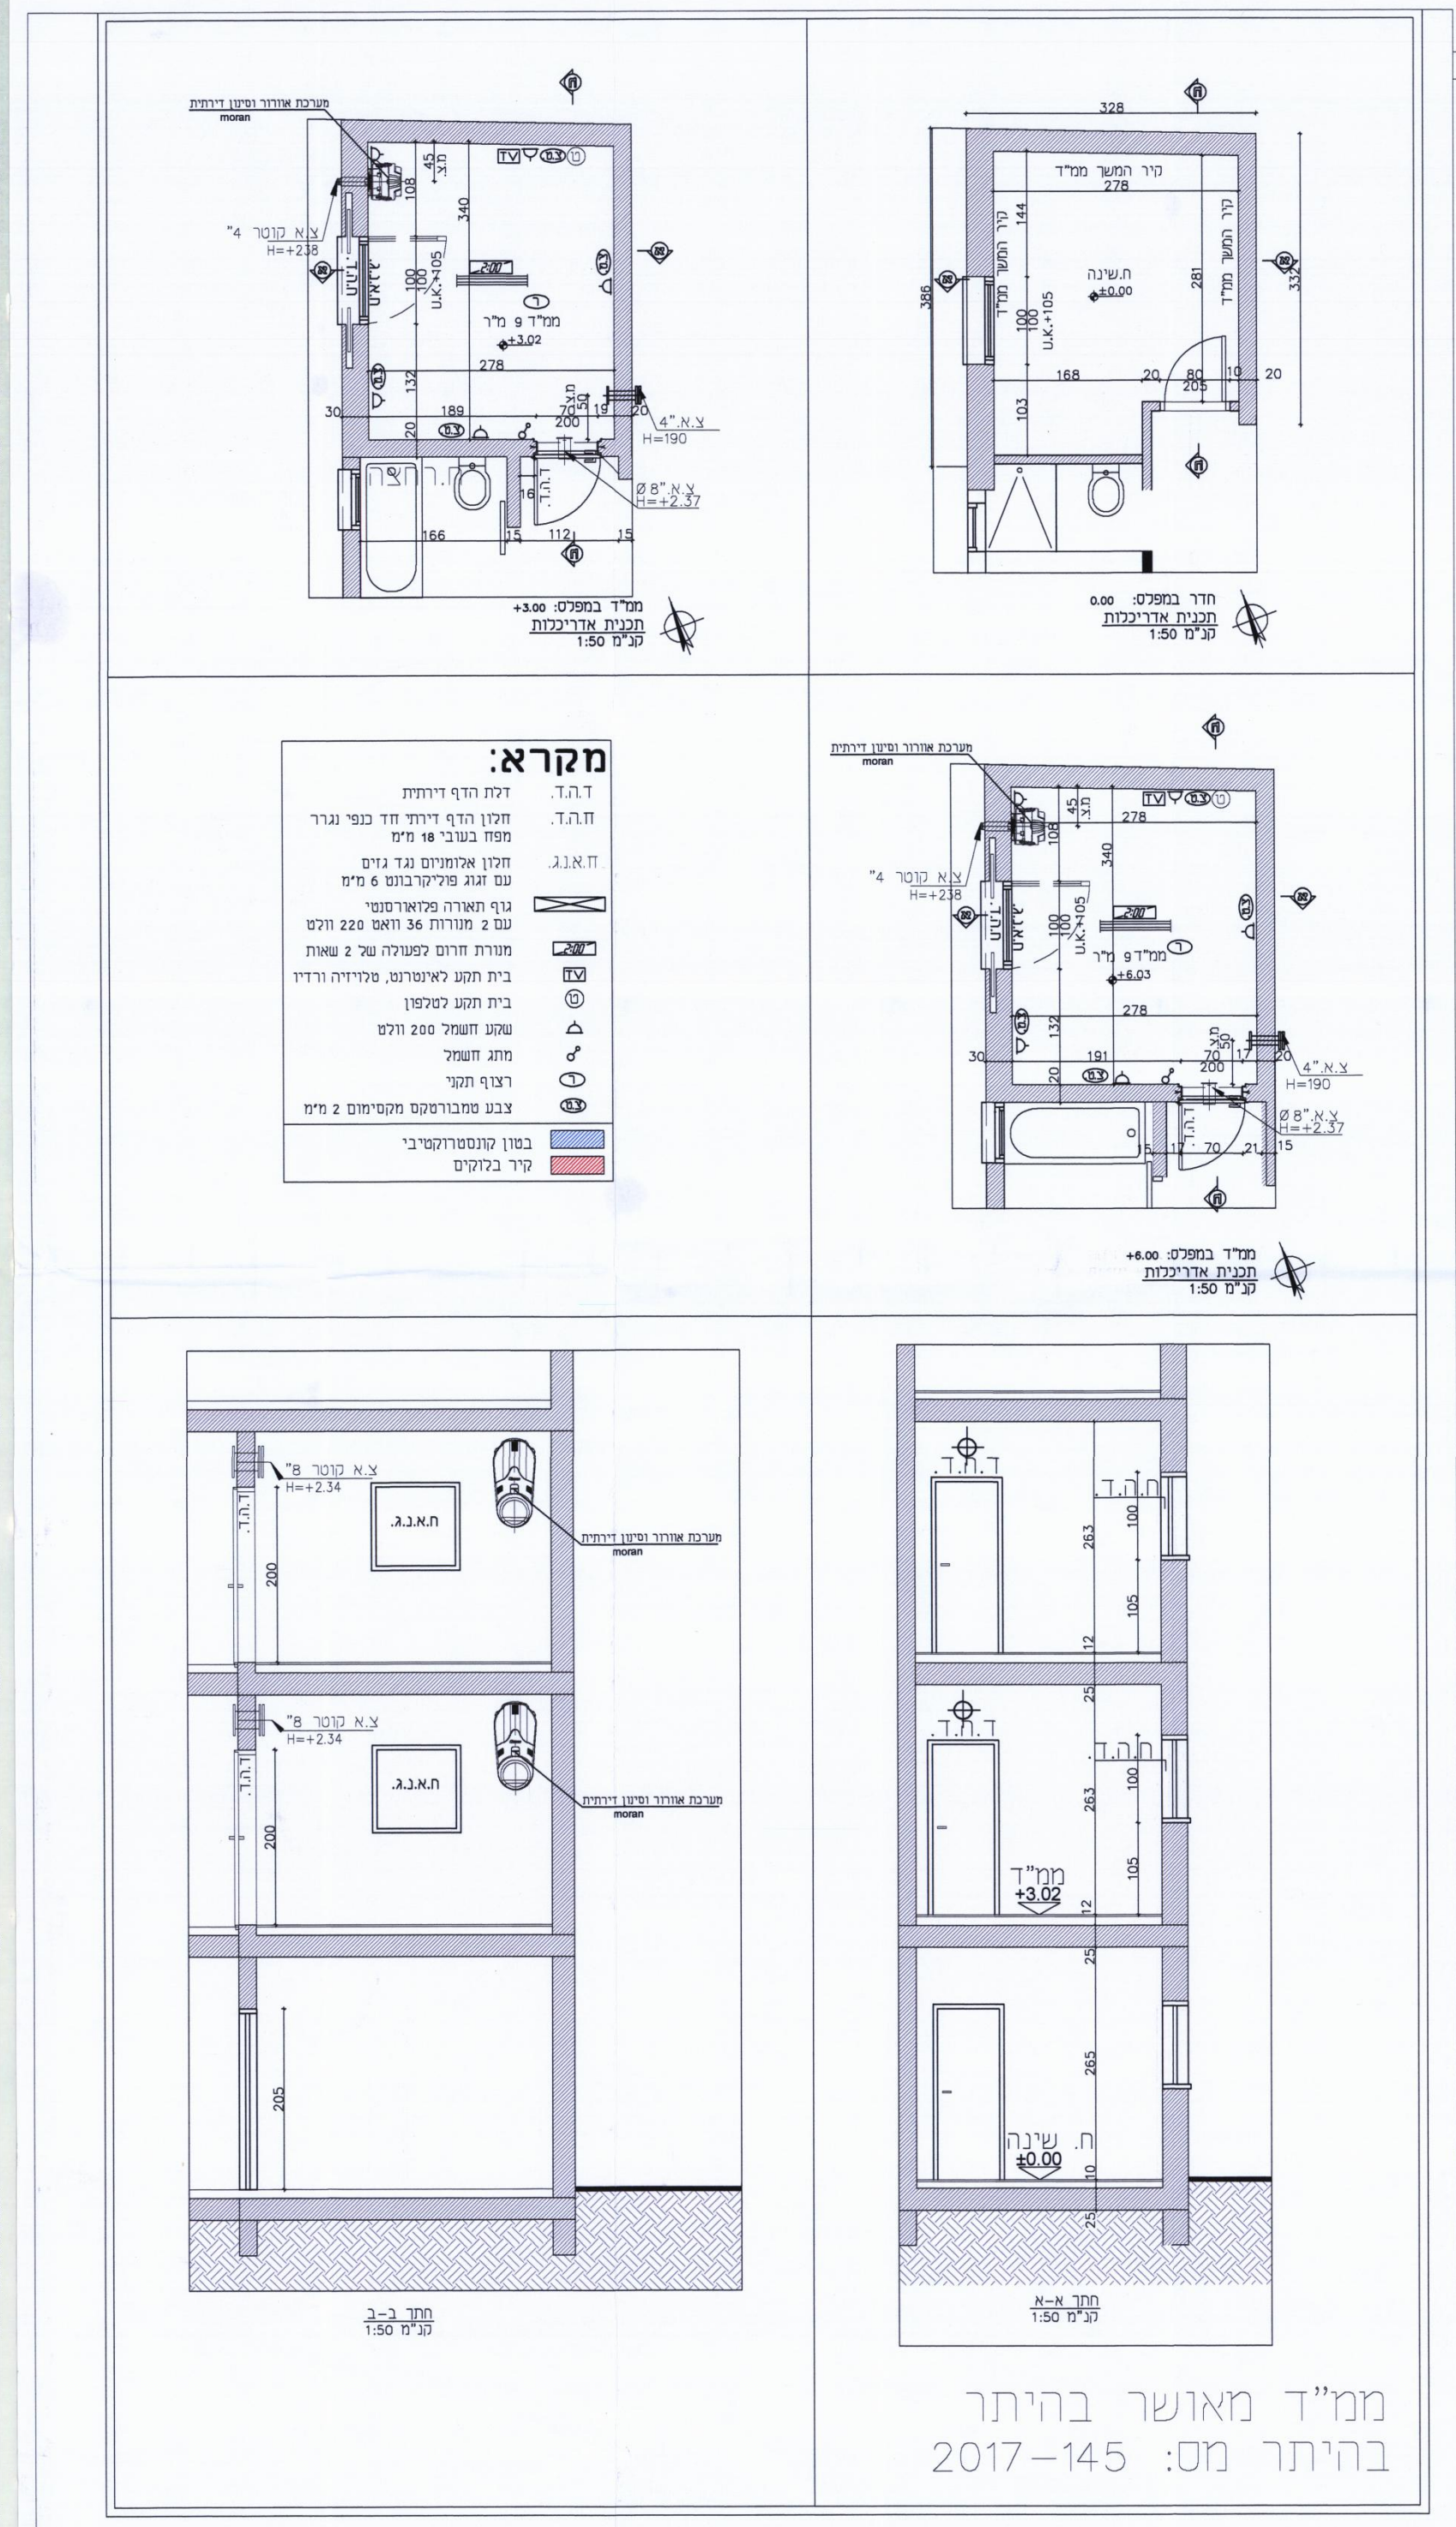
מקרא:
ד.ה.ד. דלת הדף דירתית
ח.ה.ד. חלון הדף דירתי חד כנפי נגרר
ח.א.נ.ג. חלון אלומיניום נגד גזים
בטון קונסטרוקטיבי
קיר בלוקים
ממ"ד במפלס +3.00 תכנית אדריכלות קנ"מ 1:50
חדר במפלס 0.00 תכנית אדריכלות קנ"מ 1:50
ממ"ד במפלס +6.00 תכנית אדריכלות קנ"מ 1:50
חתך ב-ב קנ"מ 1:50
חתך א-א קנ"מ 1:50

ממ"ד מאושר בהיתר
בהיתר מס: 2017-145

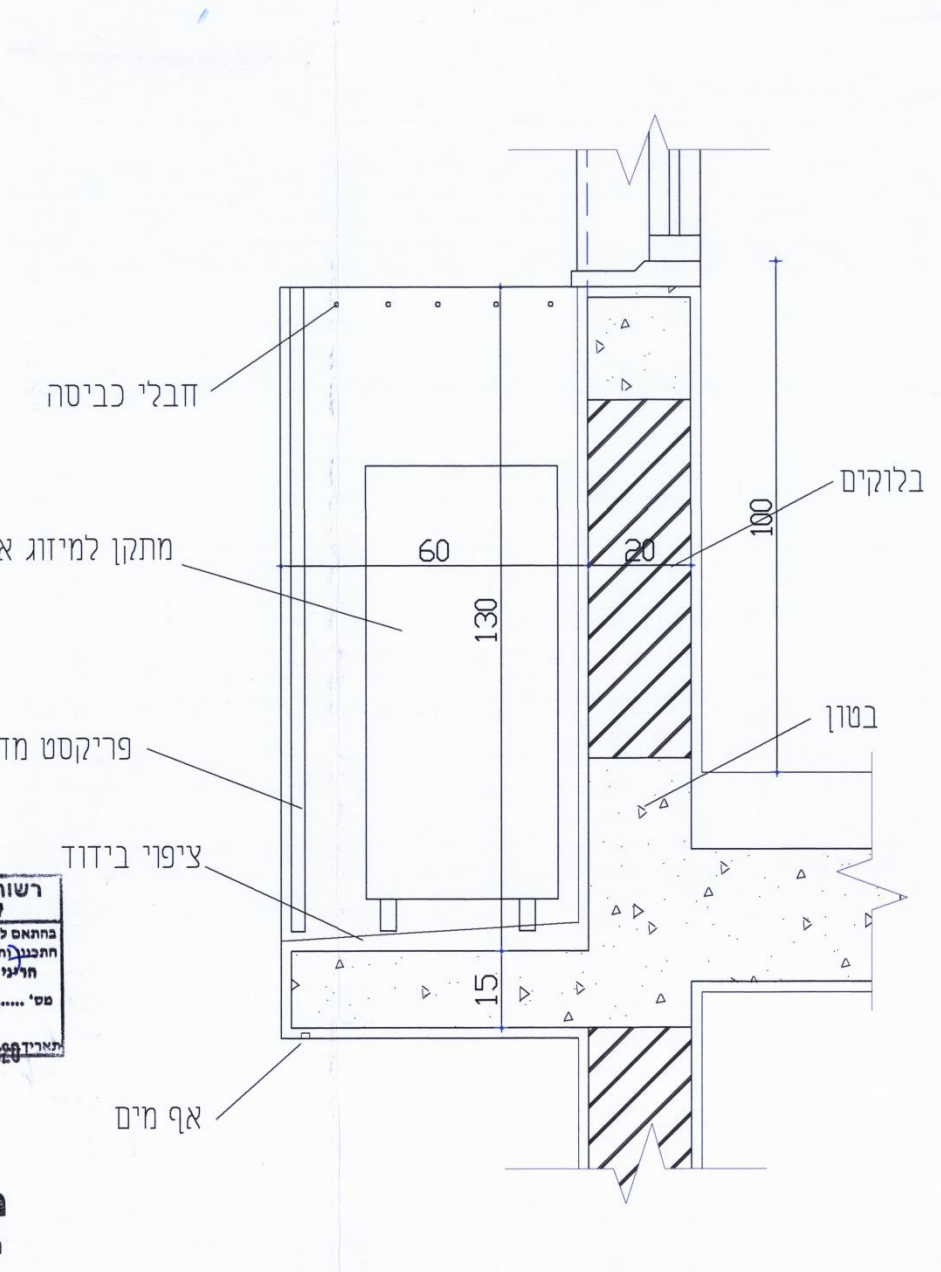
חבלי כביסה
בלוקים
מתקן למיזוג אויר
פריקסט מחורר
בטון
ציפוי בידוד
אף מים
60
130
100
20
15
סוף המסתור

פרט מסתור כביסה ומזגנים
קנה מידה 1:20

רשות רישוי מקומית לתכנון ולבניה למרחב תכנון תל-אביב-יפו
מינהל הנדסה
אגף רישוי בניה
העתק מאושר
חתימה