סוף מסמך

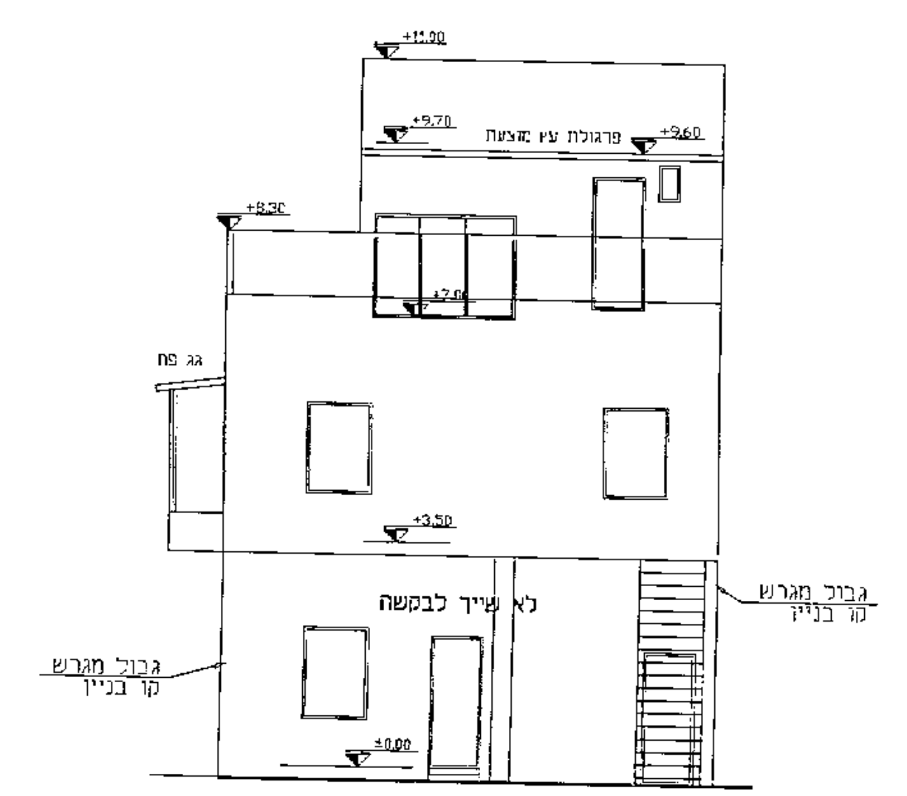
+11.00
+9.70
פרגולת עץ מוצעת
+9.60
+8.20
+7.00
גג פח
+3.50
לא שייך לבקשה
גבול מגרש
קו בניין
±0.00

חזית לרח' אביטל ק.מ.1:100

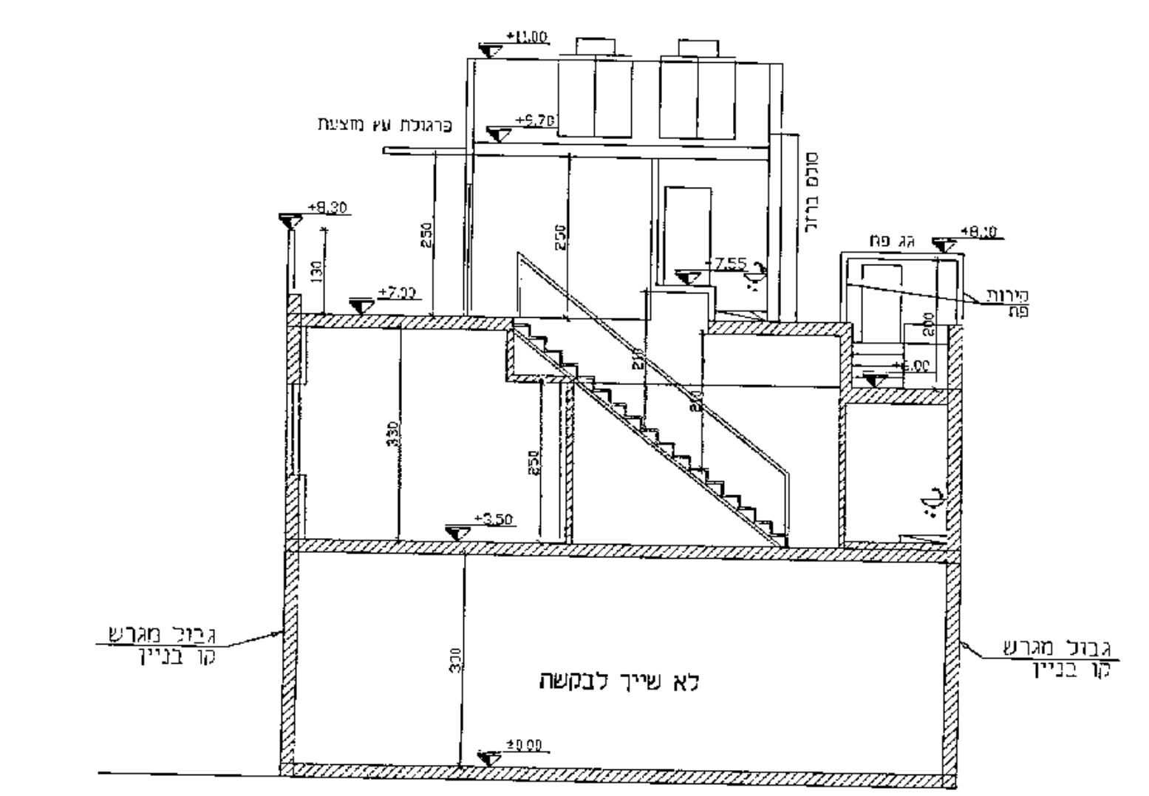
+11.00
פרגולת עץ מוצעת
+9.70
+8.20
+7.00
+7.55
+8.10
+3.50
לא שייך לבקשה
גבול מגרש
קו בניין
±0.00

חתך א-א ק.מ.1:100

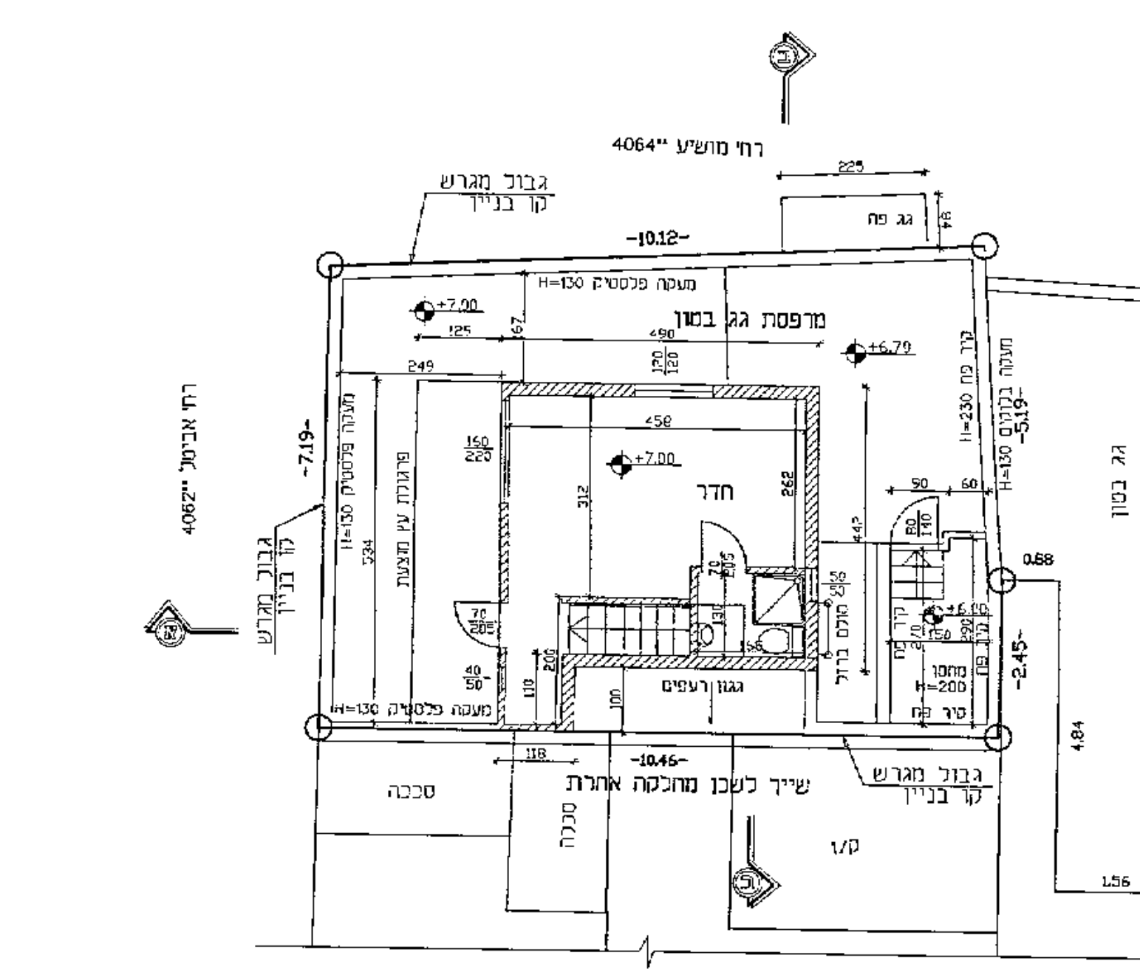
רח' מושיע 4064"
רח' אביטל 4062"
גבול מגרש
קו בניין
מרפסת גג בטון
חדר
גגון רעפים
סככה
שייך לשכן מחלקה אחרת
גג בטון
1/ק
-10.12-
-10.46-
-7.19-
-5.19-
-2.45-
א

תכנית קומת גג ק.מ.1:100

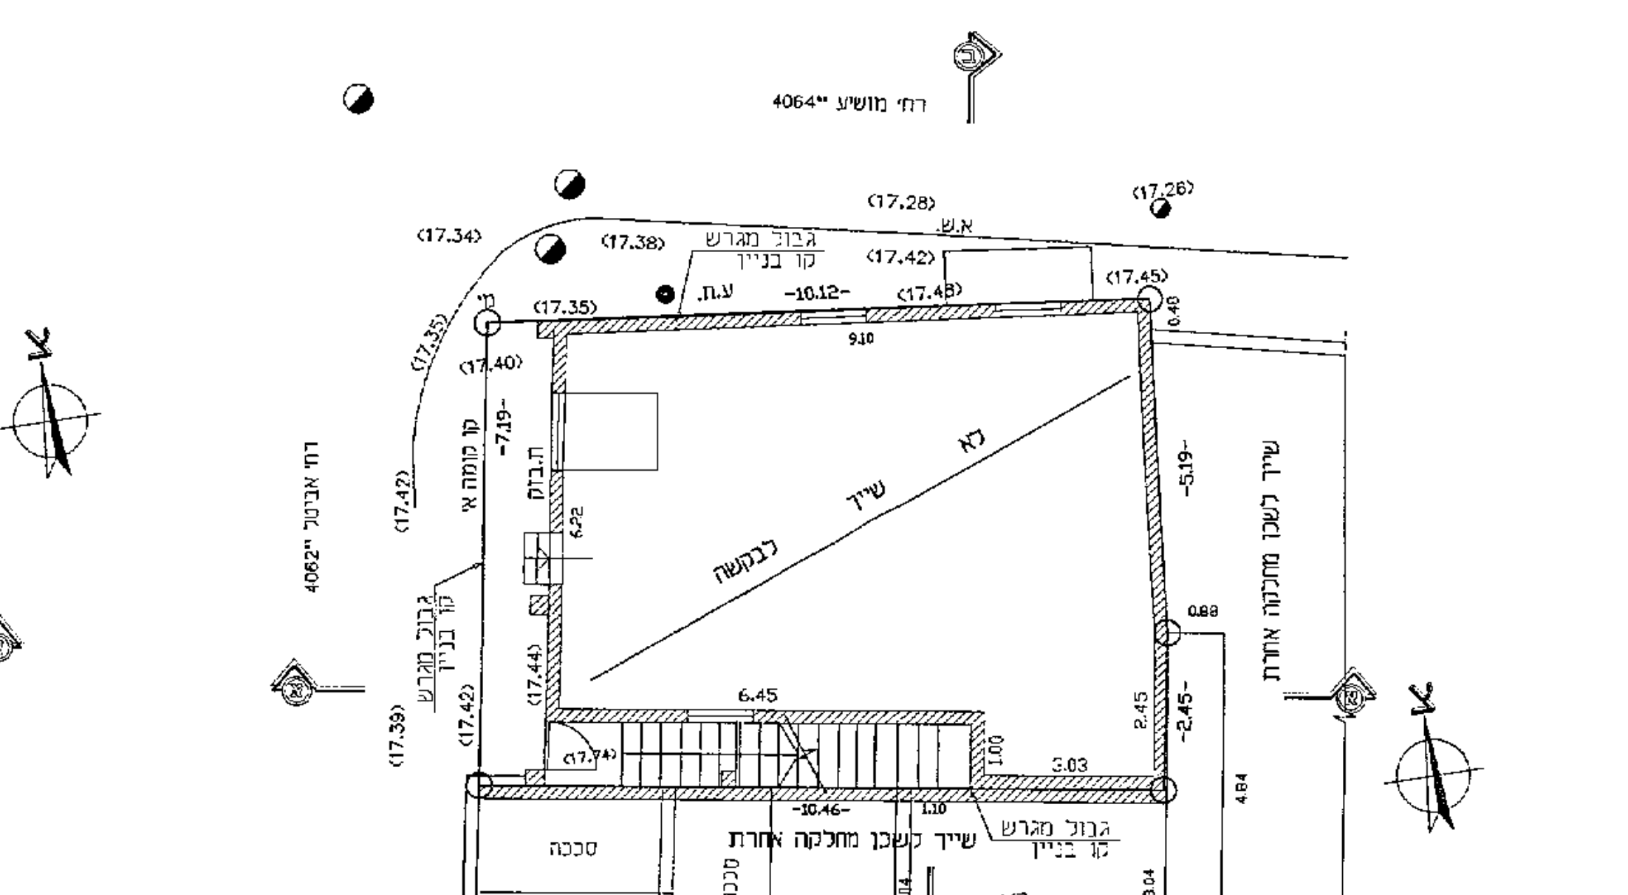
רח' מושיע 4064"
רח' אביטל 4062"
גבול מגרש
קו בניין
לא שייך לבקשה
סככה
שייך לשכן מחלקה אחרת
1/ק
3/ק
-10.12-
-10.46-
-7.19-
-5.19-
-2.45-
(17.28)
(17.26)
(17.34)
(17.38)
(17.42)
(17.45)
(17.48)
(17.35)
(17.40)
(17.44)
(17.39)
א

תכנית ק.קרקע ק.מ.1:100

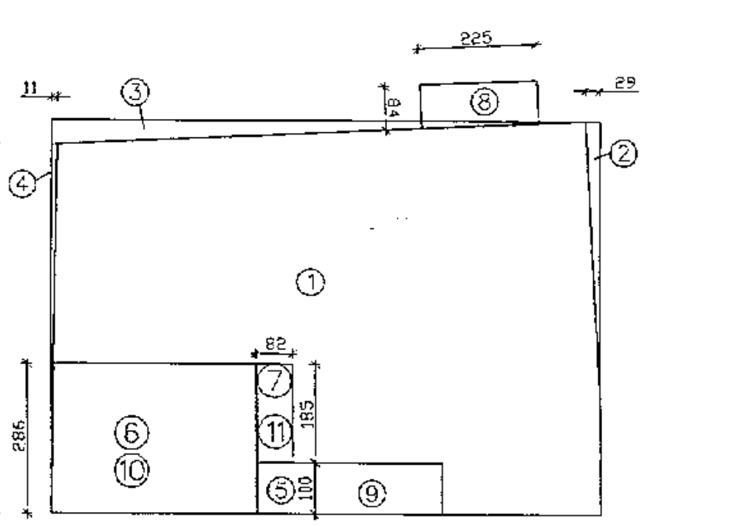
225
28
11
763
717
46
286
185
82
389
355
1050
①
②
③
④
⑤
⑥
⑦
⑧
⑨
⑩
⑪

חישוב שטחים

קומה א'

שטח דירה קיים

מסגרת
7.63x10.50=80.11 ①

הורדות
0.29x7.63=2.21 ②
0.46x10.50=4.83 ③
0.11x7.17=0.79 ④
1.00x3.55=3.55 ⑤
2.86x3.89=11.13 ⑥
0.82x1.85=1.52 ⑦
24.03

שטח דירה
80.11-24.03=56.08

מרפסת מקורה
2.25x0.84=1.89 ⑧

גגון כניסה
1.00x3.55=3.55 ⑨

ממ"ד
2.86x3.89=11.13 ⑩
0.82x1.85=1.52 ⑪

ס"כ שטח ממ"ד
11.13+1.52=12.65

ס"כ שטח דירה
56.08+1.89+3.55+12.65=74.17

קומת גג

חדר על הגג
4.90x4.42=21.66 ①
1.18x1.00=1.18 ②
22.84

פרגולה
1.29x5.34=6.89 ③

ס"כ שטח דירה לאחר תוספת
74.17+22.84=97.01

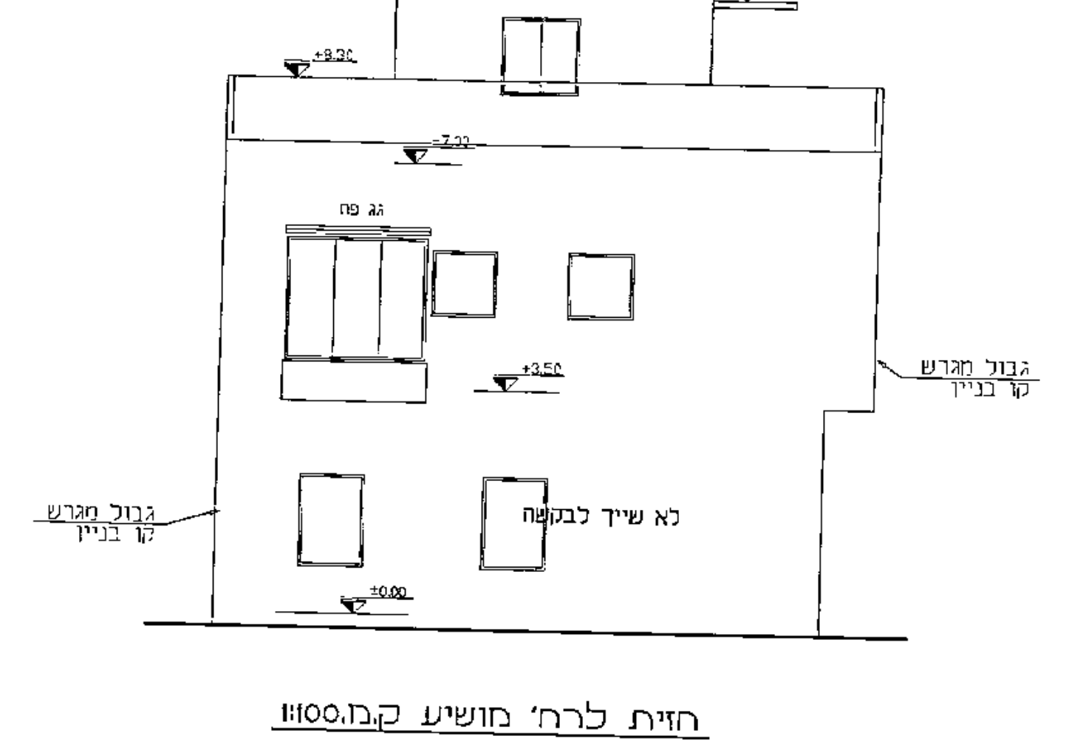
+11.00
+9.70
פרגולת עץ מוצעת
+9.62
+8.20
+7.00
גג פח
+3.50
לא שייך לבקשה
גבול מגרש
קו בניין
±0.00

חזית לרח' מושיע ק.מ.1:100

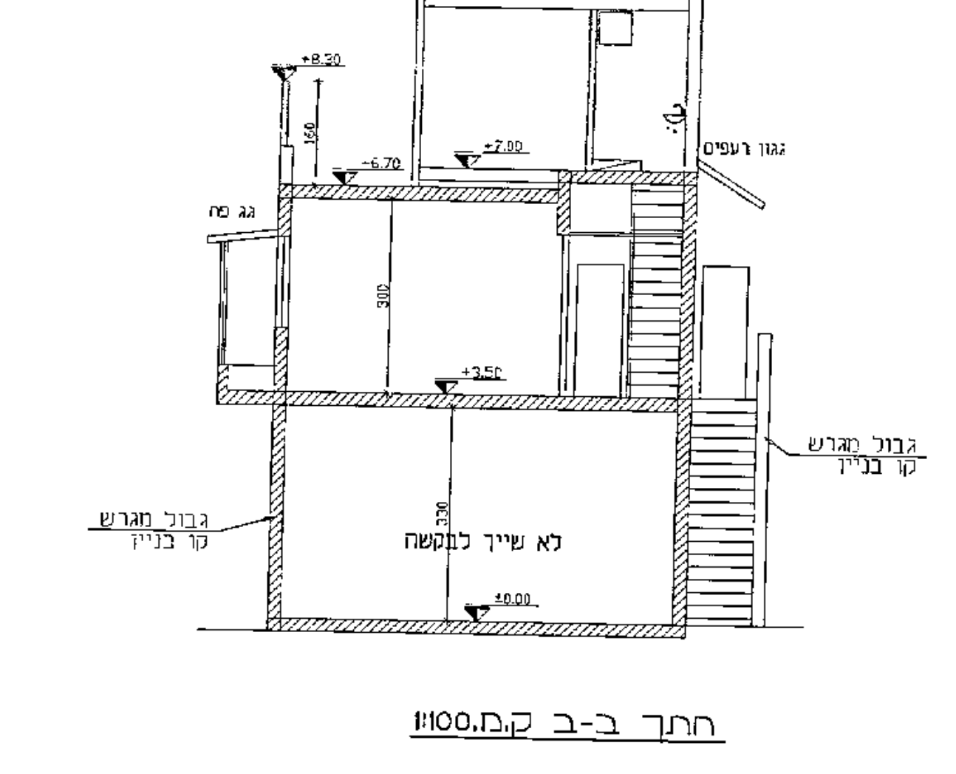
+11.00
+9.72
+8.20
+7.00
+6.70
גג פח
גגון רעפים
+3.50
לא שייך לבקשה
גבול מגרש
קו בניין
±0.00

חתך ב-ב ק.מ.1:100

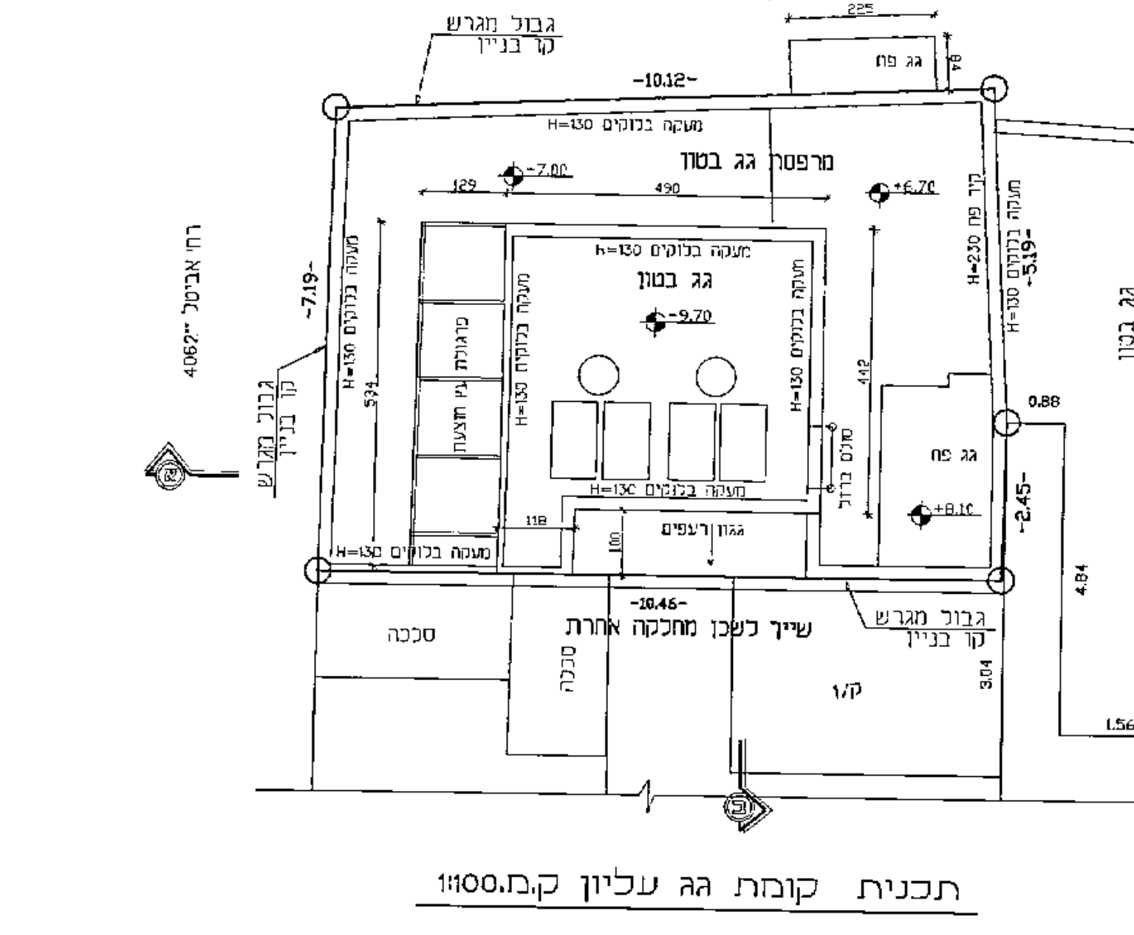
רח' מושיע 4064"
רח' אביטל 4062"
גבול מגרש
קו בניין
מרפסת גג בטון
גג בטון
+9.70
+7.00
+6.70
גג פח
גגון רעפים
סככה
שייך לשכן מחלקה אחרת
גג בטון
1/ק
-10.12-
-10.46-
-7.19-
-5.19-
-2.45-
א

תכנית קומת גג עליון ק.מ.1:100

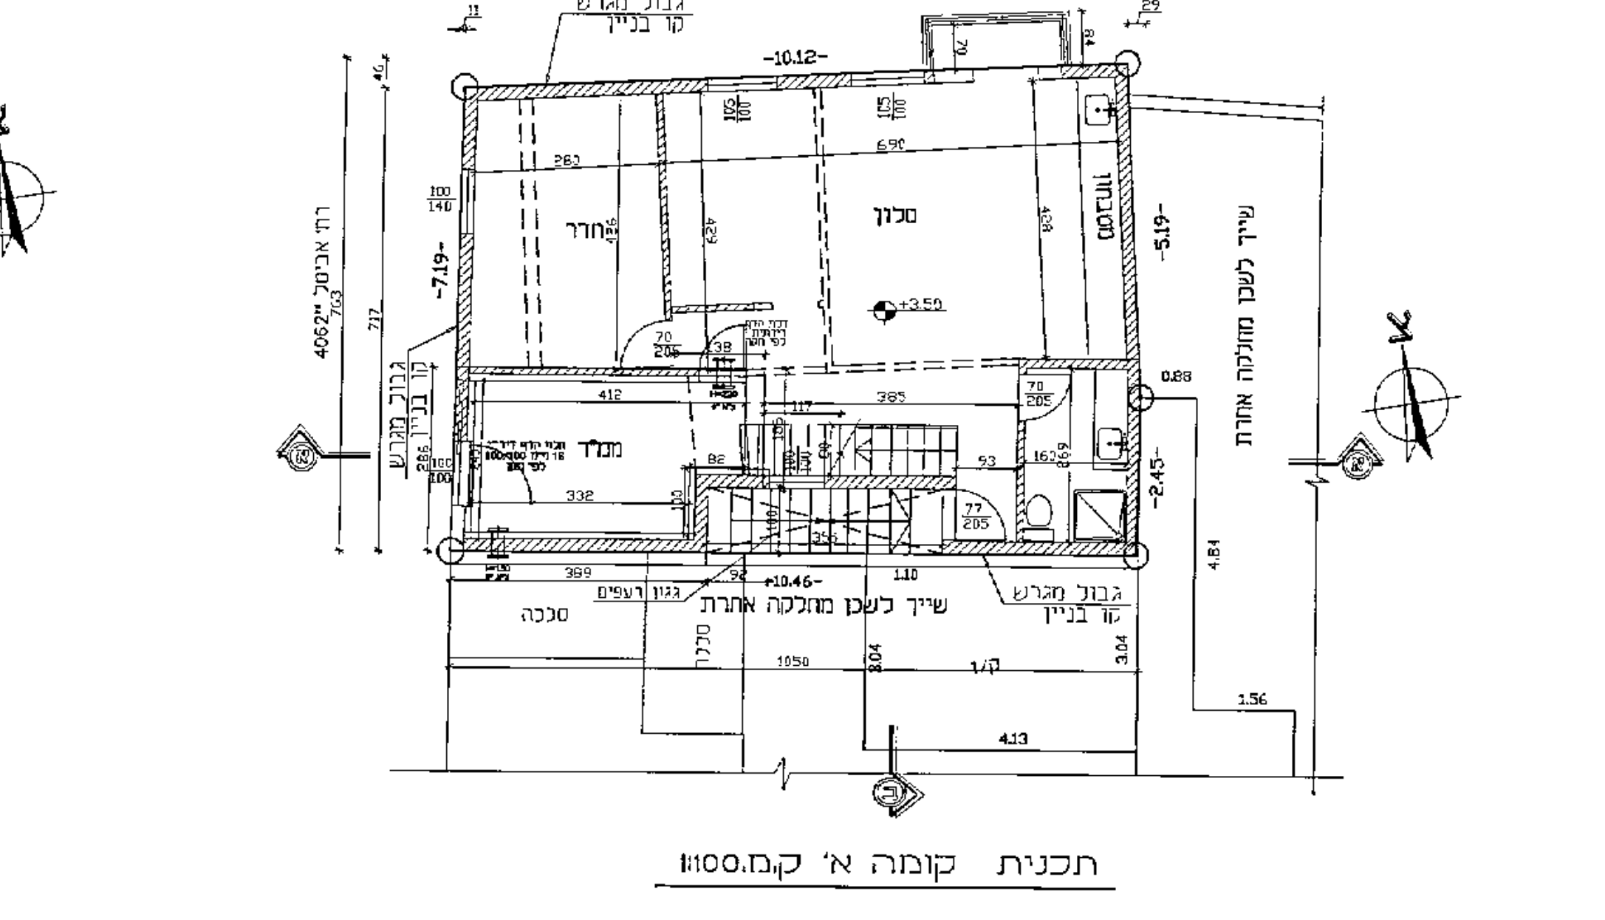
רח' מושיע 4064"
רח' אביטל 4062"
גבול מגרש
קו בניין
חדר
סלון
ממ"ד
+3.50
סככה
גגון רעפים
שייך לשכן מחלקה אחרת
שייך לשכן מחלקה אחרת
1/ק
-10.12-
-10.46-
-7.19-
-5.19-
-2.45-
א

תכנית קומה א' ק.מ.1:100

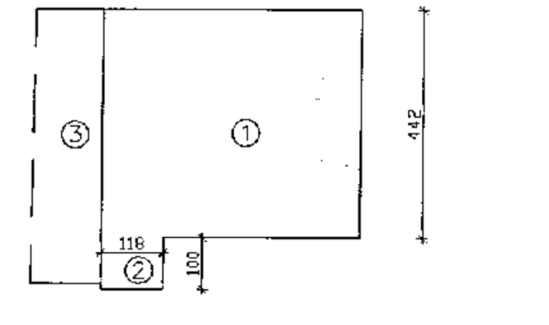
129
490
534
442
118
100
①
②
③

מפה טופוגרפית

קנה מידה 1:250

מחוז : תל-אביב
נפה : תל-אביב-יפו
גוש : 6135
חלקה : 44 (חלק)
כתובת : רח' אביטל 28

מטרת המדידה: הגדרת מגרש משני עפ"י תב"ע 2215

שם הבעלים כרשום בנסח טאבו+מס' ת.ז:

דוידוב ויטלי	310123278
דוידוב תמרה	306519794
יעקוב אילנה	22041917

שטח לפי נסח:

שטח החלקה כולה: 11.476 ד.מ.

בעלות בחלקים (כרשום בנסח טאבו):

דוידוב ויטלי	15/5738
דוידוב תמרה	15/5738
יעקוב אילנה	108/11447

בעלות במ"ר: 168
שטח מדוד (מ"ר): 78
שטח מגרש משני: ד.מ.
שטח לגריעה: ד.מ.

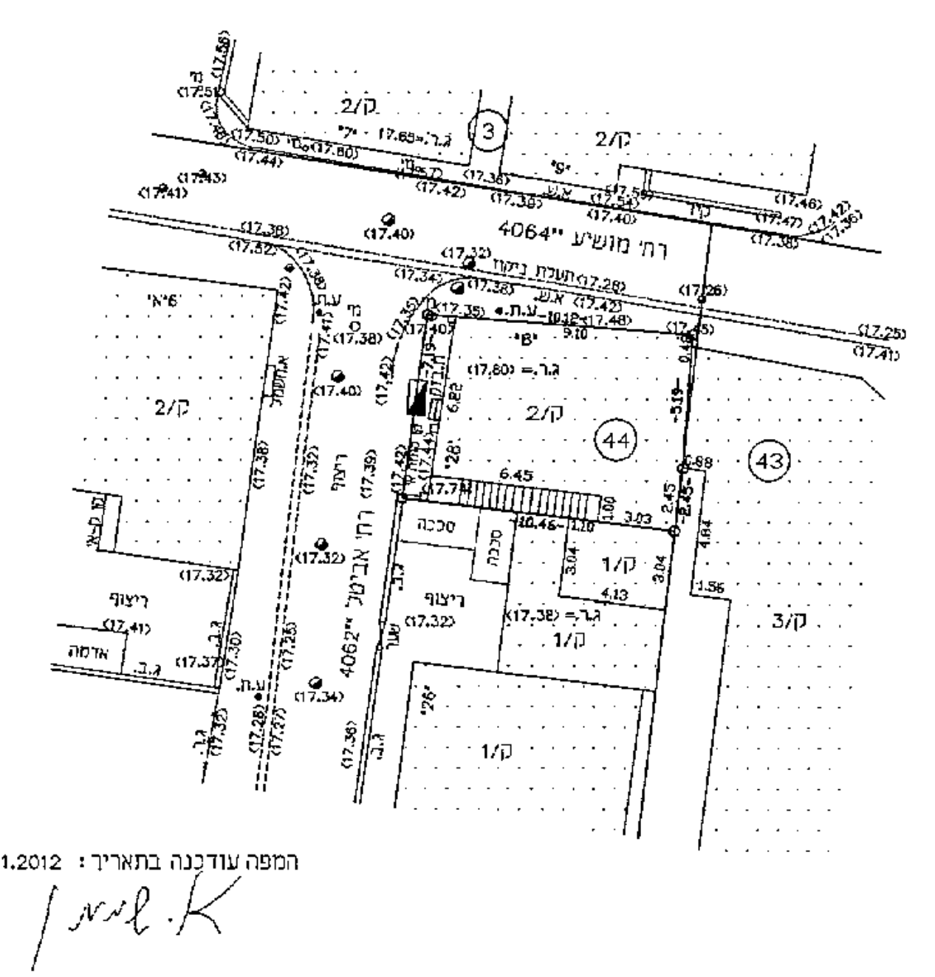
130/550
130/575
130/600
162/075
162/050
רח' מושיע 4064"
רח' אביטל 4062"
2/ק
1/ק
3/ק
(44)
(43)
(3)
סככה
ריצוף
אדמה
6.45
3.03

תרשים הסביבה 1 : 1250

המפה עודכנה בתאריך: 5.01.2012

K. שמע

לא לצרכי רישום

K. שמע

תל-אביב
תאריך: 7.06.2007

הנני מצהיר כי התוכנית ערוכה לפי חוק התכנון והבניה ולפי הנחיות עיריית ת"א-יפו

א.שמעון, מודד מוסמך, רשיון מס' 256
א.שמעון, רח' רימלט, 12 רמת גן, טל. 03-6741012, 052-647718

הערות:
1. המספרים בסוגריים מציינים גבהים.
2. הגבהים מבוססים על נ.ק. עירונית מס' 188 שגובהה 17.530 מ'.

מיה מורגן 0504555896

21

002

עיריית תל-אביב - יפו
מינהל ההנדסה, אגף רישוי ופיקוח על הבנייה
שדרות בן-גוריון 68 תל-אביב 64514 (פקס 5231340) טלפון 5217120, 5217045

חוק התכנון והבניה, התשכ"ה-1965
תקנות התכנון והבניה (בקשה להיתר תנאיו ואגרות) התש"ל-1970

לכבוד ☐ הועדה המקומית לתכנון ולבנייה ☐ רשות הרישוי המקומית

בקשה להיתר בנייה או לשימוש במקרקעין

יש להקפיד למלא את כל הפרטים בטופס הבקשה ולצרף מסמכים כמפורט בדרישות החוק המצורפות

מס' תיק הבניין | מס' בקשה קודמת להיתר בנייה | מס' הבקשה למידע | מתאריך

א. פרטי הנכס והמבקשים

הכתובת	רחוב	מס' בית	גוש	חלקה	תת חלקה	מגרש	הוראות התכניות החלות על המקום
	אביטל	28	6135	44			ג, 2215

פרטים אישיים	שם משפחה / שם פרטי	מס' זהות	רחוב ומספר בית	טלפון
מבקש 1	דוידוב ויטלי	310123278	רח' אביטל 28 ת"א	0502124026
מבקש 2	דוידוב תמרה	306519794	רח' אביטל 28 ת"א	0502124026
מבקש 3				
בעל הזכות בנכס	דוידוב ויטלי דוידוב תמרה	310123278 306519794	רח' אביטל 28 ת"א רח' אביטל 28 ת"א	
החוכר				
עורך הבקשה הראשי	סטולבון ולנטינה	319192290	רח' הירשנברג 12 ת"א	0525775755 03-6730730
מתכנן שלד הבניין	בנדרסקי רוברט	313683468	רח' שער העמים 11 ת"א	0502124026

ב. מהות הבקשה

☐ בקשה לתוספת בנייה ☐ בקשה להרחבת דיור

☐ תוספת ___ קומות לבניין

☐ הכוללות: ___ יחידות דיור

☐ תוספת בנייה בקומה גג ☐ לצד ☐ לאחור ☐ לחזית

בשטח של 22.84 מ"ר

שטח הדירה / המשרד לאחר התוספת יהיה 97.01 מ"ר

☐ שינויים פנימיים הכוללים:

☐ אישור מצב קיים

המקום משמש כיום ל-

☐ בהיתר ☐ בלי היתר

ג. מפרט - תיאור הבקשה

תיאור הקיים על המגרש: קיים בנין מגורים בן 2 קומות שתי יחידות דיור

שימוש עיקרי: ☑ מגורים ☐ משרדים ☐ מסחר ☐ מלונאות ☐ תעשיה ☐ מלאכה ☐ תוספת לבנייה ☐ בידור ☐ נופש וספורט ☐ בנין ציבורי ☐ חקלאי ☐ שימוש אחר

סוג העבודה: ☐ תוספת לבנייה ☐ שינוי לבנייה ☐ הריסה ☐ תיקונים ☐ שינוי בשימוש

הגורם שבבעלותו הבנייה: ☐ רשות מקומית ☐ גורם פרטי ☑ ☐ מוסד ציבורי ☐ משרד ממשלתי ☐ בנה ביתך

שטח המגרש/החלקה	שטח הבנייה המבוקש	שטח הבנייה הכולל	אחוזי הבנייה
78 מ"ר	מ"ר	97.01 מ"ר	124 %

ד. חומרי הבנייה

סוג הבנייה: ☐ רגילה ☐ בית מגורים ☐ תעשייתי ☐ אחר

ה. השטחים המבוקשים לבנייה (על-פי תכנית הבנייה) והמותרים לבנייה (על-פי "אסמכתא": חוק, תקנות, תכנית) בכל מפלס בנפרד ולפי שימוש

קומה	קיים בהיתר	קיים ללא היתר ומבוקש לאישור בדיעבד	בנייה חדשה מוצעת	מותר	מ"ר	אחוזים	סך כל השטחים המותרים	האסמכתא	מקלט	קיים	אחוזים	סך כל השטחים המותרים	מ"ר	אחוזים	סך כל השטחים המותרים	שטחים לא מקורים פרגולה
קומה א'		61.52		61.52	61.52	79	61.52		12.65	12.65	16	12.65	74.17	95	74.17	6.89
קומת גג			22.84	23	22.84	29	23	ה					22.84	29	23.00	
סה"כ מעל הקרקע		61.52	22.84	84.52	84.36	108	84.52		12.65	12.65	16	12.65	97.01	124	97.17	6.89
סה"כ מתחת לקרקע																
סה"כ																

ז. קווי בנייה

	הבניין	מוצע	מותר
לרחוב (שם)	אביטל	0.0	0.0
לרחוב (שם)	מושיע	0.0	0.0
לצד	קיר משותף	0.0	0.0
לאחור	קיר משותף	0.0	0.0

יב. מינויים מסוג מבקש ההיתר

אני מבקש בזה את ולנטינה סטולבון מס' זהות 319192290 להיות עורך הבקשה הראשי

שם משפחה ושם פרטי	מס' זהות	תאריך	חתימה
ולנטינה סטולבון			
דוידוב ויטלי	310123278		

הצהרת מתכנן שלד הבניין: אני החתום מטה בנדרסקי רוברט מס' זהות 313683468

הצהרת האחראי לביצוע שלד הבניין: בנדרסקי רוברט 313683468

יא. הצהרת עורך הבקשה הראשי: ולנטינה סטולבון

8975

FOLD