20

007

עיריית תל-אביב-יפו

מינהל ההנדסה, אגף רישוי ופיקוח על הבנייה
שדרות בן-גוריון 68 תל-אביב 64514 (פקס 5231340) טלפון 5217120, 5217045

חוק התכנון והבניה, התשכ"ה-1965
תקנות התכנון והבנייה (בקשה להיתר תנאיו ואגרות) התש"ל-1970

בקשה להיתר בנייה או לשימוש במקרקעין

יש להקפיד למלא את כל הפרטים בטופס הבקשה ולצרף מסמכים כמפורט ברשימת התיוג המצורפת.

על פי טופס 1 תקנה 2(א)

לכבוד ☐ הוועדה המקומית לתכנון ולבנייה
☐ רשות הרישוי המקומית

08926

מס' תיק הבניין	מס' בקשה קודמת להיתר בנייה	מס' הבקשה למידע	מתאריך
4063-017	2003-0292	N2007-2899	22/112007

א. פרטי הנכס והמבקשים

הכתובת	רחוב	מס' בית	גוש	חלקה	תת חלקה	מגרש	הוראות התכניות החלות על המקום
	וילון	17	6135	43			ג 2215

פרטים אישיים	שם משפחה ושם פרטי / שם חברה או תאגיד	מס' זהות/חברה או מס' רישום תאגיד	רחוב ומספר בית / ישוב ומיקוד	מספר טלפון / מספר פקס
מבקש 1	זבולונוב אנגליקה	3009397933	רח' וילון 17, ת"א	053985358
מבקש 2				
מבקש 3				
בעל הזכות בנכס				
החוכר				
עורך הבקשה הראשי	ד'בגורסקי אלכס	14687859	רח' גרינבוים 14 תל אביב-יפו, 68109	0522544457 03 9510030
מתכנן שלד הבניין	ד'בגורסקי אלכס	14687859	רח' גרינבוים 14 תל אביב-יפו, 68109	0522544457 03 9510030

אם המבקש הוא חברה או תאגיד, יש לרשום את שם המורשה מטעם המבקש שיחתום 1

אלכסנדר

ב. מהות הבקשה

☐ בקשה לתוספת בנייה ☐ בקשה להרחבת דיור (במסגרת הרחבת דיור שכונתית)
☐ תוספת ____ קומות לבניין
הכוללות: ☐ ____ יחידות דיור
☐ ____
☒ תוספת בנייה בקומה גג ☒ לחזית ☒ לאחור ☐ לצד
בשטח של 11.80 מ"ר
שטח הדירה / המשרד לאחר התוספות יהיה 81.97 מ"ר
☐ שינויים פנימיים הכוללים: ____
☐ אישור מצב קיים
☐ ____
המקום משמש כיום ל- מגורים
☒ בהיתר ☐ בלי היתר

ג. מפרט - תיאור הבקשה

תיאור הקיים על המגרש: פרט מספר מבנים, גובהם, מקומם, ייעודם וכד'
קיים בניין בן 2 קומות
2 יח' דיור

שימוש עיקרי: ☒ מגורים ☐ משרדים ☐ מסחר ☐ מלונאות ☐ בידור ☐ נופש וספורט ☐ תעשיה ☐ בנין ציבורי ☐ שימוש אחר ☐ חקלאי ☐ מלאכה

סוג העבודה או השימושים המוצעים: ☒ תוספת לבניין ☐ שינוי לבניין ☐ הריסה ☐ תיקונים ☐ שינוי בשימוש ממטרה ____ למטרה ____

הגורם שמבוצעת בעבורו הבנייה: ☐ משרד ממשלתי ☐ רשות מקומית ☐ מוסד ציבורי ☒ גורם פרטי ☐ בנה ביתך ☐ אחר: ____

שטחים: שטח המגרש/החלקה 85.00 מ"ר; שטח הבנייה הכולל המבוקש 81.97 מ"ר; אחוזי הבנייה 96.66

אם במסגרת הרחבת דיור שכונתית: מספר יחידות דיור מורחבות 1; מספר תכנית ההרחבה ג 2215

ד. חומרי הבנייה

סוג הבנייה: ☒ רגילה ☐ בית מוכן ☐ מתועשת ☐ אחר
קירות חיצוניים: ☐ בטון מזוין ☒ בלוקים ☐ אבן טבעית ☐ לבנים שרופות ☐ אחר
חומרי גימור: ☐ אבן מלאכותית ☐ אבן טבעית ☒ טיח ☐ זכוכית ☐ אחר
תקרות: ☒ בטון מזוין ☐ עץ ☐ אחר
גג: ☐ בטון מזוין ☐ אסבסט ☒ רעפים ☐ טיח ☐ אחר
גדרות: ☐ אבן טבעית ☐ אבן מלאכותית ☐ בטון ☐ בלוקים ☐ ברזל ☐ עץ ☐ רשת ☐ אחר
קיימות ____ מ"א מוצעות ____ מ"א סה"כ ____ מ"א

מקרא חומרים (צבעים):

🟦	בטון או בטון מזויין	☐	איטונג
🟥	בלוקים או לבנים מבטון	☐	זכוכית
☐	סיליקט או לבנים אדומות	🟨	הריסה
☐	אבן	☐	אחר
🟩	עץ	☐	

ה. השטחים המבוקשים לבנייה (על-פי תכנית הבנייה) והמותרים לבנייה (על-פי "אסמכתא": חוק, תקנות, תכנית) בכל מפלס בנפרד ולפי שימוש

הקומה/המפלס בבניין (לפי פירוט המופיע בהסברים בכריכת התיק הוורוד – תיק הבקשה להיתר)	(א) 1) מגורים: קיים בהיתר	קיים ללא היתר ומבוקש לאישור בדיעבד	בנייה חדשה מוצעת	מותר	2) קיים בהיתר	קיים ללא היתר ומבוקש לאישור בדיעבד	בנייה חדשה מוצעת	מותר	סך כל שטחי הבנייה העיקריים לשימושים השונים (קיים ומוצע): מ"ר	%משטח המגרש	סך כל השטחים המותרים	ה"אסמכתא" לשטחים המותרים לשימושים העיקריים ולשטחי השרות	(ב) שטחי השירות: מקלט	מתקנים חדרים ומערכות טכניות	החסנה	חניה	מבואות וחדרי מדרגות	קומת עמודים מפולשת	מעברים לכלל הציבור	בליטות	אחר	בנייה קיימת	סך כל שטחי השירות: מ"ר קיים	מ"ר מוצע	%משטח המגרש	סך כל השטחים המותרים	(ג) סך כל שטחי הבניין: מ"ר	%משטח המגרש	סך כל השטחים המותרים	משטחים לא מקורים
±0.00	37.78								37.78	44.44		2215															37.78	44.44		
+3.00	32.39								32.39	38.10		2215															32.39	38.10		
+6.00			11.80	12.00					11.80	14.12	12.00	ג															11.80	14.12	12.00	
ס"ה מעל לקרקע	70.17		11.80						81.97	96.66																	81.97	96.66		
ס"ה מתחת לקרקע																														
סה"כ	70.17		11.80						81.97	96.66																	81.97	96.66		

רישום הוועדה/ בודק מסמכים | תאריך | שם | חתימה

ו. פרטי הבנייה - לשימוש הלשכה המרכזית לסטטיסטיקה

הייעוד	פירוט הייעוד (כגון דירות למגורים, בתי מלון וכו')	השטח על פי ההיתר	מספר חדרים	מספר דירות	מספר מגורים
למגורים			1		
להארחה			2		
לעסקים ולמסרדים			3		
לבנייני ציבור			4		
לתעשייה ולמלאכה			5		
למשק חקלאי			6		
למקלט או למרתף					
למבני עזר					
סך כל שטח הבנייה			סה"כ		

מספר היתר הבנייה:
תאריך היתר הבנייה: שנה ____ חודש ____
תאריך התחלת הבנייה: שנה ____ חודש ____
תאריך גמר הבנייה: שנה ____ חודש ____
מספר הקומות כולל קומת עמודים מפולשת

51318 11/95

ז. קווי בנייה

הכיוון		מוצע	מותר	הסטייה במטר	ב- %
לרחוב (שם)					
לרחוב (שם)					
לצד					
לאחור					

ח. מספר יחידות דיור

אם השימוש המבוקש הוא מגורים – רשום להלן:
מספר הדירות קיימות: מעל ל – 120 מ"ר ____ מתחת ל – 120 מ"ר ____
מספר הדירות המבוקשות ____
מספר הדירות המותרות ____

ט. הבקשה מוגשת לאישור

☐ הוועדה המקומית
הבקשה כוללת בקשה להקלה – כלהלן:

	פירוט הבקשה להקלה	נימוקי הבקשה להקלה
.1		
.2		
.3		

☐ רשות הרישוי המקומית
☐ רשות הרישוי המקומית באמצעות מורשה להיתר

לשימוש המשרד: התוכנית תואמת את המצב בשטח ☐ כן ☐ לא; הערות הפיקוח
☐ הוכן דוח לתביעה משפטית ☐ הוגשה תביעה משפטית ☐ הוגשה תביעה חוזרת
מס' הדוח/ התביעה ____ תאריך הדוח/ התביעה ____
הנדון בדוח / הנדון בתביעה ____
הערות | תאריך | שם | חתימה

י. הצהרת עורך הבקשה הראשי

☐ אני מצהיר על נכונות הפרטים בסעיפים א עד ט.
תאריך 04/2008 שם ז'בגורסקי א. חתימה X

ד'בגורסקי אלכס מהנדס בניין מס' 15320

יא. חתימות נוספות

	תאריך	שם	חתימה
המבקש	04/2008	זבולונוב	X
בעל הזכות בנכס/ בעל הנכס/ החוכר	04/2008	זבולונוב	
מתכנן שלד הבניין	04/2008	ז'בגורסקי	

יב. מינויים מטעם מבקש ההיתר - נתמנה אדם אחד ליותר מתפקיד אחד, ימולאו פרטיו ליד כל אחד מהתפקידים שהוא ממלא על פי הוראות כל דין.

מינוי עורך הבקשה הראשי: אני ממנה בזה את ד'בגורסקי אלכס בעל/ת מס' זהות 14687859 הרשום בסעיף א' להיות עורך הבקשה הראשי להיתר, ולייצגני לפני מוסדות התכנון והרשויות המוסמכות בכל הנוגע לטיפול בבקשה להיתר ולקבלתו, לרבות התיקונים ככל שידרשו הרשויות המוסמכות.

מינוי עורכי בקשה לפי תחומים: אני ממנה בזה את הרשומים להלן להיות עורכי הבקשה להיתר בתחום הפעולה כרשום ליד שמם, ולייצגני בתחום פעולתם לפני מוסדות התכנון והרשויות המוסמכות בכל הנוגע לטיפול בבקשה להיתר ולקבלתו, לרבות התיקונים ככל שידרשו הרשויות המוסמכות.

	שם משפחה ושם פרטי	תחום פעולה	המען	מספר טלפון	מספר פקס
.1		מתכנן האינסטלציה הסניטרית			
.2					

מינוי מתכנן שלד הבניין: אני ממנה בזה את ד'בגורסקי אלכס בעל/ת מס' זהות 14687859 הרשום בסע' א' להיות אחראי לתיכנון שלד הבנין שבעבורו מבוקש ההיתר, להגיש לוועדה המקומית לרשות הרישוי המקומית את החישובים לגבי הבניה שבעבורה מבוקש היתר ולפקח פיקוח עליון על הקמת השלד.

מינוי הקבלן האחראי לבניית:
☐ אני ממנה בזה את ____ בעל/ת מס' זהות ____ ובעל תעודת רישום בפנקס הקבלנים מספר ____ במדור ____ ובעל ____ לביצוע עבודה בתוקף עד ____ לבצע את העבודה הנדונה בהיתר כמתחייב לפי כל דין.
☐ אני מצהיר, כי טרם מסרתי את ביצוע העבודה הנדונה בהיתר לידי קבלן, ומתחייב כי אמסור אותה לידי קבלן רשום בפנקס הקבלנים, כמתחייב על פי כל דין, והודיע על כך לרשות הרישוי המקומית טרם התחלת ביצוע העבודה, וחתימתו של הקבלן תצורף להודעה המפרטת את פרטי רישומו של הקבלן.

מינוי האחראי לבניית שלד הבניין:
☐ אני ממנה בזה את ____ בעל/ת מס' זהות ____ כתובת ____ טלפון ____ פקס ____ הרשום לעיל להיות אחראי לביצוע שלד.
☐ אני מצהיר, כי טרם מיניתי אחראי/ת לביצוע עבודות בתחומים האלה: ____ ומתחייב לעשות זאת כמפורט בתקנות, ולהודיע על כך לרשות הרישוי המקומית טרם התחלת ביצוע העבודה.

מינוי אחראים לביקורת:
☐ אני ממנה בזה את הרשומים להלן להיות אחראים לביקורת על ביצוע עבודות בתחום הפעולה כרשום ליד שמם.

	שם משפחה ושם פרטי	תחום פעולה	המען	מספר טלפון	מספר פקס
.1		אחראי ראשי			
.2					
.3					

☐ אני מצהיר כי טרם מיניתי אחראי/ם לביקורת על ביצוע עבודות את כולם או את קצתם בתחומים האלה: ____ ומתחייב לעשות זאת כמפורט בתקנות, ולהודיע על כך לרשות הרישוי המקומית טרם התחלת ביצוע העבודה.

חתימת המבקש על המינויים X ____ X

יג. הצהרות

הצהרת עורכי הבקשה כולל הצהרת עורך הבקשה על לחץ המים:
אנו החתומים מטה מצהירים בזה:
1) כל אחד מאתנו מאשר שהאמור בנוגע לרשימה שבסעיף "לעיל הוא נכון.
2) כל אחד מאתנו מסכים לקבל עליו את התפקיד המיועד לו בסעיף "לעיל.
3) אנו מצהירים, כל אחד בנוגע לתחום פעולתו, שיש לנו כישורים מקצועיים לערוך בקשה זו וכי בדקנו את המסמכים הנוגעים לבקשה, לרבות כל תכנית הנוגעת לבקשה, וידוע לנו כי אם הצהרה זו אינה נכונה, הרי היא תיחשב מסירת ידיעה שהיא כוזבת או מטעה בפרט חשוב, כמשמעותה בסעיף 214 לחוק, וצפויים לנו העונשים הקבועים לפי כל דין.
אני ד'בגורסקי אלכס (עורך בקשה ראשי) אחראי/ת לכך שהבקשה, ובכלל זה נספחיה, נערכה לפי מיטב הידיעה המקצועית ובהתאם לכל חיקוק החל על או העבודה המוצעת, שכל הנתונים שנמסרו על ידי בבקשה זו נכונים ושהתכנון המוצע תואם את כל התכניות, פרט לסטיות שפורטו לעיל.
☐ אני עורך הבקשה מתכנן האינסטלציה הסניטרית, מצהיר בזאת ואחראי לכך שתכניות הבקשה בכל הנוגע לסידורים הסניטריים נערכו כדין וכי קויימו בהן הוראות החוק וההוראות למתקני תברואה התש"ל 1970 (הל"ת) לענין זה, לרבות בדיקת לחץ המים הקיים בבנין ותיכנון בהתאם.

	תאריך	שם משפחה ושם פרטי	מספר רישיון	חתימה
עורך בקשה ראשי		ד'בגורסקי אלכס	15320	ד'בגורסקי אלכס מהנדס בניין מס' 15320
עורך בקשה 1 מתכ' האינס הסניט'				
עורך בקשה 2				

הצהרת מתכנן שלד הבניין:
אני החתום מטה (שם משפחה ושם פרטי) ד'בגורסקי אלכס מס' זהות 14687859
מהנדס רשוי מס' 15320 /הנדסאי בעל רישיון מס' ____ (ל"מבנה פשוט") מצהיר בזאת כדלקמן:
1) אני מסכים להיות מתכנן שלד הנדון בבקשה ולפקח פיקוח עליון על הקמת השלד.
2) אני מתחייב להגיש לפני מתן ההיתר, נושא הבקשה את החישובים הסטטיים בדבר ש בעבורה ההיתר.
3) ידוע לי, שאם אחרי הגשת הנתונים הסטטיים יתגלה צורך בשינוי מהותי בהם, אני מתחייב להגיש חישובים סטטיים מתוקנים מיד עם גילוי הצורך בכך.
4) אני מצהיר, כי יש לי כישורים מקצועיים לערוך בקשה זו וכי בדקתי את כל המסמכים הנוגעים לבקשה, לרבות כל תכנית הנוגעת לבקשה, וידוע לי כי אם הצהרה זו אינה נכונה, הרי היא תיחשב מסירת ידיעה שהיא כוזבת או מטעה בפרט חשוב, כמשמעותה בסעיף 214 לחוק וצפויים לי העונשים הקבועים לפי כל דין.
5) ידוע לי כי עלי לשמור את תכניות הקונסטרוקציה לתקופה של לא פחות מ-10 שנים לאחר גמר הבנייה.
תאריך ____ חתימה ____

ד'בגורסקי אלכס מהנדס בניין מס' 15320

הצהרת האחראי לביצוע שלד הבניין (כאשר מונה):
אני החתום מטה (שם משפחה ושם פרטי) ____ מס' זהות ____
מהנדס רשוי מס' ____ /הנדסאי בעל רישיון מס' ____ (ל"מבנה פשוט") מצהיר בזאת כדלקמן:
1) אני מסכים להיות האחראי לבצוע שלד הבניין
2) אני מצהיר, כי יש לי כישורים מקצועיים להיות אחראי לביצע שלד ____, ואני מתחייב לדאוג לביצוע שלד ____ על פי תוכניות והוראות של מתכנן השלד כפי ____ בכתב וכן למלא את תפקידי על פי שנקבע בכל חיקוק הנוגע להן.
תאריך ____ חתימה ____

הצהרת אחראים לביקורת (כאשר מונו):
אנו החתומים מטה מצהירים בזה:
1) כל אחד מאיתנו מאשר שהאמור בנוגע לו ברשימה שבסעיף י"ב לעיל הוא נכון.
2) כל אחד מאיתנו מסכים לקבל עליו את התפקיד המיועד לו בסעיף י"ב.
3) אנו מצהירים כל אחד בנוגע לתחום פעולתו, שיש לנו כישורים מקצועיים לערוך את הביקורת כהלכה ולדווח על תוצאותיה לרשות הרישוי המקומית כמתחייב על פי כל דין.
אני ____ (עורך הביקורת הראשי) אחראי/ת לכך שהביקורת תיערך על פי מיטב הידיעה המקצועית, ושכל הדיווחים לרשות הרישוי המקומית ייערכו על פי כל דין.

תאריך	שם משפחה ושם פרטי	מספר רישיון	חתימה

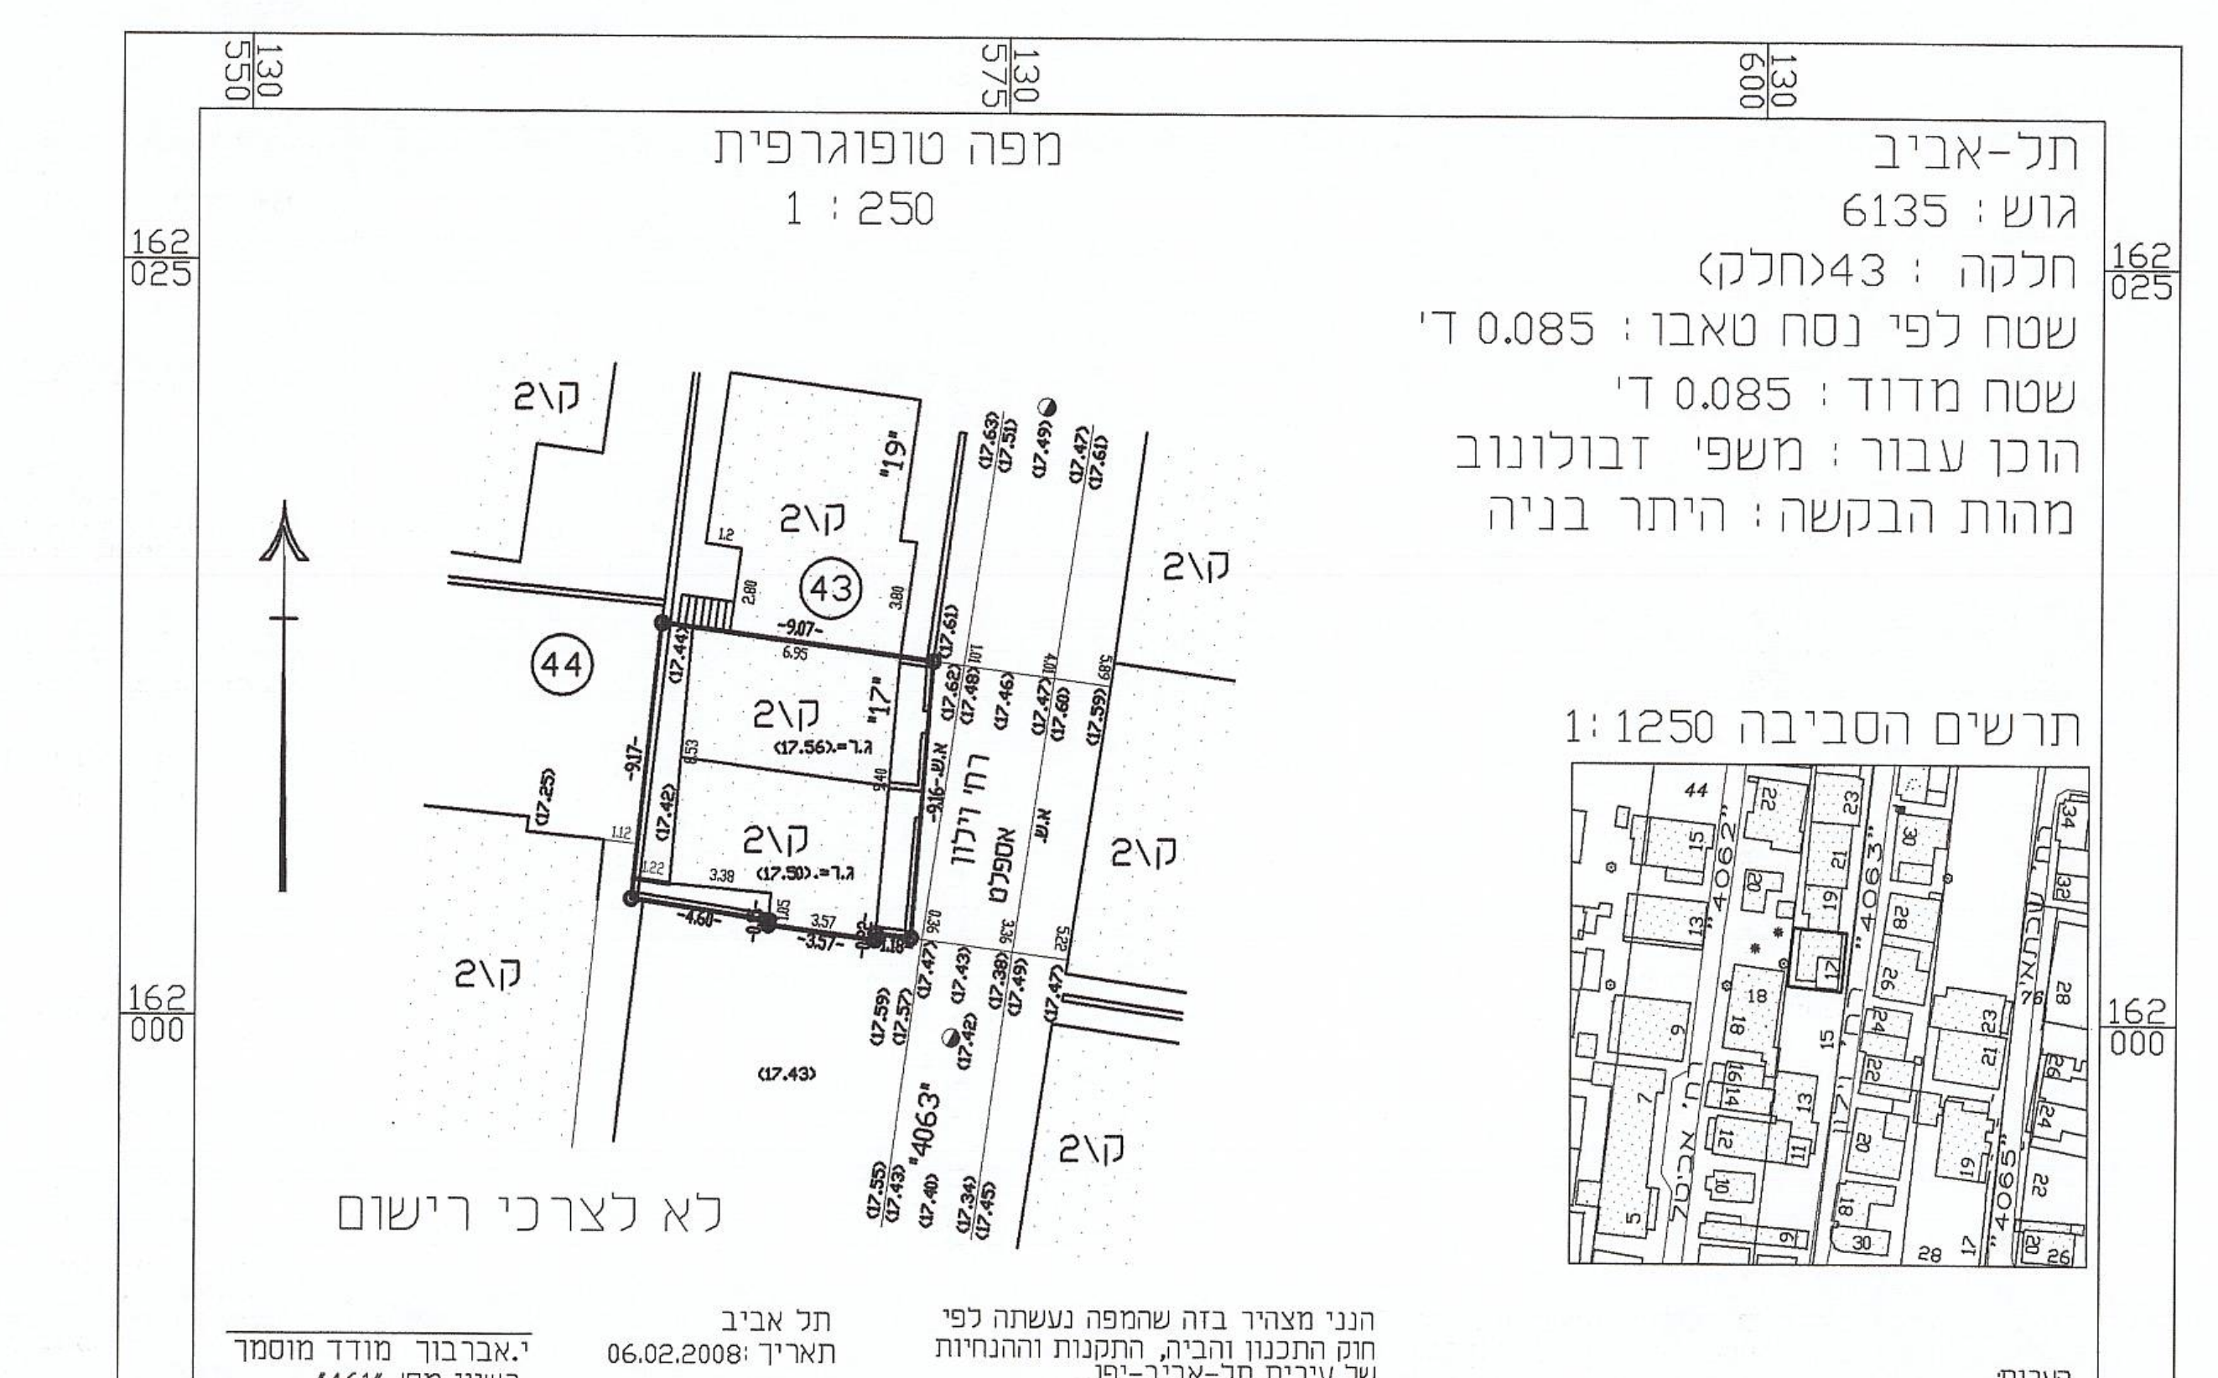

תל-אביב
גוש: 6135
חלקה: 43(חלק)
שטח לפי נסח טאבו: 0.085 ד'
שטח מדוד: 0.085 ד'
הוכן עבור: משפי זבולונוב
מהות הבקשה: היתר בניה

מפה טופוגרפית
1 : 250

תרשים הסביבה 1:1250

הערות:
1. המספרים בסוגריים מציינים גבהים.
2. הגבהים מבוססים על נ.ג. עירונית מס' 187 שגובהה 17.549 מ'.

הנני מצהיר בזה שהמפה נעשתה לפי חוק התכנון והביה, התקנות וההנחיות של עירית תל-אביב-יפו.

תל אביב
תאריך: 06.02.2008

י.אברבוך מודד מוסמך
רשיון מס' "461"

חב' אברבוך ושותי מודדים מוסמכים בעים
רח' דיזנגוף, 190, תל-אביב טל.5235891, 03-5226791

חישוב שטחים

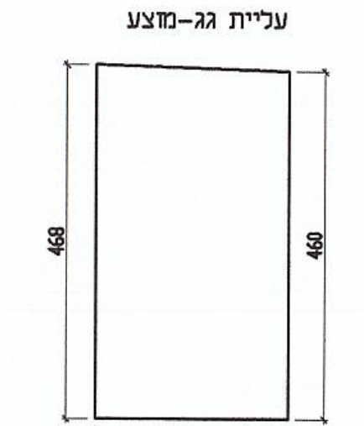

דירה מס' 1

שטח	מס'	חישובים	סה"כ מ"ר
ק.קרקע-קיים בהיתר	⊕	5.40 × 12.00	37.78
ק.א'-קיים בהיתר	⊕	1.45 × 0.70	32.39
עליית גג-מוצע	⊕	(4.68+4.60)/2x2.55	11.80
סה"כ שטח הדירה			81.97

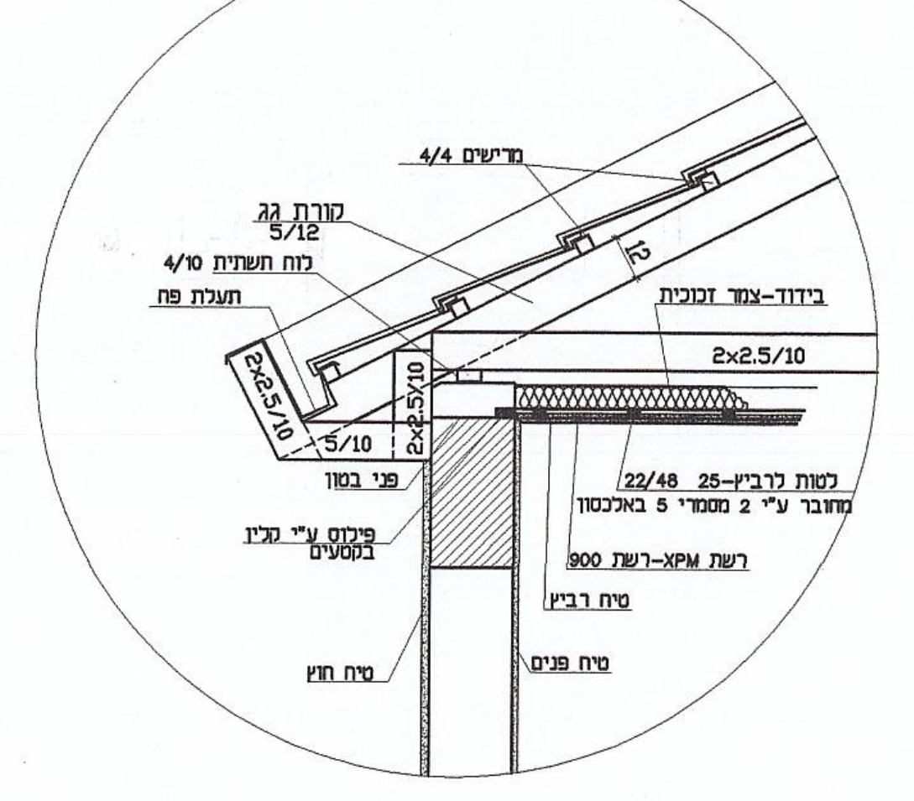

פרט ארגז רוח ק.מ. 1:20

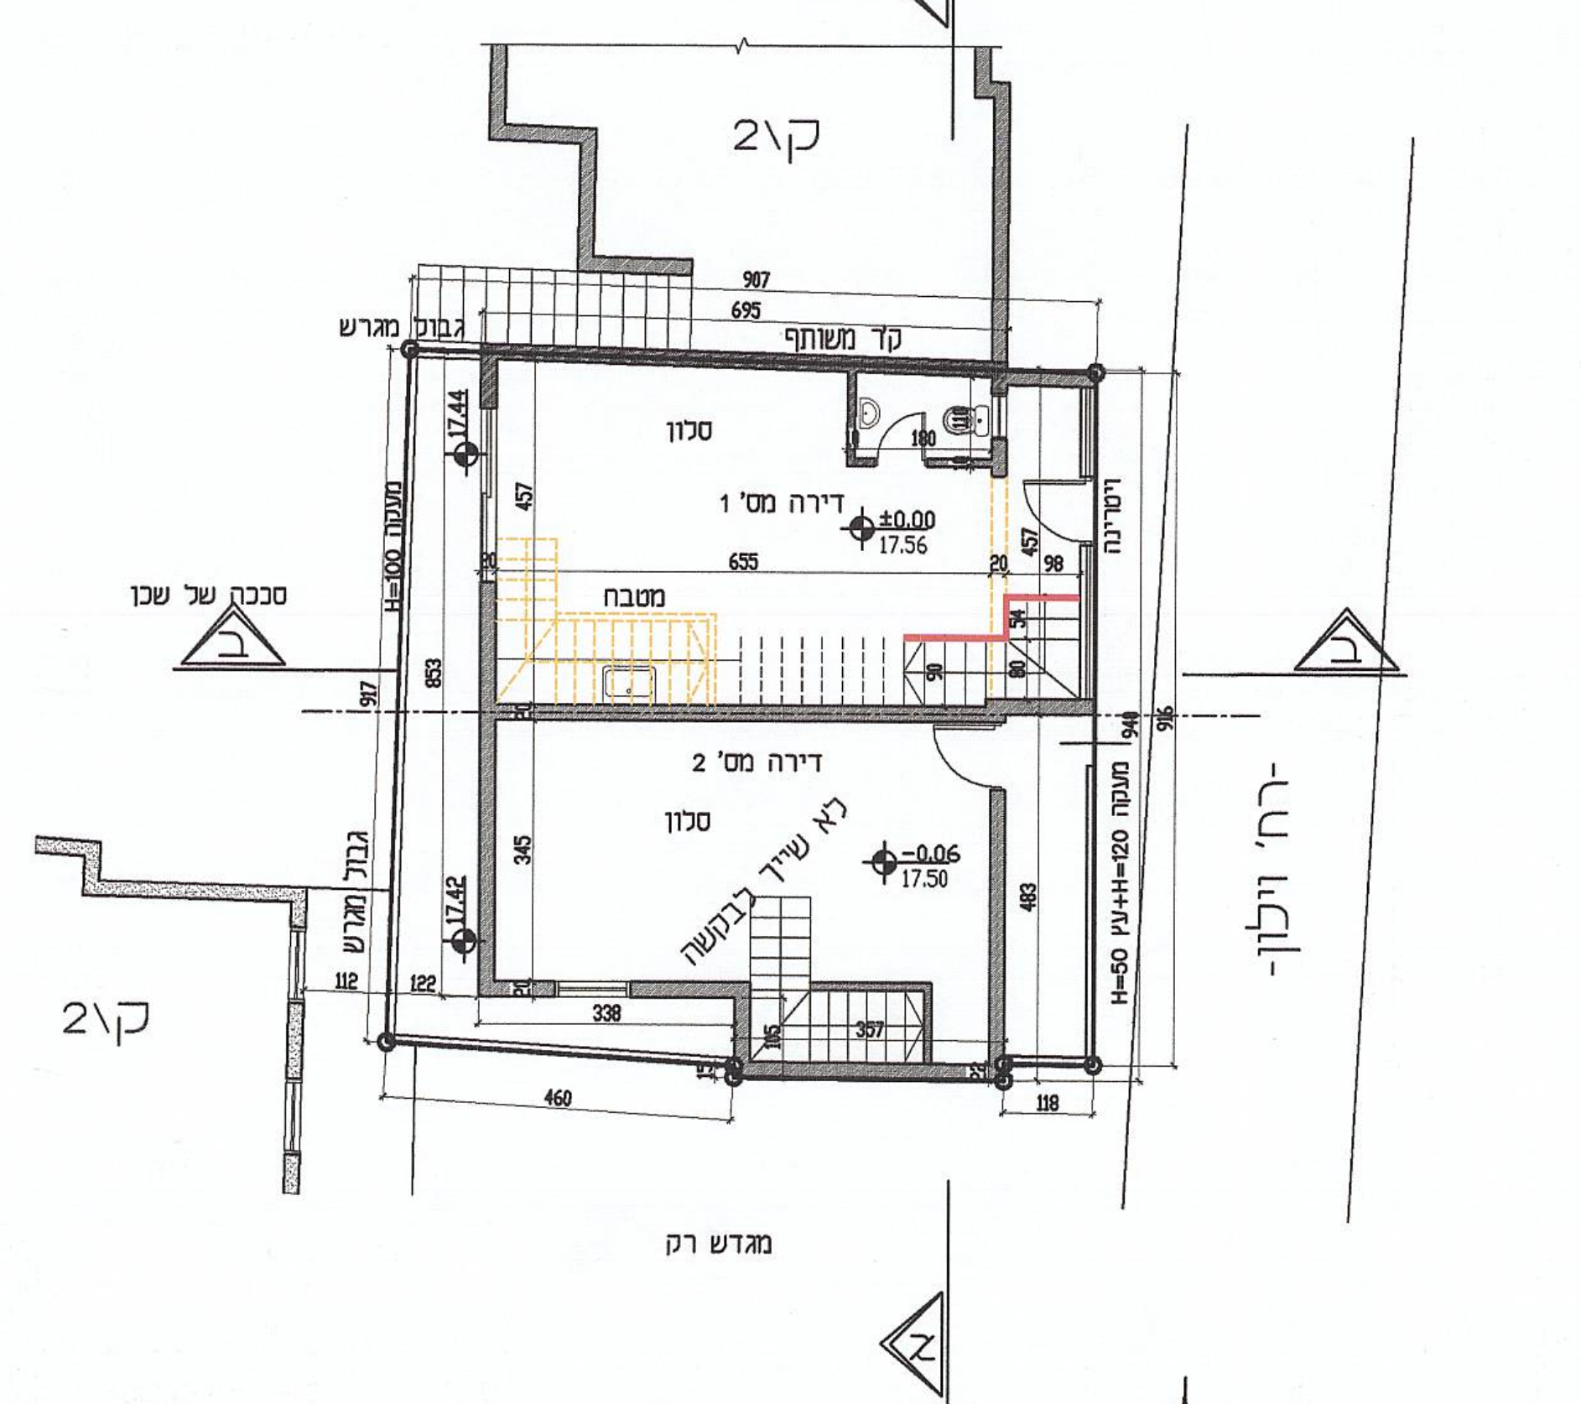

תכנית קומת קרקע

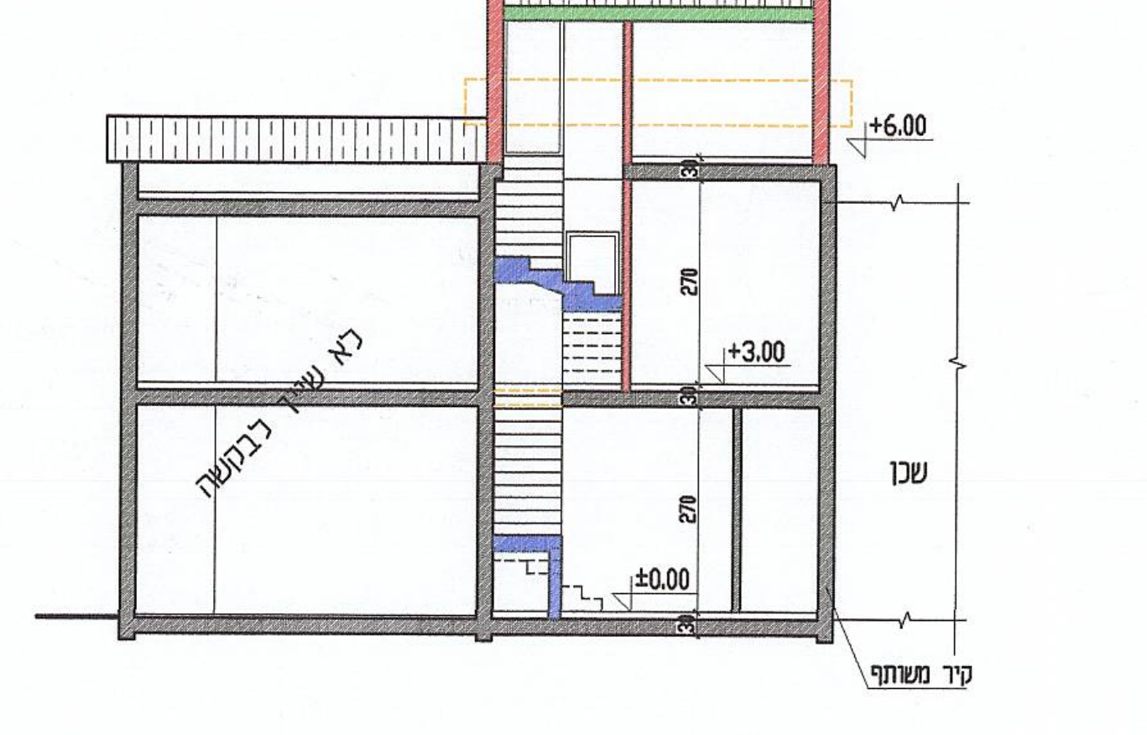

חתך א-א ק.מ. 1:100

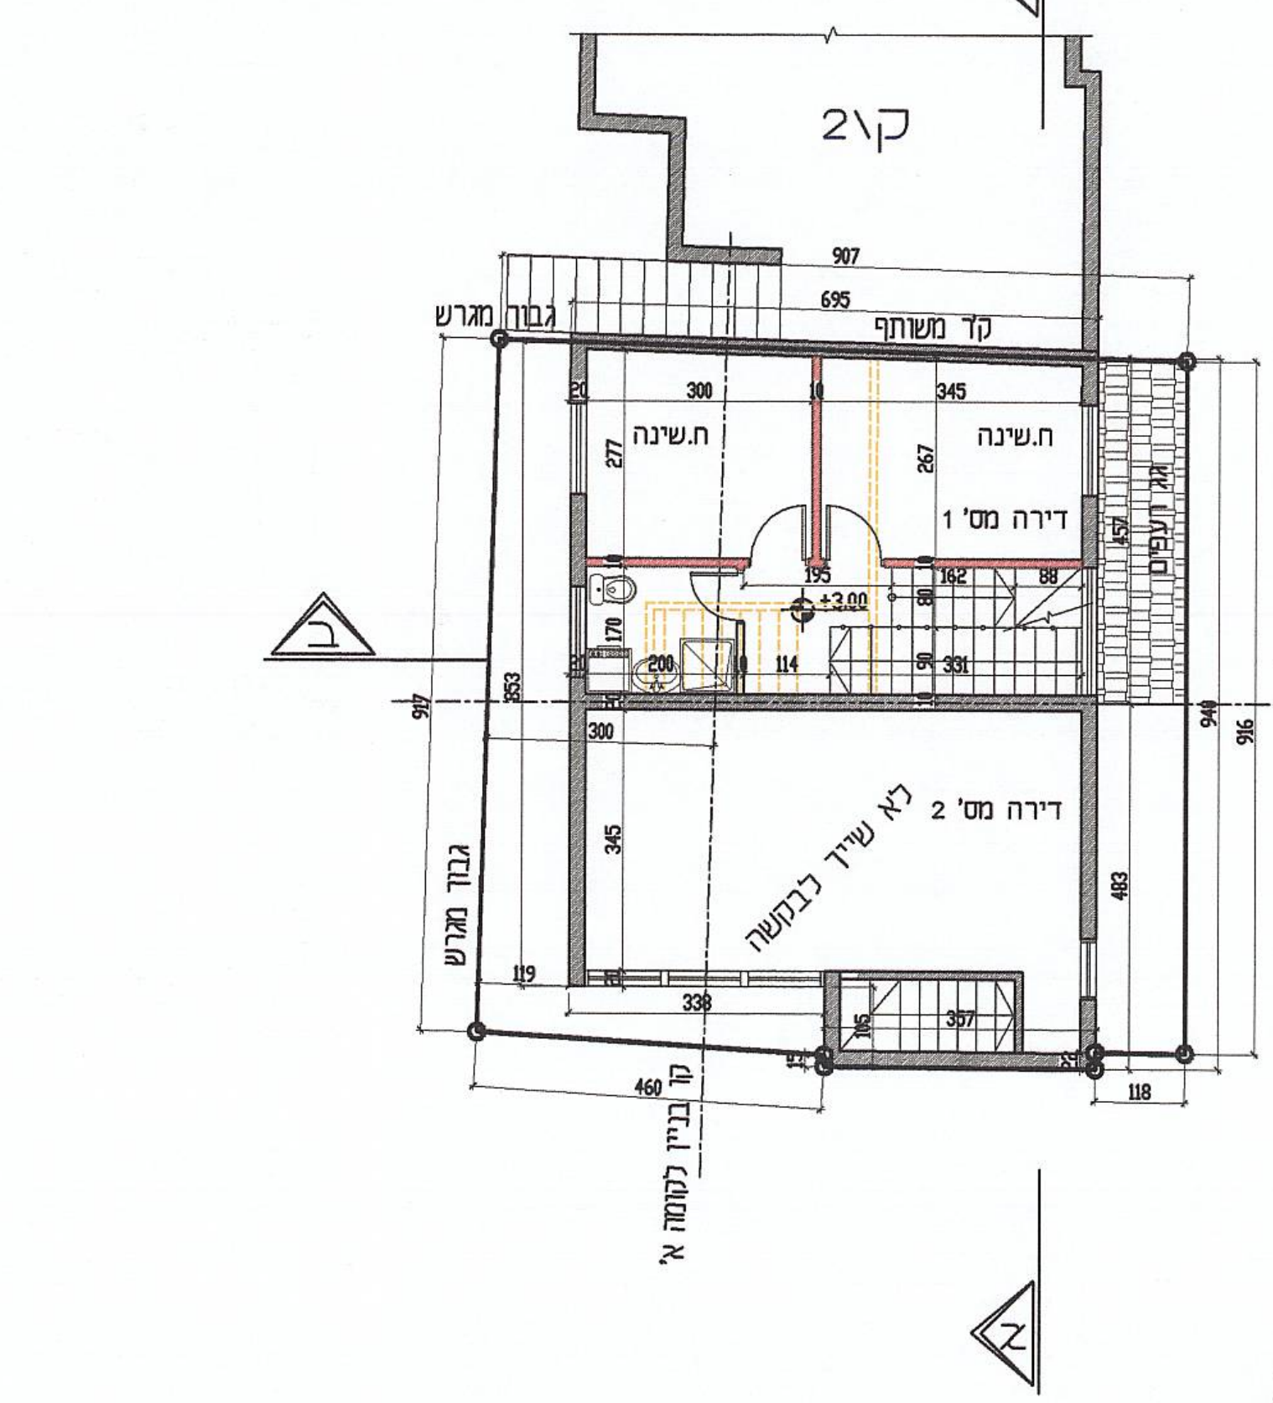

תכנית קומה א' ק.מ. 1:100

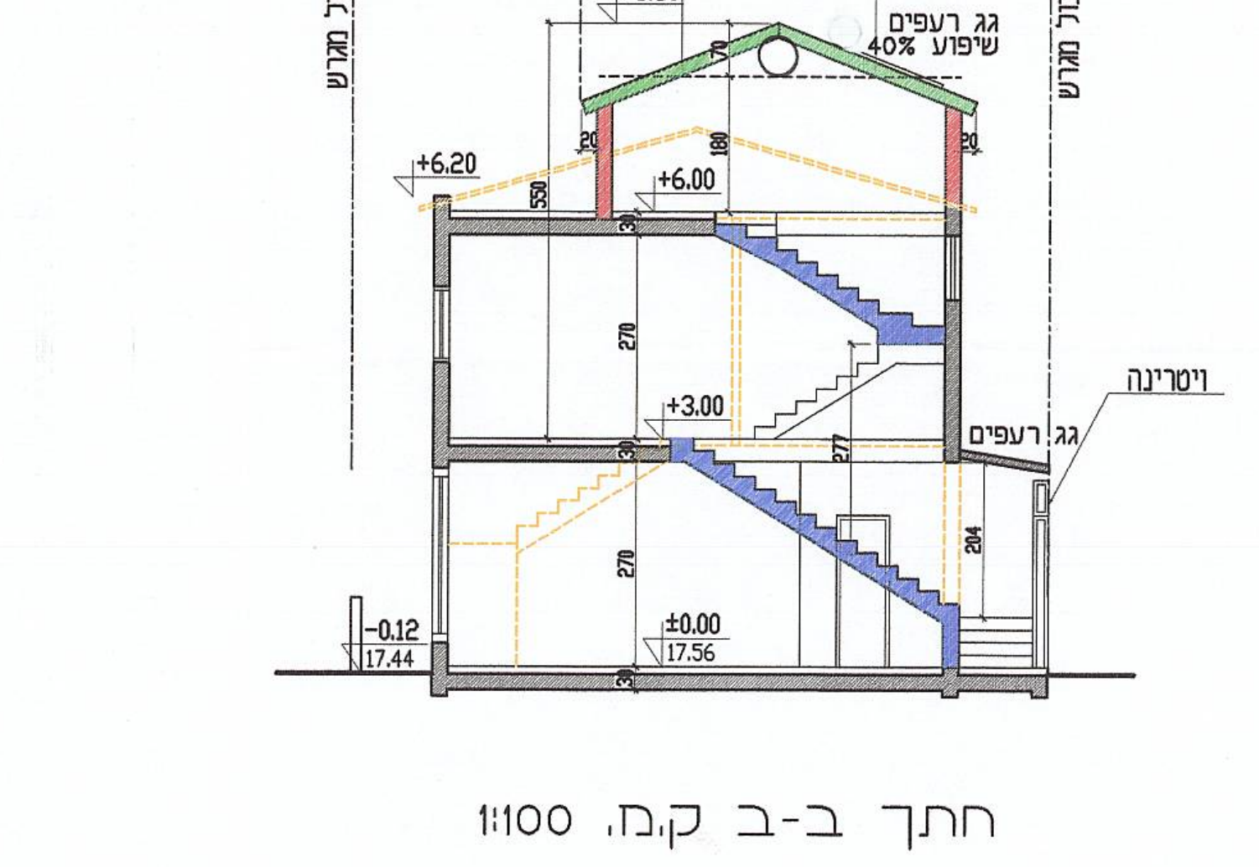

חתך ב-ב ק.מ. 1:100

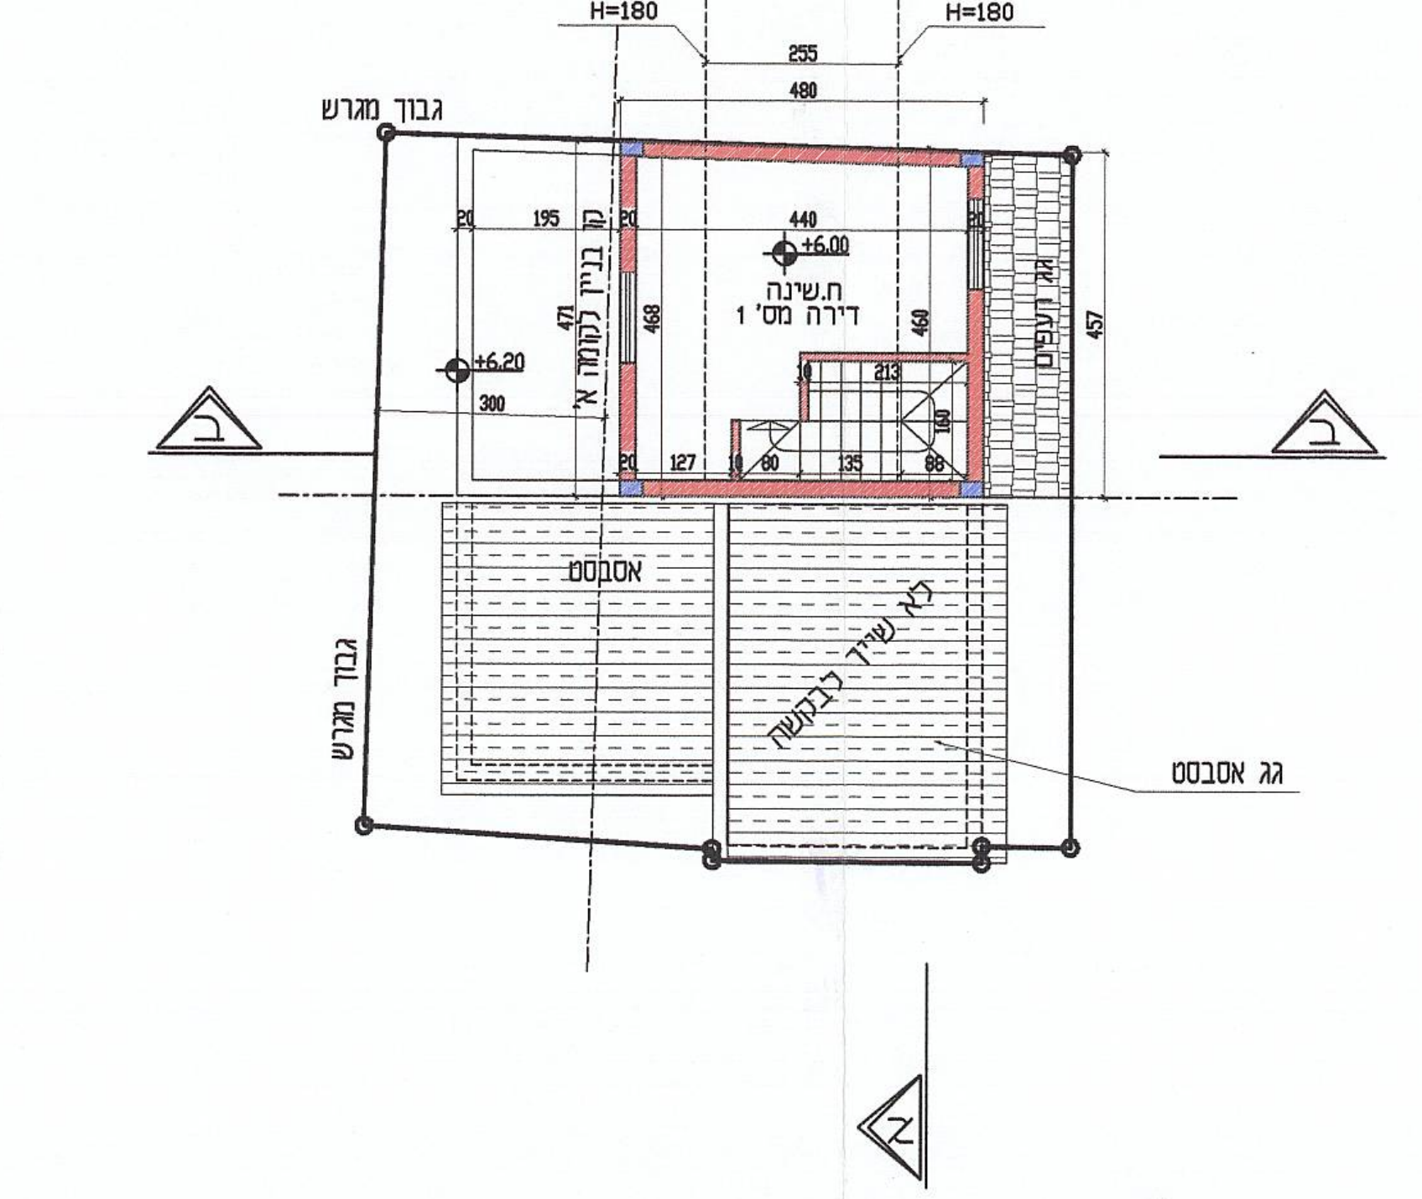

תכנית קומת גג ק.מ. 1:100

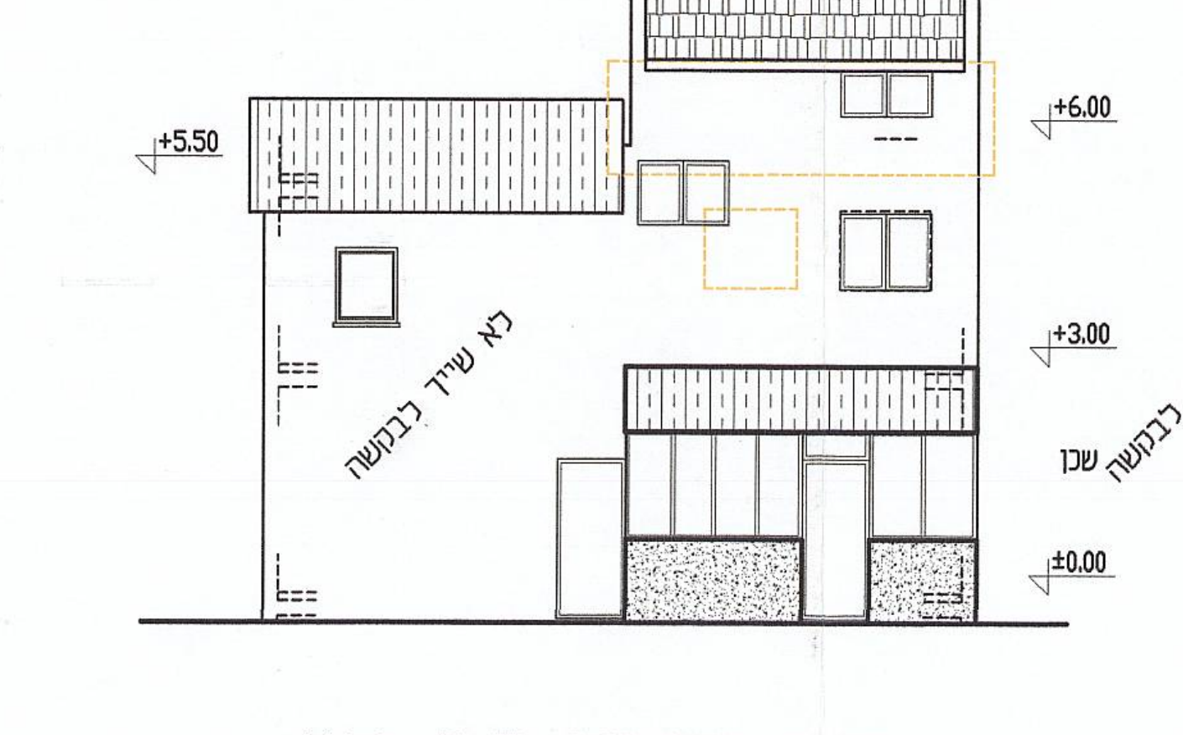

חזית מזרחית ק.מ. 1:100

708-0926

רשות רישוי מקומית לתכנון ולבניה
למרחב תכנון תל-אביב-יפו
בהתאם לסעיף 30 לחוק התכנון והבניה וסעיף 16 (ב) לחוק התכנון והבניה (בקשה להיתר, תנאים ואגרות) תש"ל - 1970
הרינו לאשר כי לספח זה צורף היתר בניה/שימוש
מס 2009093 מיום 9.3.09
ומהווה חלק בלתי נפרד ממנו.
מהנדס העיר

מינהל ההנדסה
אגף הרישוי
העתק מאושר
חתימה

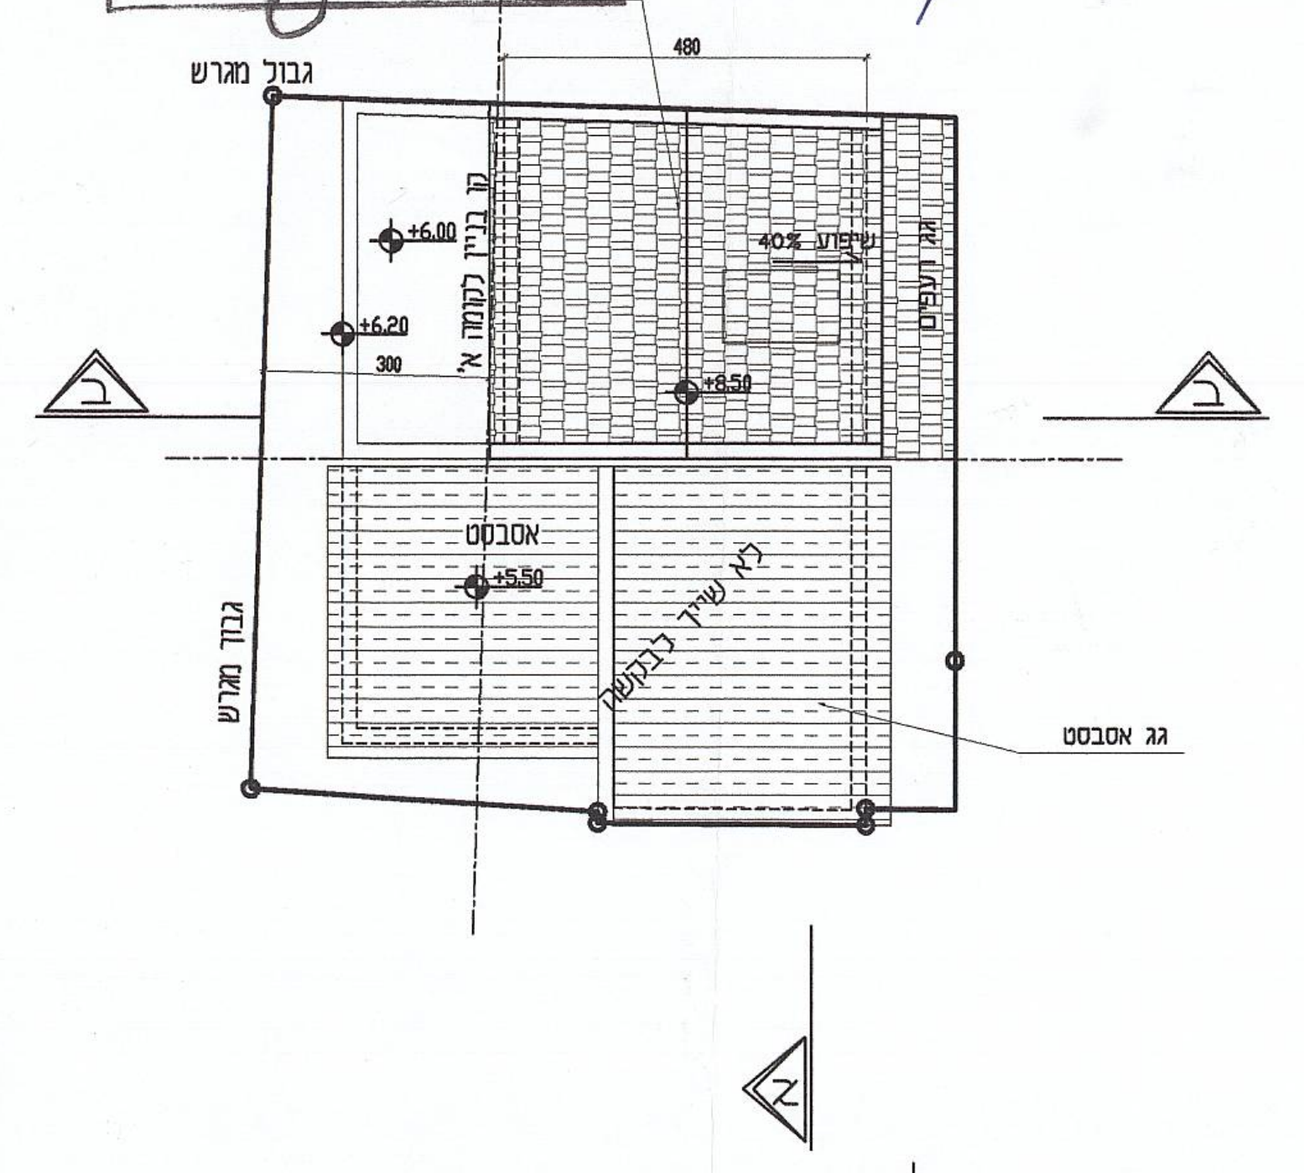

תכנית גג ק.מ. 1:100

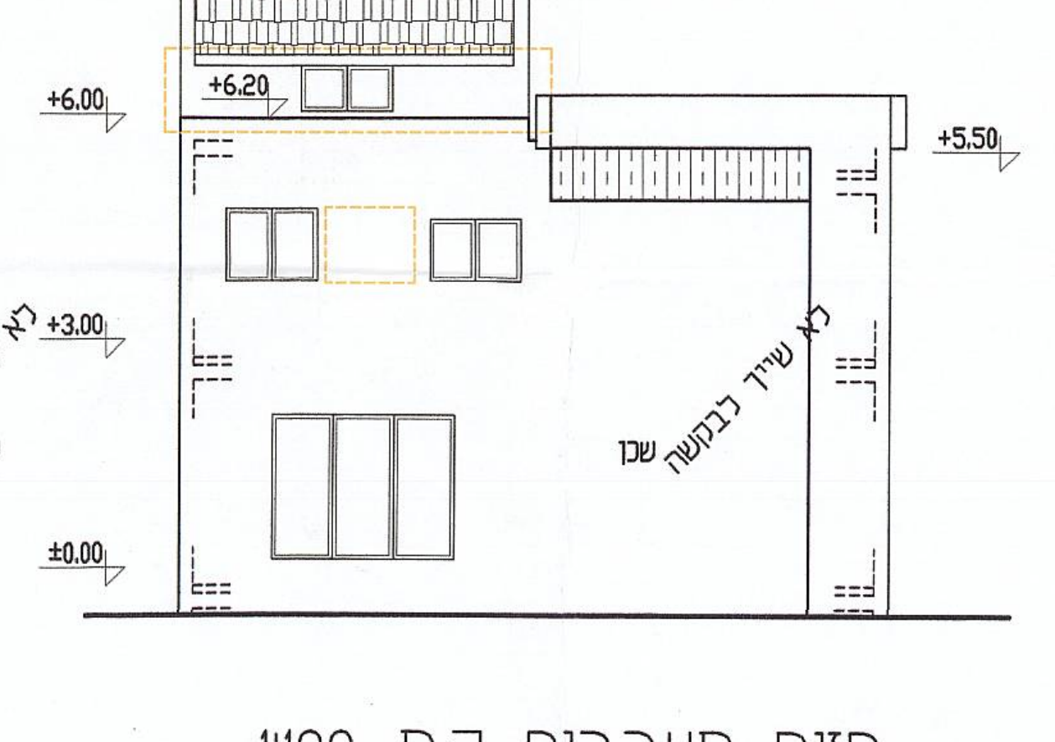

חזית מערבית ק.מ. 1:100

סוף מסמך