סוג מסמך

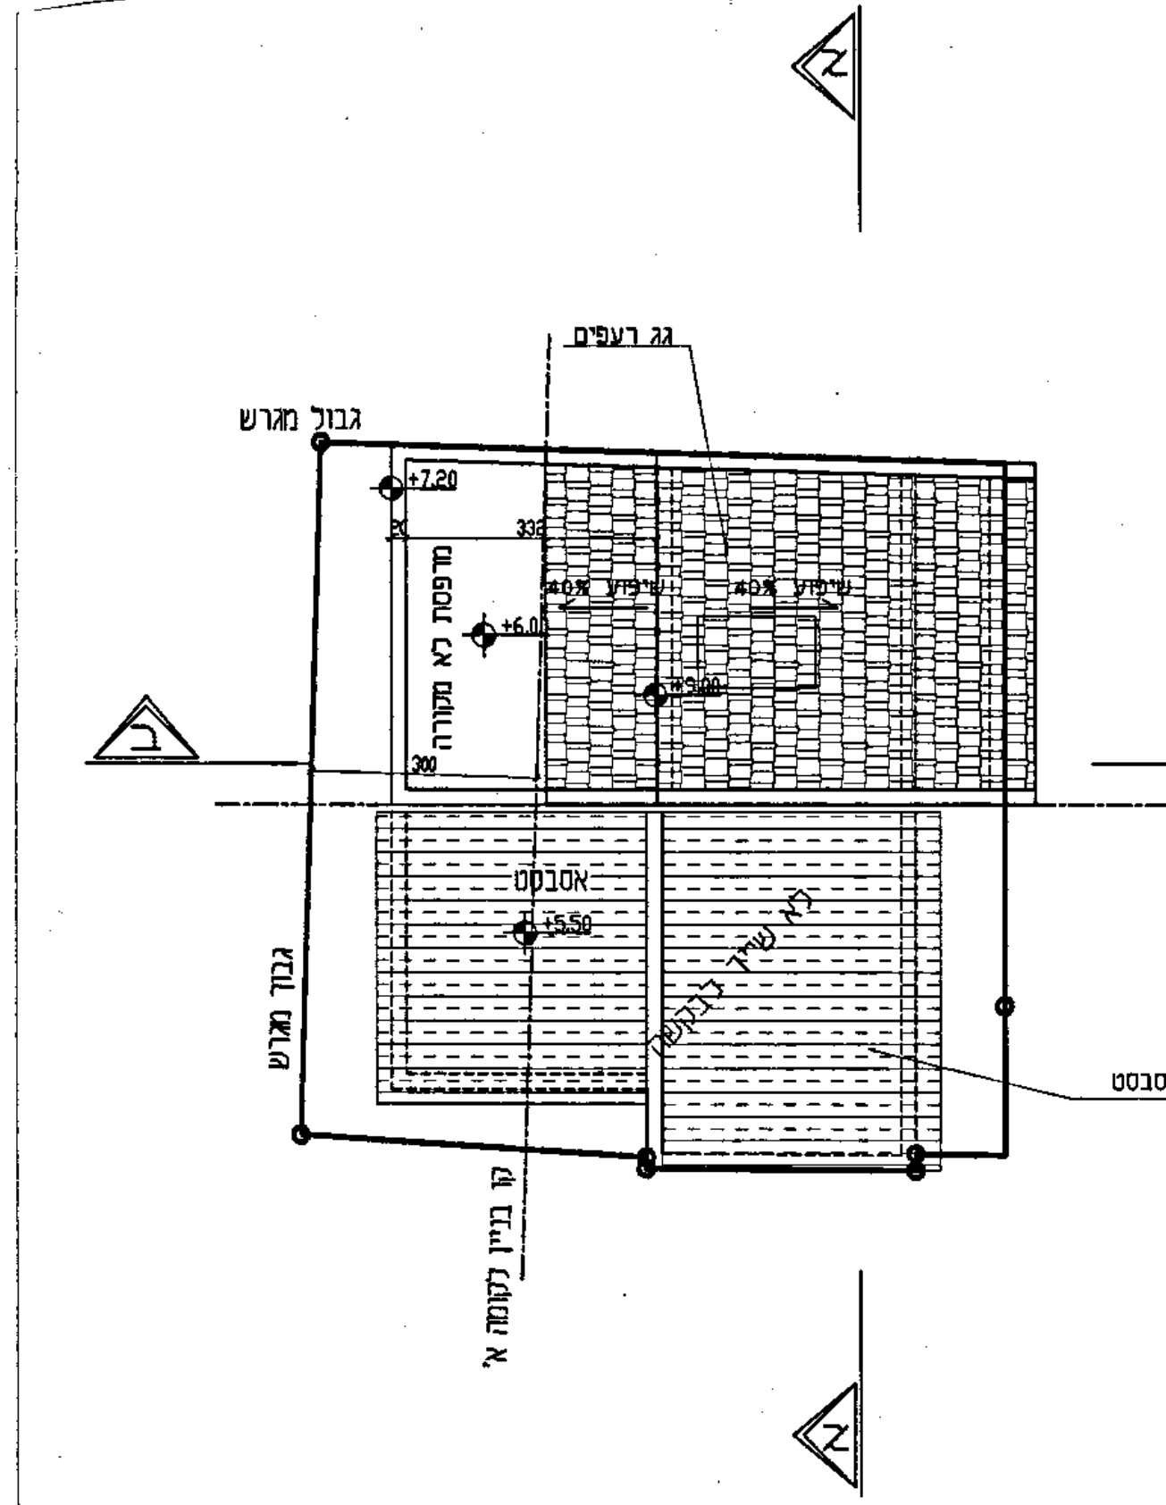

תכנית גג ק.מ. 1:100

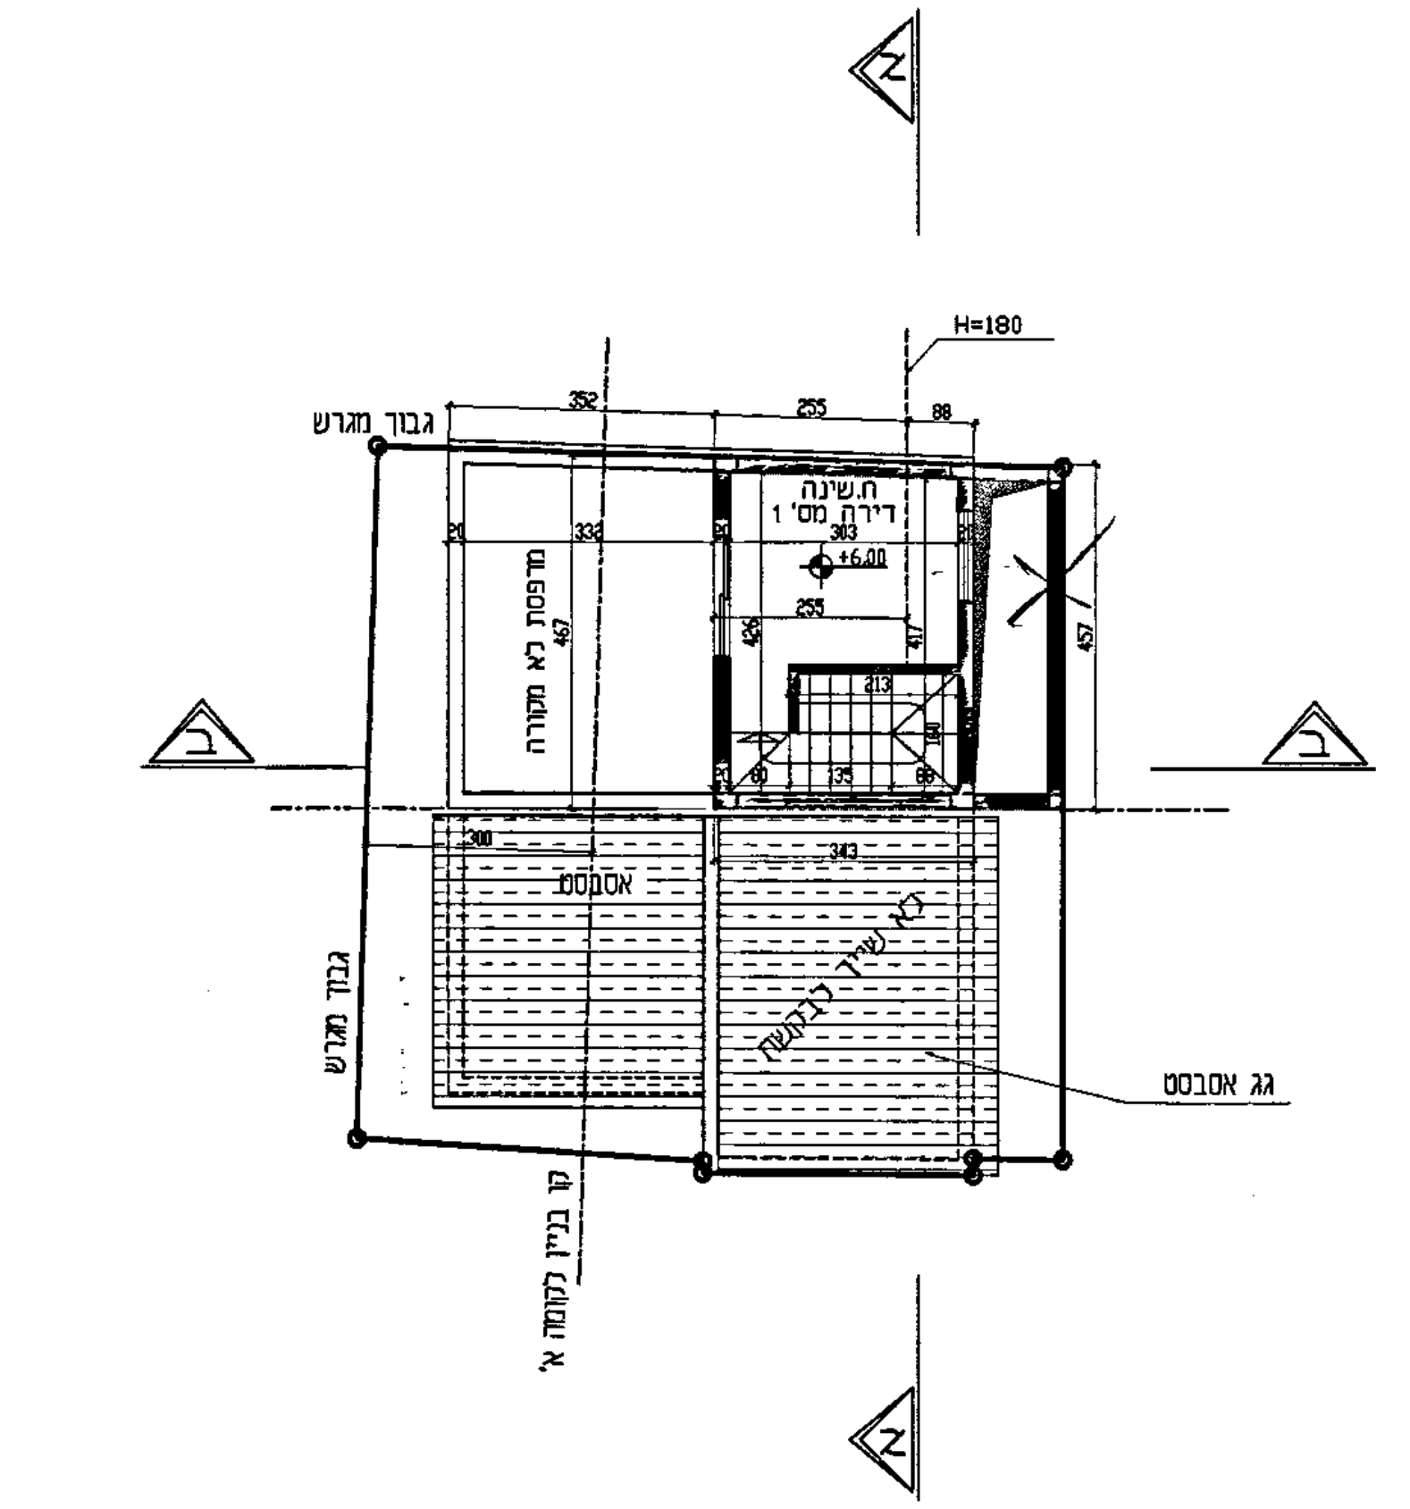

תכנית קומת גג ק.מ. 1:100

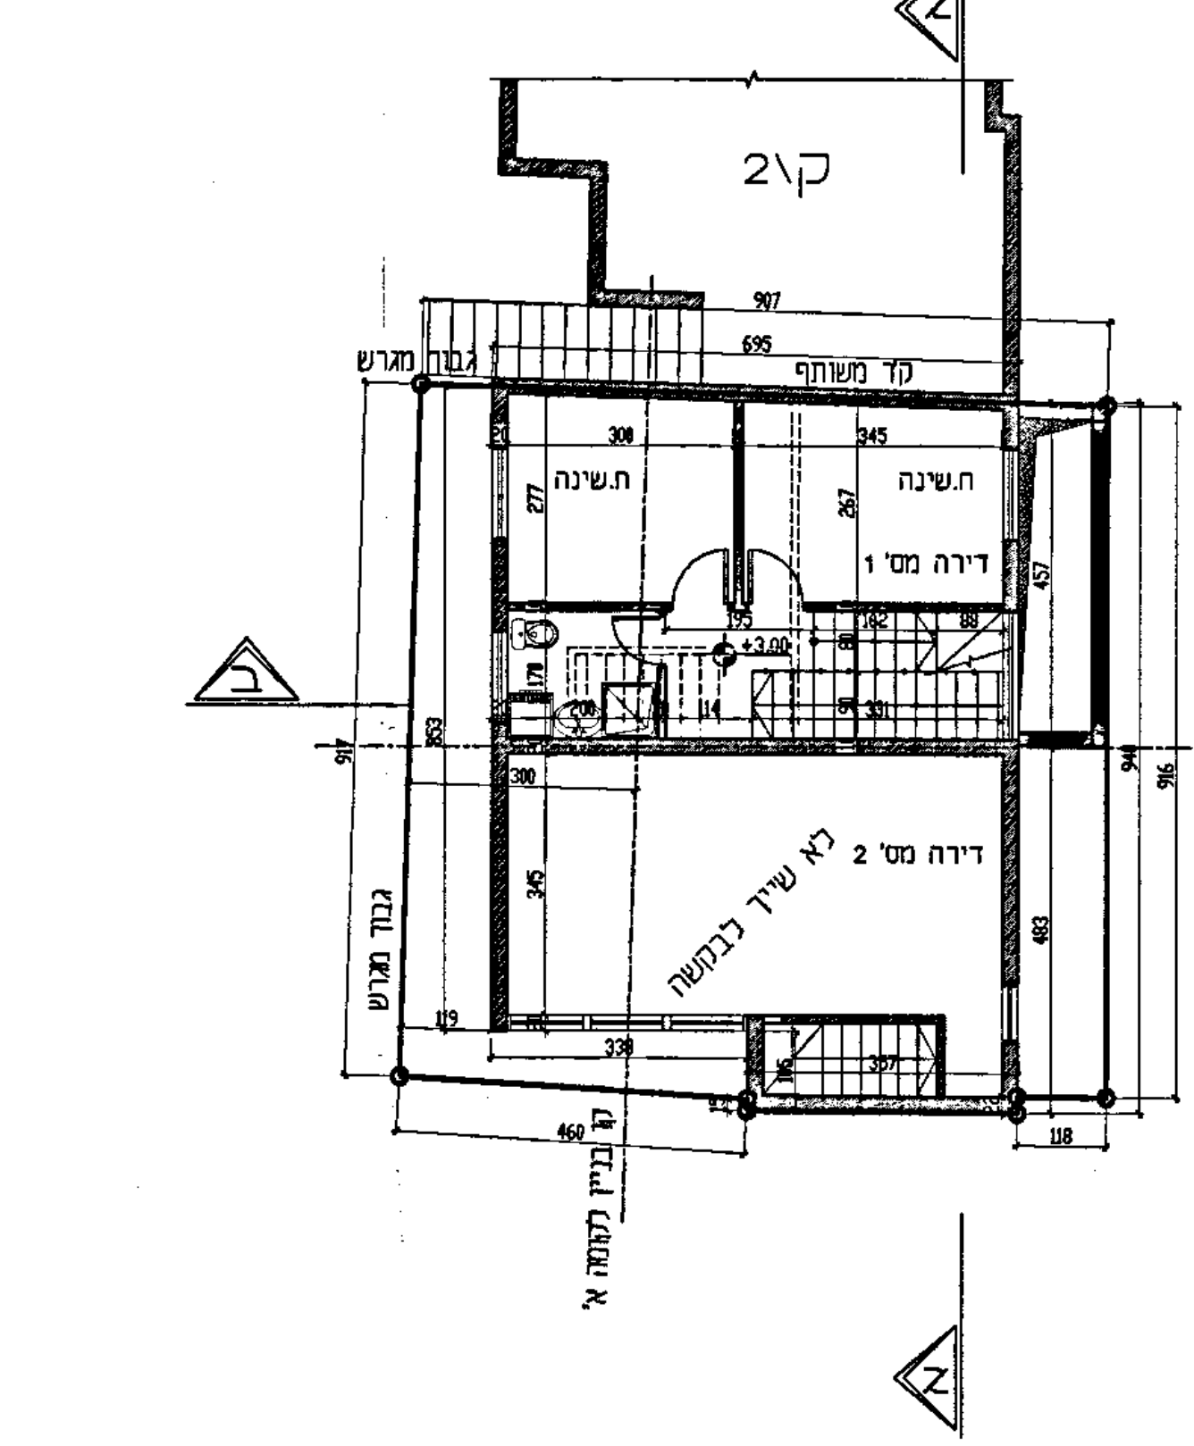

תכנית קומה א' ק.מ. 1:100

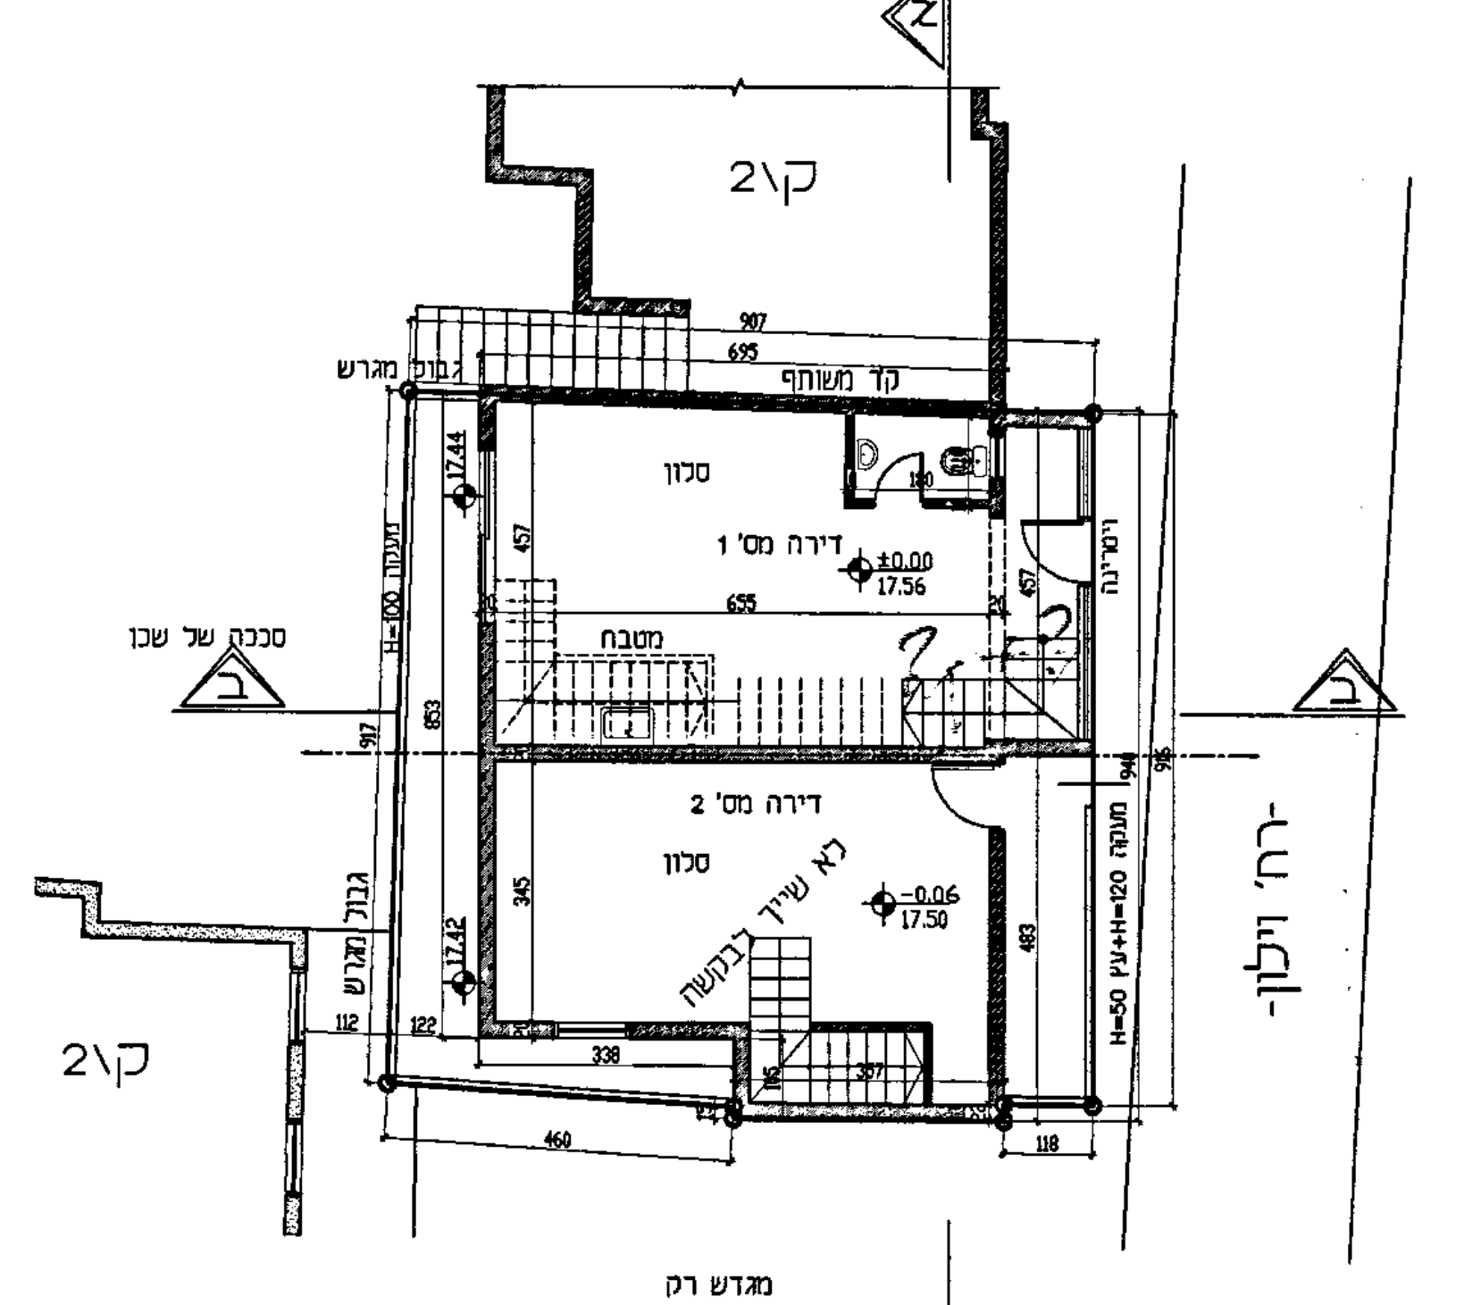

תכנית קומת קרקע

חישוב שטחים

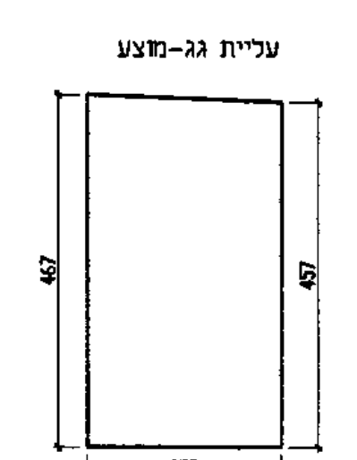

דירה מס' 1

שטח	מס'	חישובים	סה"כ מ"ר
ק.קרקע-קיים בהיתר	⊕	5.40 x 12.00	37.78
ק.א'-קיים בהיתר	⊕	1.45 x 0.70	32.39
עליית גג-מוצע	⊕	(4.70+4.57)/2x3.30	11.78
סה"כ שטח הדירה			81.95

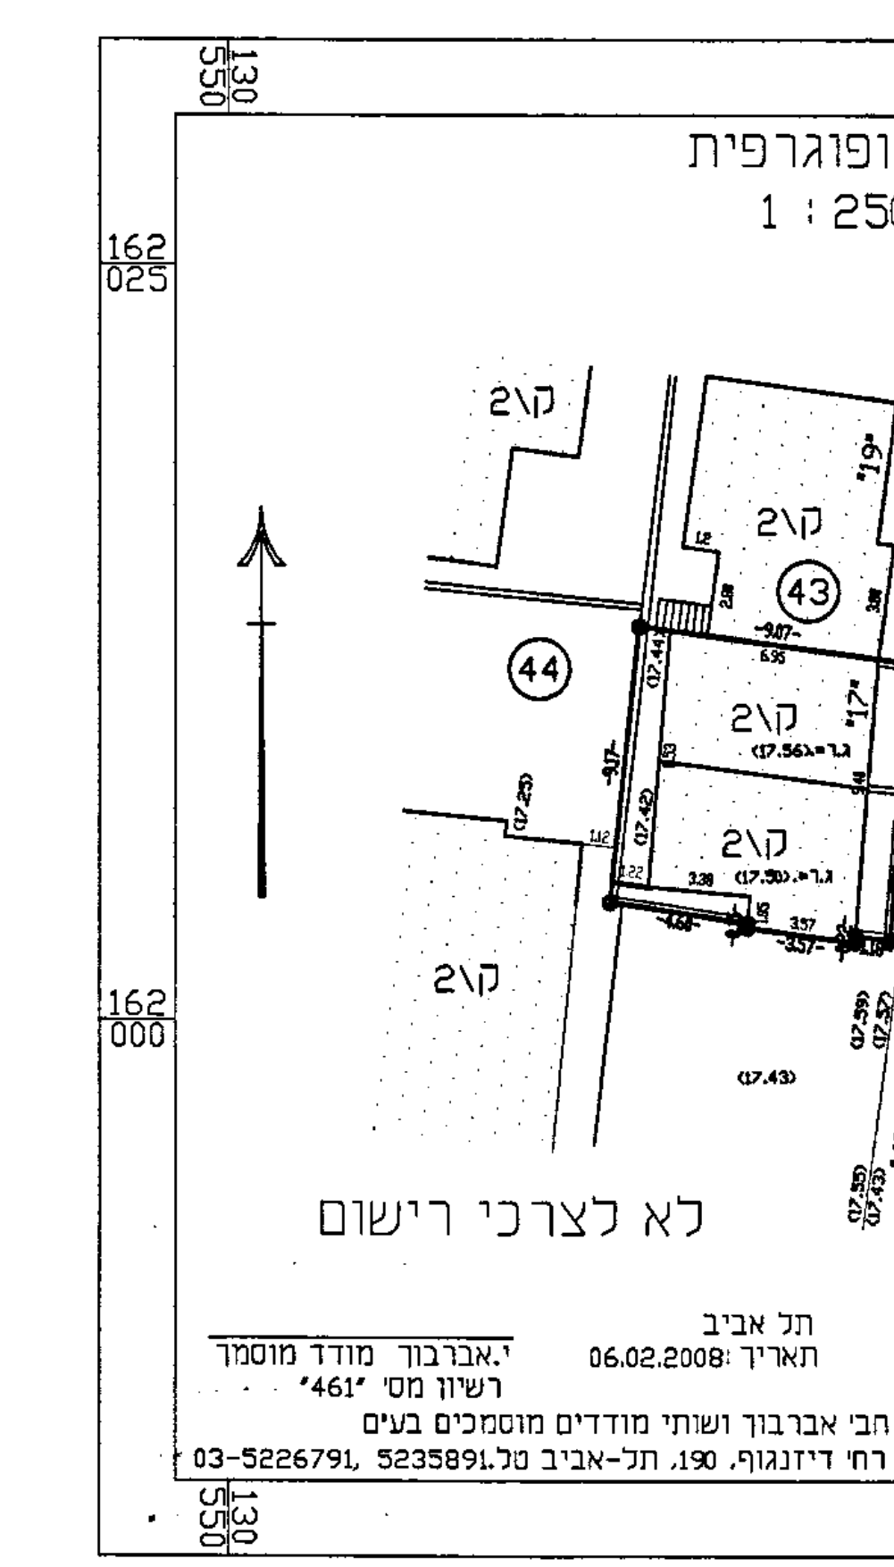

מפה טופוגרפית
1 : 250

תל-אביב
גוש : 6135
חלקה : 43(חלק)
שטח לפי נסח טאבו : 0.085 ד'
שטח מדוד : 0.085 ד'
הוכן עבור : משפי זבולונוב
מהות הבקשה : היתר בניה

תרשים הסביבה 1:1250

לא לצרכי רישום

הנני מצהיר בזה שהמפה נעשתה לפי חוק התכנון והבניה, התקנות וההנחיות של עיריית תל-אביב-יפו.

תל אביב
תאריך: 06.02.2008

י. אברבוך מודד מוסמך
רשיון מס' "461"

הערות:
1. המספרים בסוגריים מציינים גבהים.
2. הגבהים מבוססים על נ.ג. עירונית מס' 187 שגובהה 17.549 מ'.

חבי אברבוך ושותי מודדים מוסמכים בעים
רחי דיזנגוף, 190, תל-אביב טל. 03-5226791, 5235891

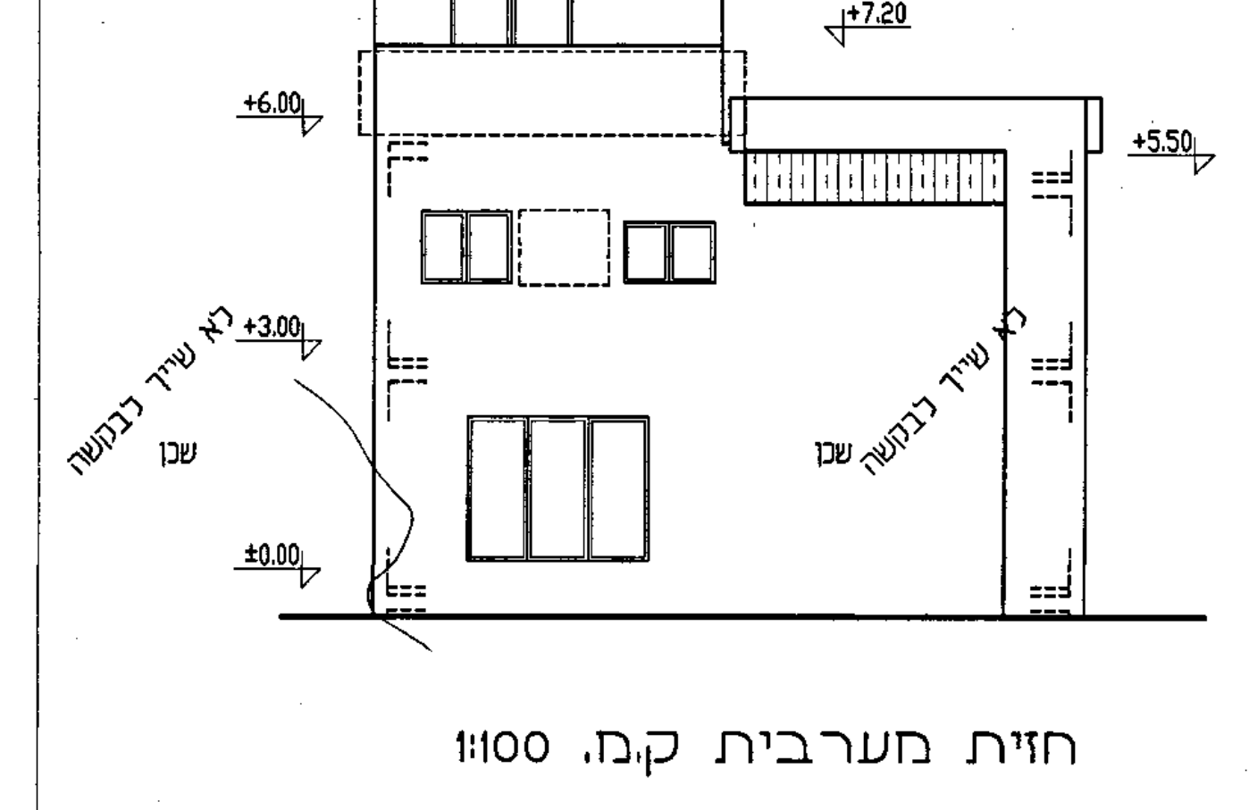

חזית מערבית ק.מ. 1:100

חומרי גמר:
טיח חלק בהיר כדוגמת הקיים וכדוגמת בית שכן

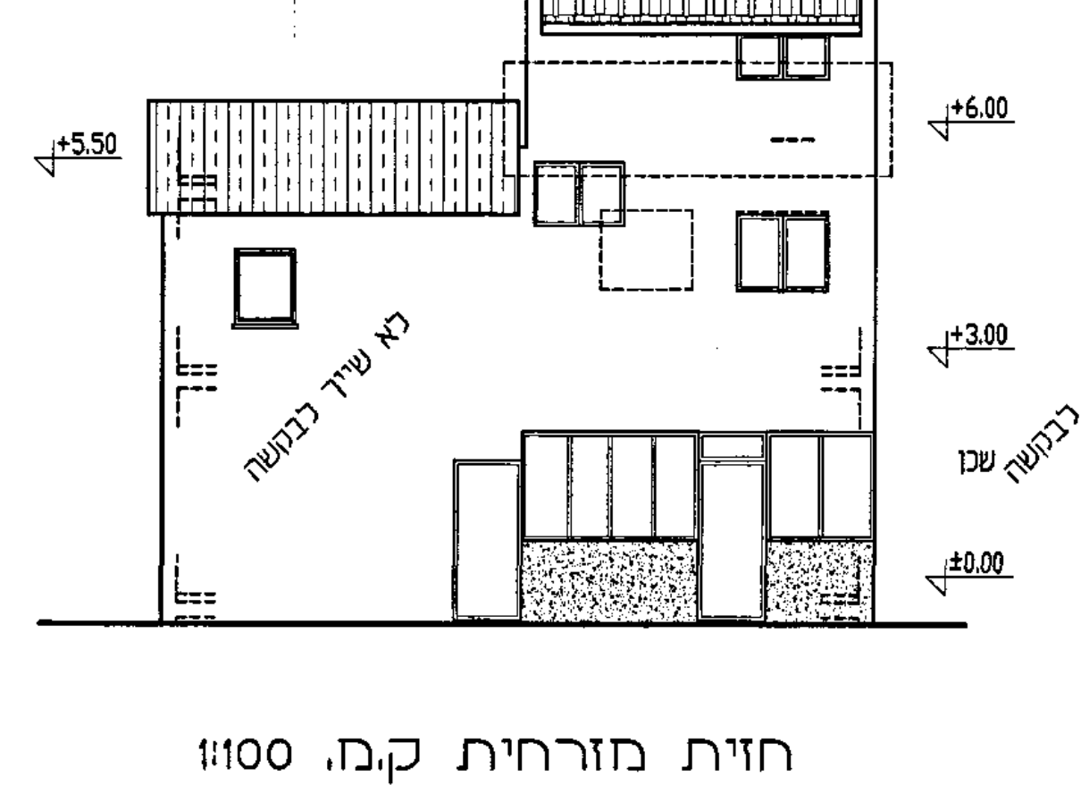

חזית מזרחית ק.מ. 1:100

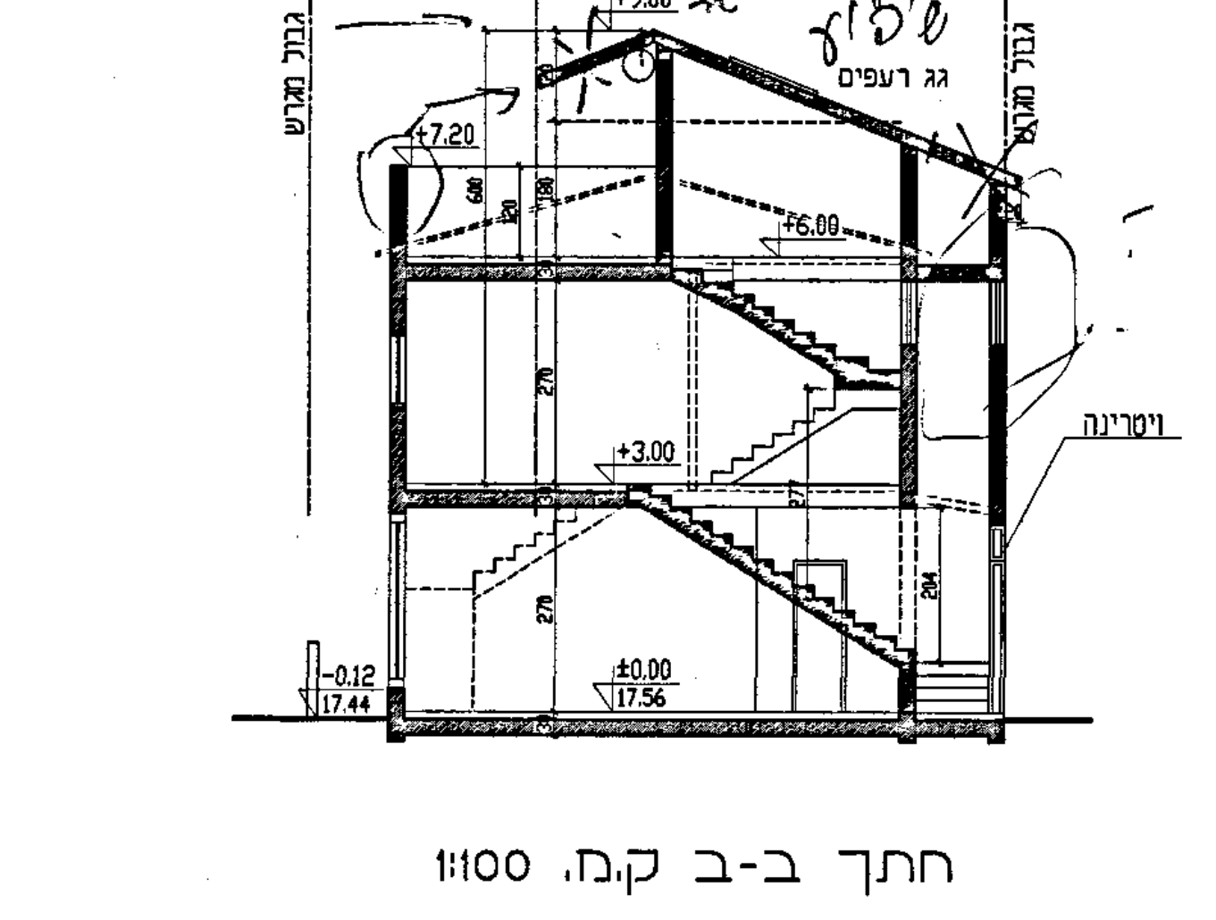

חתך ב-ב ק.מ. 1:100

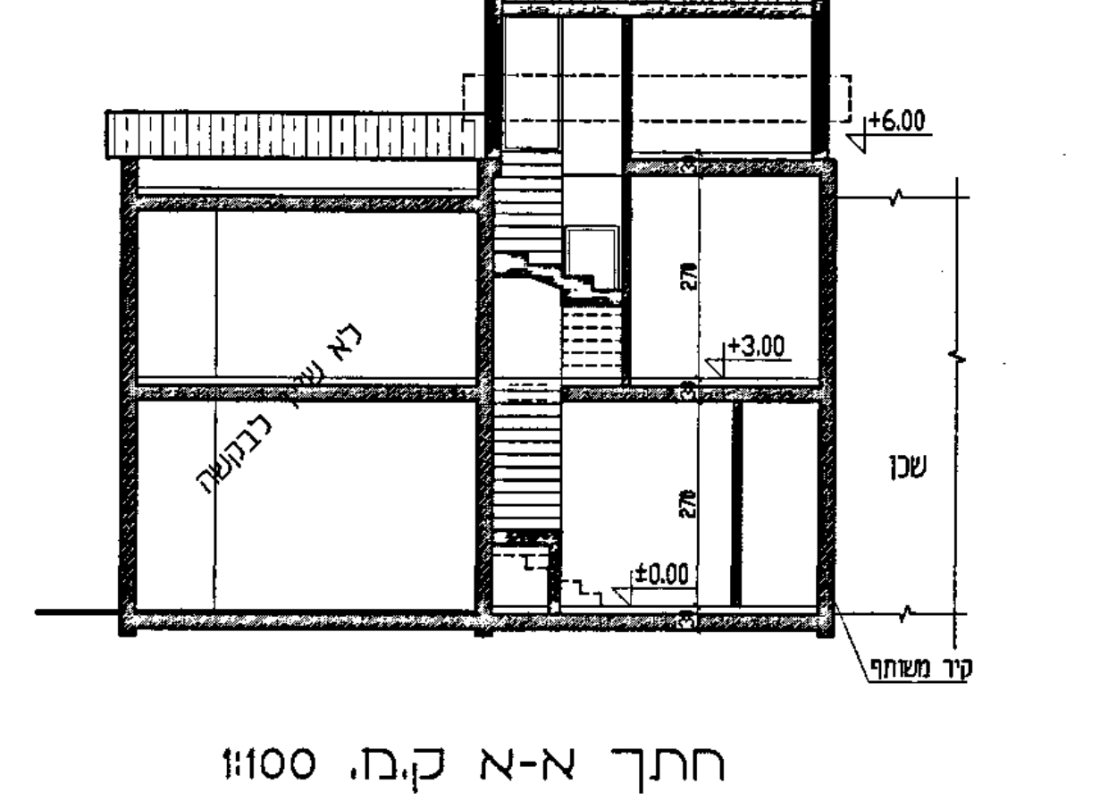

חתך א-א ק.מ. 1:100

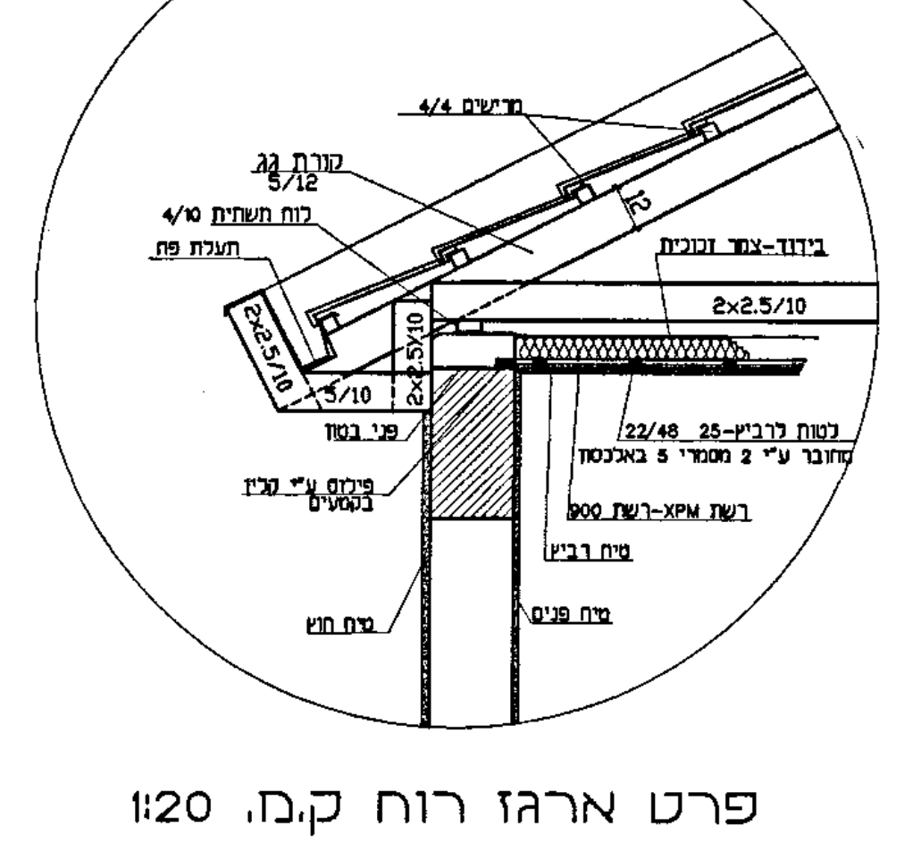

פרט ארגז רוח ק.מ. 1:20

22

עיריית תל-אביב-יפו
אגף רישוי בנייה
אדריכל דוד גוטמן
אדריכל הרישוי

עיריית תל-אביב-יפו

מינהל ההנדסה, אגף רישוי ופיקוח על הבנייה
שדרות בן-גוריון 68 תל-אביב 64514 (פקס 5231340) טלפון 5217045 ,5217120

לכבוד
☐ הוועדה המקומית לתכנון ולבנייה
☐ רשות הרישוי המקומית

08926

חוק התכנון והבנייה, התשכ"ה-1965
תקנות התכנון והבנייה (בקשה להיתר תנאיו ואגרות) התש"ל-1970

בקשה להיתר בנייה או לשימוש במקרקעין

יש להקפיד למלא את כל הפרטים בטופס הבקשה ולצרף מסמכים כמפורט ברשימת התיוג המצורפת.

על פי טופס 1 תקנה 2(א)

מס' תיק הבניין	מס' בקשה קודמת להיתר בנייה	מס' הבקשה למידע	מתאריך
4063-017	2003-0292	N2007-2899	22/112007

עיריית תל-אביב-יפו
מח' רישוי בנייה
נתקבל
05-12-2008

א. פרטי הנכס והמבקשים

הכתובת	רחוב	מס' בית	גוש	חלקה	תת חלקה	מגרש	הוראות התכניות החלות על המקום
	וילון	17	6135	43			ג 2215

פרטים אישיים	שם משפחה / שם פרטי	שם חברה או תאגיד	מס' זהות/חברה או מס' רישום תאגיד	רחוב ומספר בית / ישוב ומיקוד	מספר טלפון / מספר פקס
מבקש 1	זבולונוב אנגליקה		3009397933	רח' וילון 17, ת"א	053985358
מבקש 2					
מבקש 3					
בעל הזכות בנכס					
החוכר					
עורך הבקשה הראשי	ז'בגורסקי אלכס		14687859	רח' גרינבוים 14 תל אביב-יפו, 68109	0522544457 03 9510030
מתכנן שלד הבניין	ז'בגורסקי אלכס		14687859	רח' גרינבוים 14 תל אביב-יפו, 68109	0522544457 03 9510030

ב. מהות הבקשה

☐ בקשה לתוספת בנייה ☐ בקשה להרחבת דיור (במסגרת הרחבת דיור שכונתית)

☐ תוספת ______ קומות לבניין

הכוללות : ☐ ______ יחידות דיור

☐ ______

☒ תוספת בנייה בקומה גג ☒ לחזית ☒ לאחור ☐ לצד

בשטח של 11.78 מ"ר

שטח הדירה / המשרד לאחר התוספות יהיה 81.95 מ"ר

☐ שינויים פנימיים הכוללים: ______

☐ אישור מצב קיים

☐ ______

המקום משמש כיום ל- מגורים

☒ בהיתר ☐ בלי היתר

ג. מפרט - תיאור הבקשה

תיאור הקיים על המגרש: פרט מספר מבנים, גובהם, מקומם, ייעודם וכד'
קיים בניין בן 2 קומות
2 יח' דיור

שימוש עיקרי: ☒ מגורים ☐ מלונאות ☐ תעשיה ☐ חקלאי ☐ משרדים ☐ בידור ☐ בנין ציבורי ☐ מלאכה ☐ מסחר ☐ נופש וספורט ☐ שימוש אחר

סוג העבודה או השימושים המוצעים: ☒ תוספת לבניין ☐ הריסה ☐ שינוי בשימוש ☐ שינוי לבניין ☐ תיקונים ממטרה ______ למטרה ______

הגורם שמבוצעת בעבורו הבנייה: ☐ משרד ממשלתי ☐ מוסד ציבורי ☐ בנה ביתך ☐ רשות מקומית ☒ גורם פרטי ☐ אחר: ______

שטחים	שטח המגרש/החלקה		שטח הבנייה הכולל המבוקש		אחוזי הבנייה	
	85.00	מ"ר	81.95	מ"ר	96.66	

אם במסגרת הרחבת דיור שכונתית: מספר יחידות דיור מורחבות 1; מספר תכנית ההרחבה ג 2215

ד. חומרי הבנייה

סוג הבנייה: ☒ רגילה ☐ בית מוכן ☐ מתועשת ☐ אחר

קירות חיצוניים: ☐ בטון מזוין ☒ בלוקים ☐ אבן טבעית ☐ לבנים שרופות ☐ אחר

חומרי גימור: ☐ אבן מלאכותית ☐ אבן טבעית ☒ טיח ☐ זכוכית ☐ אחר

תקרות: ☒ בטון מזוין ☐ עץ ☐ אחר

גג: ☐ בטון מזוין ☒ רעפים ☐ אסבסט ☐ טיח ☐ אחר

גדרות: ☐ אבן טבעית ☐ אבן מלאכותית ☐ בטון ☐ בלוקים ☐ ברזל ☐ עץ ☐ רשת ☐ אחר; קיימות ___מ"א מוצעות ___מ"א סה"כ ___מ"א

מקרא חומרים (צבעים): בטון או בטון מזוין; בלוקים או לבנים מבטון; סיליקט או לבנים אדומות; אבן; עץ; איטונג; זכוכית; הריסה; אחר

ה. השטחים המבוקשים לבנייה (על-פי תכנית הבנייה) והמותרים לבנייה (על-פי "אסמכתא": חוק, תקנות, תכנית) בכל מפלס בנפרד ולפי שימוש

הקומה/המפלס בבניין (לפי פירוט המופיע בהסברים בכריכת התיק הוורוד – תיק הבקשה להיתר)	(א) מגורים: קיים בהיתר	קיים ללא היתר ומבוקש לאישור בדיעבד	בנייה חדשה מוצעת	מותר	(ב) שטחי השירות: סך כל שטחי השירות	"אסמכתא" לשטחים המותרים	סך כל שטחי הבנייה העיקריים לשימושים השונים: מ"ר	%משטח המגרש	סך כל השטחים המותרים	(ג) סך כל שטחי הבניין: מ"ר	%משטח המגרש	סך כל השטחים המותרים	משטחים לא מקורים
±0.00	37.78			51.00/2		2215	37.78	44.44	119.00/2	37.78	44.44	119.00/2	
+3.00	32.39			68.00/2		2215	32.39	38.10		32.39	38.10		
+6.00			11.78	12.00		ג	11.78	14.12	12.00	11.78	14.12	12.00	
ס"ה מעל לקרקע	70.17		11.78				81.95	96.66		81.95	96.66		
ס"ה מתחת לקרקע													
סה"כ	70.17		11.78				81.95	96.66		81.95	96.66		

ו. פרטי הבנייה - לשימוש הלשכה המרכזית לסטטיסטיקה

הייעוד	שטח הבנייה ברוטו – לפי ייעוד: פירוט הייעוד (כגון דירות למגורים, בתי מלון וכו')	השטח על פי ההיתר	מספר חדרים	מספר דירות	מספר מגורים	
למגורים			1			
להארחה			2			
לעסקים ולמסחרים			3			
לבנייני ציבור			4			
לתעשיה ולמלאכה			5			
למשק חקלאי			6			
למקלט או למרתף						
למבני עזר						
סך כל שטח הבנייה						סה"כ

מספר היתר הבנייה; תאריך היתר הבנייה: שנה חודש; תאריך התחלת הבנייה: שנה חודש; תאריך גמר הבנייה: שנה חודש; מספר הקומות כולל קומות עמודים מפולשת

ז. קווי בנייה

הכיוון	מוצע	מותר	במטר	ב- %
לרחוב (שם)				
לרחוב (שם)				
לצד				
לאחור				

ח. מספר יחידות דיור

אם השימוש המבוקש הוא מגורים – רשום להלן:
מספר הדירות הקיימות ______ מספר הדירות המבוקשות ______ מספר הדירות המותרות ______

ט. הבקשה מוגשת לאישור

☐ הוועדה המקומית

הבקשה כוללת בקשה להקלה – כלהלן:

פירוט הבקשה להקלה	נימוקי הבקשה להקלה
1.	
2.	
3.	

☐ רשות הרישוי המקומית
☐ רשות הרישוי המקומית באמצעות מורשה להיתר

י. הצהרת עורך הבקשה הראשי

☐ אני מצהיר על נכונות הפרטים בסעיפים א עד ט.
תאריך 04/2008 שם ז'בגורסקי א. חתימה X

יא. חתימות נוספות

	תאריך	שם	חתימה
המבקש	04/2008	זבולונוב	X
בעל הזכות בנכס/בעל הנכס/החוכר	04/2008	זבולונוב	
מתכנן שלד הבניין	04/2008	ז'בגורסקי	

לשימוש המשרד: התוכנית תואמת את המצב בשטח	הערות הפיקוח	☐ כן ☐ לא	☐ הוכן דוח לתביעה משפטית ☐ הוגשה תביעה משפטית ☐ הוגשה תביעה חוזרת	מס' הדוח/התביעה	תאריך הדוח/התביעה	הנדון בדוח / הנדון בתביעה	הערות	תאריך	שם	חתימה

יב. מינויים מטעם מבקש ההיתר - נתמנה אדם אחד ליותר מתפקיד אחד, ימלא פרטיו ליד כל אחד מהתפקידים שהוא ממלא על פי הוראות כל דין.

מינוי עורך הבקשה הראשי: אני ממנה בזה את ז'בגורסקי אלכס בעל/ת מס' זהות 14687859 הרשום בסעיף א' להיות עורך הבקשה הראשי להיתר, ולייצגני לפני מוסדות התכנון והרשויות המוסמכות בכל הנוגע לטיפול בבקשה להיתר ולקבלתו, לרבות התיקונים ככל שידרשו הרשויות המוסמכות.

מינוי עורכי בקשה לפי תחומים: אני ממנה בזה את הרשומים להלן להיות עורכי הבקשה להיתר בתחום הפעולה כרשום ליד שמם, ולייצגני בתחום פעולתם לפני מוסדות התכנון והרשויות המוסמכות בכל הנוגע לטיפול בבקשה להיתר ולקבלתו, לרבות התיקונים ככל שידרשו הרשויות המוסמכות.

שם משפחה ושם פרטי	תחום פעולה	המען	מספר טלפון	מספר פקס
1.	מתכנן האינסטלציה הסניטרית			
2.				

מינוי מתכנן שלד הבניין: אני ממנה בזה את ז'בגורסקי אלכס בעל/ת מס' זהות 14687859 הרשום בסע' א' להיות אחראי לתיכנון שלד הבנין שבעבורו מבוקש ההיתר, להגיש לוועדה המקומית לרשות הרישוי המקומית את החישובים לגבי הבניה שבעבורה מבוקש היתר ולפקח פיקוח עליון על הקמת השלד.

מינוי הקבלן האחראי לבנייה: ☐ אני ממנה בזה את ______ בעל/ת מס' זהות ______ ובעל תעודת רישום בפנקס הקבלנים מספר ______ במדור ______ ובעל ______ לביצוע עבודה בהיקף עד ______ לבצע את העבודה הנדונה בהיתר כמתחייב לפי כל דין.
☐ אני מצהיר, כי טרם מסרתי את ביצוע העבודה הנדונה בהיתר לידי קבלן, ומתחייב כי אמסור אותה לידי קבלן רשום בפנקס הקבלנים, כמתחייב על פי כל דין, והודיע על כך לרשות הרישוי המקומית טרם התחלת ביצוע העבודה, וחתימתו של הקבלן תצורף להודעה המפרטת את פרטי רישומו של הקבלן.

מינוי האחראי לביצוע שלד הבניין: ☐ אני ממנה בזה את ______ בעל/ת מס' זהות ______ כתובת ______ טלפון ______ פקס ______ הרשום לעיל להיות אחראי לביצוע שלד.
☐ אני מצהיר, כי טרם מיניתי אחראי/ת לביצוע עבודות בתחומים האלה: ______ ומתחייב לעשות זאת כמפורט בתקנות, ולהודיע על כך לרשות הרישוי המקומית טרם התחלת ביצוע העבודה.

מינוי אחראים לביקורת: ☐ אני ממנה בזה את הרשומים להלן להיות אחראים לביקורת על ביצוע עבודות בתחום הפעולה כרשום ליד שמם.

שם משפחה ושם פרטי	תחום פעולה	המען	מספר טלפון	מספר פקס
1.	אחראי ראשי			
2.				
3.				

☐ אני מצהיר כי טרם מיניתי אחראי/ם לביקורת על ביצוע עבודות את כולם או את קצתם בתחומים האלה: ______ ומתחייב לעשות זאת כמפורט בתקנות, ולהודיע על כך לרשות הרישוי המקומית טרם התחלת ביצוע העבודה.

X ______ X חתימת המבקש על המינויים

יג. הצהרות

הצהרת עורכי הבקשה כולל הצהרת עורך הבקשה על לחץ המים:
אנו החתומים מטה מצהירים בזה:
1) כל אחד מאתנו מאשר שהאמור בנוגע לרשומה שבסעיף "לעיל הוא נכון.
2) כל אחד מאתנו מסכים לקבל עליו את התפקיד המיועד לו בסעיף "לעיל.
3) אנו מצהירים, כל אחד בנוגע לתחום פעולתו, שיש לנו כישורים מקצועיים לערוך בקשה זו וכי בדקנו את המסמכים הנוגעים לבקשה, לרבות כל תכנית הנוגעת לבקשה, וידוע לנו כי אם הצהרה זו אינה נכונה, הרי היא תיחשב מסירת ידיעה שהיא כוזבת או מטעה בפרט חשוב, כמשמעותה בסעיף 214 לחוק, וצפויים לנו העונשים הקבועים לפי כל דין.
אני ז'בגורסקי אלכס (עורך בקשה ראשי) אחראי/ת לכך שהבקשה, ובכלל זה נספחיה, נערכה לפי מיטב הידיעה המקצועית ובהתאם לכל חיקוק החל על העבודה המוצעת, שכל הנתונים שנמסרו על ידי בבקשה זו נכונים ושהתכנון המוצע תואם את כל התכניות, פרט לסטיות שפורטו לעיל.
☐ אני עורך הבקשה מתכנן האינסטלציה הסניטרית, מצהיר בזאת ואחראי לכך שתכניות הבקשה בכל הנוגע לסידורים הסניטריים נערכו כדין וכי קויימו בהן הוראות החוק וההוראות למתקני תברואה התש"ל 1970 (הל"ת) לעניין זה, לרבות בדיקת לחץ המים הקיים בבנין ותכנון בהתאם.

	תאריך	שם משפחה ושם פרטי	מספר רישיון	חתימה
עורך בקשה ראשי		ז'בגורסקי אלכס	15320	
עורך בקשה 1 מתכ' האינס הסניט'				
עורך בקשה 2				

הצהרת מתכנן שלד הבניין:
אני החתום מטה (שם משפחה ושם פרטי) ז'בגורסקי אלכס מס' זהות 14687859
מהנדס רשוי מס' 15320 /הנדסאי בעל רישיון מס' ______ ("למבנה פשוט") מצהיר בזאת כדלקמן:
1) אני מסכים להיות מתכנן שלד הנדון בבקשה ולפקח פיקוח עליון על הקמת השלד.
2) אני מתחייב להגיש לפני מתן ההיתר, נושא הבקשה את החישובים הסטטיים בדבר ש בעבורה ההיתר.
3) ידוע לי, שאם אחרי הגשת הנתונים הסטטיים יתגלה צורך בשינוי מהותי בהם, אני מתחייב להגיש חישובים סטטיים מתוקנים מיד עם גילוי הצורך בכך.
4) אני מצהיר, כי יש לי כישורים מקצועיים לערוך בקשה זו וכי בדקתי את כל המסמכים הנוגעים לבקשה, לרבות כל תכנית הנוגעת לבקשה, וידוע לי כי אם הצהרה זו אינה נכונה, הרי היא תיחשב מסירת ידיעה שהיא כוזבת או מטעה בפרט חשוב, כמשמעותה בסעיף 214 לחוק, וצפויים לי העונשים הקבועים לפי כל דין.
5) ידוע לי כי עלי לשמור את תכניות הקונסטרוקציה לתקופה של לא פחות מ-10 שנים לאחר גמר הבנייה.
תאריך ______ חתימה ______ X

הצהרת האחראי לביצוע שלד הבניין (כאשר מונה):
אני החתום מטה (שם משפחה ושם פרטי) ______ מס' זהות ______
מהנדס רשוי מס' ______ /הנדסאי בעל רישיון מס' ______ ("למבנה פשוט") מצהיר בזאת כדלקמן:
1) אני מסכים להיות האחראי לביצוע שלד הבניין
2) אני מצהיר, כי יש לי כישורים מקצועיים להיות אחראי לביצוע שלד ______, ואני מתחייב לדאוג לביצוע שלד ______ על פי תוכניות והוראות של מתכנן השלד כפי ______ בכתב וכן למלא את תפקידי על פי שנקבע בכל חיקוק הנוגע לכך.
תאריך ______ חתימה ______

הצהרת אחראים לביקורת (כאשר מונו):
אנו החתומים מטה מצהירים בזה :
1) כל אחד מאיתנו מאשר שהאמור בנוגע לו ברשימה שבסעיף י"ב לעיל הוא נכון.
2) כל אחד מאיתנו מסכים לקבל עליו את התפקיד המיועד לו בסעיף י"ב.
3) אנו מצהירים כל אחד בנוגע לתחום פעולתו, שיש לנו כישורים מקצועיים לערוך את הביקורת כהלכה ולדווח על תוצאותיה לרשות הרישוי המקומית כמתחייב על פי כל דין.
אני ______ (עורך הביקורת הראשי) אחראי/ת לכך שהביקורת תיערך על פי מיטב הידיעה המקצועית, ושכל הדיווחים לרשות הרישוי המקומית ייערכו על פי כל דין.

תאריך	שם משפחה ושם פרטי	מספר רישיון	חתימה

לא מלבנה או לא מרפסת
4,67×2,53