04/06/2008

סיכום בדיקה תחנה פיקוח בניה בקשה 20080926 לכתובת וילון 17

פגישות תאום תכנון בתחנת פיקוח בניה

תא' פגישה	בעל עניין	שם משתתף	ללא מ	סטטוס
04/06/2008			V	תוכנית תוא

החלטת תחנה מ-04/06/2008 : תוכנית תואמת את המצב בשטח

תוכנית תואמת את המצב בשטח. המבוקש טרם נהרס, טרם בנוי

מטפל: רומן זייץ

אינג' רומן זייץ
מהנדס מפקח
מח' פיקוח על הבניה
עיריית תל-אביב - יפו

גוש סופי

גוש סופי

תל-אביב
גוש: 6135
חלקה: 43 (מחלקה)
שטח לפי נסח טאבו: 0.085 ד'
שטח מדוד: 0.085 ד'
הוכן עבור: משפ' דבולנוב
מהות הבקשה: היתר בניה

תרשים הסביבה 1:1250

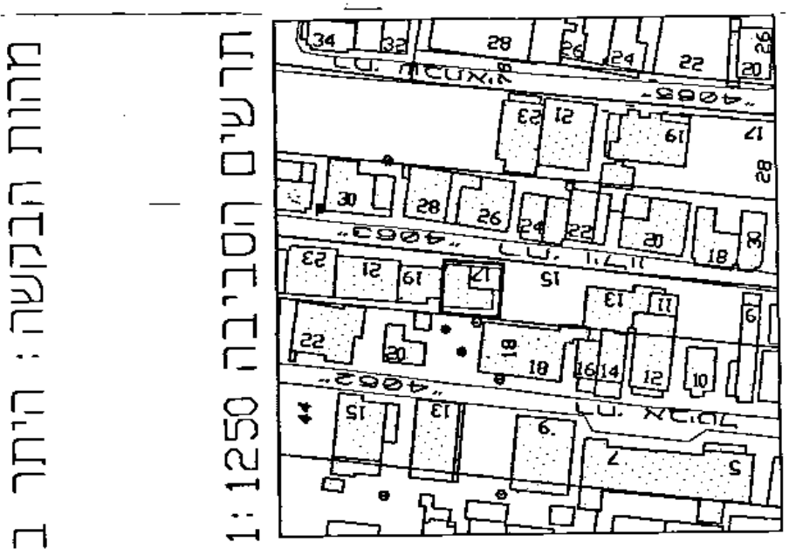

מפה טופוגרפית 1:250

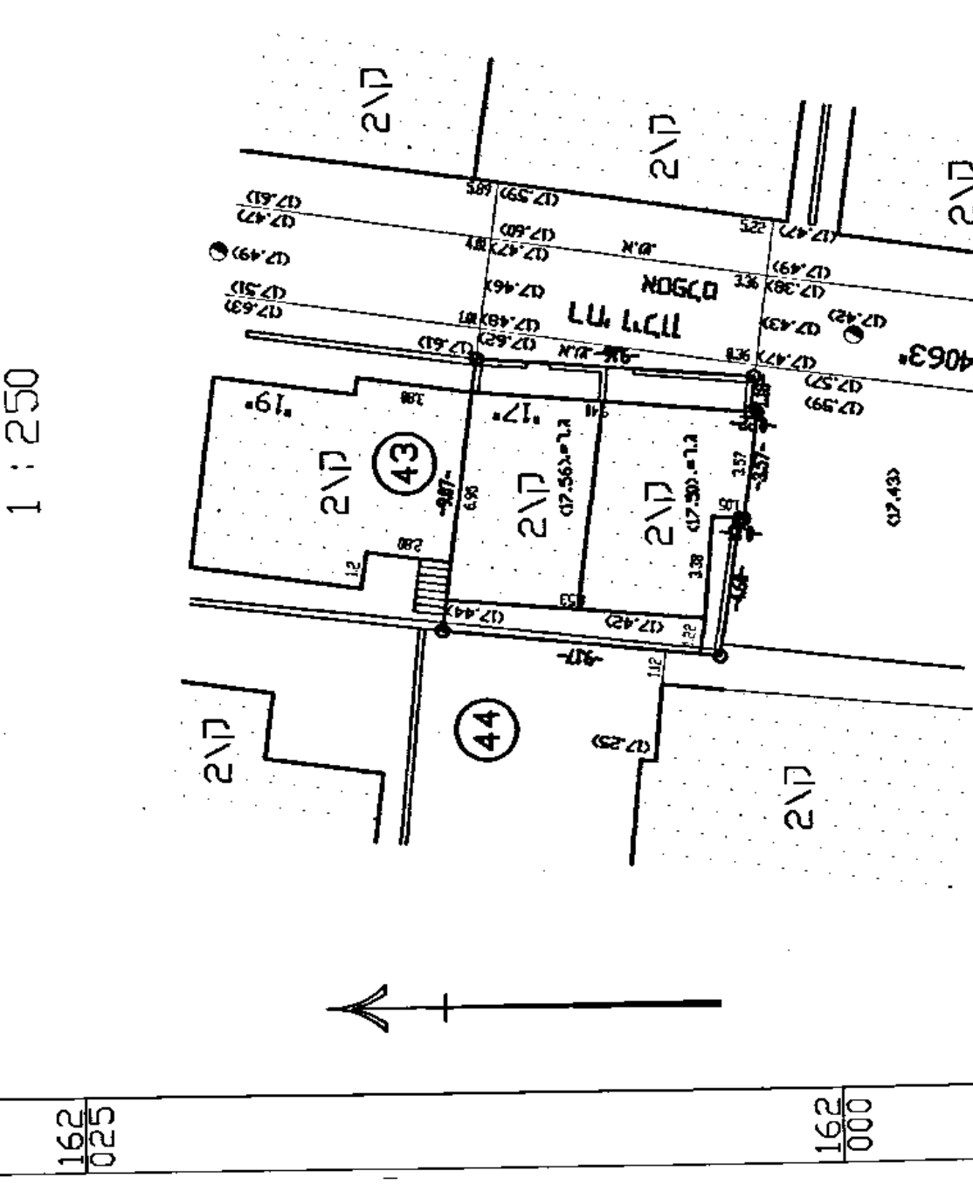

וילון
43
44
קוא

לא לצרכי רישום

הערות:
1. המספרים בסוגריים מציינים גבהים.
2. הגבהים מבוססים על נ.ג. עירוני מס' 187 שגובהה 17.549 מ'.

הנני מצהיר בזה שהמפה נעשתה לפי מדידה שנעשתה על ידי
תל אביב 06.02.2008

אברבוך מודד מוסמך
רשיון מס' 461
רח' דיזנגוף 190 תל-אביב 03-5226791, 5235891

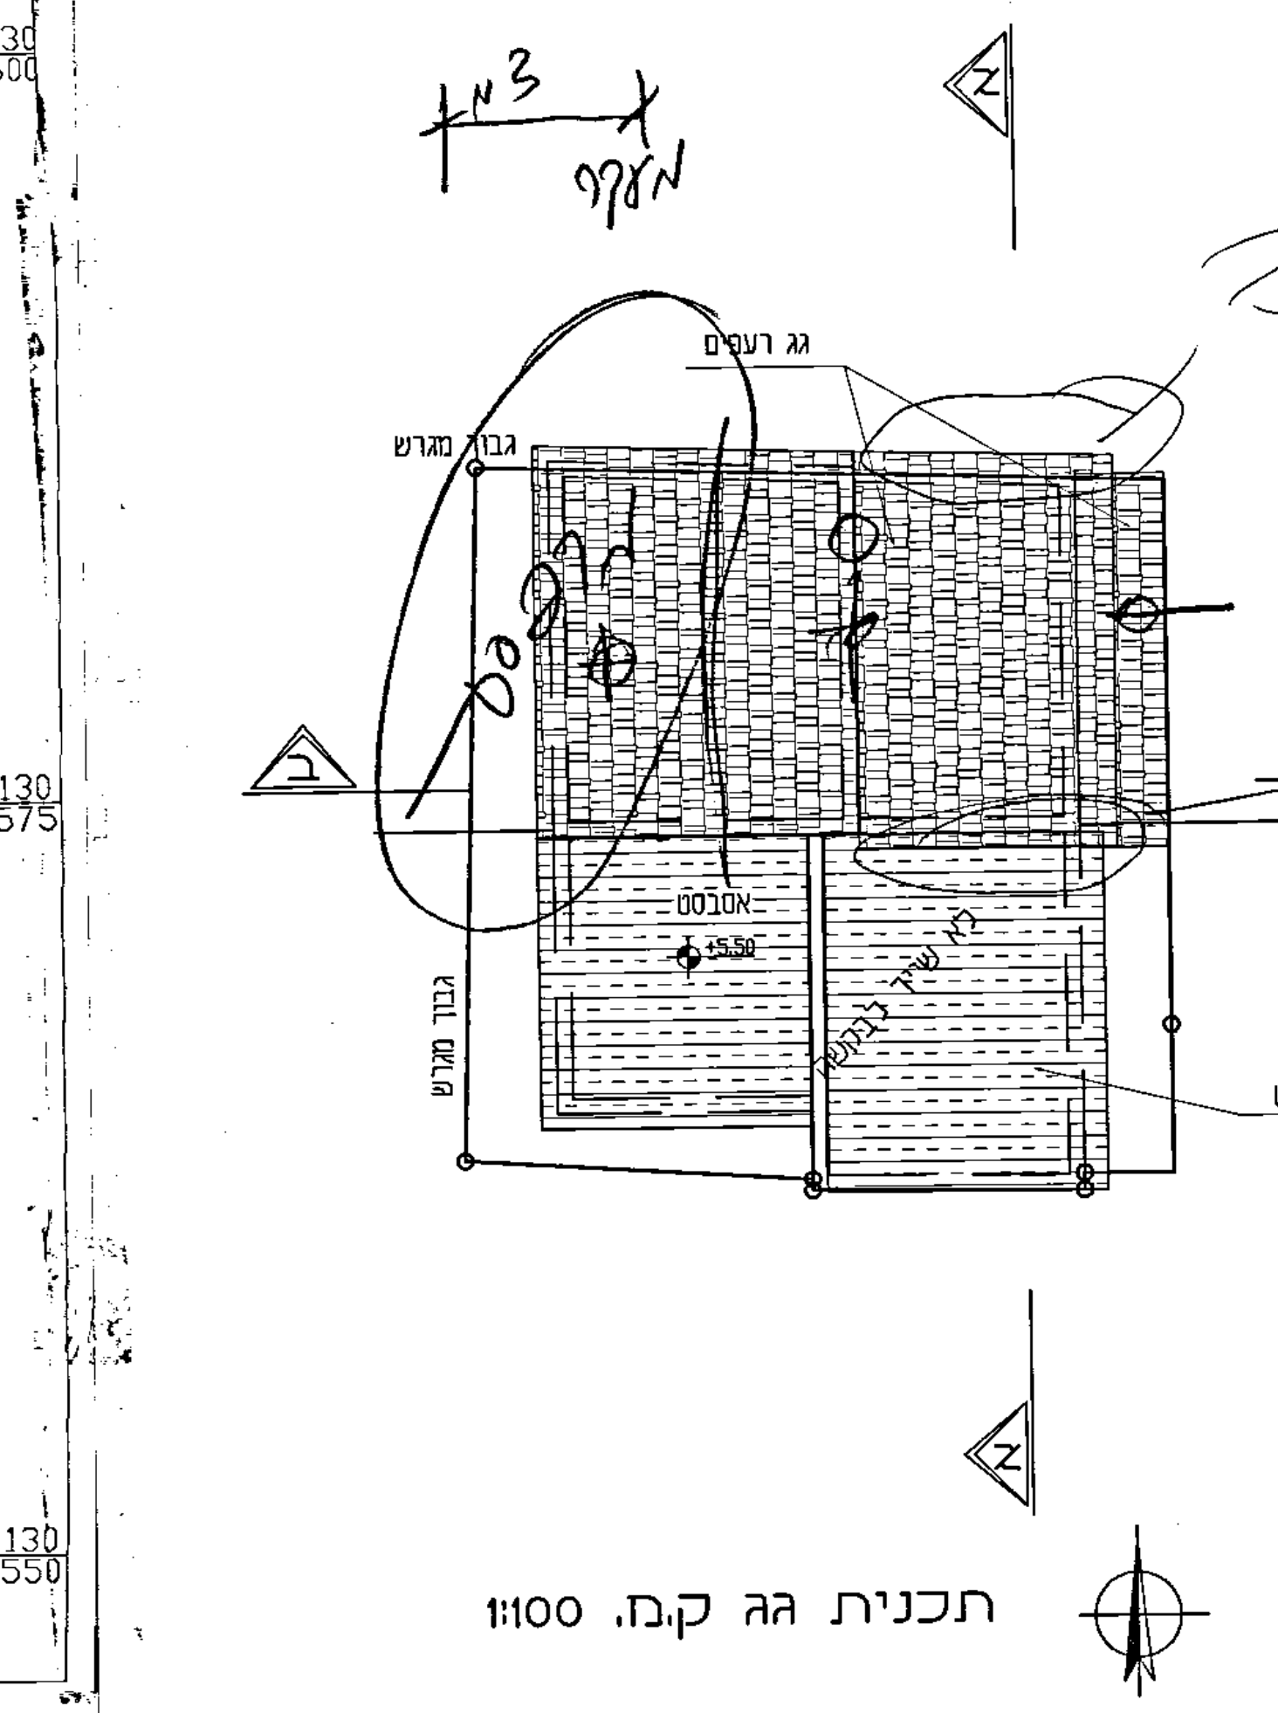

3 מ'
מעקה
גג רעפים
גבול מגרש
אסבסט
+5.50
לא שייך לבקשה
גג אסבסט
רעפים

תכנית גג קנ.מ. 1:100

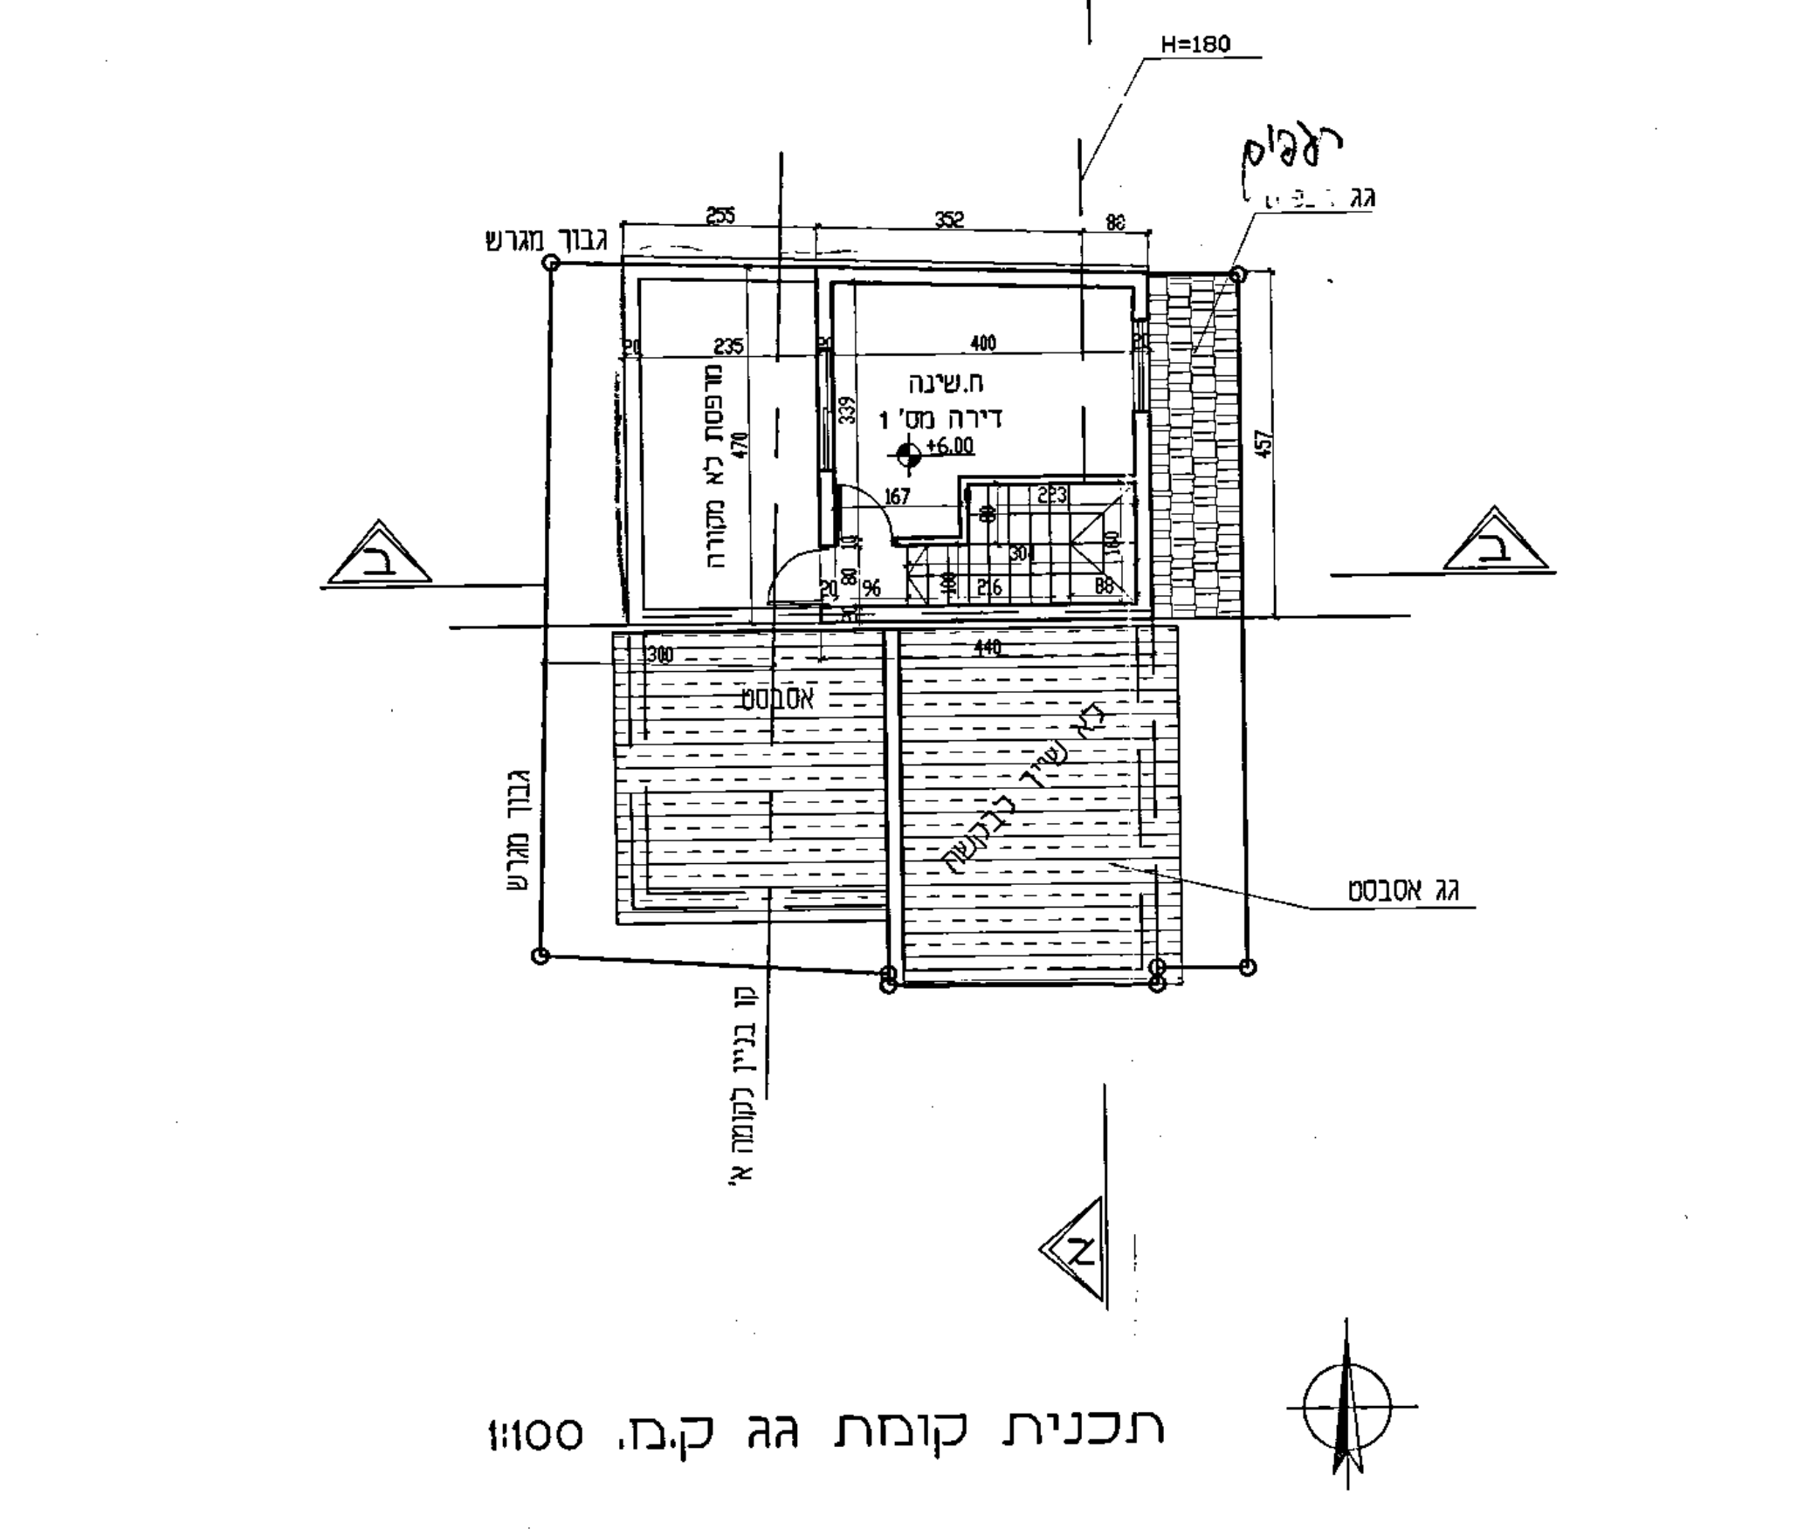

H=180
רעפים
גג אסבסט
גבול מגרש
ח.שינה
דירה מס' 1
+6.00
מרפסת לא מקורה
אסבסט
לא שייך לבקשה
קו בניין לקומה א'

תכנית קומת גג קנ.מ. 1:100

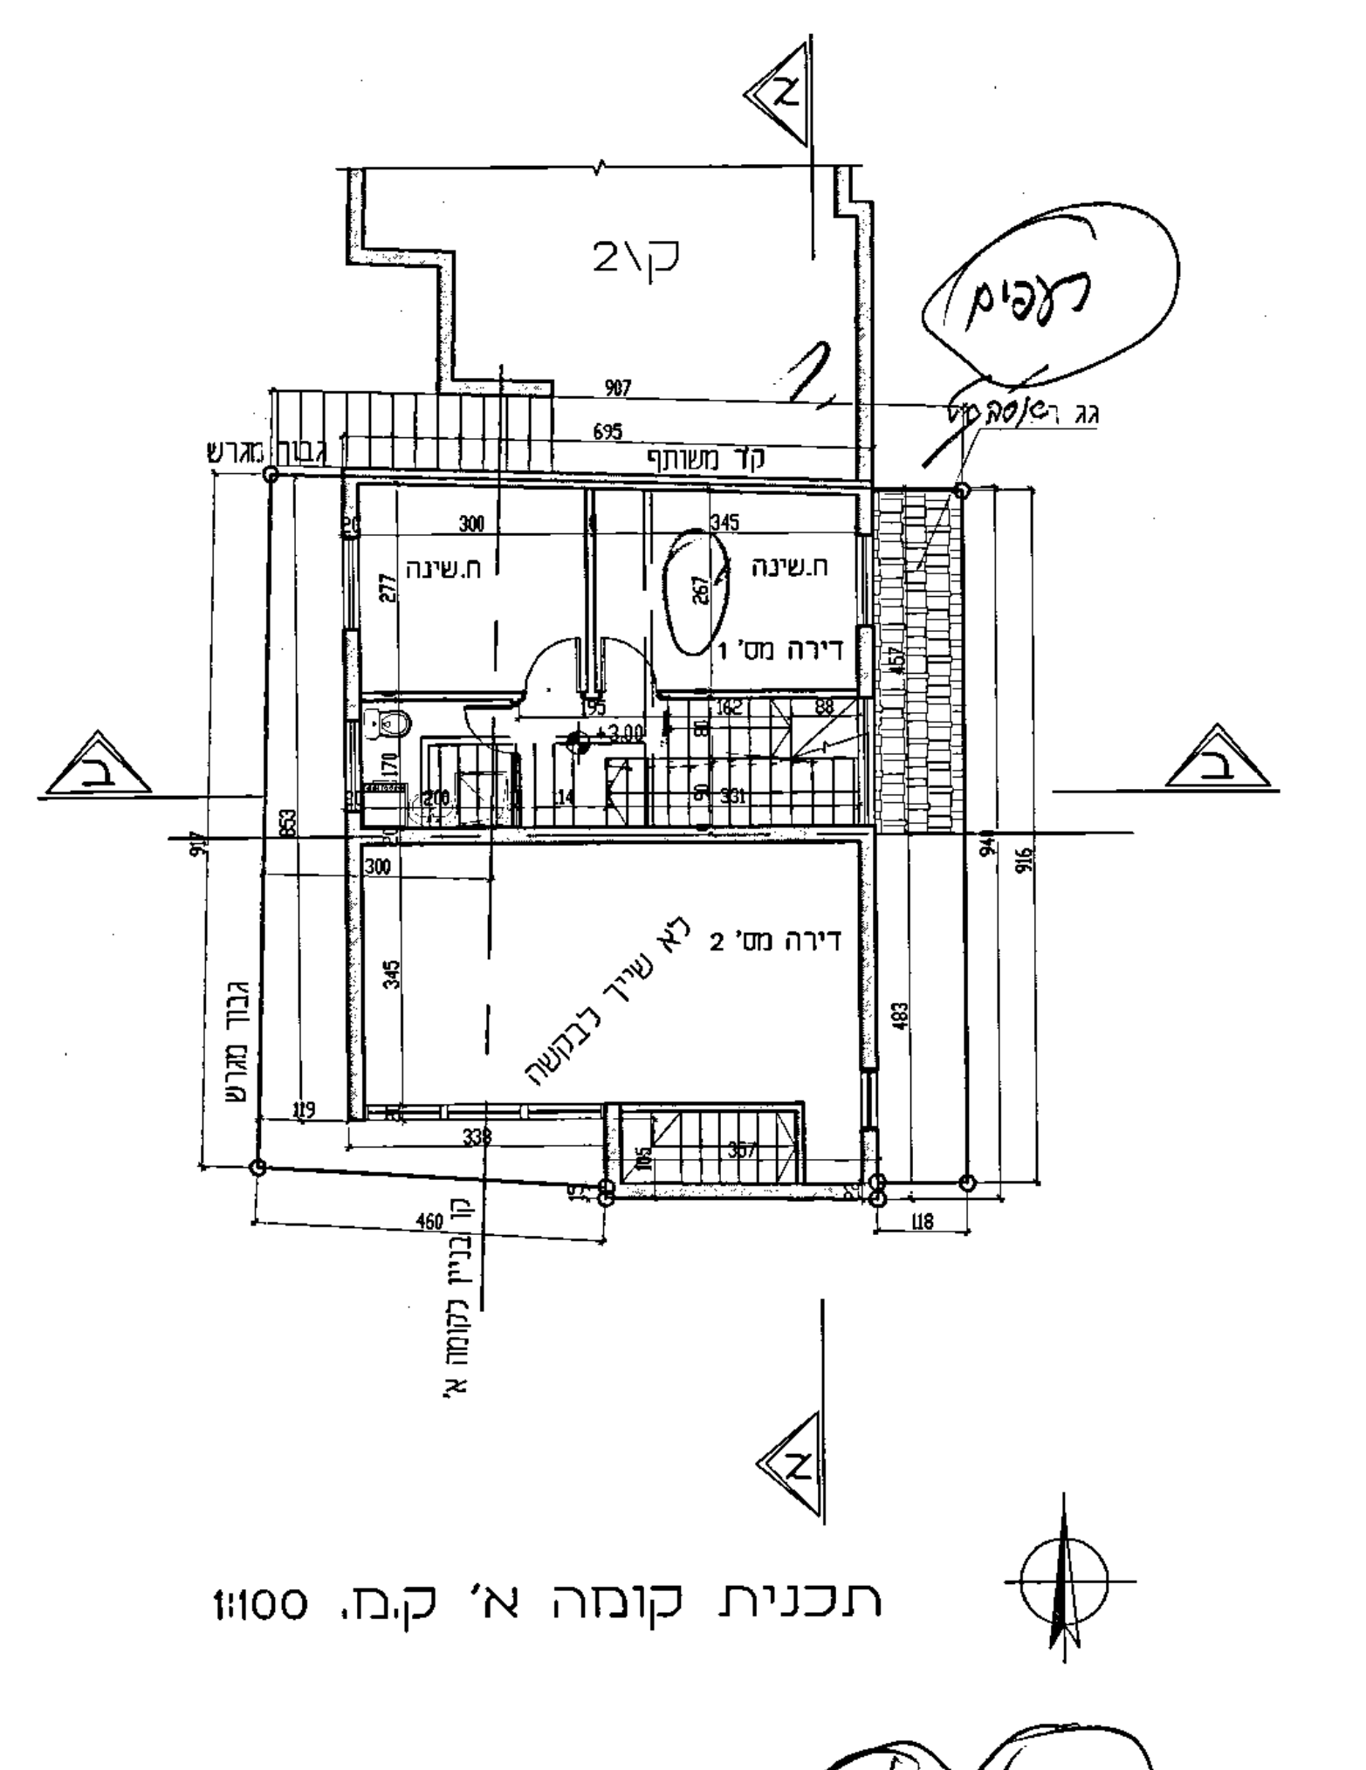

קוא
רעפים
גג אסבסט
קו משותף
גבול מגרש
ח.שינה
ח.שינה
דירה מס' 1
+3.00
דירה מס' 2
לא שייך לבקשה
קו בניין לקומה א'

תכנית קומה א' קנ.מ. 1:100

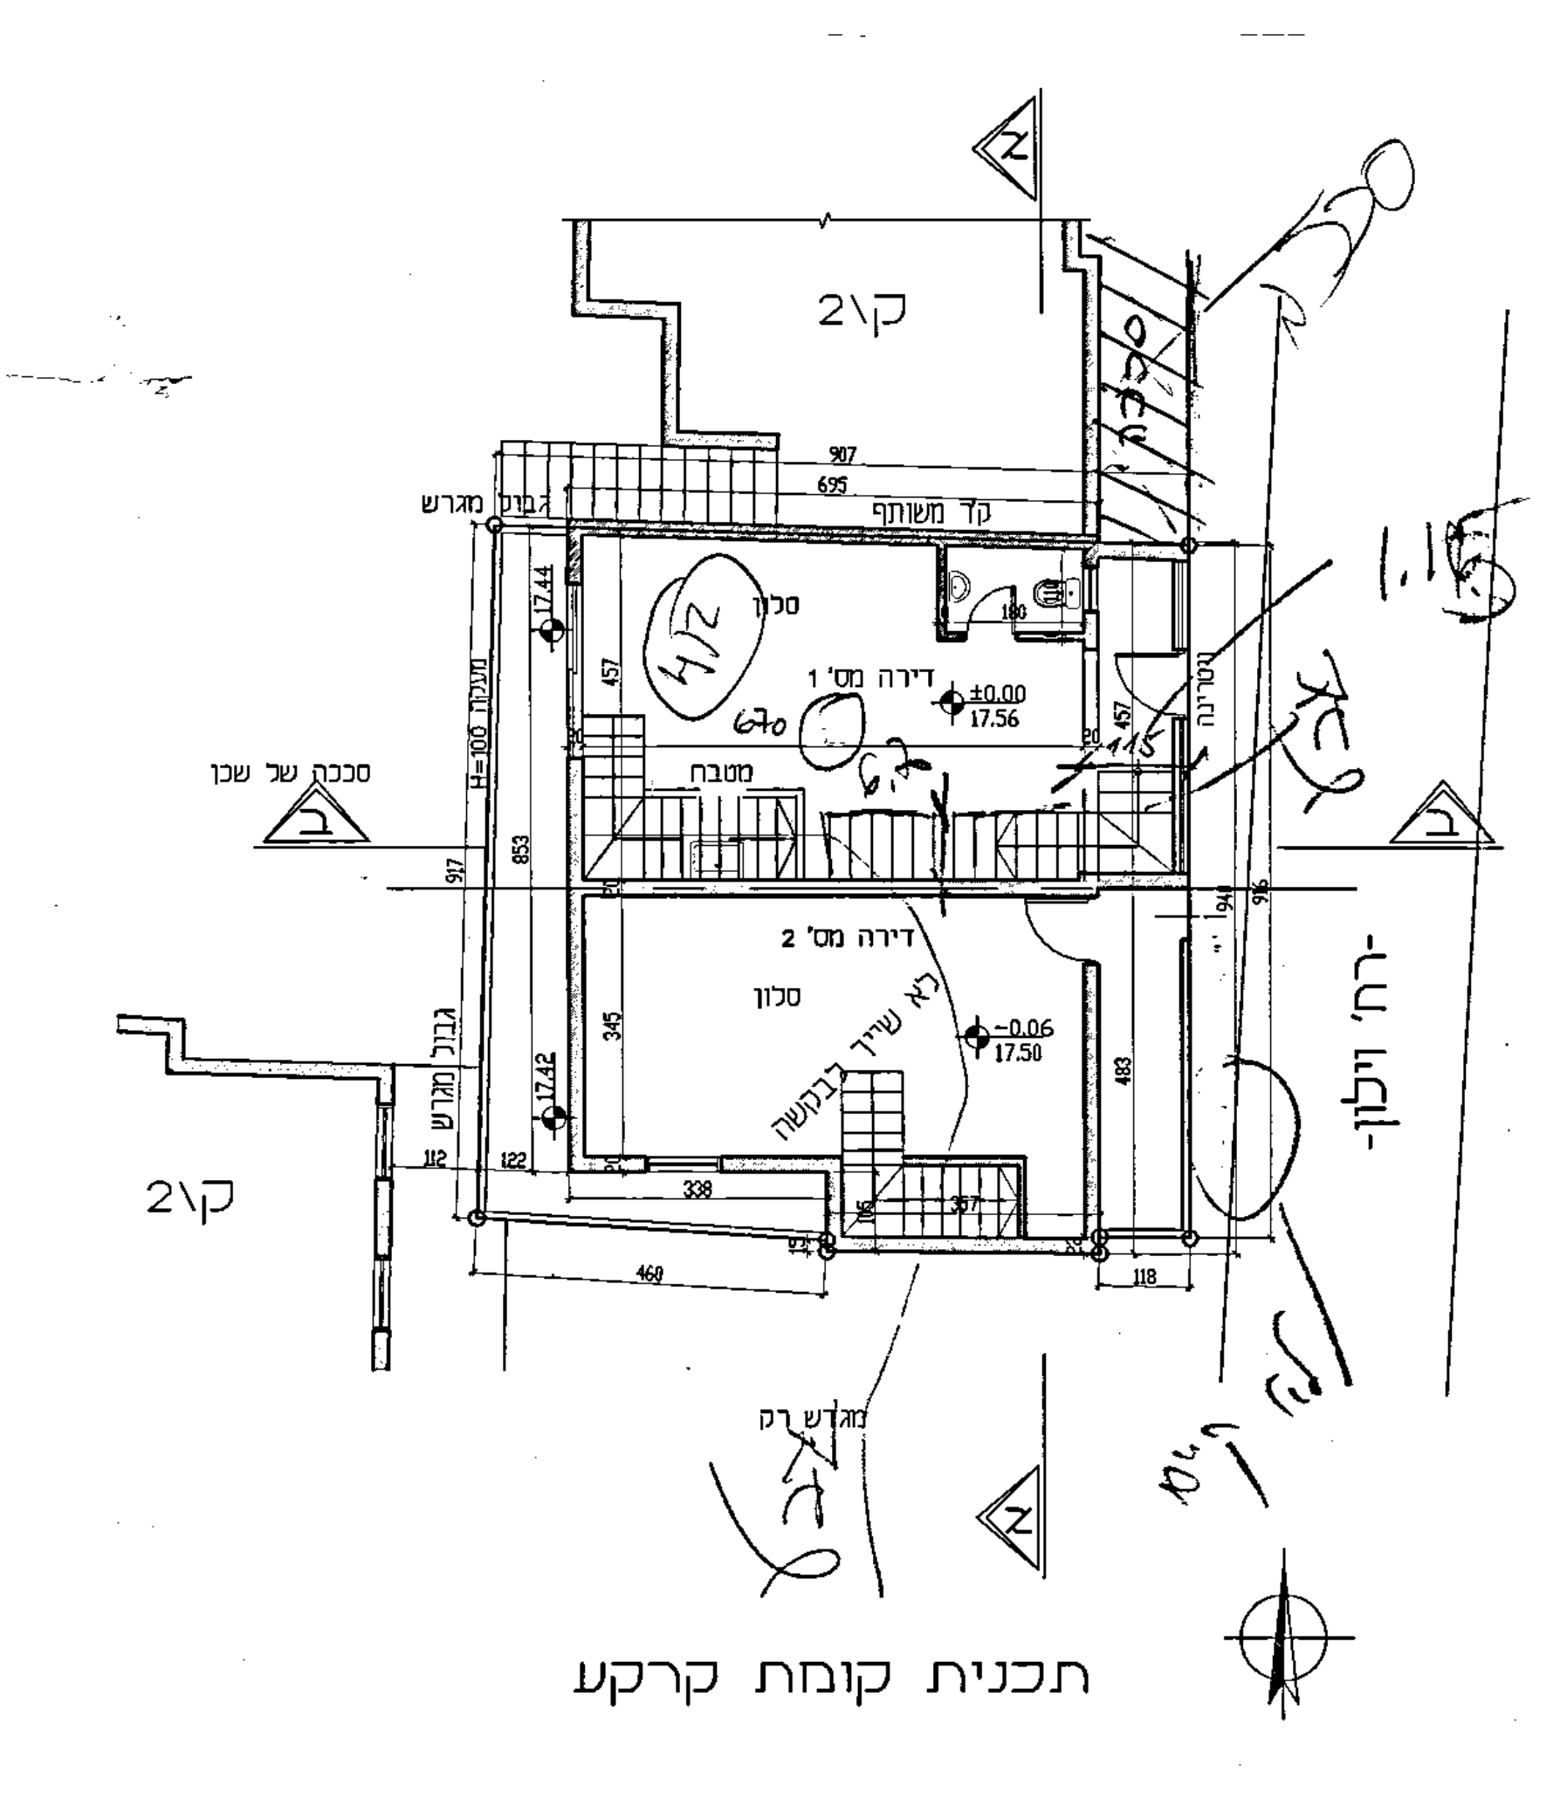

קוא
סככה
קו משותף
גבול מגרש
סכבת של שכן
סלון
דירה מס' 1
±0.00
17.56
מטבח
דירה מס' 2
סלון
-0.06
17.50
לא שייך לבקשה
רח' וילון

תכנית קומת קרקע

חישוב שטחים

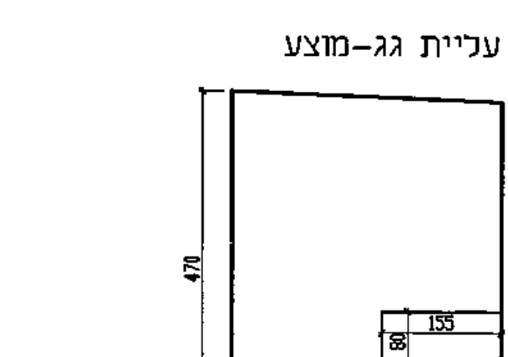

עליית גג-מוצע
חלל מדרגות

דירה מס' 1

שטח	מס'	חישובים	סה"כ מ"ר
ק.קרקע-קיים בהיתר	⊕	5.40 x 12.00	37.78
ק.א'-קיים בהיתר	⊕	1.45 x 0.70	32.39
עליית גג-מוצע	⊕	(4.70+4.57)/2x3.52- -(0.80x1.55+2.36x1.00)	12.00
סה"כ שטח הדירה			82.17

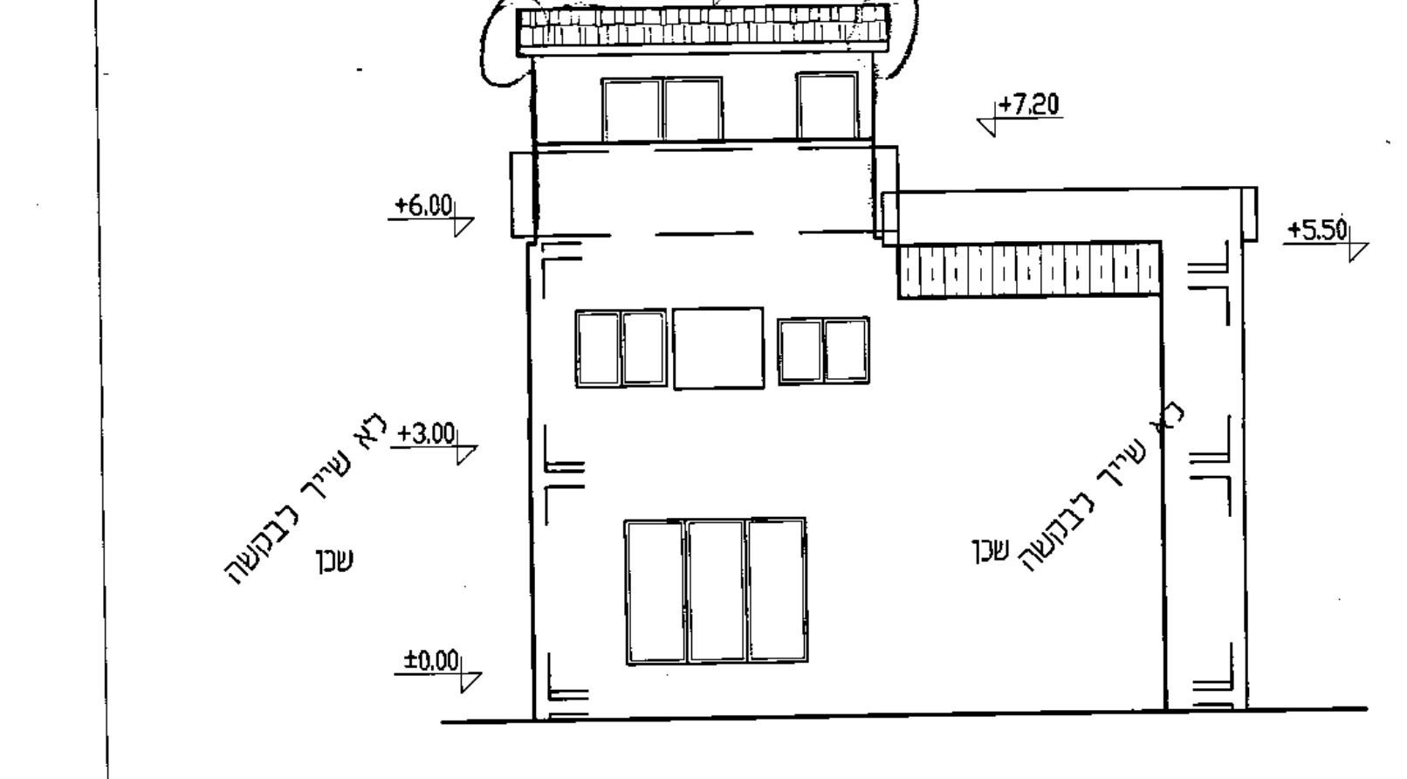

+9.00
+7.20
+6.00
+5.50
+3.00
±0.00
לא שייך לבקשה
שכן

חזית מערבית קנ.מ. 1:100

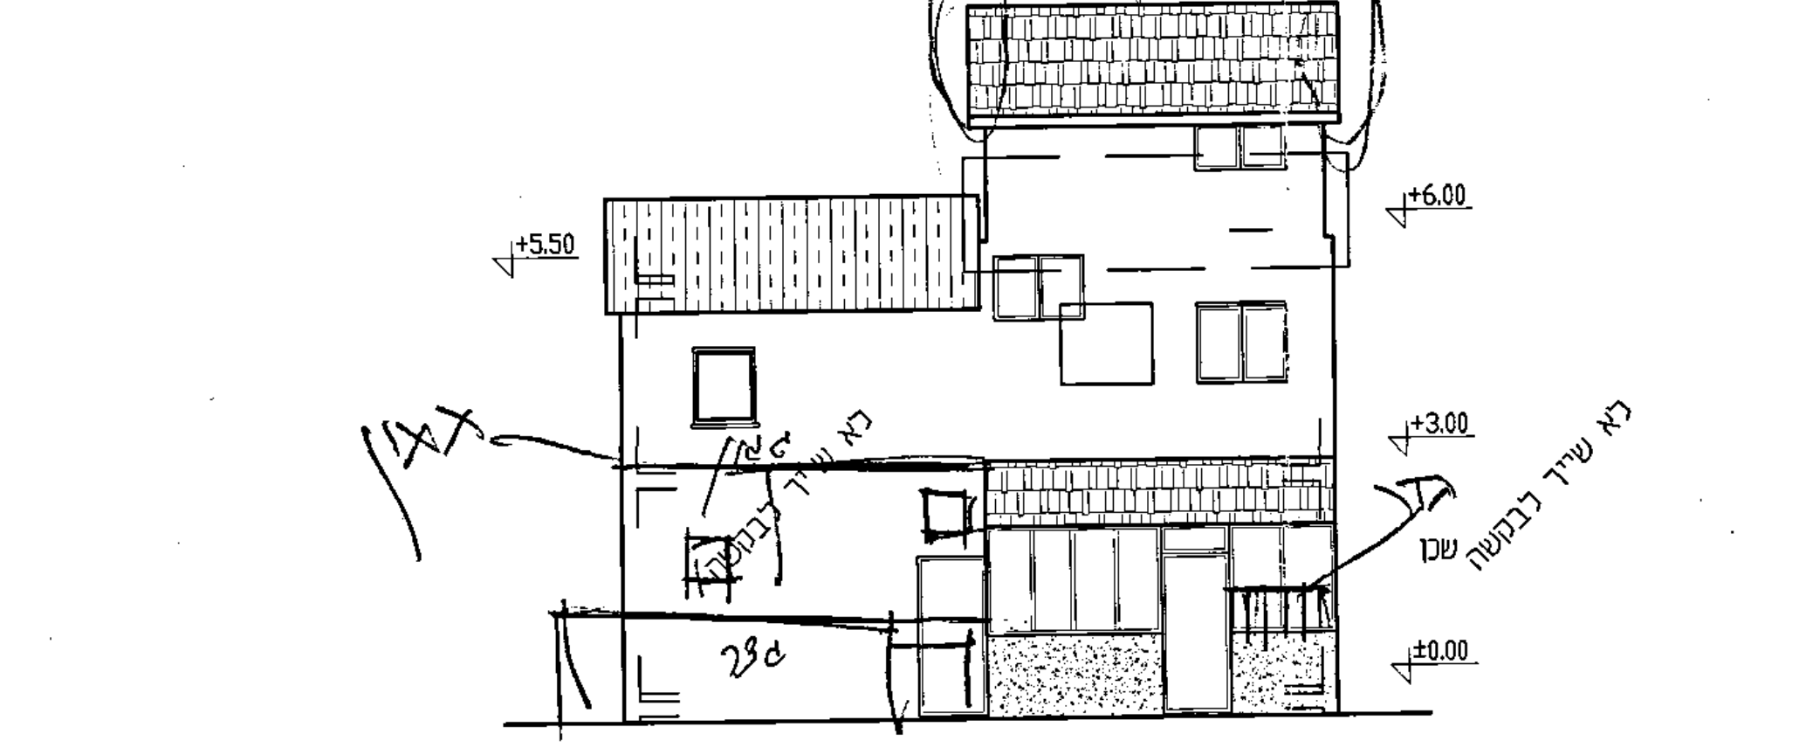

+9.00
+6.00
+5.50
+3.00
±0.00
לא שייך לבקשה
שכן

חזית מזרחית קנ.מ. 1:100

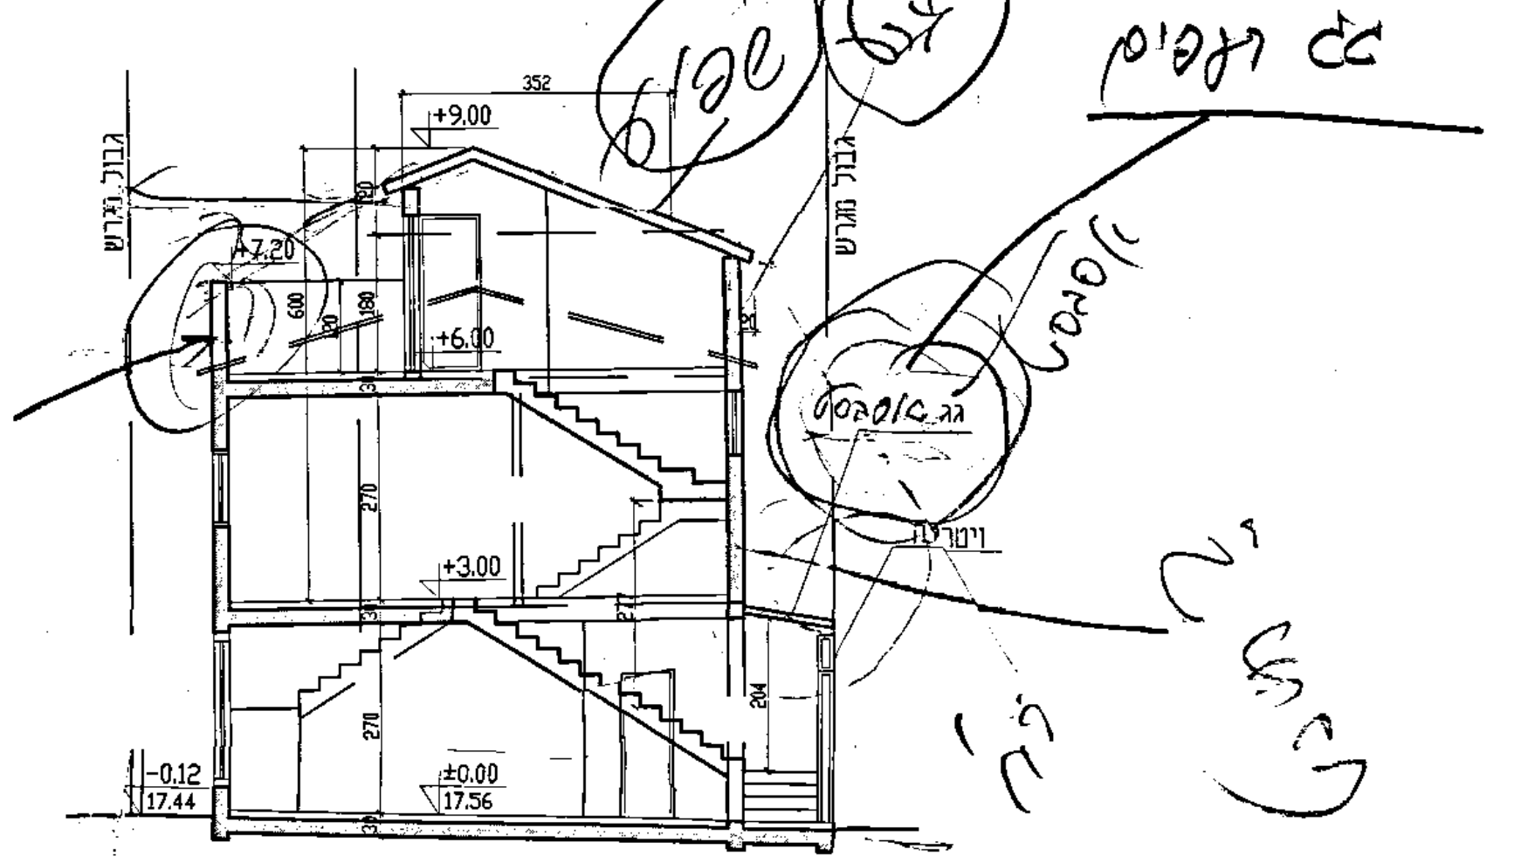

גג רעפים
שפוע
אסבסט
גג אסבסט
+9.00
+7.20
+6.00
+3.00
±0.00
17.56
-0.12
17.44
גבול מגרש

חתך ב-ב קנ.מ. 1:100

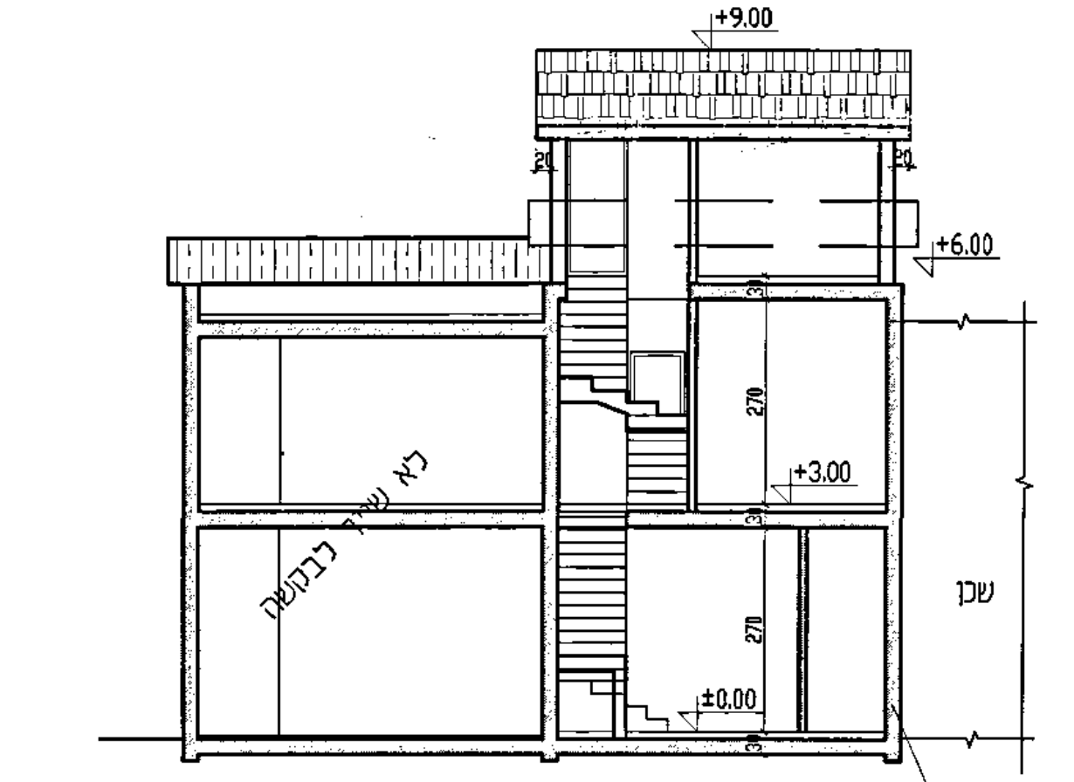

+9.00
+6.00
+3.00
±0.00
לא שייך לבקשה
שכן
קיר משותף

חתך א-א קנ.מ. 1:100

1-08-0926
22
בגשה

עיריית תל-אביב - יפו
מחלקת רישוי בנייה
27-05-2008
נתקבל

עיריית תל-אביב-יפו

מינהל ההנדסה, אגף רישוי ופיקוח על הבנייה
שדרות בן-גוריון 68 תל-אביב 64514 (פקס 5231340) טלפון 5217120, 5217045

לכבוד
☐ הוועדה המקומית לתכנון ולבנייה
☒ רשות הרישוי המקומית

חוק התכנון והבנייה, התשכ"ה-1965
תקנות התכנון והבנייה (בקשה להיתר תנאיו ואגרות) התש"ל-1970

בקשה להיתר בנייה או לשימוש במקרקעין

יש להקפיד למלא את כל הפרטים בטופס הבקשה ולצרף מסמכים כמפורט ברשימת התיוג המצורפת.

על פי טופס 1 תקנה 2(א)

מס' תיק הבניין	מס' בקשה קודמת להיתר בנייה	מס' הבקשה למידע	מתאריך
4063-017	2003-0292	N2007-2899	22/11/2007

א. פרטי הנכס והמבקשים

הכתובת	רחוב	מס' בית	גוש	חלקה	תת חלקה	מגרש	הוראות התכניות החלות על המקום
	וילון	17	6135	43			2215

פרטים אישיים	שם משפחה / שם פרטי	מס' זהות/חברה	רחוב ומספר בית, ישוב ומיקוד	מספר טלפון / פקס
מבקש 1	דבולנוב אנגליקה	309397933	וילון 17 ת"א	053985358
מבקש 2				
מבקש 3				
בעל הזכות בנכס	דבולנוב אנגליקה	309397933	וילון 17 ת"א	053985358
החוכר				
עורך הבקשה הראשי	ז'בגורסקי אלכס	14687859	רח' גרינבוים 14 תל אביב-יפו, 68109	0522544457 03 5182993
מתכנן שלד הבניין	ז'בגורסקי אלכס	14687859	רח' גרינבוים 14 תל אביב-יפו, 68109	0522544457 03 5182998

ב. מהות הבקשה

☐ בקשה לתוספת בנייה ☐ בקשה להרחבת דיור (במסגרת הרחבת דיור שכונתית)
☐ תוספת ____ קומות לבניין
הכוללות: ☐ ____ יחידות דיור
☒ תוספת בנייה בקומה גג ☒ לחזית ☒ לאחור ☐ לצד
בשטח של 12.00 מ"ר
שטח הדירה / המשרד לאחר התוספות יהיה 82.17 מ"ר
☐ שינויים פנימיים הכוללים:
☐ אישור מצב קיים
המקום משמש כיום ל- מגורים
☒ בהיתר ☐ בלי היתר

ג. מפרט - תיאור הבקשה

תיאור הקיים על המגרש: קיים בניין בן 2 קומות; 1 יח' דיור

שימוש עיקרי: ☒ מגורים ☐ מלונאות ☐ תעשייה ☐ חקלאי ☐ משרדים ☐ בידור ☐ בניין ציבורי ☐ מלאכה ☐ מסחר ☐ נופש וספורט ☐ שימוש אחר

סוג העבודה או השימושים המוצעים: ☒ תוספת לבניין ☐ הריסה ☐ שינוי בשימוש ☐ שינוי לבניין ☐ תיקונים ☐ ממטרה ____ למטרה ____

הגורם שמבצעת בעבורו הבנייה: ☐ משרד ממשלתי ☐ מוסד ציבורי ☐ בנה ביתך ☐ רשות מקומית ☒ גורם פרטי ☐ אחר

שטחים	שטח המגרש/החלקה	שטח הבנייה הכולל המבוקש	אחוזי הבנייה
	85.00 מ"ר	82.17 מ"ר	96.66

אם במסגרת הרחבת דיור שכונתית	מספר יחידות דיור מורחבות	מספר תכנית ההרחבה
	1	2215

ד. חומרי הבנייה

סוג הבנייה: ☒ רגילה ☐ בית מוכן ☐ מתועשת ☐ אחר
קירות חיצוניים: ☐ בטון מזוין ☒ בלוקים ☐ אבן טבעית ☐ לבנים שרופות ☐ אחר
חומרי גימור: ☐ אבן מלאכותית ☐ אבן טבעית ☒ טיח ☐ זכוכית ☐ אחר
תקרות: ☒ בטון מזוין ☐ עץ ☐ אחר
גג: ☐ בטון מזוין ☐ אסבסט ☒ רעפים ☐ טיח ☐ אחר
גדרות: ☐ אבן טבעית ☐ אבן מלאכותית ☐ בטון ☐ בלוקים ☐ ברזל ☐ עץ ☐ רשת ☐ אחר

ה. השטחים המבוקשים לבנייה

מפלס	שטחים עיקריים קיים בהיתר	מוצע	תכנית	מ"ר	%משטח המגרש	סך כל שטחי הבנייה מ"ר	%משטח המגרש
±0.00	37.78		2215	37.78	44.44	37.78	44.44
+3.00	32.39		2215	32.39	38.10	32.39	38.10
+6.00		12.00	ג	12.00	14.12	12.00	14.12
סה"כ מעל לקרקע	70.17	12.00		82.17	96.66	82.17	96.66
סה"כ מתחת לקרקע							
סה"כ	70.17	12.00		82.17	96.66	82.17	96.66

ו. פרטי הבנייה - לשימוש הלשכה המרכזית לסטטיסטיקה

ז. קווי בנייה

ח. מספר יחידות דיור

ט. הבקשה מוגשת לאישור

☐ הוועדה המקומית
☐ רשות הרישוי המקומית
☐ רשות הרישוי המקומית באמצעות מורשה להיתר

י. הצהרת עורך הבקשה הראשי

תאריך 04/2008 שם ז'בגורסקי א. חתימה

יא. חתימות נוספות

	תאריך	שם	חתימה
המבקש	04/2008	דבולנוב	
בעל הזכות בנכס	04/2008	דבולנוב	
בעל הנכס / החוכר			
מתכנן שלד הבניין	04/2008	ז'בגורסקי	

יב. מינויים מטעם מבקש ההיתר

אני ממנה בזה את ז'בגורסקי אלכס בעל/ת מס' זהות 14687859 לשמש כעורך הבקשה הראשי.

אני ממנה בזה את ז'בגורסקי אלכס בעל/ת מס' זהות 14687859 לשמש כמתכנן שלד הבניין.

שם משפחה ושם פרטי	תחום פעולה	המען	מספר טלפון	מספר פקס
	מתכנן האינסטלציה הסניטרית			

יג. הצהרות

תאריך	שם משפחה ושם פרטי	מספר רישיון
	ז'בגורסקי אלכס	15320

אני החתום מטה (שם משפחה ושם פרטי) ז'בגורסקי אלכס מס' זהות 14687859 מהנדס רשוי מס' 15320

ז'בגורסקי אלכס מהנדס בניין מס' 15320

עפ"י