1090 22

18 NOV 2008

24 SEP 2008

עיריית תל-אביב-יפו

מינהל ההנדסה, אגף רישוי ופיקוח על הבנייה
שדרות בן-גוריון 68 תל-אביב 64514 (פקס 5231340) טלפון 5217120, 5217045

חוק התכנון והבנייה, התשכ"ה-1965
תקנות התכנון והבנייה (בקשה להיתר תנאיו ואגרות) התש"ל-1970

בקשה להיתר בנייה או לשימוש במקרקעין

יש להקפיד למלא את כל הפרטים בטופס הבקשה ולצרף מסמכים כמפורט ברשימת התיוג המצורפת.

לכבוד ☐ הוועדה המקומית לתכנון ולבנייה
☐ רשות הרישוי המקומית

על פי טופס 1 תקנה 2(א)

מתאריך	מס' הבקשה למידע	מס' בקשה קודמת להיתר בנייה	מס' תיק הבניין
22/112007	N2007-2899	2003-0292	4063-017

08926

א. פרטי הנכס והמבקשים

הכתובת	רחוב	מס' בית	גוש	חלקה	תת חלקה	מגרש	הוראות התכניות החלות על המקום
	וילון	17	6135	43			2215 ג

פרטים אישיים	שם משפחה / שם פרטי או שם חברה או תאגיד	מס' זהות/חברה או מס' רישום תאגיד	רחוב ומספר בית / ישוב ומיקוד	מספר טלפון / מספר פקס
מבקש 1	זבולונוב אנגליקה	3009397933	רח' וילון 17, ת"א	053985358
מבקש 2				
מבקש 3				
בעל הזכות בנכס				053985358
החוכר				
עורך הבקשה הראשי	ז'בגורסקי אלכס	14687859	רח' גרינבוים 14 תל אביב-יפו, 68109	0522544457 03 9510030
מתכנן שלד הבניין	ז'בגורסקי אלכס	14687859	רח' גרינבוים 14 תל אביב-יפו, 68109	0522544457 03 9510030

ב. מהות הבקשה

☐ בקשה לתוספת בנייה ☐ בקשה להרחבת דיור (במסגרת הרחבת דיור שכונתית)

☐ תוספת ______ קומות לבניין

הכוללות: ☐ ______ יחידות דיור

☐ ______

☒ תוספת בנייה בקומה גג ☒ לחזית ☒ לאחור ☐ לצד

בשטח של 11.78 מ"ר

שטח הדירה / המשרד לאחר התוספות יהיה 81.95 מ"ר

☐ שינויים פנימיים הכוללים: ______

☐ אישור מצב קיים

☐ ______

המקום משמש כיום ל- מגורים

☒ בהיתר ☐ בלי היתר

ג. מפרט - תיאור הבקשה

תיאור הקיים על המגרש	פרט מספר מבנים, גובהם, מקומם, ייעודם וכד' קיים בניין בן 2 קומות 2 יח' דיור
שימוש עיקרי	☒ מגורים ☐ מלונאות ☐ תעשיה ☐ חקלאי ☐ משרדים ☐ בידור ☐ בנין ציבורי ☐ מלאכה ☐ מסחר ☐ נופש וספורט ☐ שימוש אחר
סוג העבודה או השימושים המוצעים	☒ תוספת לבניין ☐ הריסה ☐ שינוי בשימוש ☐ שינוי לבניין ☐ תיקונים ממטרה ______ למטרה ______
הגורם שמבוצעת בעבורו הבנייה	☐ משרד ממשלתי ☐ מוסד ציבורי ☐ בנה ביתך ☐ רשות מקומית ☒ גורם פרטי ☐ אחר: ______
שטחים	שטח המגרש/החלקה 85.00 מ"ר; שטח הבנייה הכולל המבוקש 81.95 מ"ר; אחוזי הבנייה 96.66
אם במסגרת הרחבת דיור שכונתית	מספר יחידות דיור מורחבות 1; מספר תכנית ההרחבה 2215 ג

ד. חומרי הבנייה

סוג הבנייה	☒ רגילה ☐ בית מוכן ☐ מתועשת ☐ אחר
קירות חיצוניים	☐ בטון מזוין ☐ לבנים שרופות ☒ בלוקים ☐ אחר ☐ אבן טבעית
חומרי גימור	☐ אבן מלאכותית ☐ זכוכית ☐ אבן טבעית ☐ אחר ☒ טיח
תקרות	☒ בטון מזוין ☐ עץ ☐ אחר
גג	☐ בטון מזוין ☐ אסבסט ☐ אחר ☒ רעפים ☐ פח
גדרות	☐ אבן טבעית ☐ בלוקים ☐ רשת ☐ אבן מלאכותית ☐ ברזל ☐ אחר ☐ בטון ☐ עץ קיימות ____ מ"א מוצעות ____ מ"א סה"כ ____ מ"א
מקרא חומרים (צבעים)	בטון או בטון מזוין — בלוקים או לבנים מבטון — סיליקט או לבנים אדומות — אבן — עץ — איטונג — זכוכית — הריסה — אחר

ה. השטחים המבוקשים לבנייה (על-פי תכנית הבנייה) והמותרים לבנייה (על-פי "אסמכתא": חוק, תקנות, תכנית) בכל מפלס בנפרד ולפי שימוש

הקומה/המפלס בבניין	(א) מגורים: קיים בהיתר	קיים ללא היתר ומבוקש לאשר בייעוד	בנייה חדשה מוצעת	מותר	(2) קיים בהיתר	קיים ללא היתר ומבוקש לאשר בייעוד	בנייה חדשה מוצעת	מותר	סך כל שטחי הבנייה העיקריים (קיים ומוצע) לשימושים השונים: מ"ר	%משטח המגרש	סך כל השטחים המותרים	ה"אסמכתא" לשטחים המותרים לשימושים העיקריים ולשטחי השרות
±0.00	37.78			51.00/2					37.78	44.44	119.00/2	2215
+3.00	32.39			68.00/2					32.39	38.10		2215
+6.00			11.78	12.00					11.78	14.12	12.00	ג
סה"כ מעל לקרקע	70.17		11.78						81.95	96.66		
סה"כ מתחת לקרקע												
סה"כ	70.17		11.78						81.95	96.66		

(ב) שטחי השירות: מקלט, מתקנים חדרים ומערכות טכניות, החסנה, חניה, מבואות וחדרי מדרגות, קומת עמודים מפולשת, מעברים לכלל הציבור, בליטות, אחר, בנייה קיימת; סך כל שטחי השירות: מ"ר קיים / מוצע, %משטח המגרש, סך כל השטחים המותרים

(ג) סך כל שטחי הבניין: מ"ר, %משטח המגרש, סך כל השטחים המותרים; משטחים לא מקורים

(ג) מ"ר	%משטח המגרש	סך כל השטחים המותרים
37.78	44.44	119.00/2
32.39	38.10	
11.78	14.12	12.00
81.95	96.66	
81.95	96.66	

פרק

ו. פרטי הבנייה - לשימוש הלשכה המרכזית לסטטיסטיקה

הייעוד	פירוט הייעוד (כגון דירות למגורים, בתי מלון וכו')	השטח על פי ההיתר	מספר חדרים	מספר דירות	מספר מגורים
למגורים			1		
להארחה			2		
לעסקים ולמסרדים			3		
לבנייני ציבור			4		
לתעשייה ולמלאכה			5		
למשק חקלאי			6		
למקלט או למרתף					
למבני עזר					
סך כל שטח הבנייה					

מספר היתר הבנייה; תאריך היתר הבנייה: שנה חודש; תאריך התחלת הבנייה: שנה חודש; תאריך גמר הבנייה: שנה חודש; מספר הקומות כולל קומת עמודים מפולשת

ז. קווי בנייה

הכיוון	מוצע	מותר	הסטייה במטר	ב- %
לרחוב (שם)				
לרחוב (שם)				
לצד				
לאחור				

ח. מספר יחידות דיור

אם השימוש המבוקש הוא מגורים – רשום להלן:
מספר הדירות קיימות ______ מספר הדירות המבוקשות ______ מספר הדירות המותרות ______

ט. הבקשה מוגשת לאישור

☐ הוועדה המקומית
הבקשה כוללת בקשה להקלה – כלהלן:

פירוט הבקשה להקלה	נימוקי הבקשה להקלה
.1	
.2	
.3	

☐ רשות הרישוי המקומית
☐ רשות הרישוי המקומית באמצעות מורשה להיתר

י. הצהרת עורך הבקשה הראשי

☐ אני מצהיר על נכונות הפרטים בסעיפים א עד ט.
תאריך 04/2008 שם ז'בגורסקי א. חתימה

יא. חתימות נוספות

	תאריך	שם	חתימה
המבקש	04/2008	זבולונוב	זבולונוב
בעל הזכות בנכס/ בעל הנכס/ החוכר	04/2008	זבולונוב	
מתכנן שלד הבניין	04/2008	ז'בגורסקי	

ז'בגורסקי אלכס מהנדס בניין מס' 15320

לשימוש המשרד	התוכנית תואמת את המצב בשטח	הוכן דוח	מס' הדוח/ התביעה	הנדון בדוח / הנדון בתביעה	הערות
הערות הפיקוח	☐ כן ☐ לא	☐ הוכן דוח לתביעה משפטית ☐ הוגשה תביעה משפטית ☐ הוגשה תביעה חוזרת	תאריך הדוח/ התביעה		תאריך / שם / חתימה

מפקדת מחוז דן
המלצת רשות מוסמכת
* כאשר יהיה פטור מבנית... תוספת ... לתוספת ... מטר ליחידת דיור.
* כל תוספת בנייה בעתיד תחויב בבניית מרחב מוגן לפי החוק.
מוסמכת

המלצת רשות מוסמכת
המבקש חייב בבניית מרחב מוגן/שיפוץ מקלט קיים עבור תוספת בניית בשטח 15.5 מ"ר

ניתן פטור מהחובה לבניית מקלט
16/11/08 (1090)

חייב בבנית מ"מ 930 6/11/08

אברם אוריל - בחייב מהנדס הג"א ורשות מוסמכת

סגן מפקד המחוז אלים צביקה סלר 3737

ראובן... מהנדס הג"א רשות מוסמכת

יב. מינויים מטעם מבקש ההיתר - נתמנה אדם אחד ליותר מתפקיד אחד, ימולא פרטיו ליד כל אחד מהתפקידים שהוא ממלא על פי הוראות כל דין.

מינוי עורך הבקשה הראשי: אני ממנה בזה את ז'בגורסקי אלכס בעל/ת מס' זהות 14687859 הרשום בסעיף א' להיות עורך הבקשה הראשי להיתר, ולייצגני לפני מוסדות התכנון והרשויות המוסמכות בכל הנוגע לטיפול בבקשה להיתר ולקבלתו, לרבות התיקונים ככל שידרשו הרשויות המוסמכות.

מינוי עורכי בקשה לפי תחומים: אני ממנה בזה את הרשומים להלן להיות עורכי הבקשה להיתר בתחום הפעולה הרשום ליד שמם, ולייצגני בתחום פעולתם לפני מוסדות התכנון והרשויות המוסמכות בכל הנוגע לטיפול בבקשה להיתר ולקבלתו, לרבות התיקונים ככל שידרשו הרשויות המוסמכות.

שם משפחה ושם פרטי	תחום פעולה	המען	מספר טלפון	מספר פקס
.1	מתכנן האינסטלציה הסניטרית			
.2				

מינוי מתכנן שלד הבניין: אני ממנה בזה את ז'בגורסקי אלכס בעל/ת מס' זהות 14687859 הרשום בסע' א' להיות אחראי לתיכנון שלד הבנין שבעבורו מבוקש ההיתר, להגיש לוועדה המקומית לרשות הרישוי המקומית את החישובים לגבי הבניה שבעבורה מבוקש היתר ולפקח פיקוח עליון על הקמת השלד.

מינוי הקבלן האחראי לבניית: ☐ אני ממנה בזה את ______ בעל/ת מס' זהות ______ ובעל תעודת רישום בפנקס הקבלנים מספר ______ במדור ______ ובעל ______ לביצוע עבודה בתוקף עד ______ לבצע את העבודה הנדונה בהיתר כמתחייב לפי כל דין.
☐ אני מצהיר, כי טרם מסרתי את ביצוע העבודה הנדונה בהיתר לידי קבלן, ומתחייב כי אמסור אותה לידי קבלן רשום בפנקס הקבלנים, כמתחייב על פי כל דין, והודיע על כך לרשות הרישוי המקומית טרם תחילת ביצוע העבודה, וחתימתו של הקבלן תצורף להודעה המפרטת את פרטי רישומו של הקבלן.

מינוי האחראי לביצוע שלד הבניין: ☐ אני ממנה בזה את ______ בעל/ת מס' זהות ______ כתובת ______ טלפון ______ פקס ______ הרשום לעיל להיות אחראי לביצוע שלד.
☐ אני מצהיר, כי טרם מיניתי אחראי/ת לביצוע עבודות בתחומים האלה: ______ ומתחייב לעשות זאת כמפורט בתקנות, ולהודיע על כך לרשות הרישוי המקומית טרם התחלת ביצוע העבודה.

מינוי אחראים לביקורת: ☐ אני ממנה בזה את הרשומים להלן להיות אחראים לביקורת על ביצוע עבודות בתחום הפעולה הרשום ליד שמם.

שם משפחה ושם פרטי	תחום פעולה	המען	מספר טלפון	מספר פקס
.1	אחראי ראשי			
.2				
.3				

☐ אני מצהיר כי טרם מיניתי אחראי/ם לביקורת על ביצוע עבודות ______ את כולם או את קצתם בתחומים האלה: ______ ומתחייב לעשות זאת כמפורט בתקנות, ולהודיע על כך לרשות הרישוי המקומית טרם התחלת ביצוע העבודה.

X ______ חתימת המבקש על המינויים X ______

יג. הצהרות

הצהרת עורכי הבקשה / כולל הצהרת עורך הבקשה על לחץ המים:
אנו החתומים מטה מצהירים בזה:
1) כל אחד מאתנו מאשר שהאמור בנוגע לרשומה שבסעיף "לעיל הוא נכון.
2) כל אחד מאתנו מסכים לקבל עליו את התפקיד המיועד לו בסעיף "לעיל.
3) אנו מצהירים, כל אחד בנוגע לתחום פעולתו, שיש לנו כישורים מקצועיים לערוך בקשה זו וכי בדקנו את המסמכים הנוגעים לבקשה, לרבות כל תכנית הנוגעת לבקשה, וידוע לנו כי אם הצהרה זו אינה נכונה, הרי היא תיחשב מסירת ידיעה שהיא כוזבת או מטעה בפרט חשוב, כמשמעותה בסעיף 214 לחוק, וצפויים לנו העונשים הקבועים לפי כל דין.
אני ז'בגורסקי אלכס (עורך בקשה ראשי) אחראי/ת לכך שהבקשה, ובכלל זה נספחיה, נערכה לפי מיטב הידיעה המקצועית ובהתאם לכל חיקוק החל על העבודה המוצעת, שכל הנתונים שנמסרו על ידי בבקשה זו נכונים ושהתכנון המוצע תואם את כל התכניות, פרט לסטיות שפורטו לעיל.
☐ אני עורך הבקשה מתכנן האינסטלציה הסניטרית, מצהיר בזאת שתכניות הבקשה בכל הנוגע לסידורים הסניטריים נערכו כדין וכי קיים בהן הוראות החוק וההוראות למתקני תברואה התש"ל 1970 (הל"ת) לענין זה, לרבות בדיקה לחץ המים הקיים בבניין ותכנון בהתאם.

	תאריך	שם משפחה ושם פרטי	מספר רישיון	חתימה
עורך בקשה ראשי		ז'בגורסקי אלכס	15320	
עורך בקשה 1 מתכ' האינס הסני'				
עורך בקשה 2				

הצהרת מתכנן שלד הבניין:
אני החתום מטה (שם משפחה ושם פרטי) ז'בגורסקי אלכס מס' זהות 14687859 מהנדס רשוי מס' 15320 /הנדסאי בעל רישיון מס' ______ ("מבנה פשוט") מצהיר בזאת כדלקמן:
1) אני מסכים להיות מתכנן שלד הבניין בבקשה ולפקח פיקוח עליון על הקמת השלד.
2) אני מתחייב להגיש לפני מתן ההיתר, נושא הבקשה את החישובים הסטטיים בדבר בעבודה ההיתר.
3) ידוע לי, שאם אחרי הגשת הנתונים הסטטיים יתגלה צורך בשינוי מהותי בהם, אני מתחייב להגיש חישובים סטטיים מתוקנים מיד עם גילוי הצורך בכך.
4) אני מצהיר, כי יש לי כישורים מקצועיים לערוך בקשה זו וכי בדקתי את כל המסמכים הנוגעים לבקשה, לרבות כל תכנית הנוגעת לבקשה, וידוע לי כי אם הצהרה זו אינה נכונה, הרי היא תיחשב מסירת ידיעה שהיא כוזבת או מטעה בפרט חשוב, כמשמעותה בסעיף 214 לחוק, וצפויים לי העונשים הקבועים לפי כל דין.
5) ידוע לי כי עלי לשמור את תכניות הקונסטרוקציה לתקופה של לא פחות מ-10 שנים לאחר גמר הבנייה.
תאריך ______ חתימה ______ X

הצהרת האחראי לביצוע שלד הבניין (כאשר מונה):
אני החתום מטה (שם משפחה ושם פרטי) ______ מס' זהות ______ מהנדס רשוי מס' ______ /הנדסאי בעל רישיון מס' ______ ("מבנה פשוט") מצהיר בזאת כדלקמן:
1) אני מסכים להיות האחראי לביצוע שלד הבניין
2) אני מצהיר, כי יש לי כישורים מקצועיים להיות אחראי לביצוע שלד, ואני מתחייב לדאוג לביצוע שלד על פי תוכניות והוראות של מתכנן השלד כפי בכתב וכן למלא את תפקידי על פי שנקבע בכל חיקוק הנוגע לכך.
תאריך ______ חתימה ______

הצהרת אחראים לביקורת (כאשר מונו):
אנו החתומים מטה מצהירים בזה:
1) כל אחד מאיתנו מאשר שהאמור בנוגע לו ברשימה שבסעיף י"ב לעיל הוא נכון.
2) כל אחד מאיתנו מסכים לקבל עליו את התפקיד המיועד לו בסעיף י"ב.
3) אנו מצהירים כל אחד בנוגע לתחום פעולתו, שיש לנו כישורים מקצועיים לערוך את הביקורת כהלכה ולדווח על תוצאותיה לרשות הרישוי המקומית כמתחייב על פי כל דין.
אני ______ (עורך הביקורת הראשי) אחראי/ת לכך שהביקורת תיערך על פי מיטב הידיעה המקצועית, ושכל הדיווחים לרשות הרישוי המקומית ייערכו על פי כל דין.

תאריך	שם משפחה ושם פרטי	מספר רישיון	חתימה

תל-אביב
גוש : 6135
חלקה : 43(חלק)
שטח לפי נסח טאבו : 0.085 ד'
שטח מדוד : 0.085 ד'
הוכן עבור : משפי זבולונוב
מהות הבקשה : היתר בניה

מפה טופוגרפית
1 : 250

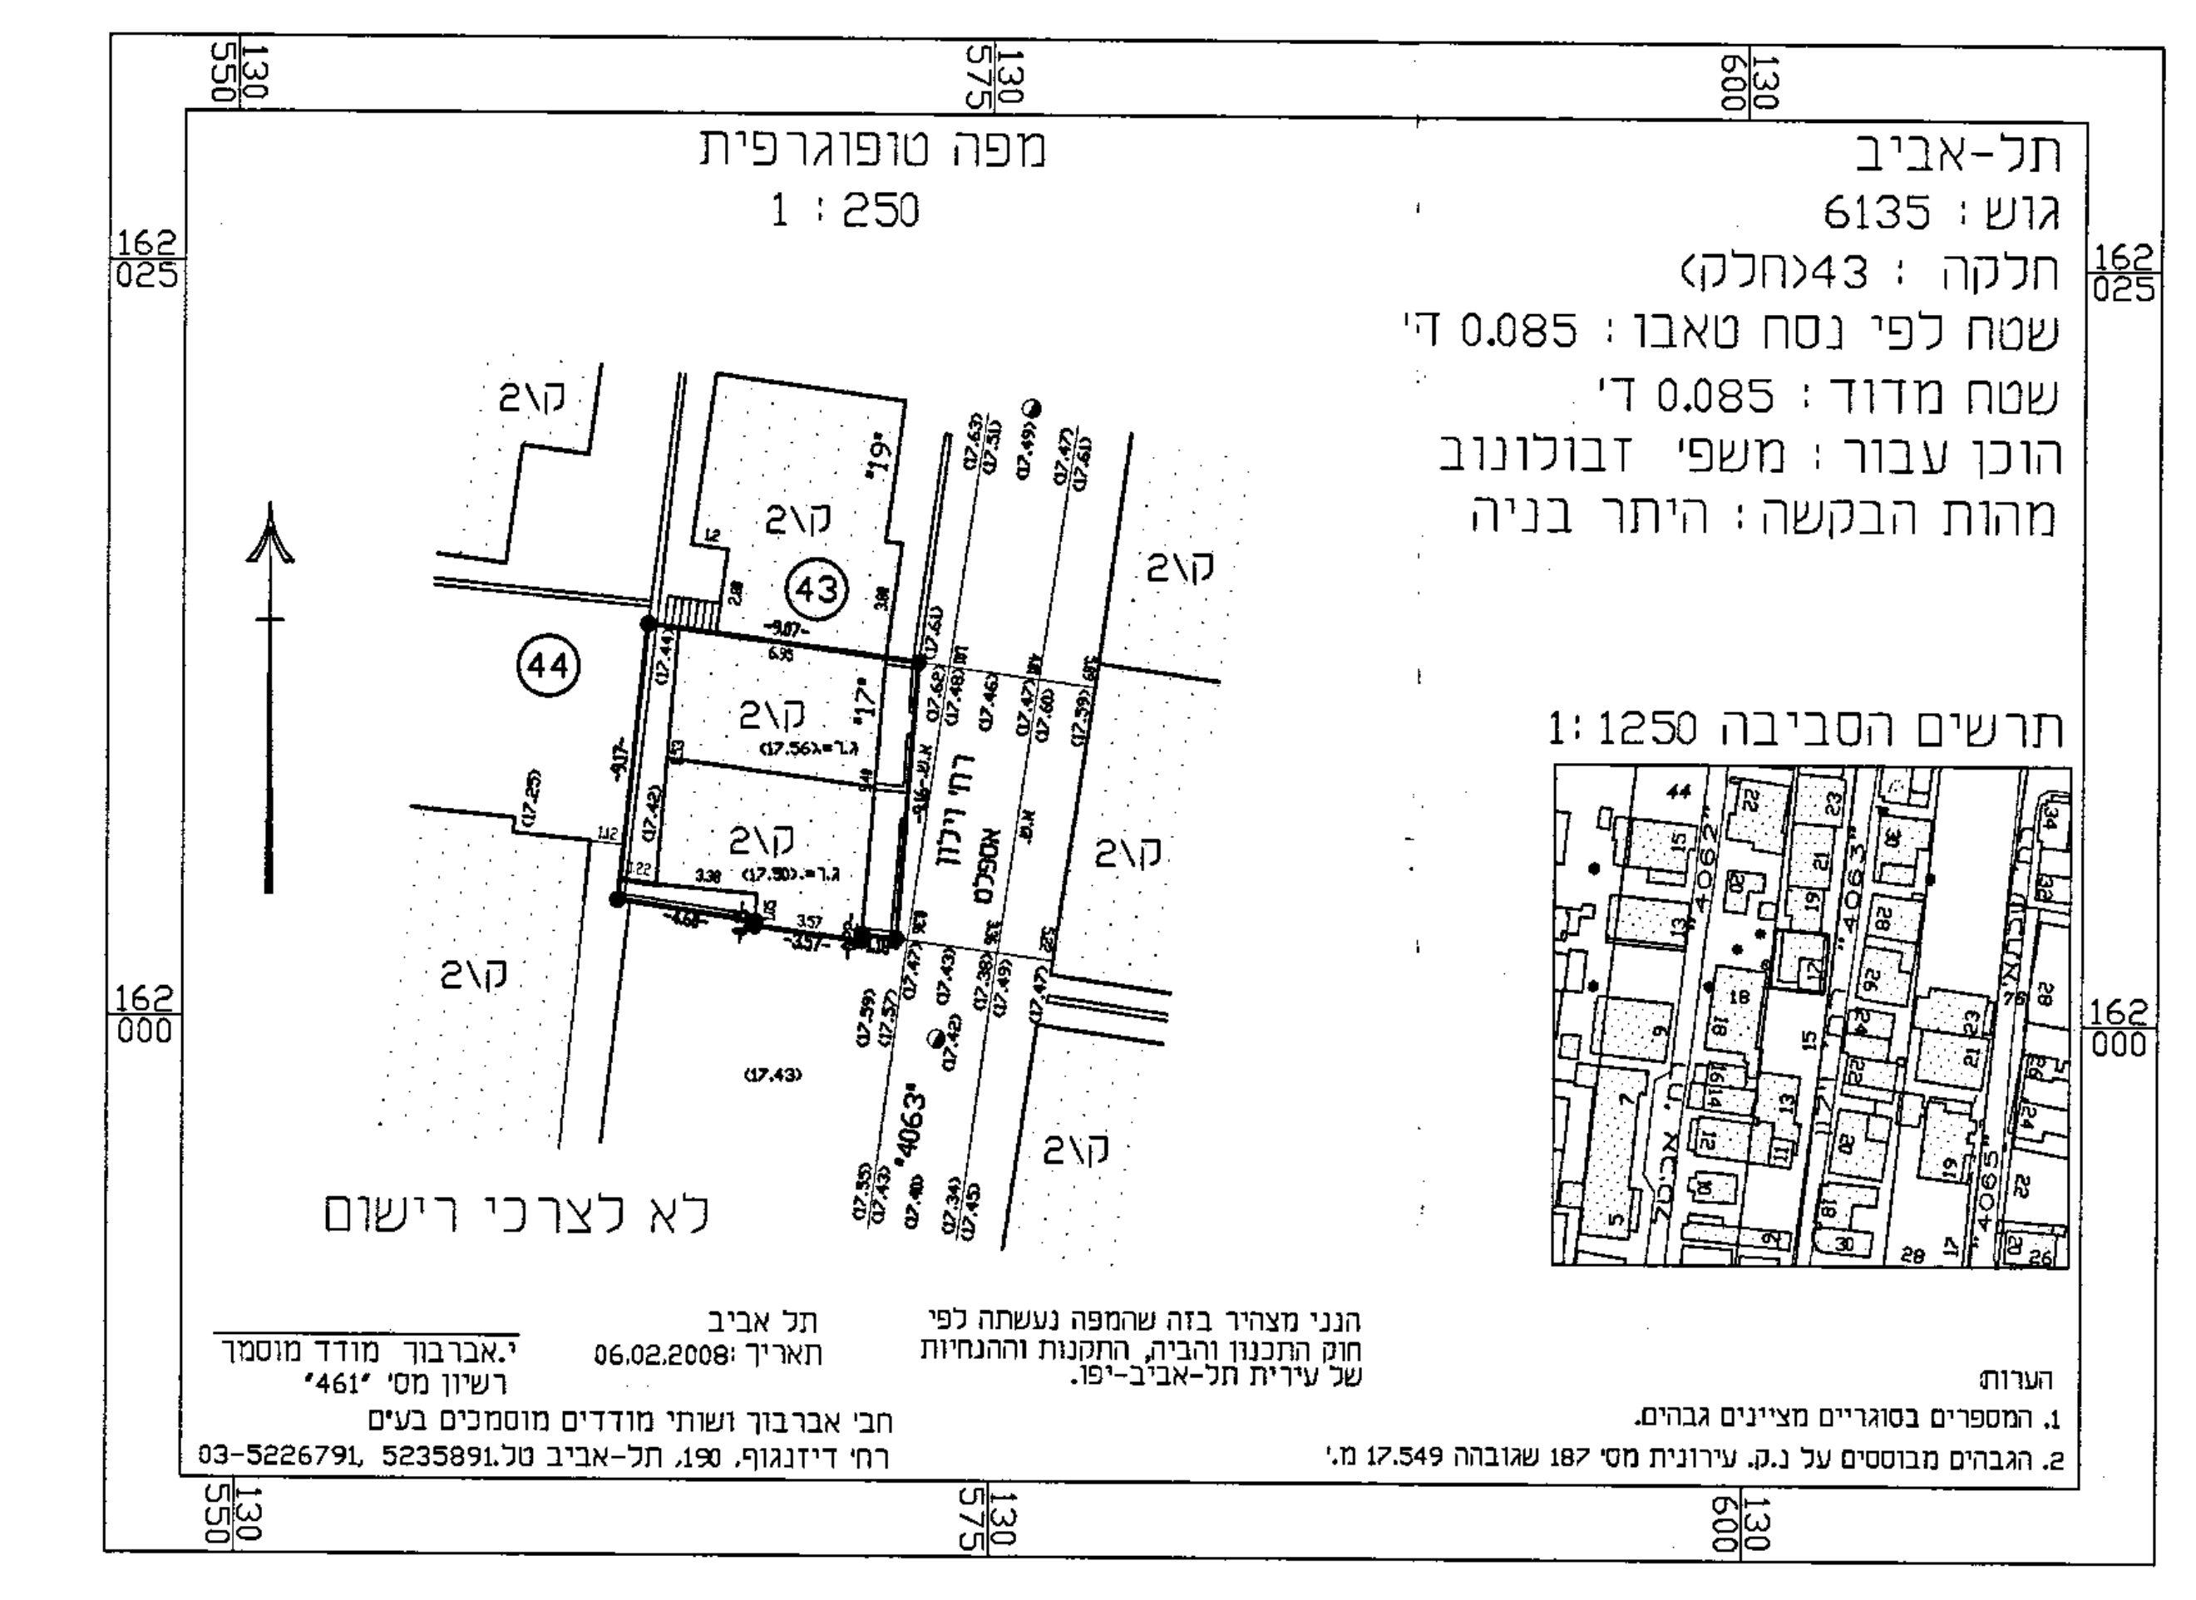

תרשים הסביבה 1:1250

לא לצרכי רישום

הנני מצהיר בזה שהמפה נעשתה לפי חוק התכנון והבניה, התקנות וההנחיות של עיריית תל-אביב-יפו.

תל אביב
תאריך: 06.02.2008

י.אברבוך מודד מוסמך
רשיון מס' "461"

חב' אברבוך ושותי מודדים מוסמכים בעיים
רחי דיזנגוף 190, תל-אביב טל.5235891, 03-5226791

הערות:
1. המספרים בסוגריים מציינים גבהים.
2. הגבהים מבוססים על נ.ג. עירונית מס' 187 שגובהה 17.549 מ'.

חישוב שטחים

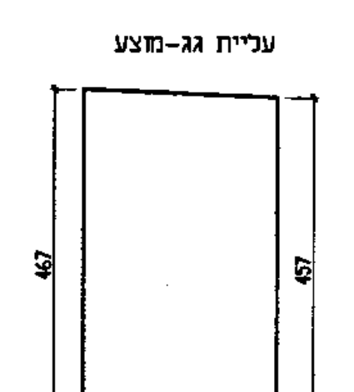

דירה מס' 1

שטח	מס'	חישובים	סה"כ מ"ר
ק.קרקע-קיים בהיתר	⊕	5.40 × 12.00	37.78
ק.א'-קיים בהיתר	⊕	1.45 × 0.70	32.39
עליית גג-מוצע	⊕	(4.70+4.57)/2×3.30	11.78
סה"כ שטח הדירה			81.95

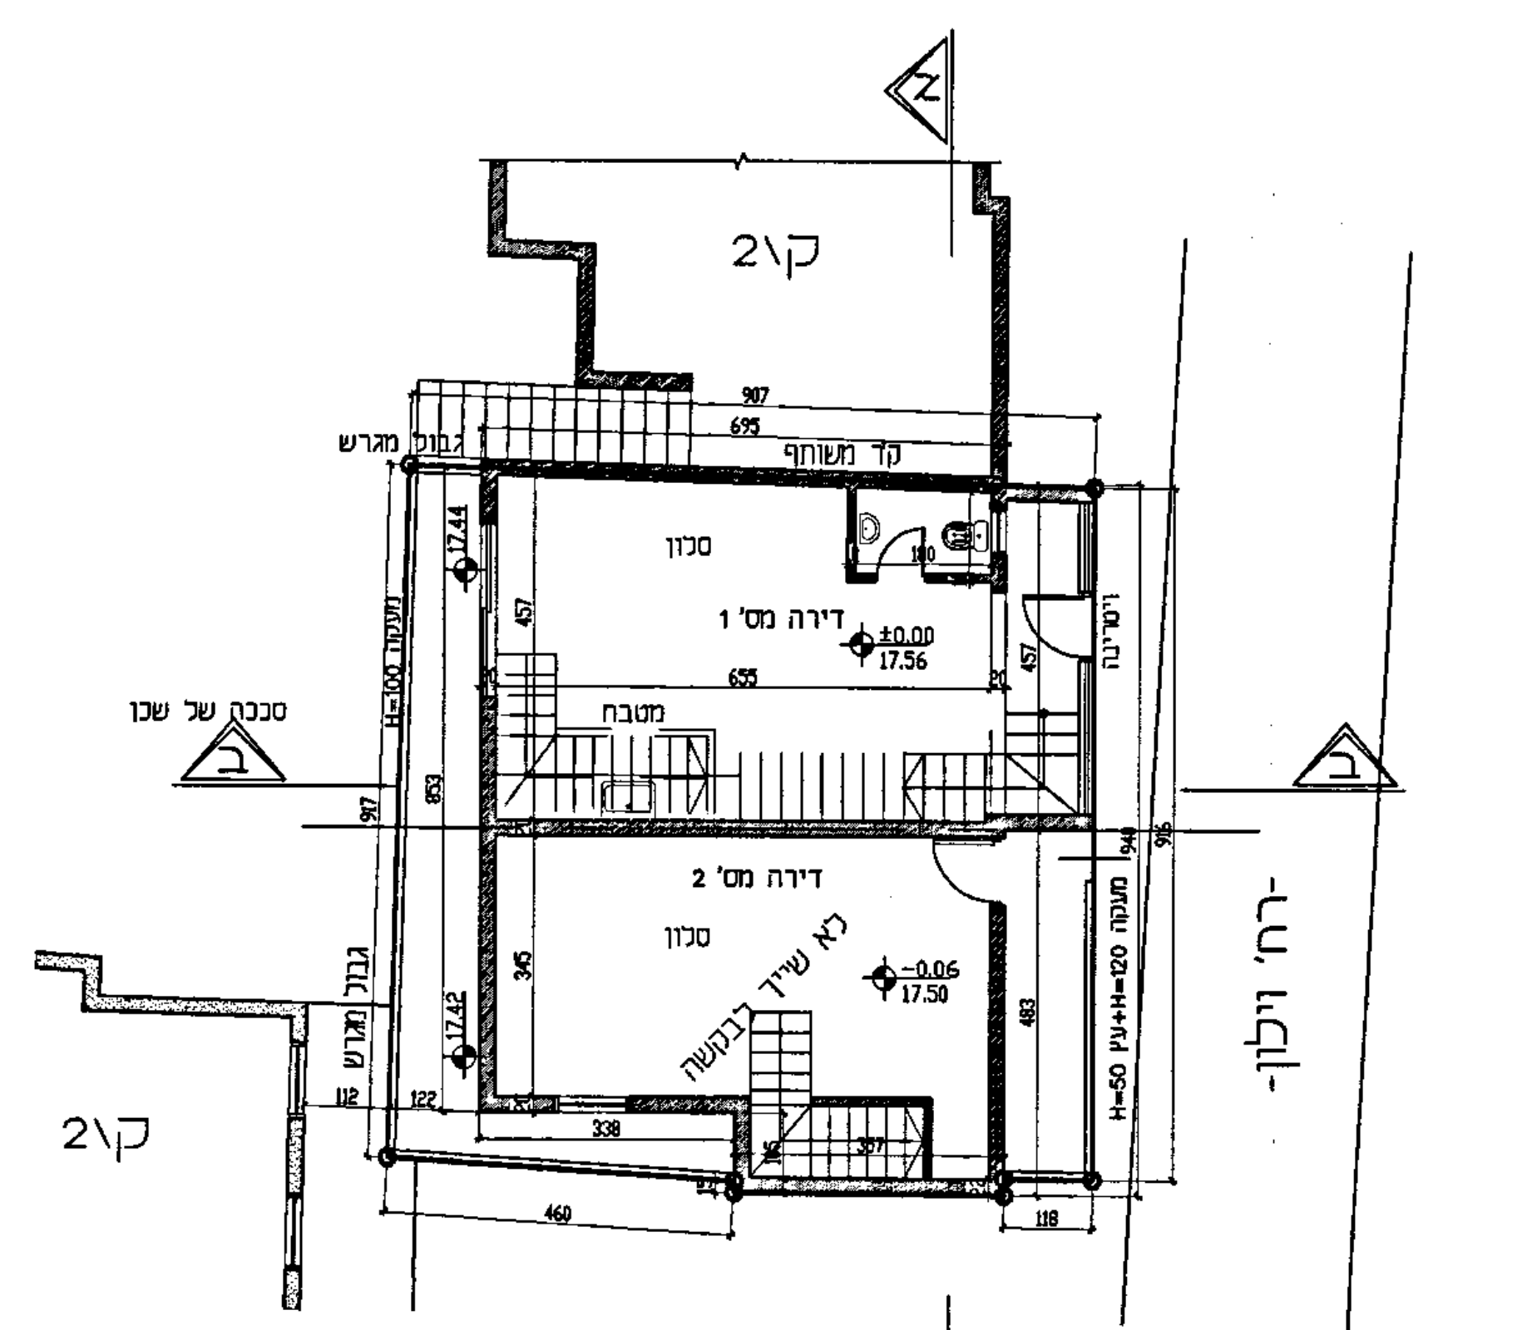

תכנית קומת קרקע

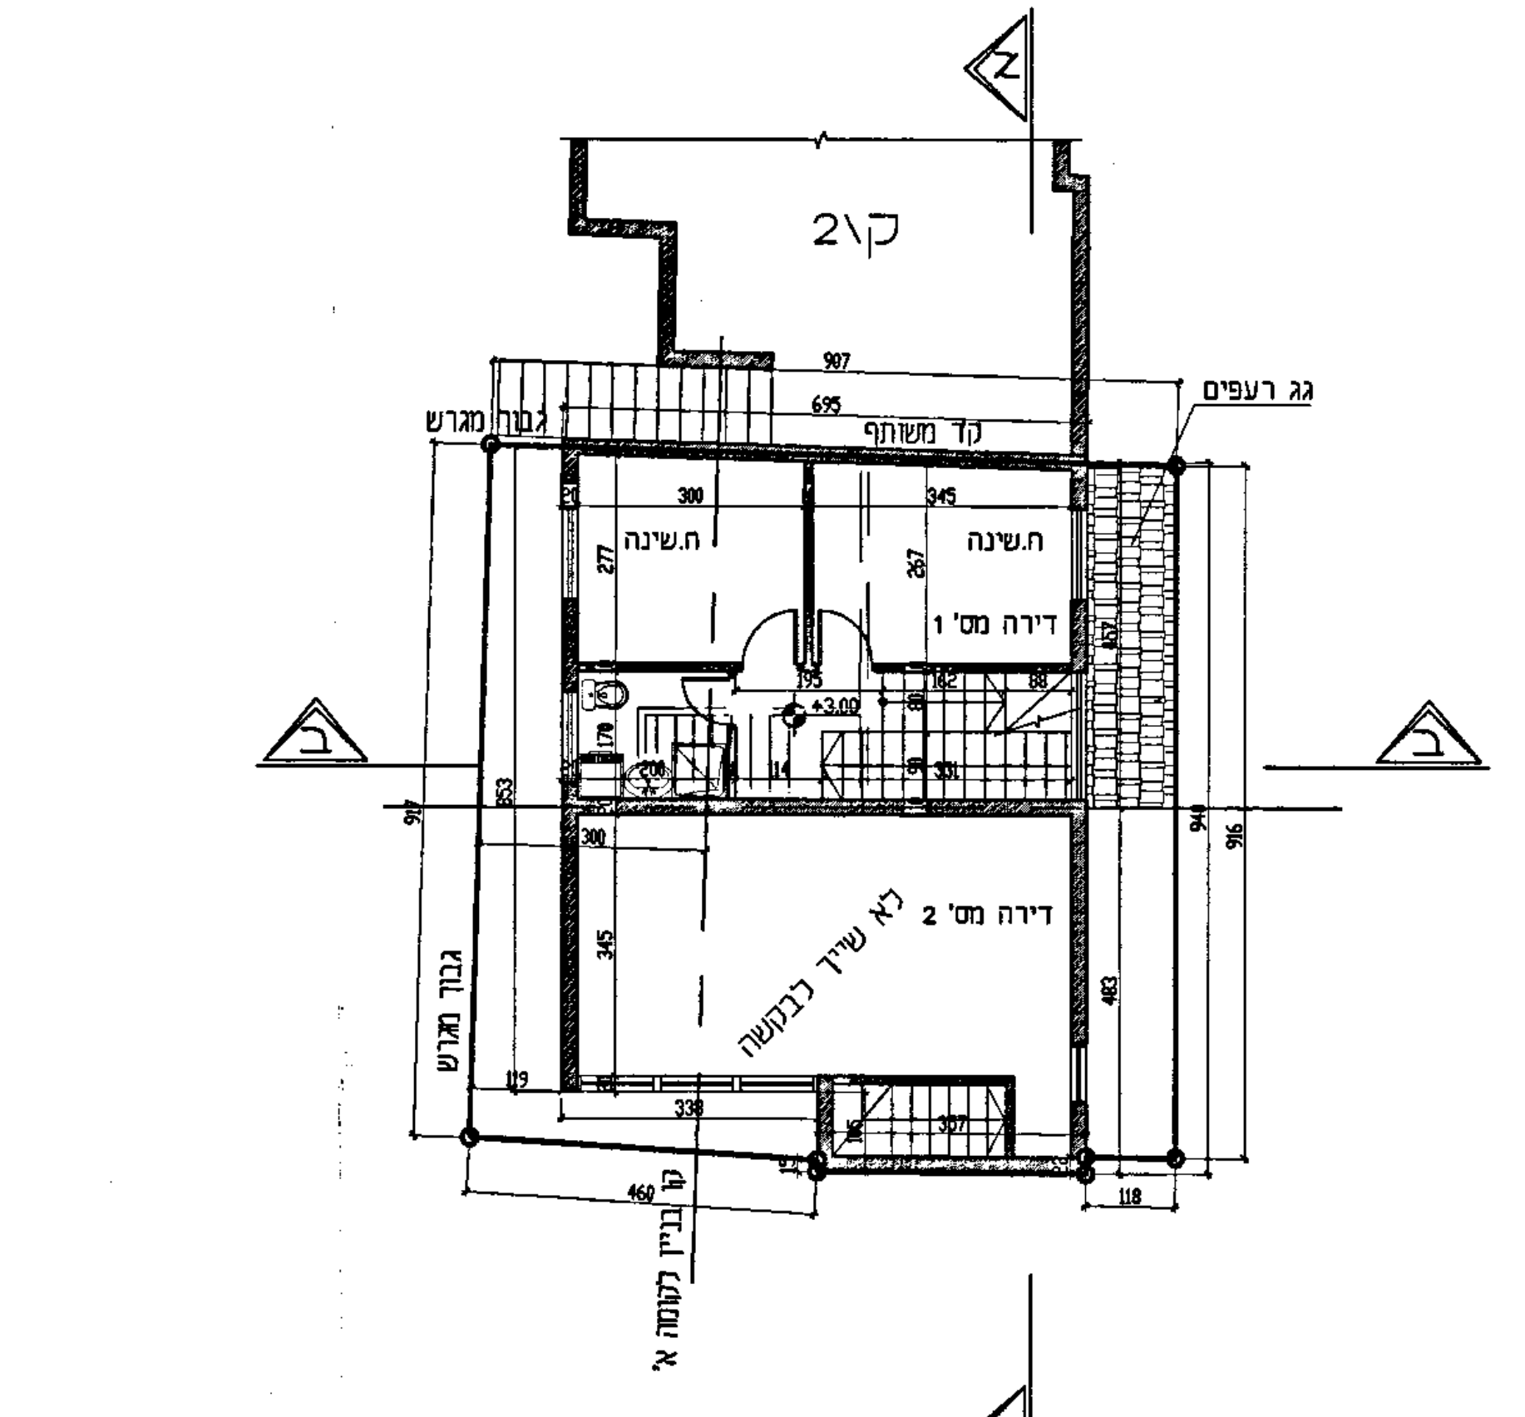

תכנית קומה א' ק.מ. 1:100

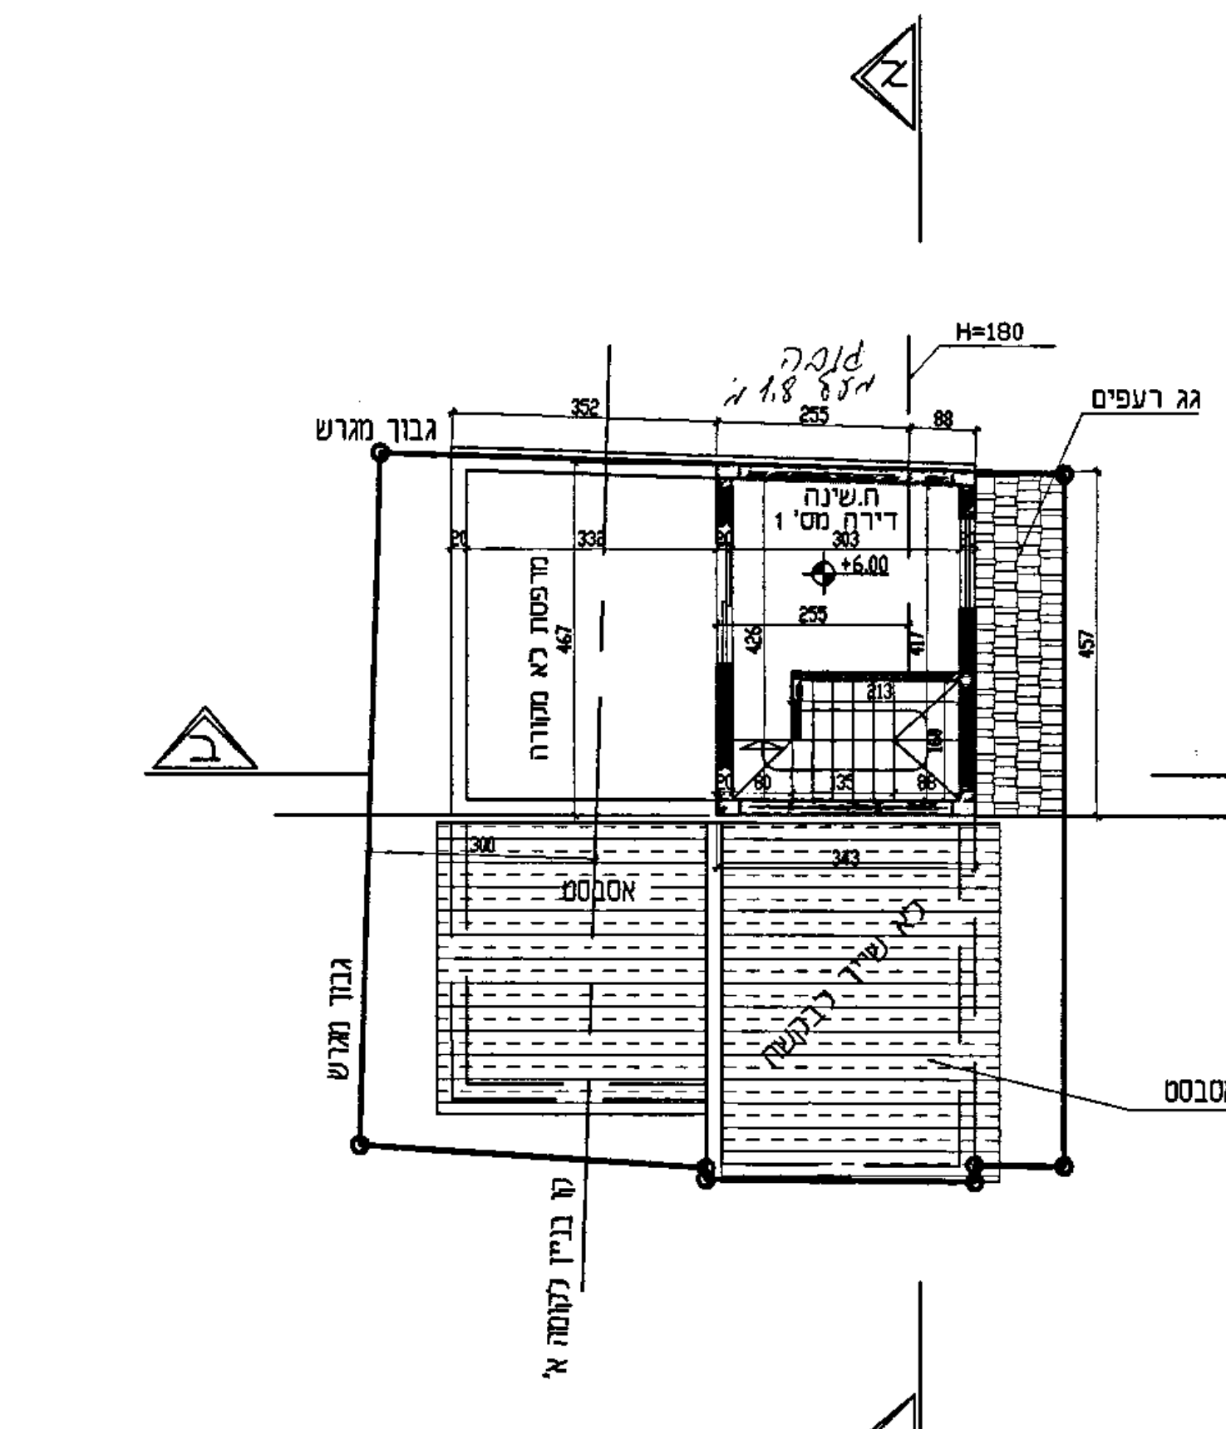

תכנית קומת גג ק.מ. 1:100

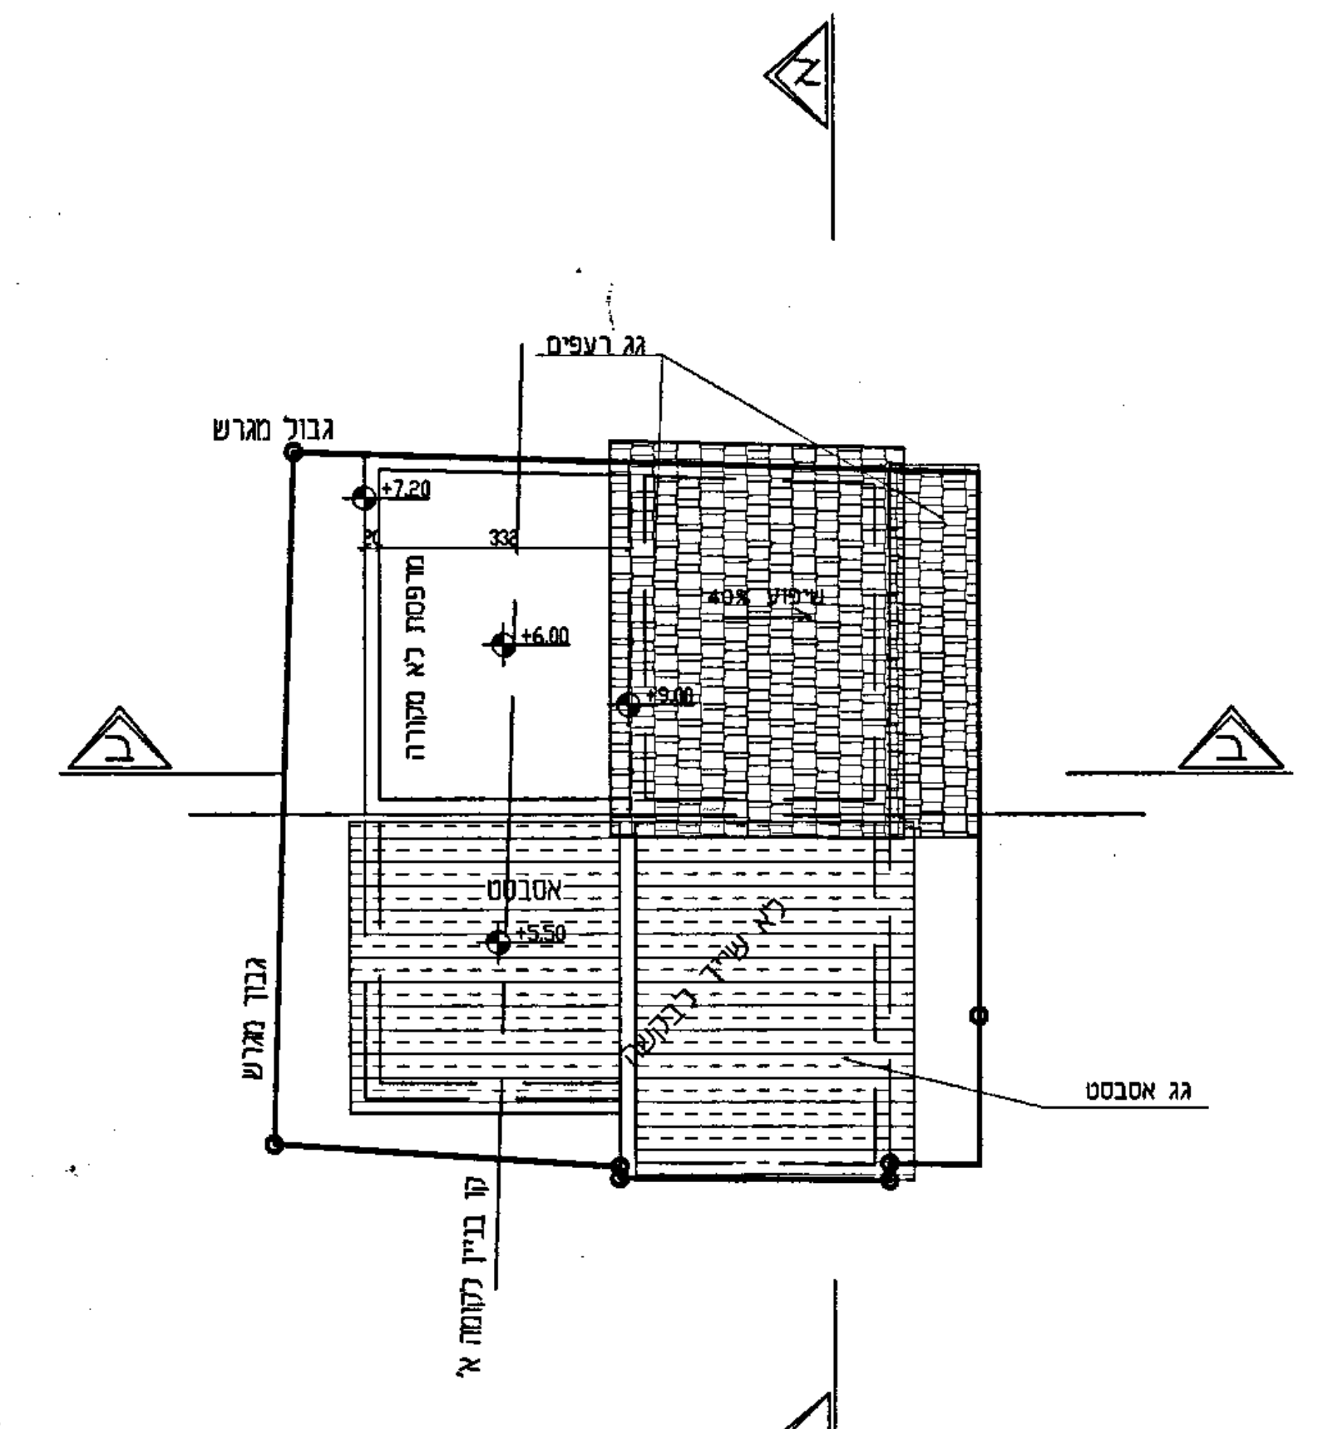

תכנית גג ק.מ. 1:100

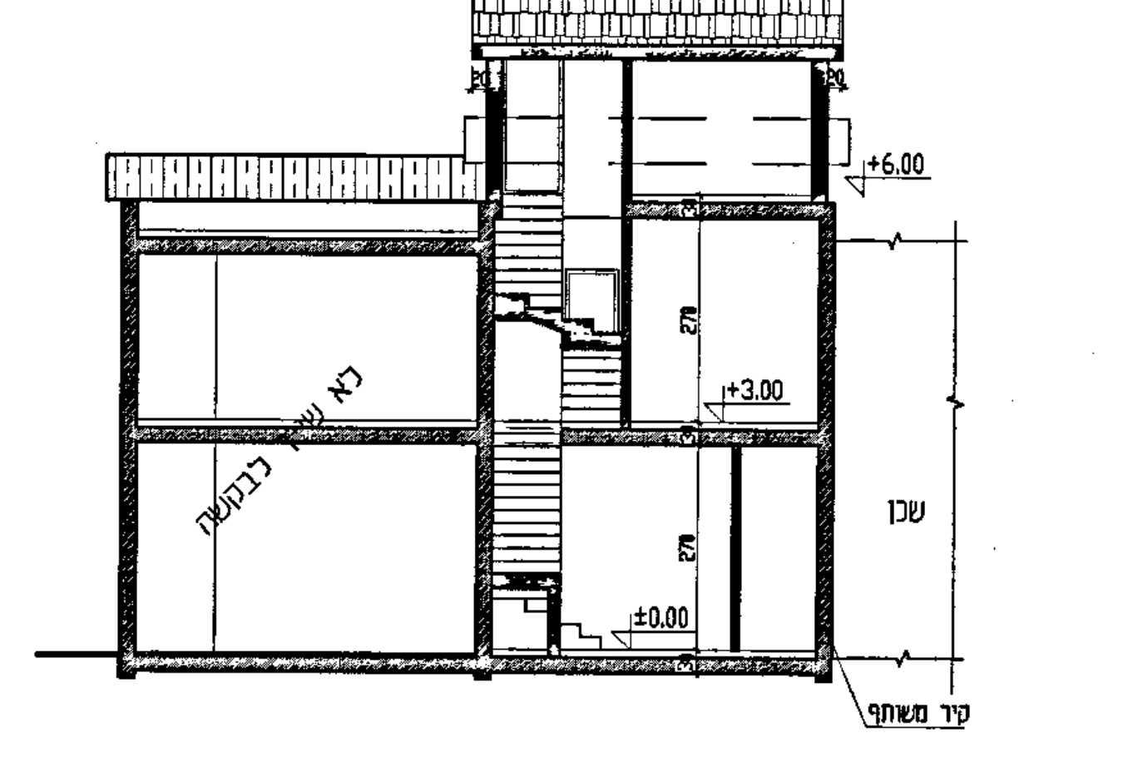

חתך א-א ק.מ. 1:100

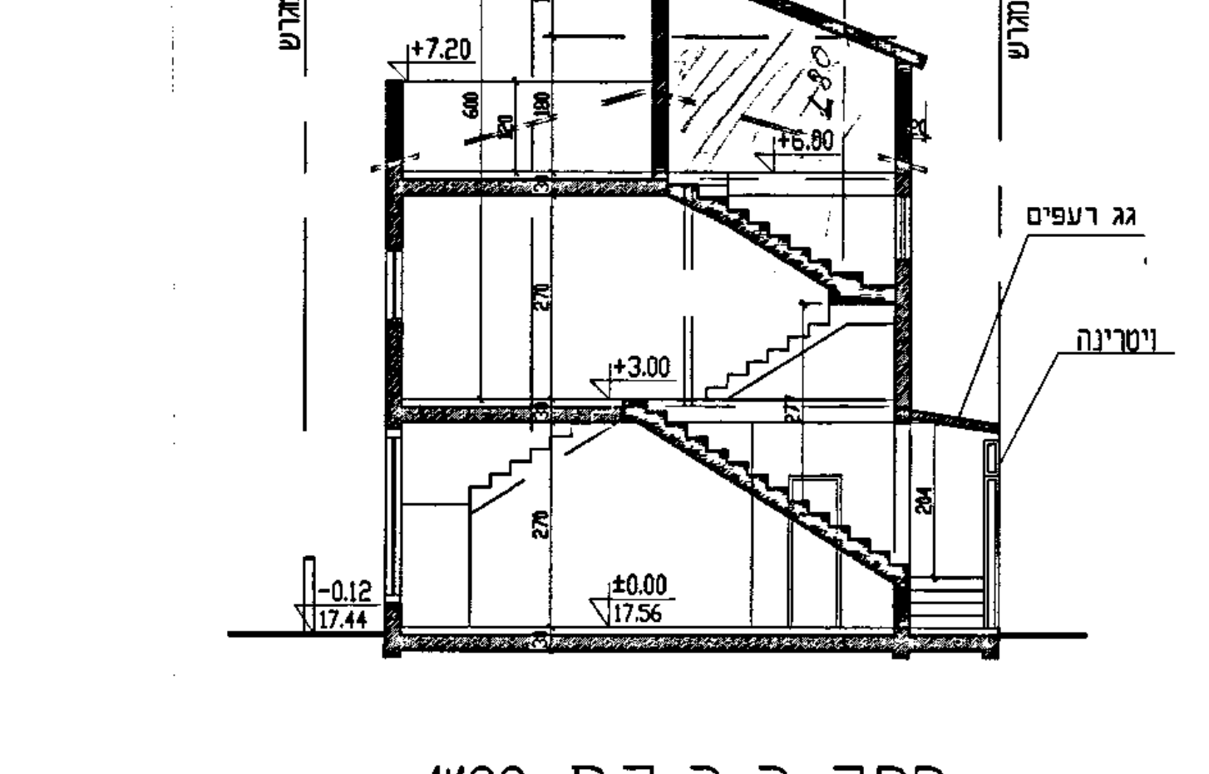

חתך ב-ב ק.מ. 1:100

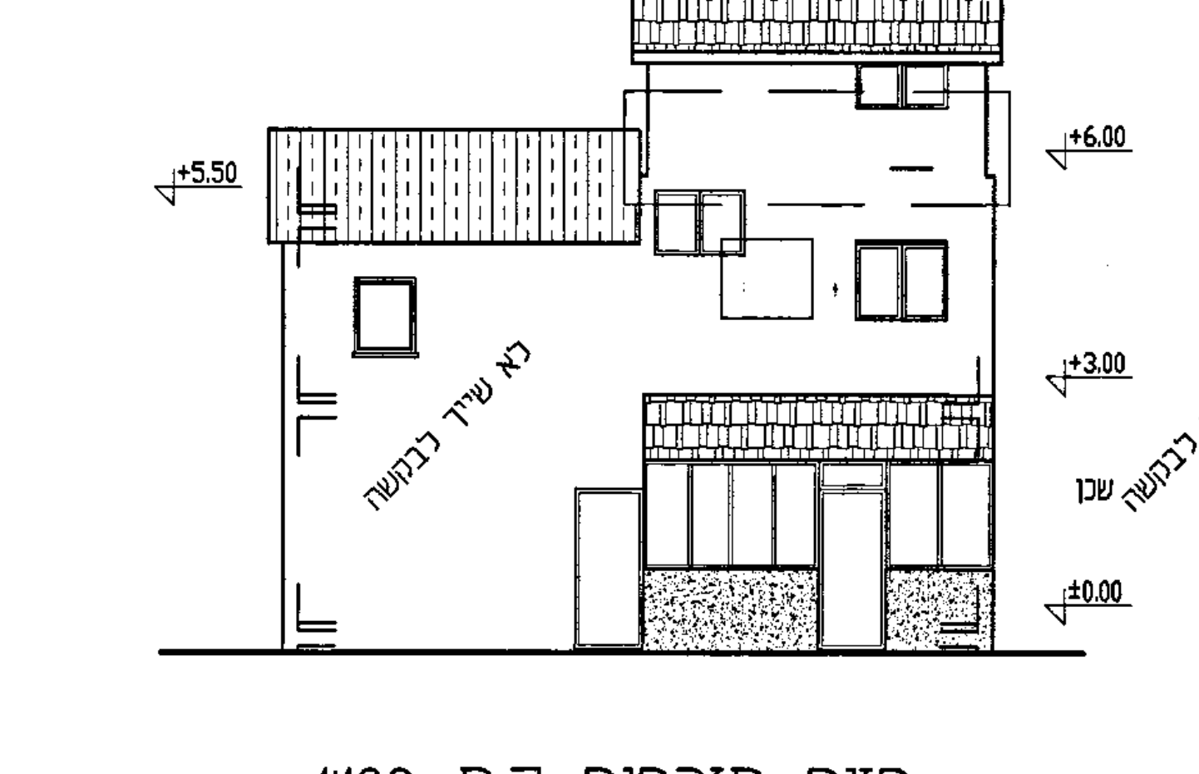

חזית מזרחית ק.מ. 1:100

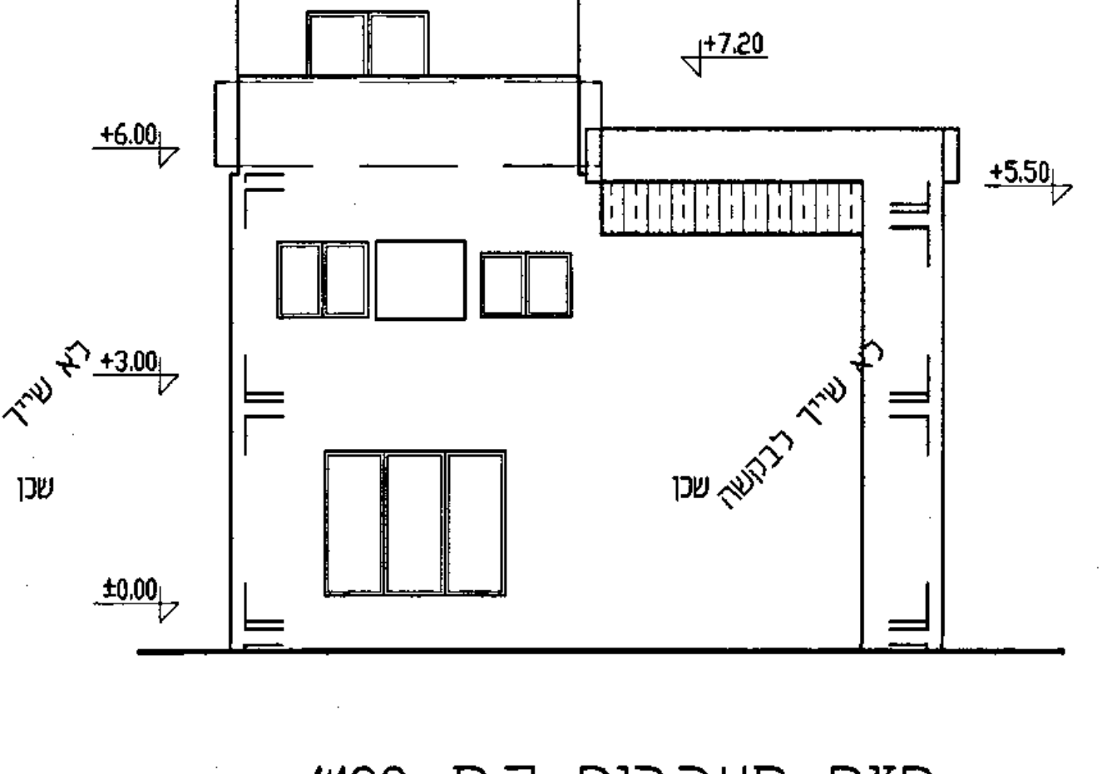

חזית מערבית ק.מ. 1:100