


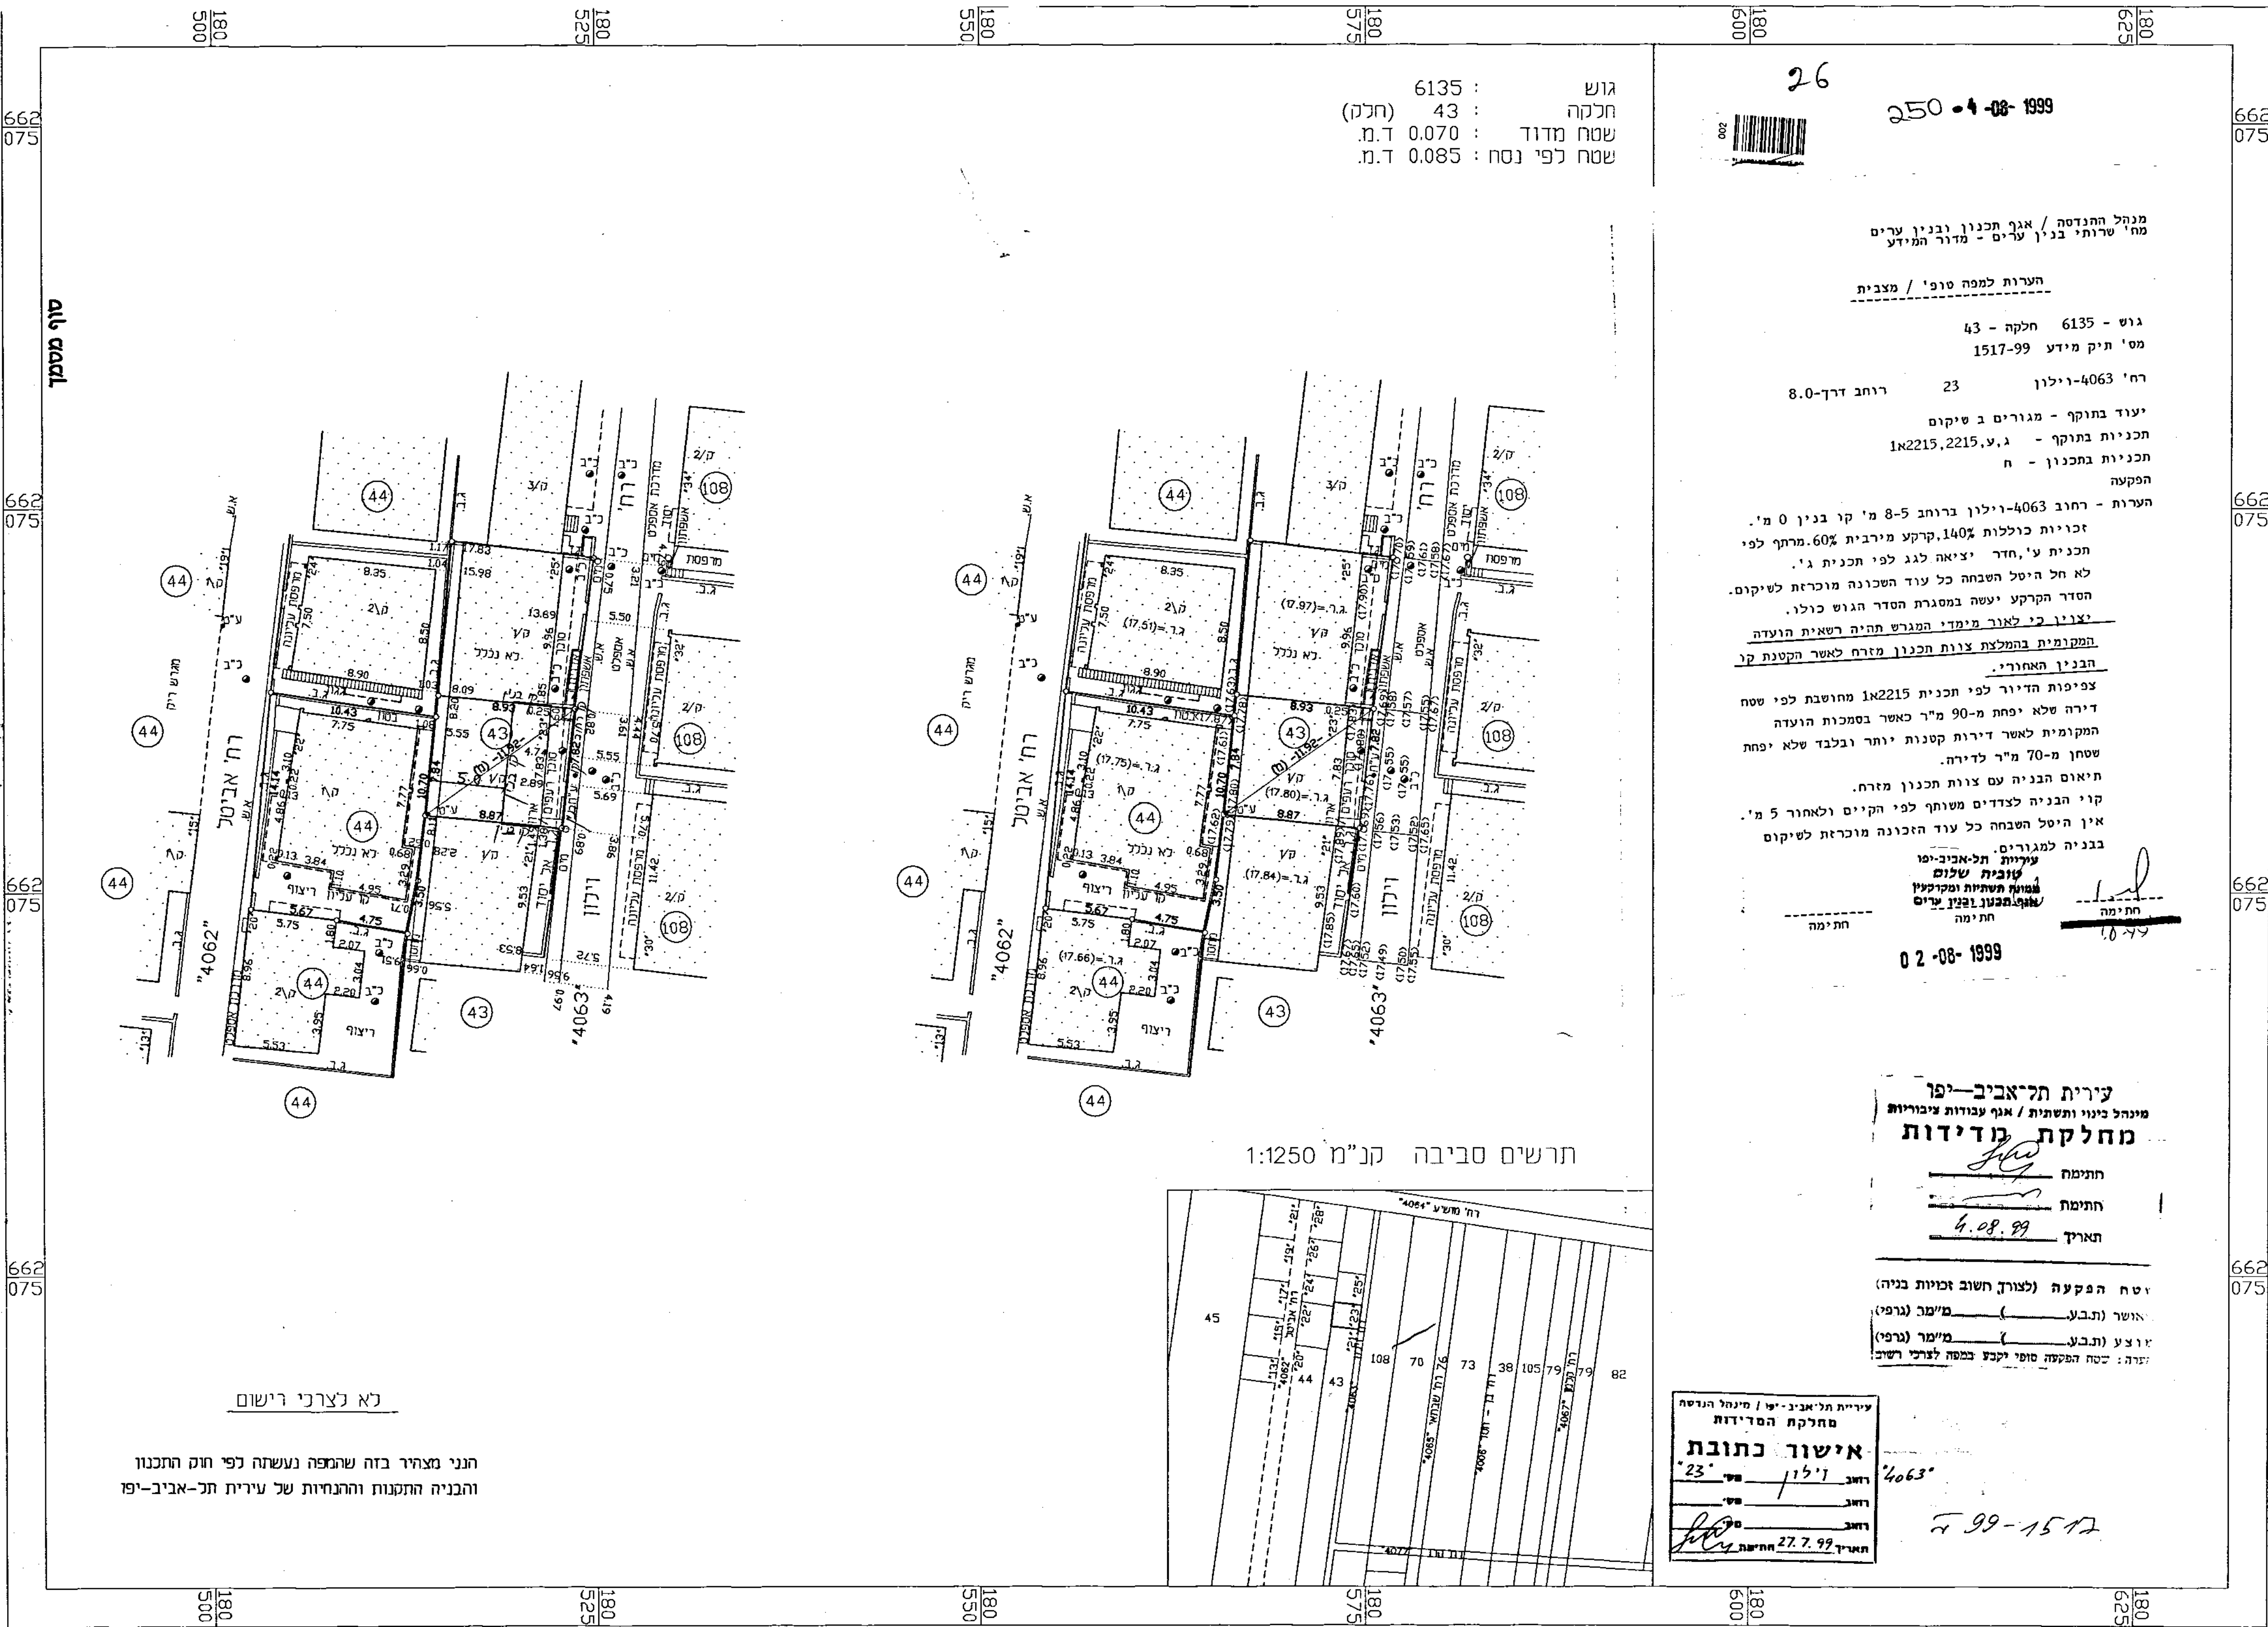

26
250-1-08-1999

מנהל ההנדסה / איגוד הנדסאי יבנה
מח' שירותי בניין ערים - מדור המידע

הערות למפה טופ' / מצבית

גוש - 6135 חלקה - 43
מס' תיק מידע - 1517-99

רח' 4063-וילון 23 רחוב דרך-8.0
יעוד בתוקף - מגורים ב שיקום
תכנית בתוקף - ג, ג, 2215, 2215א
תכנית בתכנון - ח
הפקעה

הערות - רחוב 4063-וילון ברובו 8-5 מ' קו בנין 0 מ'.
זכויות כוללות 140%, קרקע מירבית 60%. מרחף לפי
תכנית ע', חדר, ציאה לגג לפי תכנית ג'.
לא חל היסל השבחה כל עוד השכונה מוכרזת לשיקום.
הסדר הקרקע יעשה במסגרת הסדר הגוש כולו.
יצונו כי לאור מ'מדי המגרש תהיה רשאית הועדה
התקומית בהחלטת צוות התכנון מזהר לאשר הקטנת קו
הבנין האחורי.
צפיפות הדירור לפי תכנית 2215א מחושבת לפי שטח
דירה שלא יפחת מ-90 מ"ר כאשר בסמכות הועדה
התקומית לאשר דירות קטנות יותר ובלבד שלא יפחת
שטחן מ-70 מ"ר לדירה.
תיאום הבניה עם צוות תכנון מזהר.
קוי הבניה לצדדים משותף לפי הקיים ולאחר 5 מ'.
אין היסל השבחה כל עוד הזכונה מוכרזת לשיקום
בבניה למגורים.

עיריית תל-אביב-יפו
שירותי תכנון
מחלקת תכנון ומידע
מח' תכנון ומידע
תח"מ
לפי 1.0
02-08-1999

עיריית תל-אביב-יפו
מנהל בנין ותשתיות / איגוד הנדסאי יבנה
מחלקת מדידות

תח"מ
תח"מ
תאריך 4.08.99


יש להפקעה (לצורך חשבון זכויות בניה)
אשר (תבע) מ"מ (נרפס)
אוצע (תבע) מ"מ (נרפס)
יזהר: יסח הפקעה סופי יקבע בבמה לצדרי רשמי

עיריית תל-אביב-יפו / מנהל הנדסה
מחלקת המדידות
אישור נתובת
רשם 23
רשם 23
רשם 23
תאריך 27.7.92

שבתאי הפנר -מודד מוסמך BA רישון מס' 484
רחוב המעלות 12 גבעתיים, טלפון 03-5731402

הוכן עבור : סטואני נתן

קנה מידה 1:250

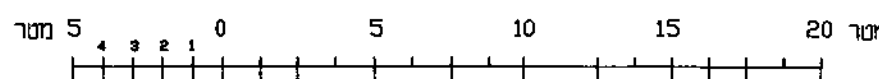

הערות:
1. המטרה שלשמה נערכה המפה: בניה
2. שיטת ביצוע עבודה פלנימטרית:קוטבית
3. שיטת ביצוע עבודה אלטימטרית: איוון
4. הפלנימטריה מבוססת על נק: ית/3012, ית/3013
5. האלטימטריה מבוססת על נק: 413=17.638 מ
גובה מתואם (חדש/שח):

אני מאשר כי מפה זו היא העתק נכון של המפה הטופוגרפית שהכנתי
על סמך מדידה שהסתיימה ביום 21 בחודש 07 שנת 1999
וכי כל הפרטים שצוינו במפה הם מדויקים ודרגה היא: א'
המפה בוצעה בהתאם לתקנות המודדים (מדידות ומפוי) התשנ"ח-1998
תאריך: 22.07.1999 ש. הפנר, המעלות 12 גבעתיים, מס' רישון: 484
שם המודד ומענו: חתומה:

