

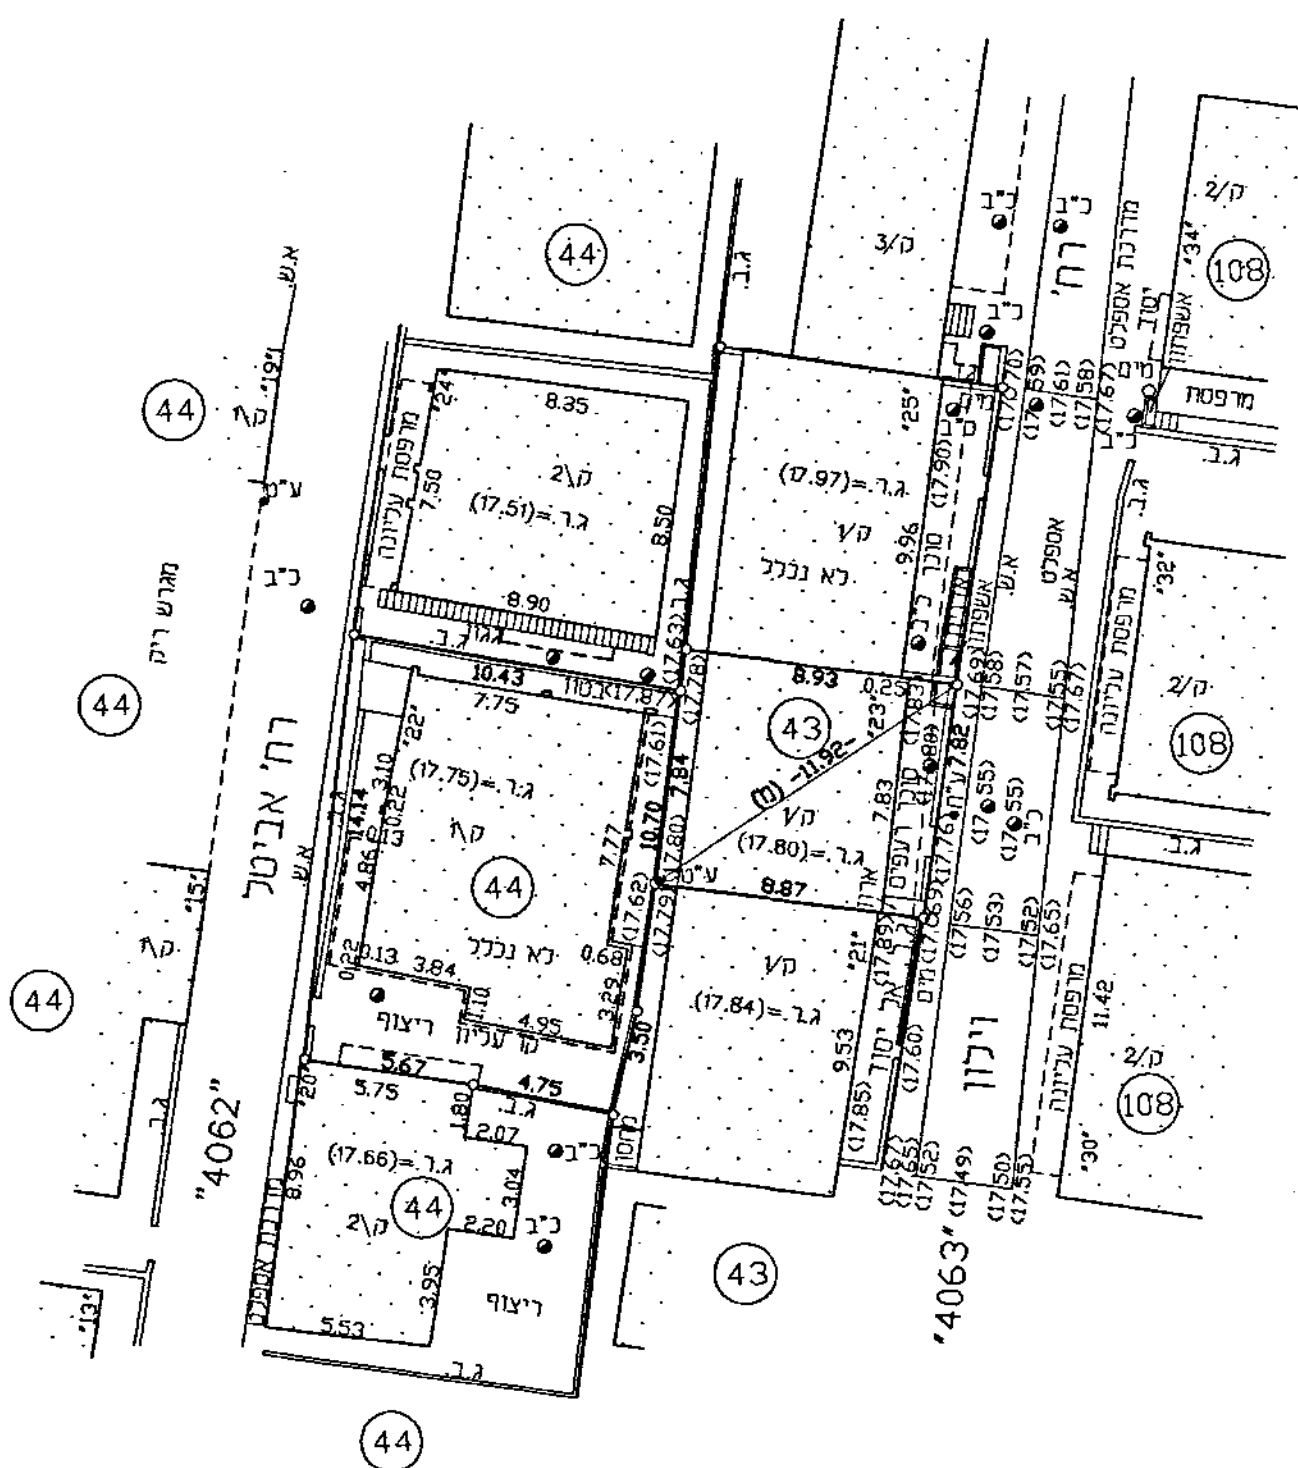


26

גוש : 6135
חלקה : 43 (חלק)
שטח מדוד : 0.070 ד.מ.
שטח לפי נסח : 0.085 ד.מ.

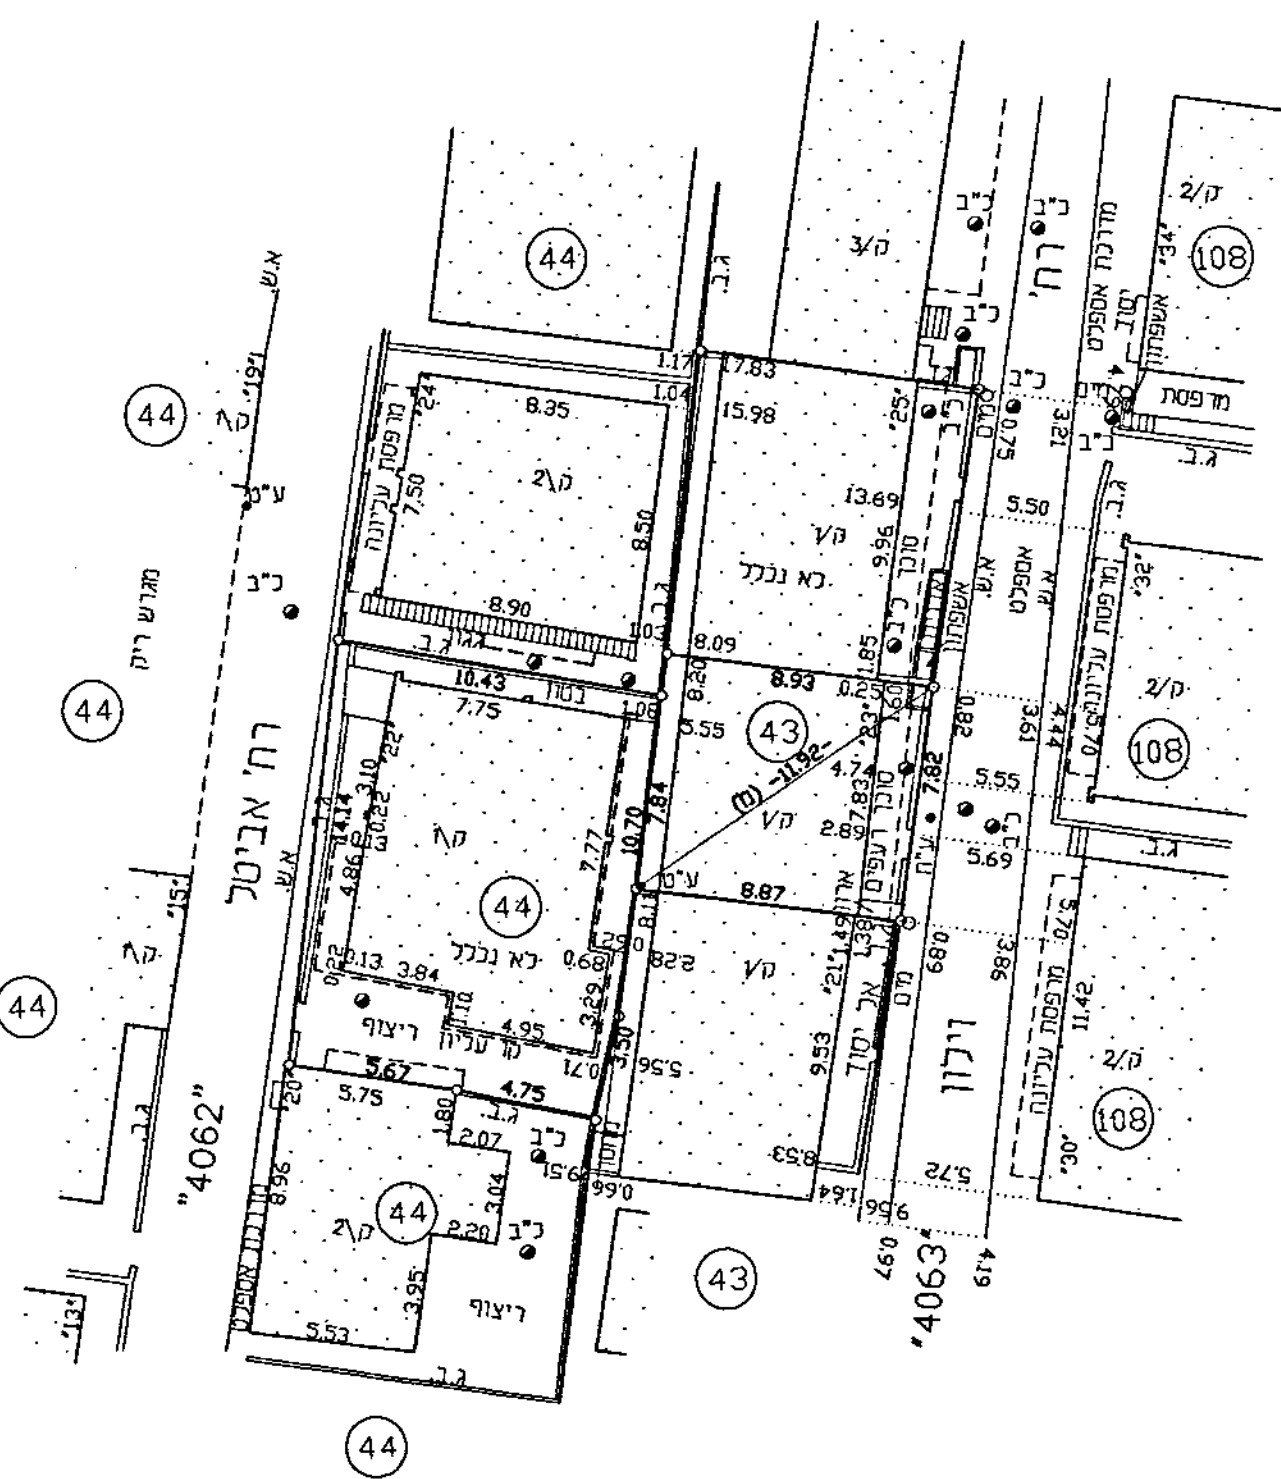

חרשים סביבה קנ"מ 1:250

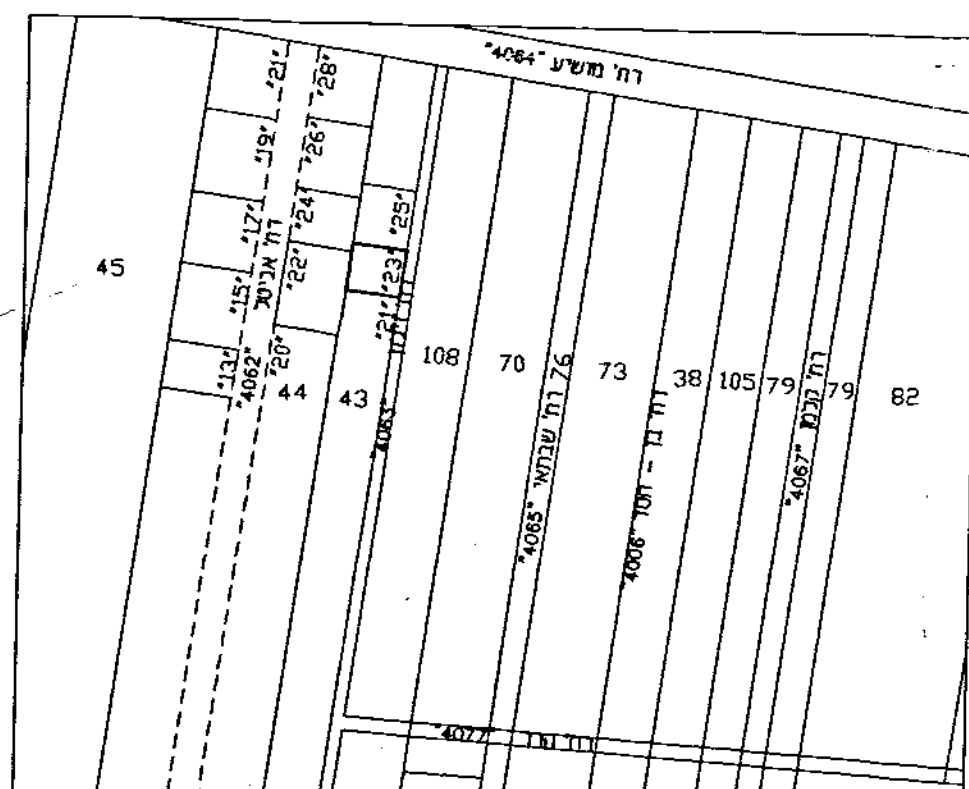

עדיית תלמידי-ישי / מינהל הנדסה
מחלקת המדידות
אישור כתובת
רחוב: 1517
מס': 23
רחוב: 1517
מס': 23
תאריך: 27.7.99 חתימה: [Signature]

1517-99

לא לצרכי רישום
הגני מצויר בזה שהמפה נעשתה לפי חוק התכנון
והבניה התקנות וההנחיות של עיריית תל-אביב-יפו

אני מאשר כי מפה זו היא העתק נכון של המפה הטופוגרפית שהכנת
על סמך מדידה שהסתיימה ביום 21 בחודש 07 שנת 1999
וכי כל הפרטים שצוינו במפה הם מדויקים ודרגתה היא: א'
המפה בוצעה בהתאם לתקנות המודדים (מדידות ומפוי) התשנ"ח-1998
תאריך: 22.07.1999 ש. הפנר המעלות 12 גבעתיים מס' רשיון: 284
שם המודד ומענו חתימה: [Signature]

- הערות:
1. המטרה שלשמה נערכה המפה: בניה
 2. שיטת ביצוע עבודה פלנימטרית: קוטבית
 3. שיטת ביצוע עבודה אלטימטרית: אידון
 4. הפלנימטריה מבוססת על נק: ית/3012: ית/3013
 5. האלטימטריה מבוססת על נק: 413=17.638 מ
- גובה מתואם (חדש/ישן):

הוכן עבור : סנואני נתן

שבתאי הפנר - מודד מוסמך BA רשיון מס' 484
רחוב המעלות 12 גבעתיים, טלפון 5731402/3-03.

קנה מידה 1:250

