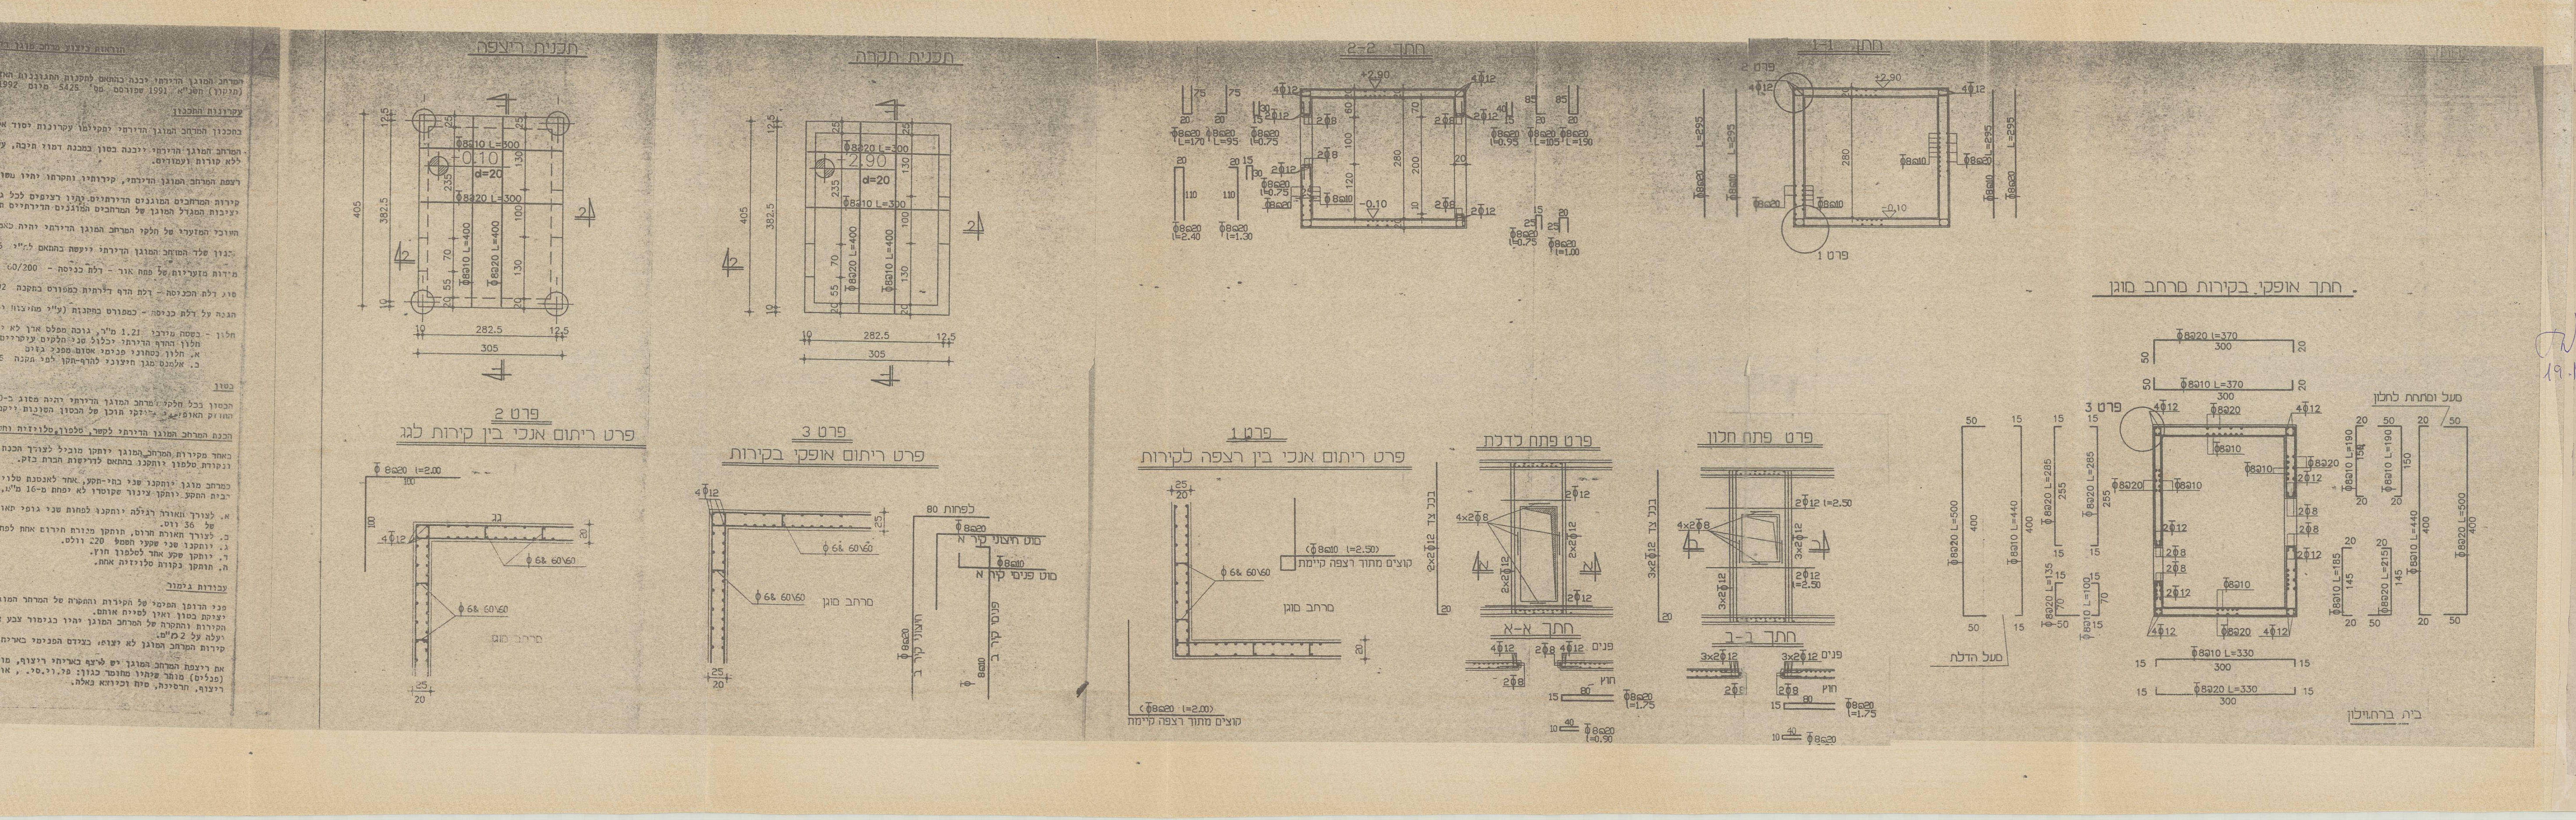
תכנית רצפה
תכנית תקרה
פרט 2
פרט ריתום אנכי בין קירות לגג
פרט 3
פרט ריתום אופקי בקירות
פרט 1
פרט ריתום אנכי בין רצפה לקירות
פרט פתח לדלת
פרט פתח חלון
חתך א-א
חתך ב-ב
חתך אופקי בקירות מרחב מוגן
פתח הלה
בית ברתמכן

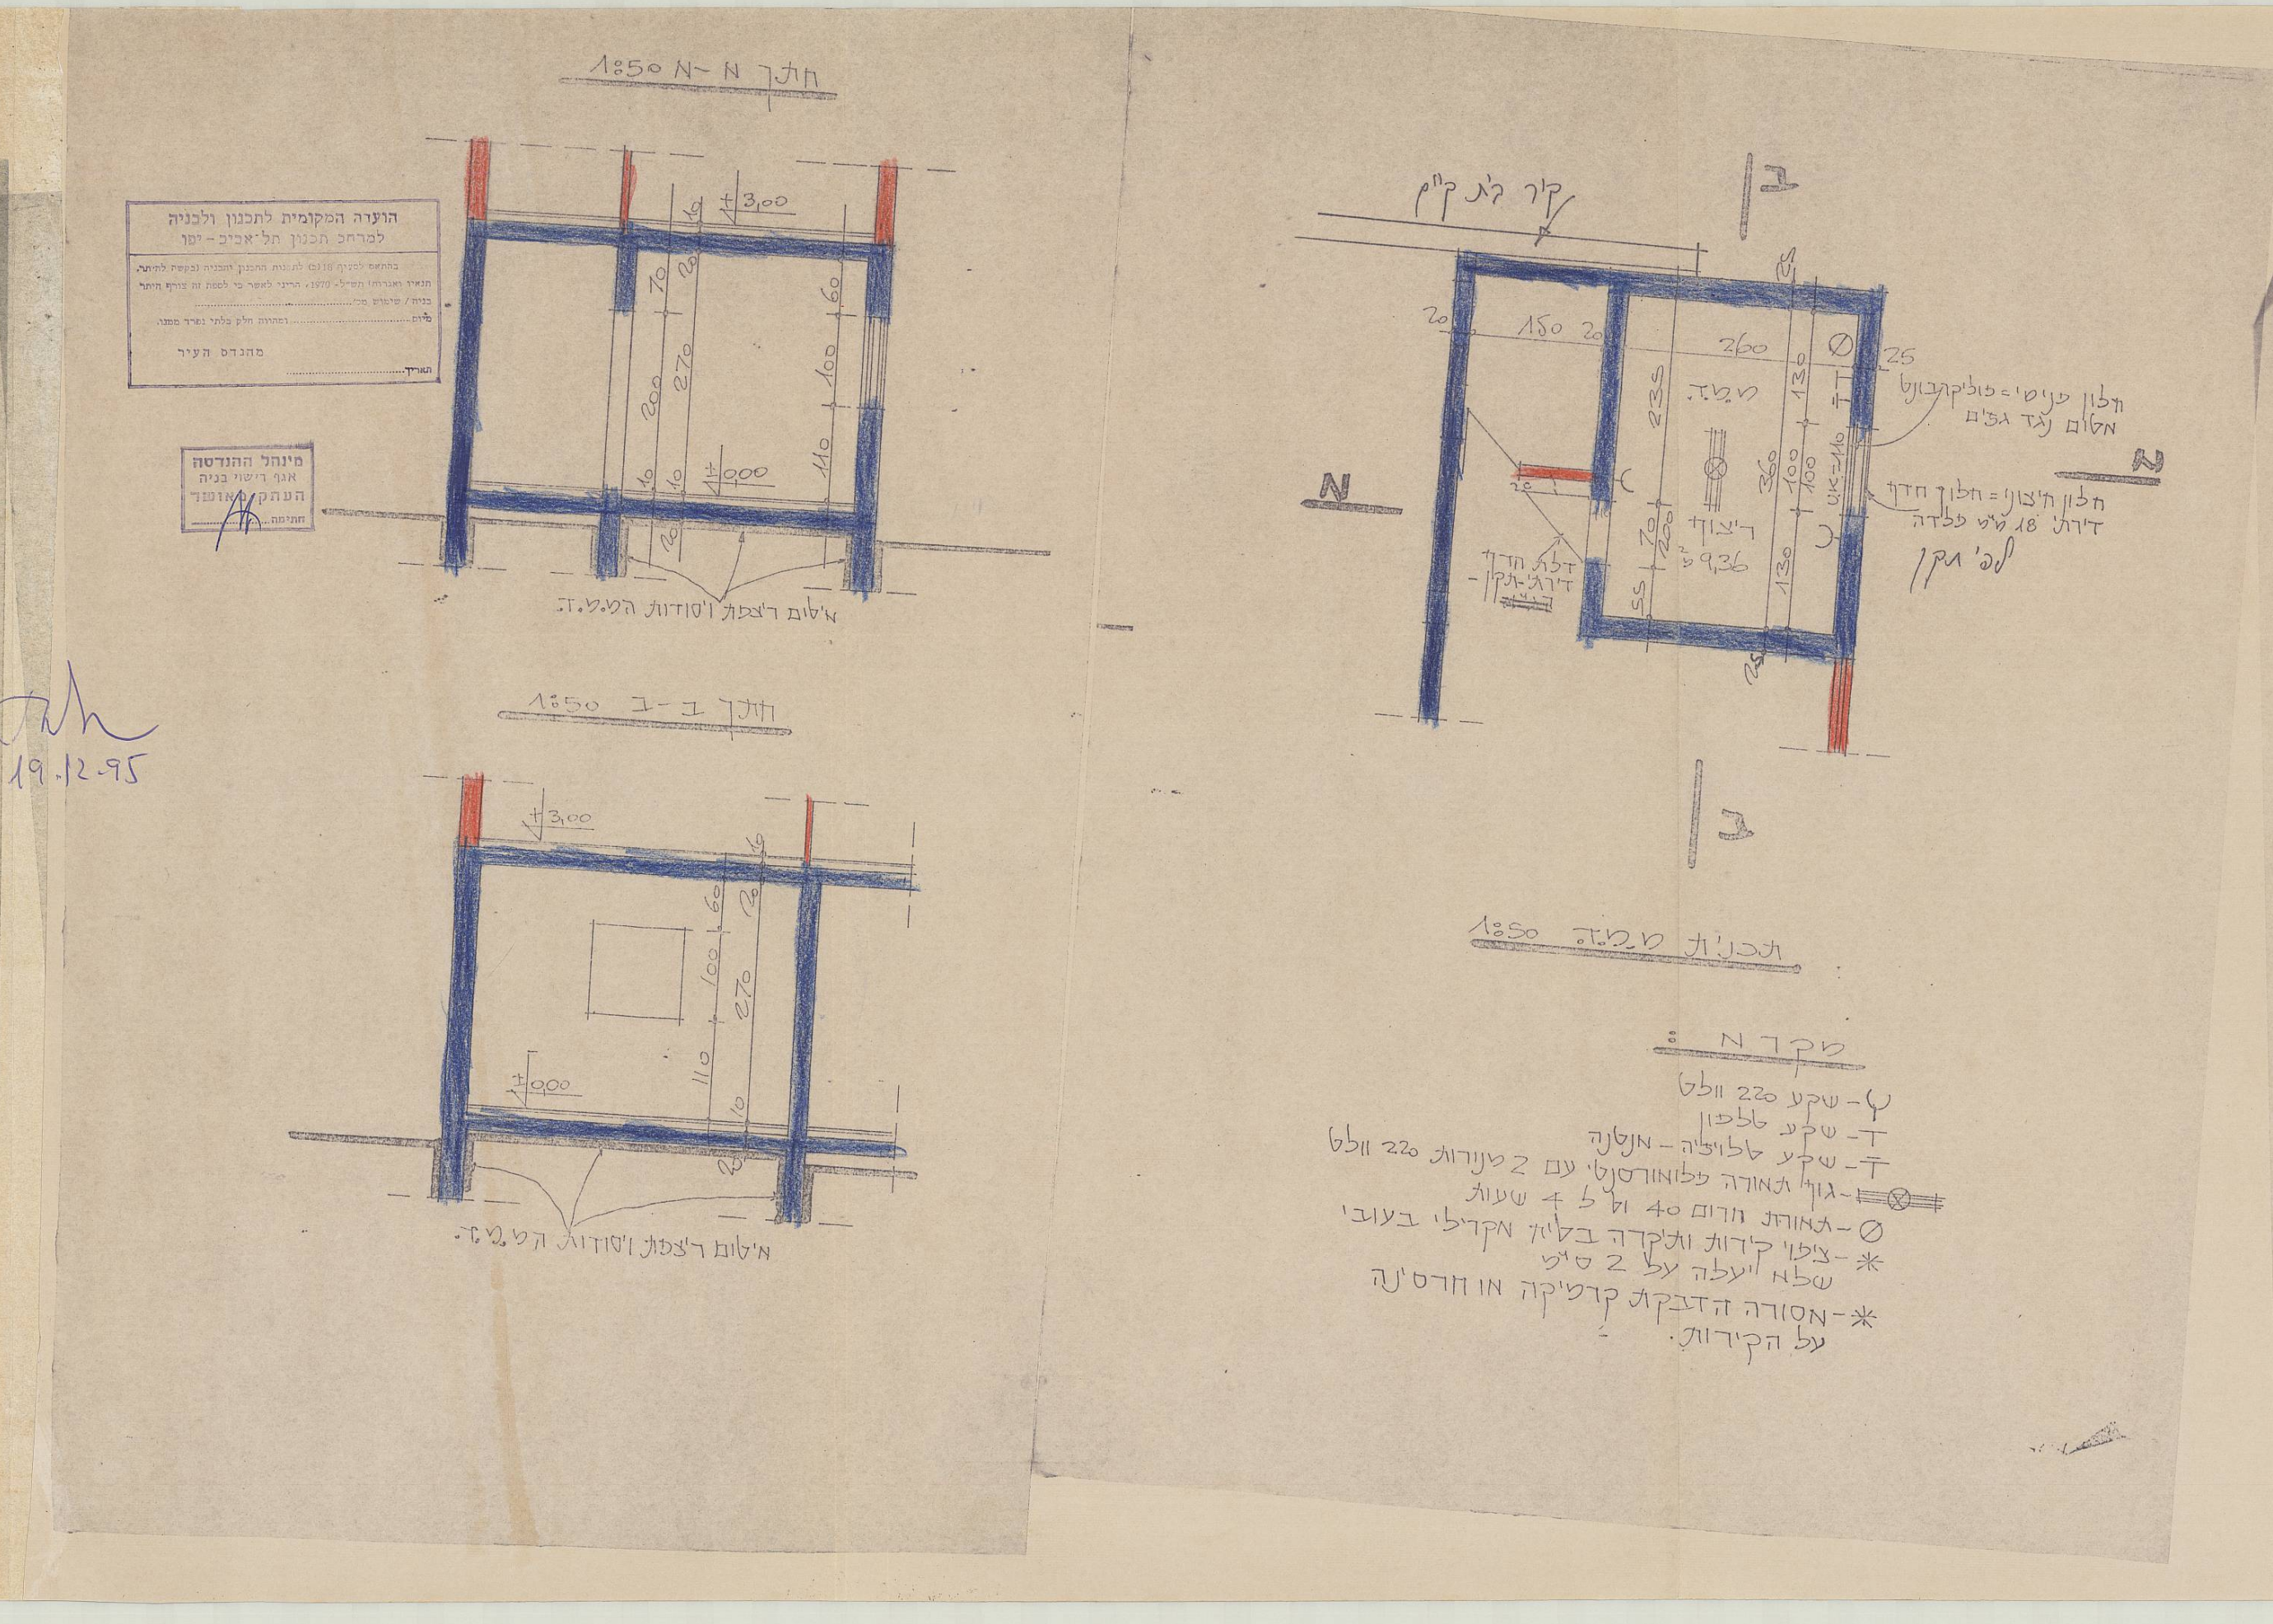
חתך א-א
חתך ב-ב
קיר של שכן
N
ב
ב

19.12.95

בית שכן
ב
ב
N
N
N
N
N
N
N
חזית צדדית-דרומית
חזית אחורית
חזית לרחוב
חתך ב-ב
חתך א-א
תכנית גגג
תכנית קומה "ב"
תכנית קומה "א"
תכנית קומת קרקע

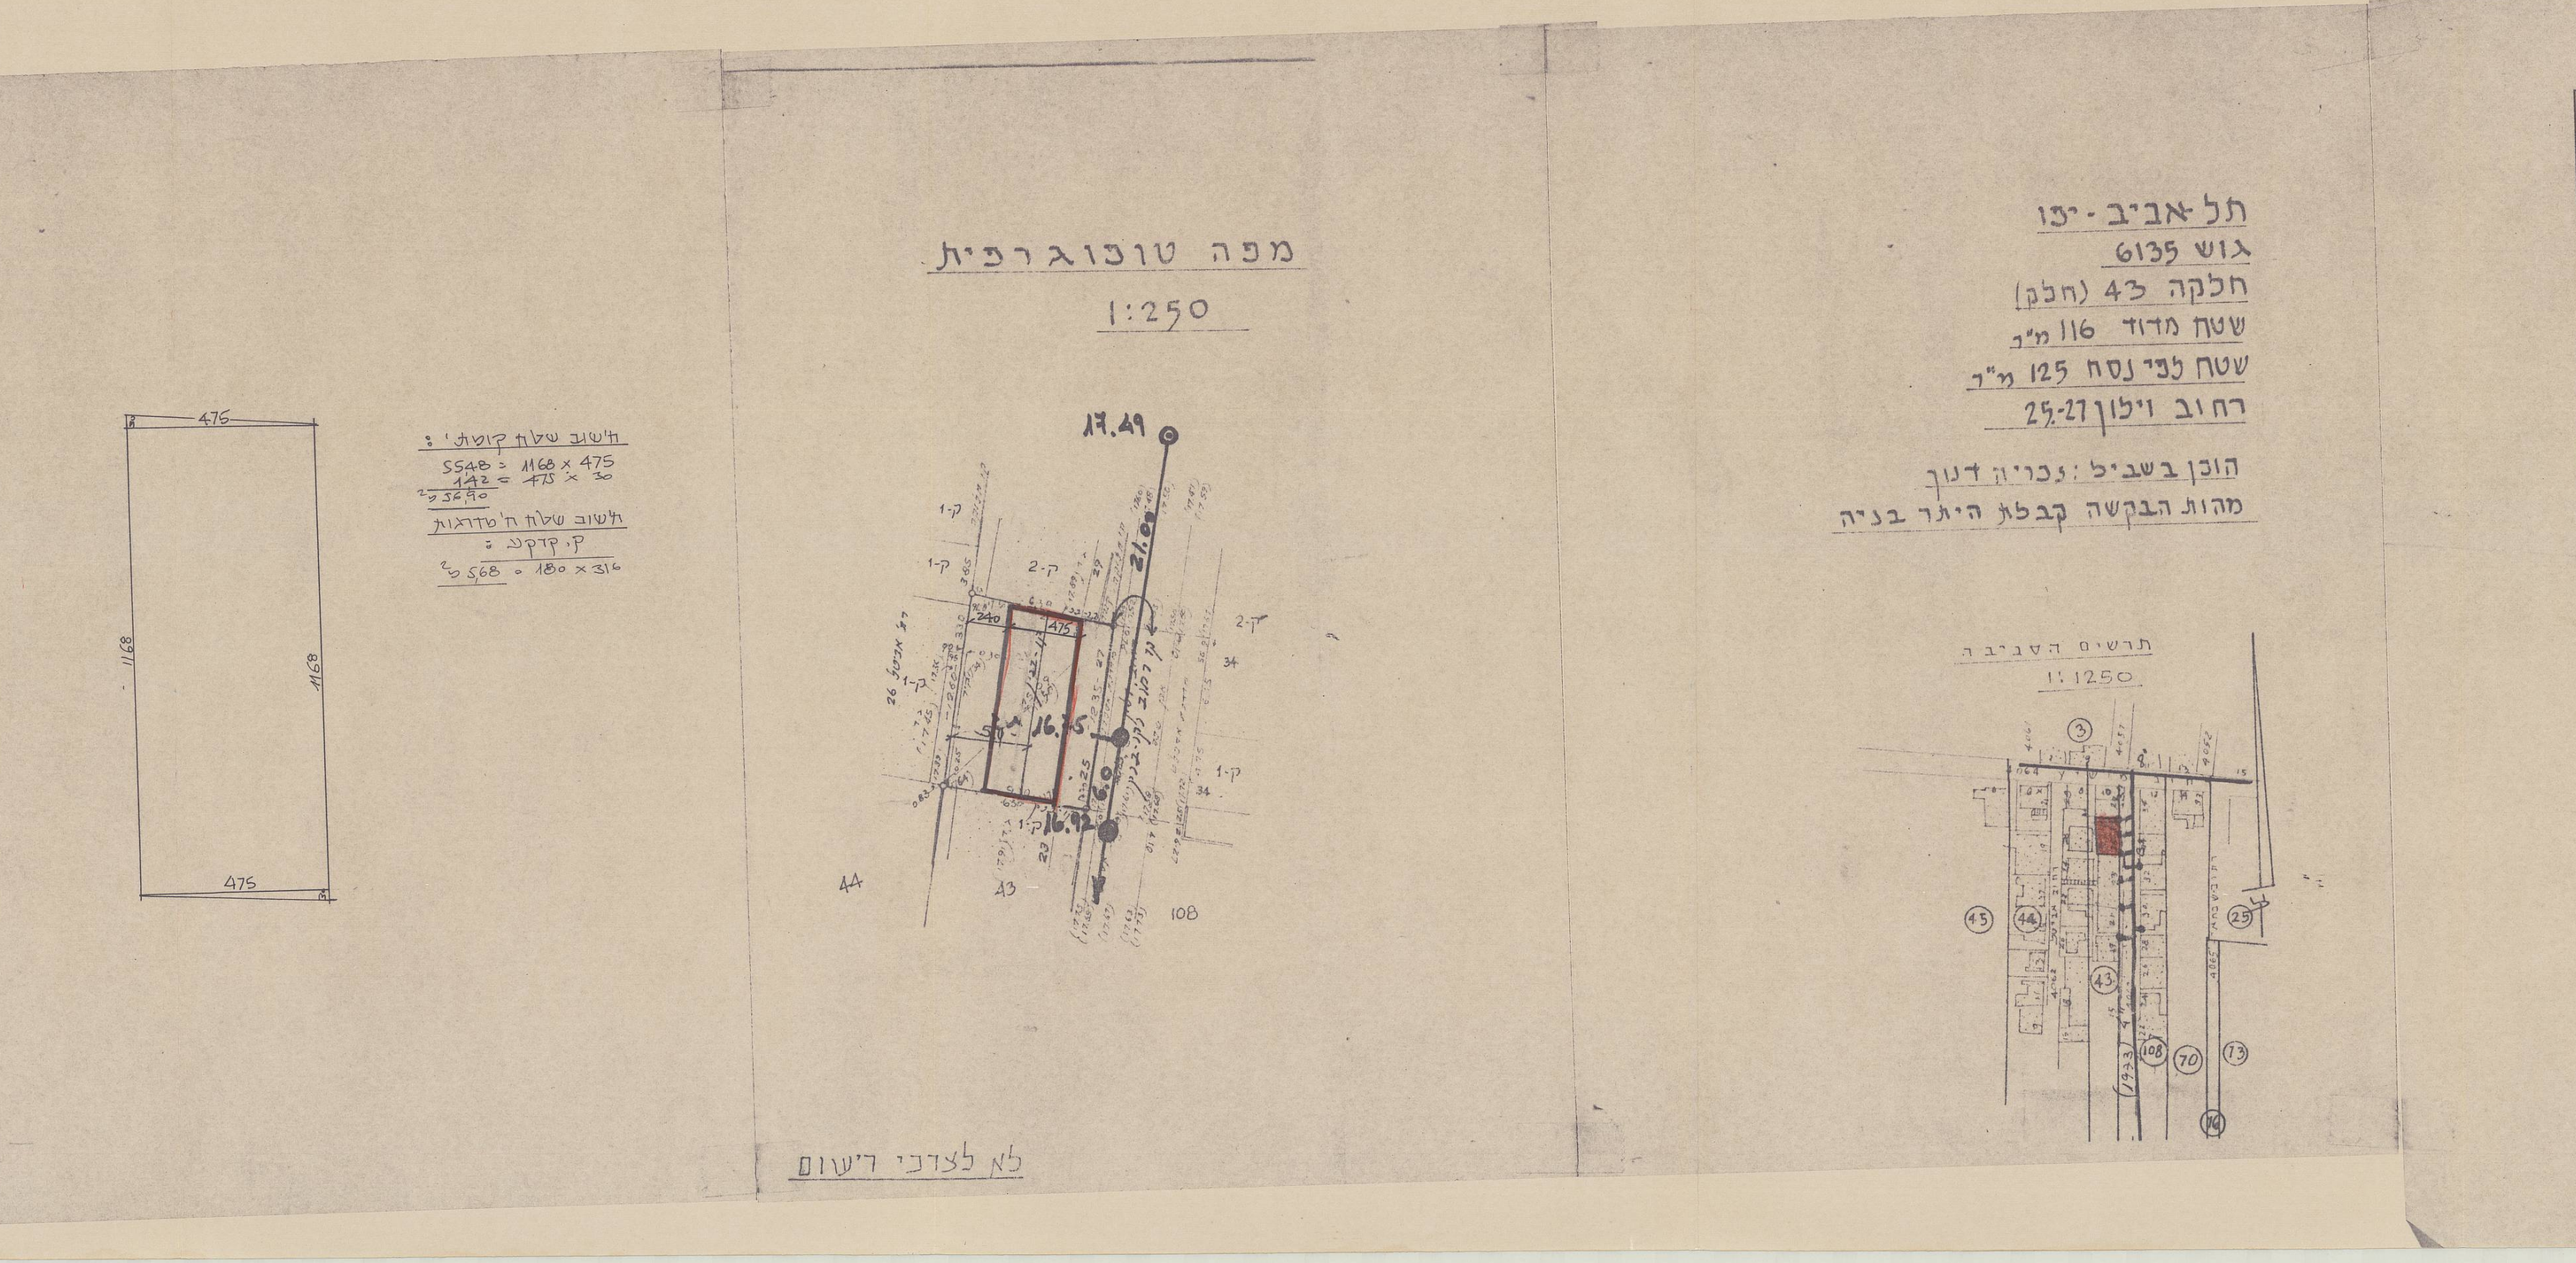
מפה טופוגרפית
1:250
חישוב שטח קומות:
5548 = 1168 × 475
142 = 475 × 30
56,90 מ"ר
חישוב שטח המדרגות
ק. קרקע:
5,68 מ"ר = 180 × 316
476
475
1168
17.69
16.75
16.92
21.60
43
44
108
לא לצרכי רישום
תרשים הסביבה
1:1250

תל-אביב - יפו

גוש 6135

חלקה 43 (חלק)

שטח מדוד 116 מ"ר

שטח לפי נסח 125 מ"ר

רחוב וילון 25-27

הוכן בשביל: זכריה דנוך

מהות הבקשה קבלת היתר בניה

עיריית תל-אביב-יפו

מינהל התחנדסה

טופס השו[illegible]

חלק א' - תאור הבקשה

6903184

29.3.94

29948

בנימין סוק

בן גוריון 63

מ. כהן

השטחים המבוקשים לבניה בכל מפלס בנפרד (עפ"י תכנית הבניה)

4491	56,90	11,12	12,68	5,68	7,00	38,98	44,22
4491	56,90					44,91	56,90
4491	56,90					44,91	56,90
149,73	170,70	11,12	12,68	5,68	7,00	138,60	158,02

השטחים המותרים לבניה בכל המפלסים יחד (עפ"י אסמכתא: חוק, תקנות, תכנית)

חוק התכנון והבניה, התשכ"ה-1965

בקשה להיתר בניה או לשימוש במקרקעין

מתוקן

טופס 1

תקנה 2(א)

4063-025

794-0685

תל אביב יפו

1680, ע, 2215

43

6135

25

וילון

4063

תאור הנכס

7514494

בן שמן 10 רמת-גן

5079592

בן גוריון 63 בת-ים

16310195

5221786

יהודה הלוי 17 ת"א

6903184

מיפרט

בית חדש קרקע + 2 קומות - דירה אחת

149,73

170,70

114,00

29.3.94

סוף מסמך

הועדה המקומית לתכנון ולבניה
למרחב תכנון תל-אביב-יפו
6-960130
31.1.96
מהנדס העיר
-7-01-1996

מינהל ההנדסה
אגף רישוי בניה
הותר לאישור
חתימה

הוראות ביצוע מרחב מוגן דירתי

המרחב המוגן הדירתי יבנה בהתאם לתקנות התגוננות האזרחית (מפרטים לבנית מקלט-ם). (תיקון) תשנ"א 1991 שפורסם מס' 5425 מיום 3.3.1992 .

עקרונות התכנון

בתכנון המרחב המוגן הדירתי יתקיימו עקרונות יסוד אלה:

המרחב המוגן הדירתי ייבנה בטון במבנה דמוי תיבה, עשוי מקשה אחת ורתום בכל חלקיו. ללא קורות ועמודים.

רצפת המרחב המוגן הדירתי, קירותיו ותקרתו יהיו מסוריים (יצוקים בדיקטים בלבד).

קירות המרחבים המוגנים הדירתיים יהיו רציפים לכל גובה הבנין, ליצירת מגדל מוגן. יציבות המגדל המוגן של המרחבים המוגנים הדירתיים תובטח מפני כוחות אופקיים.

העוכי המזערי של חלקי המרחב המוגן הדירתי יהיה כאמור בתקניה 208.

הגנון שלד המרחב המוגן הדירתי ייעשה בהתאם לת"י 466.

מידות מזעריות של פתח אור - דלת כניסה - 60/200 ס"מ או 70/200 .

סוג דלת הכניסה - דלת הדף דירתית כמפורט בתקנה 202.

הגנה על דלת כניסה - כמפורט בתקנות (ע"י מהיצות ימרחקים מקירי בניין).

חלון - בשטח מירבי 1.21 מ"ר, גובה מפלס ארן לא יפחת מ-1.05 מ'
חלון ההדף הדירתי יכלול שני חלקים עיקריים:
א. חלון בטחוני פנימי אטום מפני גזים
ב. אלמנט מגן חיצוני להדף-תקן לפי תקנה 205 .

בטון

הבטון בכל חלקי המרחב המוגן הדירתי יהיה מסוג ב-300 לפי דרישות ת"י 118. החוזק האופייני ותנאי תוכן של הבטון השונות ייקבע לפי ת"י 466.

הכנת המרחב המוגן הדירתי לקשר, טלפון, טלויזיה וחשמל

באחד מקירות המרחב המוגן יותקן מוביל לצורך הכנה כבל טלפון, תיבת הסתעפות לטלפון ונקודת טלפון יותקנו בהתאם לדרישות חברת בזק.

במרחב מוגן יותקנו שני בתי-תקע, אחד לאנטנת טלויזיה ואחד לאנטנת רדיו. בבית התקע יותקן צינור שקוטרו לא יפחת מ-16 מ"מ, אשר יוביל אל מחוץ למרחב.

א. לצורך תאורה רגילה יותקנו לפחות שני גופי תאורה פלורסנטיים, כל אחד שתי מנורות של 36 ווט.
ב. לצורך תאורת חרום, תותקן מנורת חירום אחת לפחות של 36 ווט לפעולה של 4 שעות.
ג. יותקנו שני שקעי חשמל 220 וולט.
ד. יותקן שקע אחד לטלפון חוץ.
ה. תותקן נקודת טלויזיה אחת.

עבודות גימור

פני הדופן הפנימי של הקירות והתקרה של המרחב המוגן הדירתי יהיו חלקים עם גמר יציקת בטון ואין לסייח אותם.
הקירות והתקרה של המרחב המוגן יהיו בגימור צבע או ציפוי אקרילי בעובי שלא יעלה על 2 מ"מ.
קירות המרחב המוגן לא יצופו בצידם הפנימי באריחי חרסינה, באריחים מסוג אחר או בטיח.

את ריצפת המרחב המוגן יש לרצף באריחי ריצוף, מותר להשתמש בכל חומר ציפוי. שיפולים (פנלים) מותר שיהיו מחומר כגון: פי.וי.סי. , אולם אין להשתמש בחומרים כגון אריחי ריצוף, חרסינה, סיח וכיוצא באלה.

תכנית ריצפה

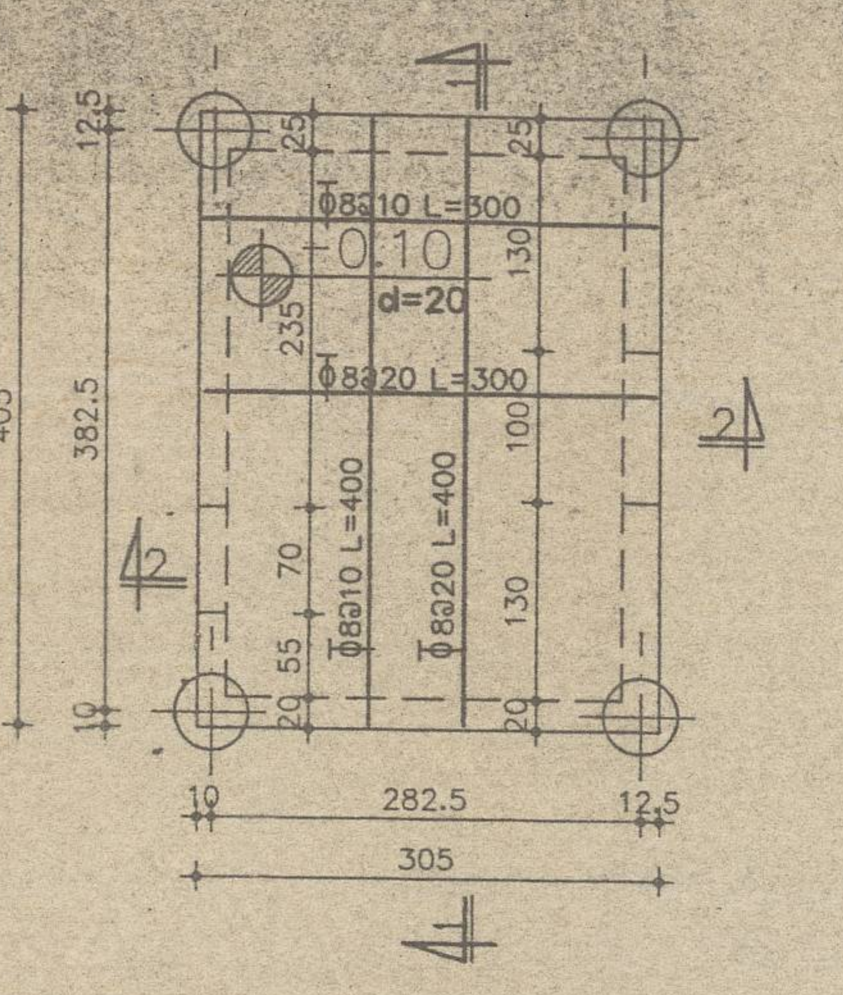

Φ8@10 L=300
+0.10
d=20
Φ8@20 L=300
Φ8@10 L=400
Φ8@20 L=400
405
382.5
12.5
10
25
235
130
100
70
55
20
282.5
305
1
2

תכנית תקרה

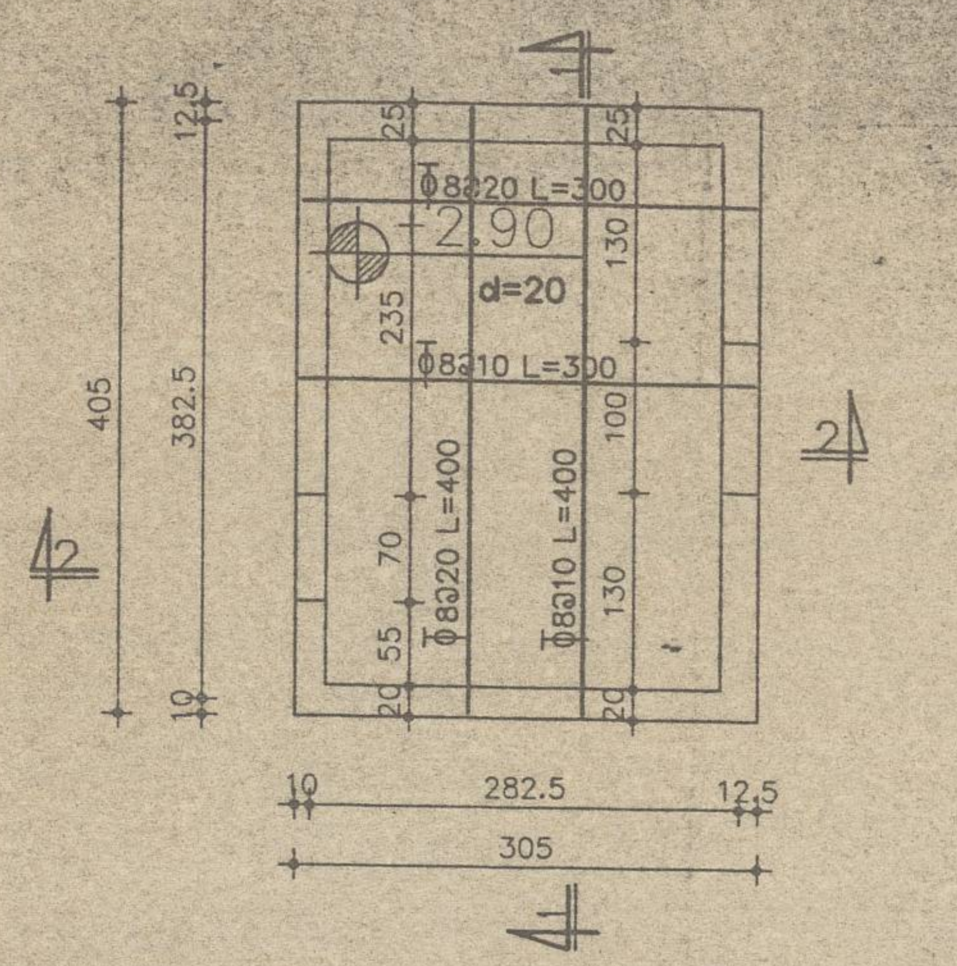

Φ8@20 L=300
+2.90
d=20
Φ8@10 L=300
Φ8@20 L=400
Φ8@10 L=400
405
382.5
12.5
10
25
235
130
100
70
55
20
282.5
305
1
2

חתך 2-2

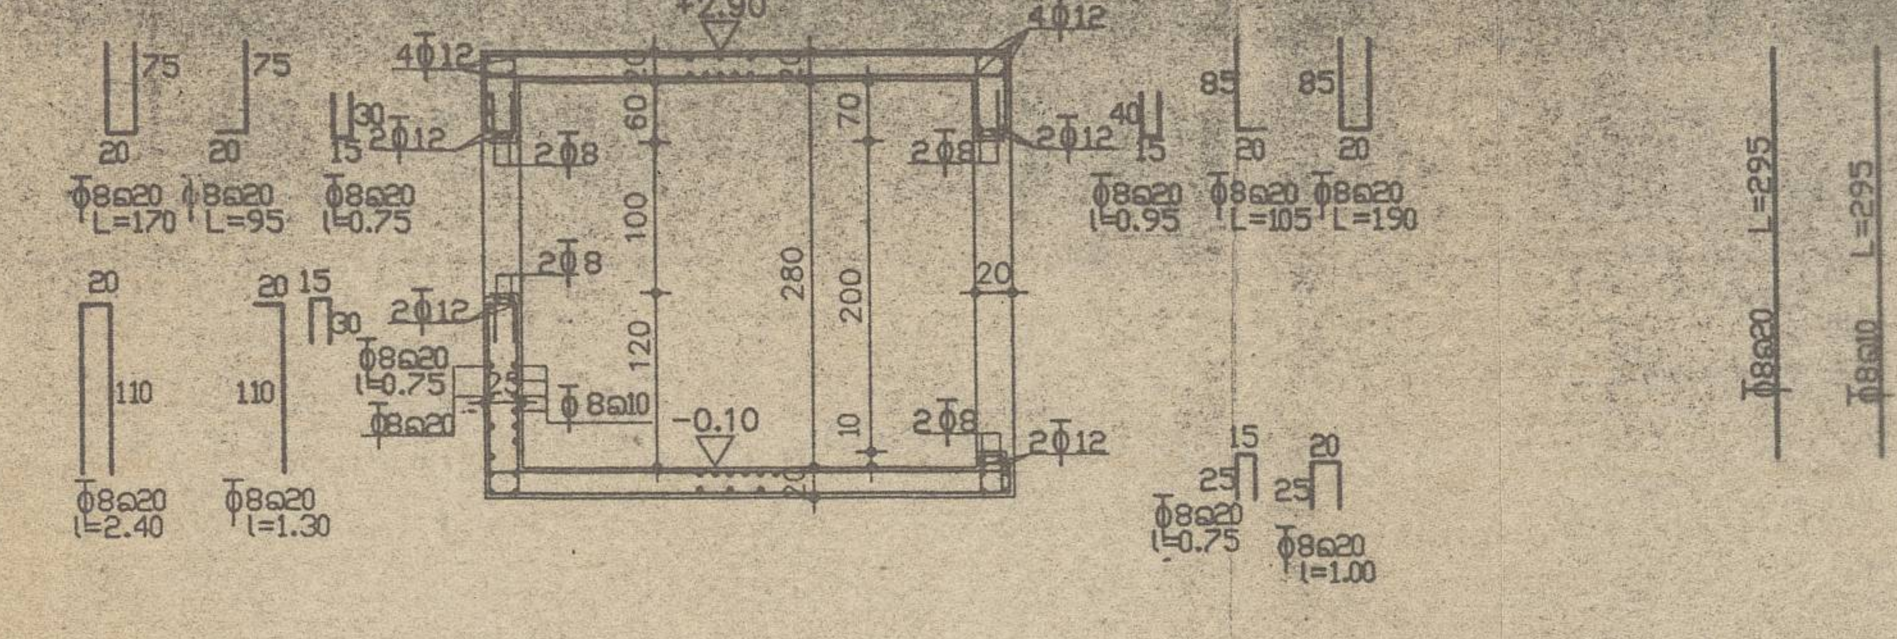

+2.90
-0.10
4Φ12
2Φ12
2Φ8
Φ8@10
Φ8@20 L=170
Φ8@20 L=95
Φ8@20 l=0.75
Φ8@20 l=0.95
Φ8@20 L=105
Φ8@20 L=190
Φ8@20 l=2.40
Φ8@20 l=1.30
Φ8@20 l=0.75
Φ8@20 l=1.00
Φ8@20 L=295
Φ8@10 L=295
280
200
100
120
60
70
10

חתך 1-1

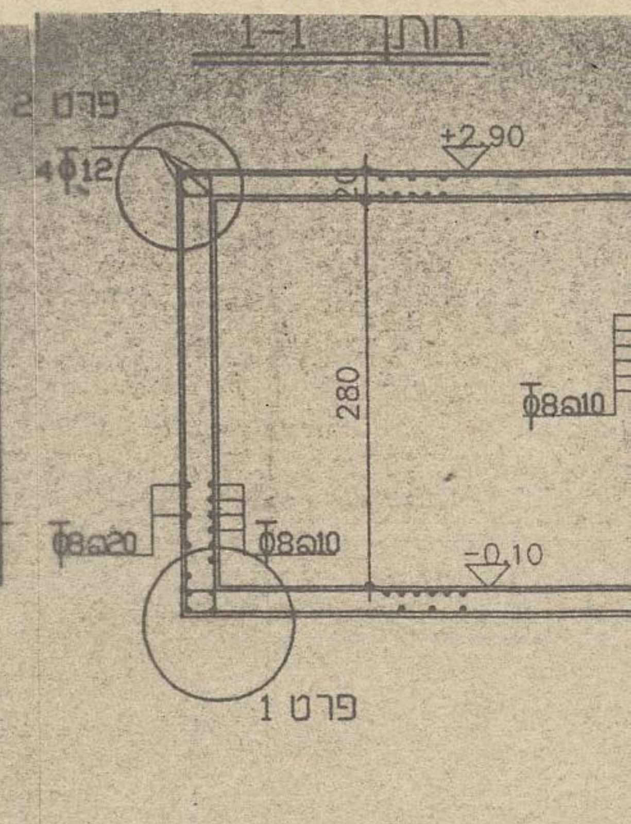

פרט 2
פרט 1
4Φ12
+2.90
-0.10
280
Φ8@20
Φ8@10

פרט 2
פרט ריתום אנכי בין קירות לגג

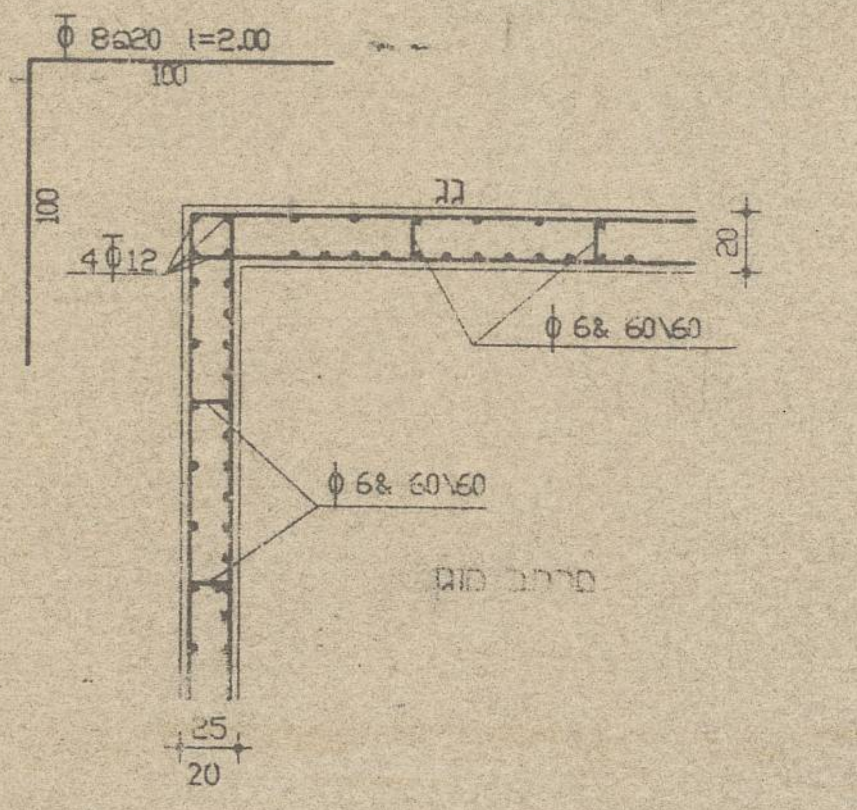

Φ 8@20 l=2.00
100
גג
4Φ12
Φ 6& 60\60
20
25
מרחב מוגן

פרט 3
פרט ריתום אופקי בקירות

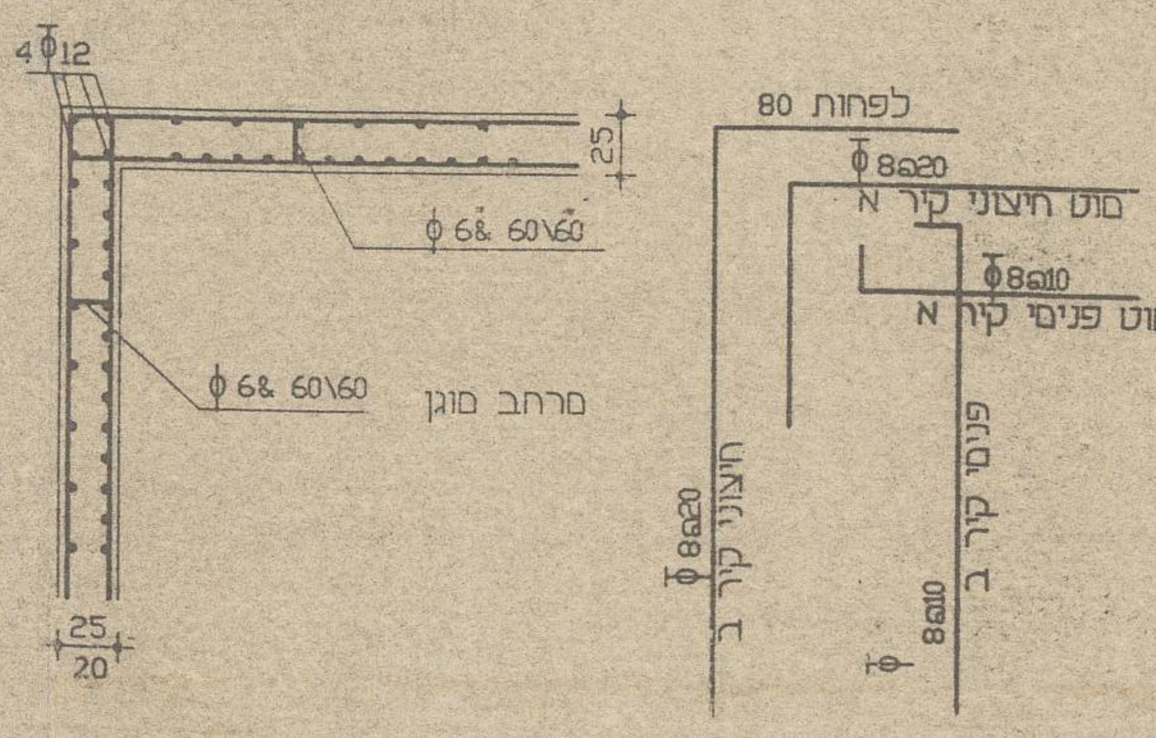

4Φ12
25
Φ 6& 60\60
מרחב מוגן
20
לפחות 80
Φ8@20
מוט חיצוני קיר א
Φ8@10
מוט פנימי קיר א
חיצוני קיר ב
פנימי קיר ב

פרט 1
פרט ריתום אנכי בין רצפה לקירות

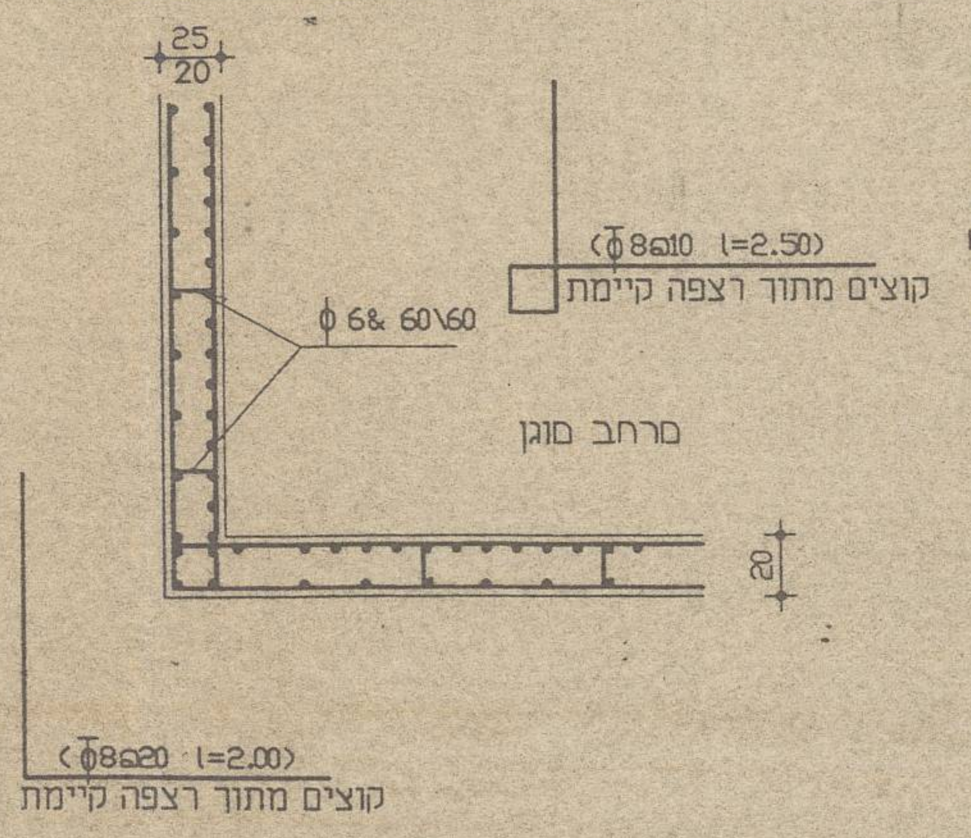

25
20
Φ 6& 60\60
(Φ8@10 l=2.50)
קוצים מתוך רצפה קיימת
מרחב מוגן
20
(Φ8@20 l=2.00)
קוצים מתוך רצפה קיימת

פרט פתח לדלת

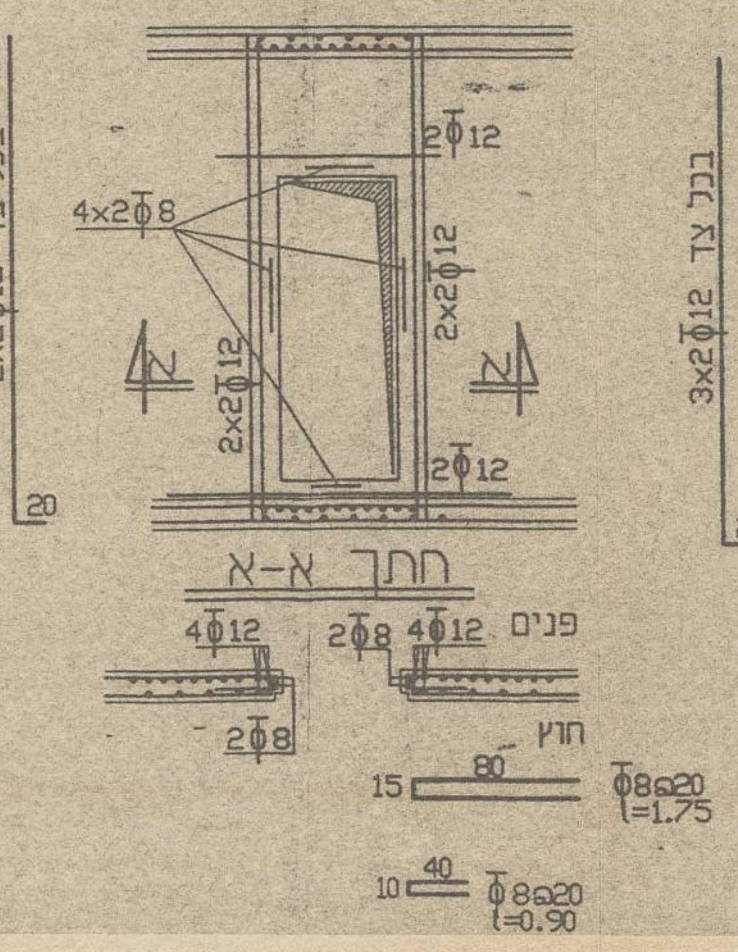

בכל צד 2x2Φ12
4x2Φ8
2Φ12
2x2Φ12
20
א
חתך א-א
4Φ12
2Φ8
פנים
חוץ
15
80
Φ8@20 l=1.75
10
40
Φ8@20 l=0.90

פרט פתח חלון

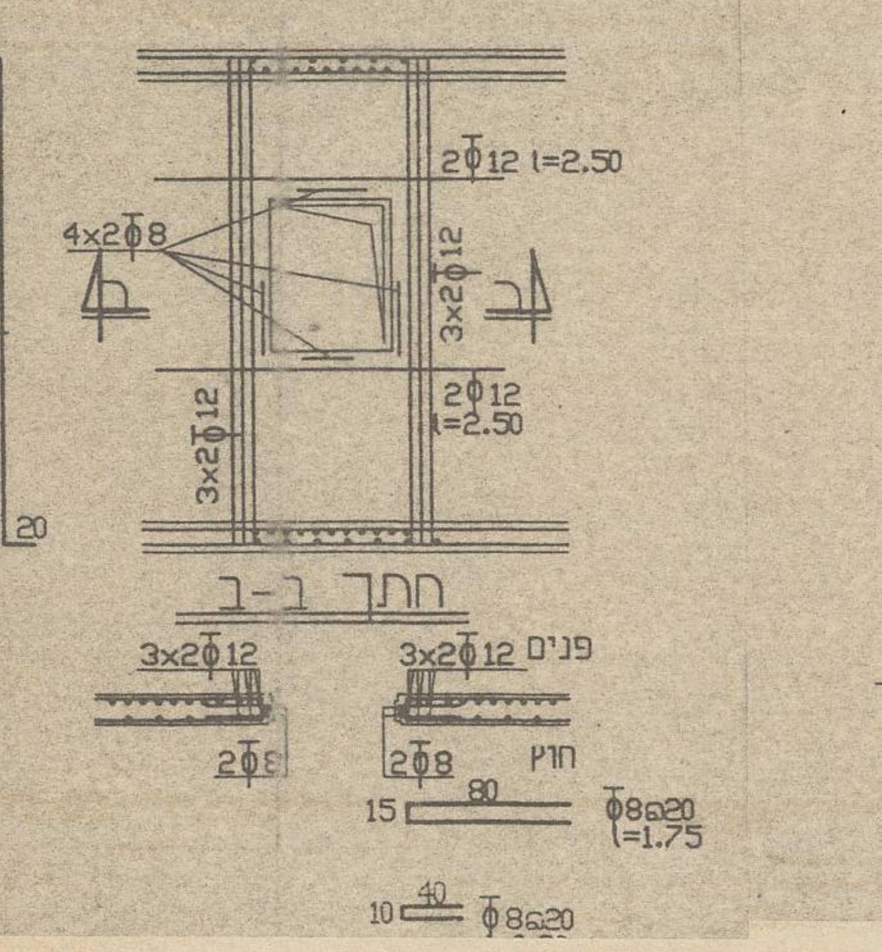

בכל צד 3x2Φ12
4x2Φ8
2Φ12 l=2.50
3x2Φ12
2Φ12 l=2.50
20
ב
חתך ב-ב
3x2Φ12
פנים
2Φ8
חוץ
15
80
Φ8@20 l=1.75
10
40
Φ8@20