

תל-אביב-יפו

גוש 6135

חלקה 43 (חלק)

שטח מדוד 160 מ"ר

שטח לפי נסח 125 מ"ר

רחוב וילון 27

26



מפה טופוגרפית


1:100

הוכן עבור: זכריה דנון
מהות הבקשה: קבלת היתר בניה

7-94-685

איתור נמוך

תרשים הסביבה-1:1250

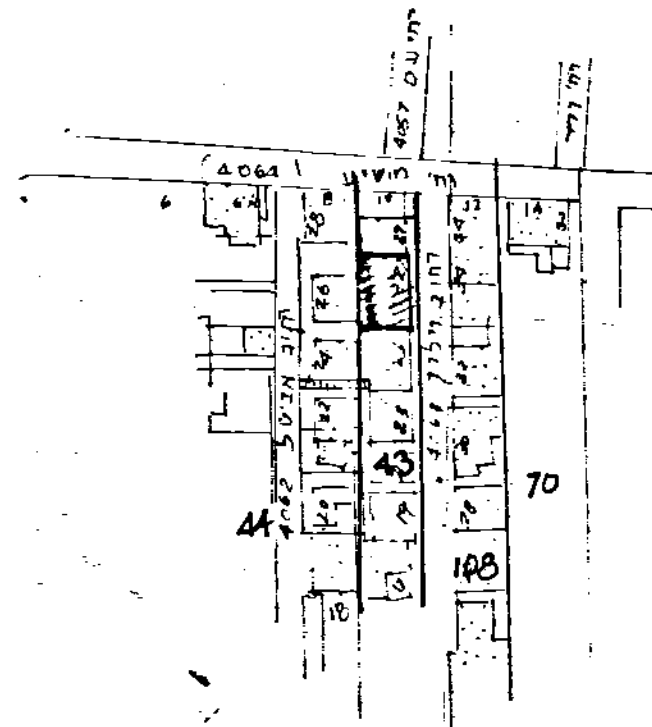


אני מאשר/ברכה שמכה נעשתה לפי חוק תכנון והבניה
הוראות וההנחיות של עיריית תל-אביב-יפו

נסדק

הערות:
1. הגבהים מבוססים על גובה נ.ק. 17530.80
2. מספרים בסוגריים מסמנים גובה ים

28.06.95

סוף מסמך

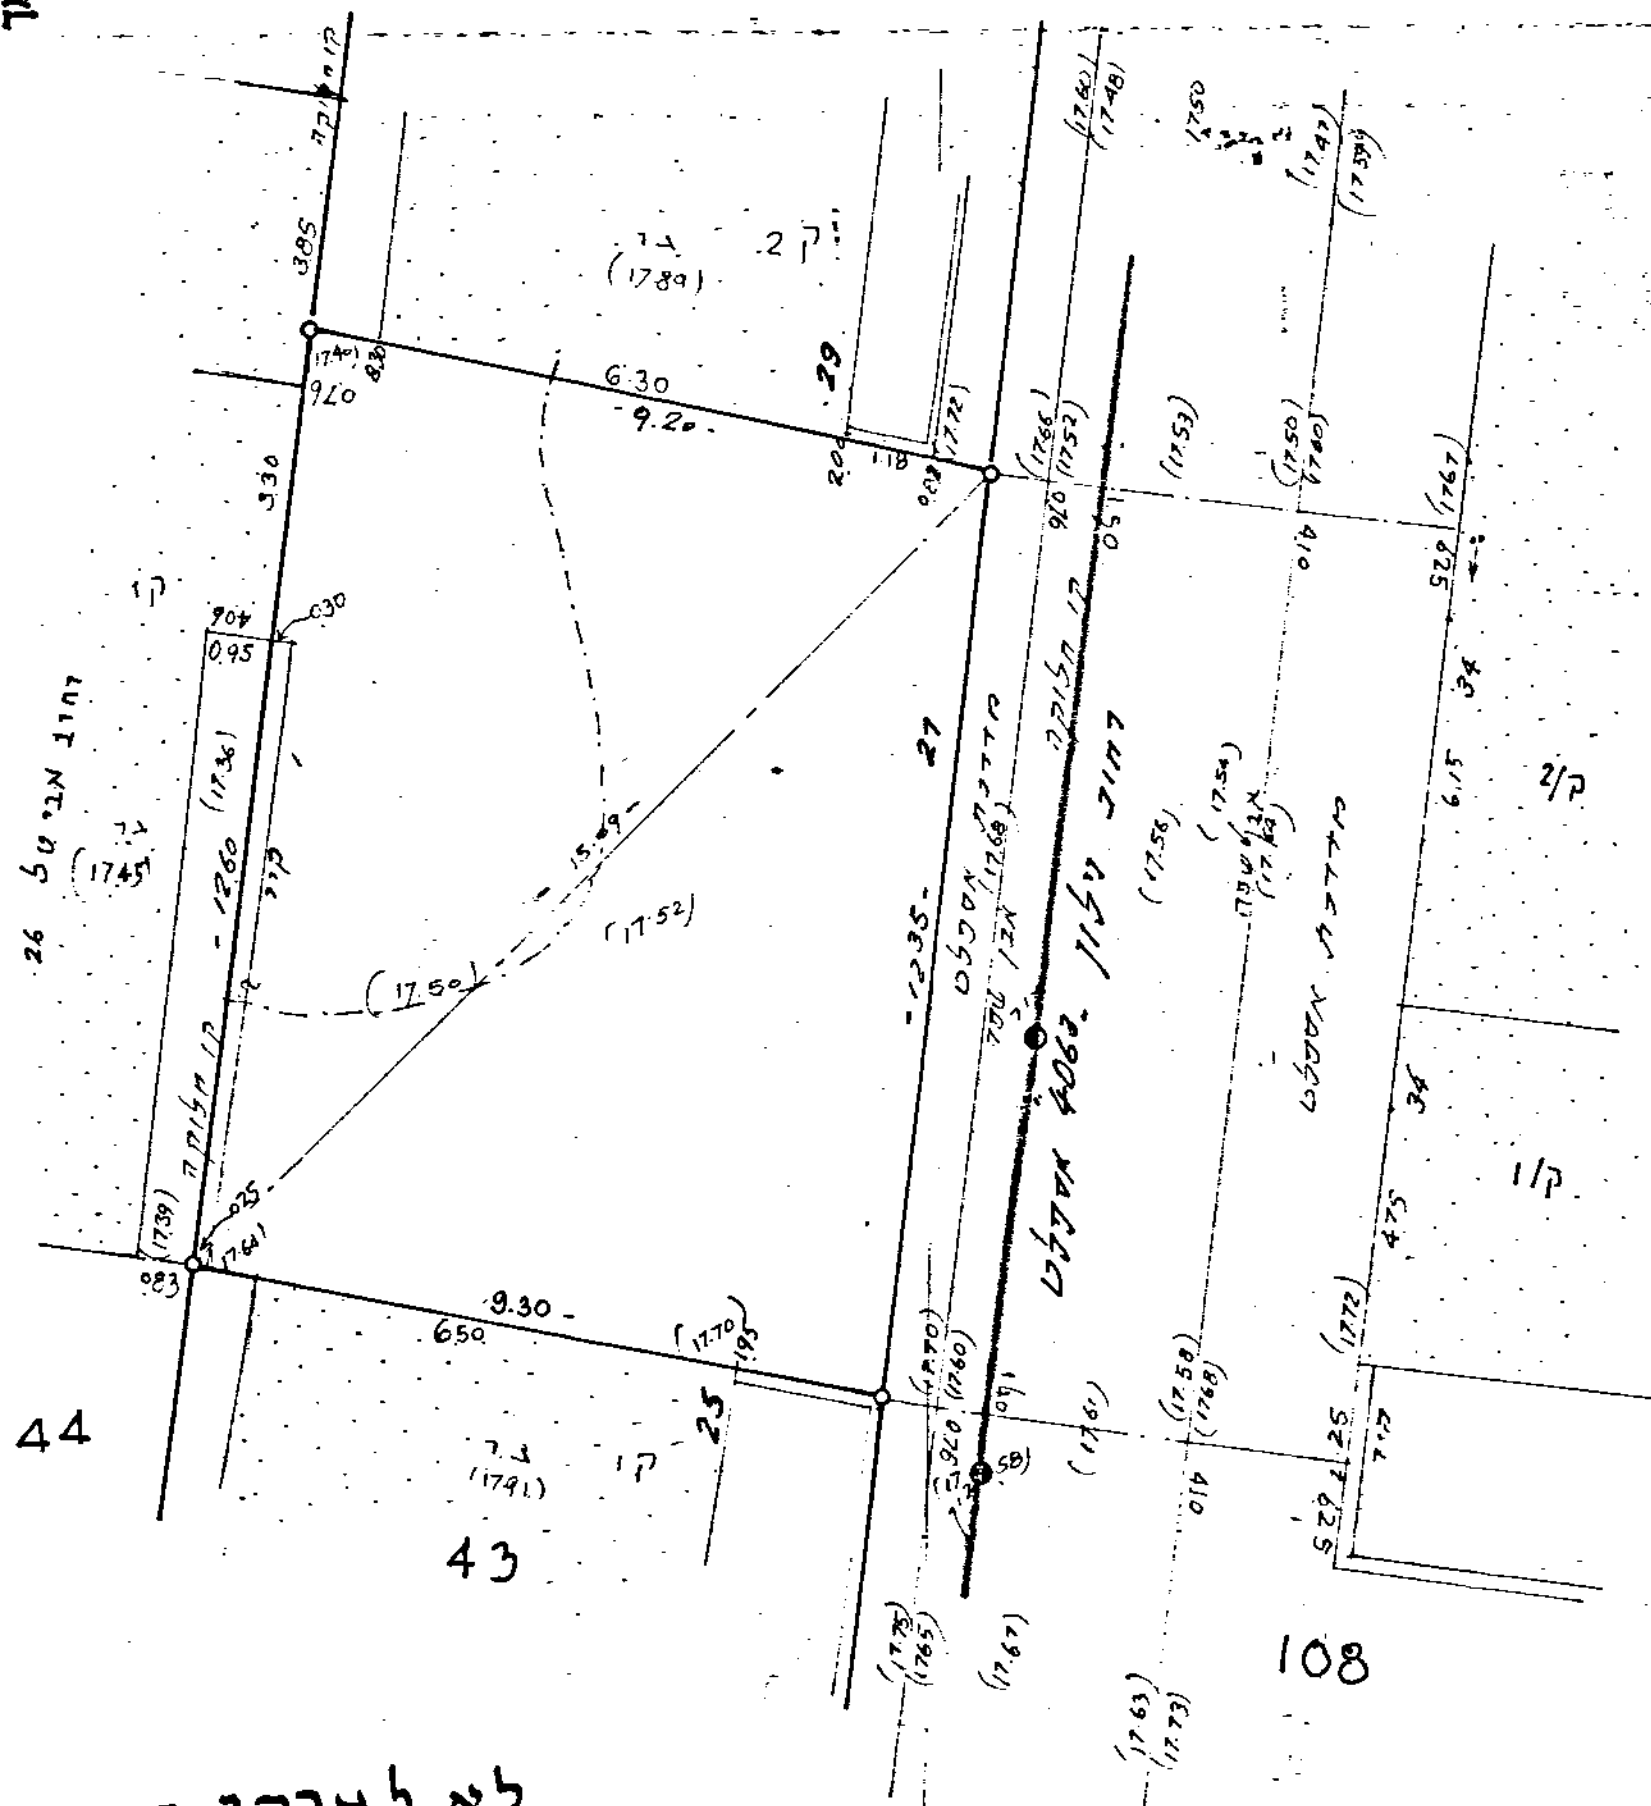

לא לערכי רישום

תל-אביב-יפו
23.06.1995
משרד סכני למדידות
תכנון ופקוח בע"מ
רח' דבטינסקי 162, תל-אביב
טל. 6957234-3