

תל-אביב-יפו

גוש 6135

חלקה 43 (חלק)

שטח מדוד 116 מ"ר

שטח לפי נסח 125 מ"ר

רחוב וילון 27

הוכן עבור: זכריה דנון
מהות הבקשה קבלת היתר בניה


794-685

26



איכות נמוכה

תרשים הסביבה-1250:

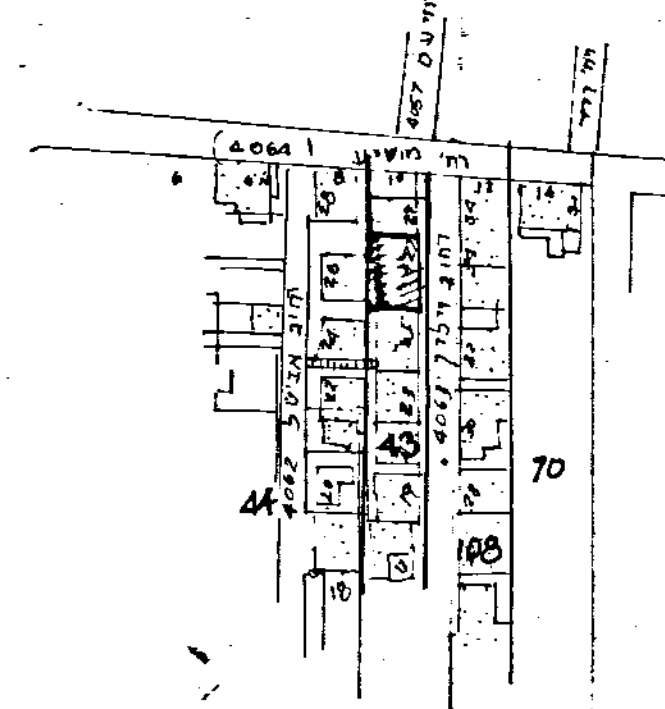

אצי מאשר בנה שמפה נעשתה לפי חוק תכנון ועבניה
הוראות והנחיות של עיריית תל-אביב-יפו


נסדק

28.90.92

הערות:
1. הגבהים מבוססים על גובה נ.ק. 17530
2. מספרים בסוגריים מסמנים גובהים

מפה טופוגרפית

1:100

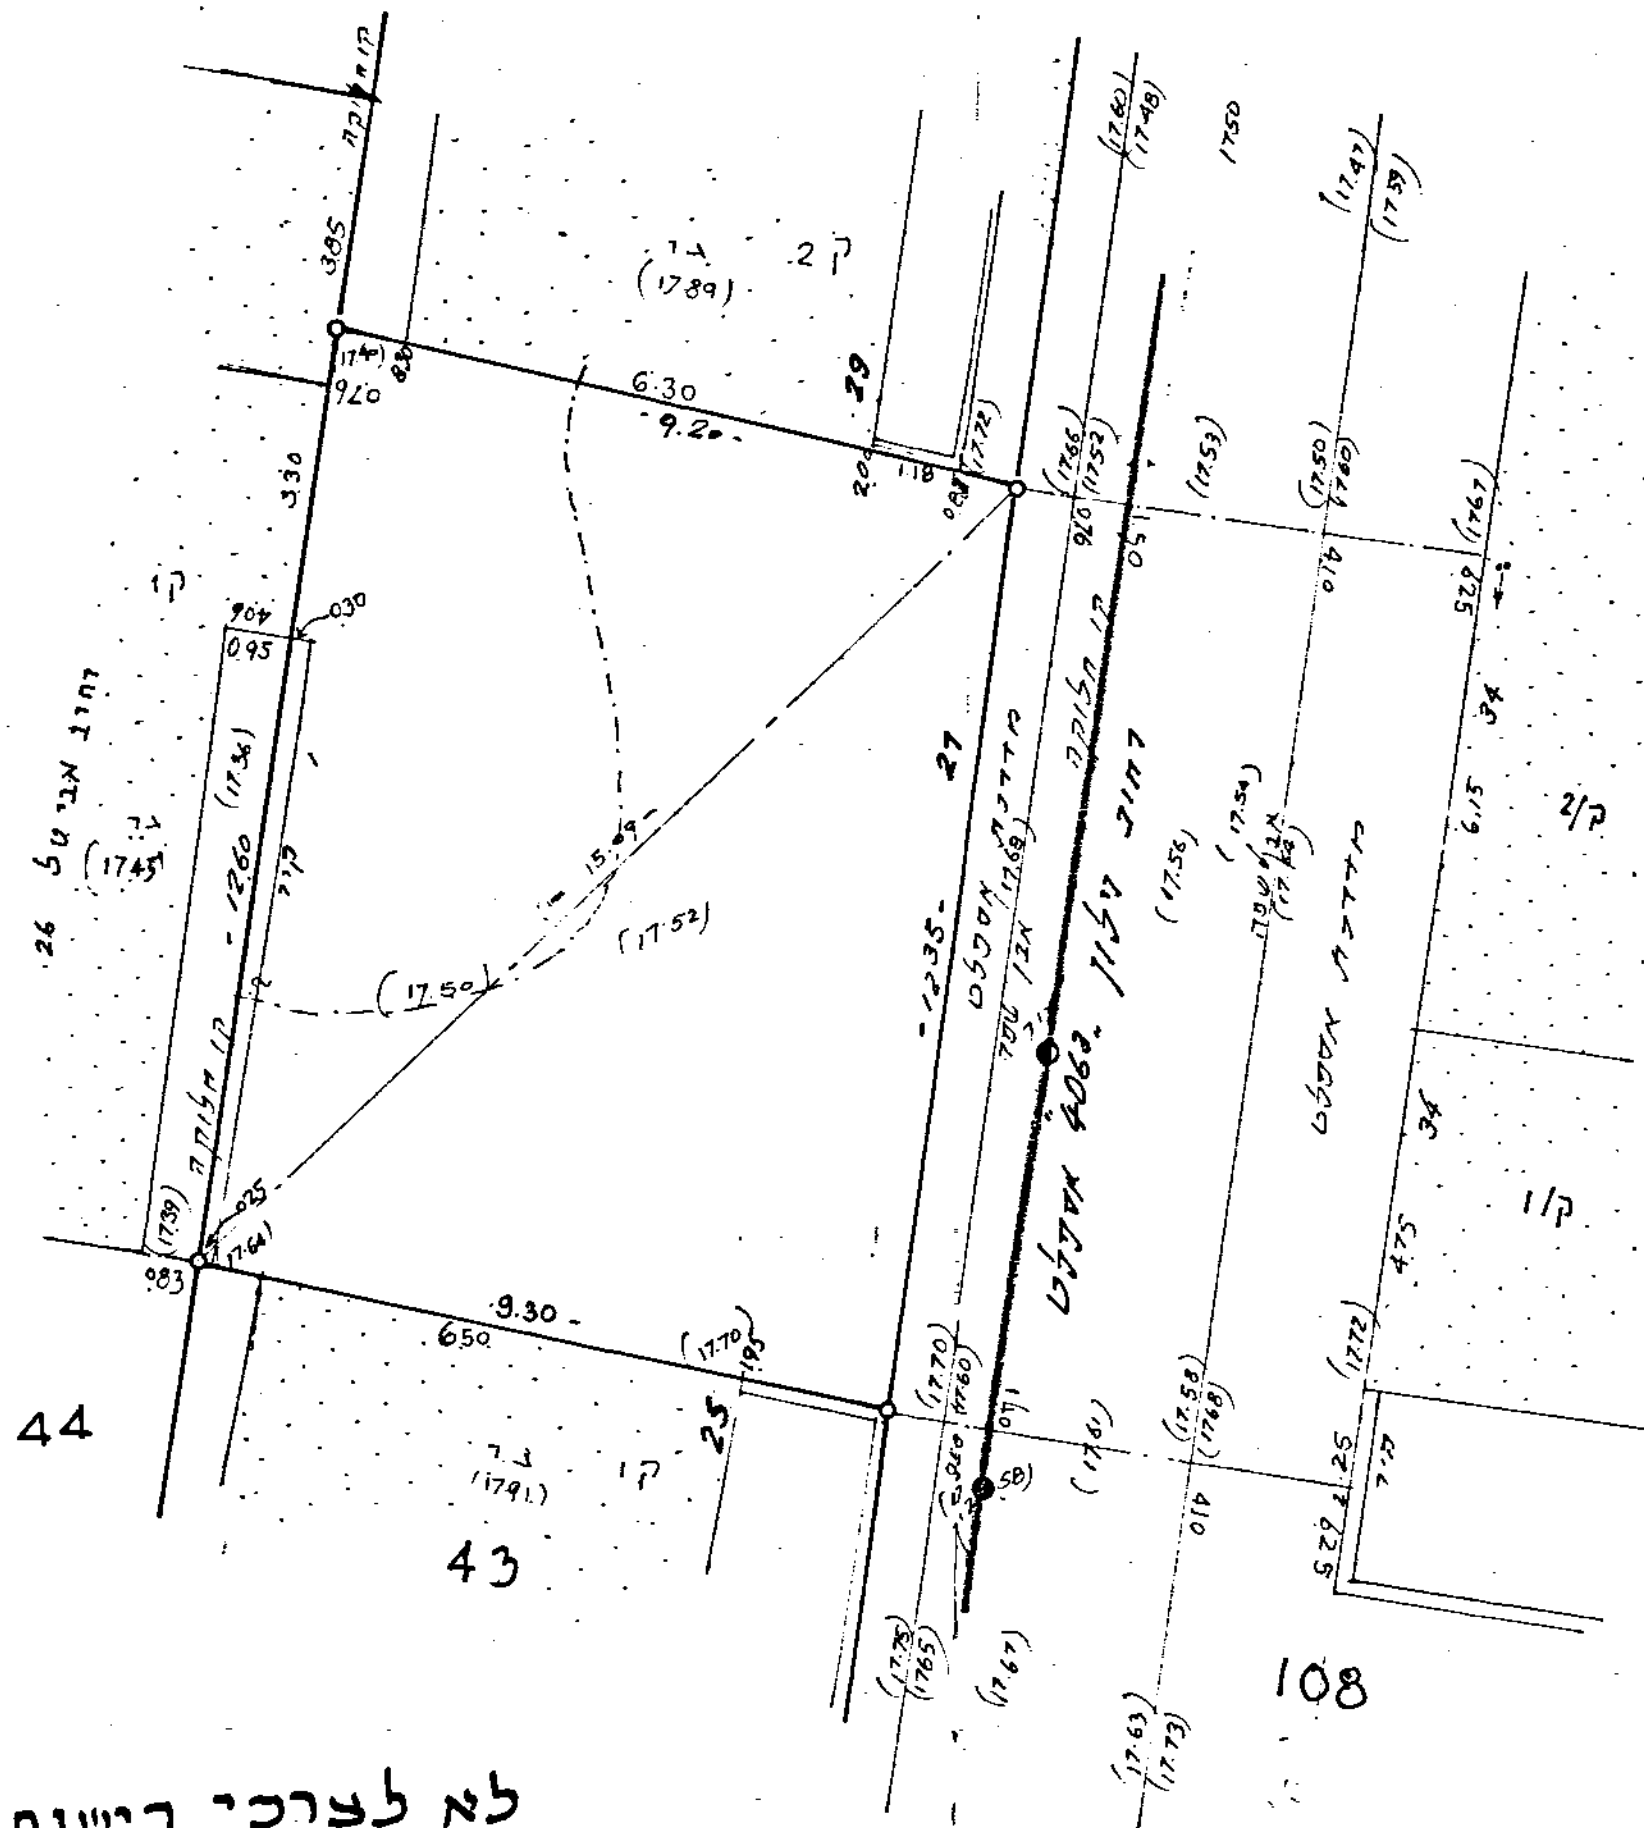

לא לצרכי רישום

סידר חוסהד
דליון 278

תל-אביב
23.06.1995

לאון כהנא
משרד סכני למדידות
תכנון ופקוח בע"מ
רח' דיבונסקי 152, תל-אביב
טל. 03-6957234