

נפרד

26




איכות נמוכה

תל-אביב-יפו
גוש 6135
חלקה 43 (חלק)
שטח מדוד 116 מ"ר
שטח למינסח 125 מ"ר
רחוב וילון 27

הוכן עבור: זכריה דנון
מהות הבקשה קבלת היתר בניה
794-685

תרשים הסביבה-1:1250

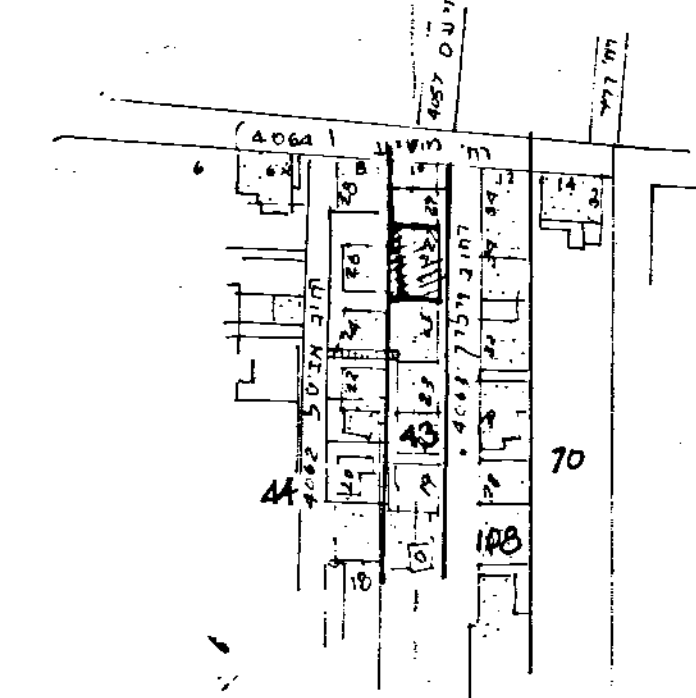


אצי מאשר ברה שפכה נעשתה לפי חוק תכנון והבניה
הוראות והנחיות של עיריית תל-אביב-יפו

- הגבהים מבוססים על גובה נ.ק. 108 = 17.330
- המספרים בסוגריים מסמנים גבהים

הערות:

28.05.95

מפה טופוגרפית
1:100

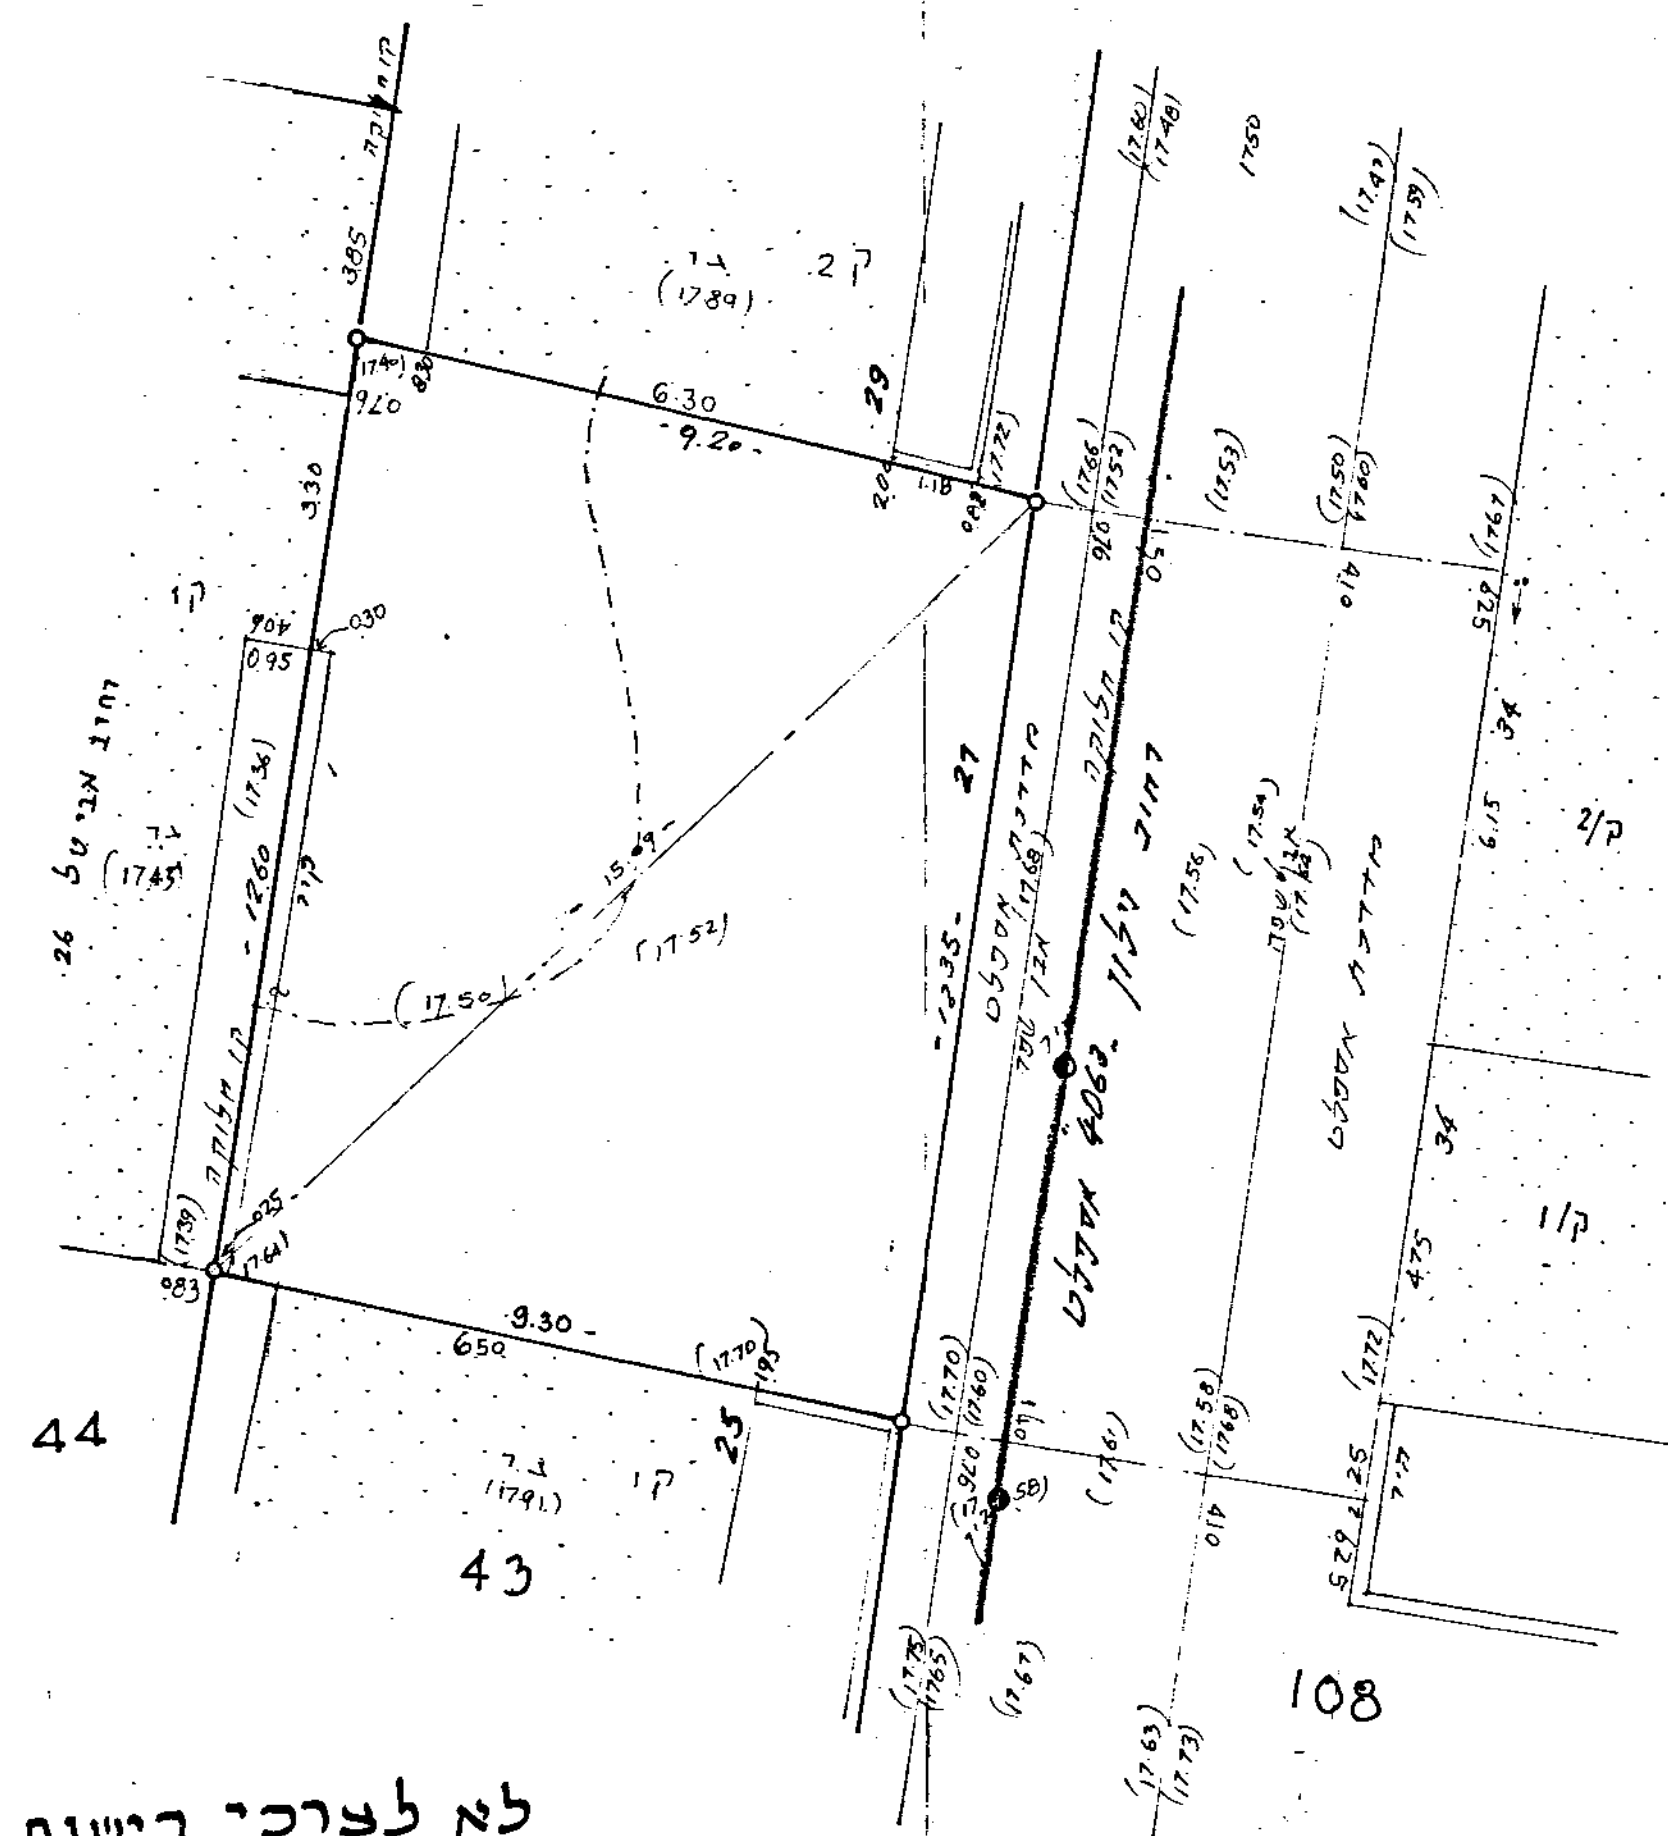

לא לצרכי רישום

תל-אביב
1995-06-23
ד"ר חסיד
278
ד"ר חסיד
278
ד"ר חסיד
278

לאון כהנא
משרד טכני למדידות
תכנון ופקוח בע"מ
רח' דובווינסקי 162, תל-אביב
טל. 03-6957234

למסמ יוא