


למסמך

מצה טופוגרפית
1:100

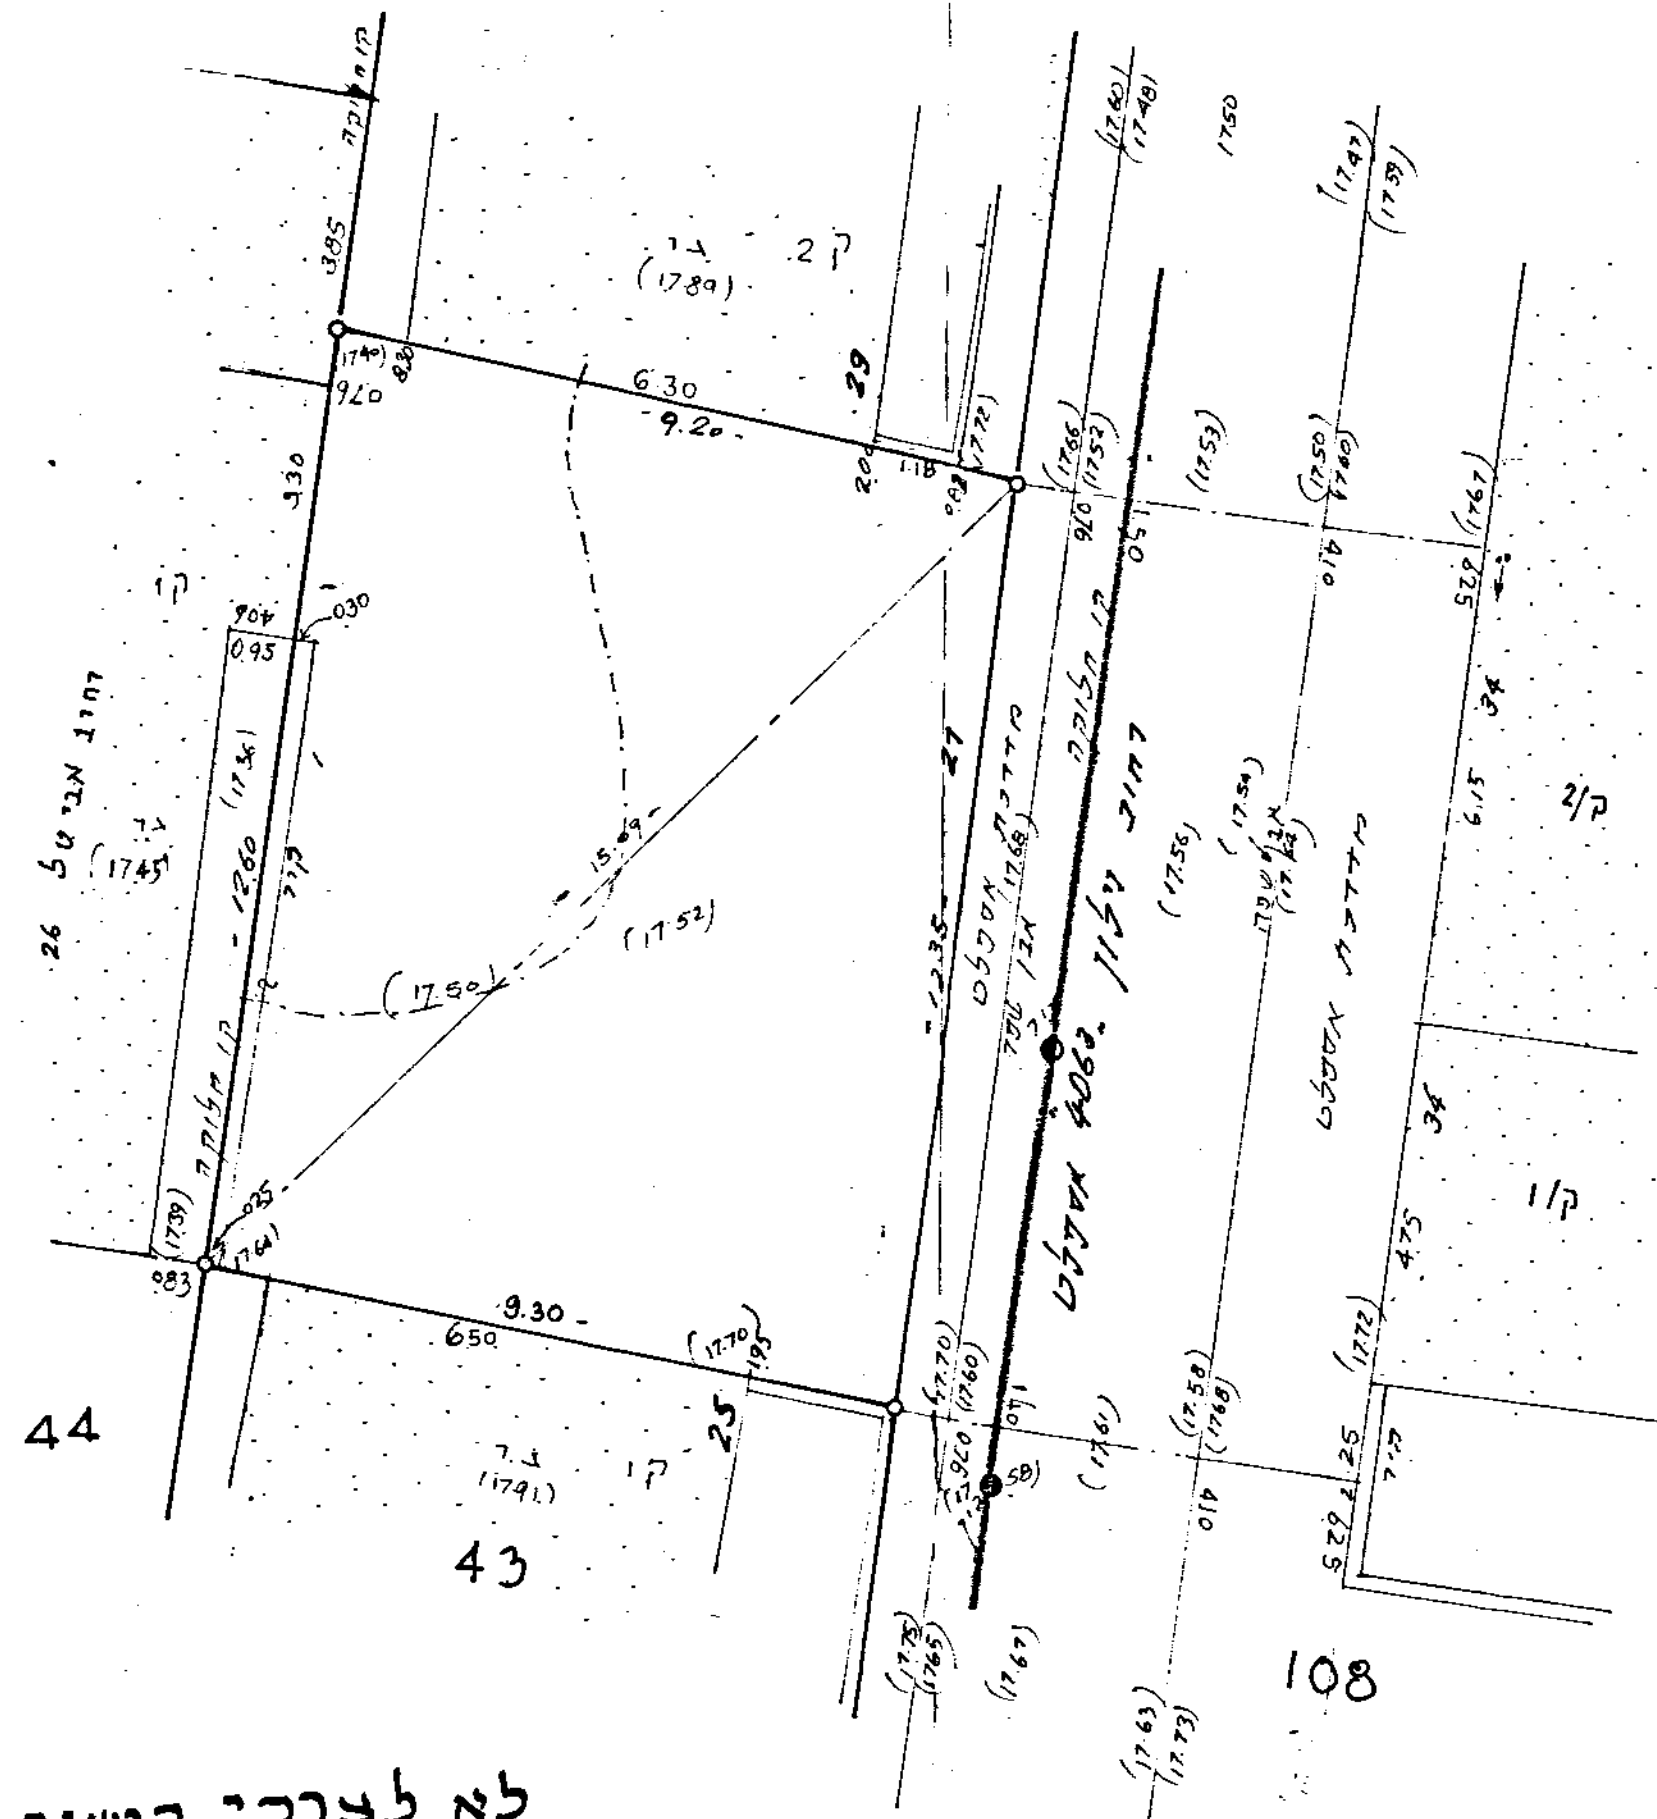

לא לצרכי רישום


תל-אביב
23.06.1995
סוידר חוסמד
דשיון 278
ל. נ. נ. נ.

לאון כהנא
משרד טכני למדידות
תכנון ופקוח בע"מ
רח' ז'בוטינסקי 182, תל-אביב
טל. 03-6957234

תל-אביב - יפו
גוש 6135
חלקה 43 (חלק)
שטח מדוד 116 מ"ר
שטח לפי נסח 125 מ"ר
רחוב וילון 27

הוכן עבור : זכריה דנון
מהות הבקשה קבלת היתר בניה
7-94-685

תרשים הטביבה 1:125

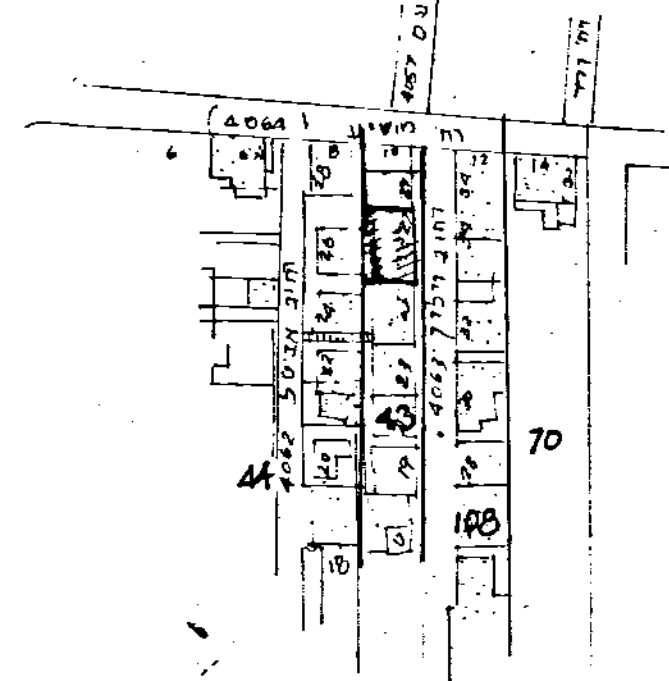

אבי מאשר בנה שחפה נעשתה לפי חוק תכנון והבניה
הוראות והנחיות של עיריית תל-אביב - יפו

נסדק

הערות:
1. הגבהים מבוססים על גובה נ.ק. 108 = 17.530
2. מספרים בסוגריים מסמנים גבהים

28.06.95