

תל-אביב-יפו

גוש 6135

חלקה 43 (חלק)

שטח מדוד 116 מ"ר

שטח לפי נסח 125 מ"ר

רחוב וילון 27


הוכן עבור : זכריה דנון
מהות הבקשה קבלת היתר בניה

794.685




איכות נמוכה

תרשים הסביבה-1:1250

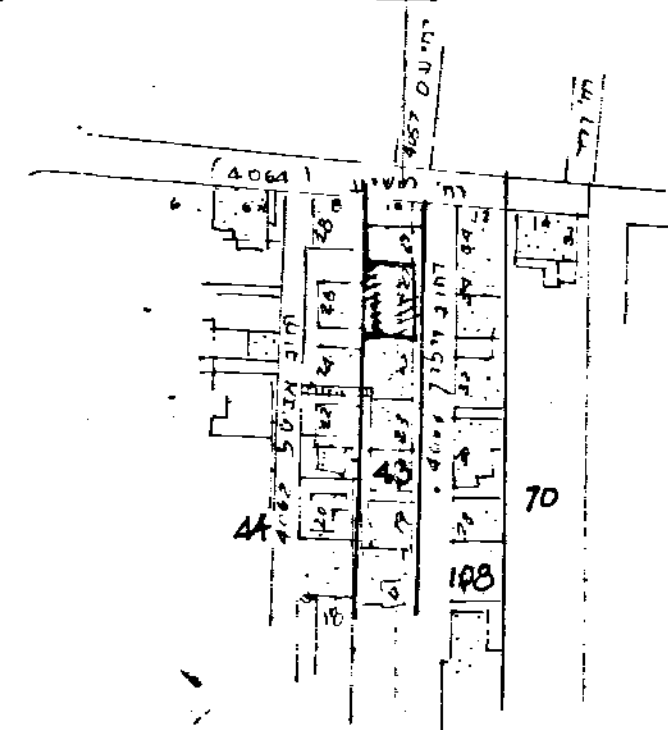

אצי מאשר ברה שחפה נעשתה לצד חוק תכנון והבניה
הוראות והנחיות של עיריית תל-אביב-יפו

מפה טופוגרפית
1:100

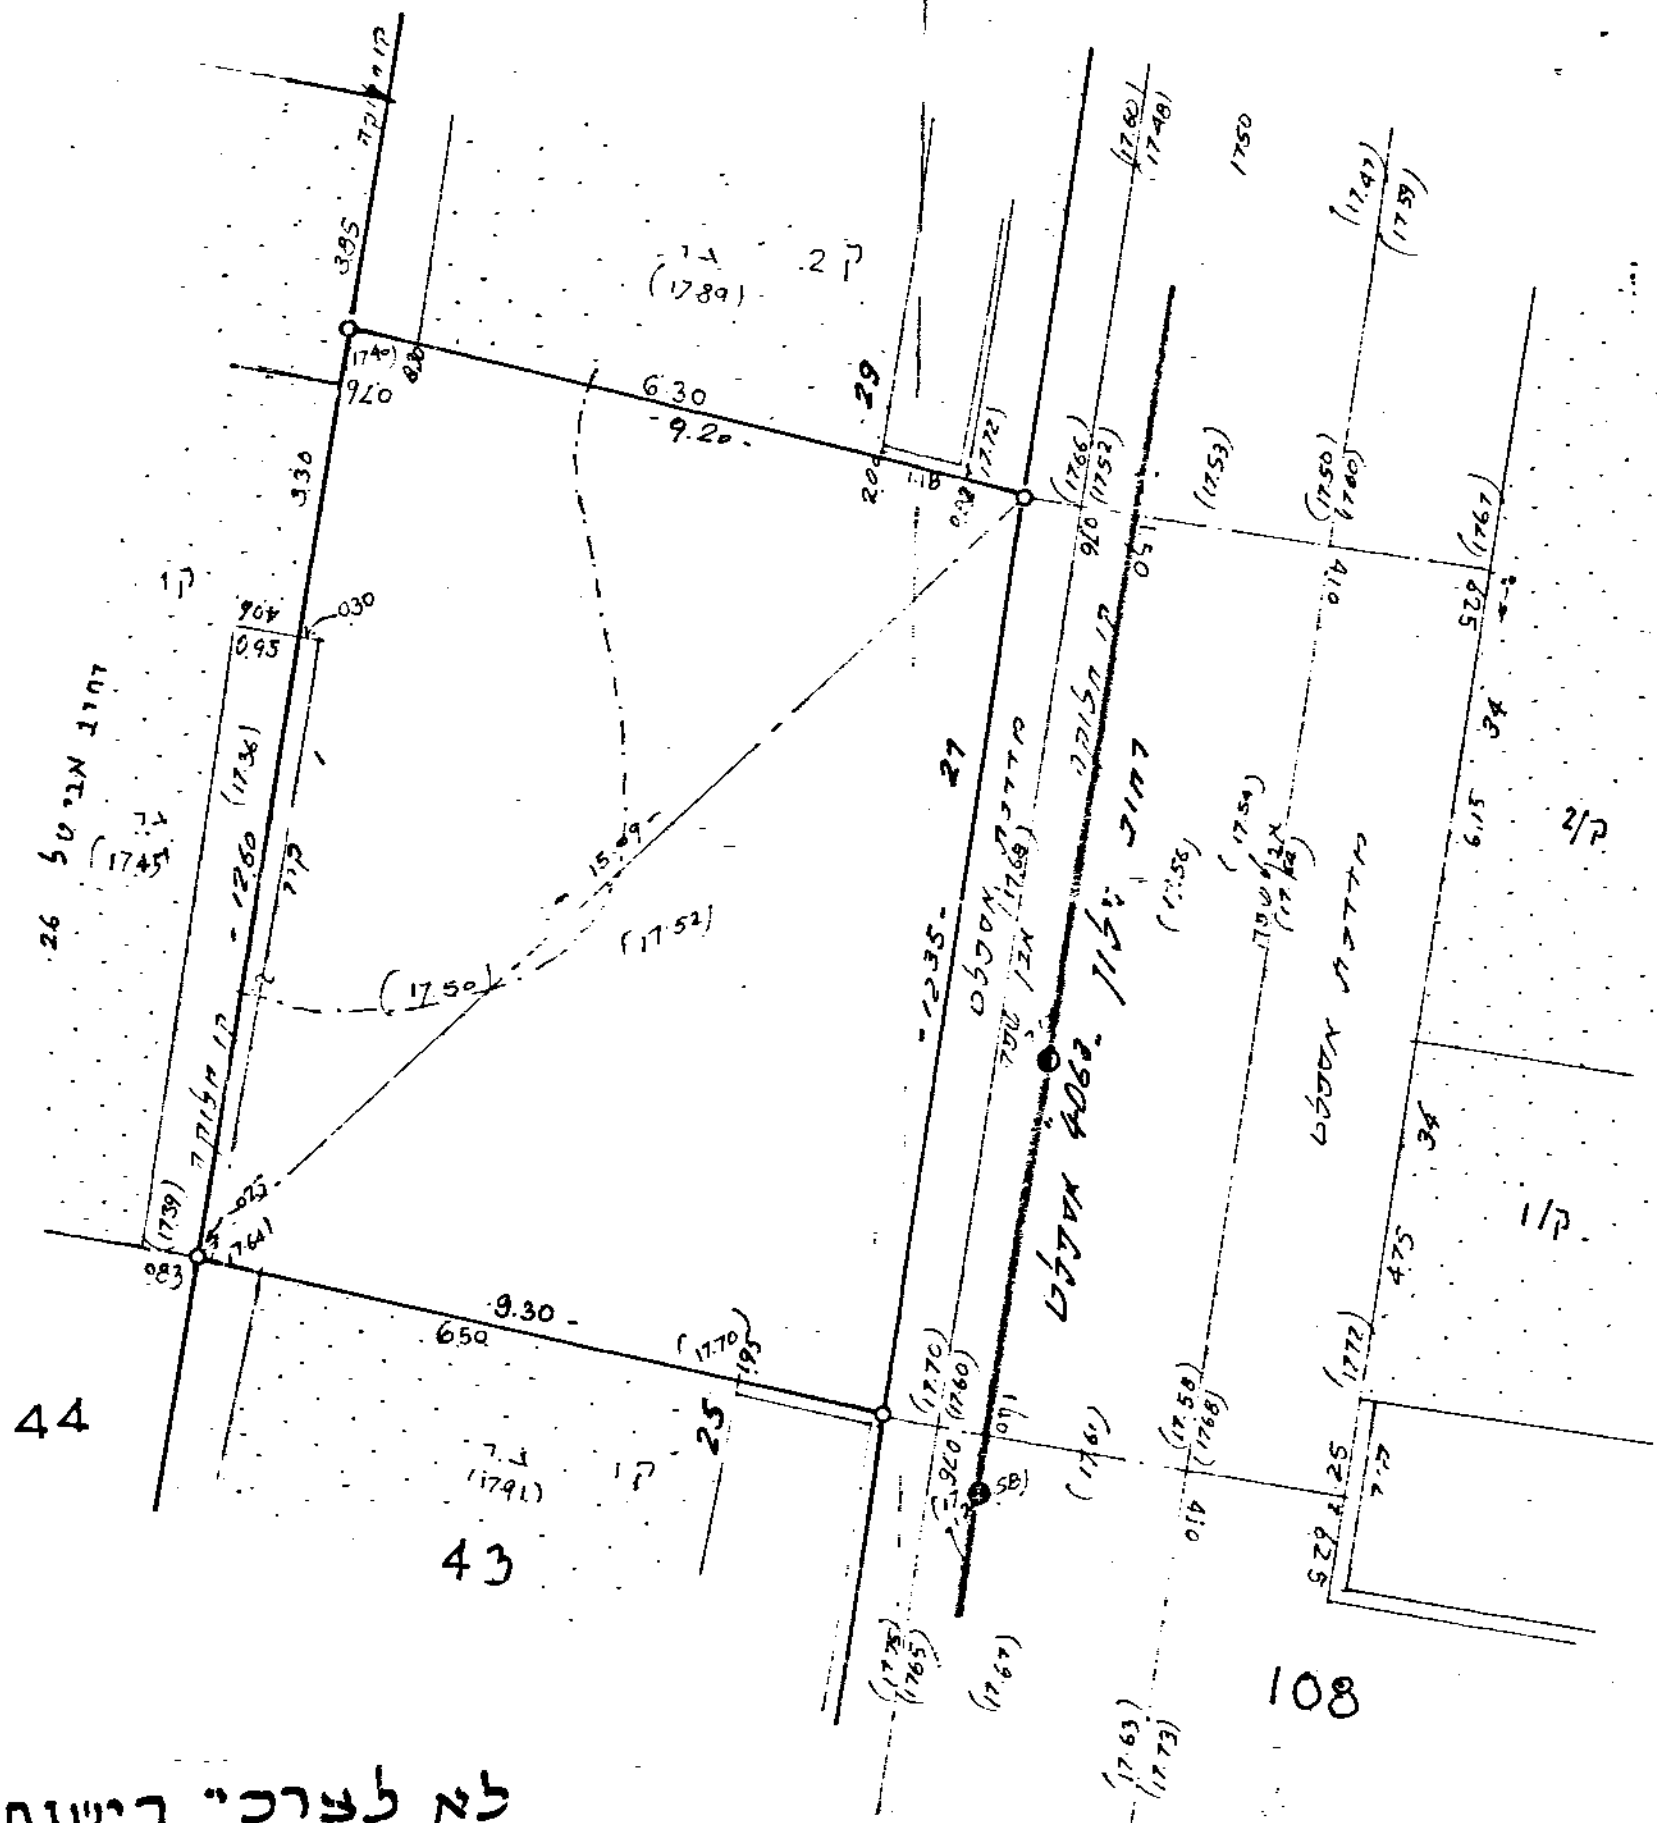

לא לצרכי רישום

תל-אביב
23.06.1995

לאון כהנא
משרד סגני למדיניות
הכנת ופקוח בע"מ
רח' רובינסקי 182, תל-אביב
טל. 03-6957434

הערות:
1. הגבהים מבוססים על גובה נ.ק. 17530 = 180
2. מספרים בסוגריים מסמנים גובהים