


1:50 מ'ק

2 חדרים וח"מ

תפנית ב"ת

למלך חירום סינואצי  
רחוב ספר מש' 10 פינת רח' סג

למלך חירום סינואצי  
רחוב ספר מש' 10 פינת רח' סג

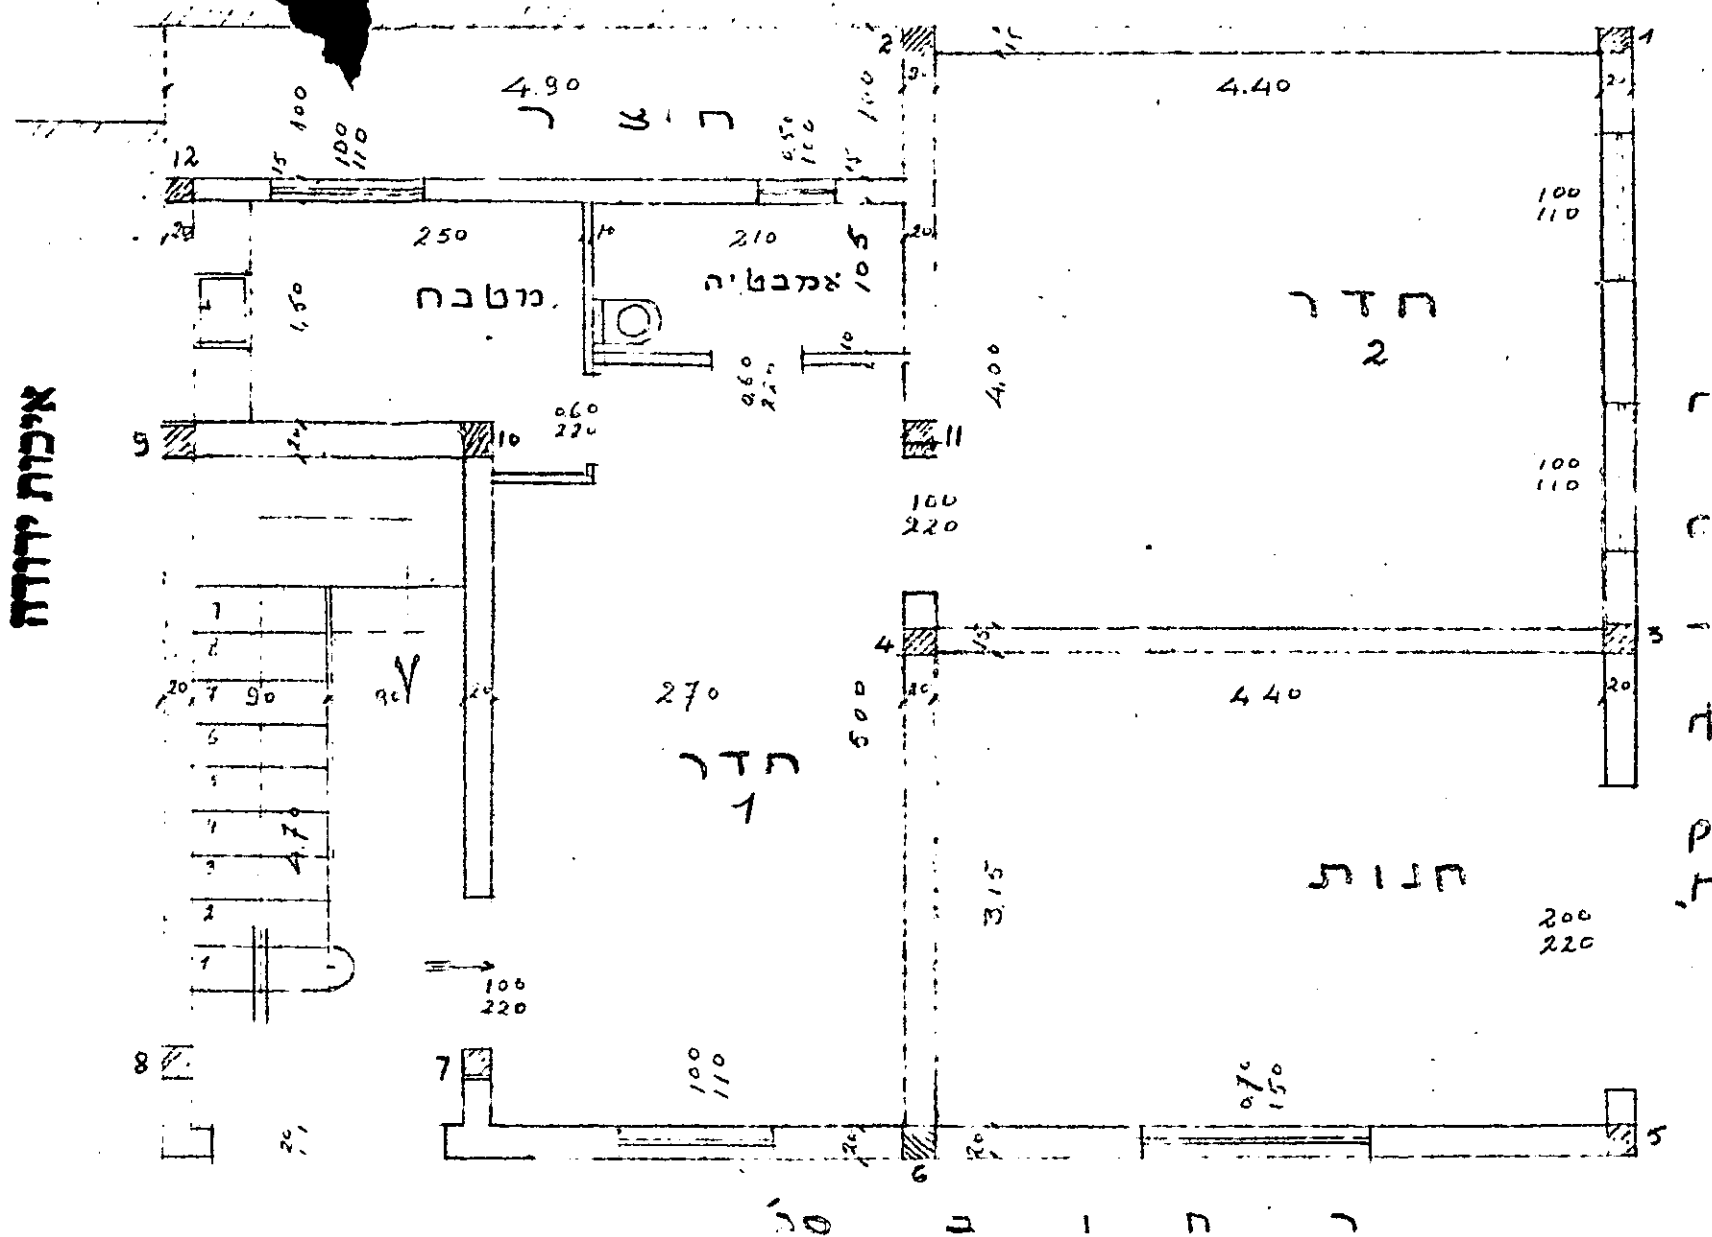

| T 175 |       |    |  |
|-------|-------|----|--|
| 6/12  | 20/30 | 1  |  |
| 6/12  | 20/30 | 2  |  |
| 6/12  | 20/40 | 3  |  |
| 6/12  | 20/40 | 4  |  |
| 4/12  | 20/30 | 5  |  |
| 4/12  | 20/30 | 6  |  |
| 6/12  | 22/35 | 7  |  |
| 6/12  | 22/35 | 8  |  |
| 6/12  | 22/35 | 9  |  |
| 4/12  | 22/35 | 10 |  |
| 4/12  | 20/30 | 11 |  |
| 4/12  | 15/30 | 12 |  |

התאחדות העובדים