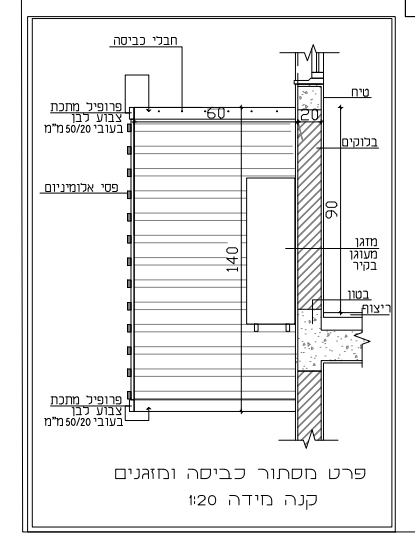

חבלי כביסה
פרופיל מתכת
בלוקים
סבכת אלומיניום
140

פרט מסתור כביסה ומזגנים
קנה מידה 1:20

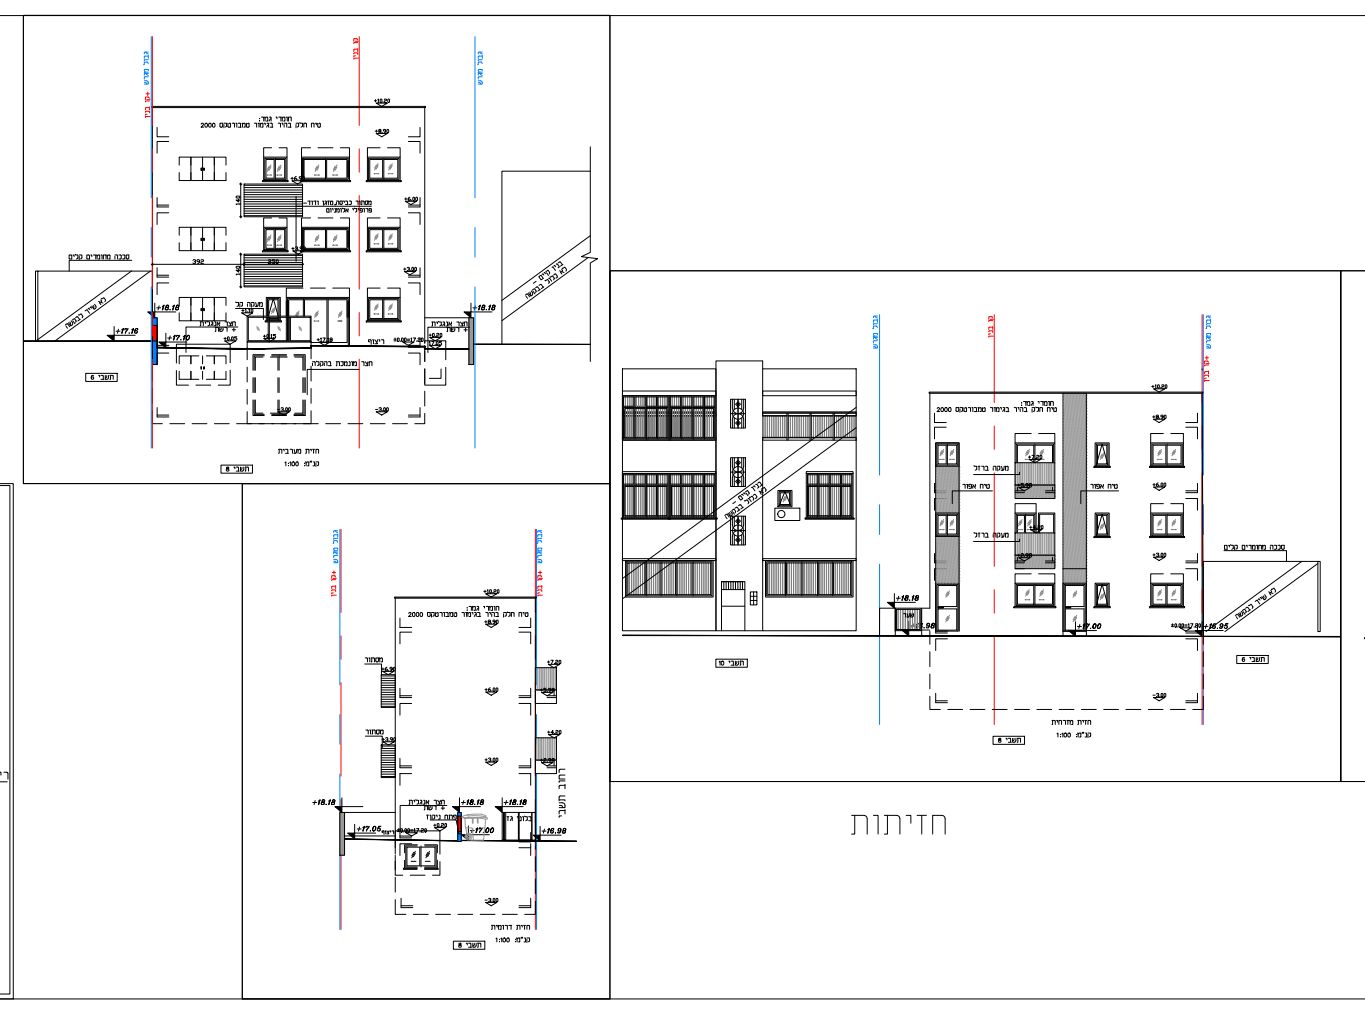

חזיתות

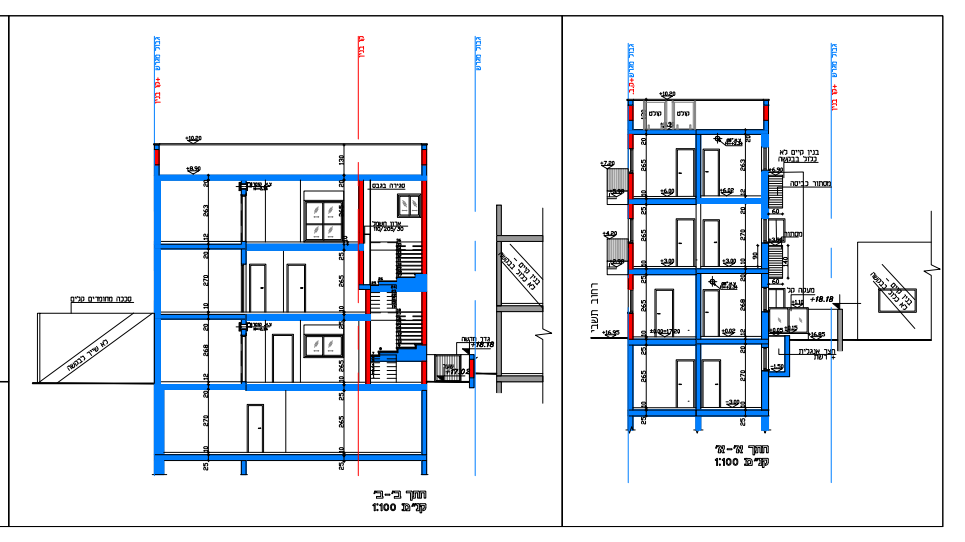

חתכים

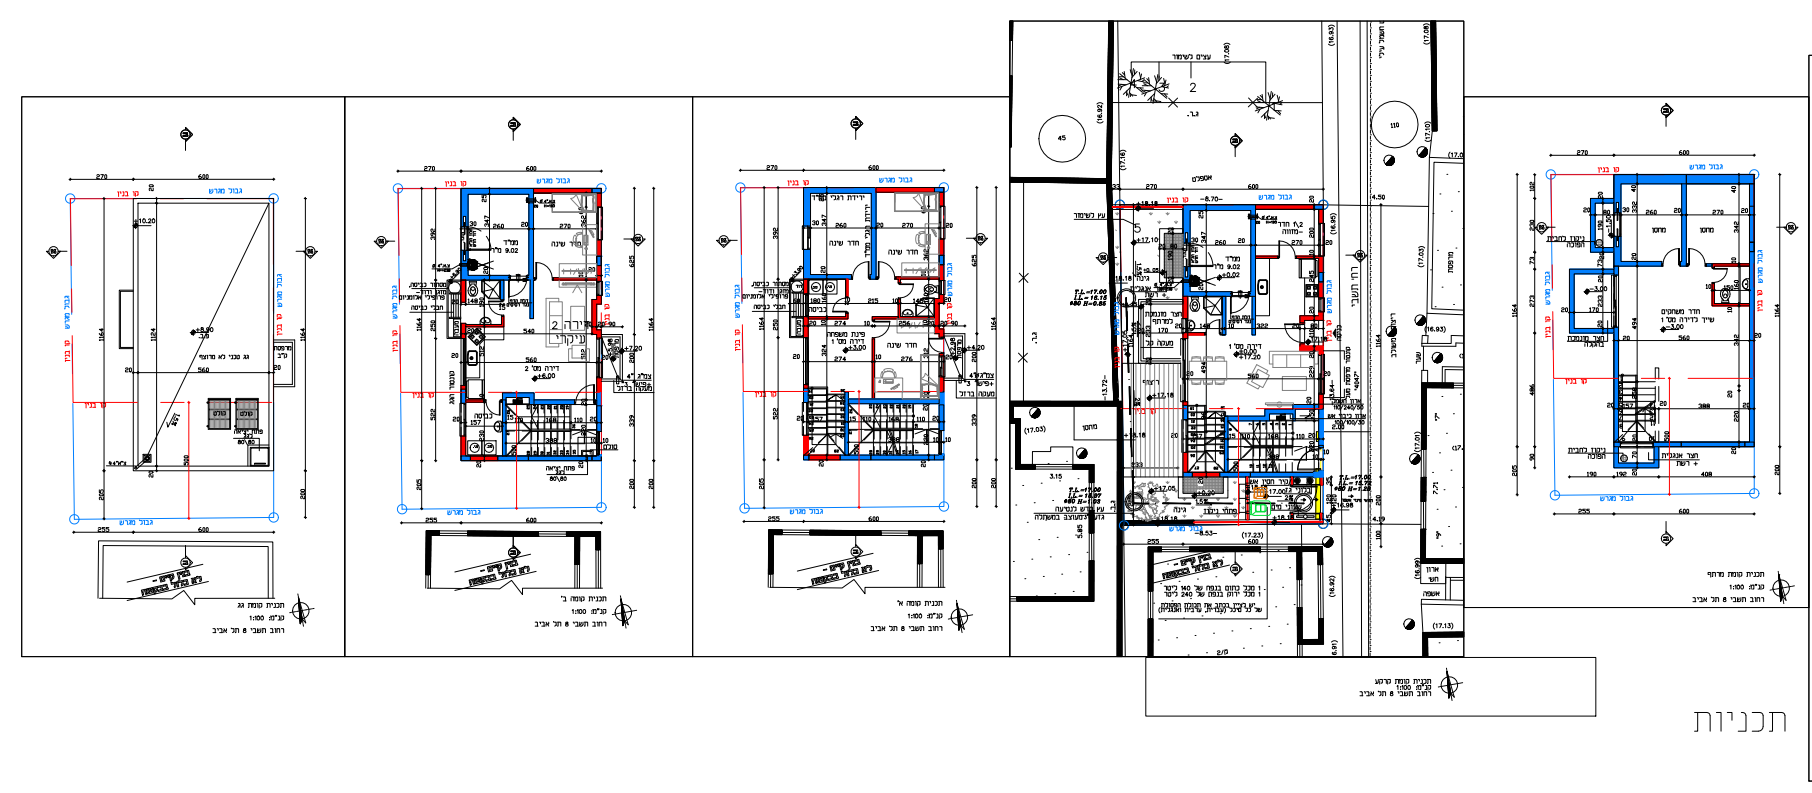

תכנית קומת מרתף
קנ"מ: 1:100
רחוב תשבי 8 תל אביב
חדר משחקים
שייך לדירה מס' 1
חצר אנגלית
+ רשת

תכניות

תכנית העמדה

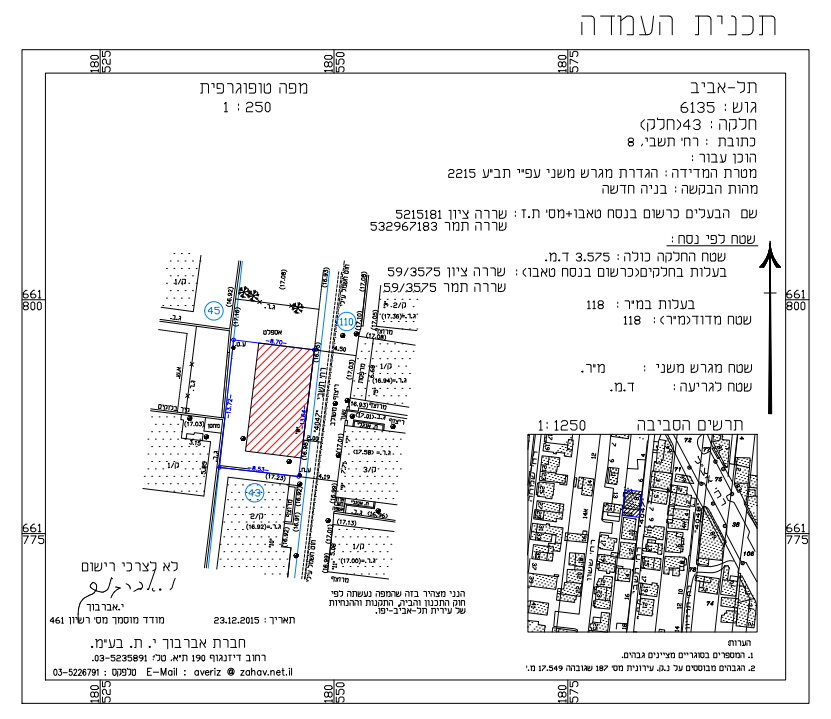

מפה טופוגרפית
1 : 250

תל-אביב
גוש : 6135
חלקה : 43(חלק)
כתובת : רח' תשבי, 8
הוכן עבור :
מטרת המדידה : הגדרת מגרש משני עפ"י תב"ע 2215
מהות הבקשה : בניה חדשה

שם הבעלים כרשום בנסח טאבו+מס' ת.ז : שרה ציון 5215181
שרה תמר 532967183

שטח לפי נסח :
שטח החלקה כולה : 3.575 ד.מ.
בעלות בחלקים(כרשום בנסח טאבו) : שרה ציון 59/3575
שרה תמר 59/3575

בעלות במ"ר : 118
שטח מדוד(מ"ר) : 118

שטח מגרש משני : מ"ר.
שטח לגריעה : ד.מ.

תרשים הסביבה 1:1250

הנני מצהיר בזה שהמפה נעשתה לפי חוק התכנון והבניה, התקנות וההנחיות של עיריית תל-אביב-יפו.

לא לצרכי רישום
י.אברבוך
מודד מוסמך מס' רשיון 461

תאריך : 23.12.2015

חברת אברבוך י. ת. בע"מ.
רחוב דיזנגוף 190 ת"א. טל': 03-5235891.
טלפקס : 03-5226791 E-Mail : averiz @ zahav.net.il

הערות:
1. המספרים בסוגריים מציינים גבהים.
2. הגבהים מבוססים על נ.ק. עירונית מס' 187 שגובהה 17.549 מ'.

180 550
180 575
180 525
661 800
661 775
45
43
110
אספלט
רח' תשבי
8.70
13.72
13.64
8.53
4047

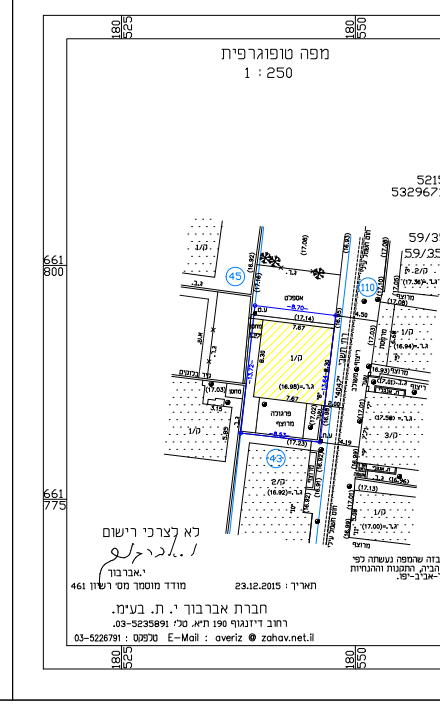

מפה טופוגרפית
1 : 250
לא לצרכי רישום
י.אברבוך
מודד מוסמך מס' רשיון 461