


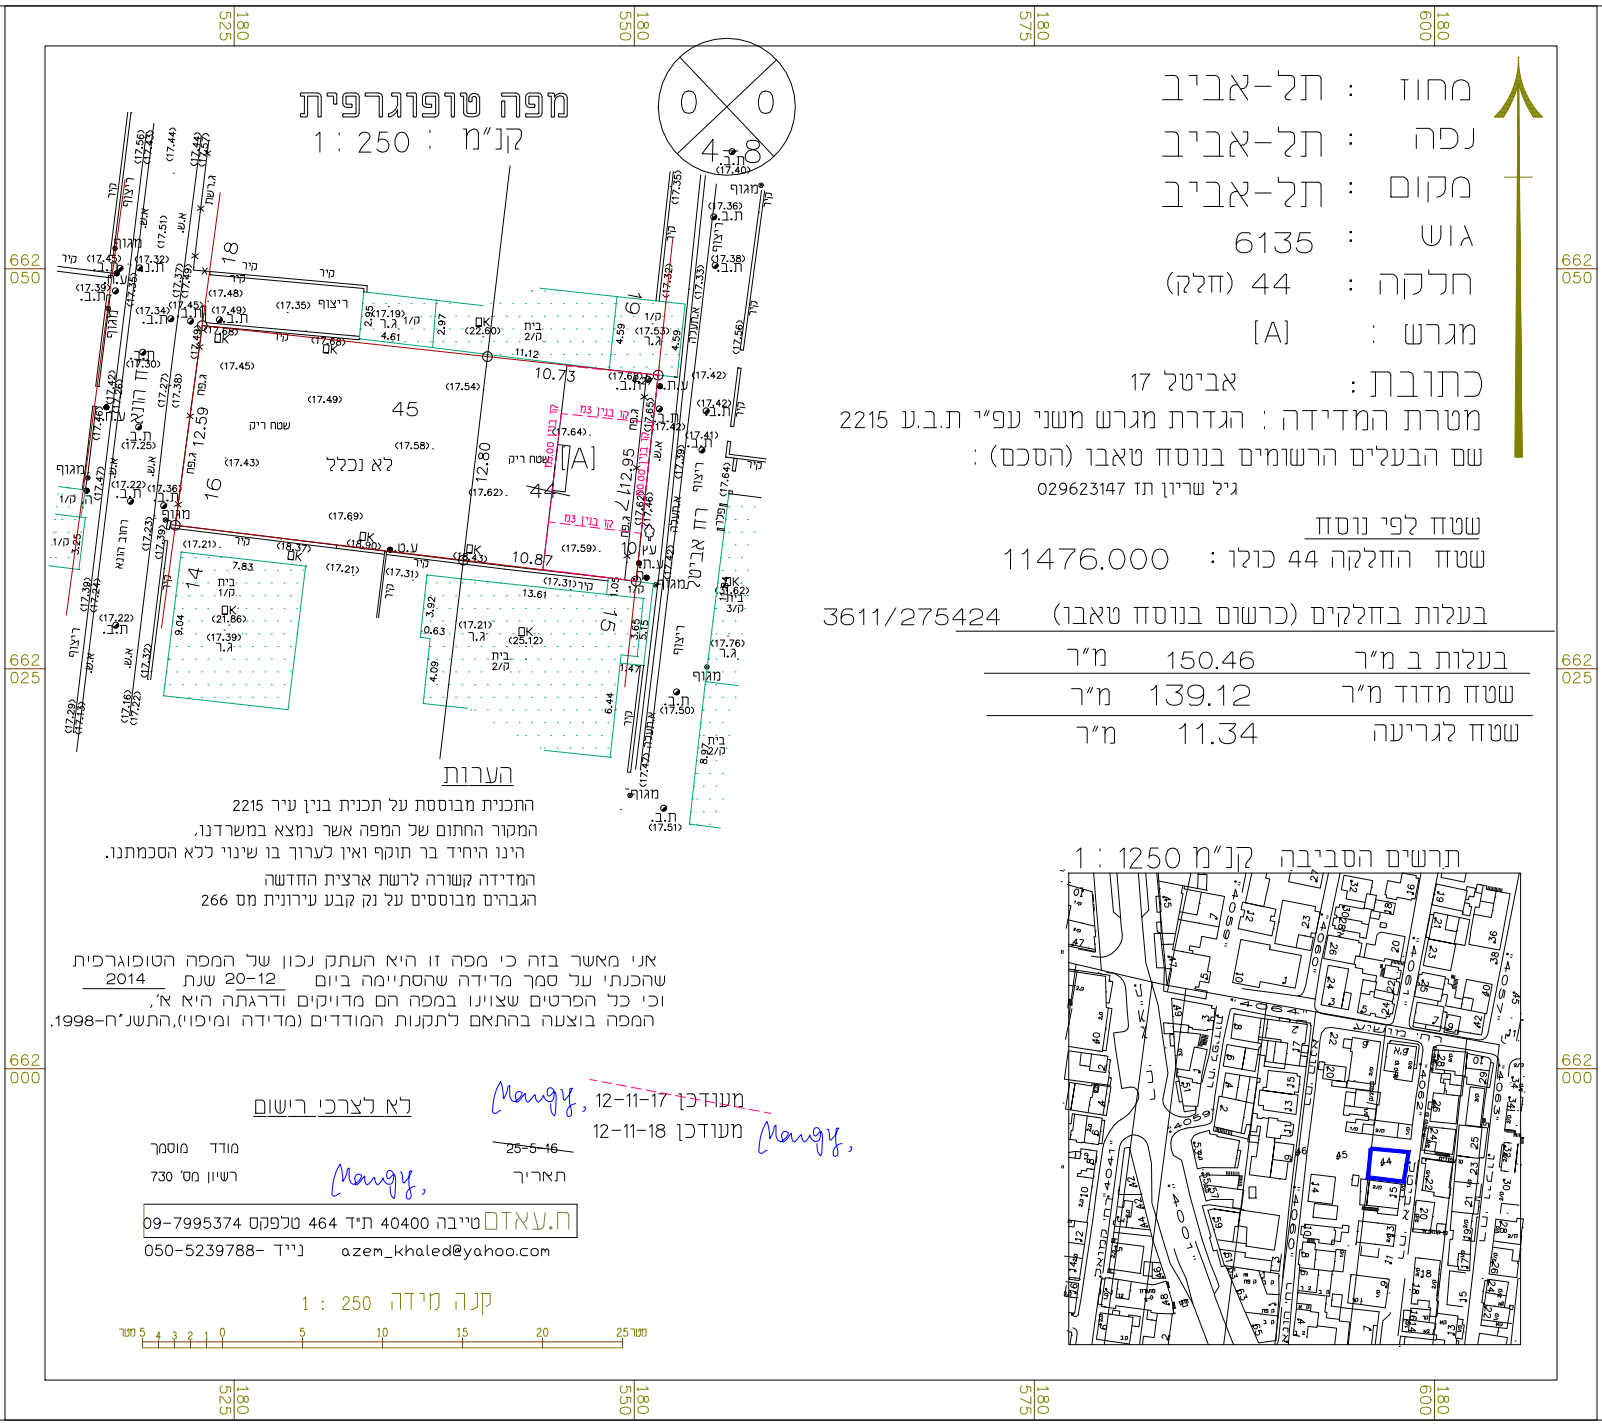

מחוז : תל-אביב
נפה : תל-אביב
מקום : תל-אביב
גוש : 6135
חלקה : 44 (חלק)
מגרש : [A]


כתובת : אביטל 17
מטרת המדידה : הגדרת מגרש משני עפ"י ת.ב.ע. 2215
שם הבעלים הרשומים בנוסח טאבו (הסכם) :
גיל שריון תז 029623147

שטח לפי נוסח
שטח החלקה 44 כולו : 11476.000

בעלות בחלקים (כרשום בנוסח טאבו) 3611/275424

בעלות ב מ"ר	150.46	מ"ר
שטח מדוד מ"ר	139.12	מ"ר
שטח לגריעה	11.34	מ"ר

תרשים הסביבה קנ"מ 1 : 1250

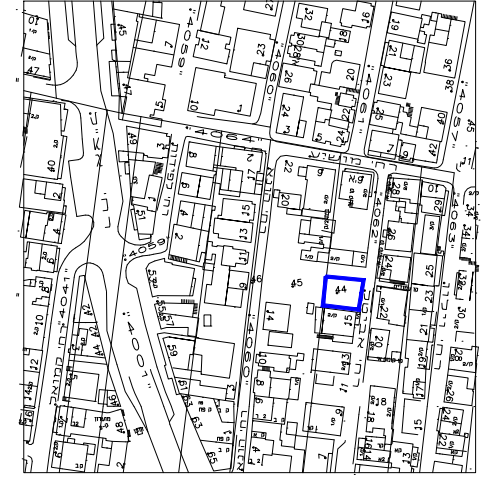

התכנית מבוססת על תכנית ביון עיר 2215
המקור החתום של המפה אשר נמצא במשרדנו.
הינו היחיד בר תוקף ואין לערוך בו שינוי כלא הסכמתנו.
המדידה קשורה לרשת ארצית החדשה
הגבהים מבוססים על נק קבע עירונית מס 266

אני מאשר בזה כי מפה זו היא העתק נכון של המפה הטופוגרפית
שהכנתי על סמך מדידה שהסתיימה ביום 12-20 שנת 2014
וכי כל הפרטים שצוינו במפה הם מדויקים ודרגתה היא א'
המפה בוצעה בהתאם לתקנות המודדים (מדידה ומיפוי) התשס"ח-1998.

לא לצרכי רישום
מודד מוסנר
רשיון מס' 730
מערבון 12-11-17 Mangy,
מערבון 12-11-18 Mangy,
תאריך 25-5-16
ח.ע.א.ד.מ טייבה 40400 תיד 464 טלפקס 09-7995374
azem_khaled@yahoo.com נייד 050-5239788

