


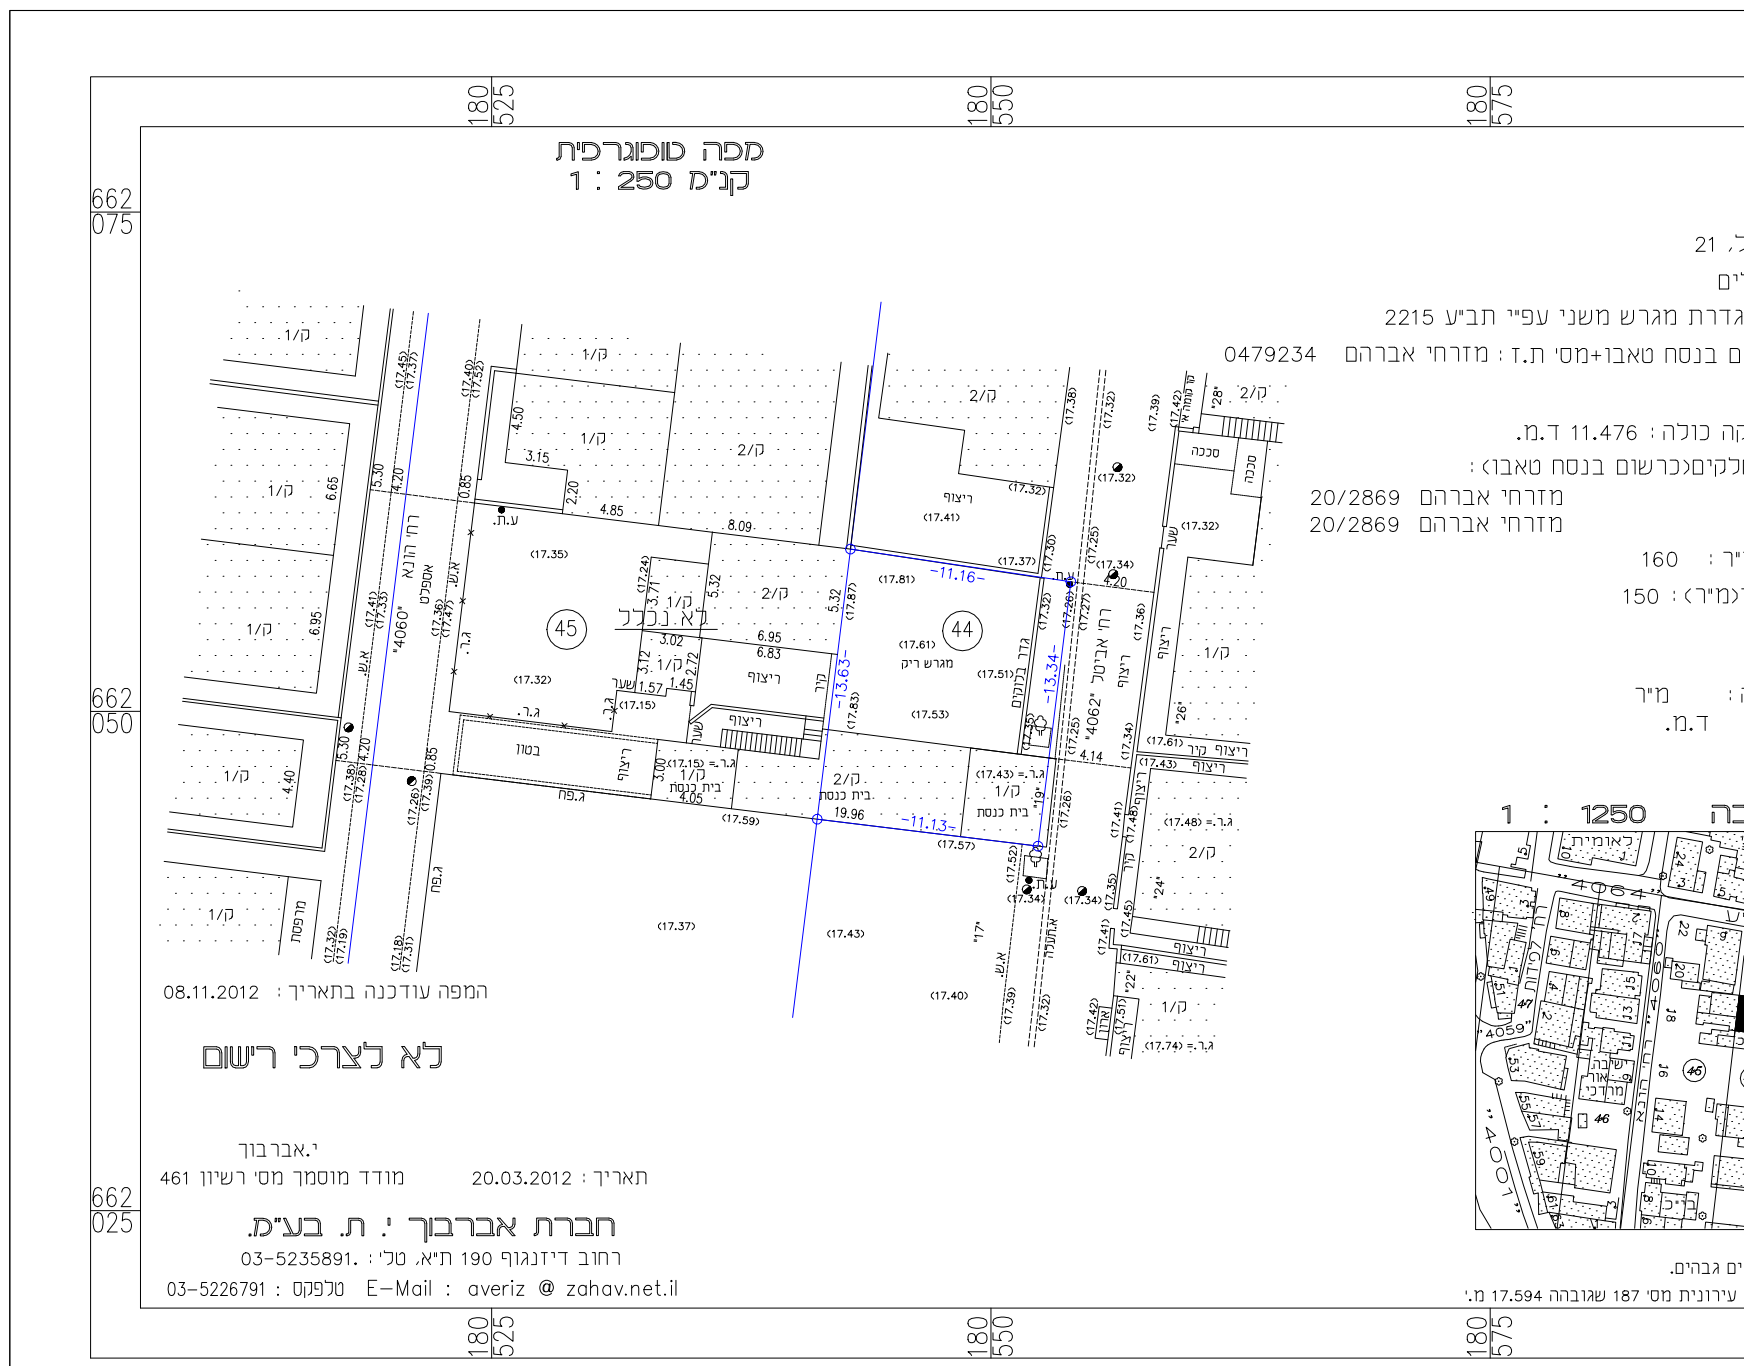
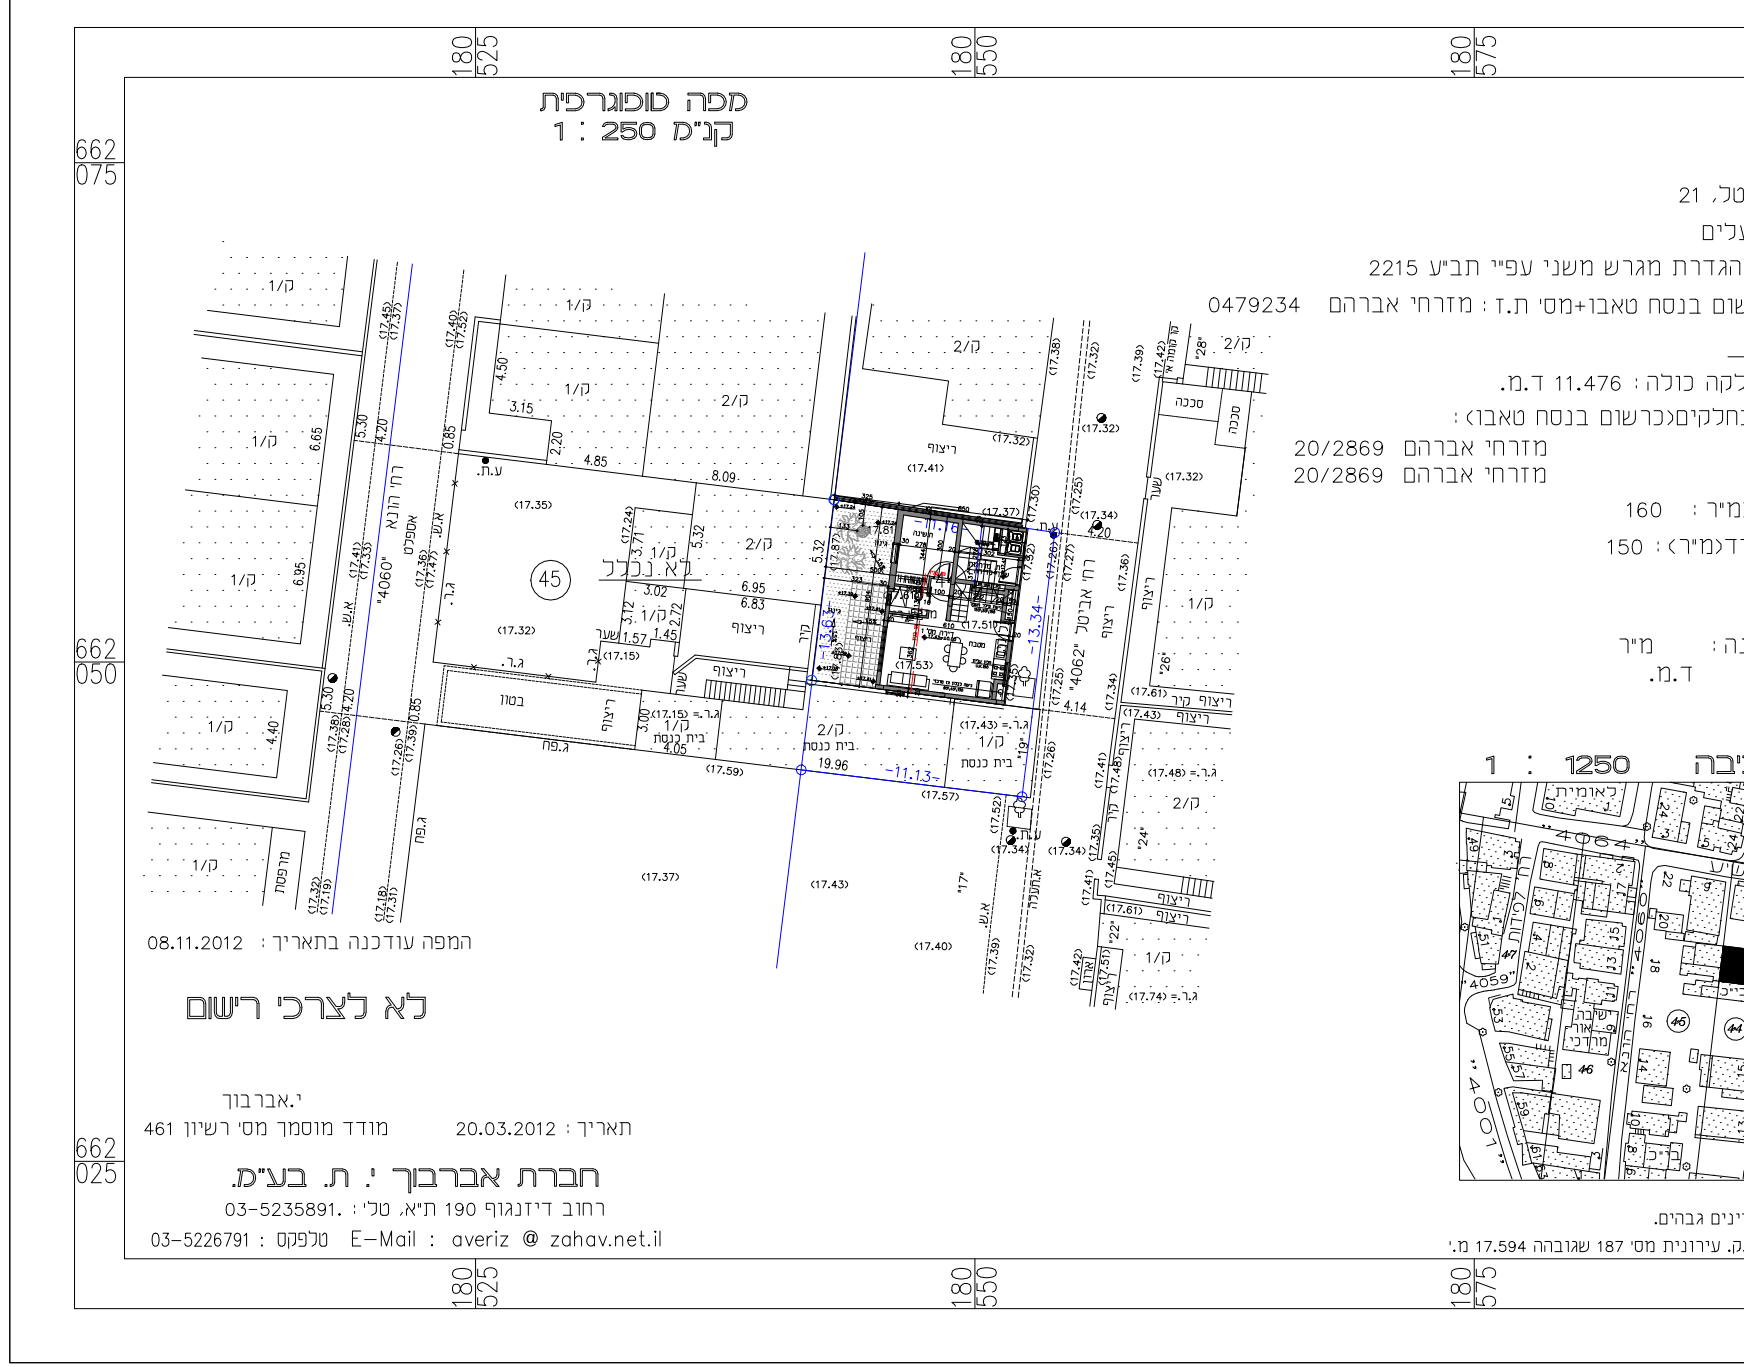
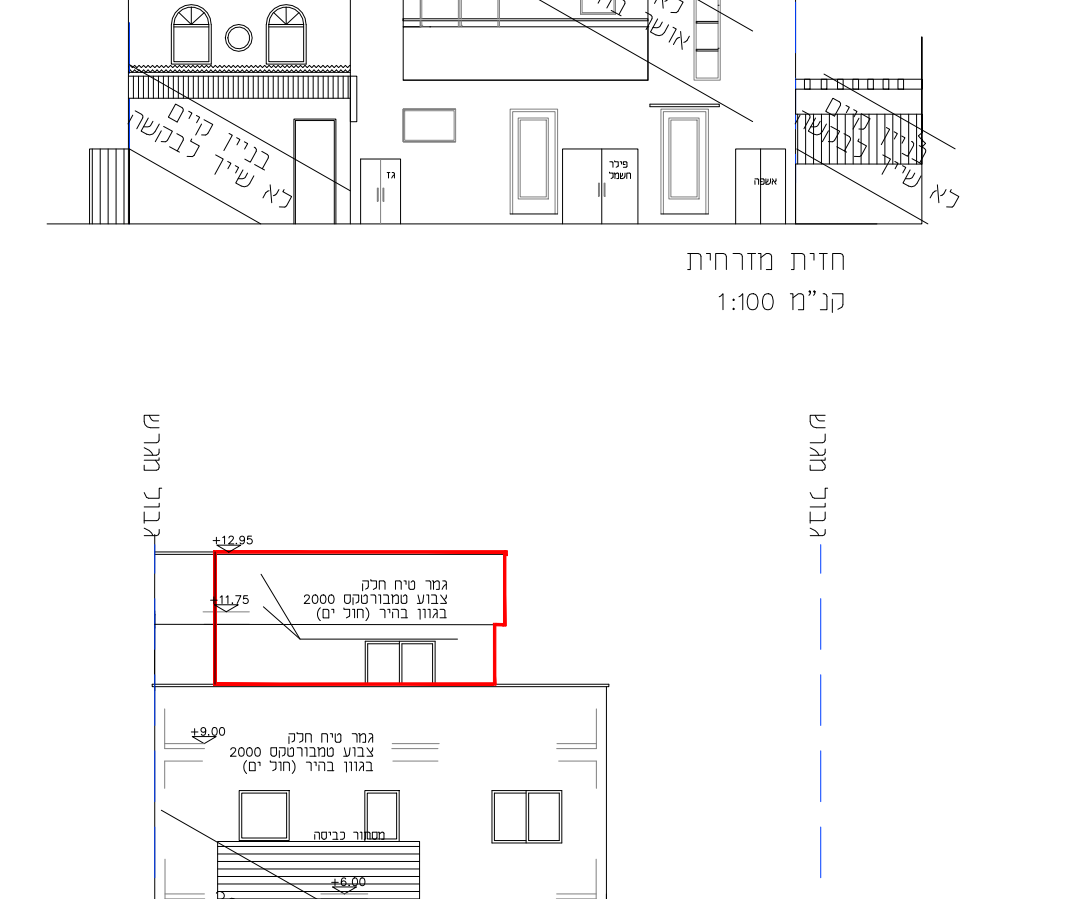
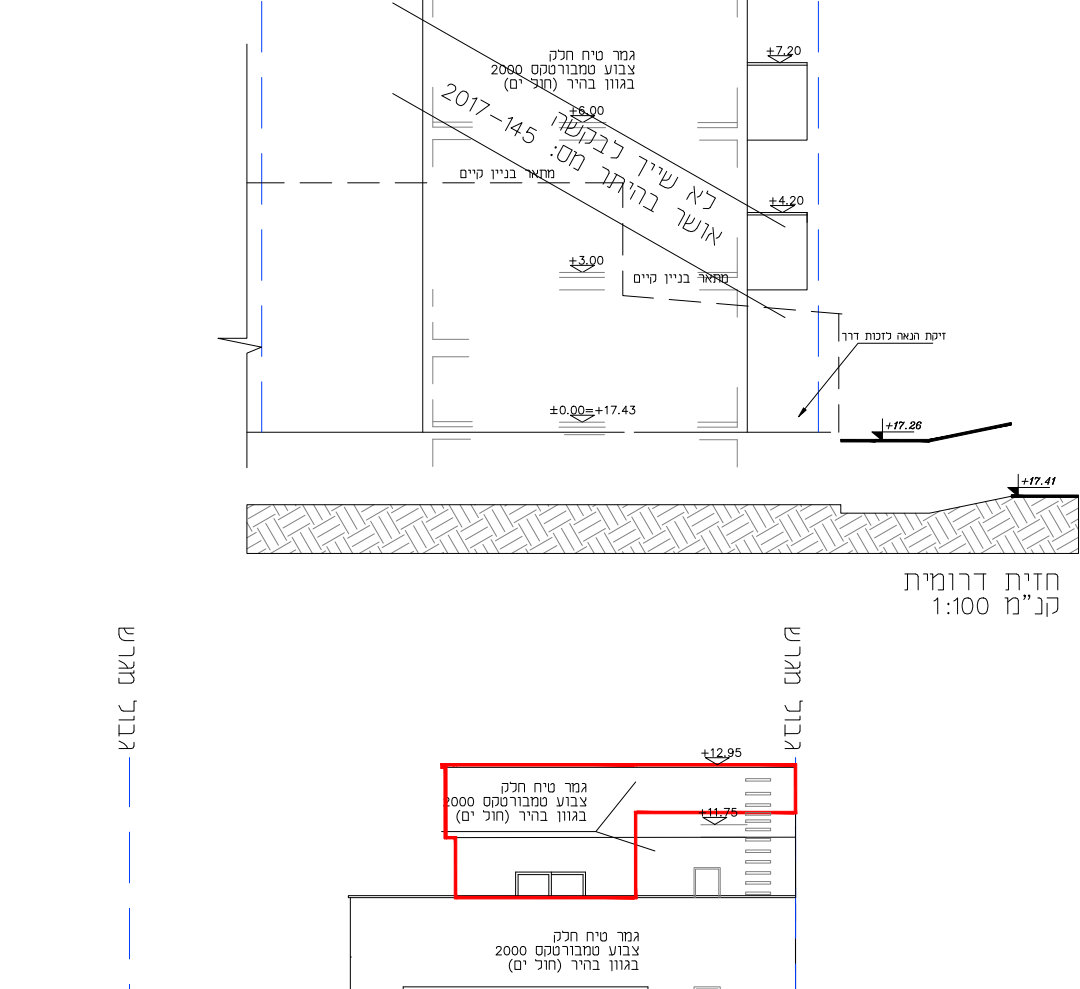
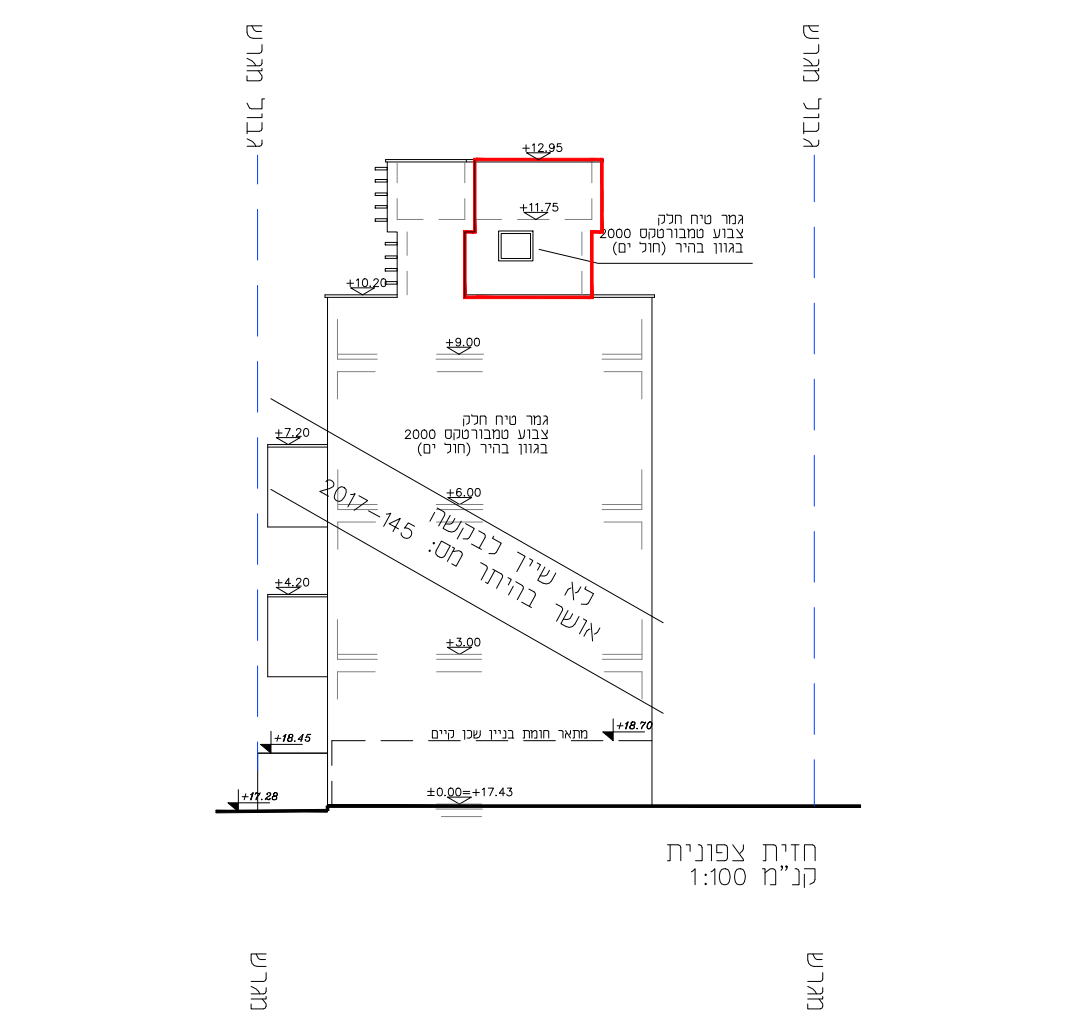
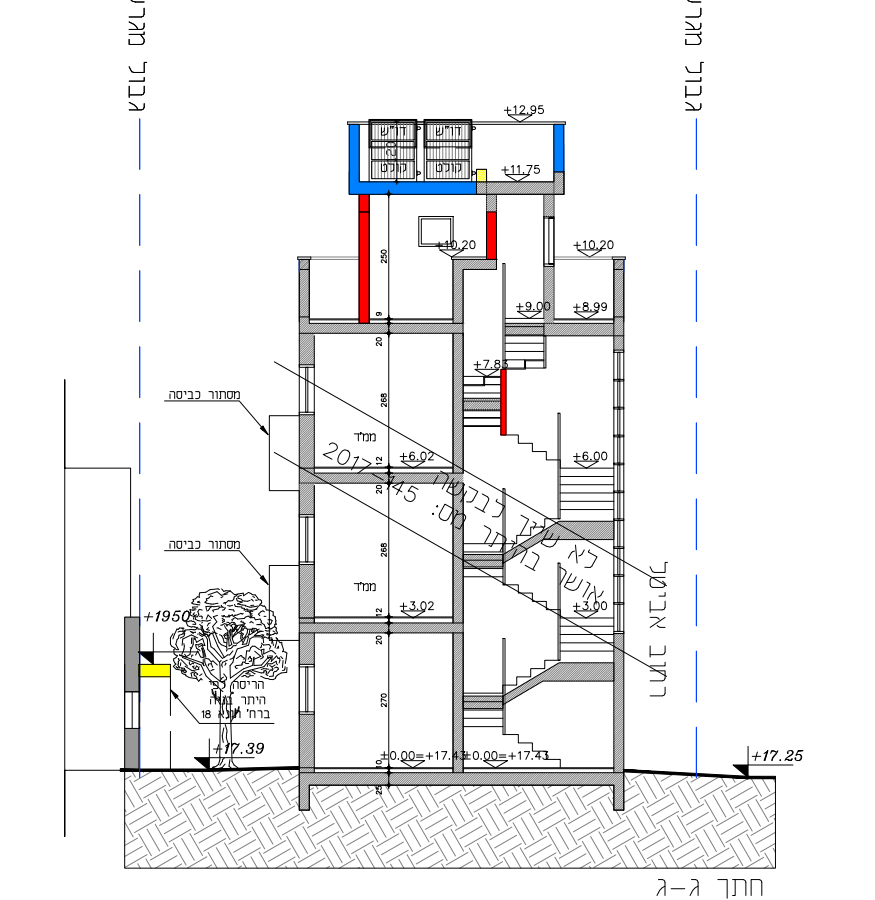
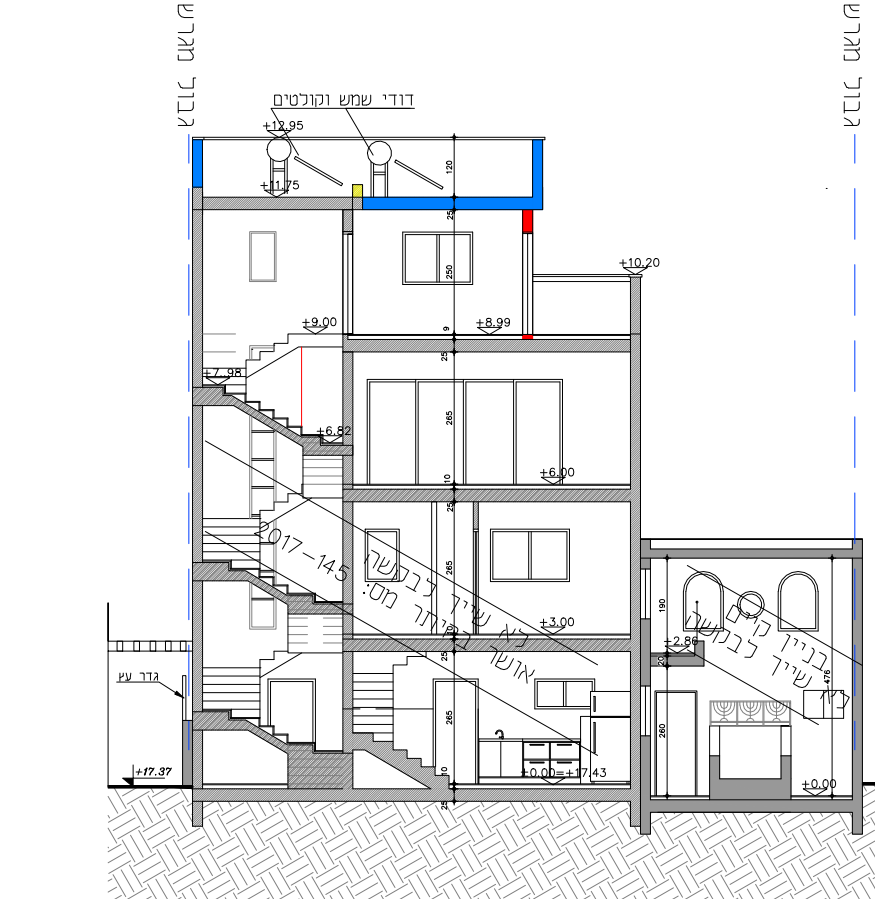
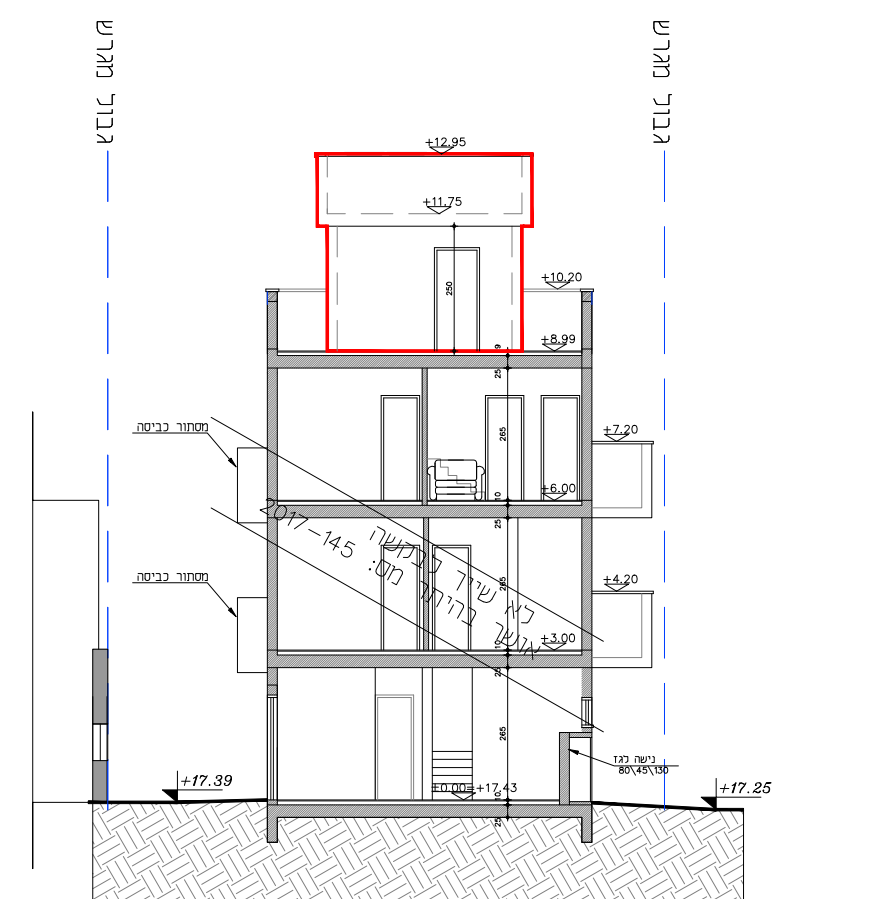
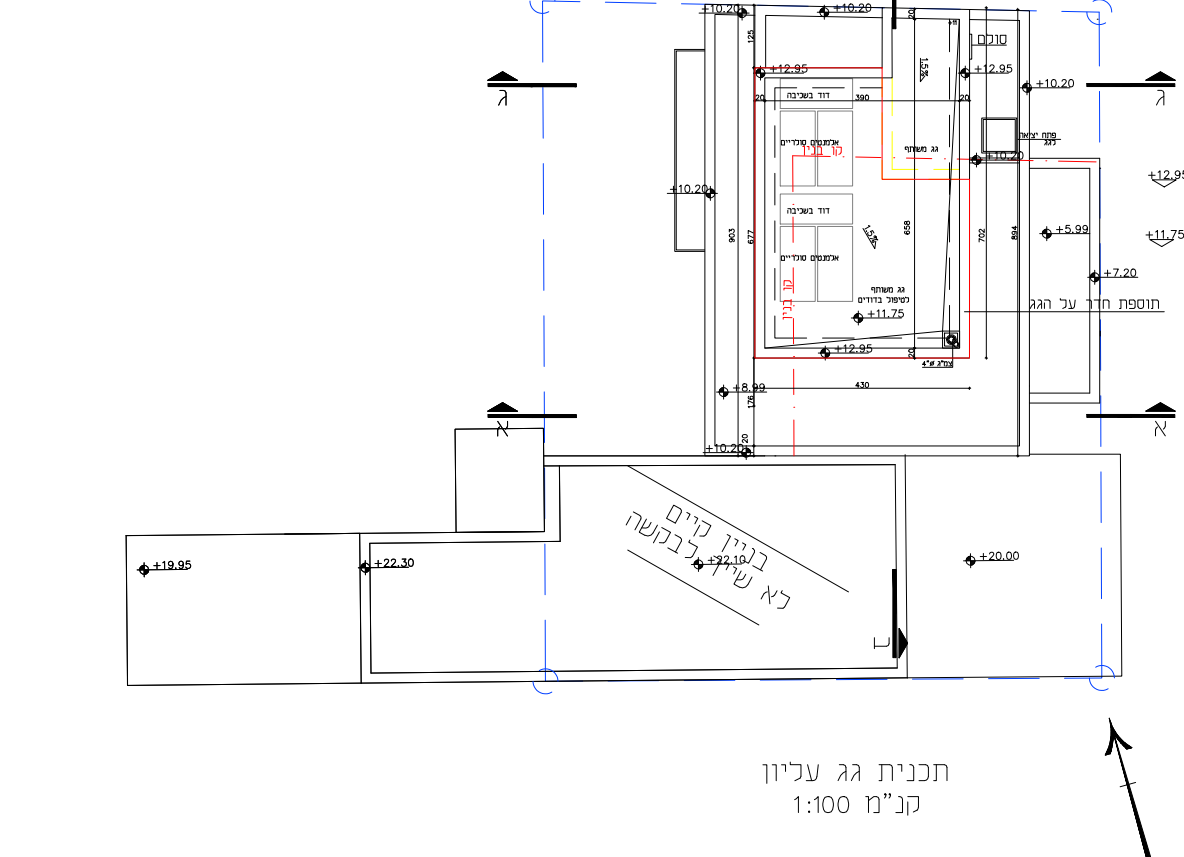
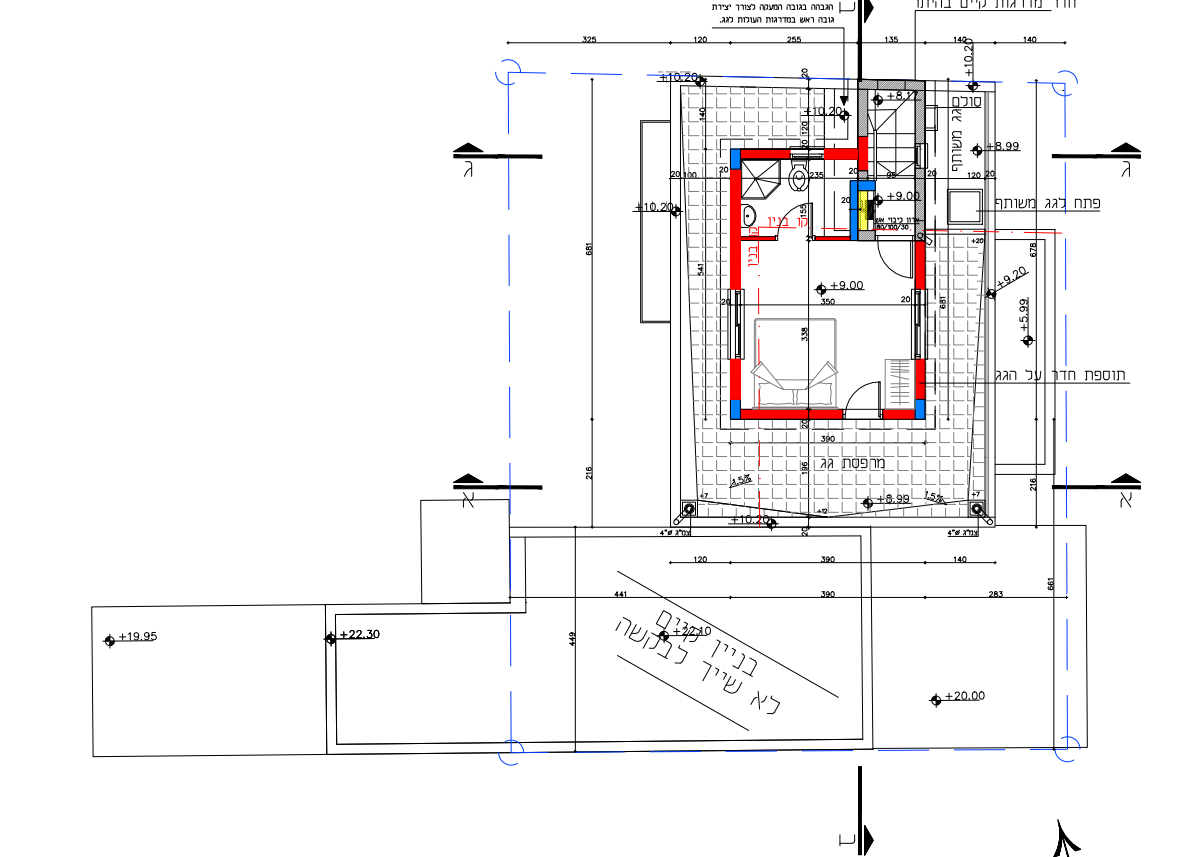


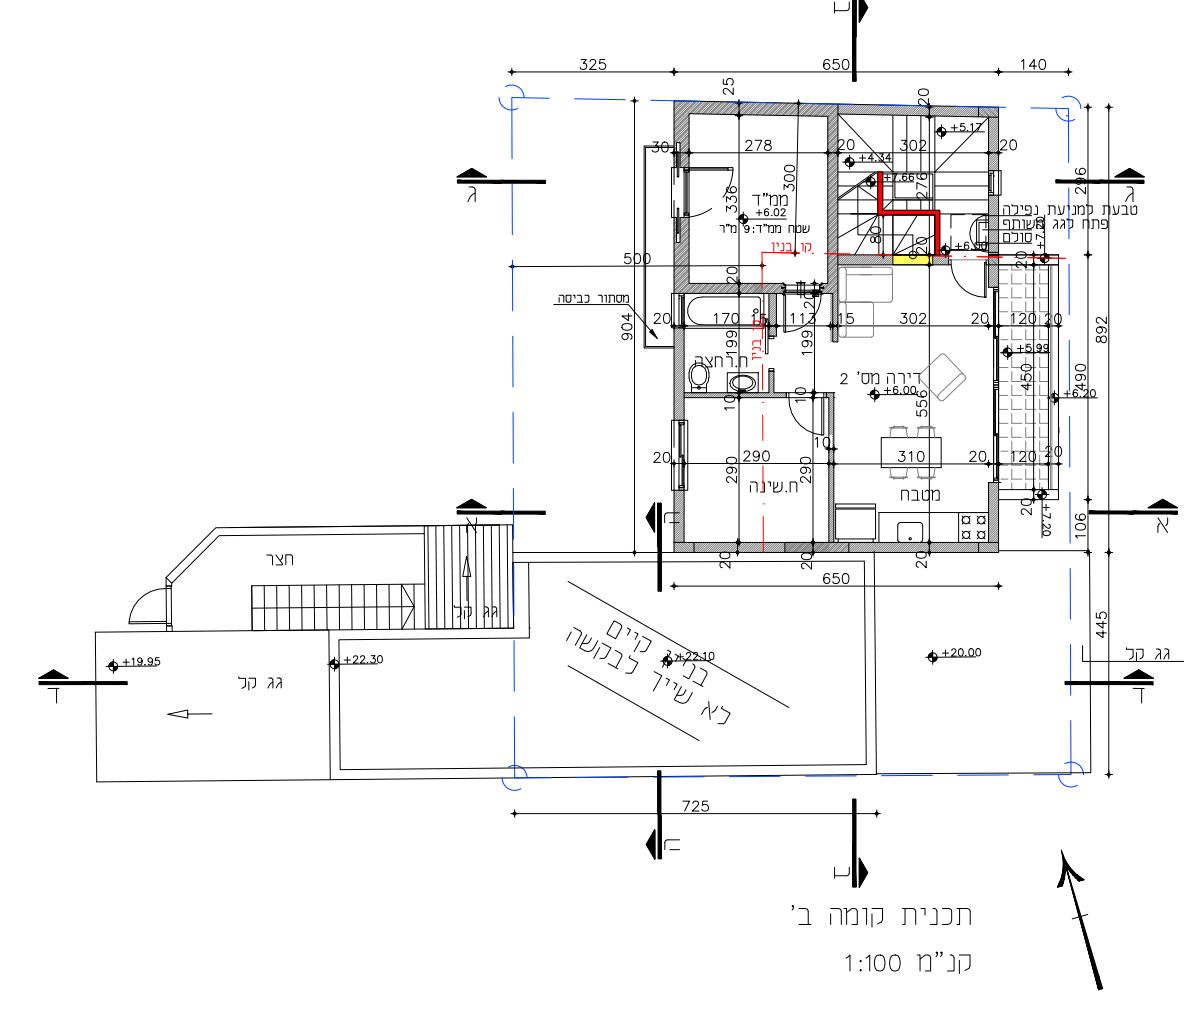

מפה טופוגרפית

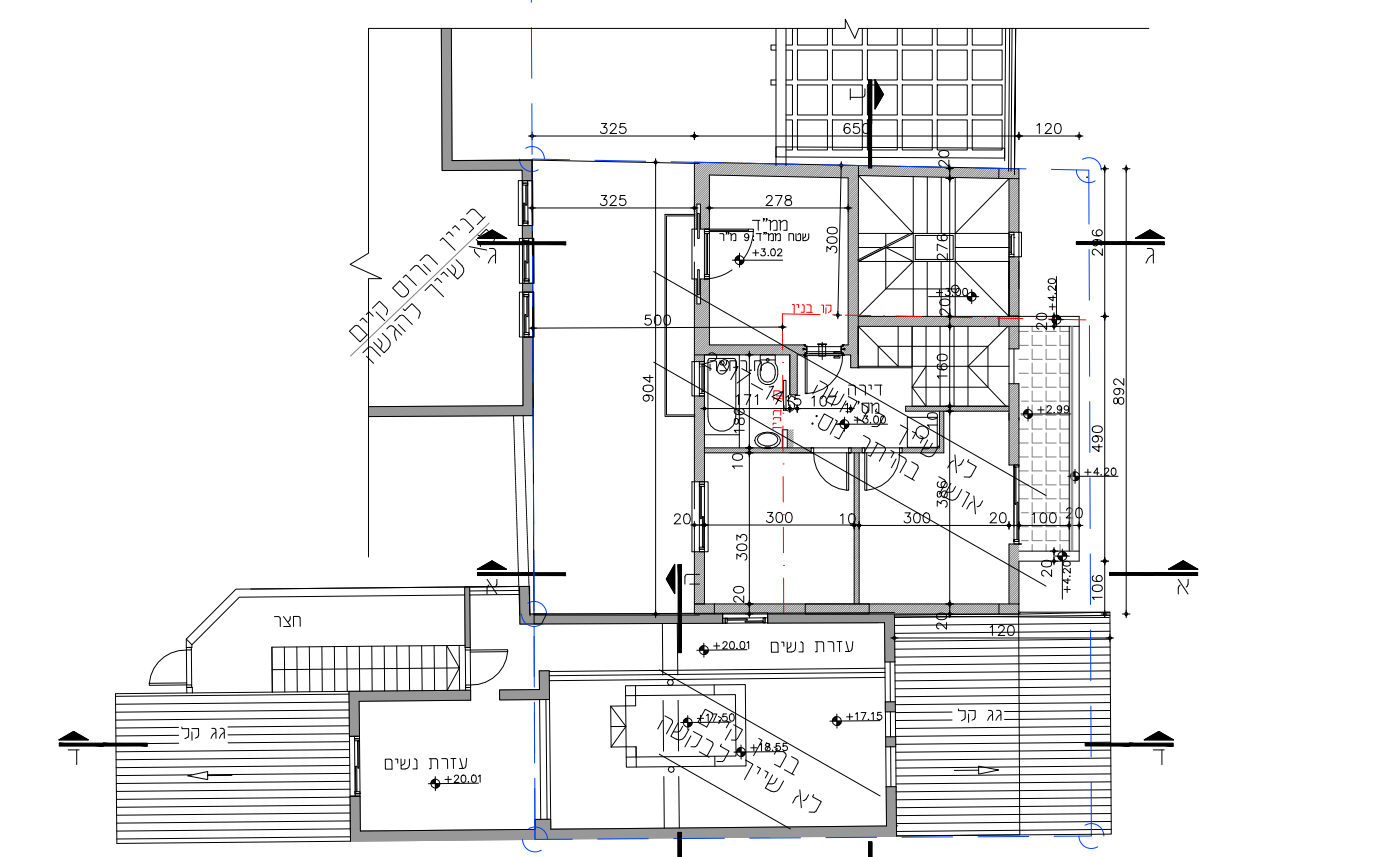



תוכנית העמדה

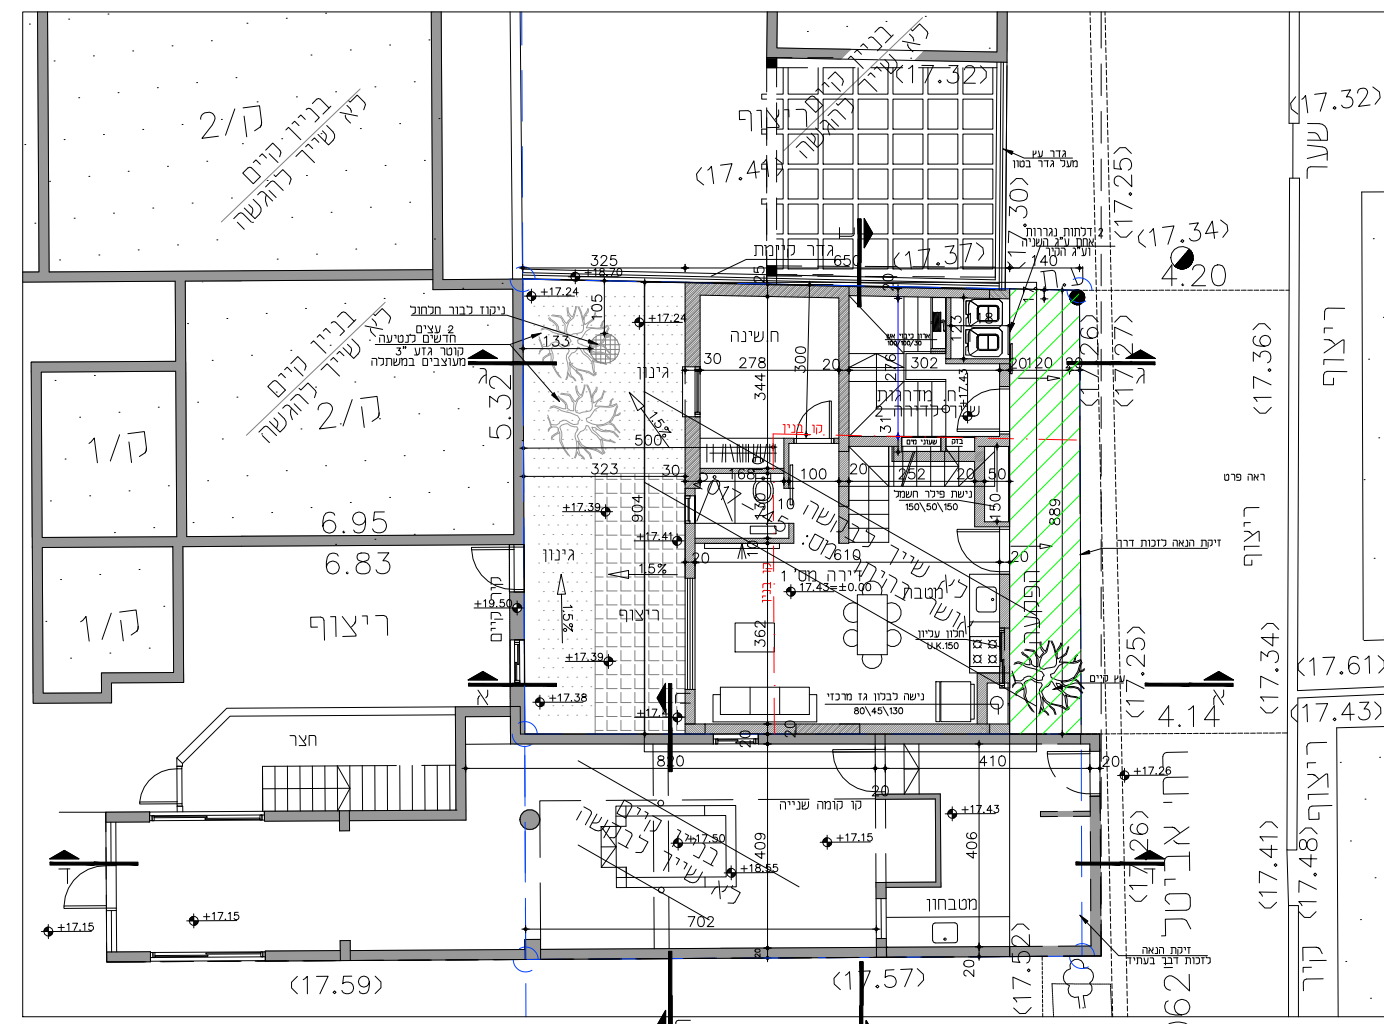

חזיתות

חתכים

תוכניות

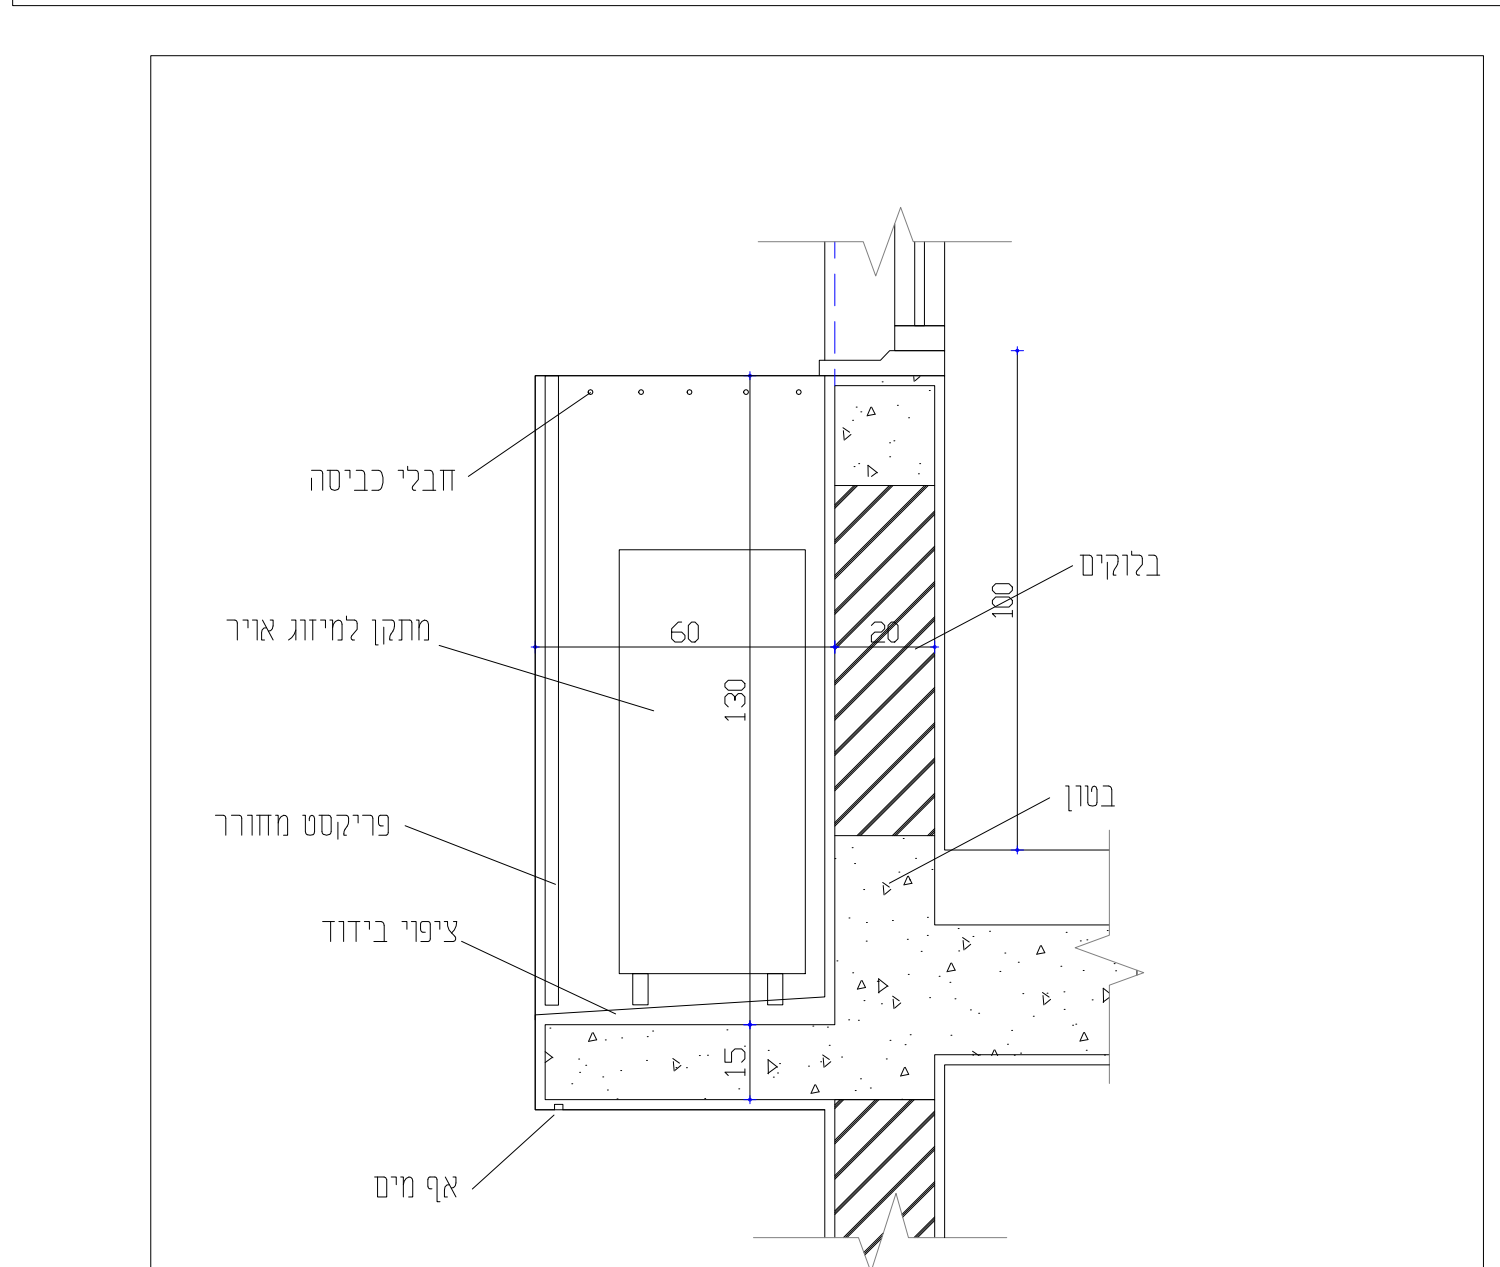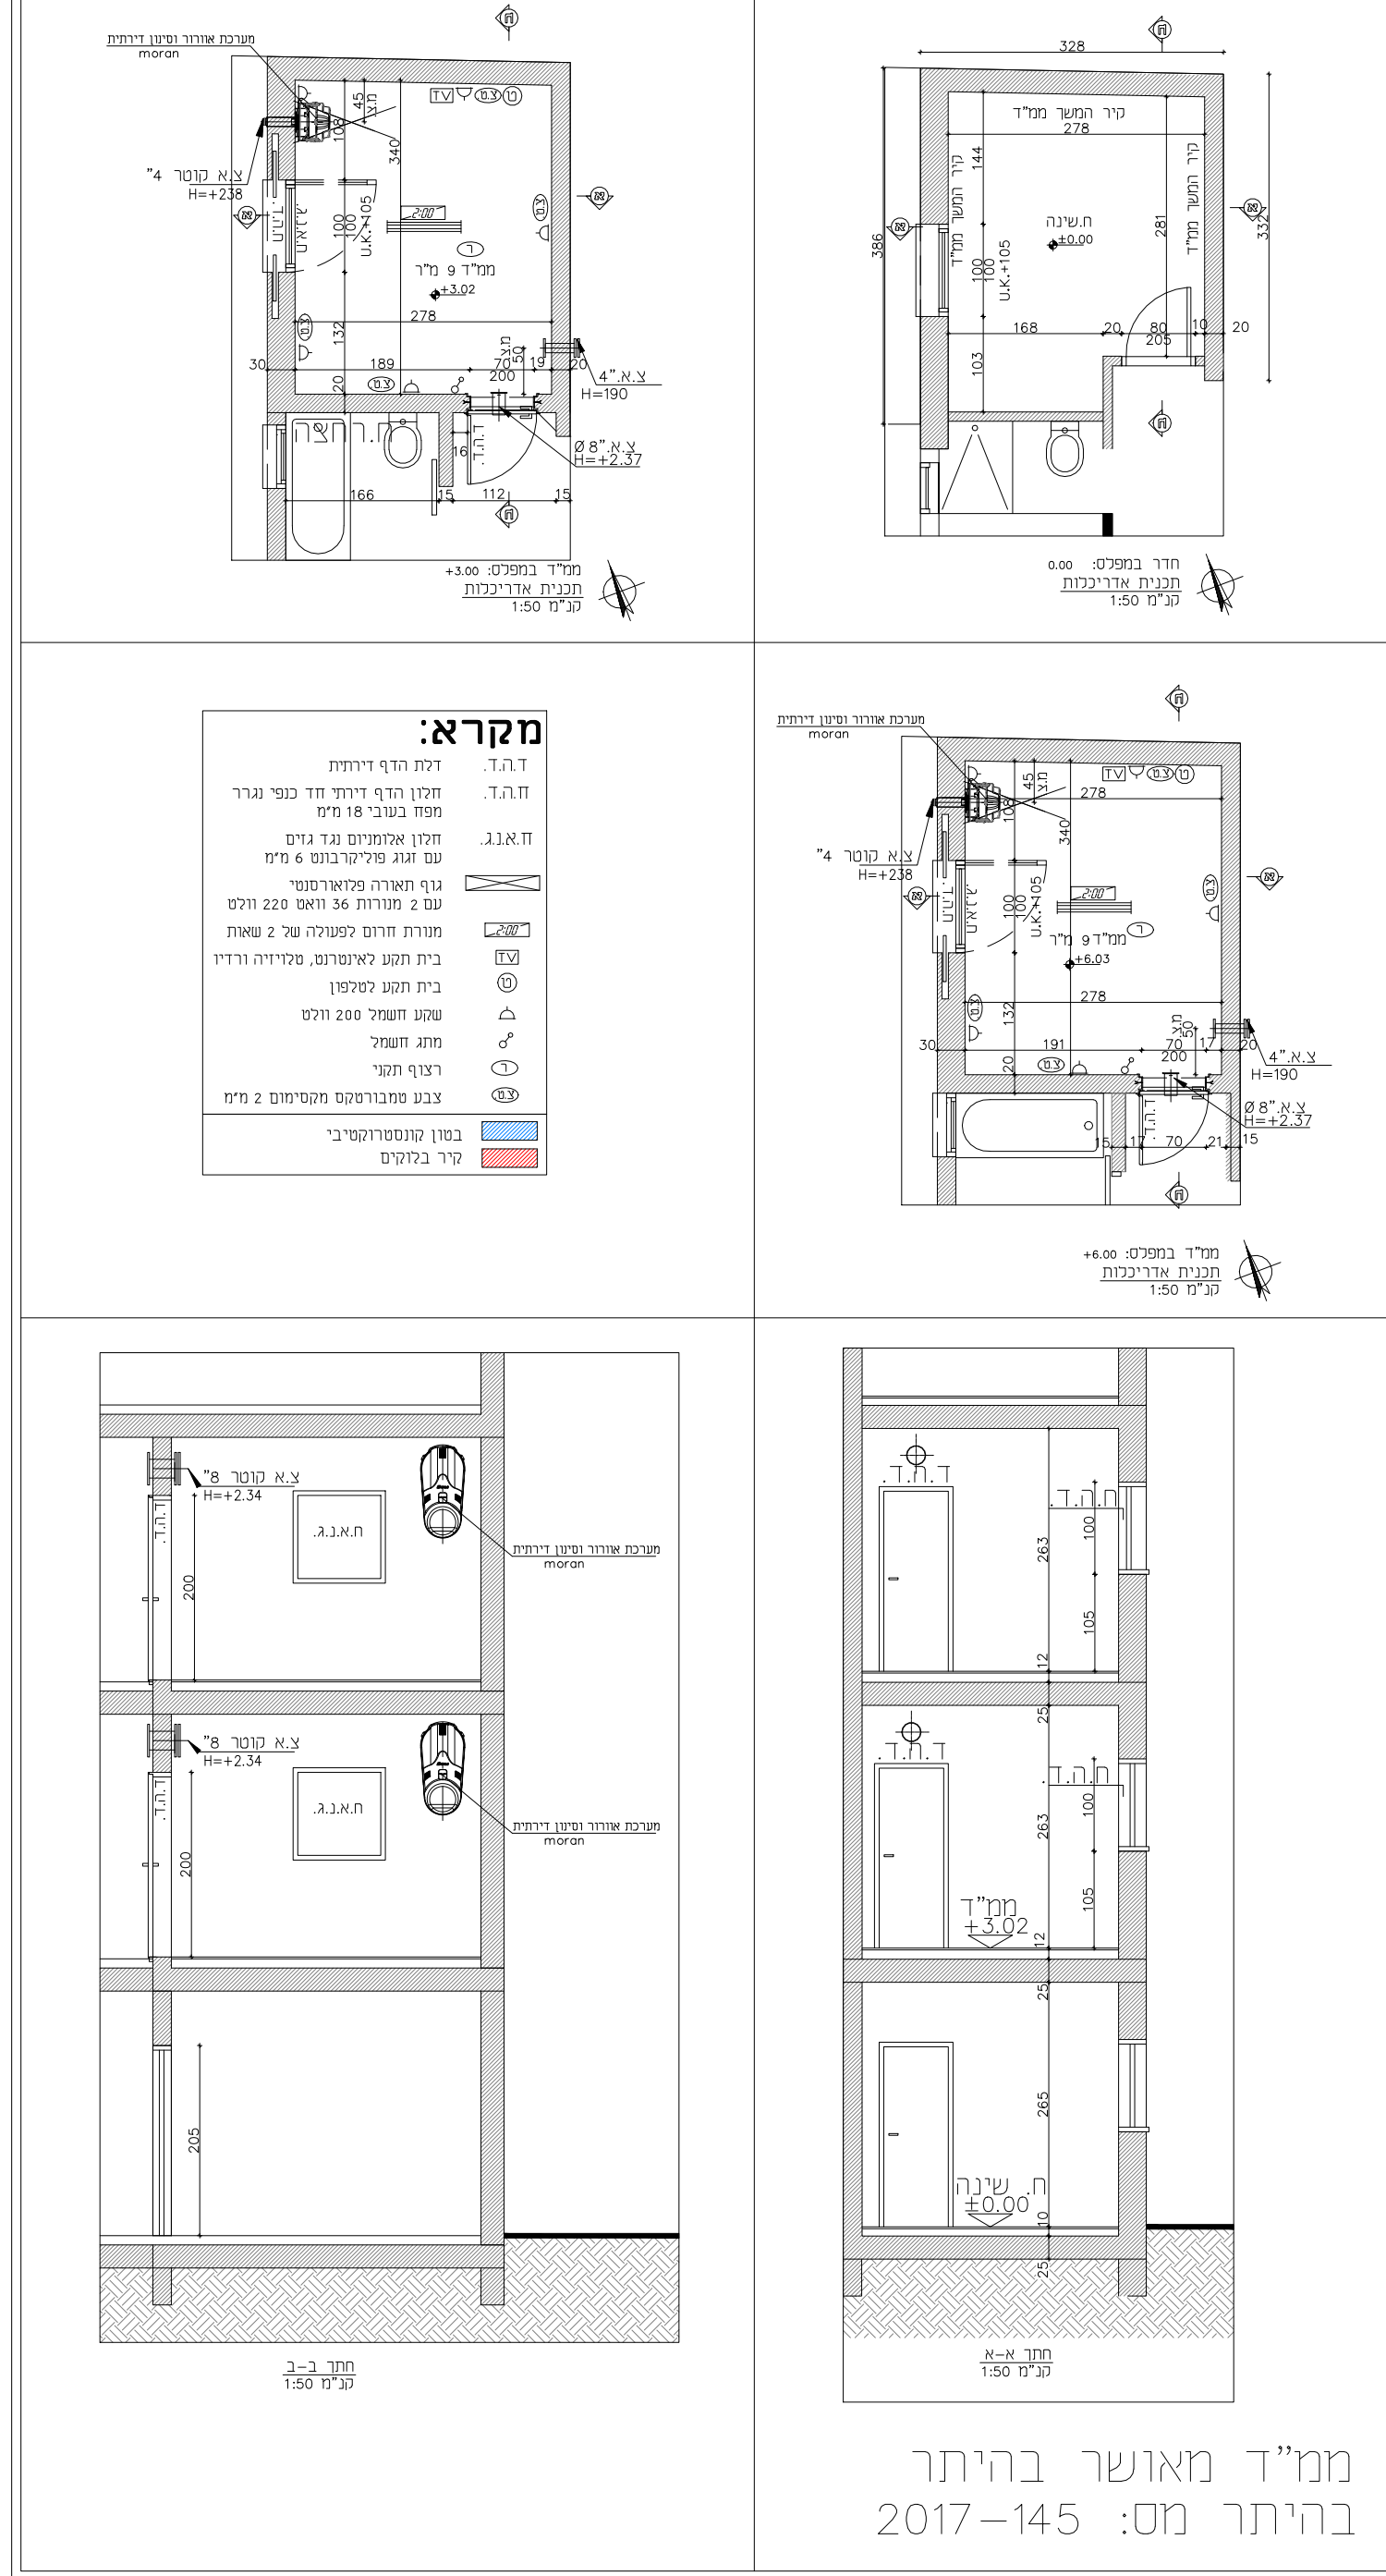

פרט מסתור כביסה ומזגנים
קנה מידה 1:20